

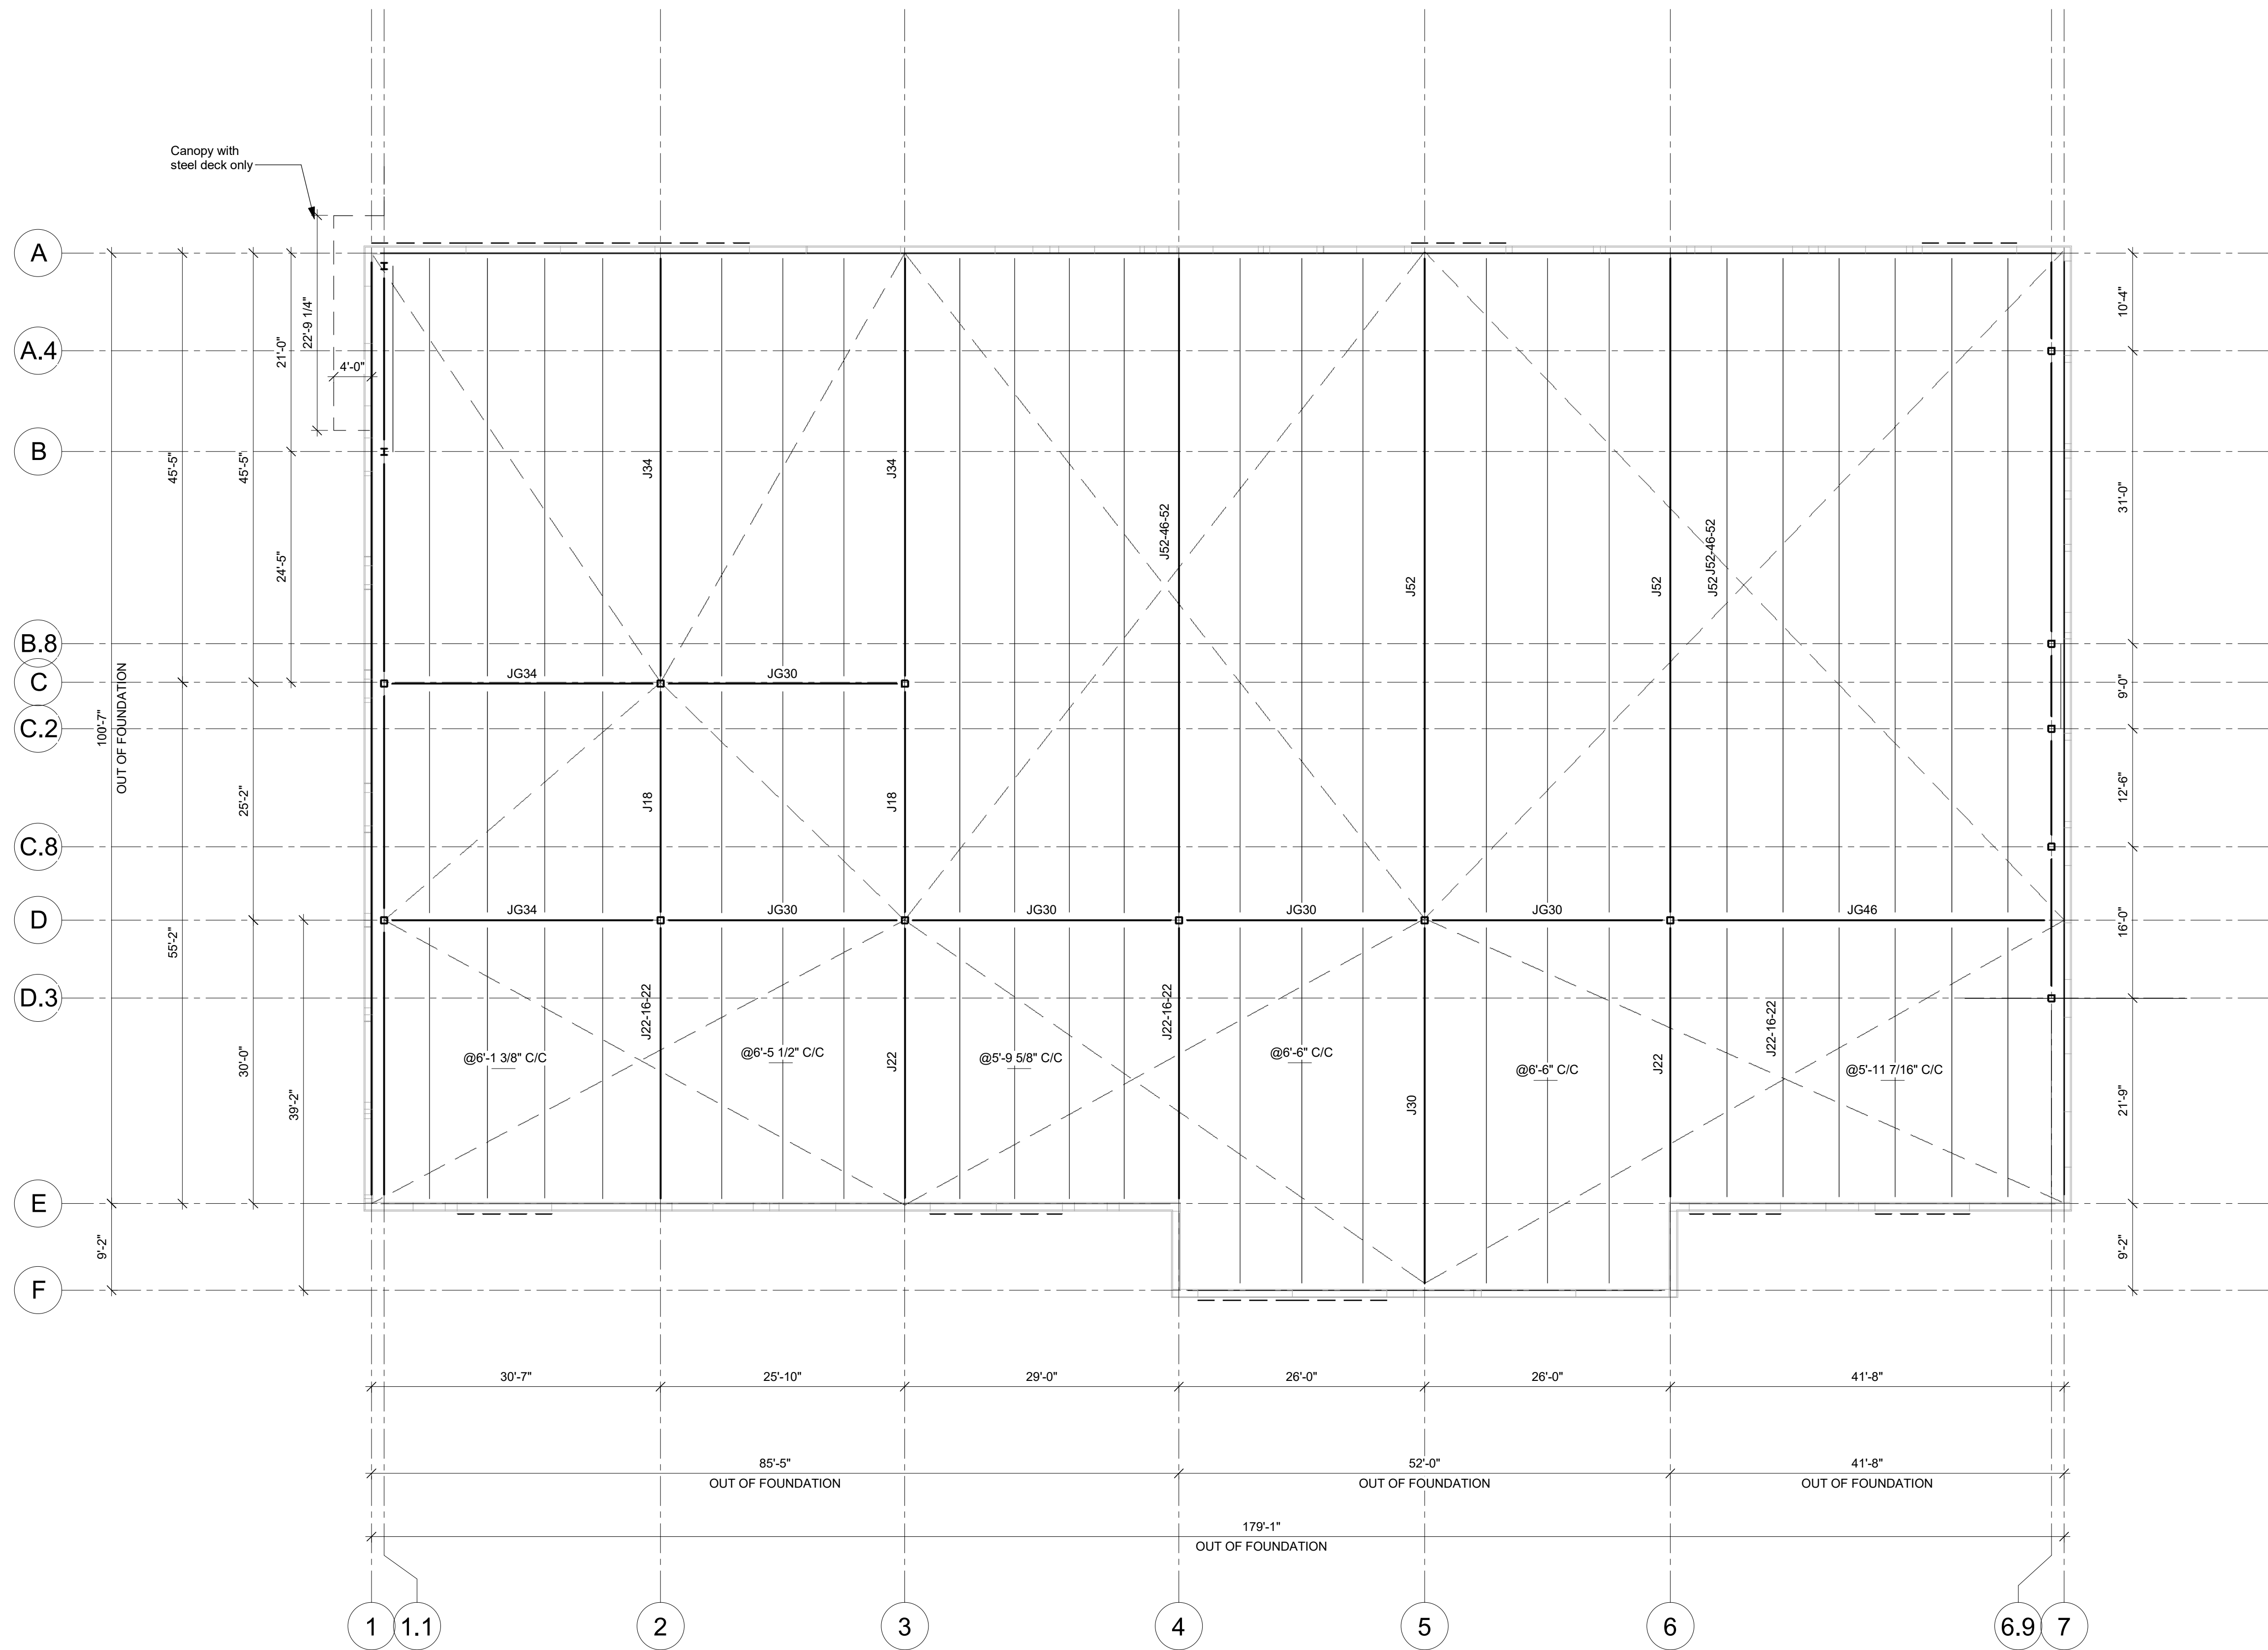


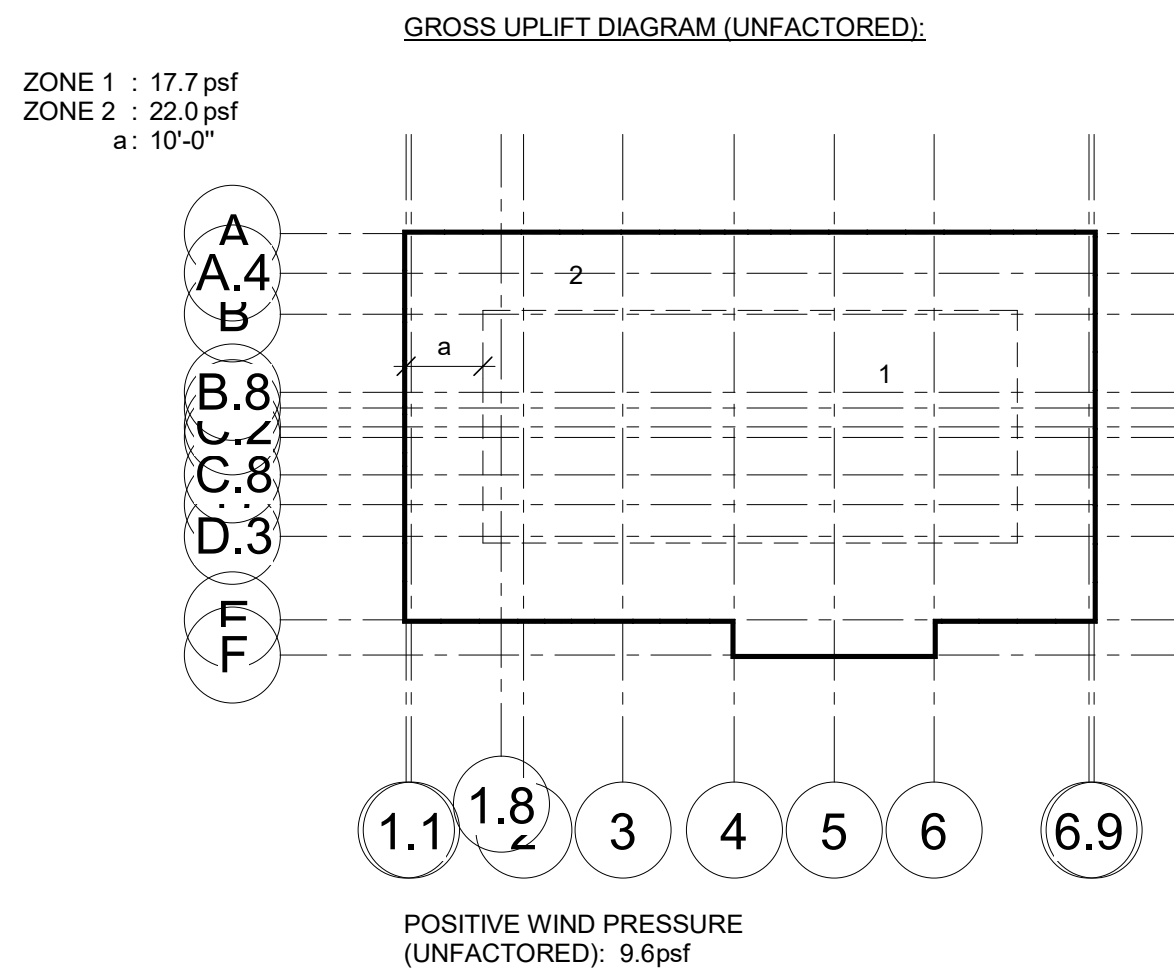

SNOW LOAD ACCUMULATION

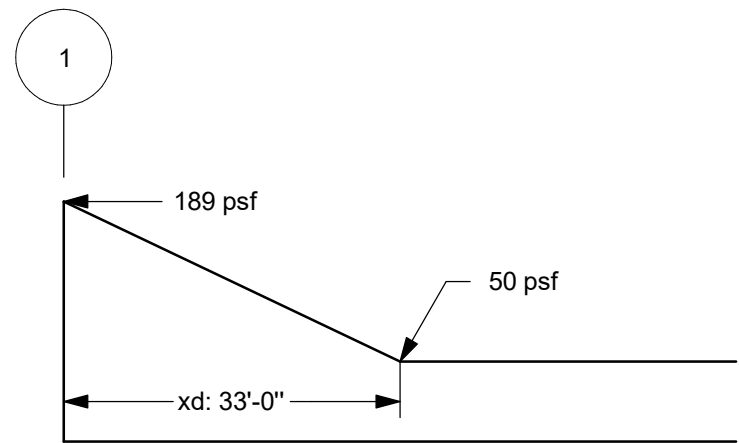

ROOF PLAN
1" = 10'-0"

CONTRACTOR/RECTOR NOTE:

IT IS PROHIBITED TO MODIFY, COPY, REPRODUCE OR OTHERWISE
DISTRIBUTE THIS DRAWING OR ANY REPRESENTATION OF THIS
DRAWING, OR ANY MEDIA, INCLUDING ELECTRONIC, WITHOUT THE
PRIOR WRITTEN APPROVAL OF CANAM GROUP INC.

ROOF

TOP OF PLASTER RWL : 88'-0"
TOP OF PLASTER : 89'-0"
TOP OF SLAB : 100'-0"
TOP OF FOUNDATION : 100'-0"
CLEAR HEIGHT : 25'-0"
TOP OF STEEL : 129'-4"
PARAPET HEIGHT : 1'-2"
TOP OF PARAPET : 130'-6"

LOADS

D.L. : 18 psf
C.O.L. : 4.0 psf
Ss : 52.25 psf
Sr : 8.36 psf
Cb x Cw : 0.8
Roof L.L. : 0.0psf
Is : 1.0
Roof snow load : 50.1 psf
Iu : 1.0
Wind q= 150 : 8.6psf

Seismic (Site class D (Assumed))

Ie : 1.0
Ss (0.2) : 0.579
Ss (0.5) : 0.482
Ss (1.0) : 0.294
Ss (2.0) : 0.141
Ss (5.0) : 0.0394
Ss (10.0) : 0.0123
PGA : 0.34
PGV : 0.342

Position de la colonne HSS et W:

- On va conserver 1'-4" pour la majorité des cas.
- Pour la coupe de mur R-29 et 2 heures au feu, on va mettre 1'-6".
- Lorsqu'on va avoir des colonnes de panneau C10 et C12, on va déterminer la localisation de la colonne selon le design. L'idée est de rester avec 1'-4" et 1'-6", mais dans certain cas, on va devoir utiliser 1'-8".

HSS and W column position:


- We will keep 1'-4" for the majority of cases.
- For the R-29 and 2-hour fire wall, we will put 1'-6".
- When we have C10 and C12 panel columns, we will determine the location of the column according to the design. The idea is to stay with 1'-4" and 1'-6", but in some cases, we will have to use 1'-8".

PRELIMINARY

NOT TO BE USED FOR CONSTRUCTION

REVISION	DATE	DESCRIPTION	DESIGN	VER
PROJECT MANAGER				
DRAFTING				
DRAWN	DESIGNED	PROJECT ENGINEER	SCALE:	
INITIALE		PROJECT ENG.	Comme indiqué	
CHECKED	CONSULTING ENGINEERS ARCHITECTS	ENGINEER	DATE (YYYYMMDD)	
		ARCHITECT	YYYYMMDD	

CUSTOMER:

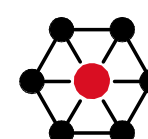

CANAM

11505, 1re Avenue, bureau 500, Saint-Georges Beauce
Châteauguay, Québec, G5V 7G3
Phone : (418) 228-8031
Toll free : (877) 499-6049
www.canam.com

PROFESSIONAL SEAL

PROJECT

DRAWING TITLE

PRELIMINARY SKETCH - ROOF PLAN

Initials

CONTRACT NUMBER	DRAWING NUMBER	DIVISION	REVISION
PJ NO.	EsMx401		