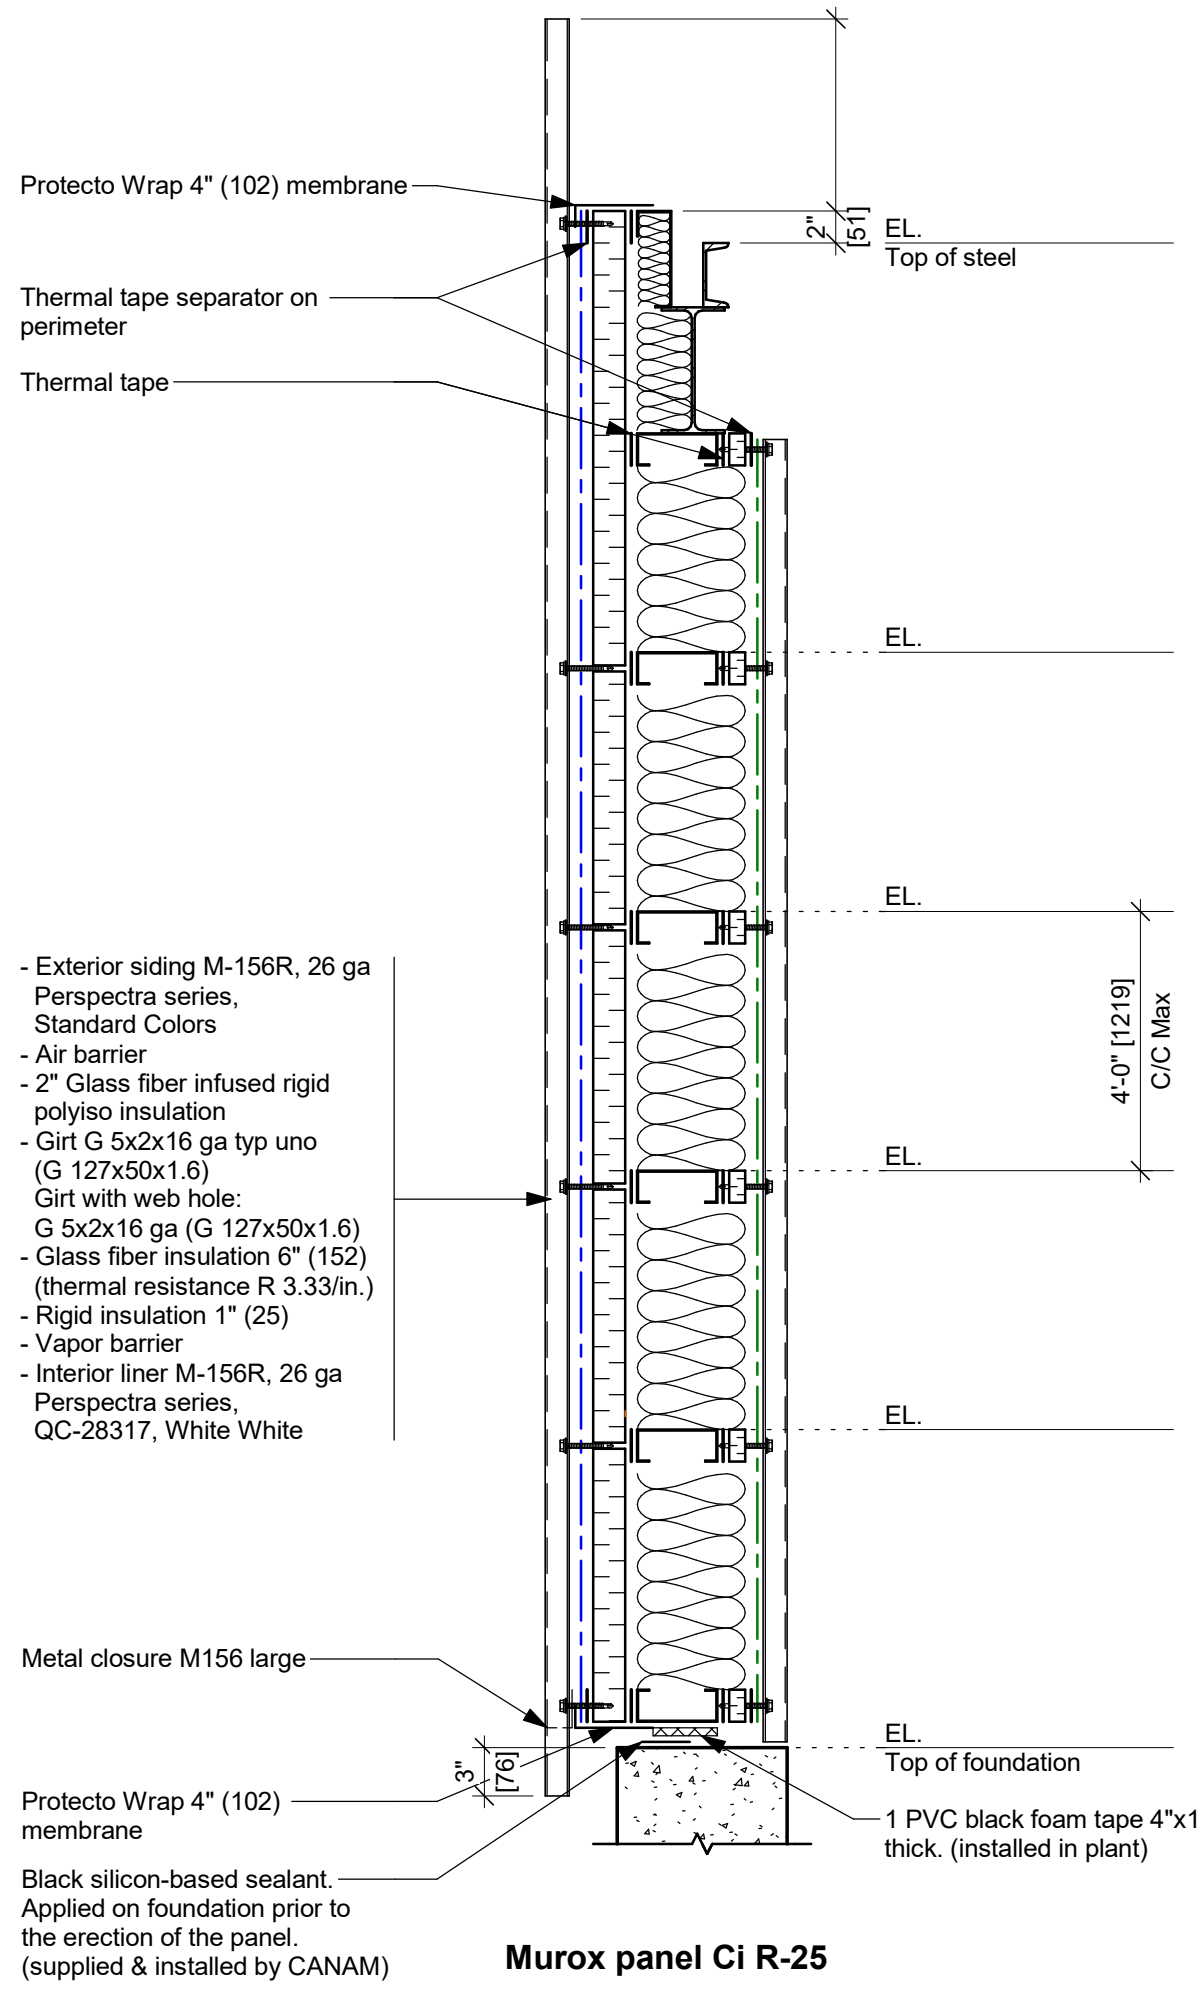


WINDOW SCHEDULE					
Identity	Qty.	Installation	Description	Size (Ext. of frame) (width & height)	Frame color
W1	18		Fixed aluminium window with thermal break and sealed glass + Low-E argon clear	8'-6" x 5'-0"	Aluminum Frame (no color)
Remarks					

OPENING SCHEDULE			
Total	Type	Tag	Remarks

DOOR SCHEDULE															
Door 18 ga.				Glass		Hardware									
Identity	Qty.	Installation	Insulation (R12)	Dimensions	Swing side	Width	Height	Steel frame 16 ga with thermal break	(3) Hinges non-rising removable pin	Door lock & latch set	Panic bar without outside trim 22EO	Panic bar with outside trim 23OL	Surface bolt Inactive door	Threshold	Astragal for inactive door
D1	5			36" x 84"		1'-10"	2'-6"								
D2	3			12x12'											
D3	3			10x12'											
D4	1			20x12'											
D5	1			72" x 84"		1'-10"	2'-6"								
D6	1			12x10'											
Remarks															

O/H & OPENING SCHEDULE			
Total	Type	Tag	Remarks
7	8'-6" x 9'-6"	OPN	
1	12'-8" x 9'-6"	OPN	
Total general: 8			



PRELIMINARY

NOT TO BE USED FOR CONSTRUCTION

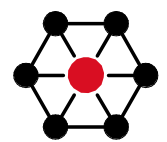
REVISION	DATE	DESCRIPTION	DESS	VER
----------	------	-------------	------	-----

PROJECT MANAGER				

DRAWING			
---------	--	--	--

DRAWN	INITIALE	DESIGNED	PROJECT ENGINEER	SCALE
				Comme indiqu�
CHECKED	CONSULTING ENGINEERS	ARCHITECTS	ENGINEER	DATE (yyyy/mm/aa)
			ARCHITECT	YYYY/MM/DD

CUSTOMER:				
-----------	--	--	--	--

**CANAM**

11505, 1re Avenue, bureau 500, Saint-Georges Beaus 
Chabec, Canada, Q5Y 7G5
Phone : (418) 228-8031
Toll free : (877) 499-6049
www.canam.com

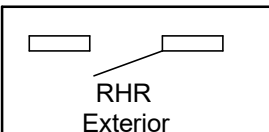
PROFESSIONAL SEAL				
-------------------	--	--	--	--

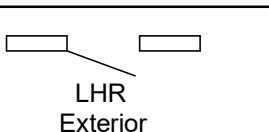
PROJECT				
---------	--	--	--	--

DRAWING TITLE				
---------------	--	--	--	--

PRELIMINARY SKETCH - ELEVATION,
WALL SECTION AND SCHEDULES

CONTRACT NUMBER	DRAWING NUMBER	DIVISION	REVISION
PJ NO.	EsMx502		

**RHR**
Exterior
KIT #1

**LHR**
Exterior
KIT #2

**LHR**
RHR-A
Exterior
KIT #3

**LHR-A**
RHR
Exterior
KIT #4

Swing designation is always determined by insert key

Supplier's standard hardware:
- Hinges : Stanley FBS175 4.5" x 4"
- Exit device : Von Duprin 22 x 689 with outside trim 230L
- Permanent cylinder : Schlage 20031C 626
- Door closure : LCN 1261 680
- Head and jamb seal : Unique 1650
- Bottom seal : Unique DS4
- Threshold : See the remarks in "Door schedule"