




MEZZANINE
 CLEAR HEIGHT UNDER MEZZ. : 10'-0"
 TOP OF STEEL MEZZ. : 111'-8"
 CLEAR HEIGHT ABOVE MEZZ. : 10'-0"

MEZZANINE
 D.L. : 70 psf
 L.L. : 100 psf
 Δ L/360

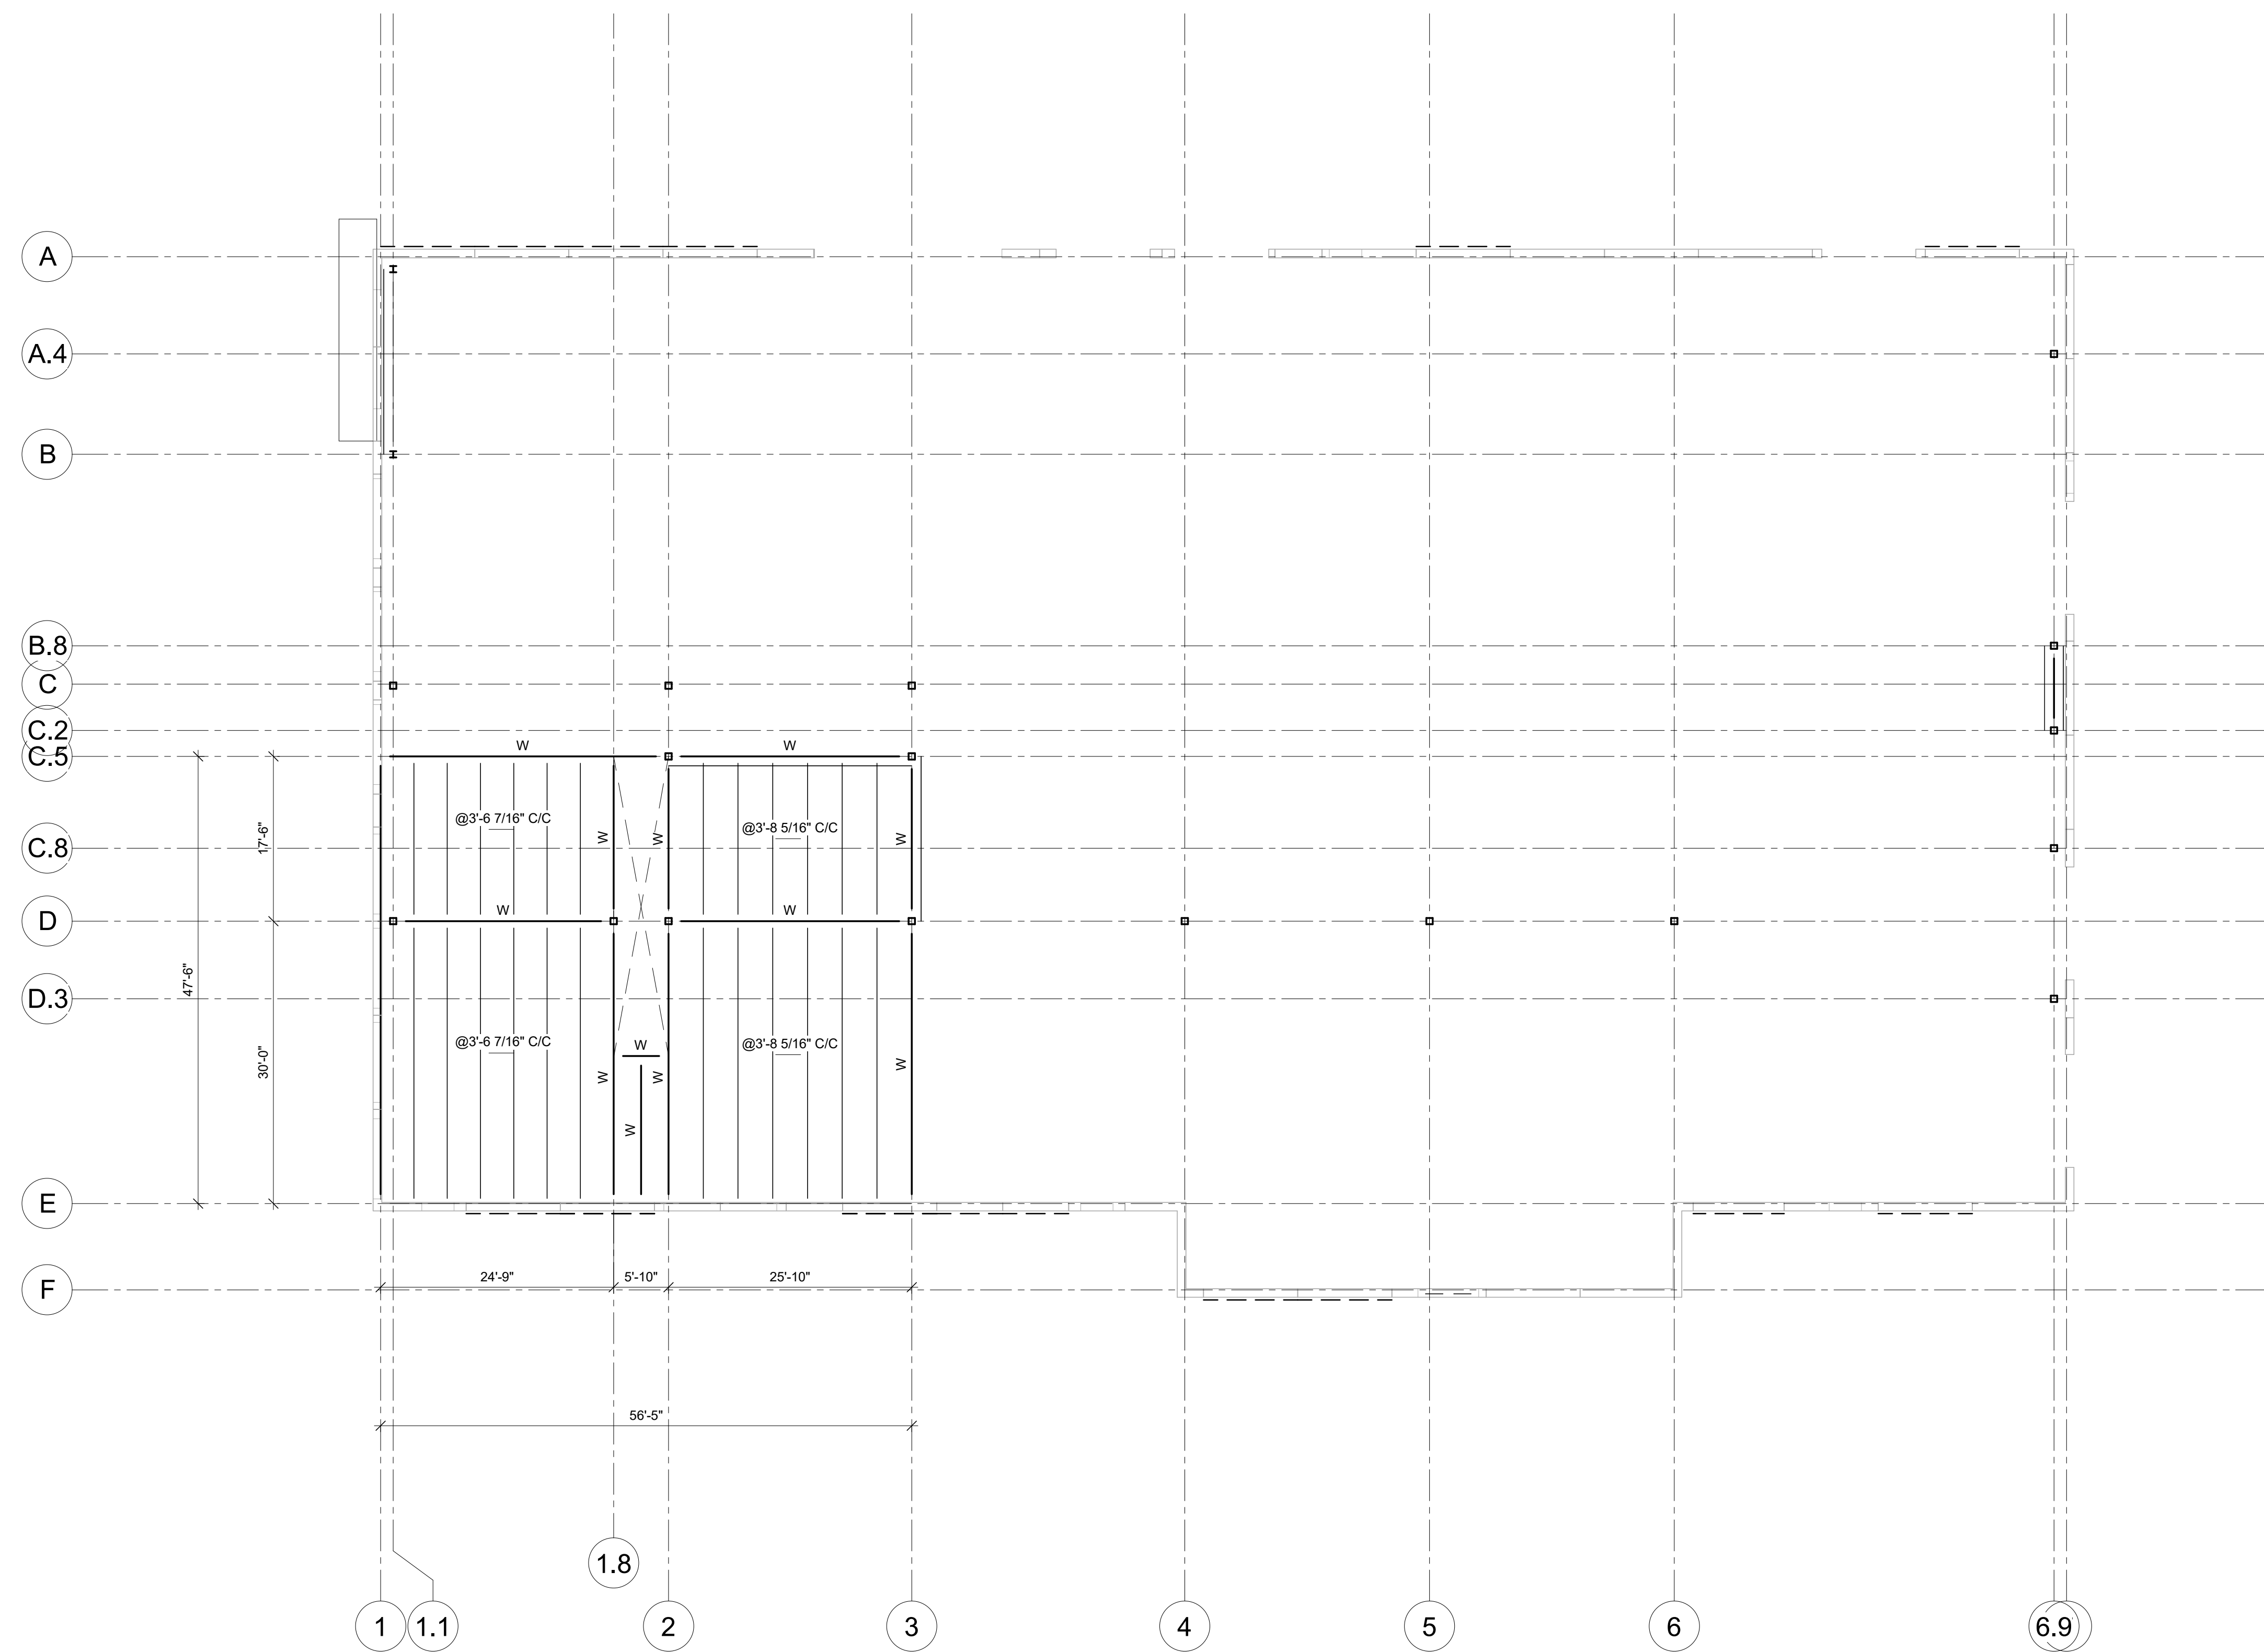

MEZZANINE PLAN
 3/32" = 1'-0"