




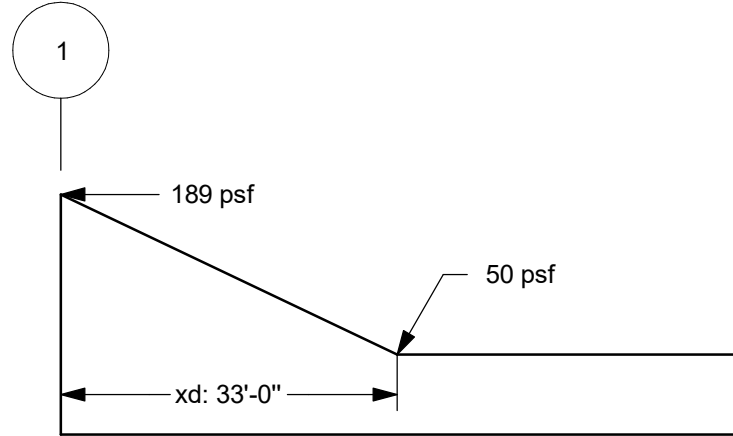

SNOW LOAD ACCUMULATION

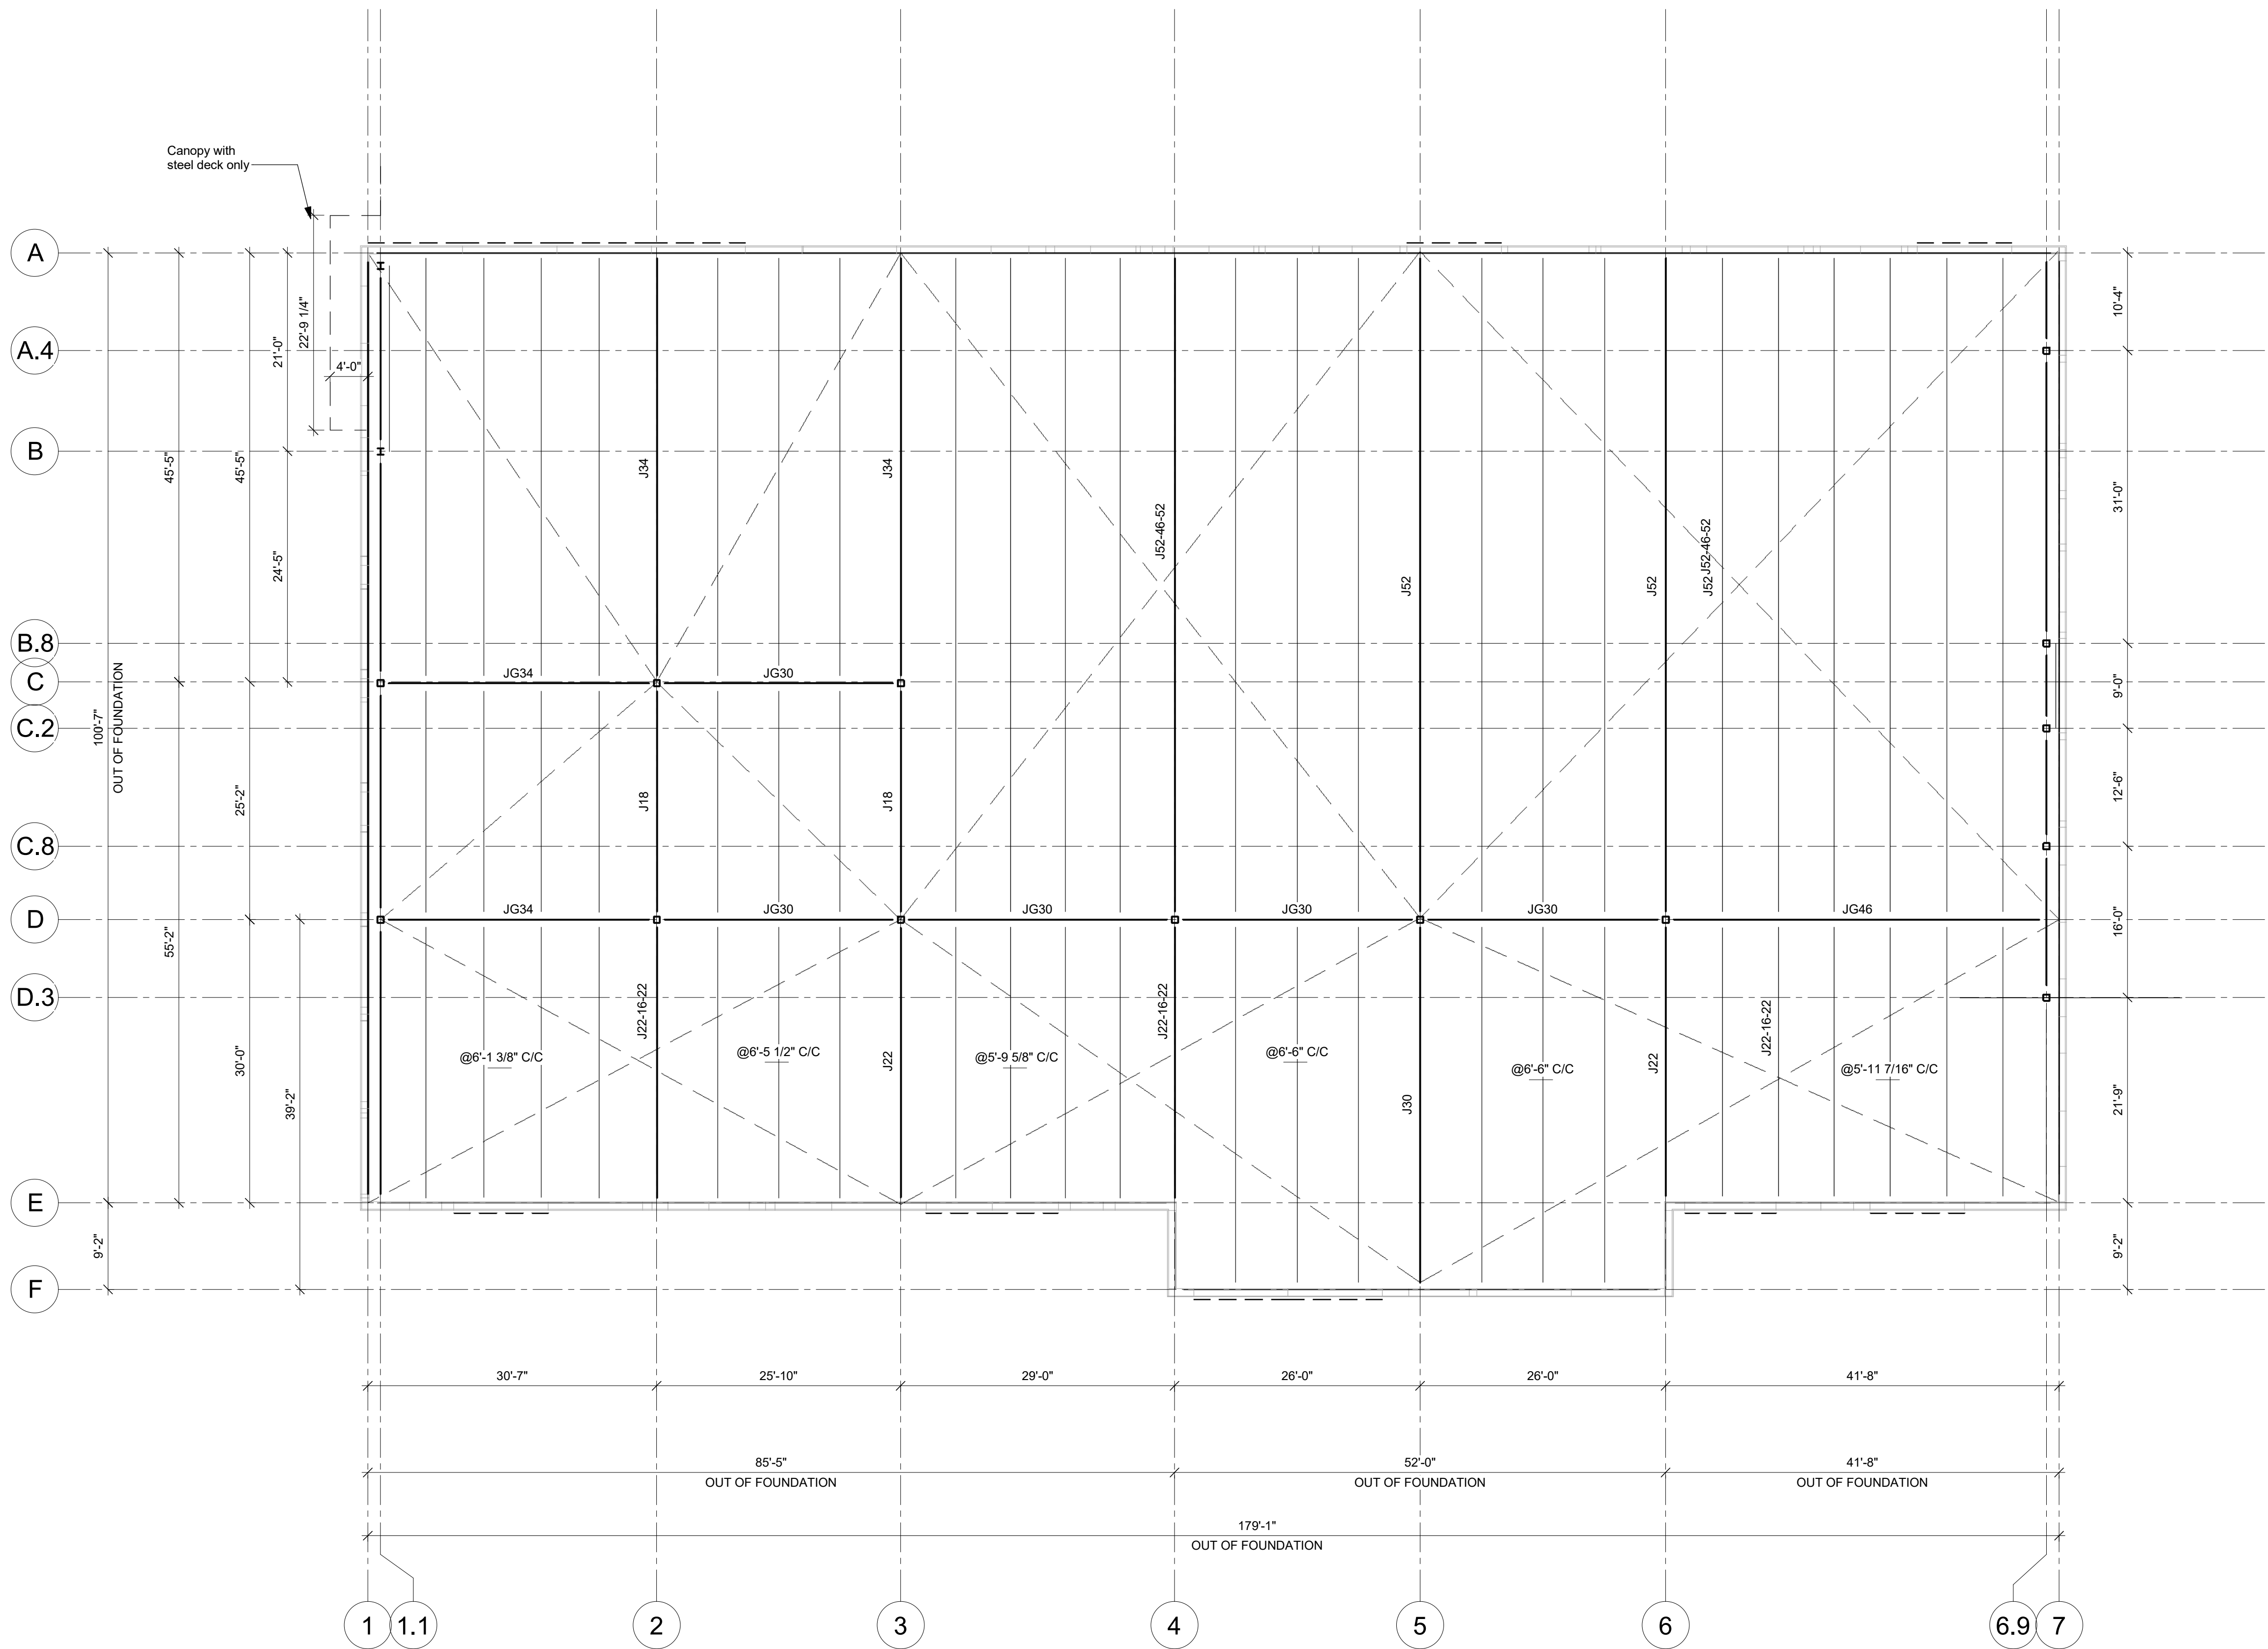

ZONE 1 : 17.7 psf
ZONE 2 : 22.0 psf
a : 10'-0"

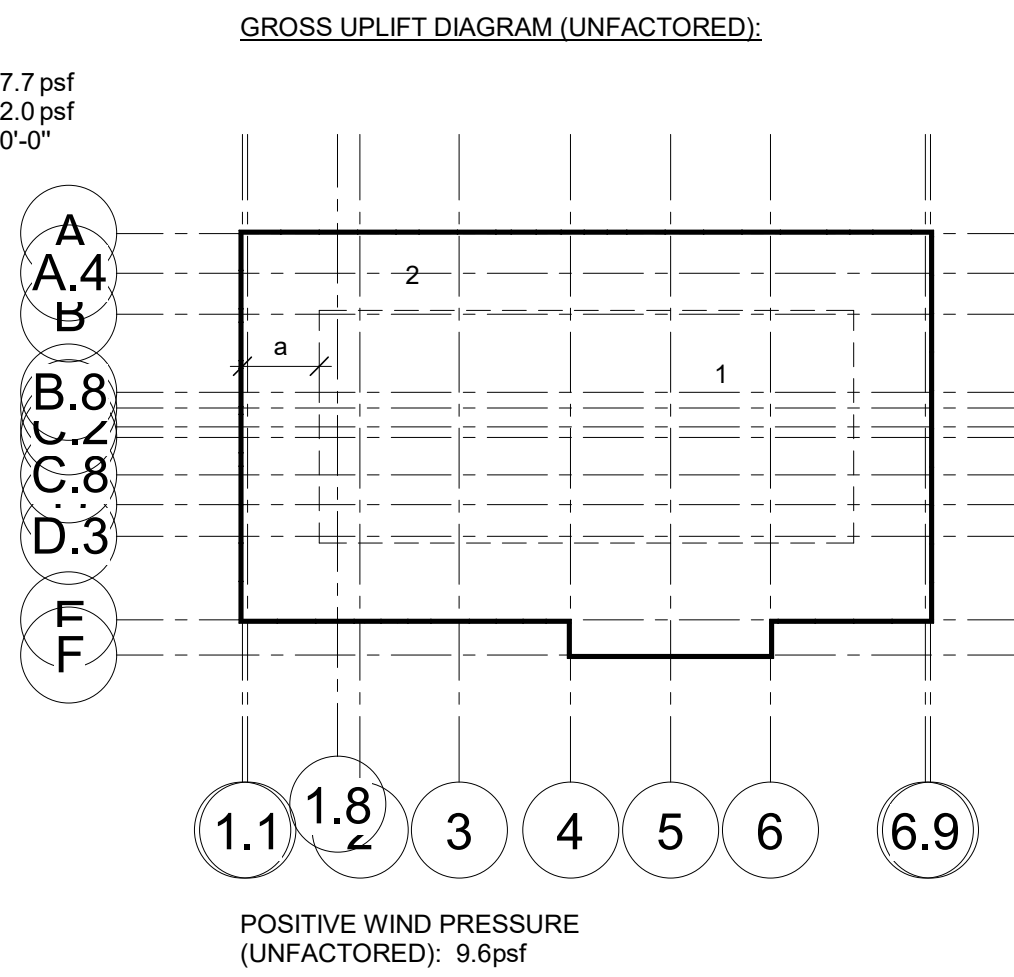

ROOF PLAN
1" = 10'-0"