

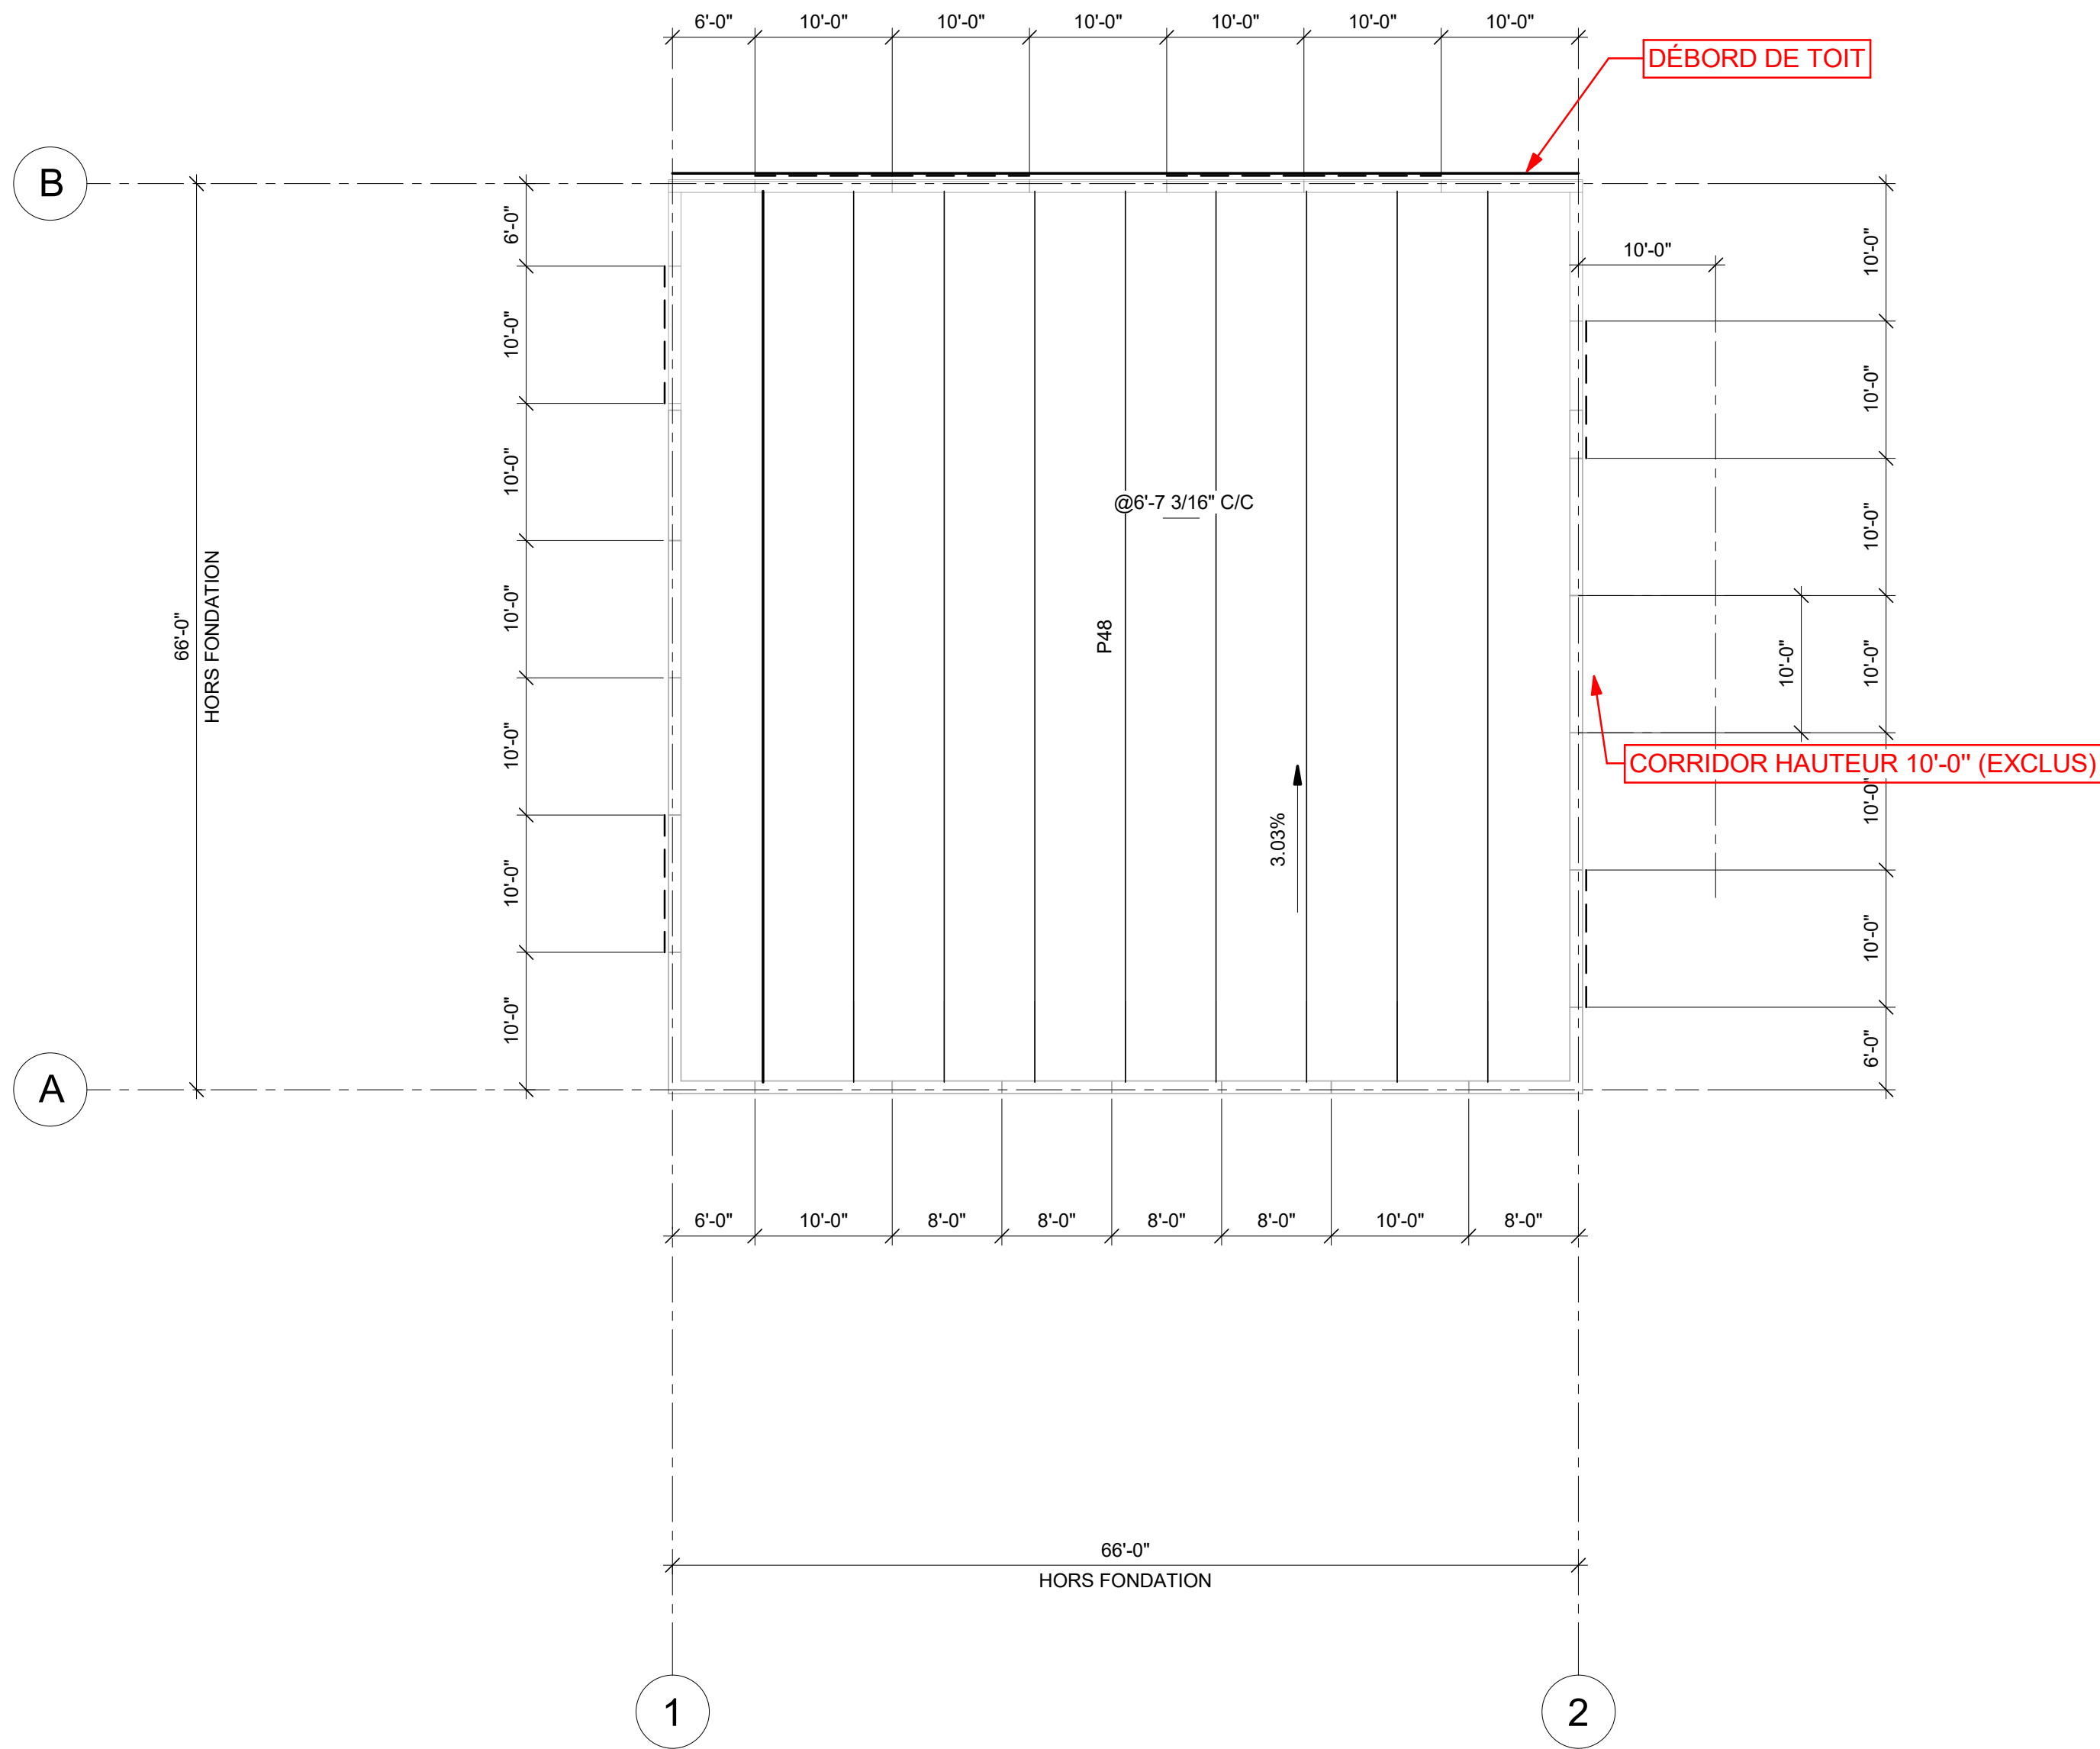


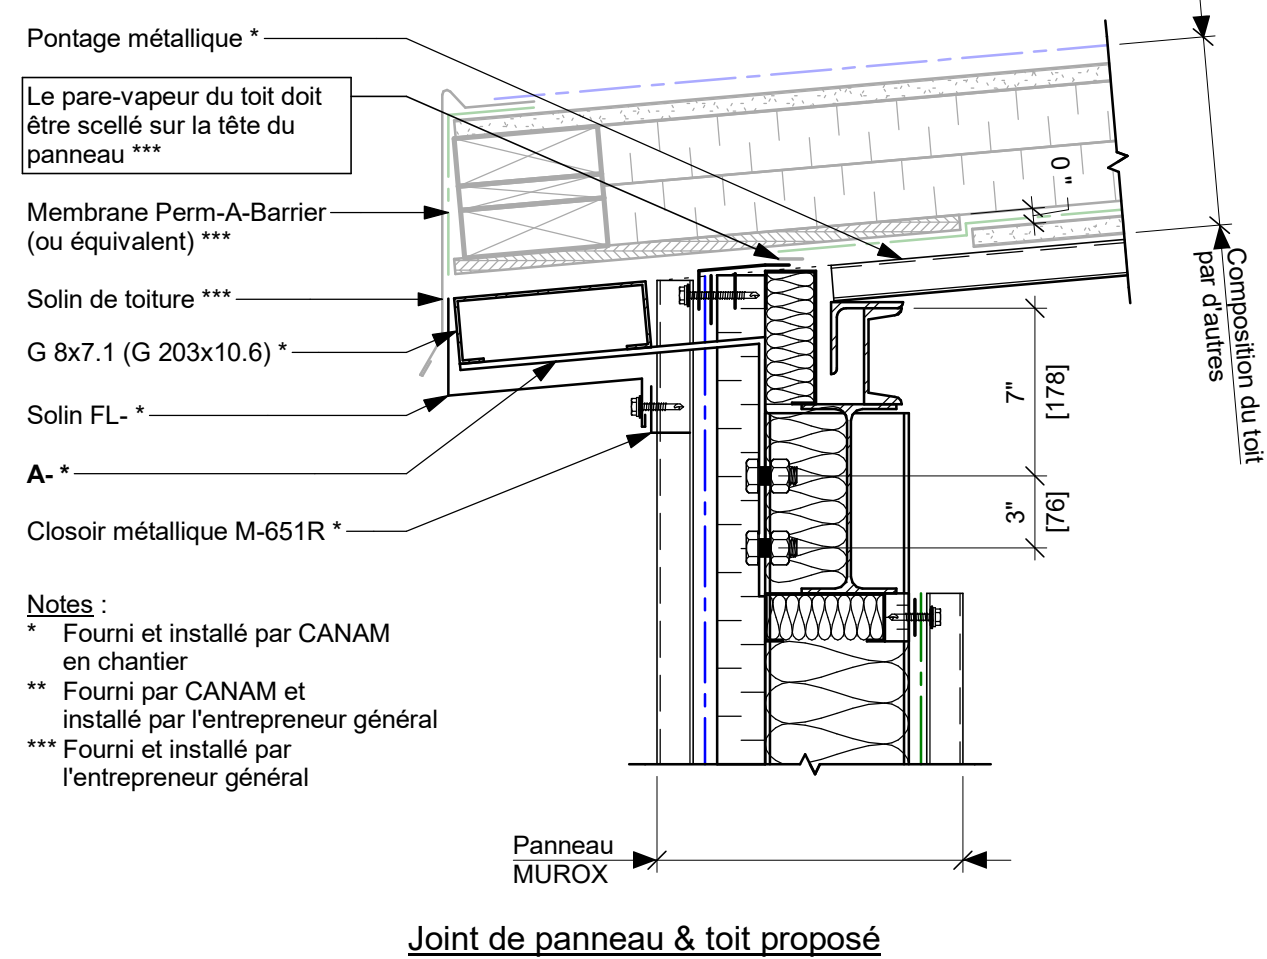

PLAN DE TOIT
3/32" = 1'-0"

DIAGRAMME DE SOULÈVEMENT BRUT (NON PONDÉRÉ)

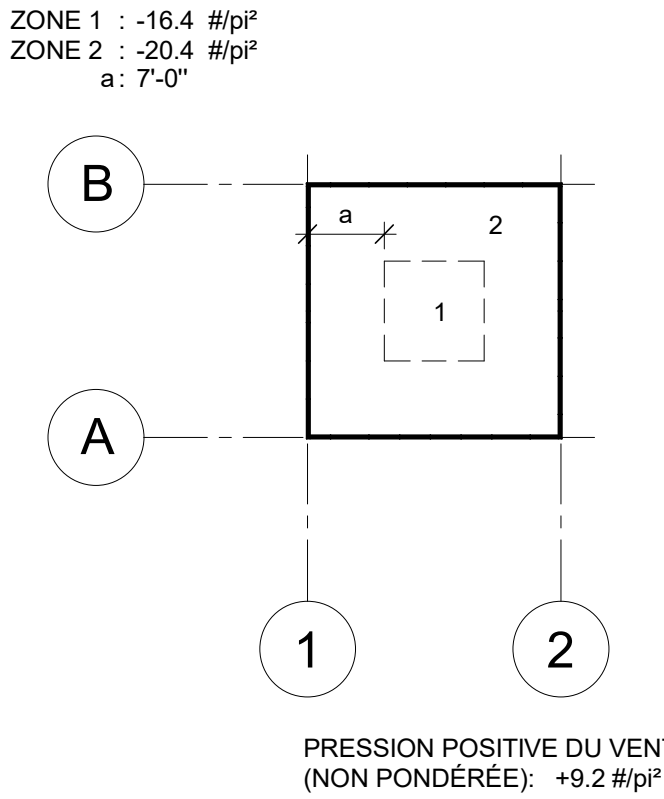

NOTE POUR LE CONTRACTEUR/ÉRECTEUR:
IL EST STRICTEMENT DÉFENDU DE MODIFIER, COPIER, REPRODUIRE OU DE DISTRIBUER CES DESSINS OU QUELQUES REPRÉSENTATIONS DE CES DESSINS, PAR TOUTES SOURCES DE MÉDIA INCLUANT ÉLECTRONIQUEMENT, SANS L'APPROBATION ÉCRITE DE GROUPE CANAM INC.

TOIT

DESSUS DE PILASTRE DDP : 98'-0"
DESSUS DE PILASTRE : 99'-0"
DESSUS DE LA DALLE : 100'-0"
DESSUS DE LA FONDATION : 101'-0"
HAUTEUR LIBRE : 21'-0"
DESSUS D'ACIER AXE A : 127'-0"
DESSUS D'ACIER AXE B : 125'-0"

CHARGES

C.M. : 18 lbs/pi²
Coll. : 5 lbs/pi²
Ss : 54.31 lbs/pi²
Sr : 8.36 lbs/pi²
Cb x Cw : 0.8
C.V. au toit : 0 lbs/pi²
Is : 1.0
Charge de neige au toit : 51.8 lbs/pi²
Iw : 1.0
Vent q= 1/50 : 8.36 lbs/pi²

Seisme (Sol de classe D assumé)

Ie : 1.0
Ss (0.2) : 0.774
Ss (0.5) : 0.571
Ss (1.0) : 0.342
Ss (2.0) : 0.163
Ss (5.0) : 0.0455
Ss (10.0) : 0.0142
PCA : 0.468
PGV : 0.407

• Code Applicable : Code National du Bâtiment du Canada
Code du bâtiment du Québec, dernières éditions adoptées
Code de Pratique Standard ICCA.

• Type de sol assumé : classe D

• NOTE :
1. Si toutefois la catégorie d'emplacement devient E ou F selon le rapport géotechnique, le concept structural préliminaire (localisation et géométrie des contreventements, etc.) devra être validé et coordonné par l'ingénieur de Canam.


PRÉLIMINAIRE

NE DOIT PAS SERVIR À LA
CONSTRUCTION

REVISION	DATE	DESCRIPTION	DESS	VER.
GERANT DE PROJET				
-	-	-	-	-
-	-	-	-	-
-	-	-	-	-
-	-	-	-	-

DESSIN:			
DESSINE PAR	CONÇU PAR	INGÉNIEUR DU PROJET	ECHELLE:
Donald Piché			Comme indiqué
VÉRIFIÉ PAR	INGÉNIEURS CONSEILS / ARCHITECTES		DATE (jj/mm/aaaa) :
			26-01-2026

CLIENT: Construction Laval Aubin Ltée

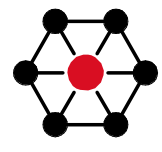**CANAM**

11505, 1re Avenue, bureau 500, Saint-Georges Beauce
Québec, Canada, G5Y 7X3
Téléphone : (418) 228-8031
Sans frais : (877) 499-6049
www.canam.com

SCEAU PROFESSIONNEL

PROJET

Garage First students
Mascouche, Québec

TITRE
CROQUIS PRÉLIMINAIRE - PLAN DE
TOIT

NUMÉRO CONTRAT P2026-012	NUMÉRO DESSIN EsMx401	DIVISION	RÉVISION

Initiales

