
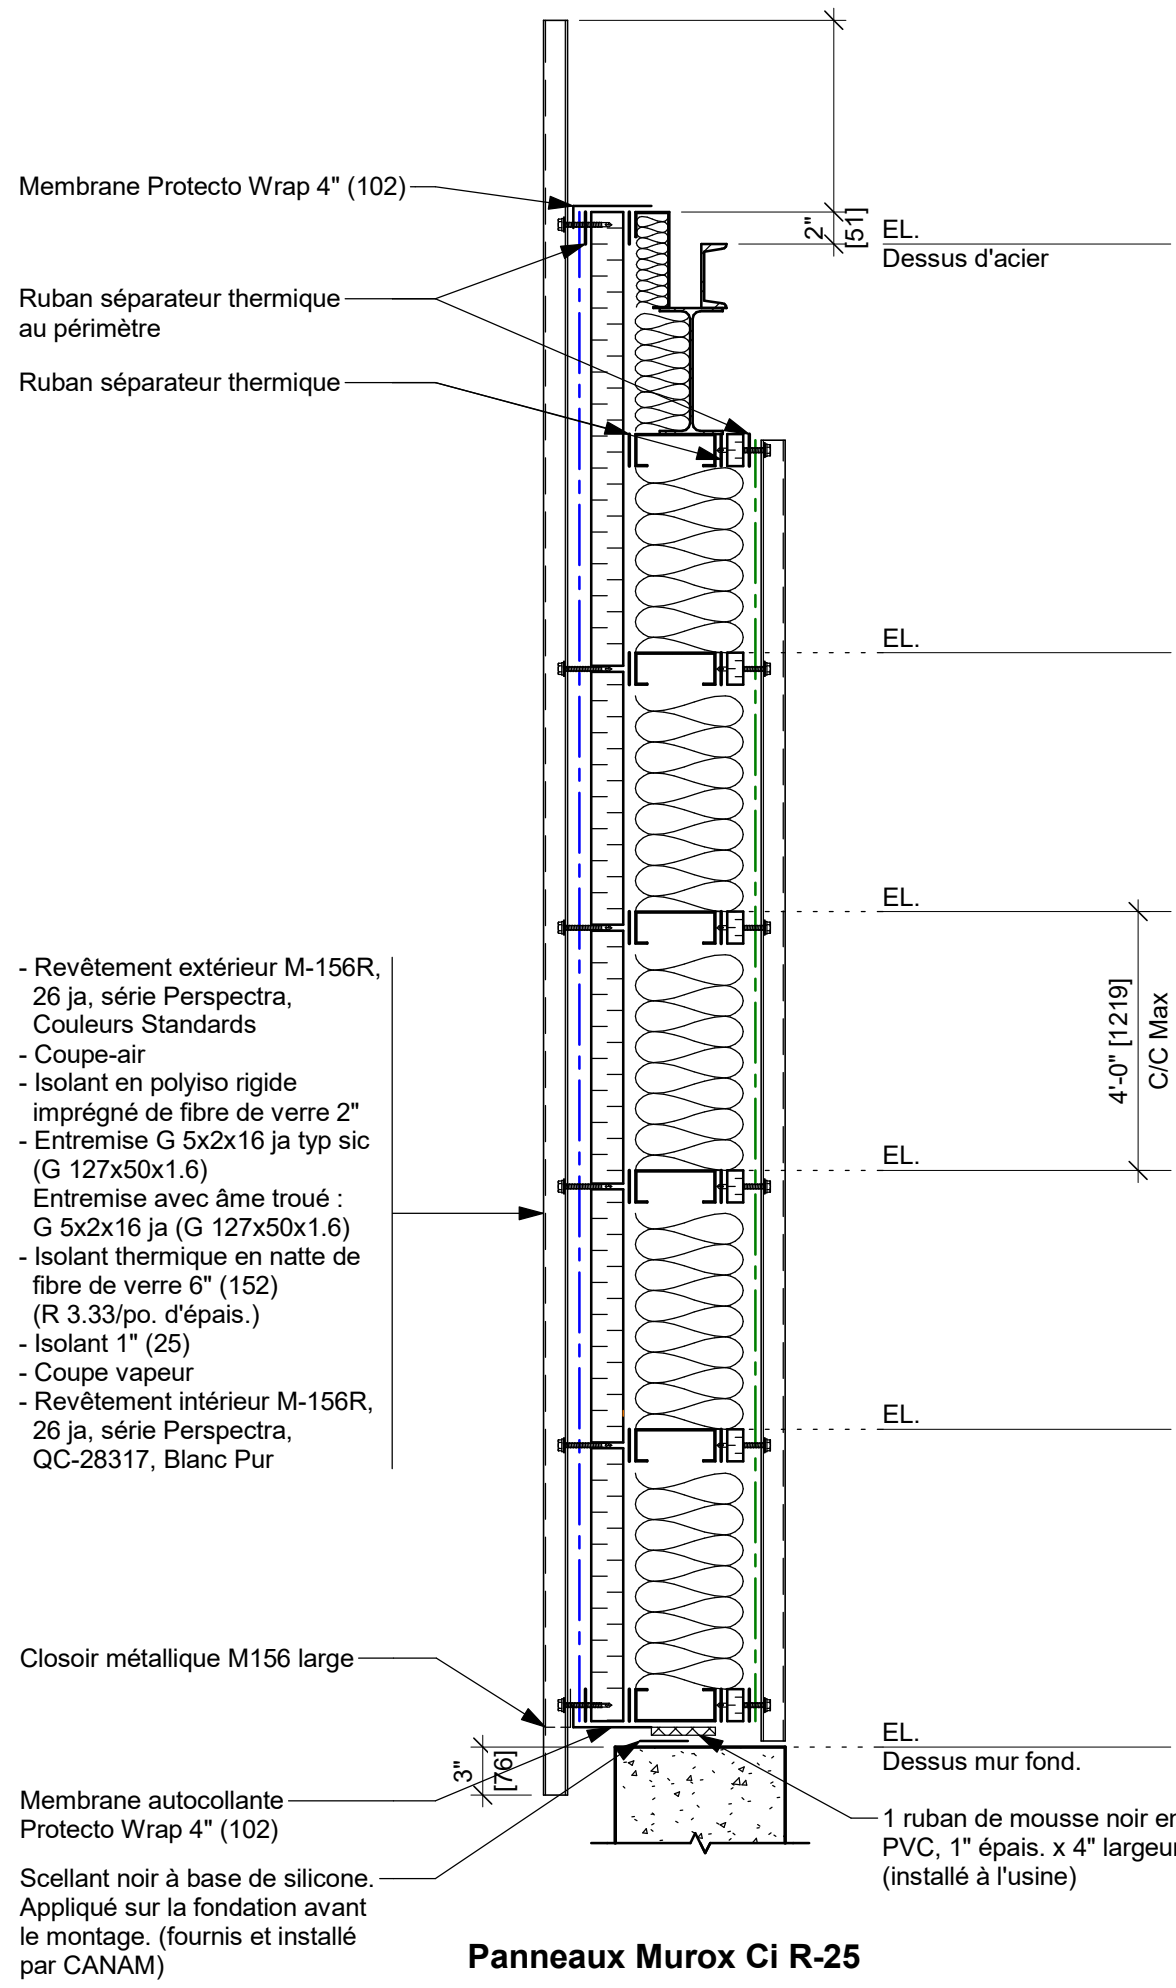
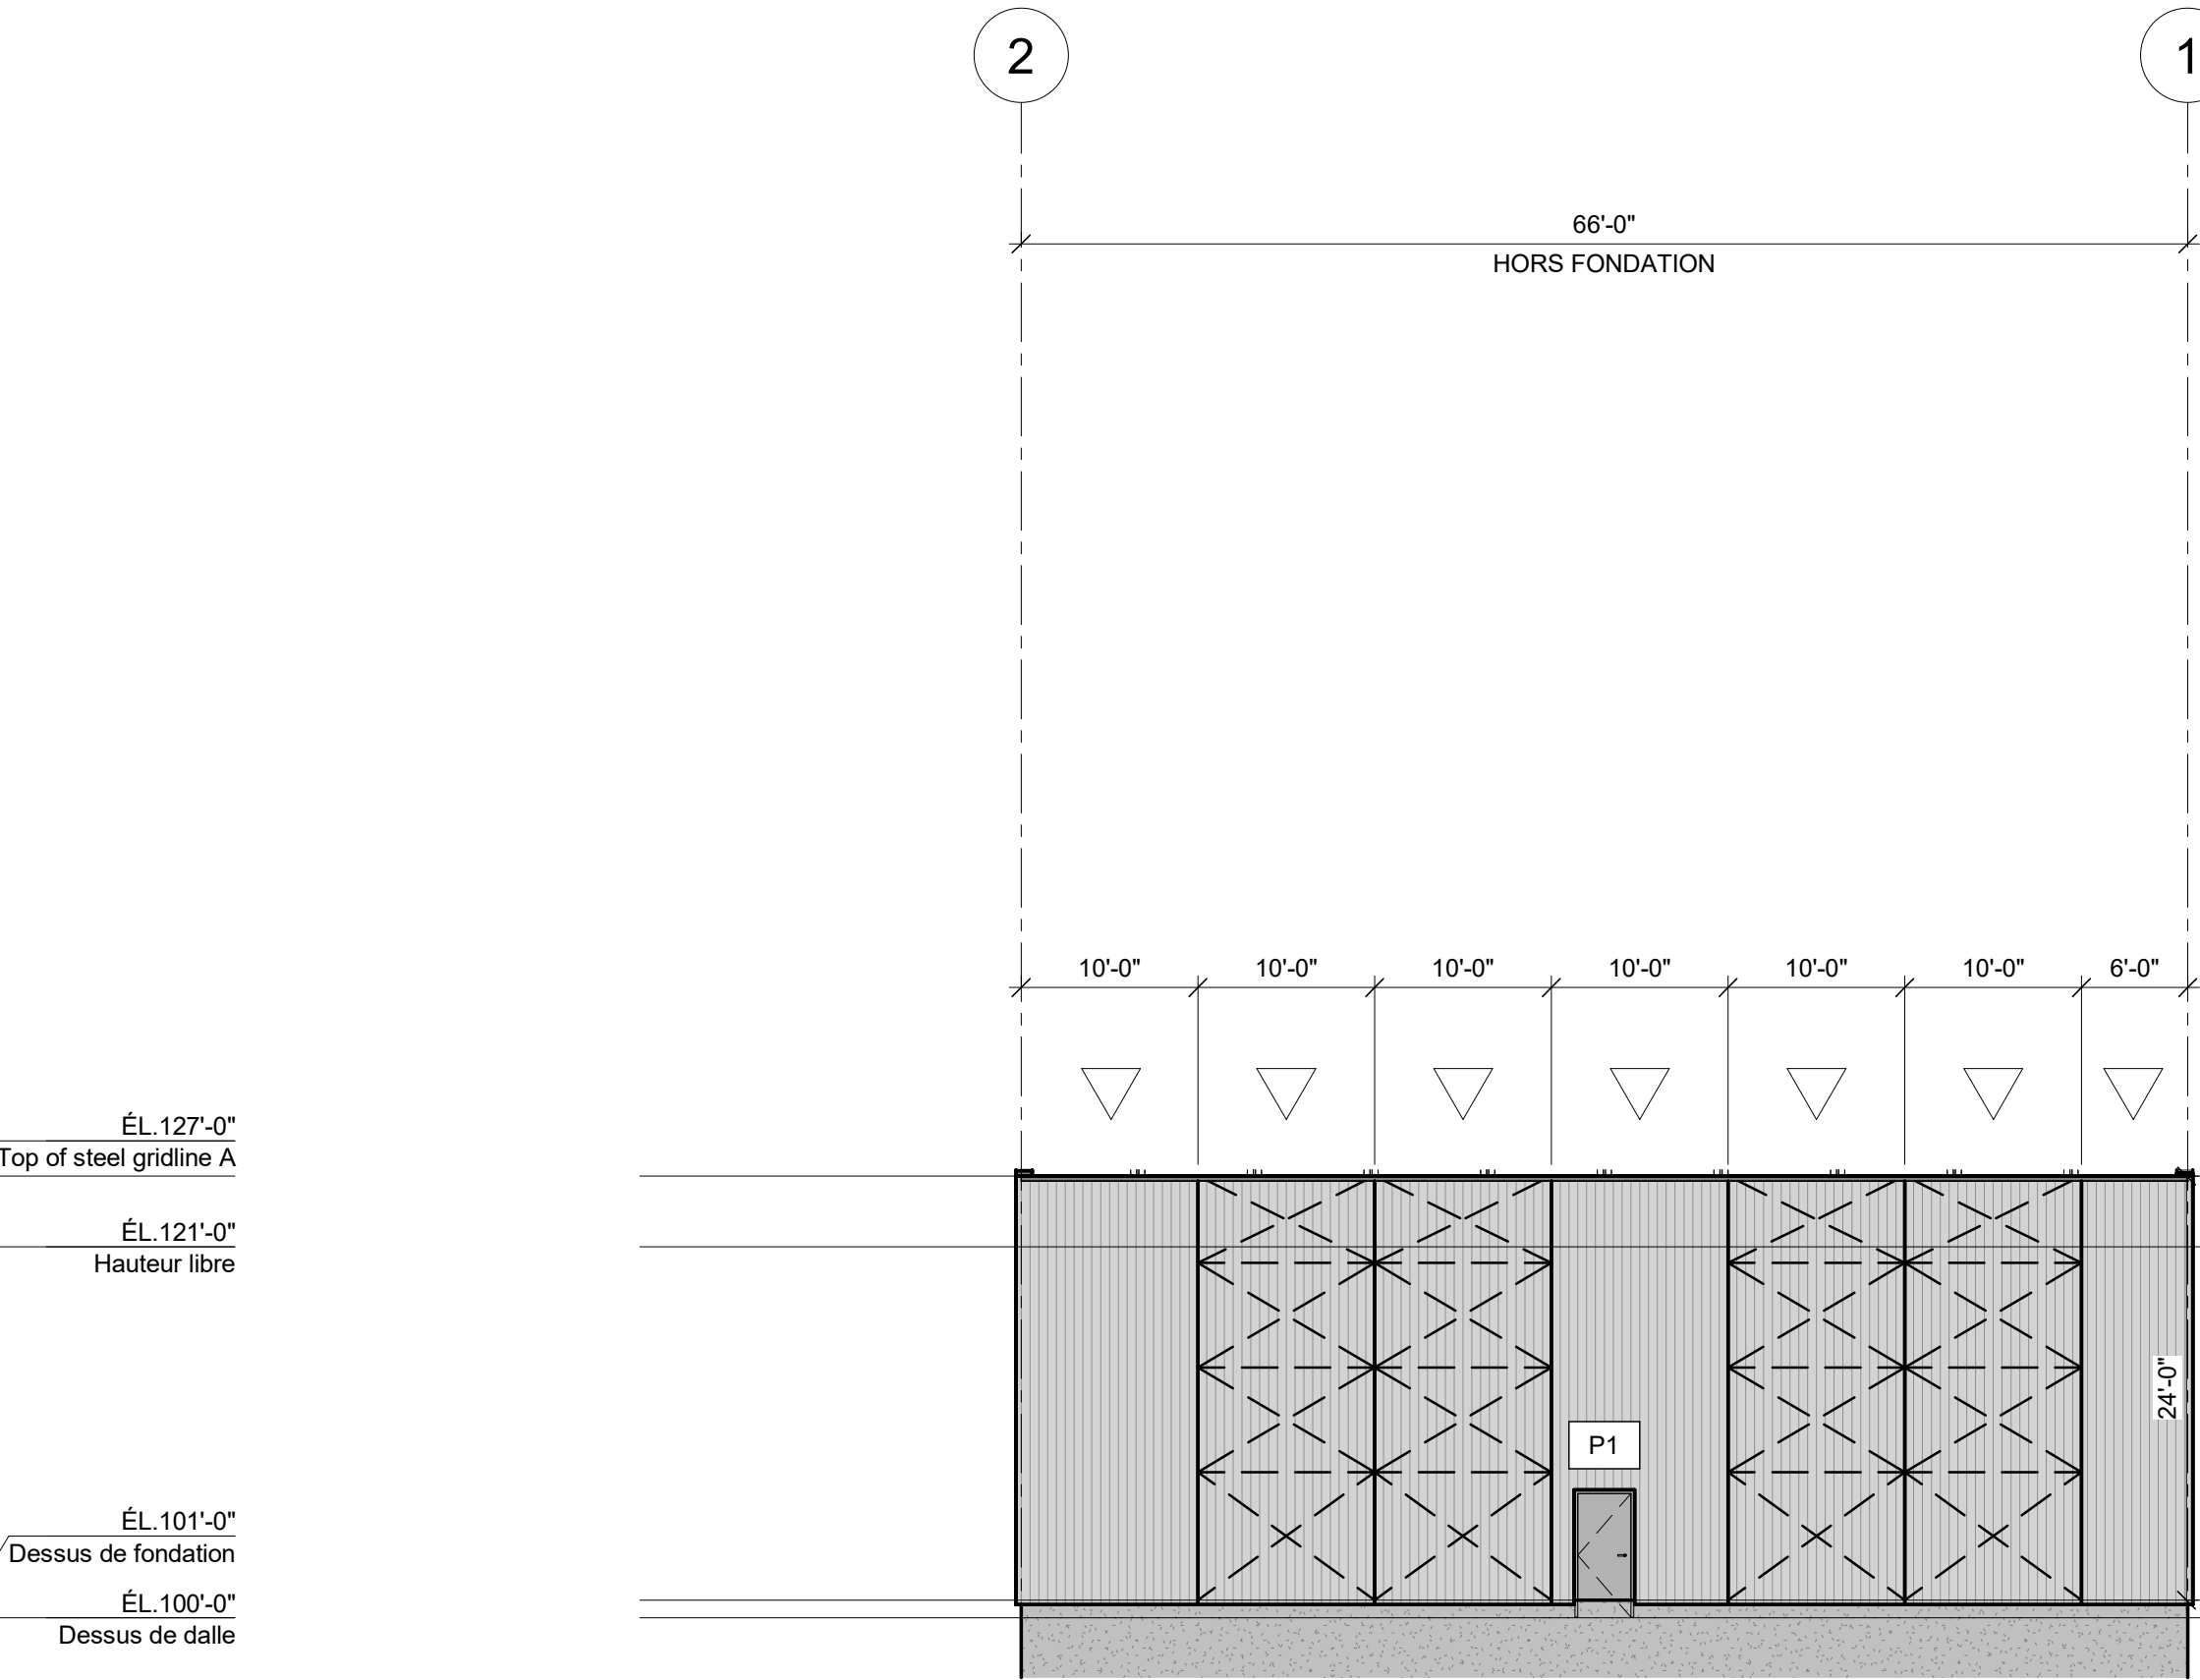
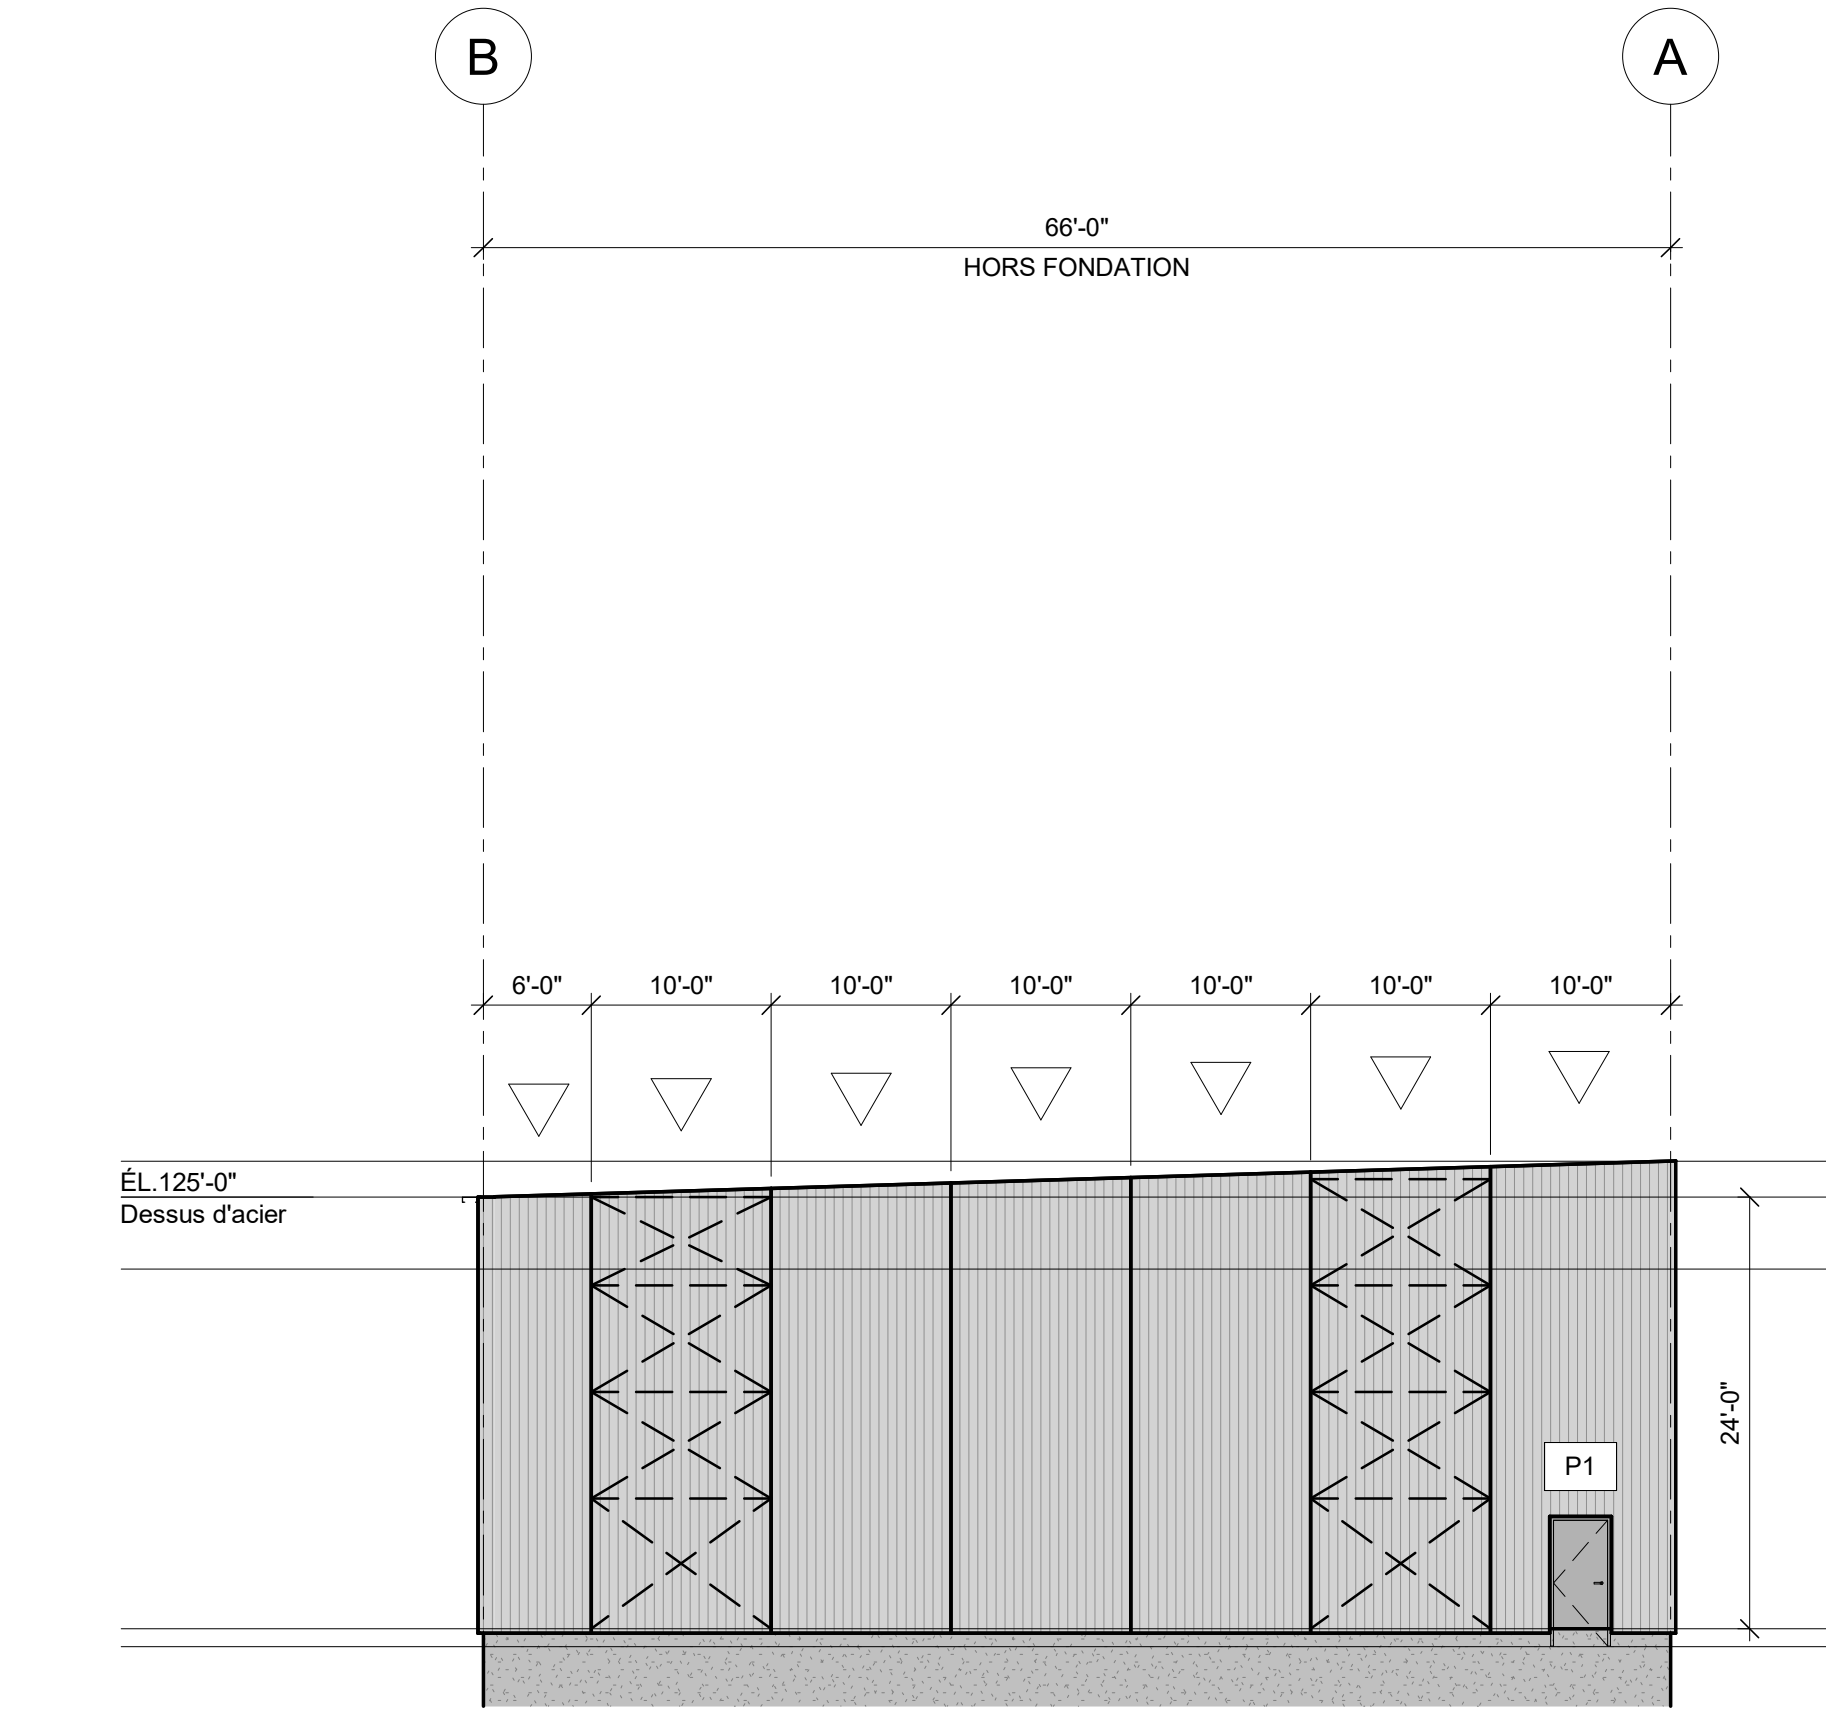
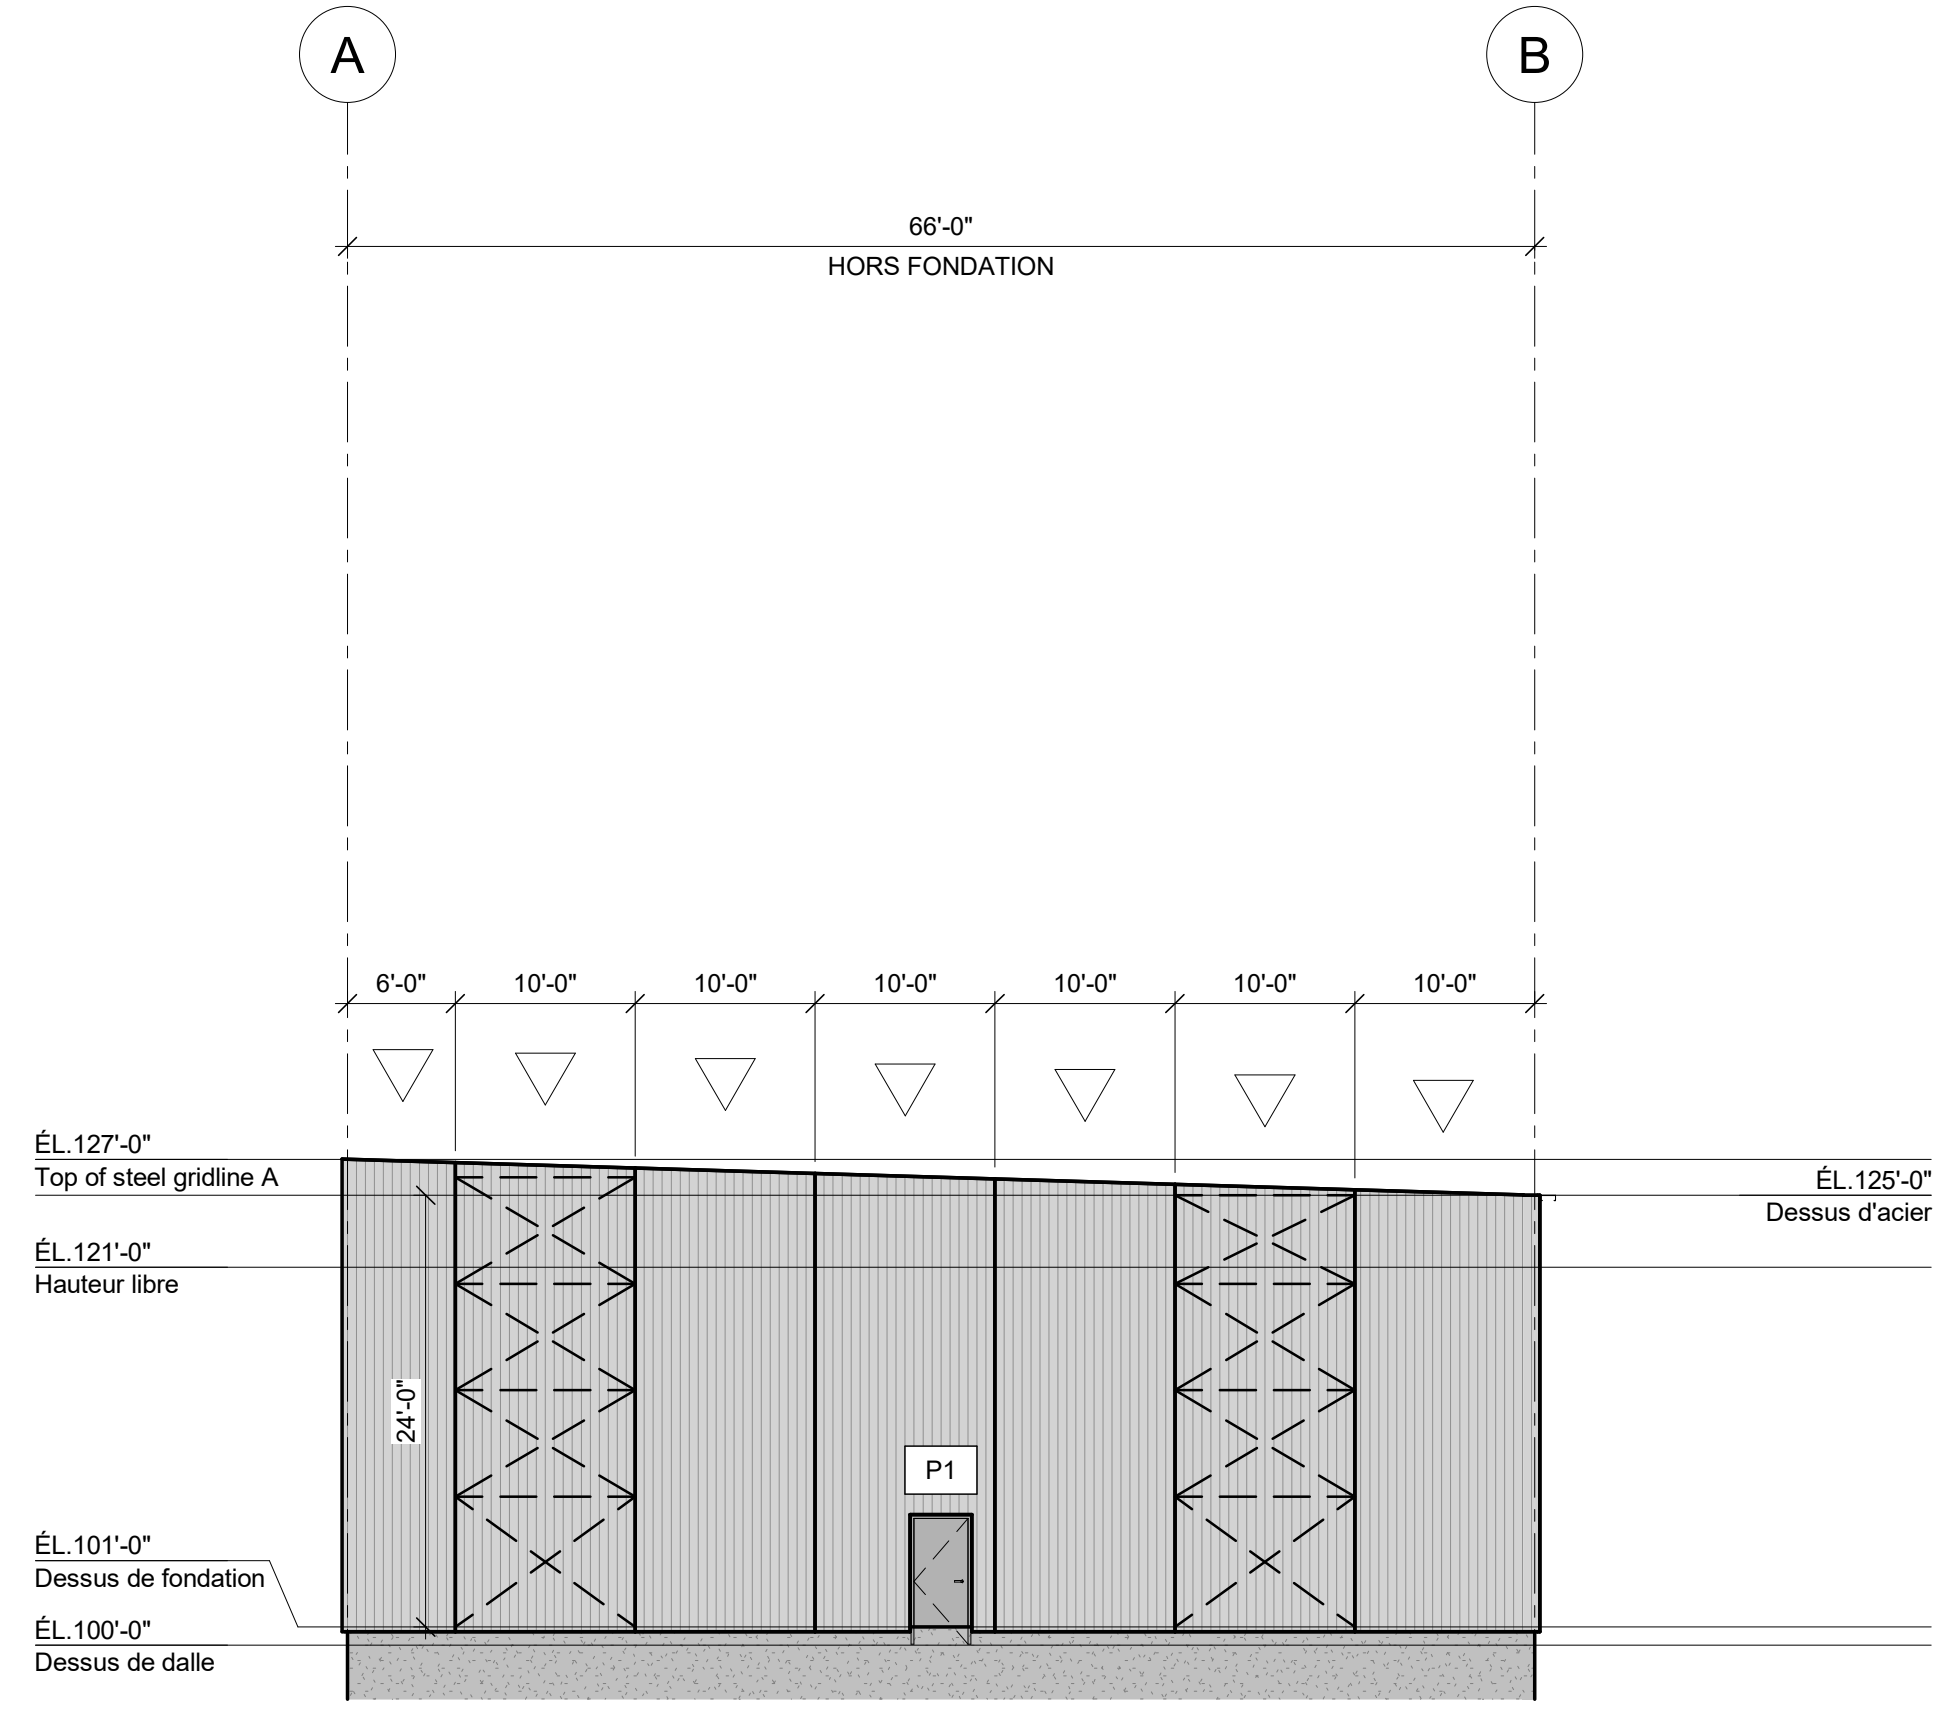


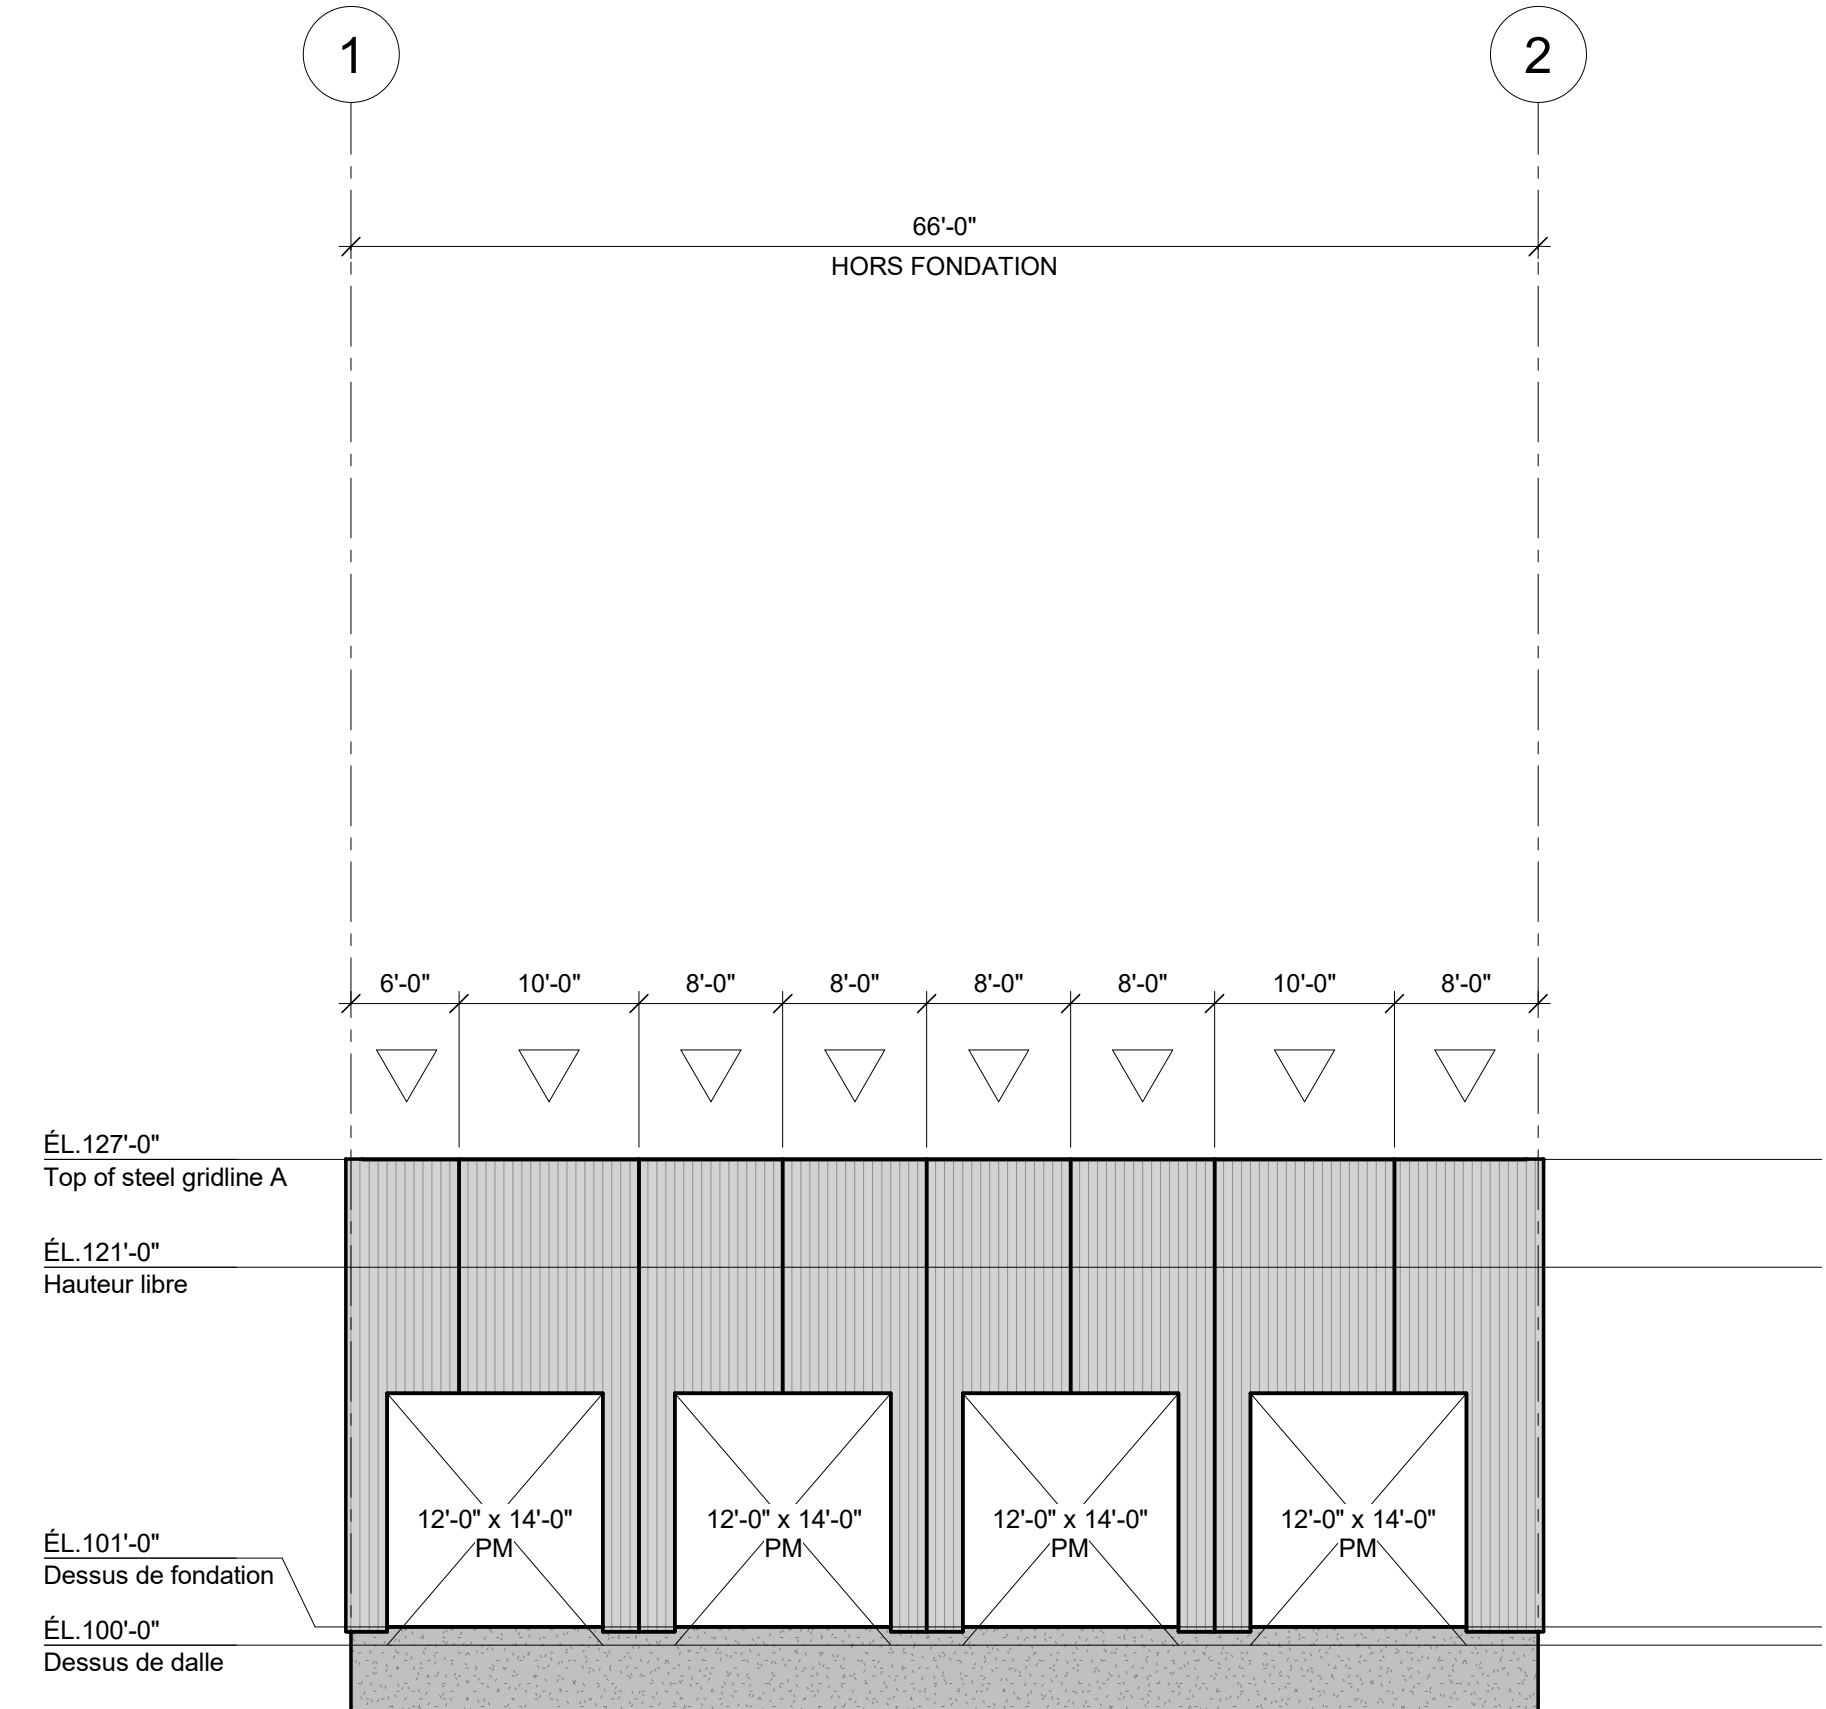

NOTE POUR LE CONTRACTEUR/ÉRECTEUR:

IL EST STRICTEMENT DÉFENDU DE MODIFIER, COPIER, REPRODUIRE OU DE DISTRIBUER CES DESSINS OU QUELQUES REPRÉSENTATIONS DE CES DESSINS, PAR TOUTES SOURCES DE MÉDIA INCLUANT ÉLECTRONIQUEMENT, SANS L'APPROBATION ÉCRITE DE GROUPE CANAM INC.

PRÉLIMINAIRE

NE DOIT PAS SERVIR À LA CONSTRUCTION

REVISION	DATE	DESCRIPTION	DESS	VER.
GERANT DE PROJET				
		-		
		-		
		-		
		-		
DESSIN:				
DESSINE PAR	CONÇU PAR	INGÉNIEUR DU PROJET	ECHELLE:	
Donald Piché			Comme indiqué	
VÉRIFIÉ PAR	INGÉNIEURS CONSEILS / ARCHITECTES		DATE (jj/mm/aaaa) :	
			26-01-2026	

CLIENT: Construction Laval Aubin Ltée



11505, 1re Avenue, bureau 500, Saint-Georges Beauce
Québec, Canada, G5Y 7X3
Téléphone : (418) 228-8031
Sans frais : (877) 499-5049
www.canam.com

SCEAU PROFESSIONNEL

PROJET

Garage First students
Mascouche, Québec

TITRE

CROQUIS PRÉLIMINAIRE - ÉLÉVATIONS

NUMÉRO CONTRAT
P2026-012

NUMÉRO DESSIN
EsMx501

DIVISION

REVISION

CÉDULE DES PORTES																			
Identifiant	Qté.	Porte 16 ja.			Sens ouv.	Vitrage		Cadre d'acier 16 ja., avec bris thermique	(3) Peintures @ tige fixe	Poignée seulement	Quincaillerie								Remarques
		Installation	Isolation (R12)	Dimensions		Largeur	Hauteur				Barre panique sans poignée ext. 22EO	Barre panique avec poignée ext. 230L	Verrou en surface (Porte inactive)	Seuil machiné	Astragale sur porte inactive	Ferme porte	Chaîne	Coupe -froid	
P1	3			3'-0" x 7'-0"															

CÉDULE DES P.M. ET DES OUVERTURES			
Total	Type	Tag	Commentaires
4	12'-0" x 14'-0"	PM	
Total général: 4			

Quincaillerie standard du fournisseur:

- Charnières : Stanley FBB179 4.5" x 4"
- Barre panique : Von Duprin 22 x 689 avec poignée extérieure 230L
- Cylindre permanent : Schlage 20001C 626
- Ferme-porte : LCN 1261 689
- Coupe-froid de tête et des montants : Unique 1650
- Coupe-froid du bas : Unique DS4
- Seuil : Voir la remarque dans la "Cédule de porte"

Initiales