


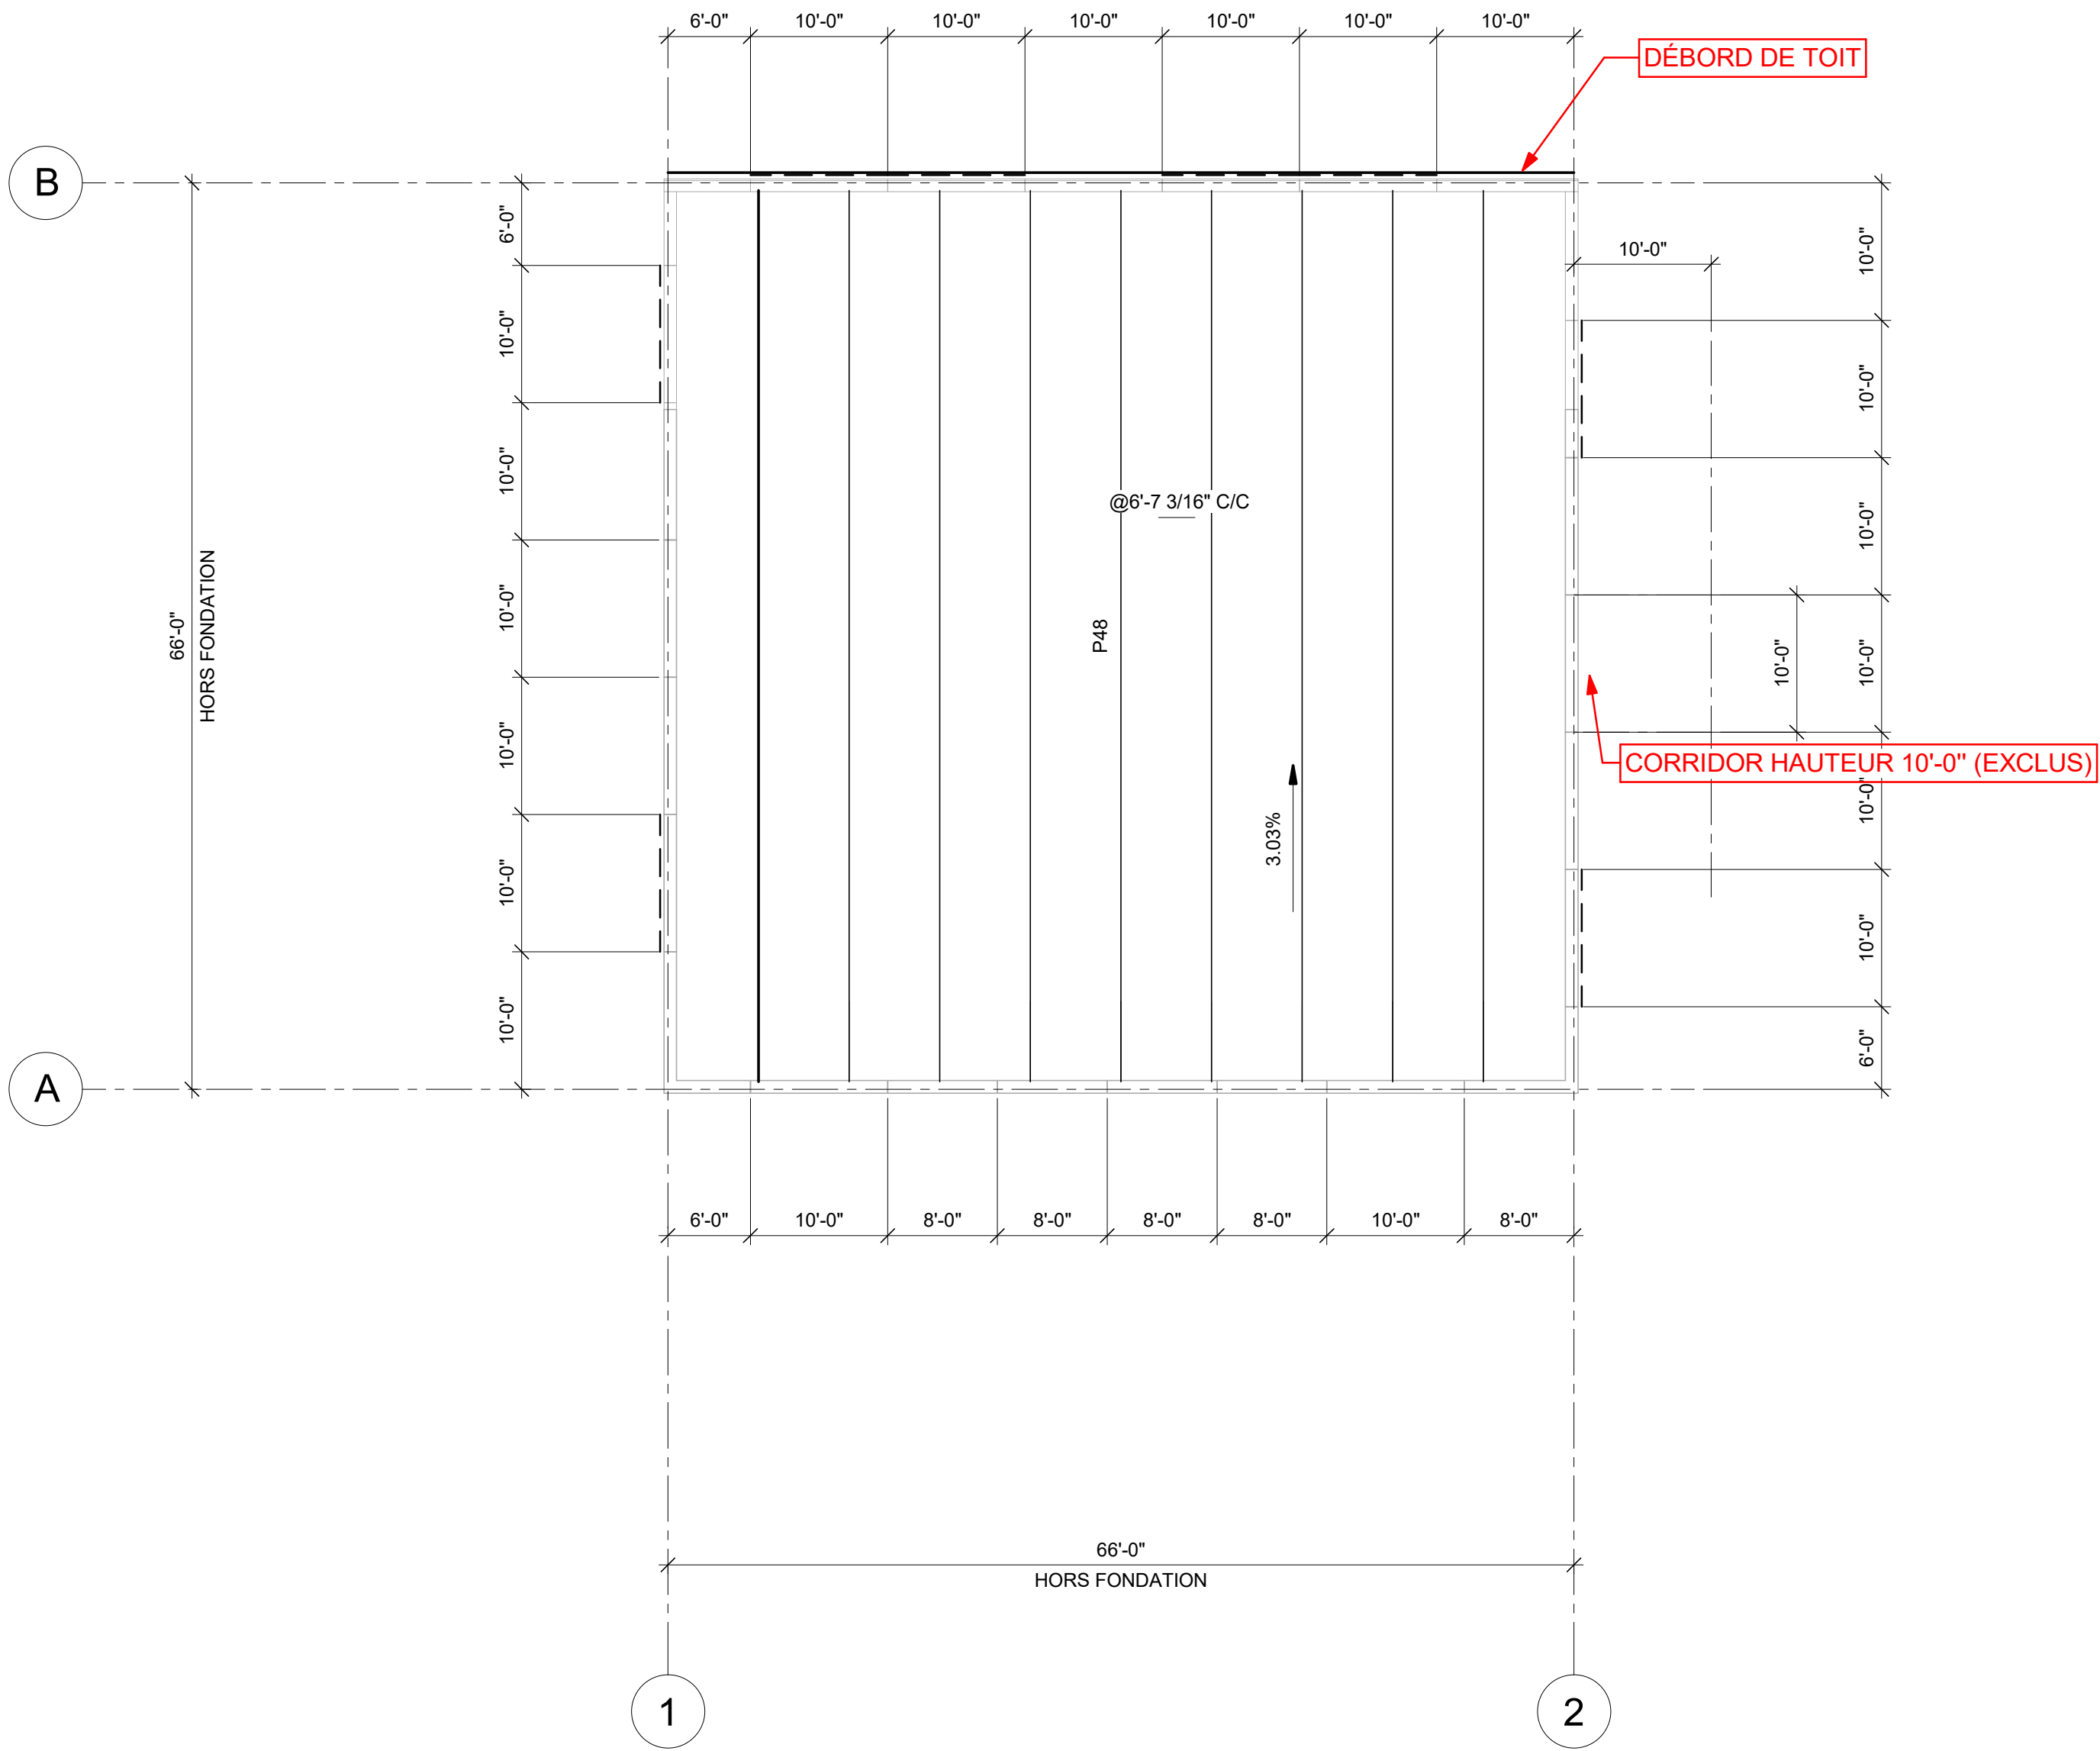

PLAN DE TOIT
3/32" = 1'-0"

DIAGRAMME DE SOULÈVEMENT BRUT (NON PONDÉRÉ)

