


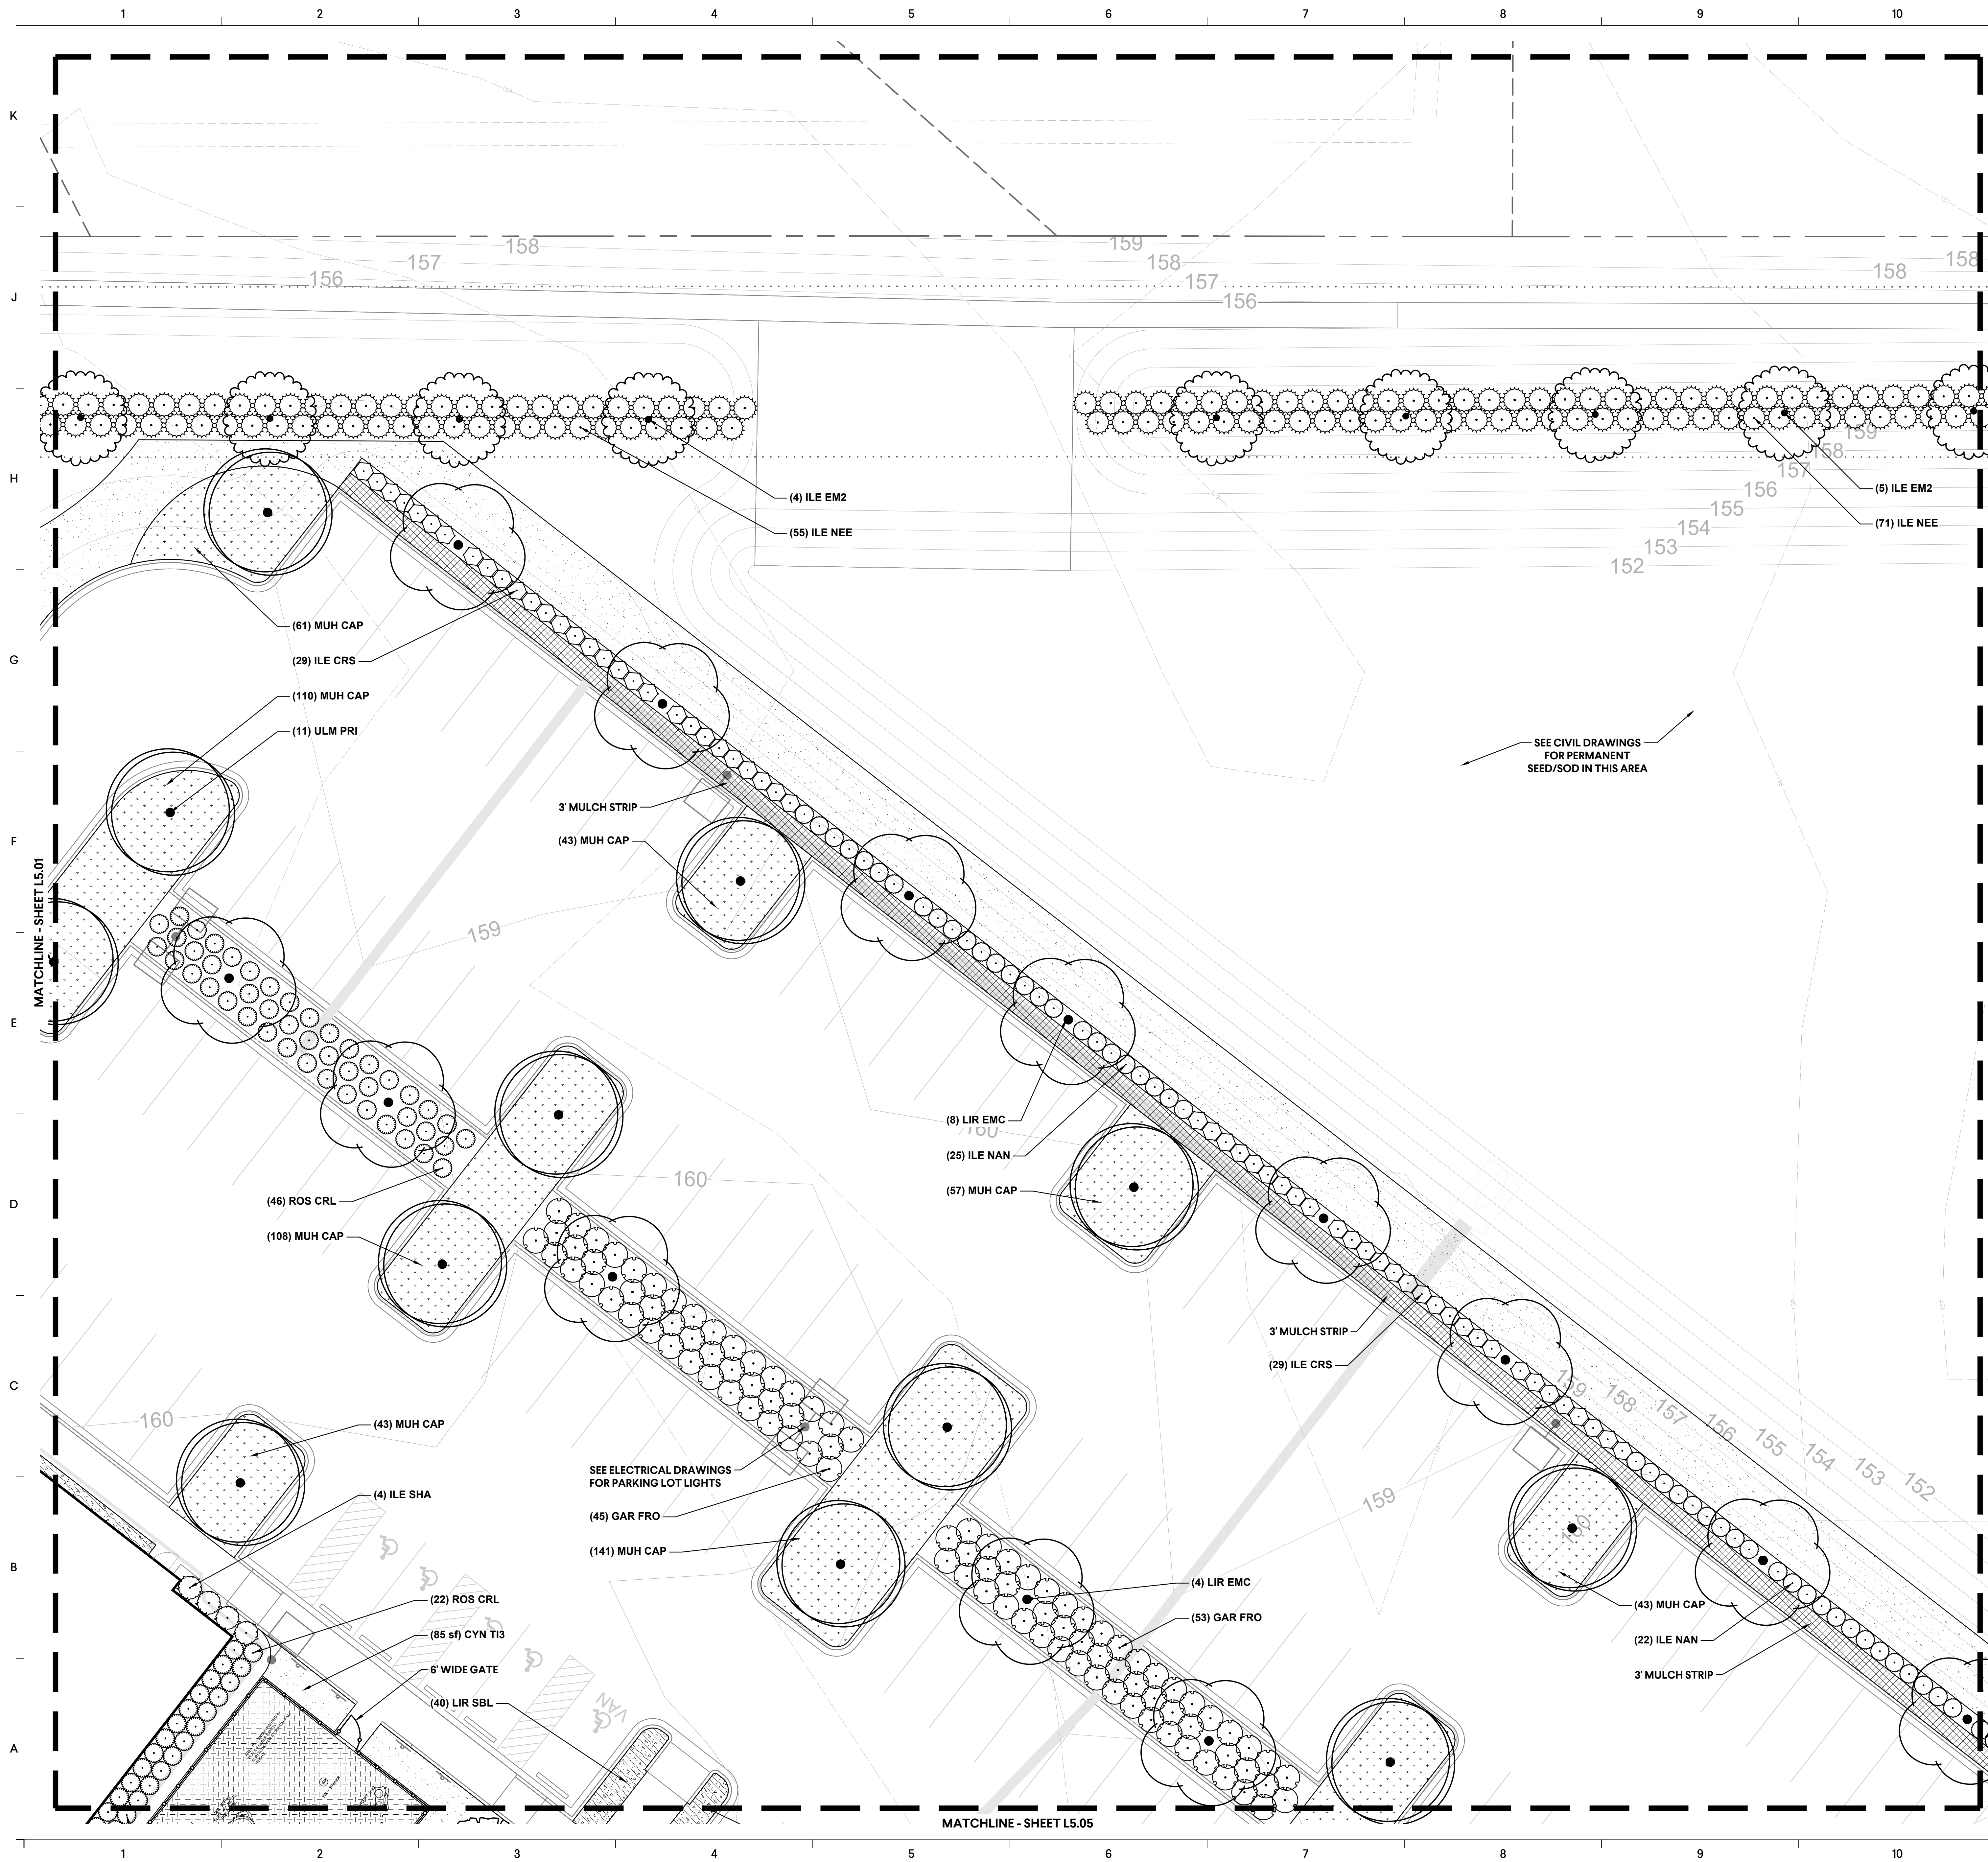

PLANT SCHEDULE

CODE	BOTANICAL NAME	COMMON NAME
TREES		
ILE LIB	ILEX X 'CONTY'	LIBERTY™ HOLLY
ILE EM2	ILEX X 'EMILY BRUNER'	EMILY BRUNER HOLLY
LAG WHI	LAGERSTROEMIA INDICA X FAURIEI 'NATCHEZ'	NATCHEZ CRAPE MYRTLE MULTI-TRUNK
LIR EMC	LIRIODENDRON TULIPIFERA 'JFS-OZ'	EMERALD CITY® TULIP POPLAR
PIS CHI	PISTACIA CHINENSIS	CHINESE PISTACHE
QOU NUT	QUERCUS NUTTALLII	NUTTALL OAK
ULM PRI	ULMUS AMERICANA 'PRINCETON'	PRINCETON AMERICAN ELM
SHRUBS		
GAR FRO	GARDENIA JASMINOIDES 'FROSTPROOF'	FROSTPROOF GARDENIA
ILE CRS	ILEX CORNUTA 'CARISSA'	CARISSA CHINESE HOLLY
ILE NEE	ILEX CORNUTA 'NEEDLEPOINT'	NEEDLEPOINT CHINESE HOLLY
ILE SHA	ILEX GLABRA 'SHAMROCK'	SHAMROCK INKBERRY HOLLY
ILE NAN	ILEX VOMITORIA 'NANA'	DWARF YAUPON HOLLY
ROS CRL	ROSA X 'CORAL DRIFT'	CORAL DRIFT ROSE
SHRUB AREAS		
MUH CAP	MUHLENBERGIA CAPILLARIS	WHITE AND PINK MUHLY GRASS
GROUND COVERS		
CYN T13	CYNODON DACTYLON 'TIF 419'	TIF 419 BERMUDA GRASS
LIR SBL	LIRIOPE MUSCARI 'SUPER BLUE'	SUPER BLUE LILYTURF
MULCH	PINE STRAW MULCH	PINE STRAW MULCH

NOTES

1. CONTRACTOR SHALL HAND WATER ALL PLANT MATERIAL AND SOD DURING CONSTRUCTION UNTIL SUBSTANTIAL COMPLETION HAS BEEN ACHIEVED.
2. CONTRACTOR IS TO PROVIDE ALL TREES WITH SLOW RELEASE WATER BAGS. WATER BAGS ARE TO BE CONSISTENTLY FILLED DURING CONSTRUCTION SO TREES WILL HAVE WATER AT ALL TIMES, AT THE TIME OF SUBSTANTIAL COMPLETION. CONTRACTOR IS TO MEET ON SITE WITH OWNER OR OWNER'S MAINTENANCE REPRESENTATIVE TO REVIEW THE INSTRUCTIONS AND THE SCHEDULING OF REFILLING THE BAGS. CONTRACTOR SHALL REFILL BAGS AT THE TIME OF SUBSTANTIAL COMPLETION.
3. ALL DISTURBED AREAS NOT COVERED BY PLANT MATERIAL OR SOD ARE TO BE SEED ACCORDING TO CIVIL DRAWINGS. SEE C-DRAWINGS FOR MORE INFORMATION.

SITE FURNISHINGS:

- (3) PETOSKEY TRASH RECEPTACLES BY LANDSCAPE FORMS OR APPROVED EQUAL. 1 TO BE PLACED AT FRONT DOOR, 1 AT SIDE DOOR AND 1 ON THE BACK PATIO.
- (4) LARCHMONT PICNIC TABLES BY COUNTRY CASUAL OR APPROVED EQUAL. ALL FOUR TABLES ARE TO BE LOCATED ON THE BACK PATIO.
- (5) 6' LONG WELLSPRING BENCHES BY LANDSCAPE FORMS OR APPROVED EQUAL. BOTH BENCHES ARE TO BE LOCATED ON THE BACK PATIO.
- SEE 02870 SITE FURNISHING SPECIFICATION FOR DETAILS. ALL SITE FURNISHING LOCATIONS TO BE APPROVED BY OWNER'S REPRESENTATIVE PRIOR TO INSTALLATION.

