


CADD FILE NAME:pw\1\218.sil.bz:Toronto_Transportation\Documents\Eglinton Crosstown LRT\Execution\43_Struct\Design\430D_DRAWINGS\8010 Mt. Dennis\RTI-ECL801_SS_SECT_BPLT_02

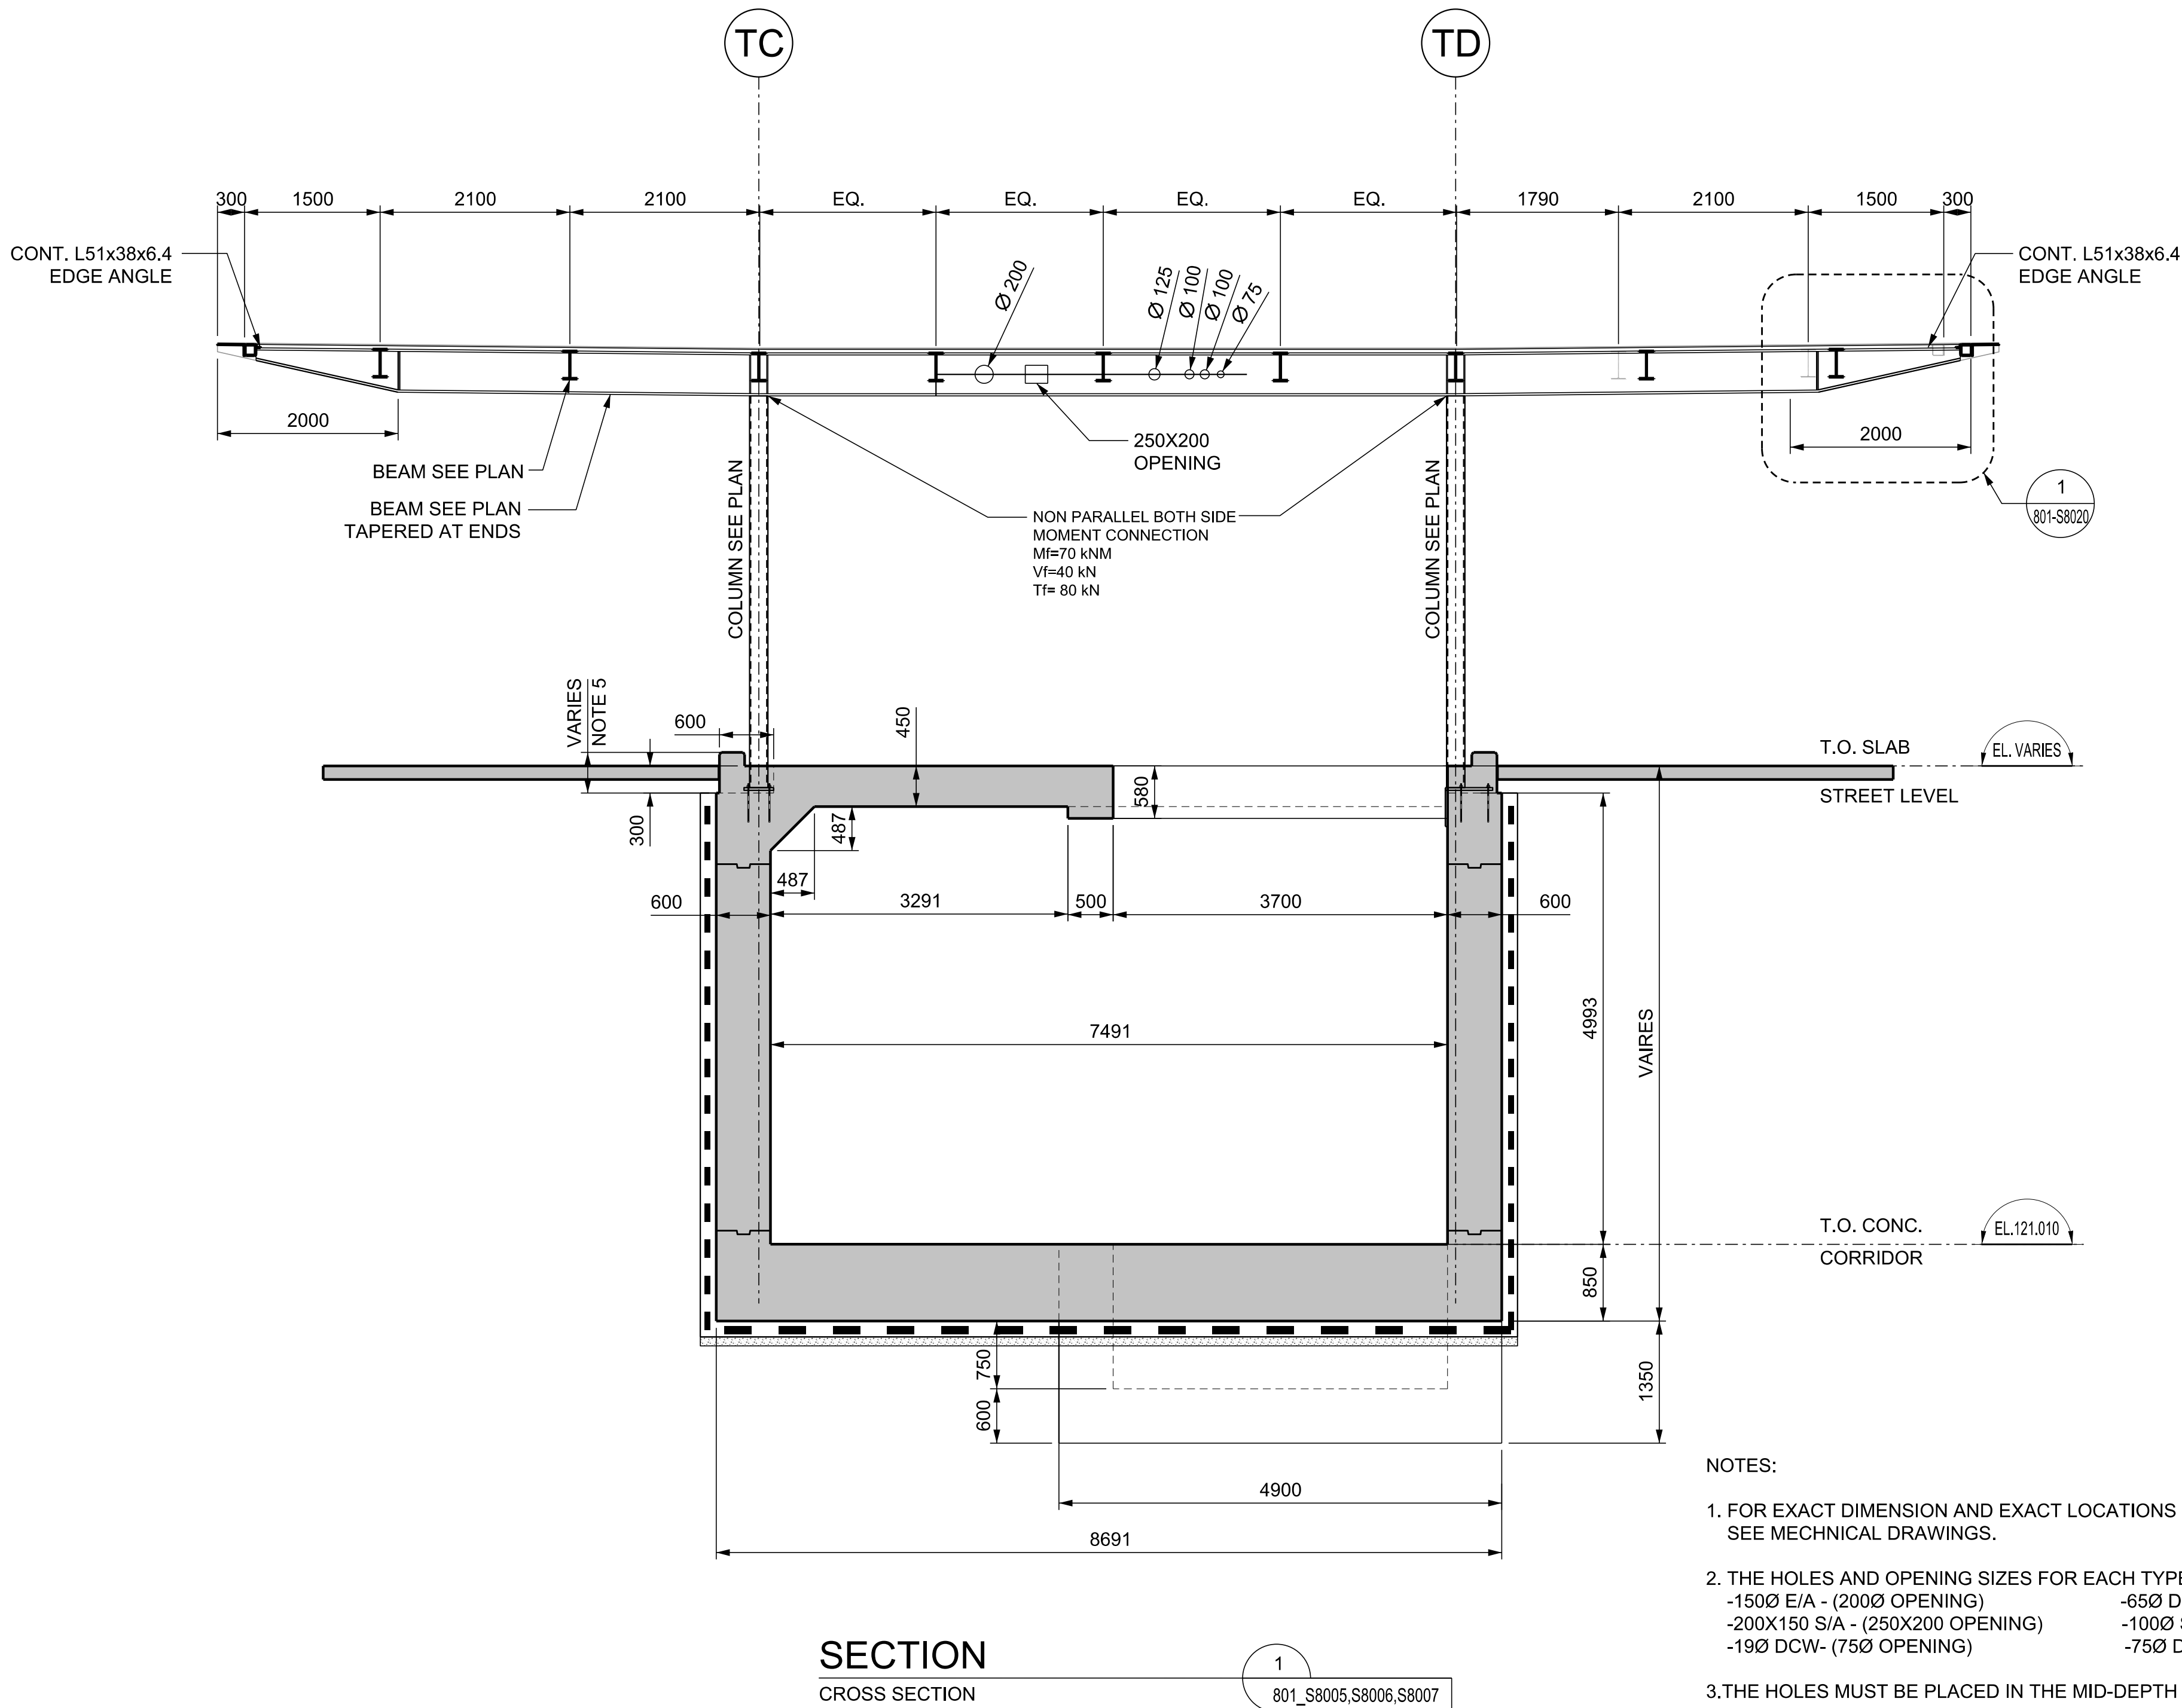

REVISIONS			REVISIONS		
PA	30% SUBMISSION	2016/02/28			
PB	60% SUBMISSION	2016/09/23			

90% REVIEW
DRAWING

CONFIDENTIAL AND PROPRIETARY
NOT FOR CONSTRUCTION

SCALE(S)⁰

1

2m

CROSSLINX
TRANSIT SOLUTIONS

IBI

DESIGNED A. LUK2016/09/23

DRAWN S. WANG2016/09/23

CHECKED Z. FU2016/09/23

APPROVED

8010-01-CTSD-43DE-8021

EGLINTON CROSSTOWN LRT
NON-INTERCHANGE STATIONS
MT. DENNIS
BUS TERMINAL
CROSS SECTION

Plot Date: 1/18/2017

METROLINX

Toronto Light Rail Transit Projects

Dwg. No.
RTI-ECL801_S8021

Rev.
PB