



CADD FILE NAME: p:\s1218.sil.bz: Toronto_Transportation\Documents\Eglinton Crosstown LRT\Execution\43_Struct\Design\43DD_DRAWINGS\8010 Mt. Dennis\RTI-ECL801_SS_PRTL_BPLT_BGLV_01

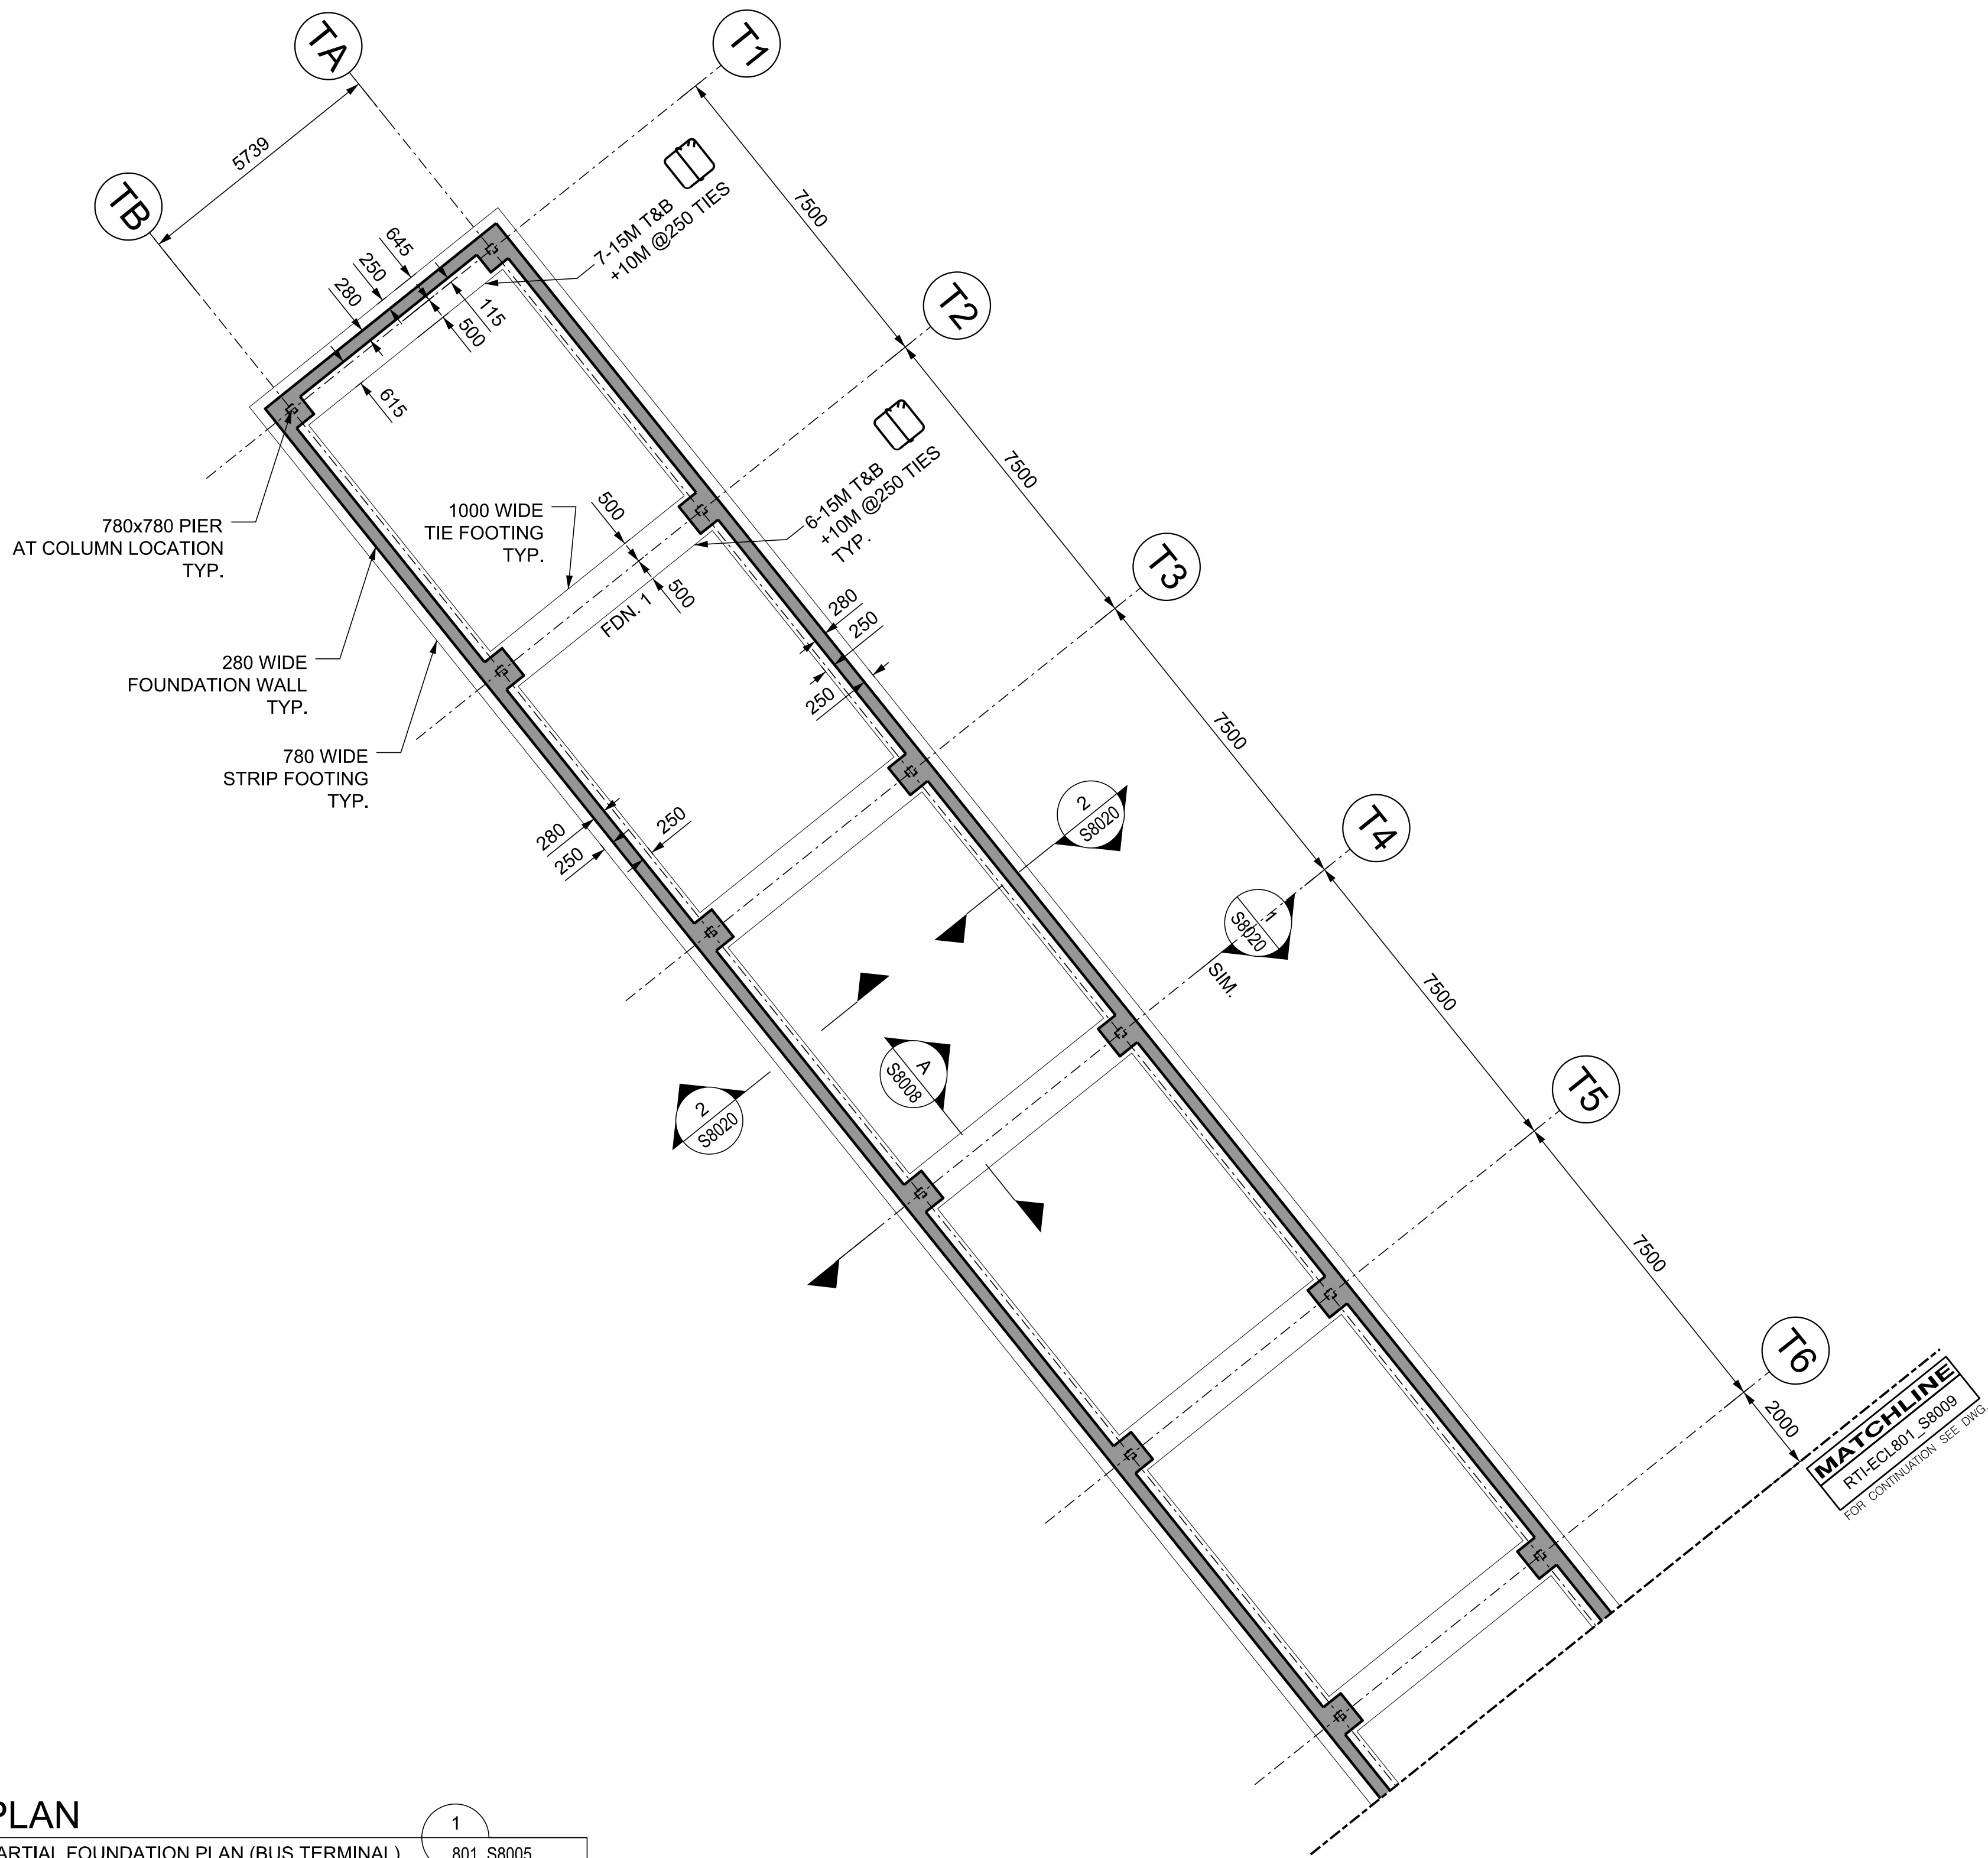

PLAN
PARTIAL FOUNDATION PLAN (BUS TERMINAL)

NOTES:
1. SEE SLAB VENTING DRAWING NO. 8010-01-LTSD-4EDE-0805

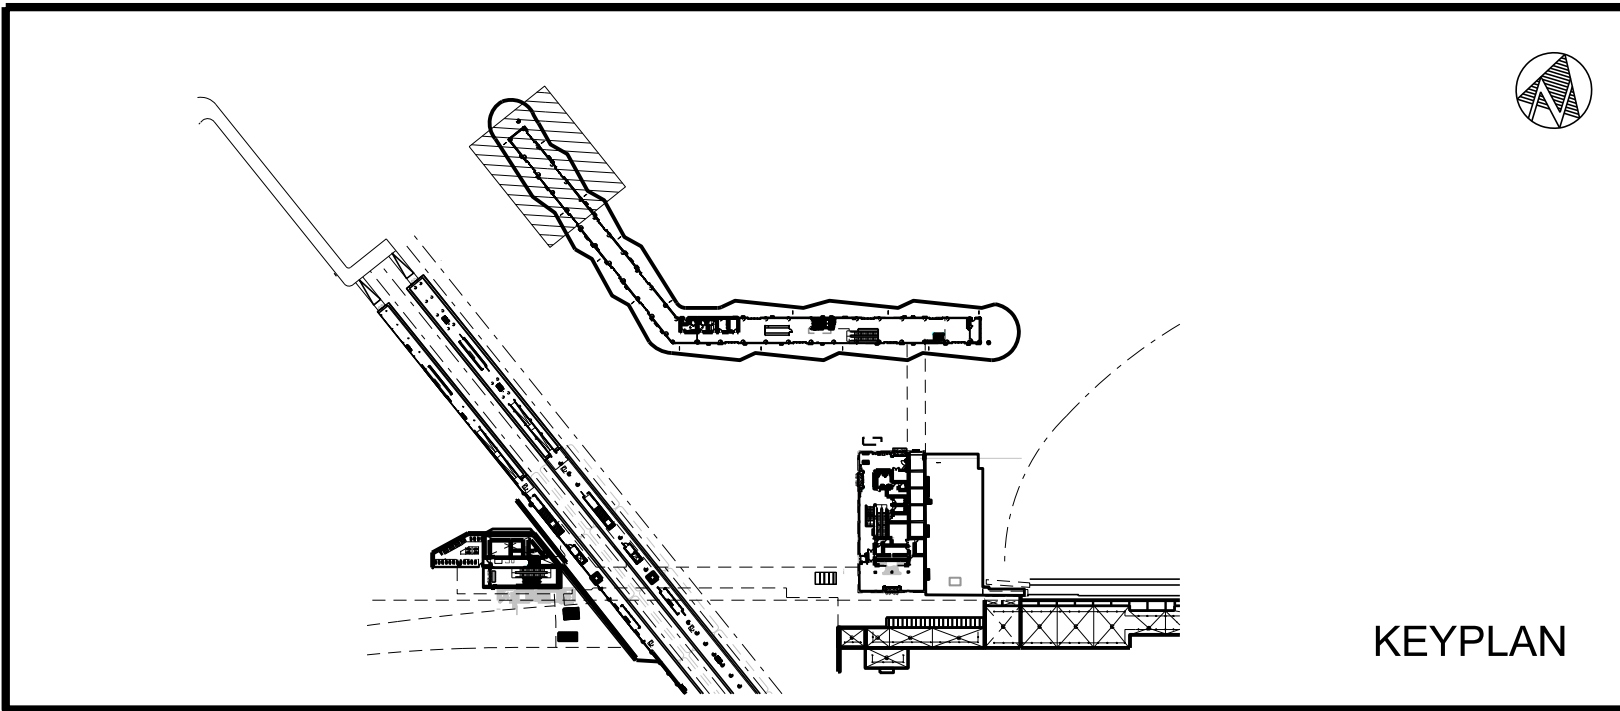

REVISIONS <table><tr><td>PA</td><td>30% SUBMISSION</td><td>2016/02/28</td><td></td></tr><tr><td>PB</td><td>60% SUBMISSION</td><td>2016/09/23</td><td></td></tr><tr><td></td><td></td><td></td><td></td></tr></table>		PA	30% SUBMISSION	2016/02/28		PB	60% SUBMISSION	2016/09/23						REVISIONS <table><tr><td></td><td></td><td></td><td></td></tr><tr><td></td><td></td><td></td><td></td></tr><tr><td></td><td></td><td></td><td></td></tr></table>														90% REVIEW DRAWING CONFIDENTIAL AND PROPRIETARY NOT FOR CONSTRUCTION SCALE(S) 0 1 2 3 4m		CROSSLINX TRANSIT SOLUTIONS	IBI			DESIGNED A. LUK 2016/09/23 DRAWN S. WANG 2016/09/23 CHECKED Z. FU 2016/09/23 APPROVED 8010-01-CTSD-43DE-8008	EGLINTON CROSSTOWN LRT NON-INTERCHANGE STATIONS MT. DENNIS BUS TERMINAL FOUNDATION PARTIAL PLAN 1	Plot Date: 1/18/2017 METROLINX Toronto Light Rail Transit Projects Dwg. No. RTI-ECL801_S8008 Rev. PB
PA	30% SUBMISSION	2016/02/28																																		
PB	60% SUBMISSION	2016/09/23																																		