


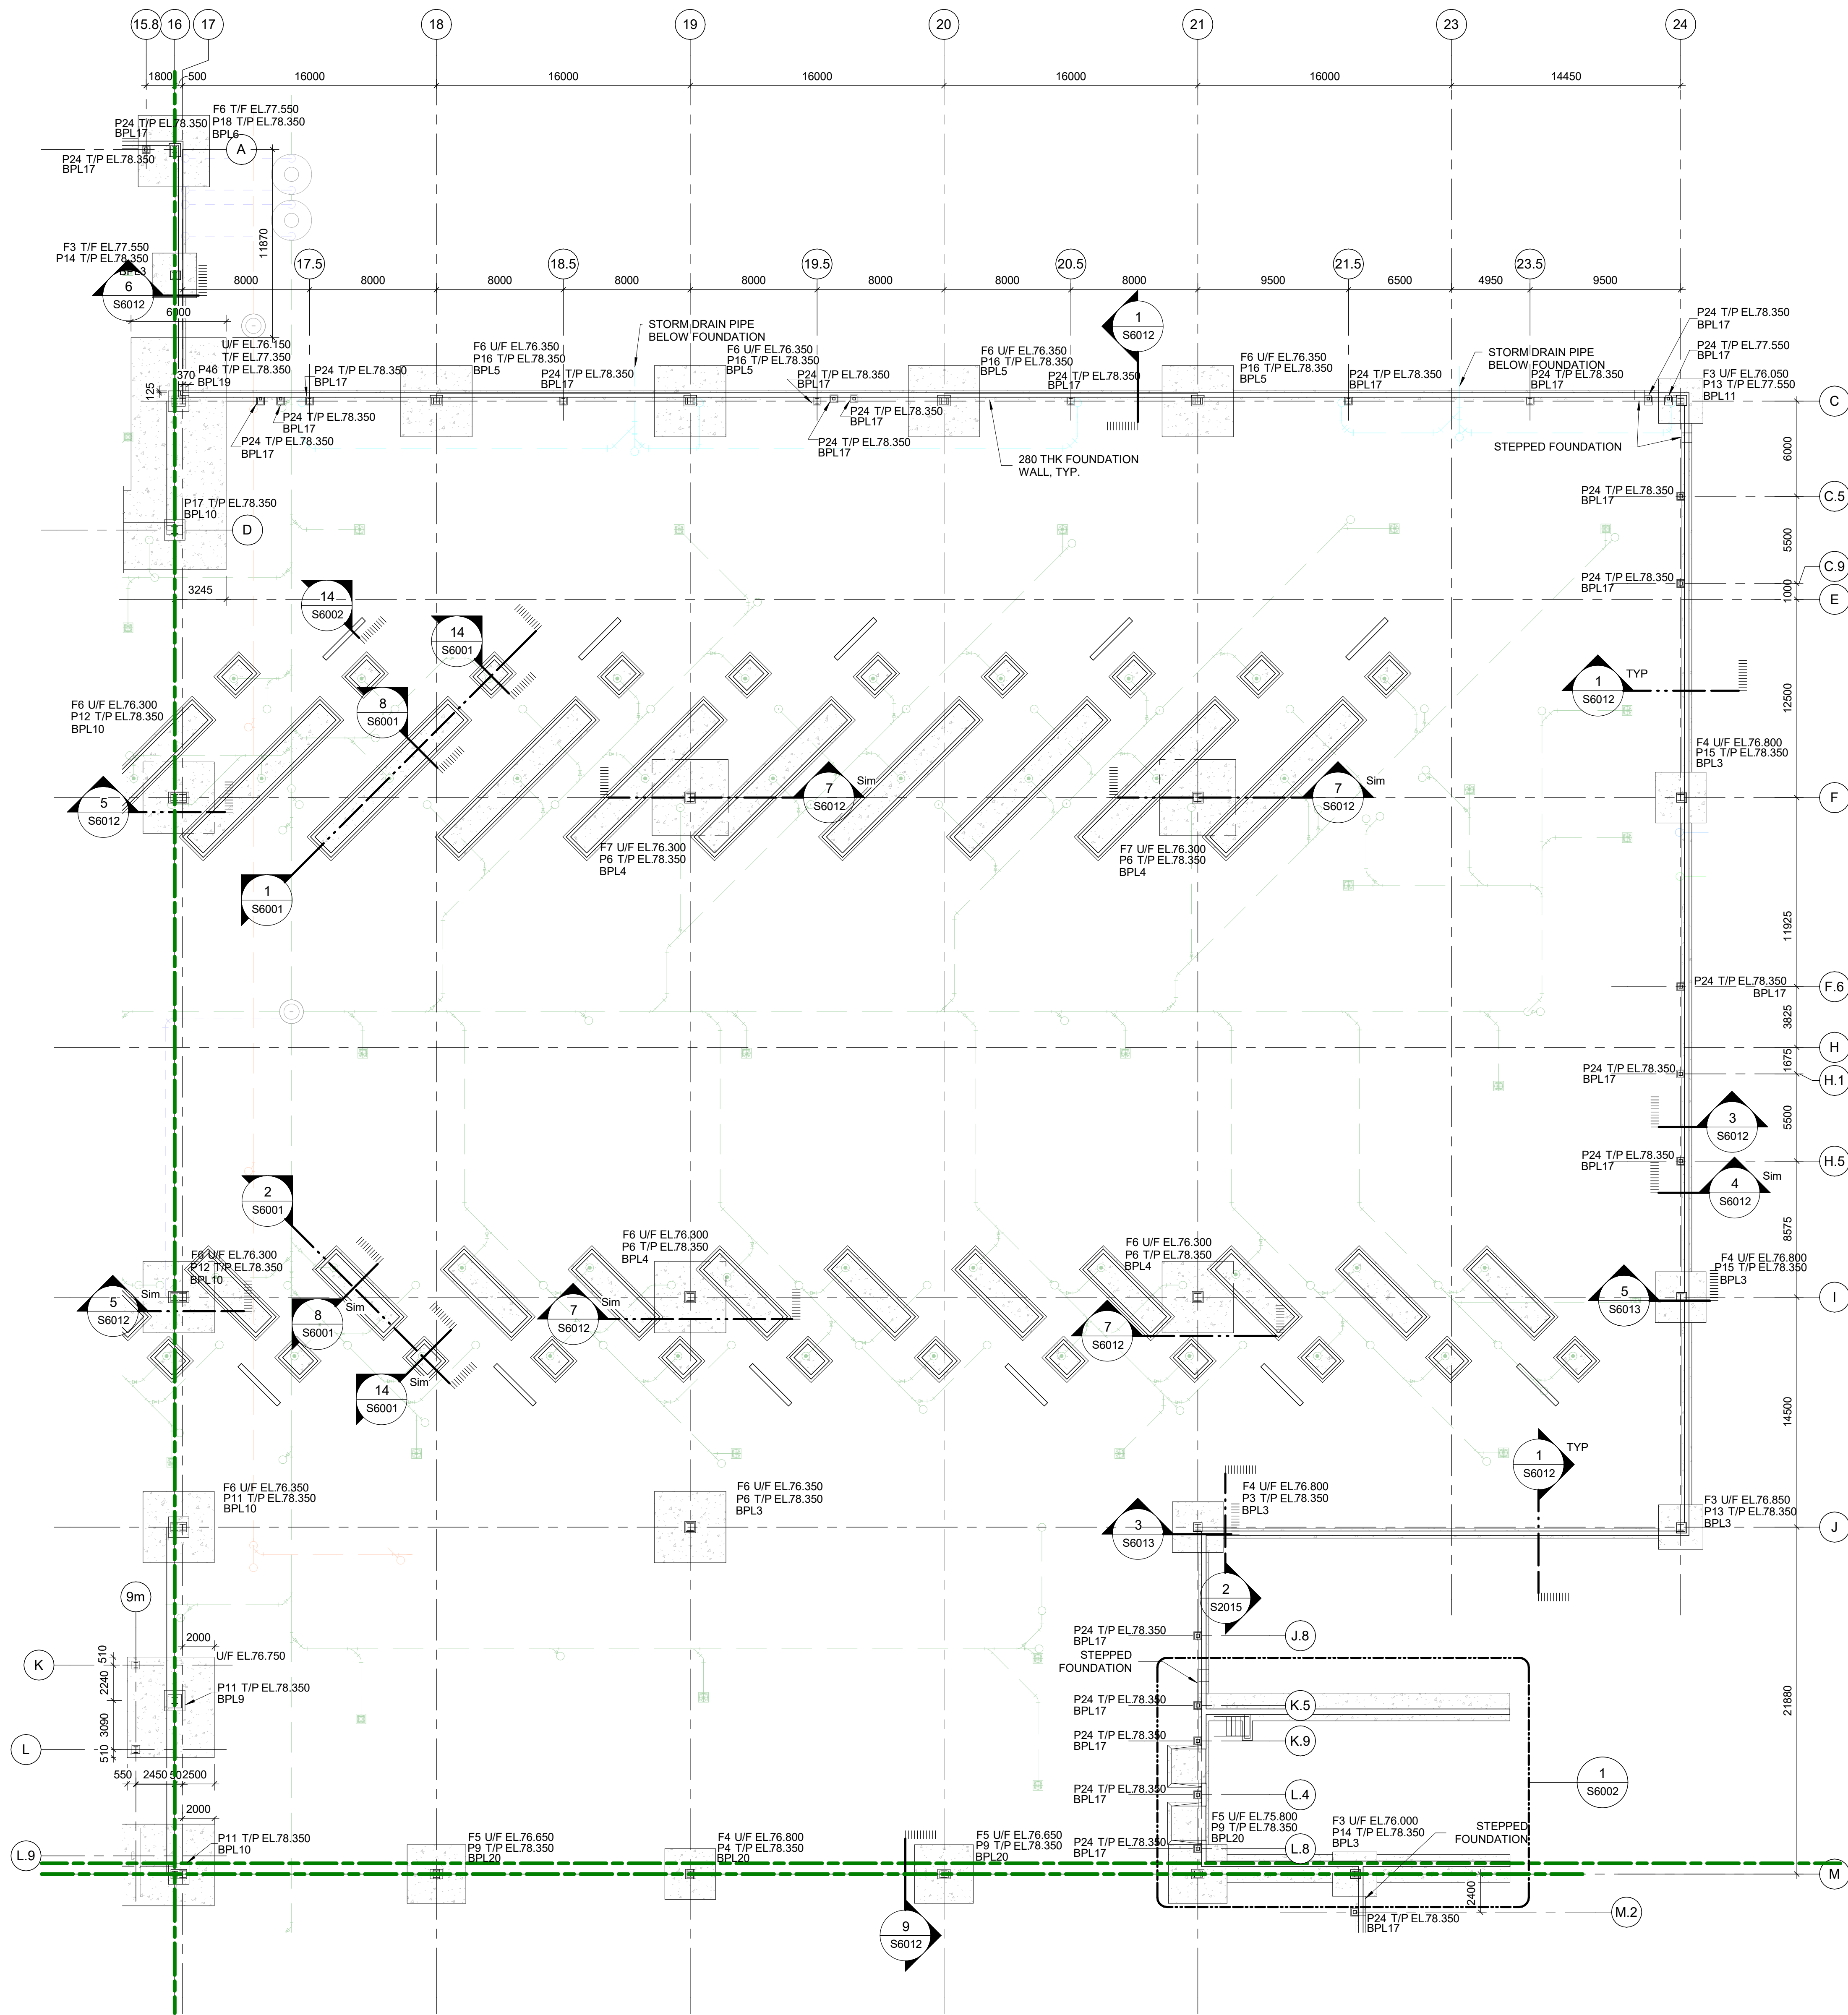

1 FOUNDATION PLAN - AREA 'A'
S2001 Scale: 1 : 200

Client Name




71 Main Street West
Hamilton, Ontario, L8P 4Y5

COPYRIGHT
This drawing has been prepared solely for the intended use. No reproduction or distribution for any purpose other than authorized by IBI Group is permitted. Without limitation, no part of this drawing may be reproduced, stored in a retrieval system, or transmitted in any form or by any means, electronic, mechanical, photocopying, recording, or by any information storage and retrieval system, without prior written permission from IBI Group Professional Services (Canada) Inc. or its authorized representative. IBI Group Professional Services (Canada) Inc. is a member of the IBI Group of companies.

ISSUES		
No.	DESCRIPTION	DATE
A	COSTING	2019-06-09
B	60% REVIEW	2019-09-11
C	90% REVIEW	2019-11-14
D	BUILDING PERMIT	2020-01-17
E	PERMIT REVISION	2020-03-17

**NOT FOR
CONSTRUCTION**

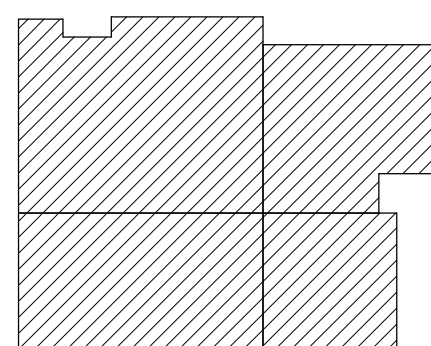

CONSULTANTS

SEAL



FILE NO: DA-19-120

PRIME CONSULTANT



IBI GROUP
175 Galloway Blvd, Unit 100
Toronto, ON M9W 6C9, Canada
Tel: 416 673 1000 Fax: 416 673 4620
ibigroup.com

PROJECT

HAMILTON TRANSIT FACILITY
281 BIRCH AVENUE
HAMILTON, ONTARIO

PROJECT NO: 115096	PROJECT MANAGER: E. CZERNIAK
DRAWN BY: D. NAUMOV	CHECKED BY: S. NASSER
ARCHITECT/ENGINEER: D. NAUMOV	APPROVED BY: K. ANGER

SHEET TITLE
FOUNDATION PLAN - AREA 'A'

SHEET NUMBER
S2001

ISSUE
E