
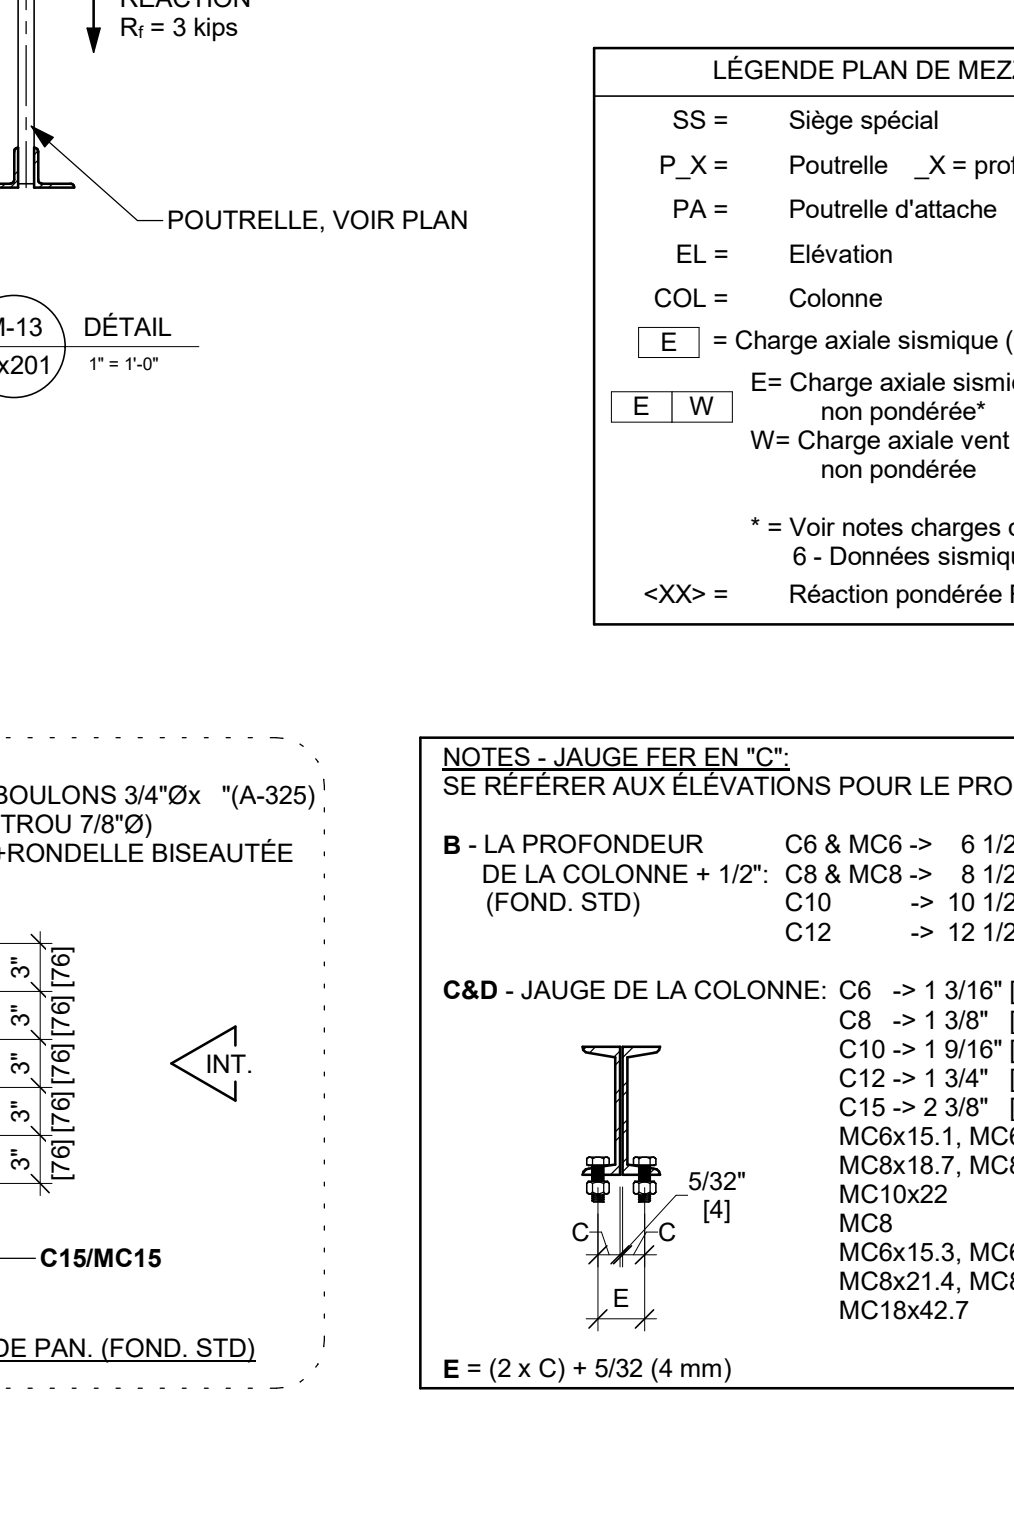
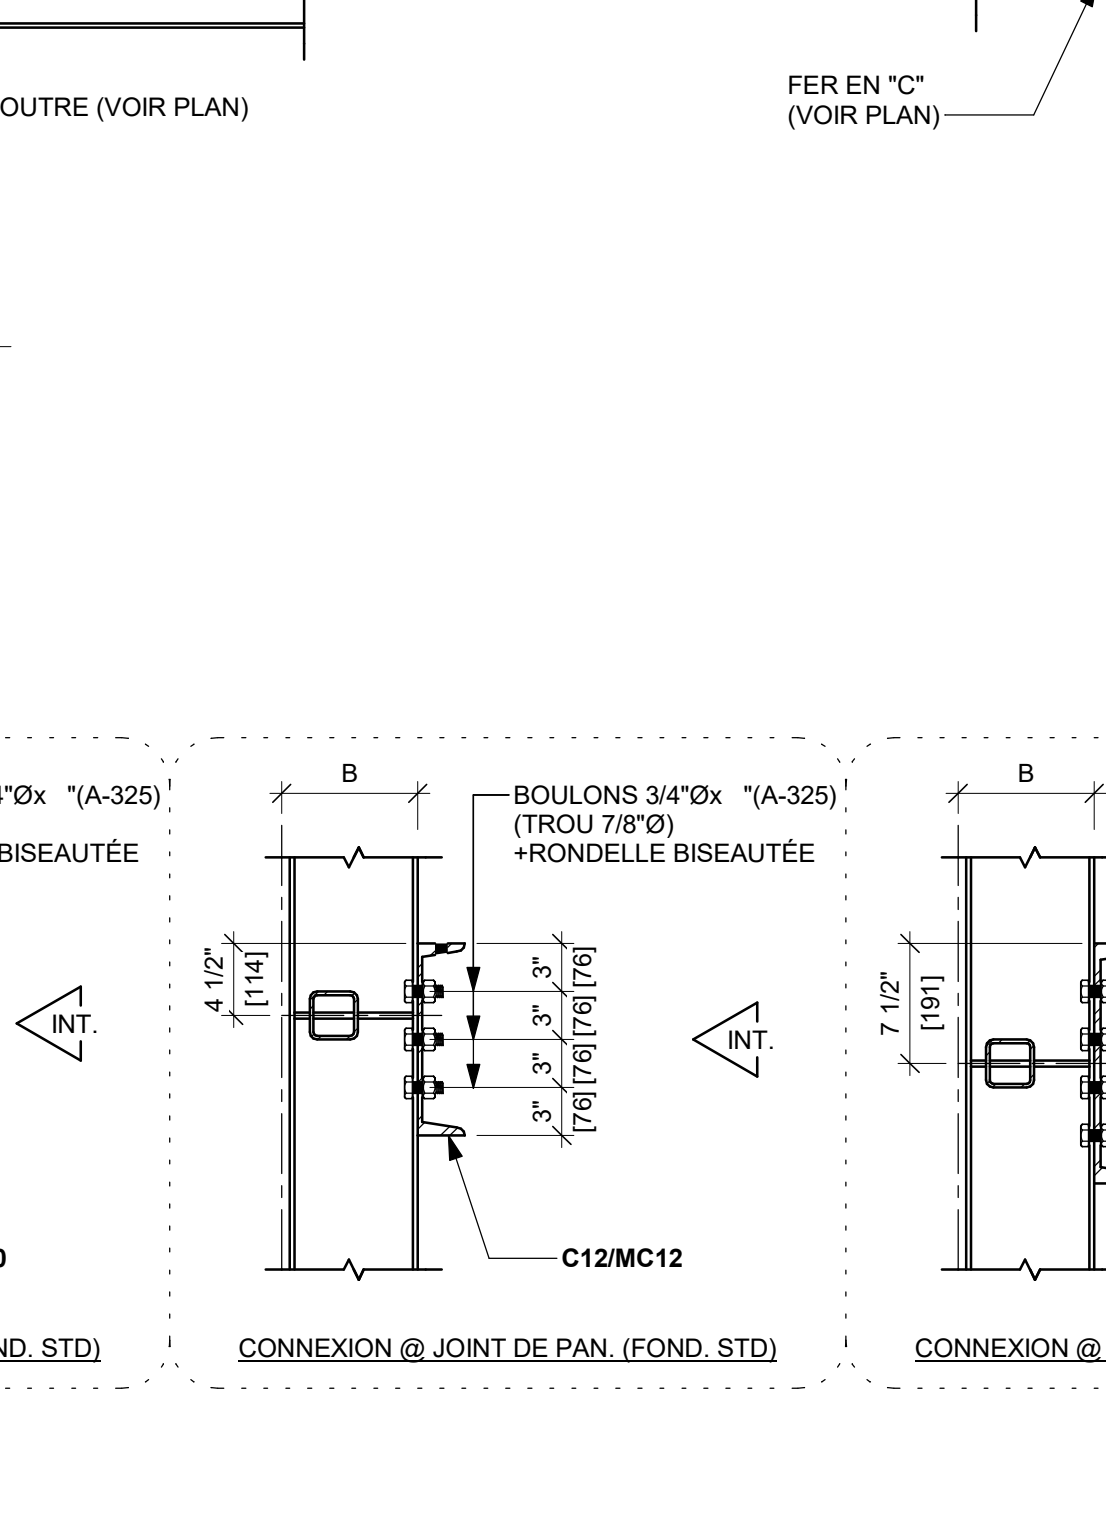
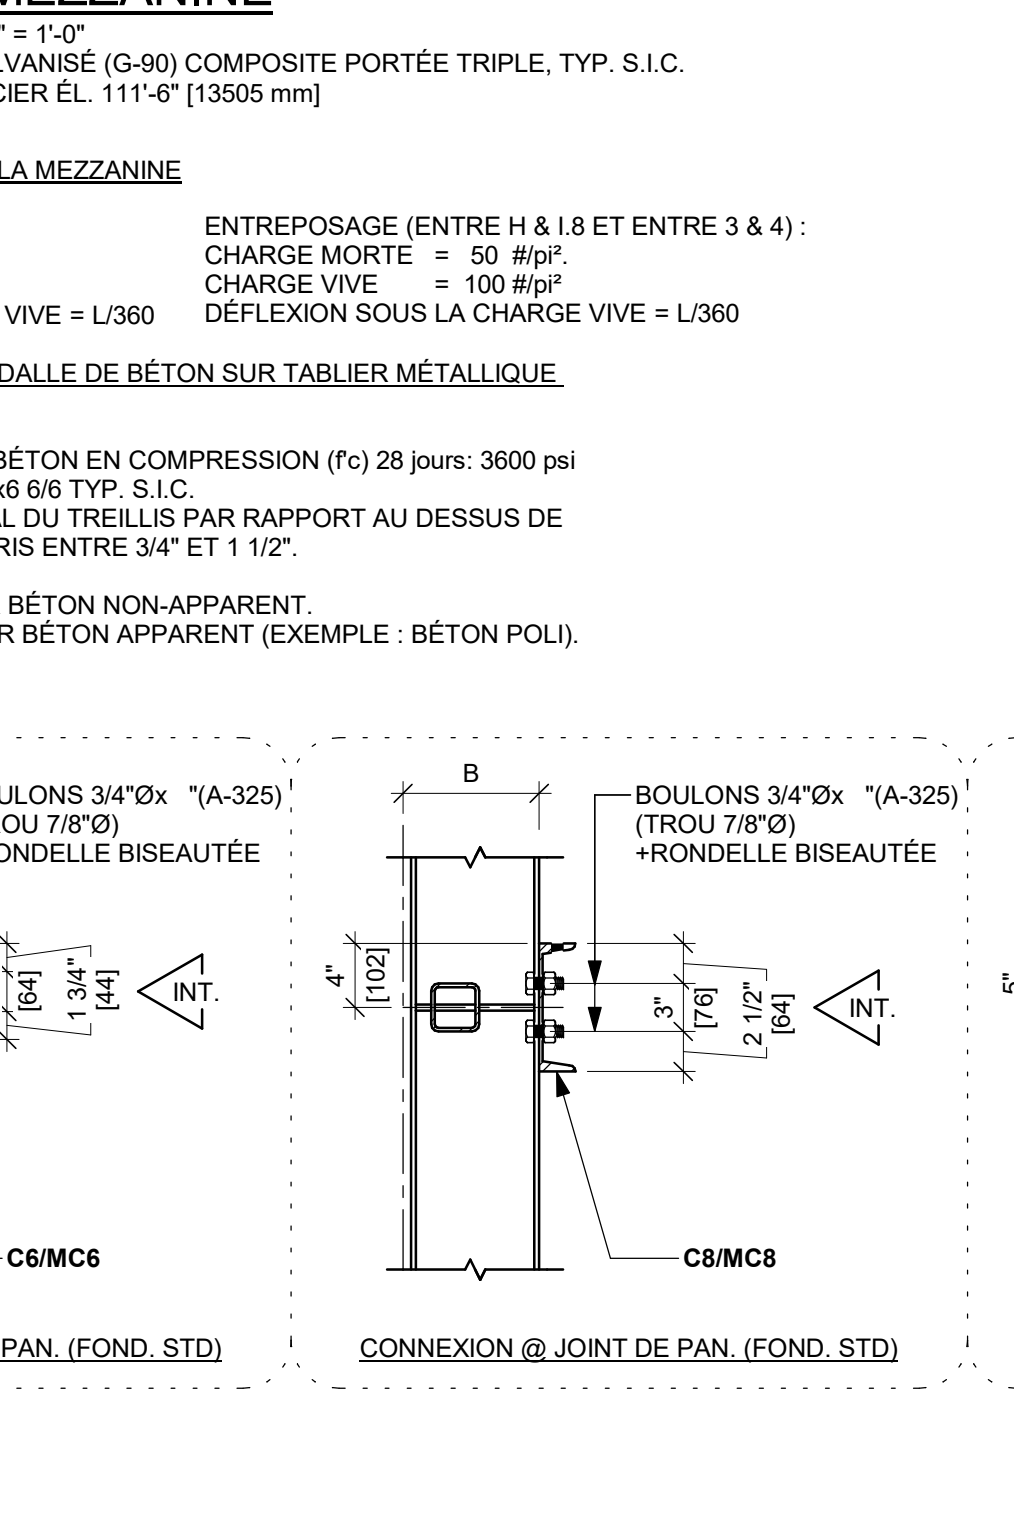
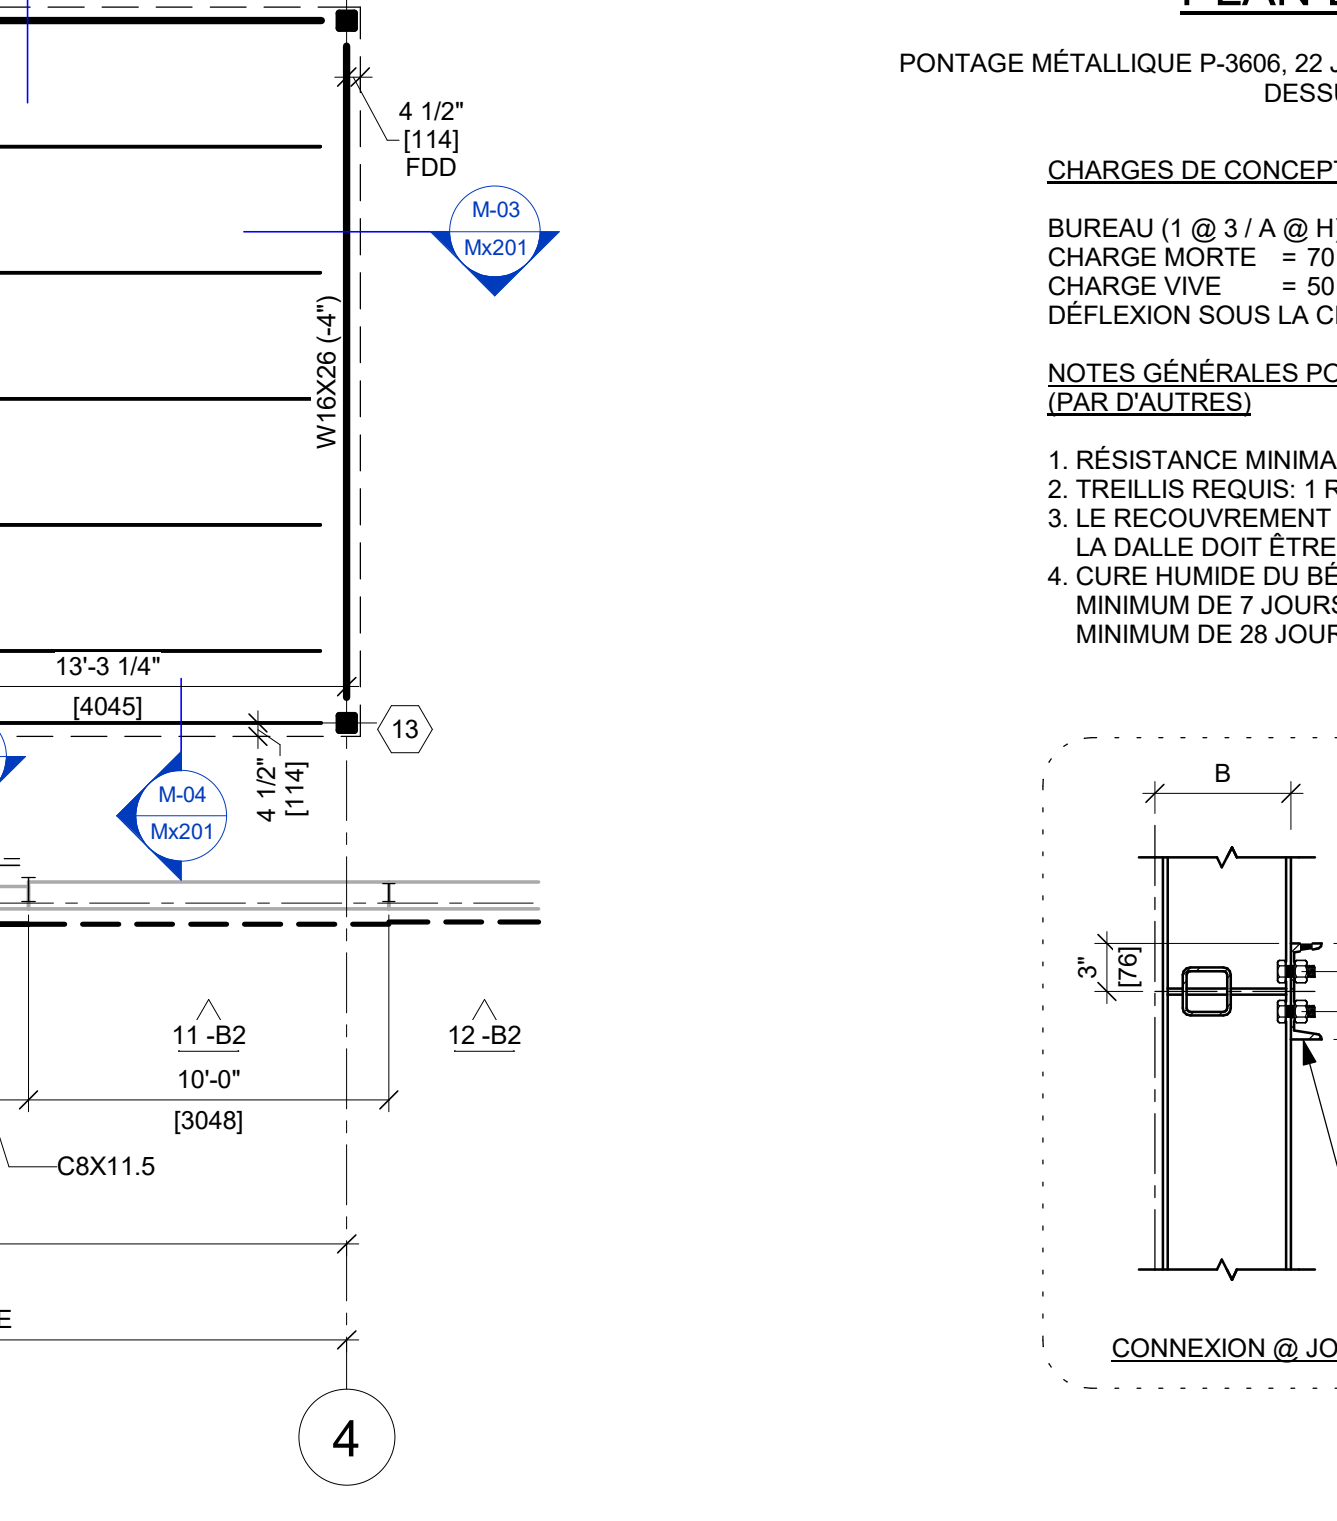
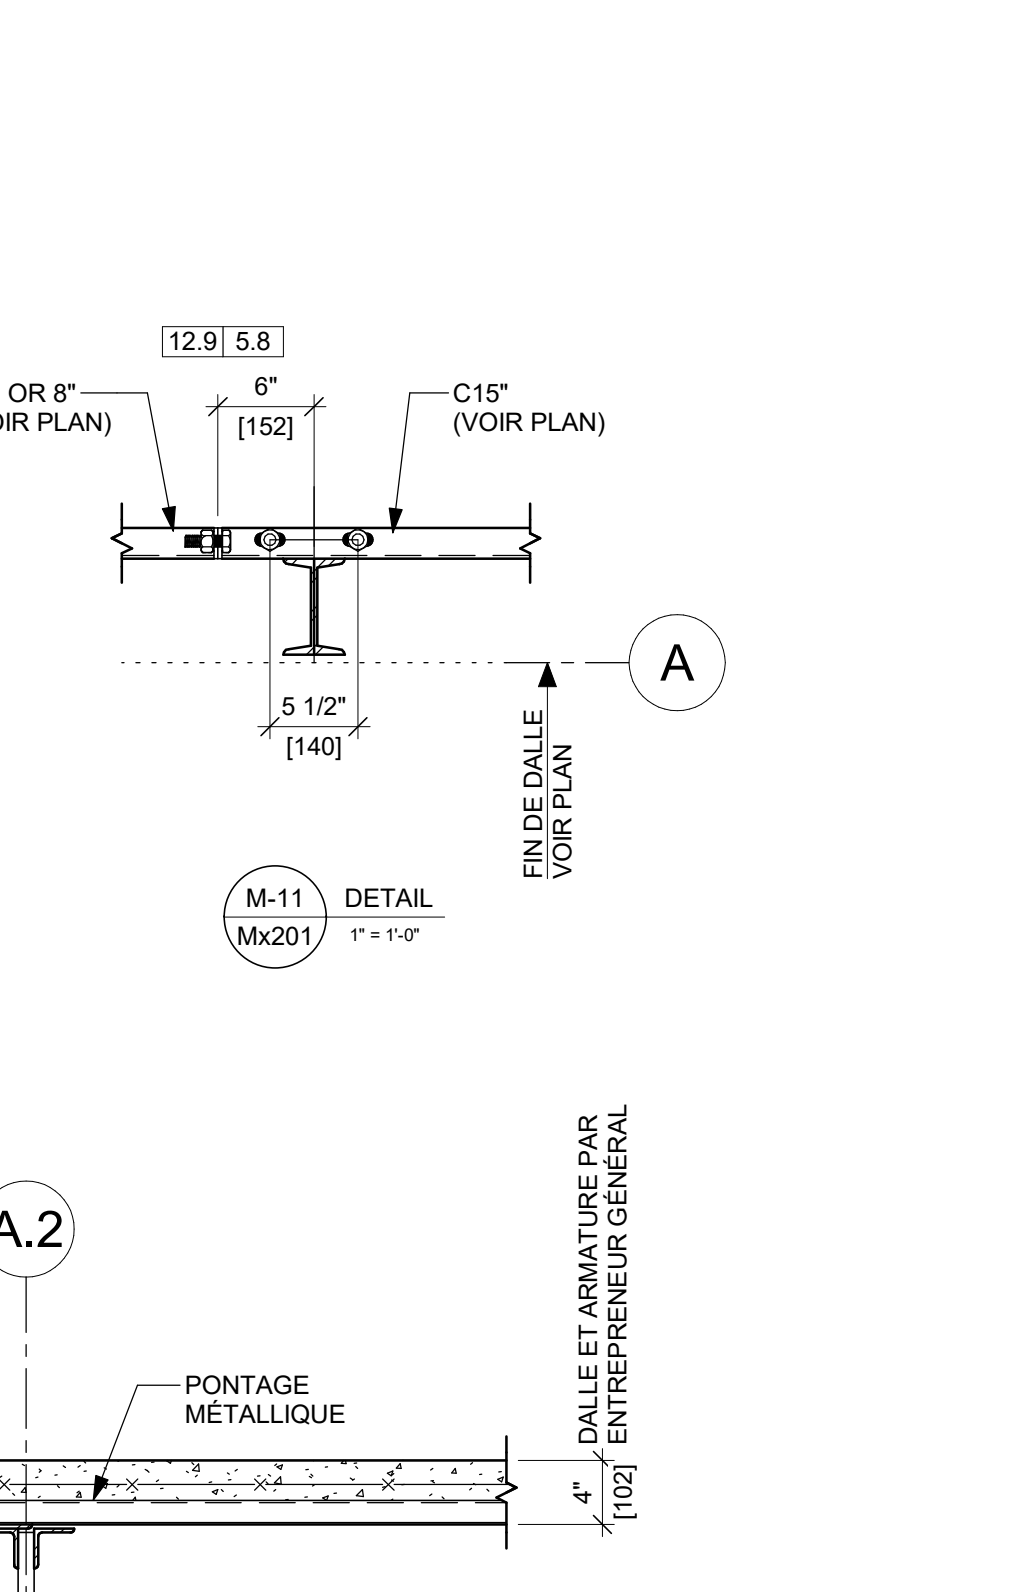
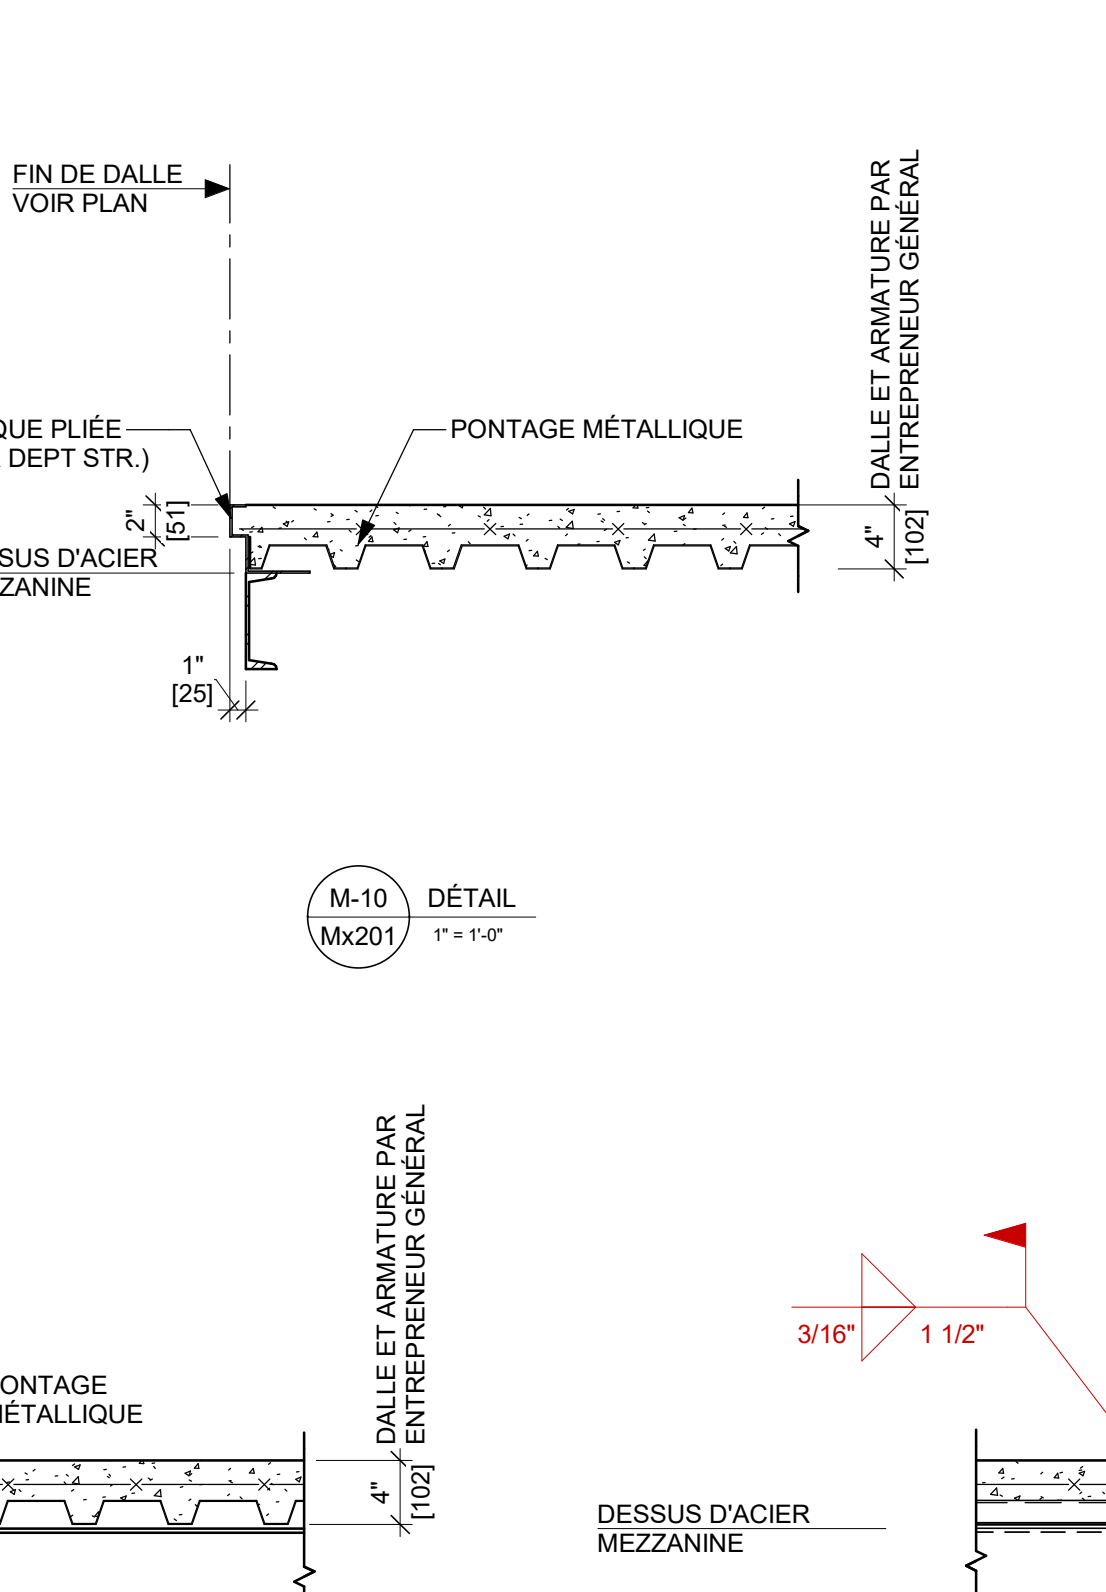
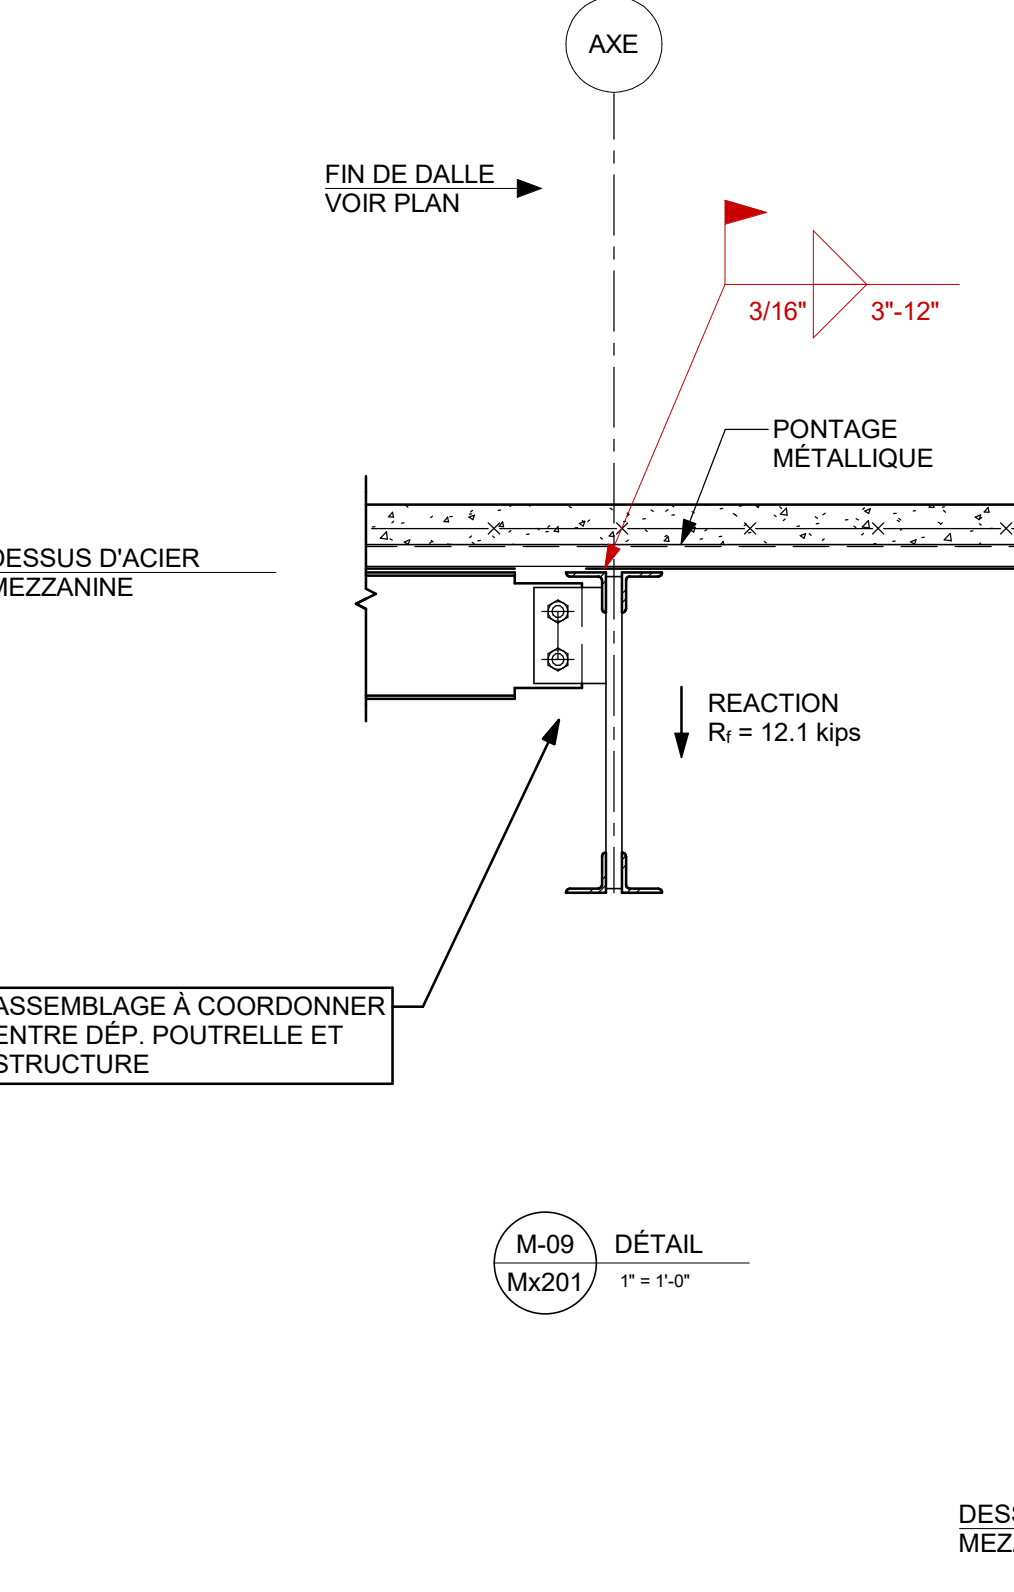
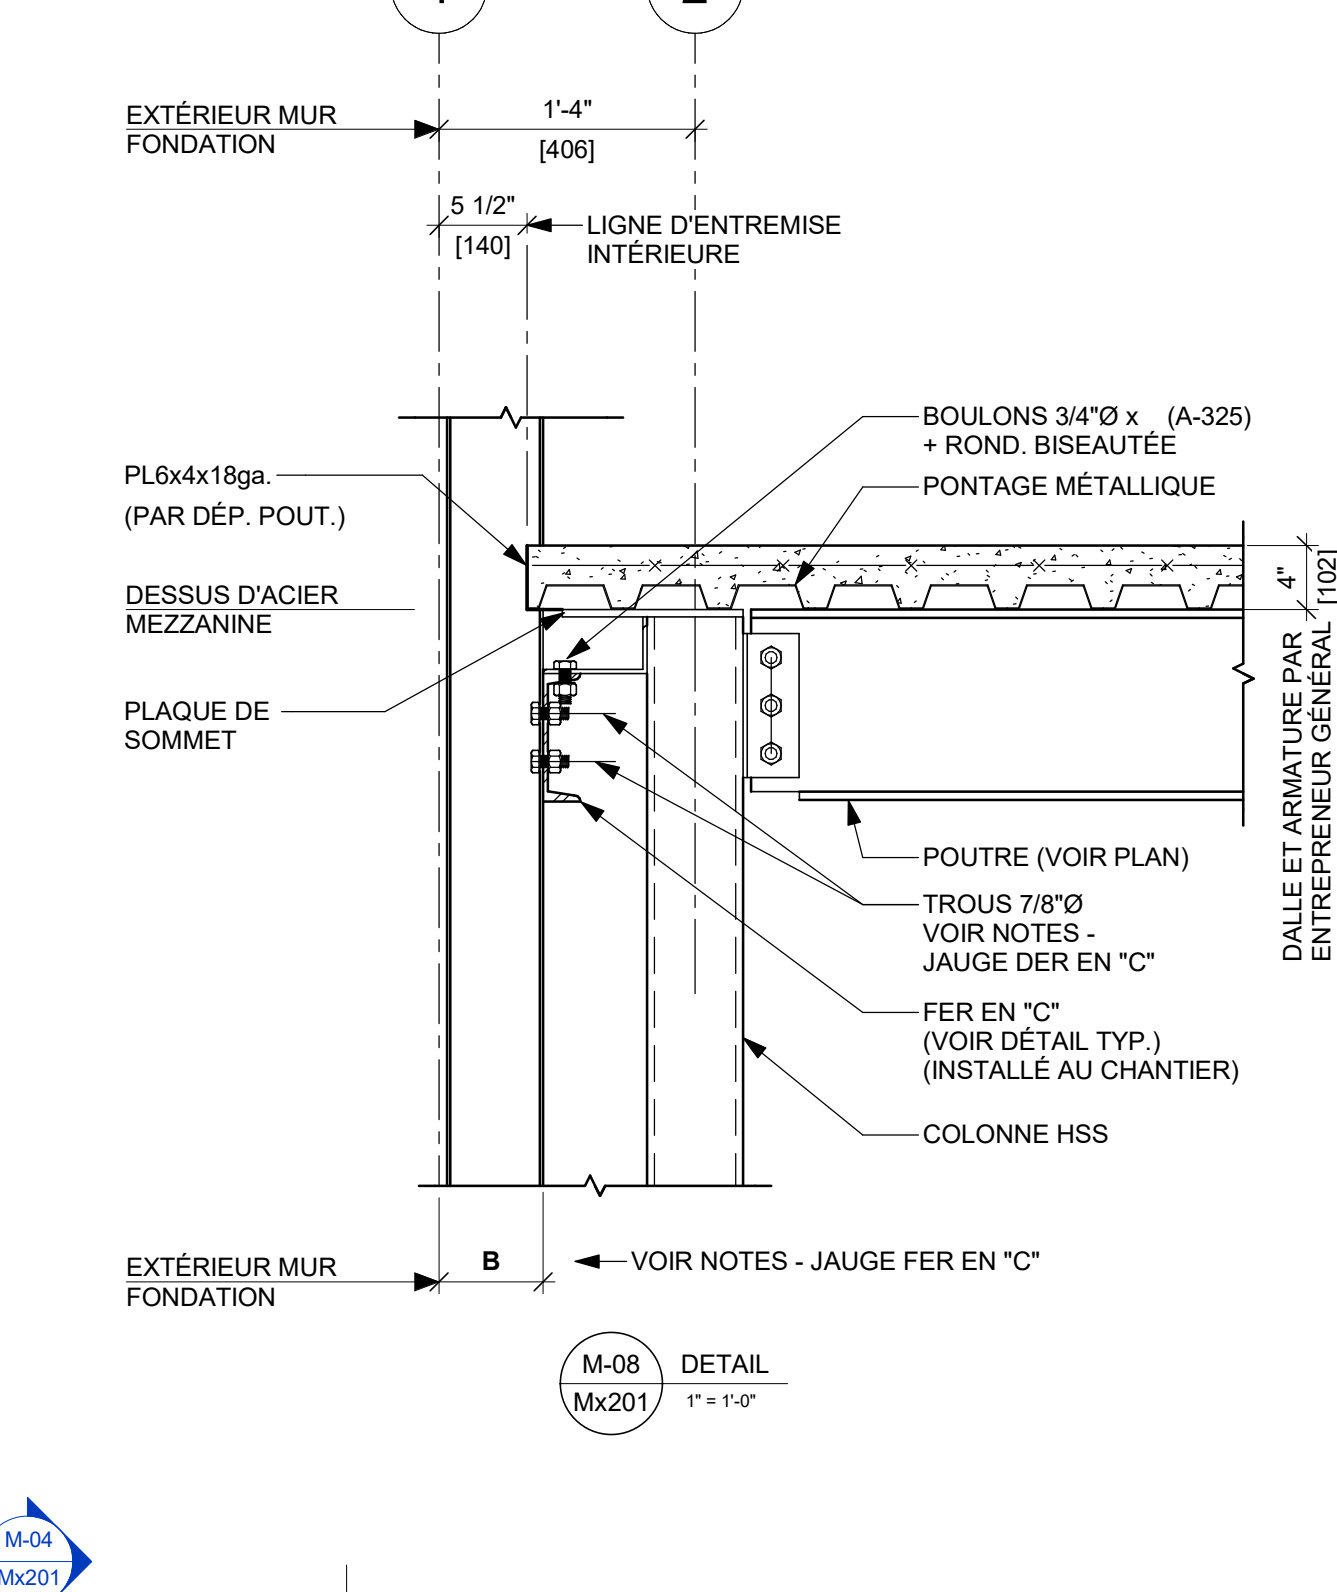
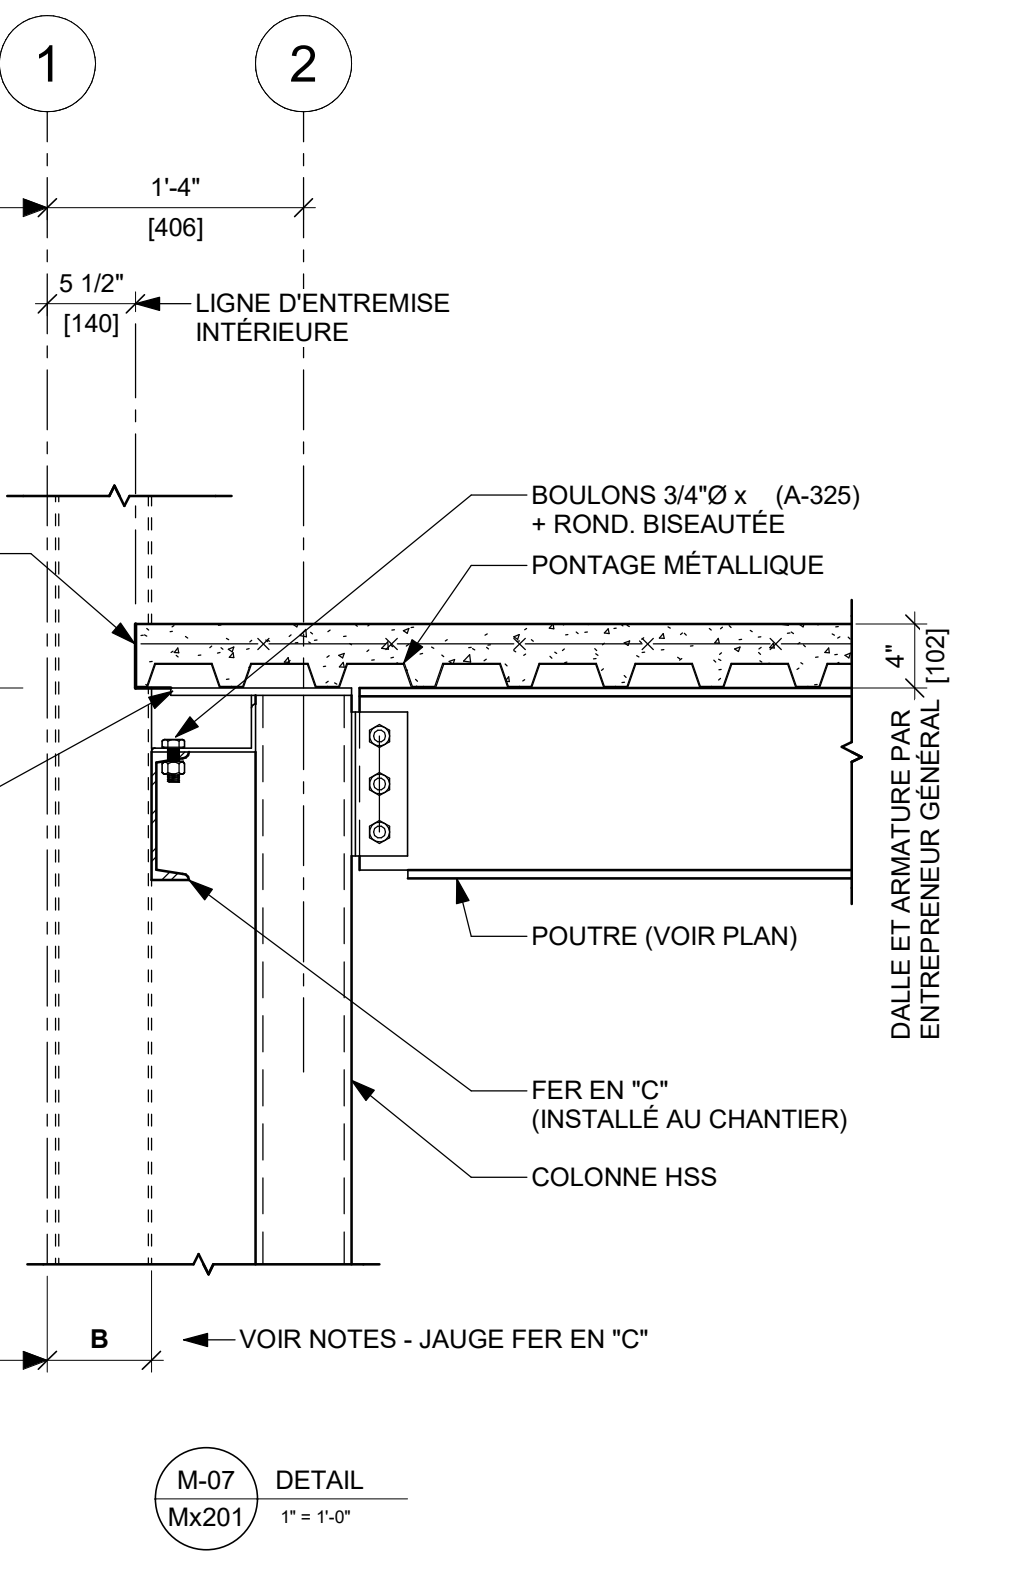
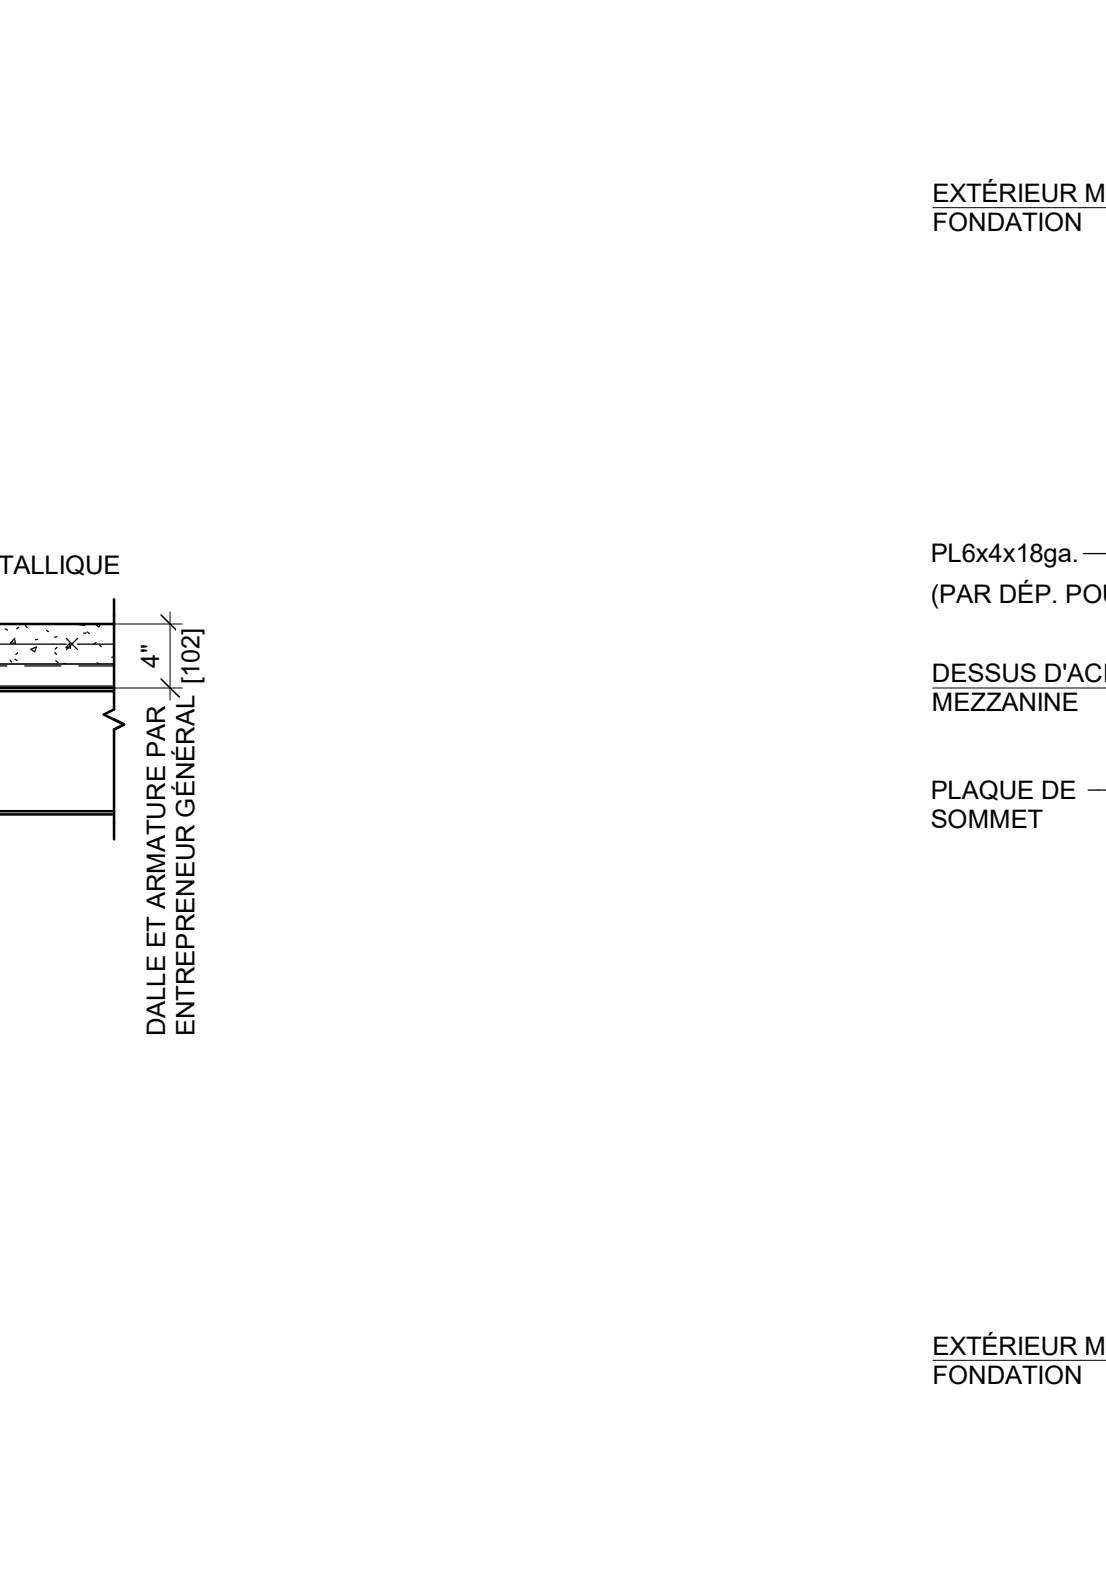
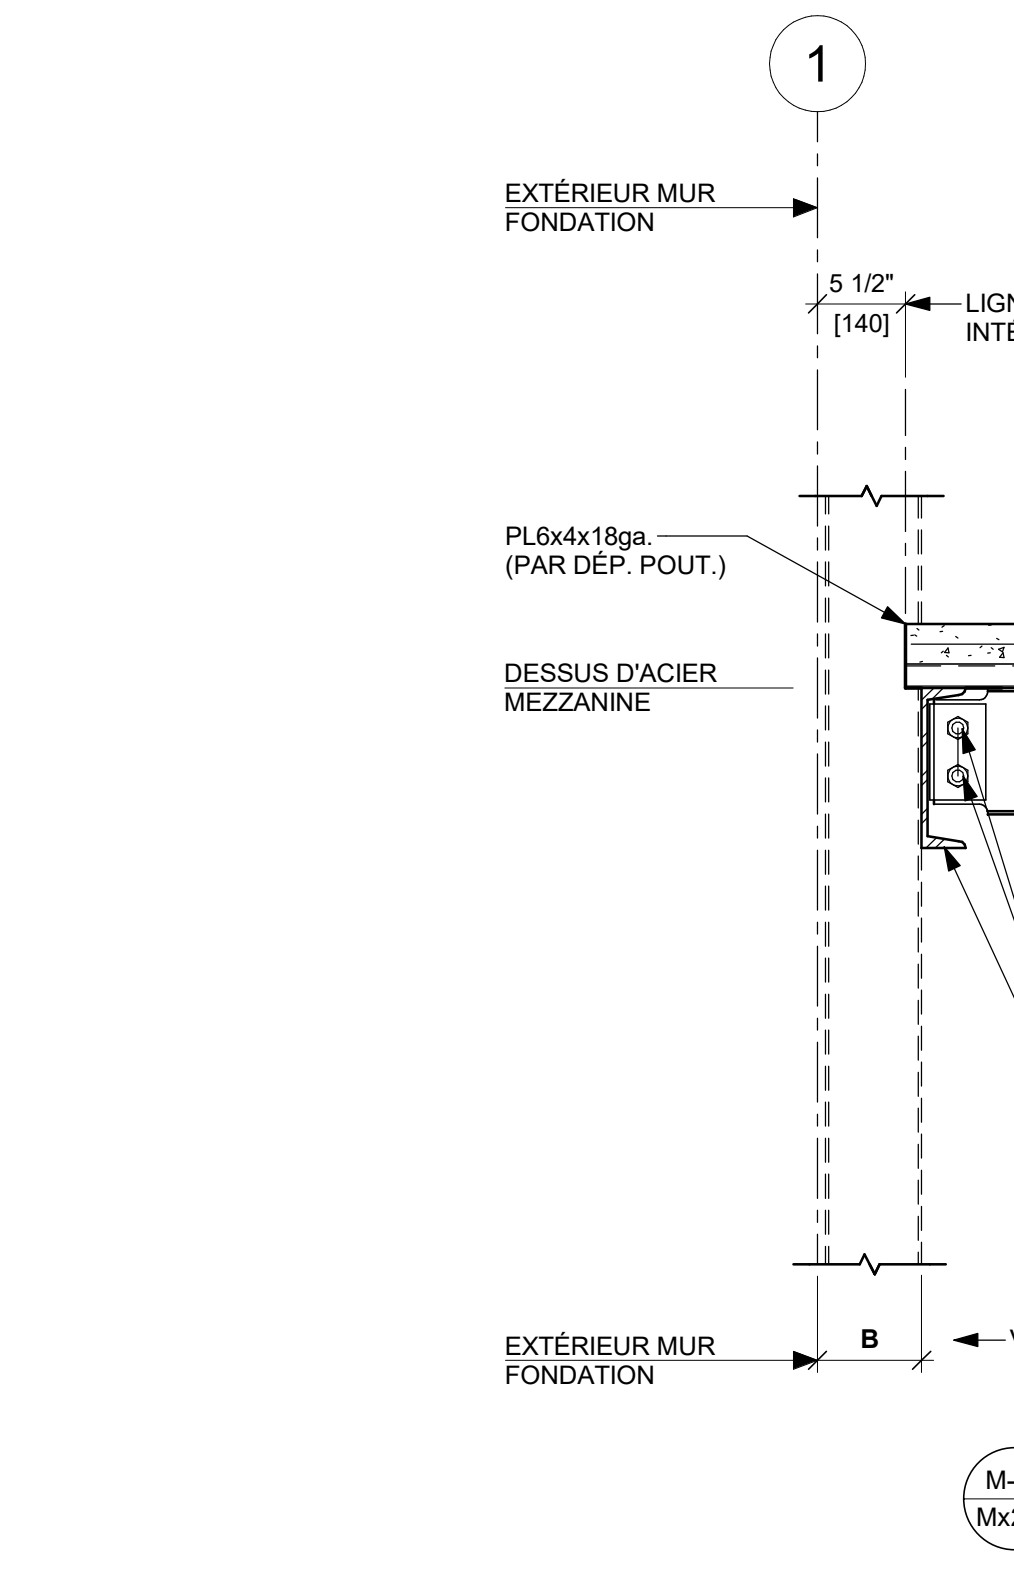
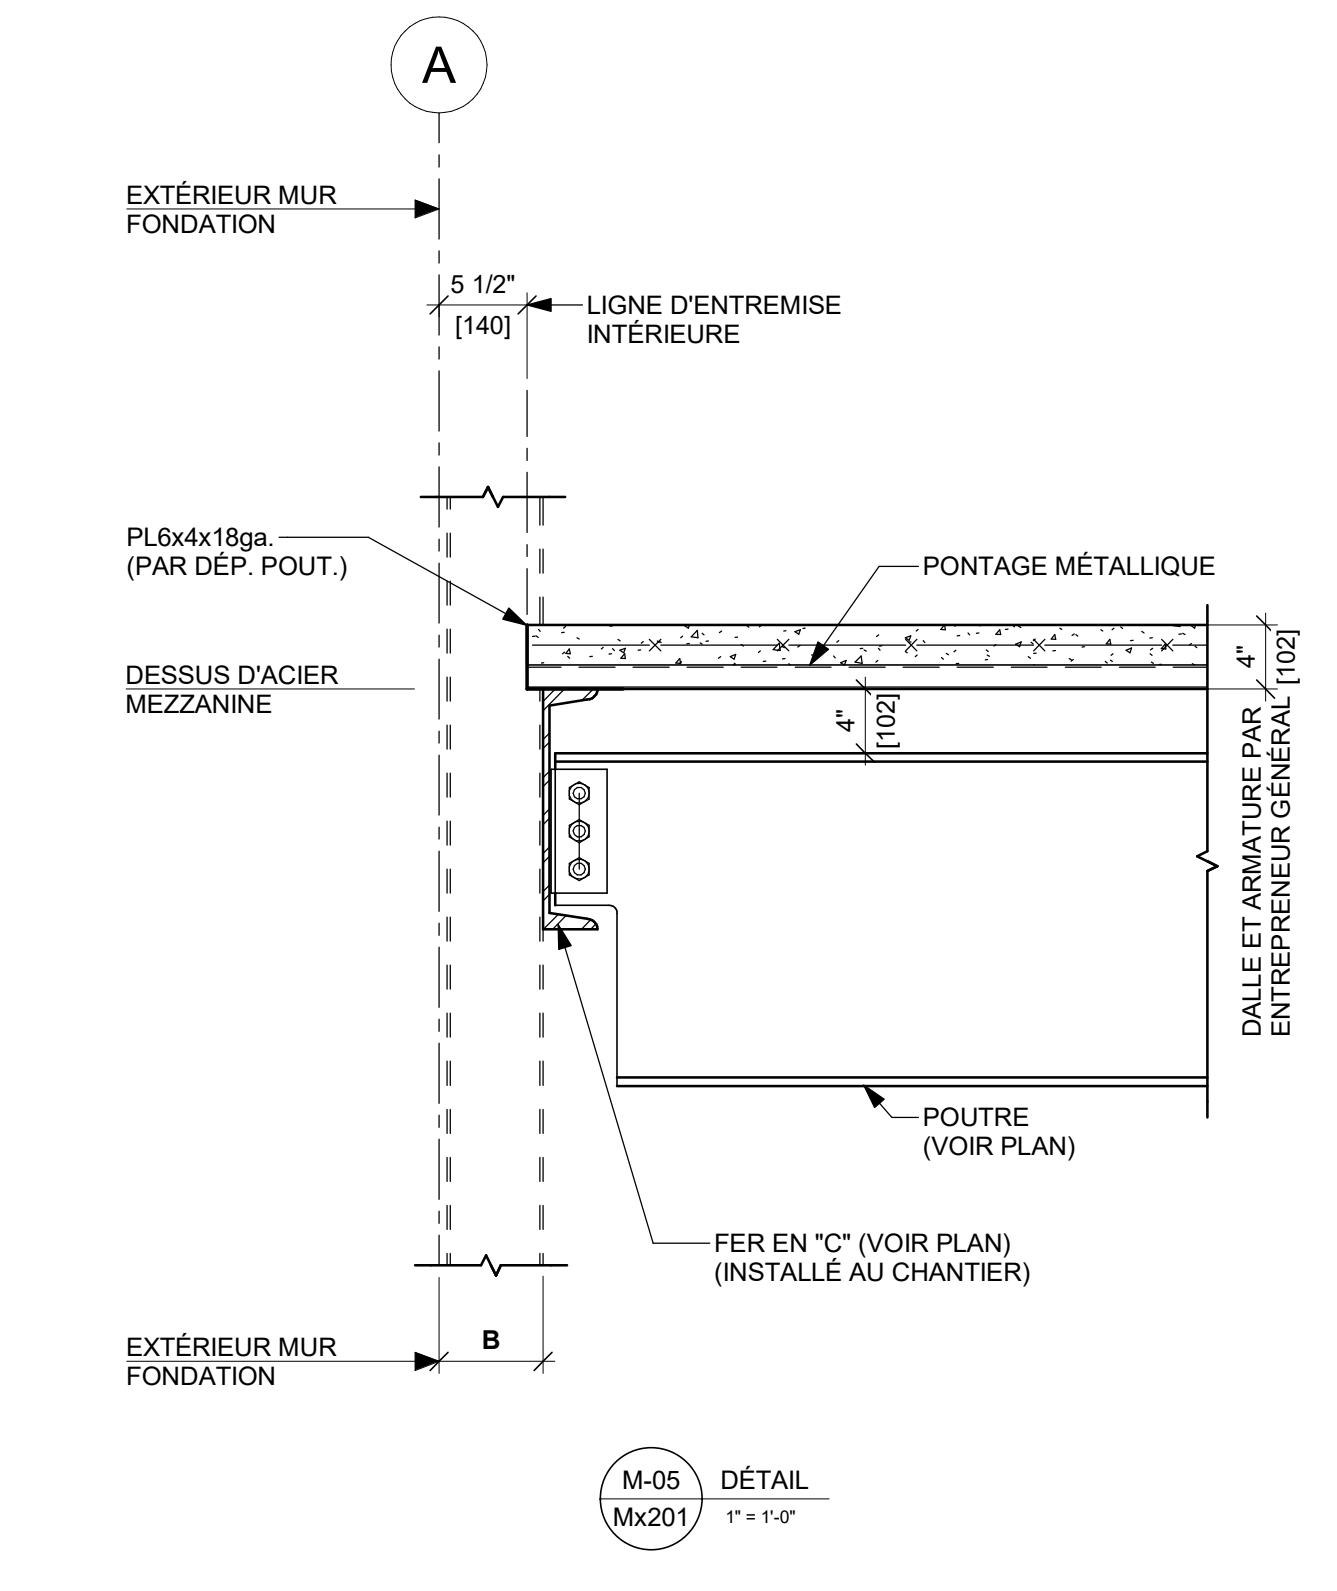
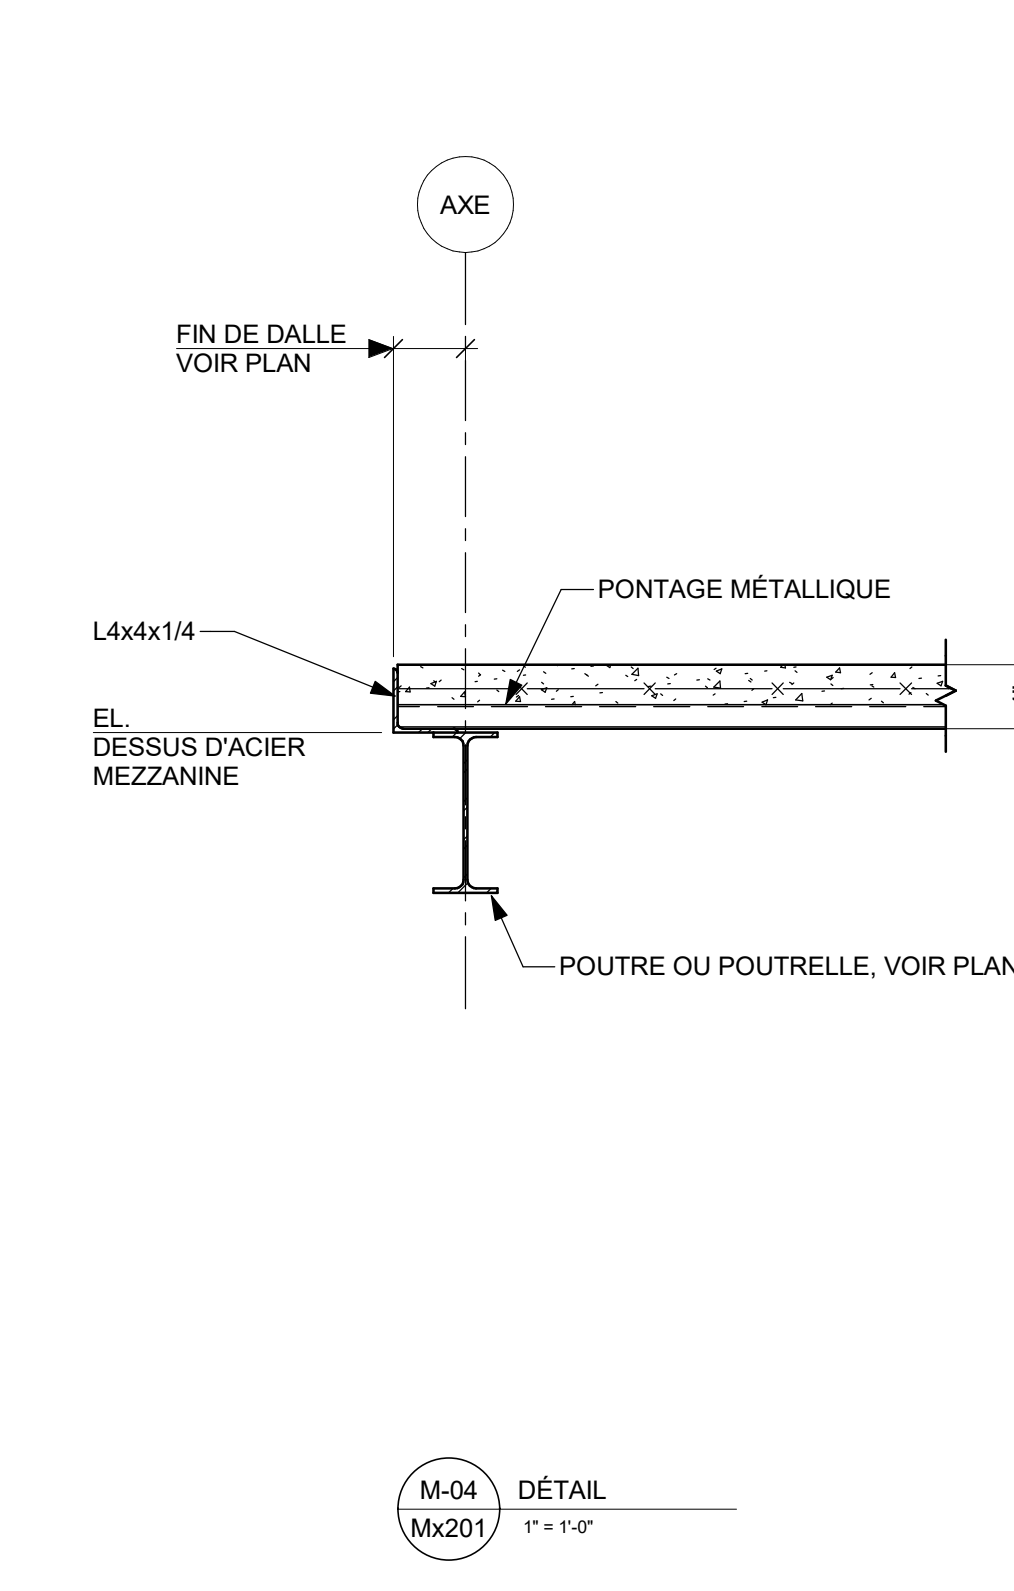
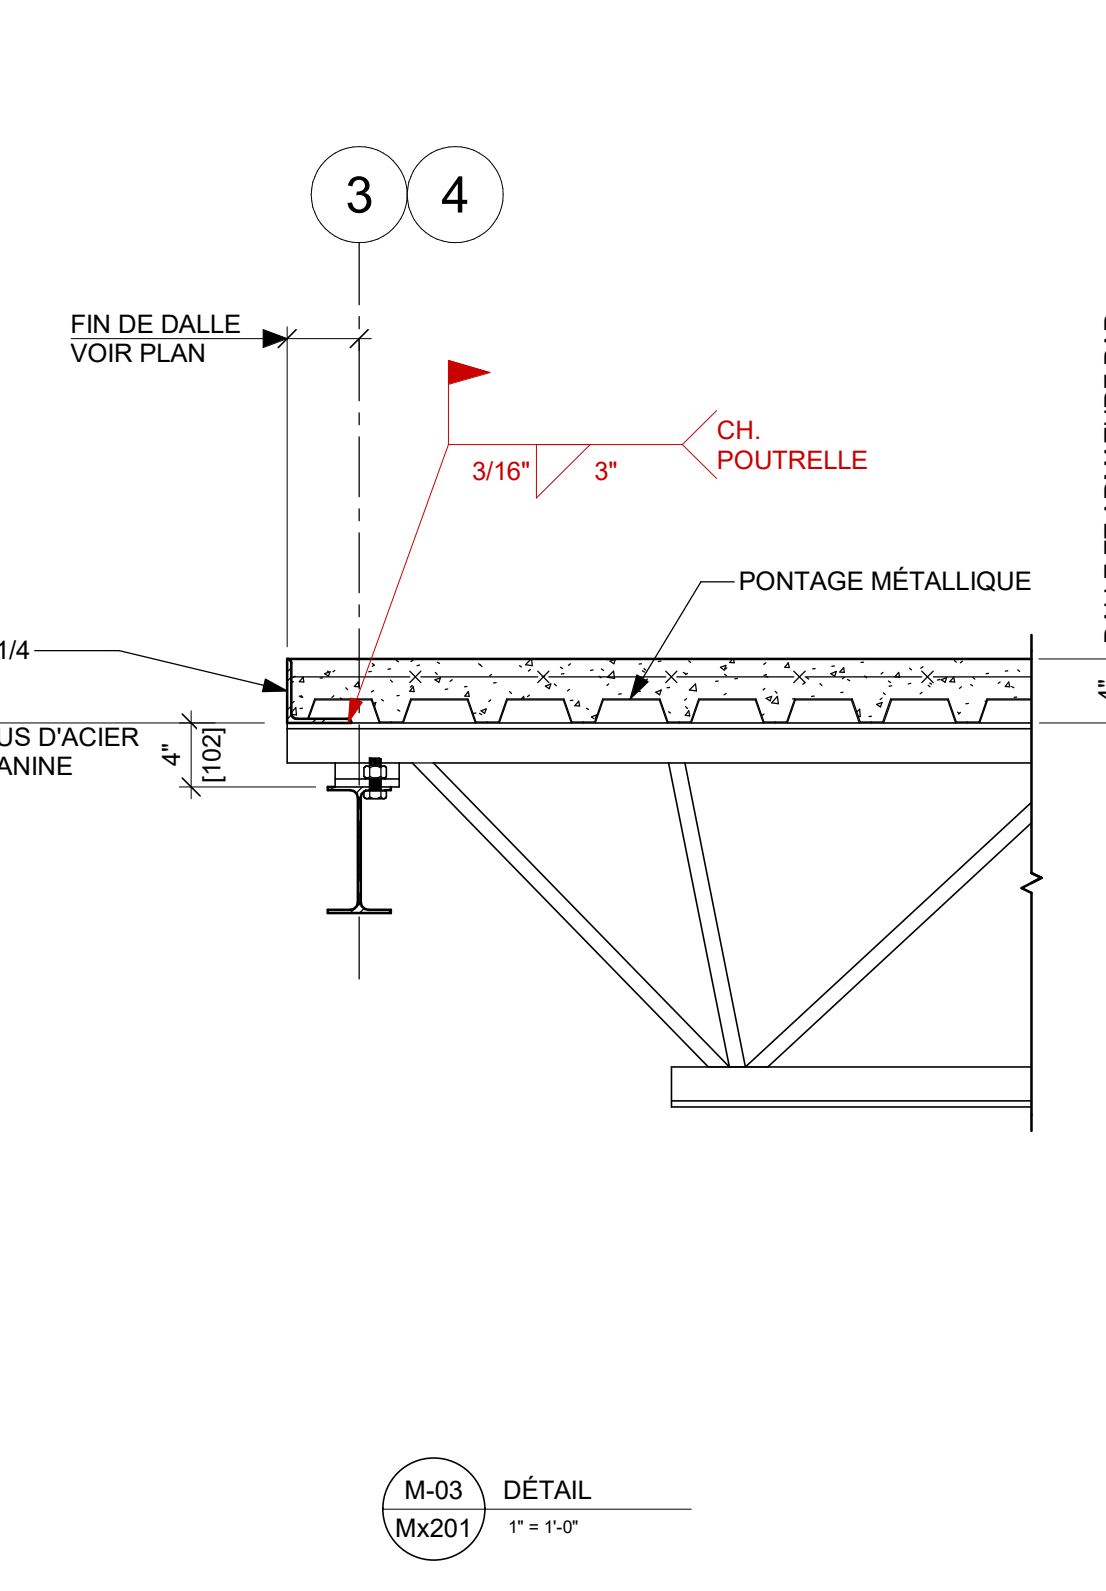
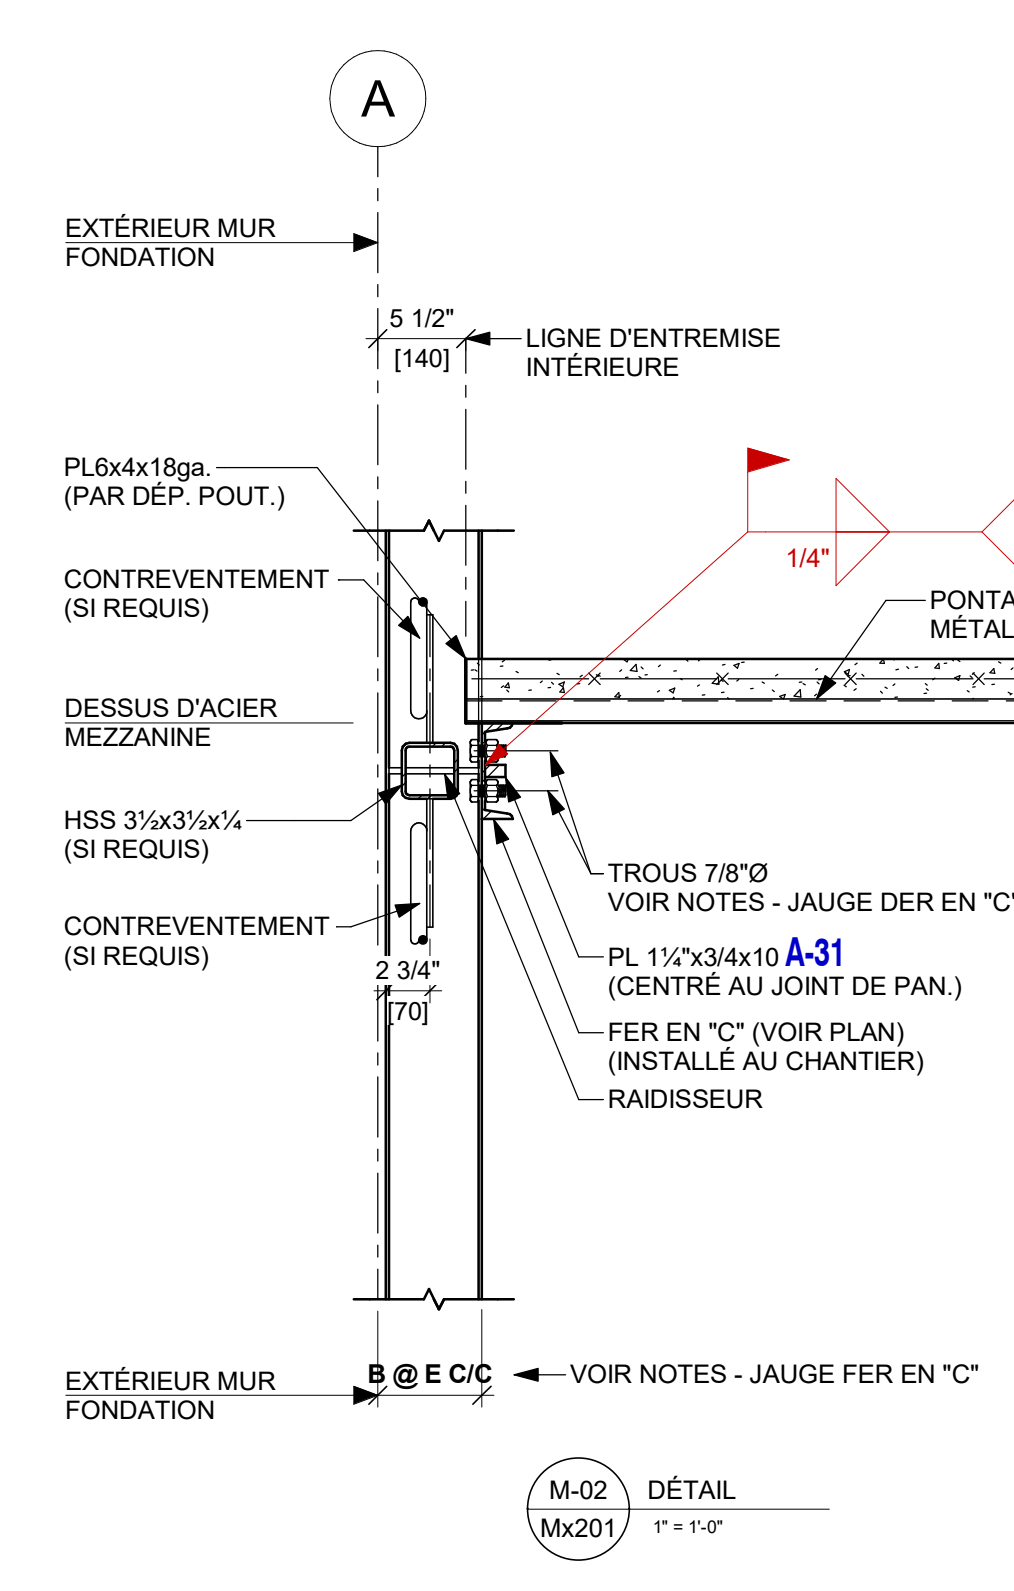
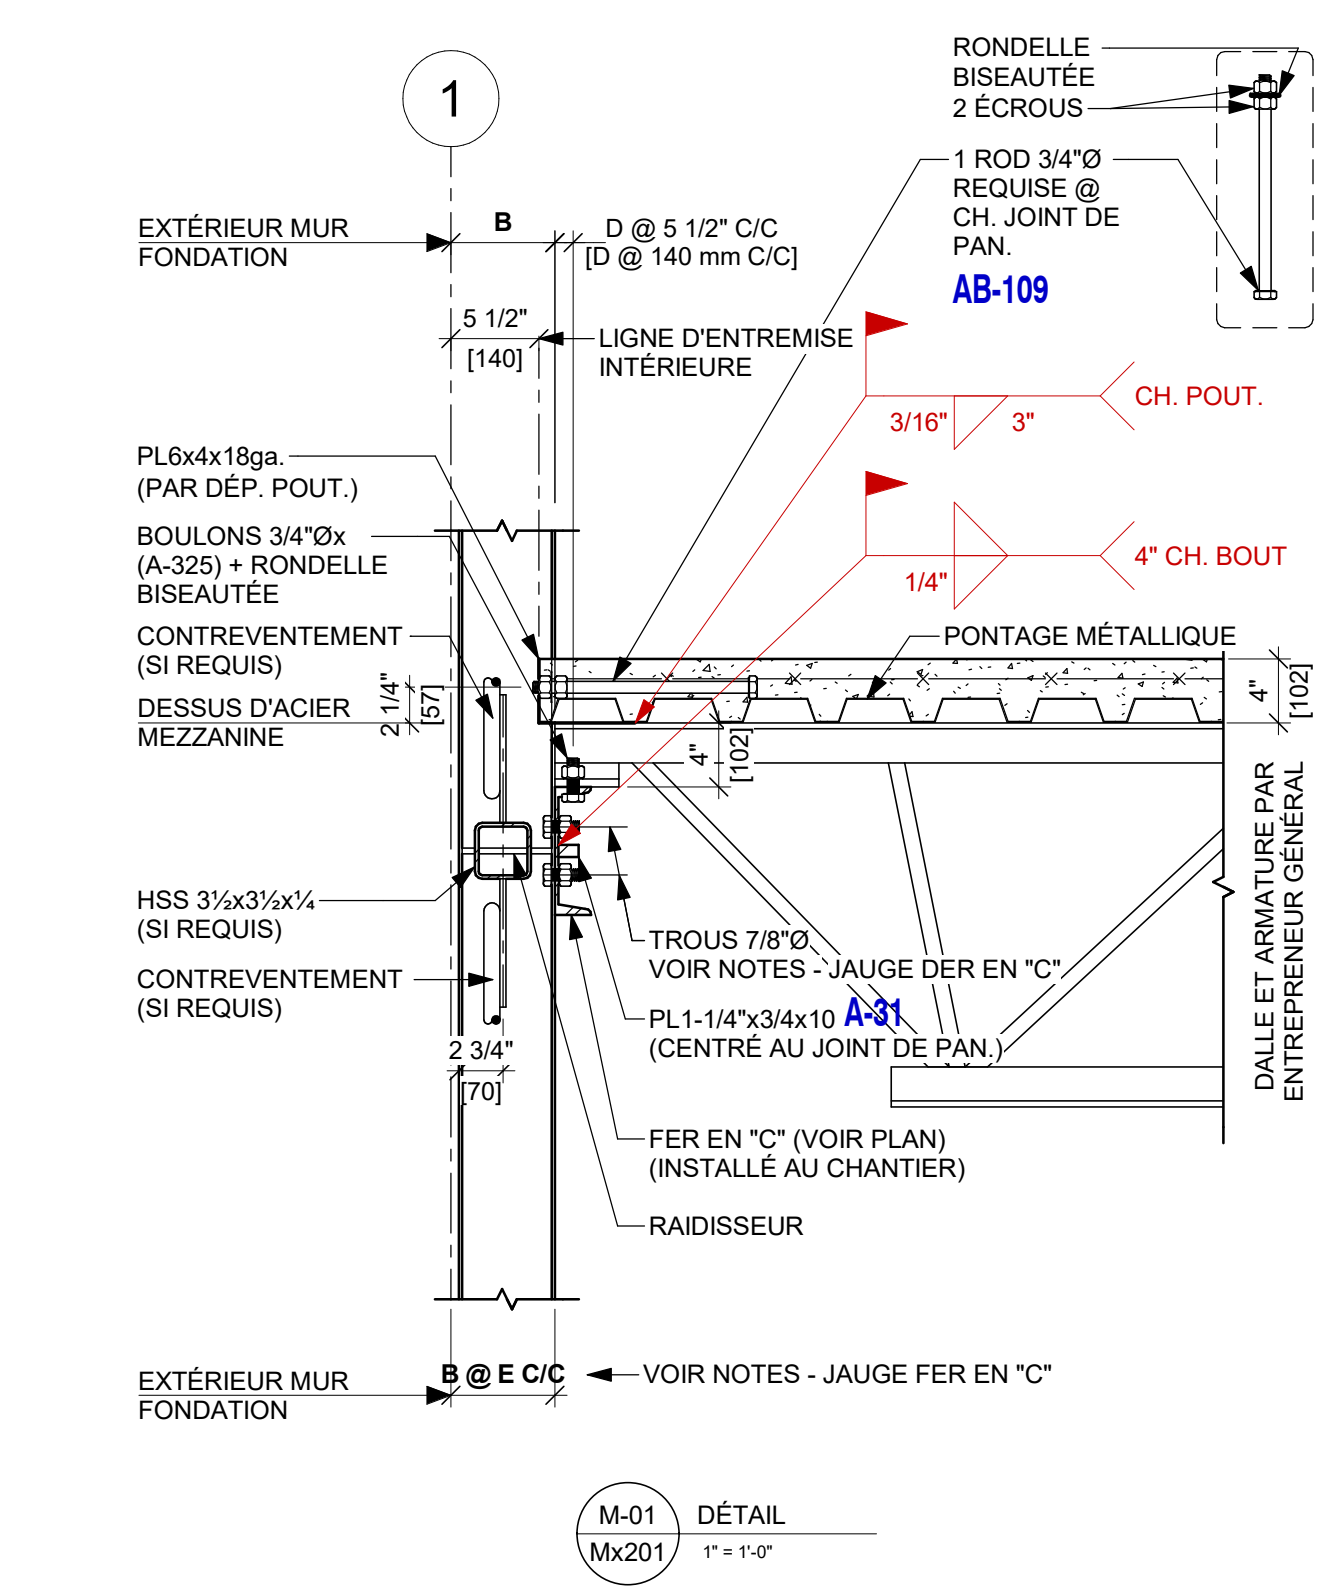


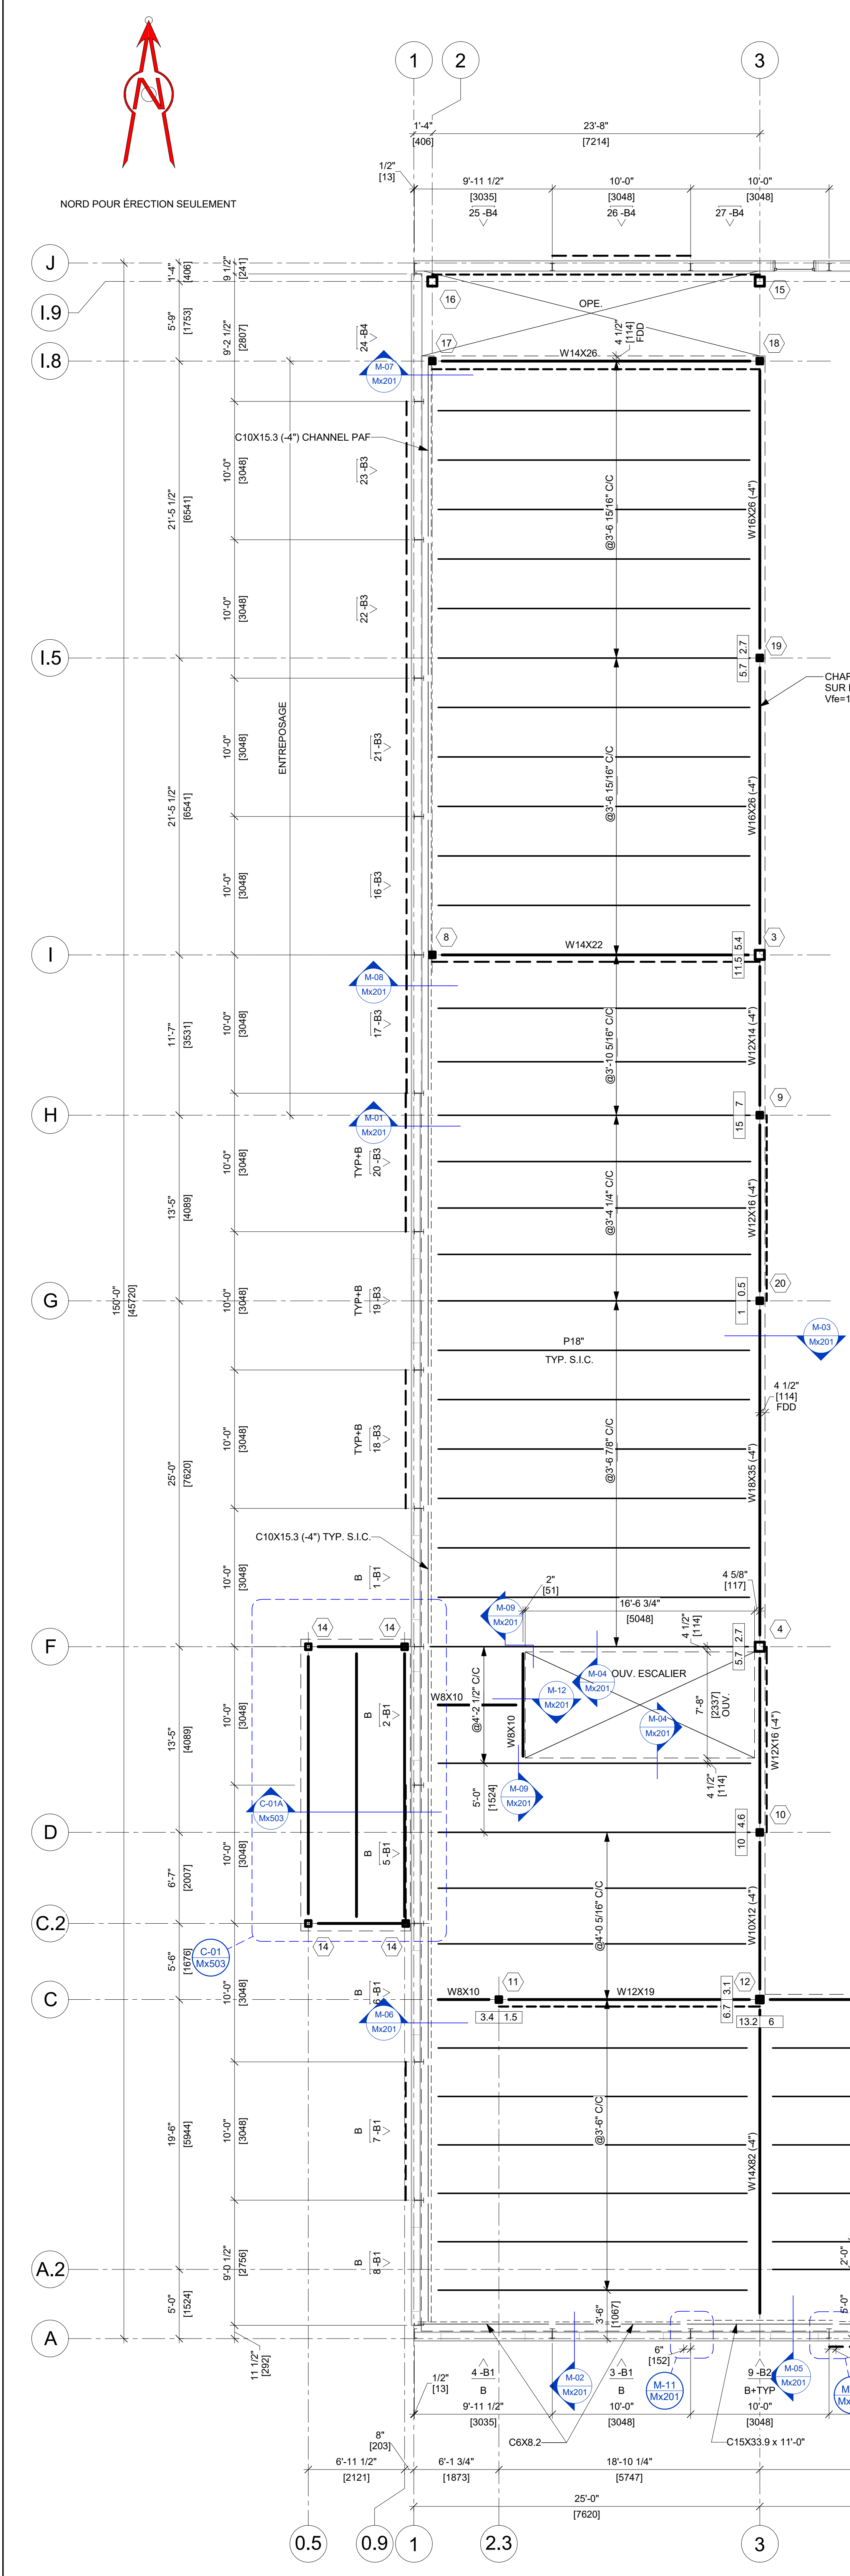

PONTAGE MÉTALLIQUE DE LA MEZZANINE AVEC ACTION DIAPHRAGME

1) NOTES GÉNÉRALES POUR LE PONTAGE

A) LE PONTAGE MÉTALLIQUE EST REQUIS AFIN D'AGIR COMME UN DIAPHRAGME POUR LA DISTRIBUTION DES FORCES LATÉRALES.

B) ☐ PONTAGE SOUDÉ

- LE PONTAGE DOIT ÊTRE SOUDÉ À LA CHARPENTE AVEC DES ÉLECTRODES DE CLASSE E400X.
- LES BOUTONS DE SOUDURE 3/4" DEVONT ÊTRE FAITS PAR UN SOUDEUR QUALIFIÉ PAR LE BUREAU CANADIAN DE LA SOUDURE.
- RETOUCHER LES SOUDURES AVEC DE LA PEAINTURE POUR COUCHE PRIMAIRE.

☐ PONTAGE VISSÉ

- LE PONTAGE DOIT ÊTRE VISSÉ À LA CHARPENTE AVEC DES VIS DE TYPE TEK 5 #12-24x1 1/2".

☒ PONTAGE CLOUÉ

- LE PONTAGE DOIT ÊTRE CLOUÉ À LA CHARPENTE AVEC DES CLOUS DE TYPE HILTI - X-HS24 - 18" (3mm) ≤ 1.5 3/8" (10mm).
- L'ÉRECTEUR EST RESPONSABLE DE LA FIXATION DU PONTAGE À LA CHARPENTE ET DE LA SÉLECTION DU CLOU, DE L'OUTIL, DE LA CARTOUCHE ANSIQUE DE LA RÉGULATION DE LA PUISSANCE DE L'OUTIL, SELON LES SPÉCIFICATIONS DES PRODUITS.

C) LA DISTANCE MINIMUM ENTRE LE CENTRE DES ATTACHES ET LES EXTRÉMITÉS DU PONTAGE DOIT ÊTRE DE 1" MIN.

D) L'ÉRECTION DOIT ÊTRE EN ACCORD AVEC LA PUBLICATION ICTAS 10M-2013, ANSI QU'AVEC TOUS LES AUTRES STANDARDS APPLICABLES.

2) CONFIGURATION DES CONNECTEURS DE PONTAGE AUX ÉLÉMENTS DE SUPPORT

☒ 30/4

☐ 30/7

☐ 30/9

☐ 30/11

3) JOINT DE FEUILLES

LES JOINTS DE FEUILLES DOIVENT ÊTRE VISSÉS :

☐ VIS TEK 2 #10-16 x 12"

☒ HILTI S-SLO 01 M HWH (22 ja., 20 ja. & 18 ja.)

☒ HILTI S-SLO 02 M HWH (16 ja.)

4) ATTACHES AU PÉRIMÈTRE

A) ATTACHER LE PONTAGE MÉTALLIQUE À LA MEMBRE DE PÉRIMÈTRE À CHAQUE NERVURE.

B) ATTACHER LE PONTAGE MÉTALLIQUE À LA MEMBRE DE PÉRIMÈTRE @ 6" C/C

C) ATTACHER LE PONTAGE MÉTALLIQUE À LA MEMBRE DE PÉRIMÈTRE DE L'OUVERTURE @ 6" C/C

POUR DÉTAILLAGE DES PANNEAUX

PLAN DE MEZZANINE

PONTAGE MÉTALLIQUE P-3608, 22 JA., GALVANISÉ (G-90) COMPOSITE PORTÉE TRIPLE, TYP. S.I.C. DESSUS D'ACIER EL. 111'-6" (13505 mm)




CHARGES DE CONCEPTION À LA MEZZANINE

BUREAU (1 @ 3 / A @ H) : CHARGE MORTE = 70 #/sq' CHARGE VIVE = 90 #/sq' DÉFLEXION SOUS LA CHARGE VIVE = L/360

ENTREPOSAGE (ENTRE H & I.8 ET ENTRE 3 & 4) : CHARGE MORTE = 50 #/sq' CHARGE VIVE = 100 #/sq' DÉFLEXION SOUS LA CHARGE VIVE = L/360

NOTES GÉNÉRALES POUR LA DALLE DE BÉTON SUR TABLIER MÉTALLIQUE (PAR D'AUTRES)

- RÉSISTANCE MINIMALE DU BÉTON EN COMPRESSION (F_c) 28 jours : 3600 psi
- TREILLIS REQUIS : 1 RANG-6#6 TYP. S.I.C.
- LE RECOURVEMENT MINIMAL DU TREILLIS PAR RAPPORT AU DESSUS DE LA DALLE DOIT ÊTRE COMPRIS ENTRE 3/4" ET 1 1/2".
- CURE HUMIDE DU BÉTON : MINIMUM DE 7 JOURS POUR BÉTON NON-APPARENT MINIMUM DE 28 JOURS POUR BÉTON APPARENT (EXEMPLE : BÉTON POLI).

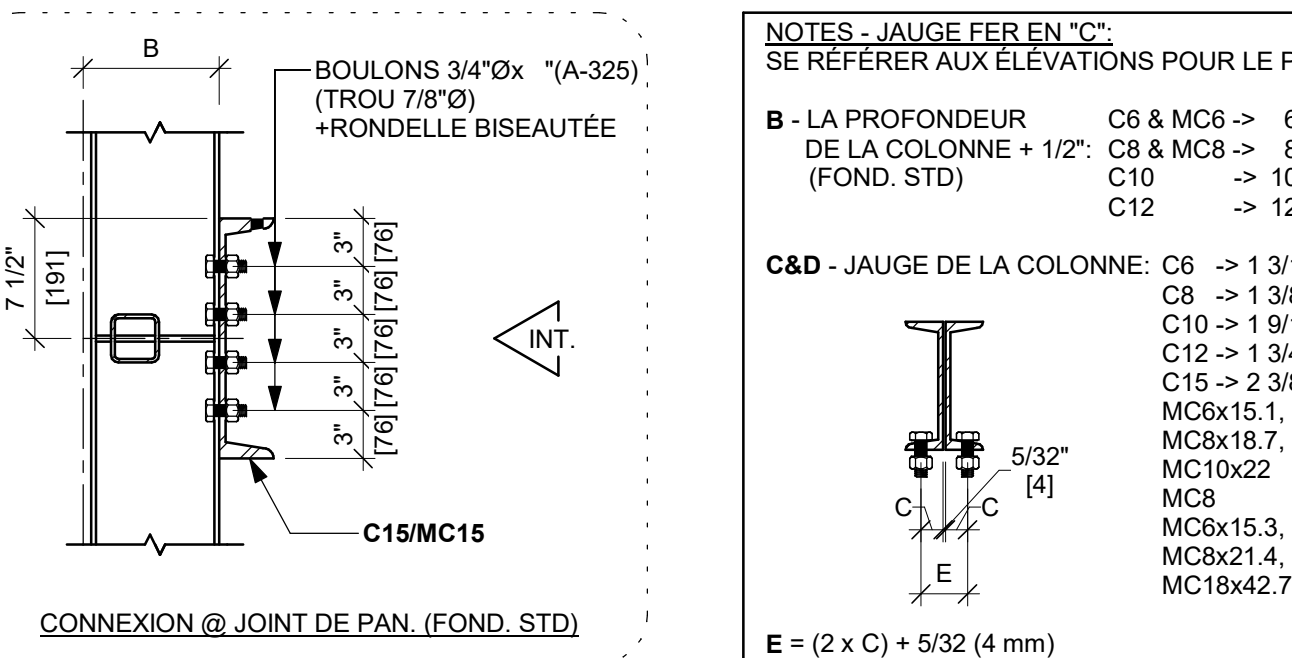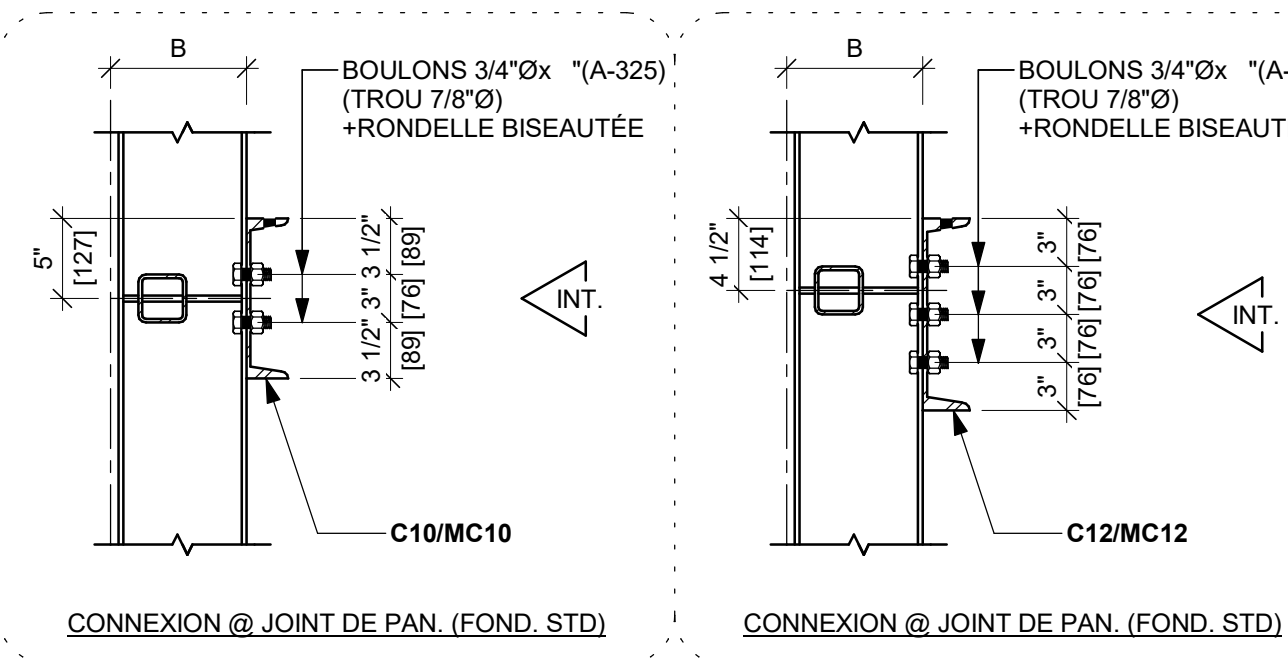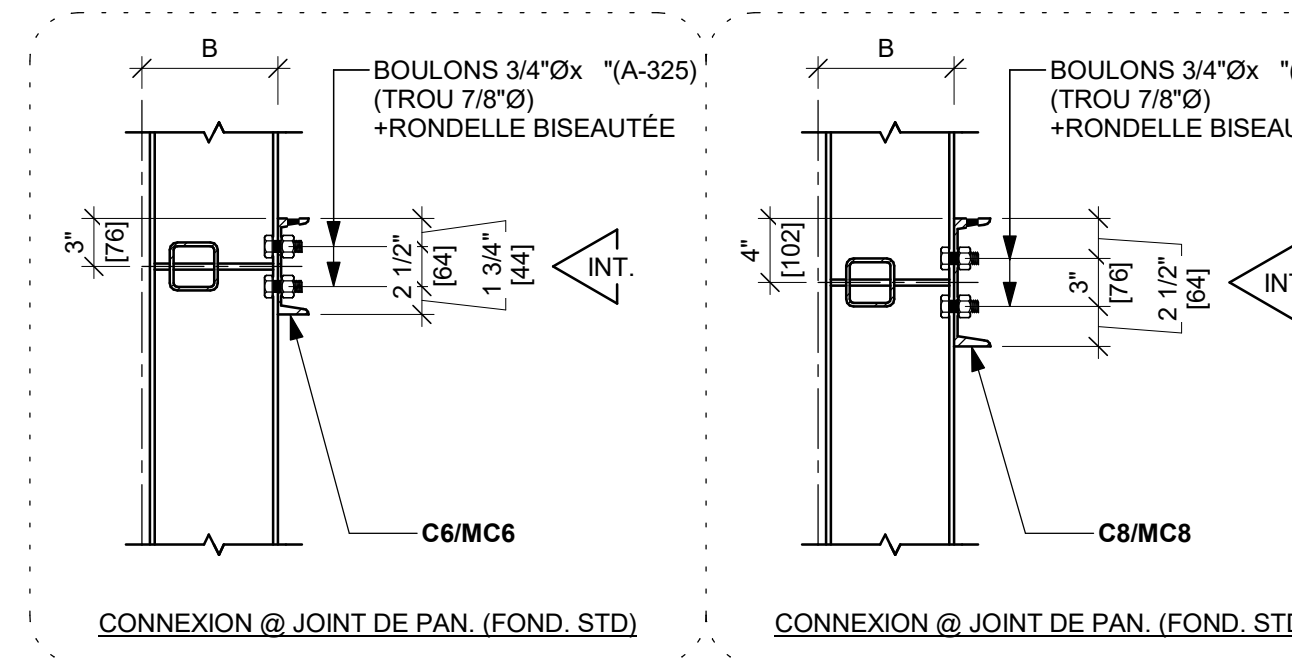

LÉGENDE PLAN DE MEZZANINE

SS = Siège spécial

P_X = Poutrelle _X = profondeur

PA = Poutrelle d'attache

EL = Élévation

COL = Colonne


E = Charge axiale sismique (kips) non pondérée

E-W = Charge axiale sismique (kips) non pondérée

W = Charge axiale vent (kips) non pondérée

* = Voir notes charges de design :

- 6 - Données sismiques, connexions
- <X> = Réaction pondérée RI (kips)

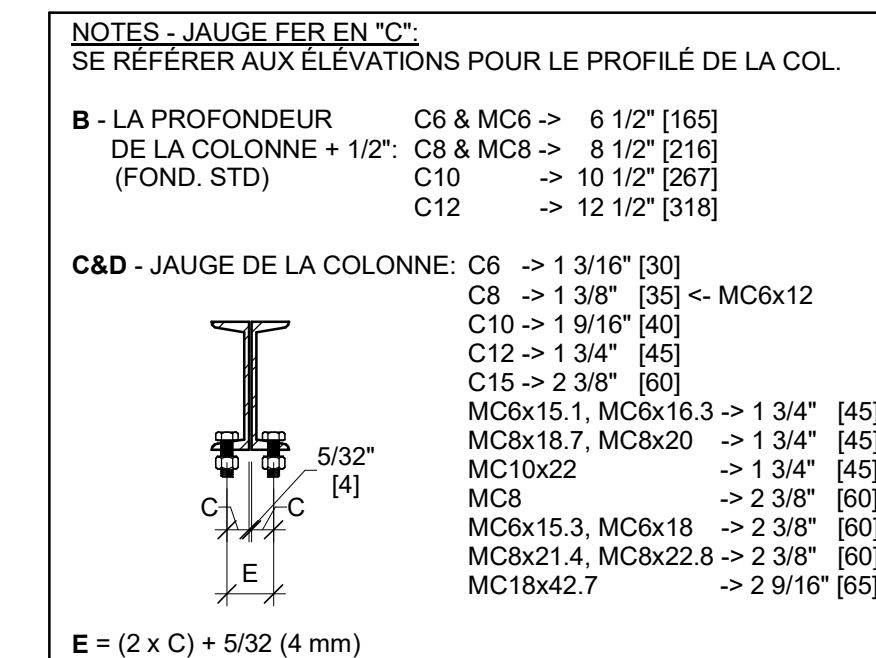

B	2025-09-02	POUR DÉTAILLAGE DES PANNEAUX	C.R.	E.G.
A	2025-08-25	POUR APPROBATION	S.G.	E.G.
DESIGNER	CAD	DESCRIPTION	DESIGN	VER
JEAN-CHRISTOPHE RODRIGUE jean-christophe.rodrique@canam.com Téléphone : (418) 228-8031, Cellulaire : (438) 864-4858 Sans frais : (877) 499-6049 Télécopieur : (418) 228-1750				
DESIGN	CONÇU PAR	INGÉNIEUR DU PROJET	ECHAPE	
DESIGNÉ PAR	CORINA FUIU	PASCAL JACQUES	MARTIN COUTURE	COMME INDICÉ
VÉRIFIÉ PAR	EMIE GAGNON	AUPONT	DATE (signature)	05/08/2024
CLIENT :				
 11505, 1re Avenue, bureau 500, Saint-Georges Beauca Québec, Canada G5Y 7A5 Téléphone : (418) 228-8031 Sans frais : (877) 499-6049 www.canam.com				
SCAUX PROFESSIONNEL				
PROJET				
NOUVELLE USINE LACMARK INC. ST-GEORGES, QUÉBEC				
TITRE				
PLAN DE MEZZANINE ET DÉTAILS				
NUMÉRO CONTRAT	POUVOIR-000	NUMÉRO DESIGN	DIVISION	REVISION
242536		Mx201		B