




TITLE BLOCK: 863 6mm x 558 9mm EJV 2019

5/22/2020 3:33:05 PM BSM 360/UTM/21026-10 - CLE - R106A000-S-NEXT-04

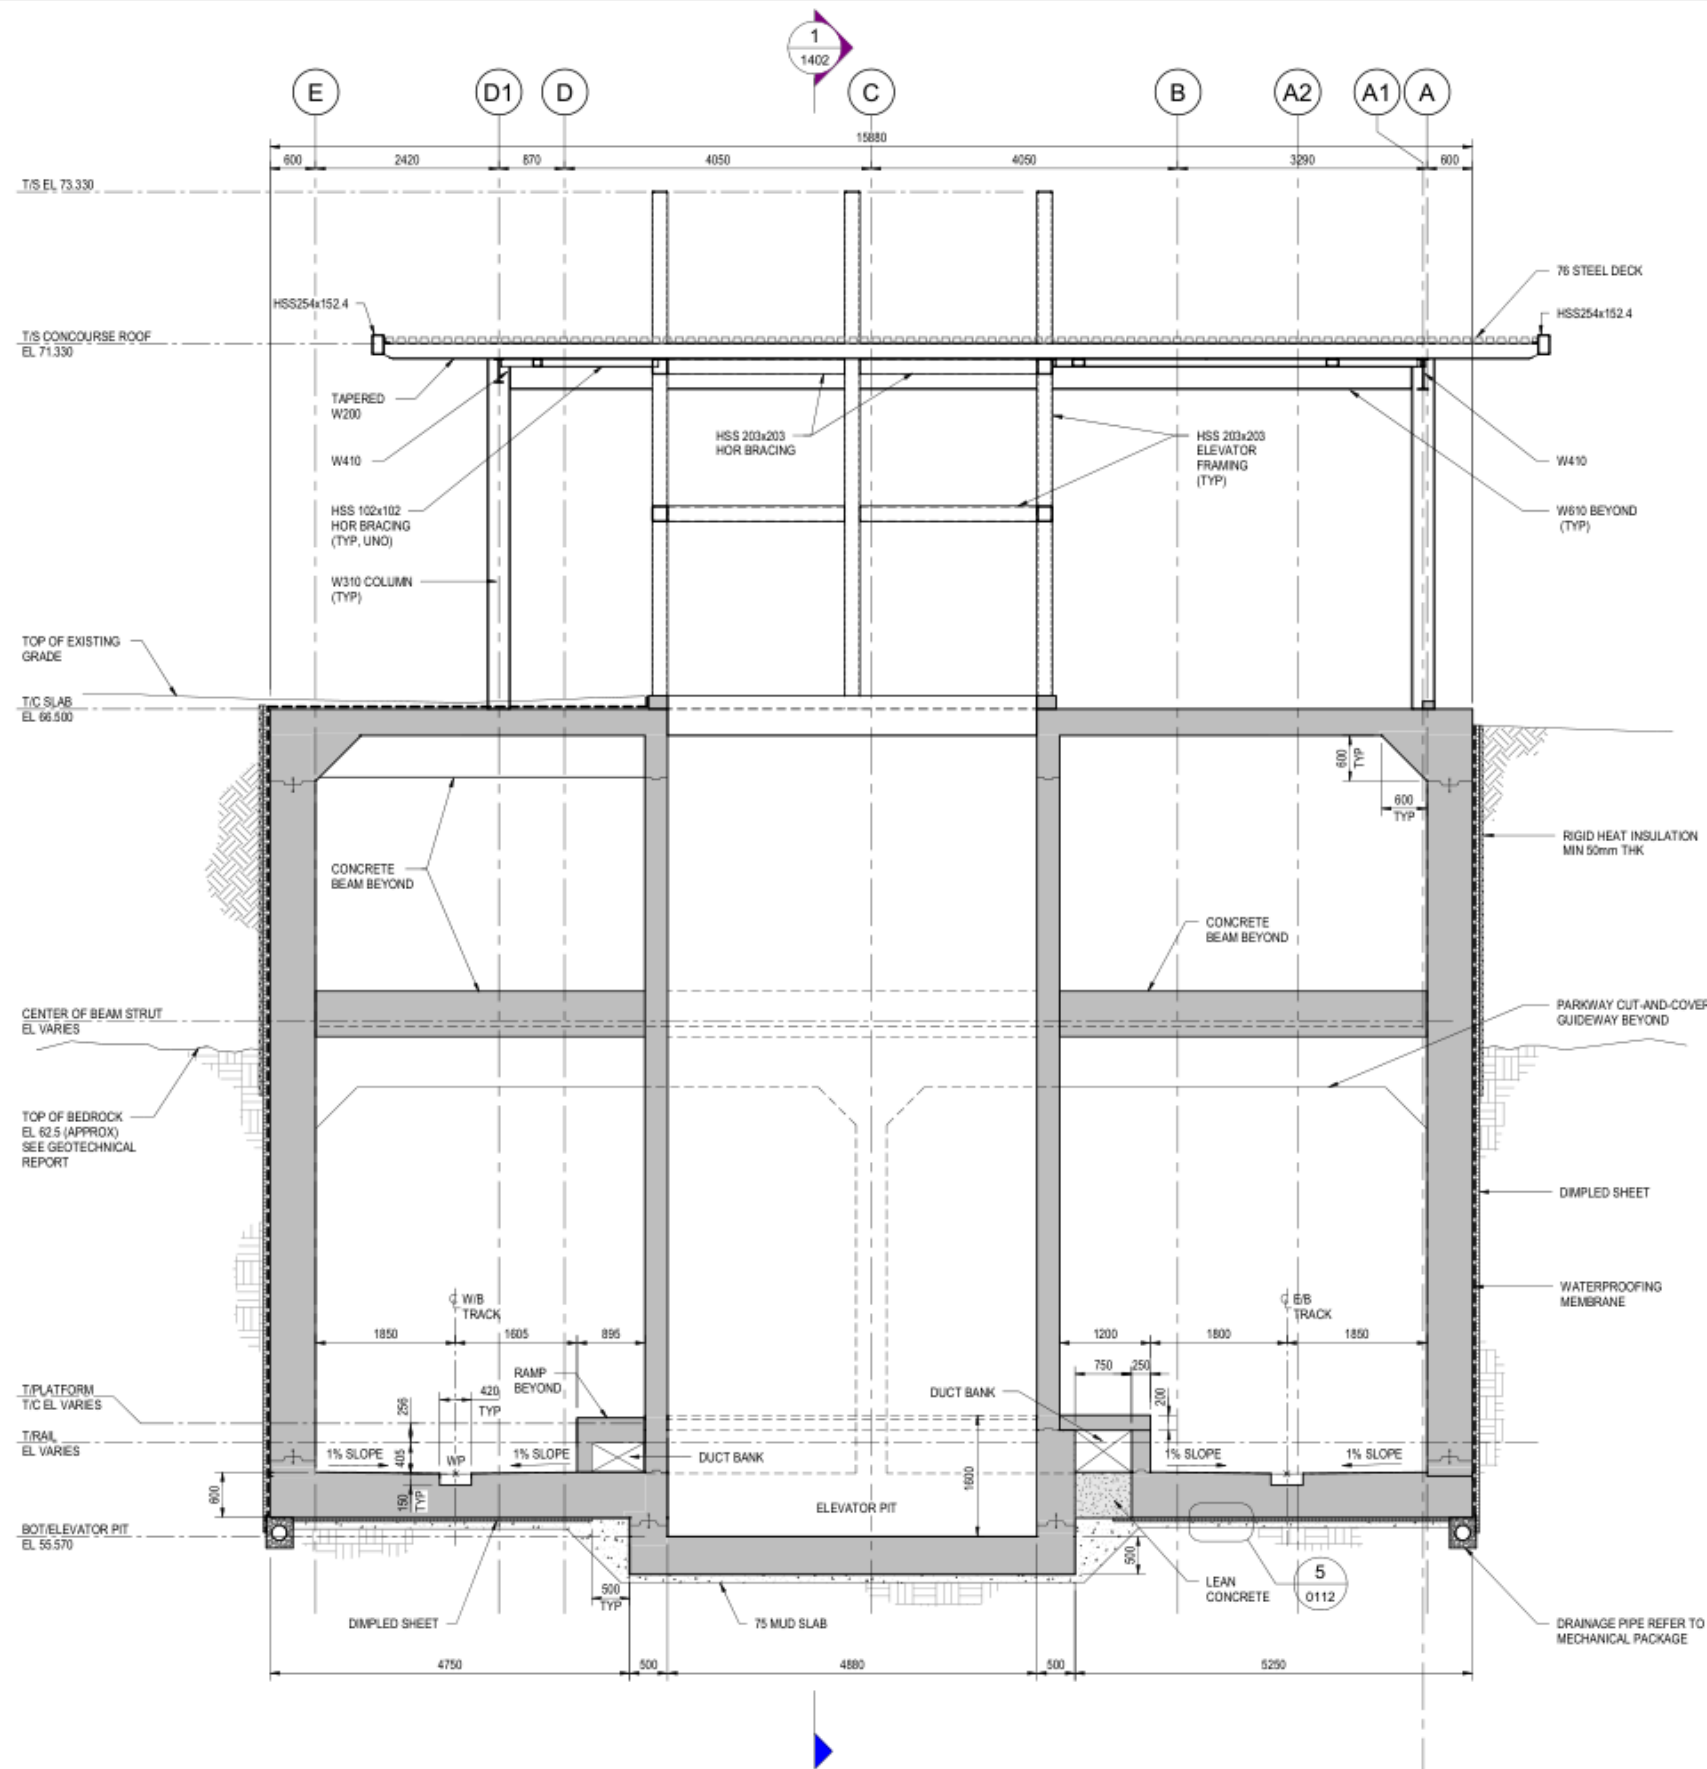


1 CROSS SECTION
1200 1:50



SCALE
0m 2.5m
1:50
1:100

REV	DESCRIPTION
A	ISSUED FOR PRE-FINAL DESIGN DEVELOPMENT - DB/JV REVIEW
B	ISSUED FOR PRE-FINAL DESIGN DEVELOPMENT - CITY REVIEW

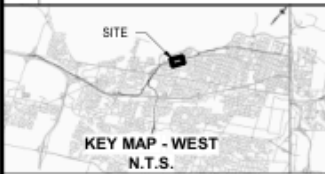

NO PART OF THIS DOCUMENT MAY BE REPRODUCED, PUBLISHED, RETRIEVAL SYSTEM, OR TRANSMITTED IN ANY FORM BY ANY MEANS, ELECTRONIC OR MECHANICAL, INCLUDING PHOTOCOPYING, RECORDING, OR OTHERWISE WITHOUT THE WRITTEN PERMISSION OF THE DESIGNER.

LAYOUT INFORMATION BASED ON 3 DEGREE ORIGINAL COORDINATE SYSTEM. COM

PRELIMINARY
NOT FOR CONSTRUCTION
2020-05-18

NOTE:
1. FOR GENERAL NOTES, SEE DWG EJV-S2STNE-STR-DWG-1410