




TITLEBLOCK 883.6mm x 558.8mm EJV 2019

BIM 360://TM-0102-10 - CLE - R19MOD-S-WEST.rvt

5/12/2020 3:35:5 PM

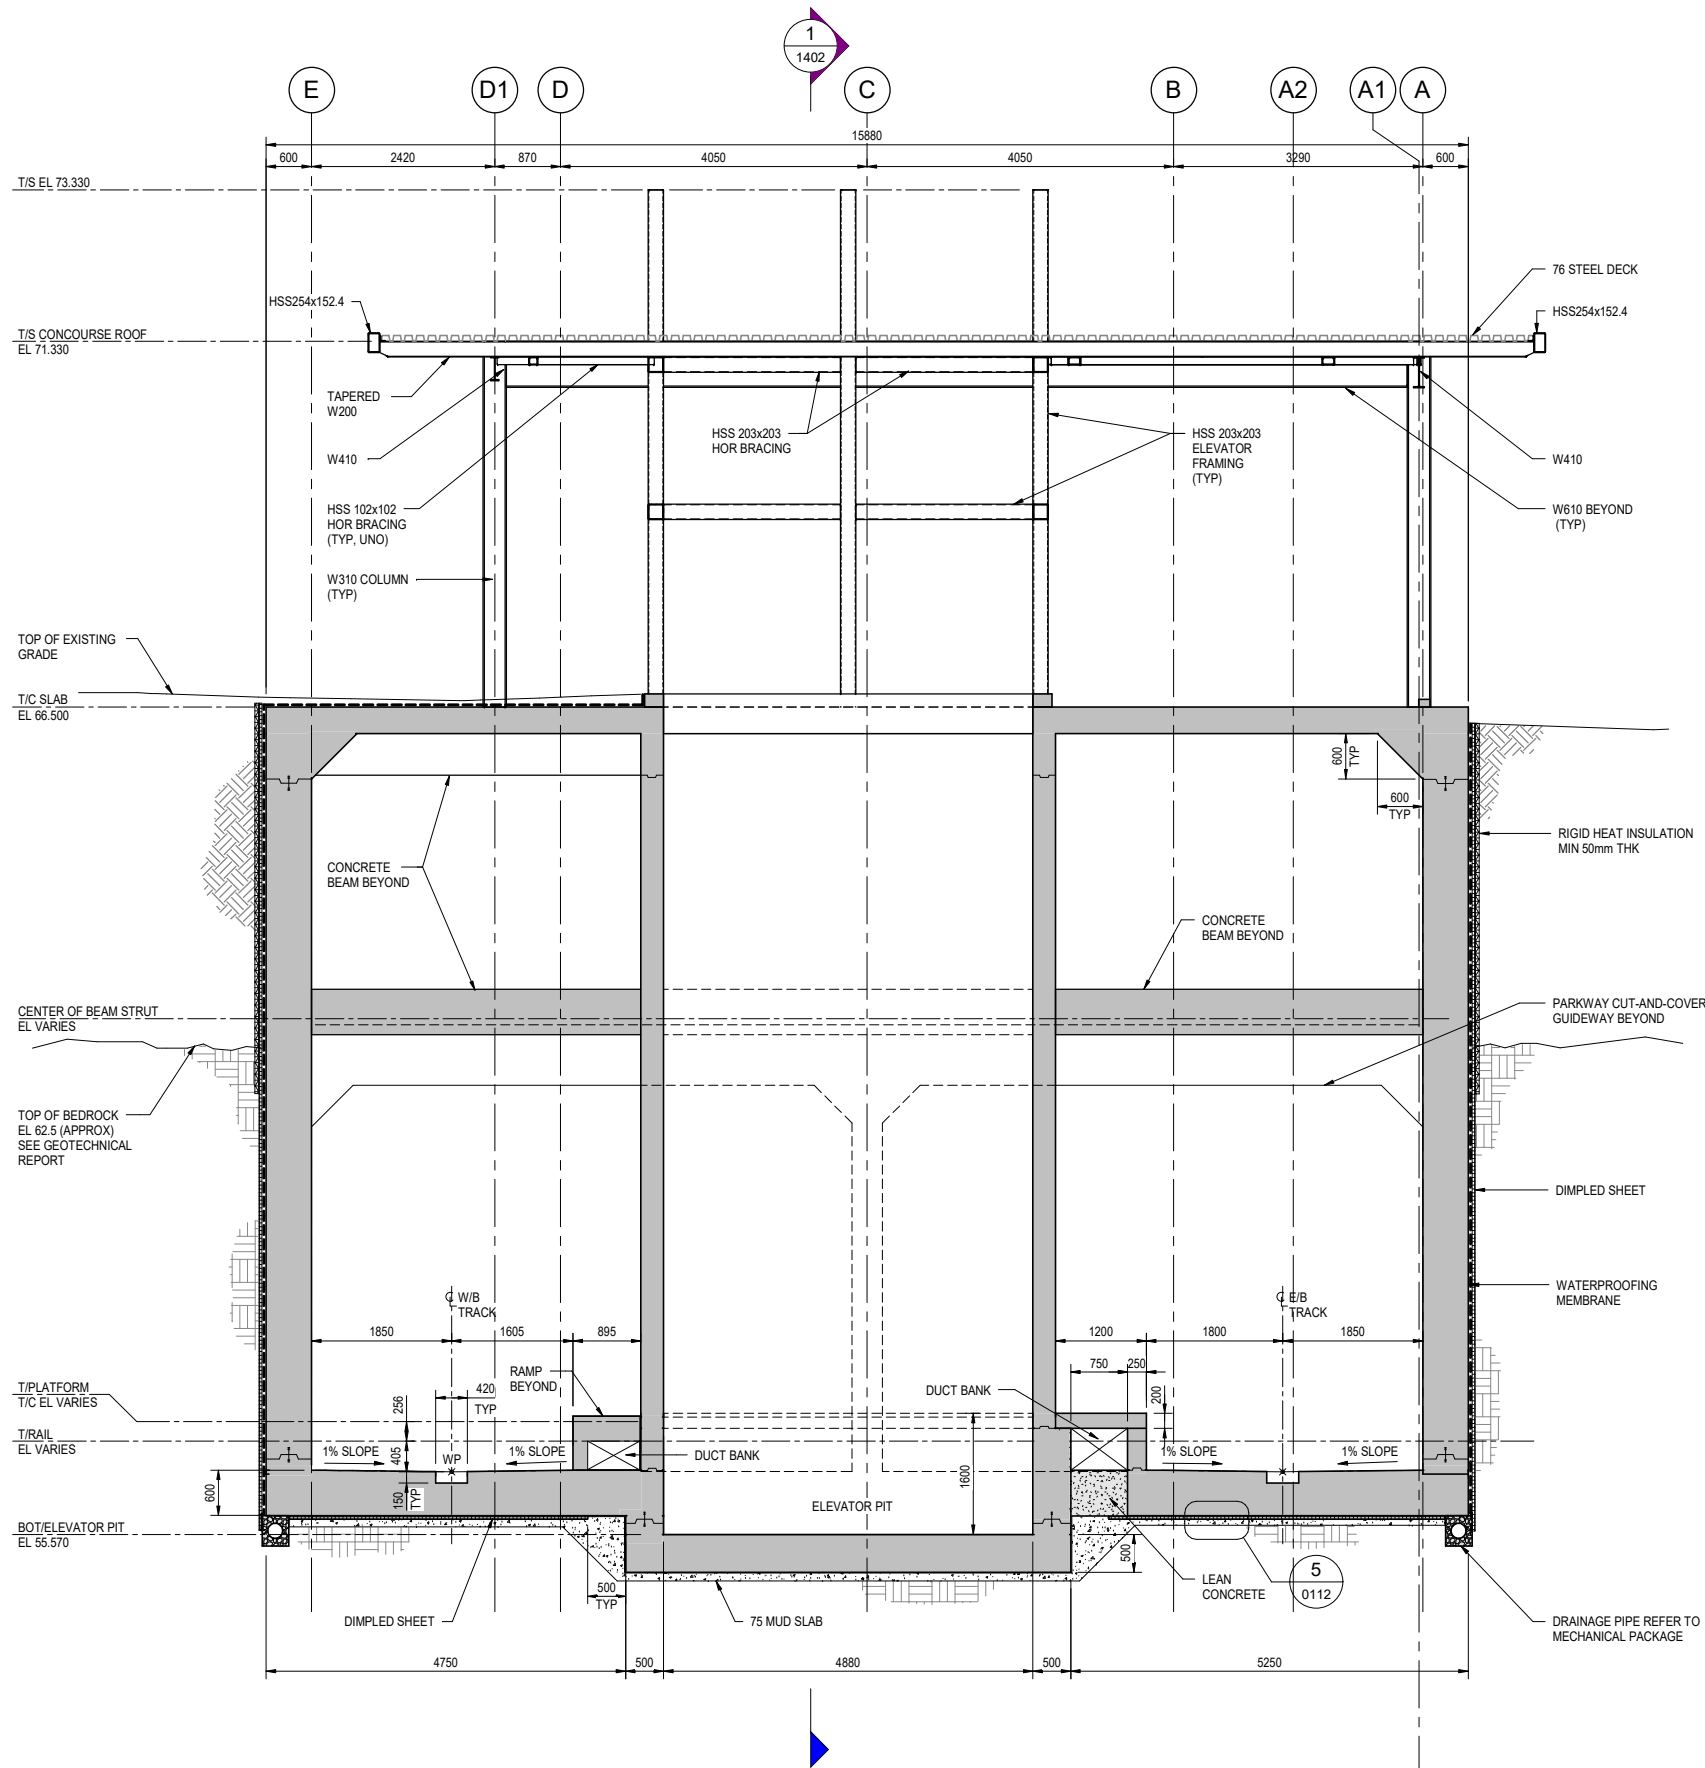

1 CROSS SECTION
1200 1:50

STAGE 2

Confederation EAST

Confederation WEST

Ottawa

DRAWING NAME

NEW ORCHARD STATION
SEGMENT 2

CROSS SECTION

DRAWING NUMBER

EJV-S2STNE-STR-DWG-1410

ENGINEERING JV

SCALE

1:50 22"x34"
1:100 11"x17"

REV

DESCRIPTION

BY

DATE

A

ISSUED FOR PRE-FINAL DESIGN DEVELOPMENT - DBJV REVIEW

JA

2020-04-20

B

ISSUED FOR PRE-FINAL DESIGN DEVELOPMENT - CITY REVIEW

JA

2020-05-18

SITE

KEY MAP - WEST
N.T.S.

KEY MAP - EAST
N.T.S.

NO PART OF THIS DOCUMENT MAY BE REPRODUCED, PUBLISHED, CONVERTED, OR STORED IN ANY DATA RETRIEVAL SYSTEM, OR TRANSMITTED IN ANY FORM BY ANY MEANS (ELECTRONIC, MECHANICAL, PHOTOCOPYING, RECORDING, OR OTHERWISE) WITHOUT THE PROPER WRITTEN PERMISSION.

LAYOUT INFORMATION BASED ON 3 DEGREE MTM ZONE 9 NAD 83
ORIGINAL COORDINATE SYSTEM. COMBINED SCALE FACTOR 0.9999

PRELIMINARY
NOT FOR CONSTRUCTION

2020-05-18

CONTRACT No.

LRT19-1019

DESIGNED

P. PARNIAN

CHECKED

J. ASPIOTIS

DRAWN

I. BALTAZAR

SEALED

PRIMARY SEAL

SECONDARY SEAL (IF REQUIRED)

ASSET No.

ASSET GROUP

NOTE:
1. FOR GENERAL NOTES, SEE DWG EJV-S2STNE-STR-DWG- 0101 AND 0102.