





TITLE BLOCK: 863.6mm x 558.8mm EJV 2019

BSM 360.017M4-21026-10 - CLE - R106A000-S-NEXT-04


5/12/2020 3:12:19 PM

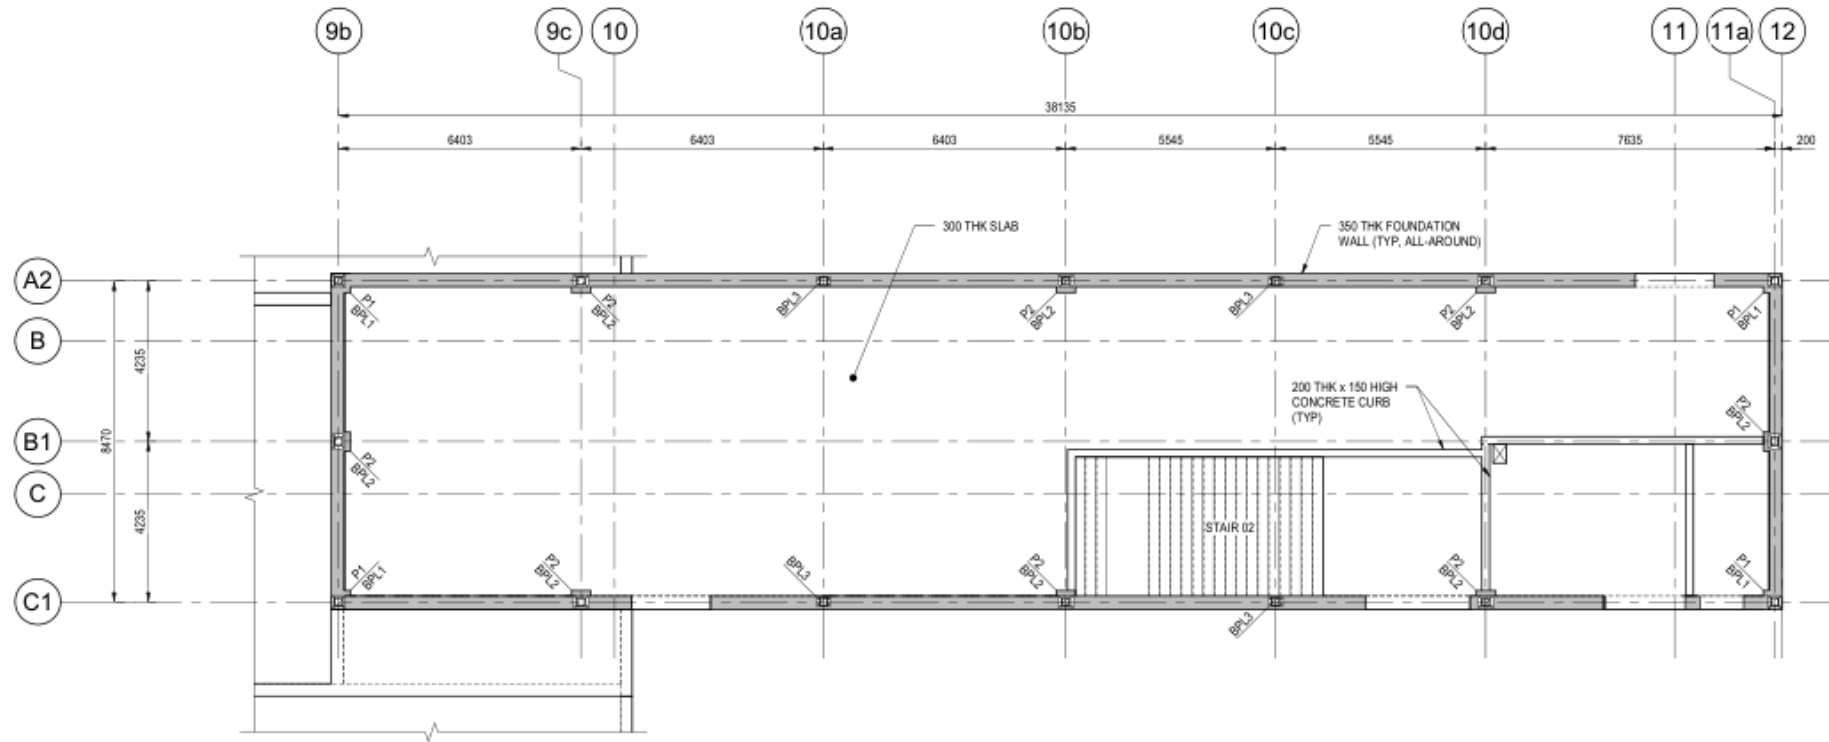


1 EAST SERVICE BUILDING - FOUNDATION PLAN
1270 1:100

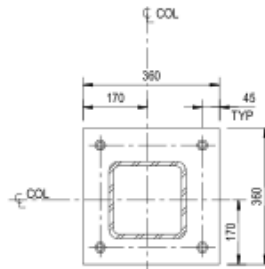

2 DETAIL
1270 1:10
BASE PLATE BPL1
(SEE NOTE 2)

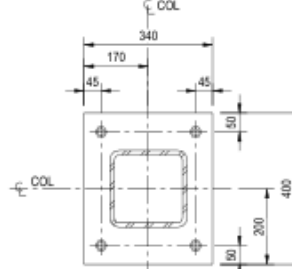

3 DETAIL
1270 1:10
BASE PLATE BPL2
(SEE NOTE 2)

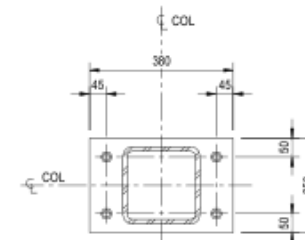


4 DETAIL
1270 1:10
BASE PLATE BPL3
(SEE NOTE 2)



SCALE
AS NOTED
AS NOTED

REV	DESCRIPTION
A	ISSUED FOR PRE-FINAL DESIGN DEVELOPMENT - DB/JV RE
B	ISSUED FOR PRE-FINAL DESIGN DEVELOPMENT - CITY REV

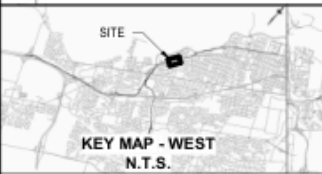

NO PART OF THIS DOCUMENT MAY BE REPRODUCED, PUBLISHED, RETRIEVAL SYSTEM, OR TRANSMITTED IN ANY FORM BY ANY MEANS, ELECTRONIC OR MECHANICAL, INCLUDING PHOTOCOPYING, RECORDING, OR OTHERWISE, WITHOUT THE WRITTEN PERMISSION OF THE ENGINEER.

LAYOUT INFORMATION BASED ON 3 DE
ORIGINAL COORDINATE SYSTEM. COM

PRELIMINARY
NOT FOR CONSTRUCTION
2020-05-18

- NOTE:
- FOR GENERAL NOTES, SEE DWG EJV-S2STNE-STR-DWG-1270-01
 - FOR BASEPLATE ORIENTATION AND LOCATION, SEE DWG EJV-S2STNE-STR-DWG-1270-02