





PRELIMINARY
NOT FOR CONSTRUCTION
2020-05-18

NOTE:


1. FOR GENERAL NOTES, SEE DWG EJV-S2STNE-5

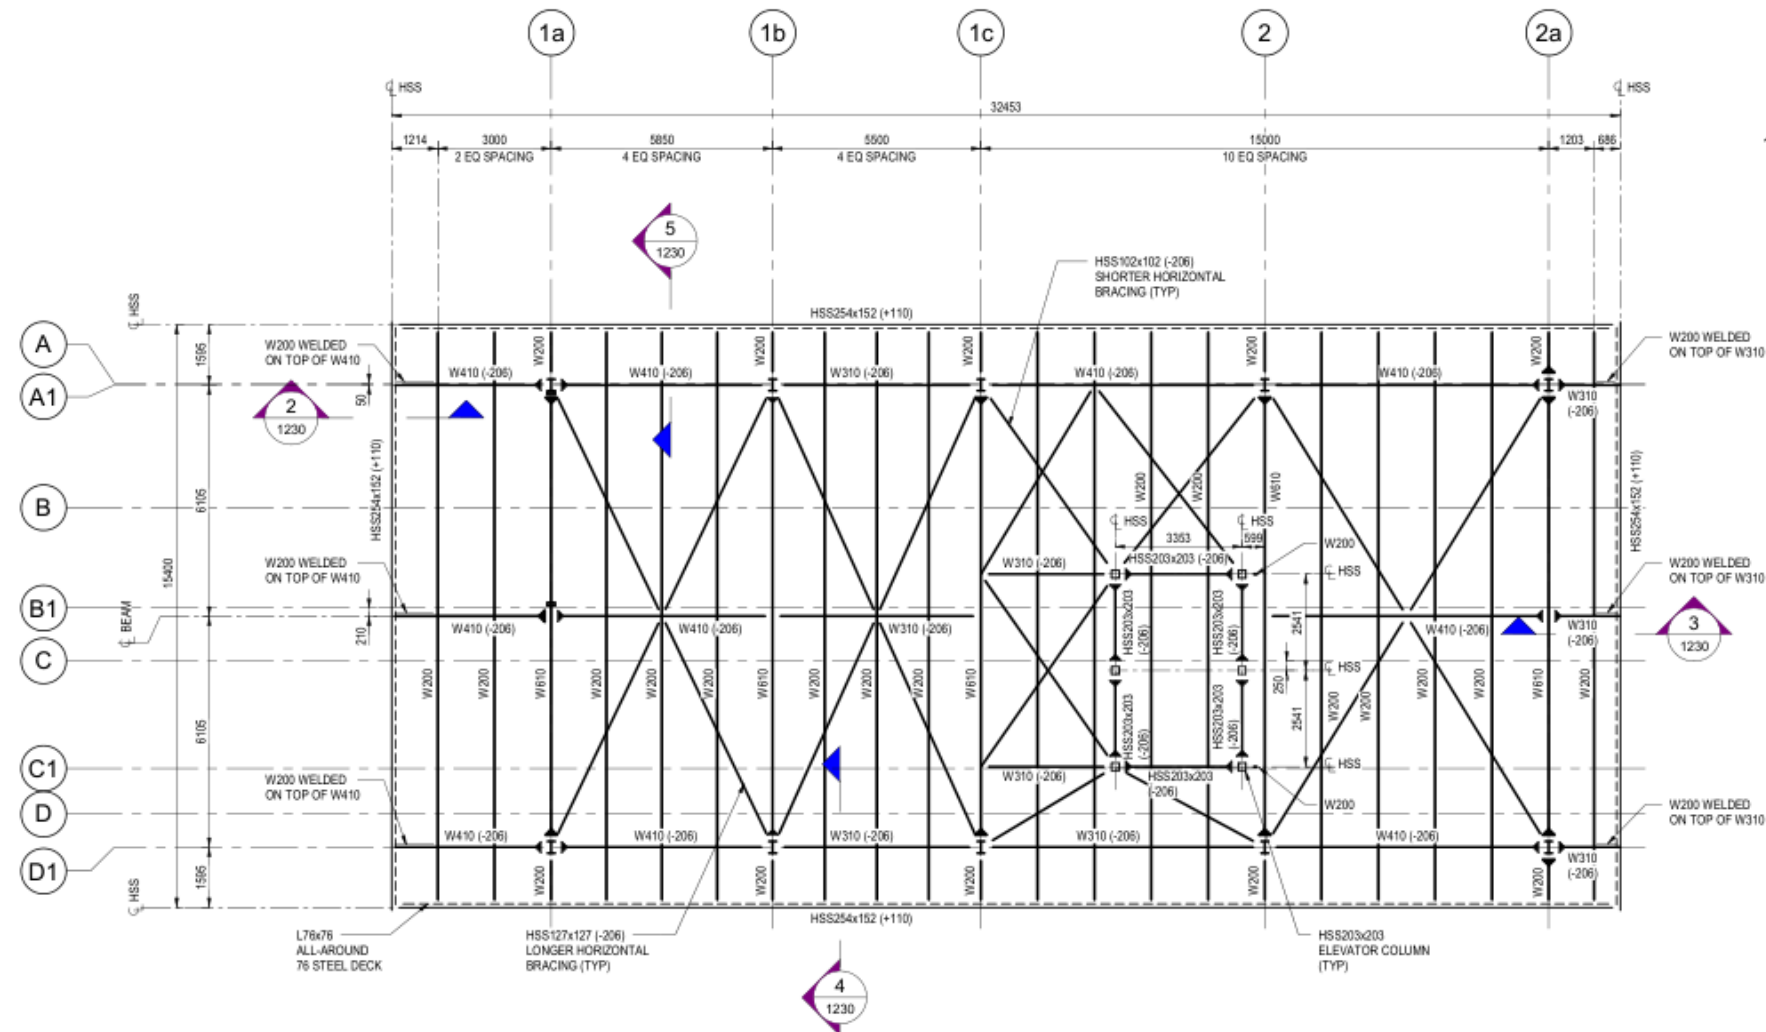

1 ROOF FRAMING PLAN - CONCOURSE (T/S EL 71.330)
1230 1:100

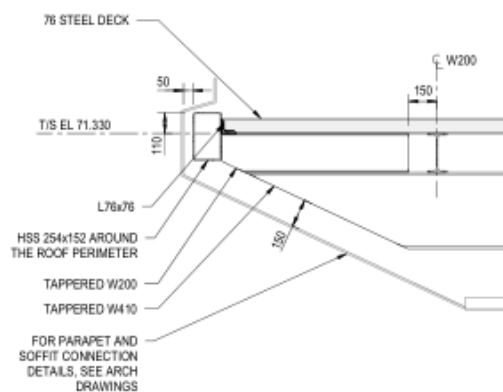


2 DETAIL
1230 1:20

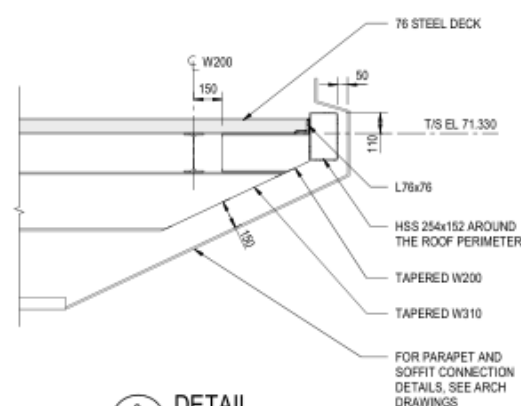


3
1230

DETAIL
1 : 20

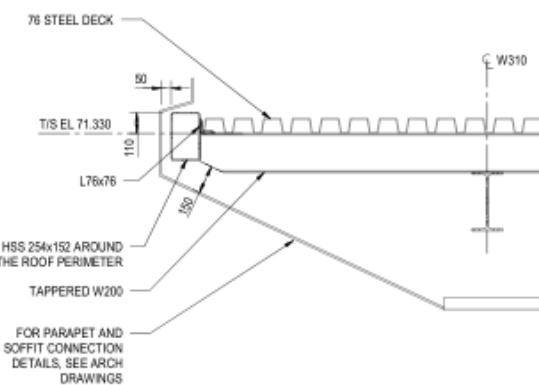

4 DETAIL
1230 1:20

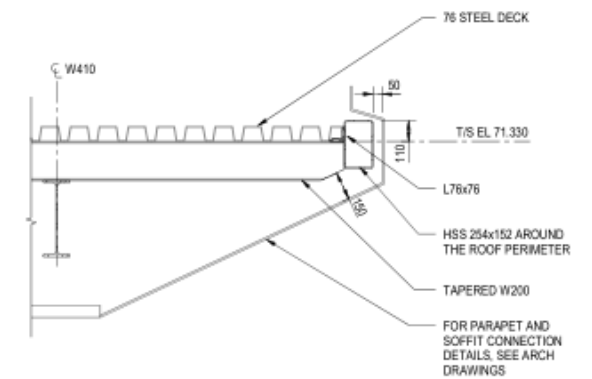

5 DETAIL
1230 1 : 20