




4 S4001 ELEVATION ON LINE A
Scale: 1 : 300

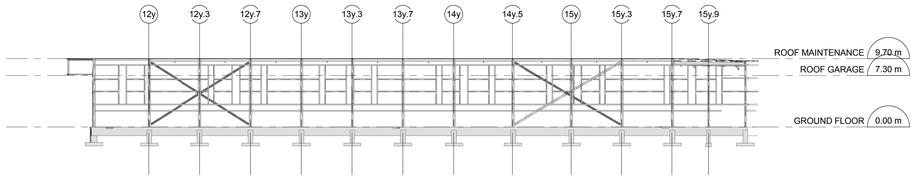


3 S4001 ELEVATION ON LINE 11x
Scale: 1 : 300

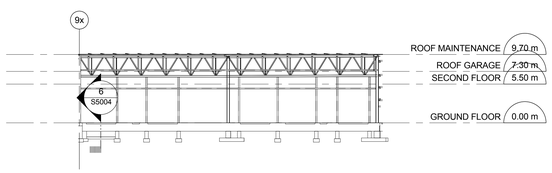


5 S4001 ELEVATION ON LINE 11y
Scale: 1 : 300

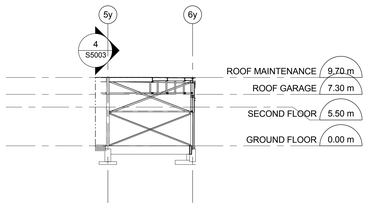


6 S4001 ELEVATION ON LINE 5x
Scale: 1 : 300

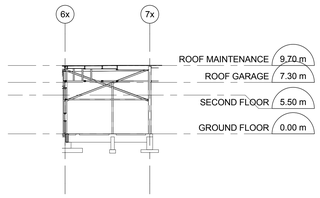


7 S4001 ELEVATION ON LINE 7y
Scale: 1 : 300

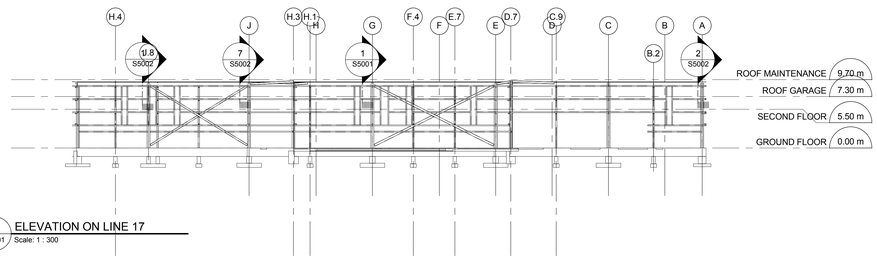

1 S4001 ELEVATION ON LINE 17
Scale: 1 : 300

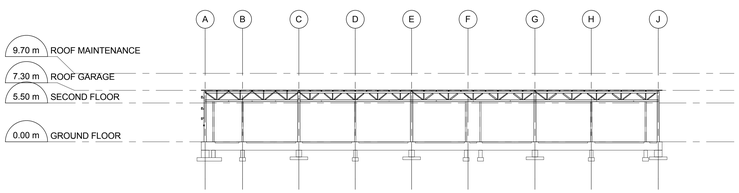

2 S4001 ELEVATION ON LINE 1
Scale: 1 : 300

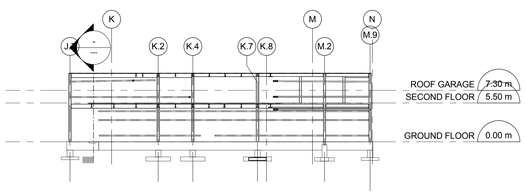

8 S4001 ELEVATION ON LINE 1.1
Scale: 1 : 300

REVISION SCHEDULE

DATE	ISSUED FOR	REV
SEP 28 2017	60% REVIEW	A

KEY PLAN

CONSULTANTS

IBI Group
100 - 175 Galaxy Boulevard
Toronto ON M9W 0C9 Canada
tel 416 679 1930 fax 416 675 4620
ibigroup.com

This drawing has been prepared solely for the use of the Region of Waterloo and there are no representations of any kind made by IBI Group to any party with whom IBI Group has not entered into a contract

Seal

North Arrow

Detail Symbol
DETAIL NUMBER
LOCATION OR DETAIL SHEET

Project Manager	Architect/Engineer
E. CZERNIAK	Designer
Project Leader	Drawn
Checker	DN
Date	Checked
	Approver

Client
REGION OF WATERLOO
Region of Waterloo

Project
GRAND RIVER TRANSIT
NORTHFIELD BUS FACILITY

Drawing Title
ELEVATIONS

Check Scale (may be photo-reduced)
0 1 Inch 0 10mm

Project No.	Drawing No.
110146	S4001

C:\Users\dmitri.raoumov\Documents\REVIT2016\110146-NORTHFIELD-S-16-M_dmitri.raoumov.rvt
06-Dec-17 10:17:17 AM