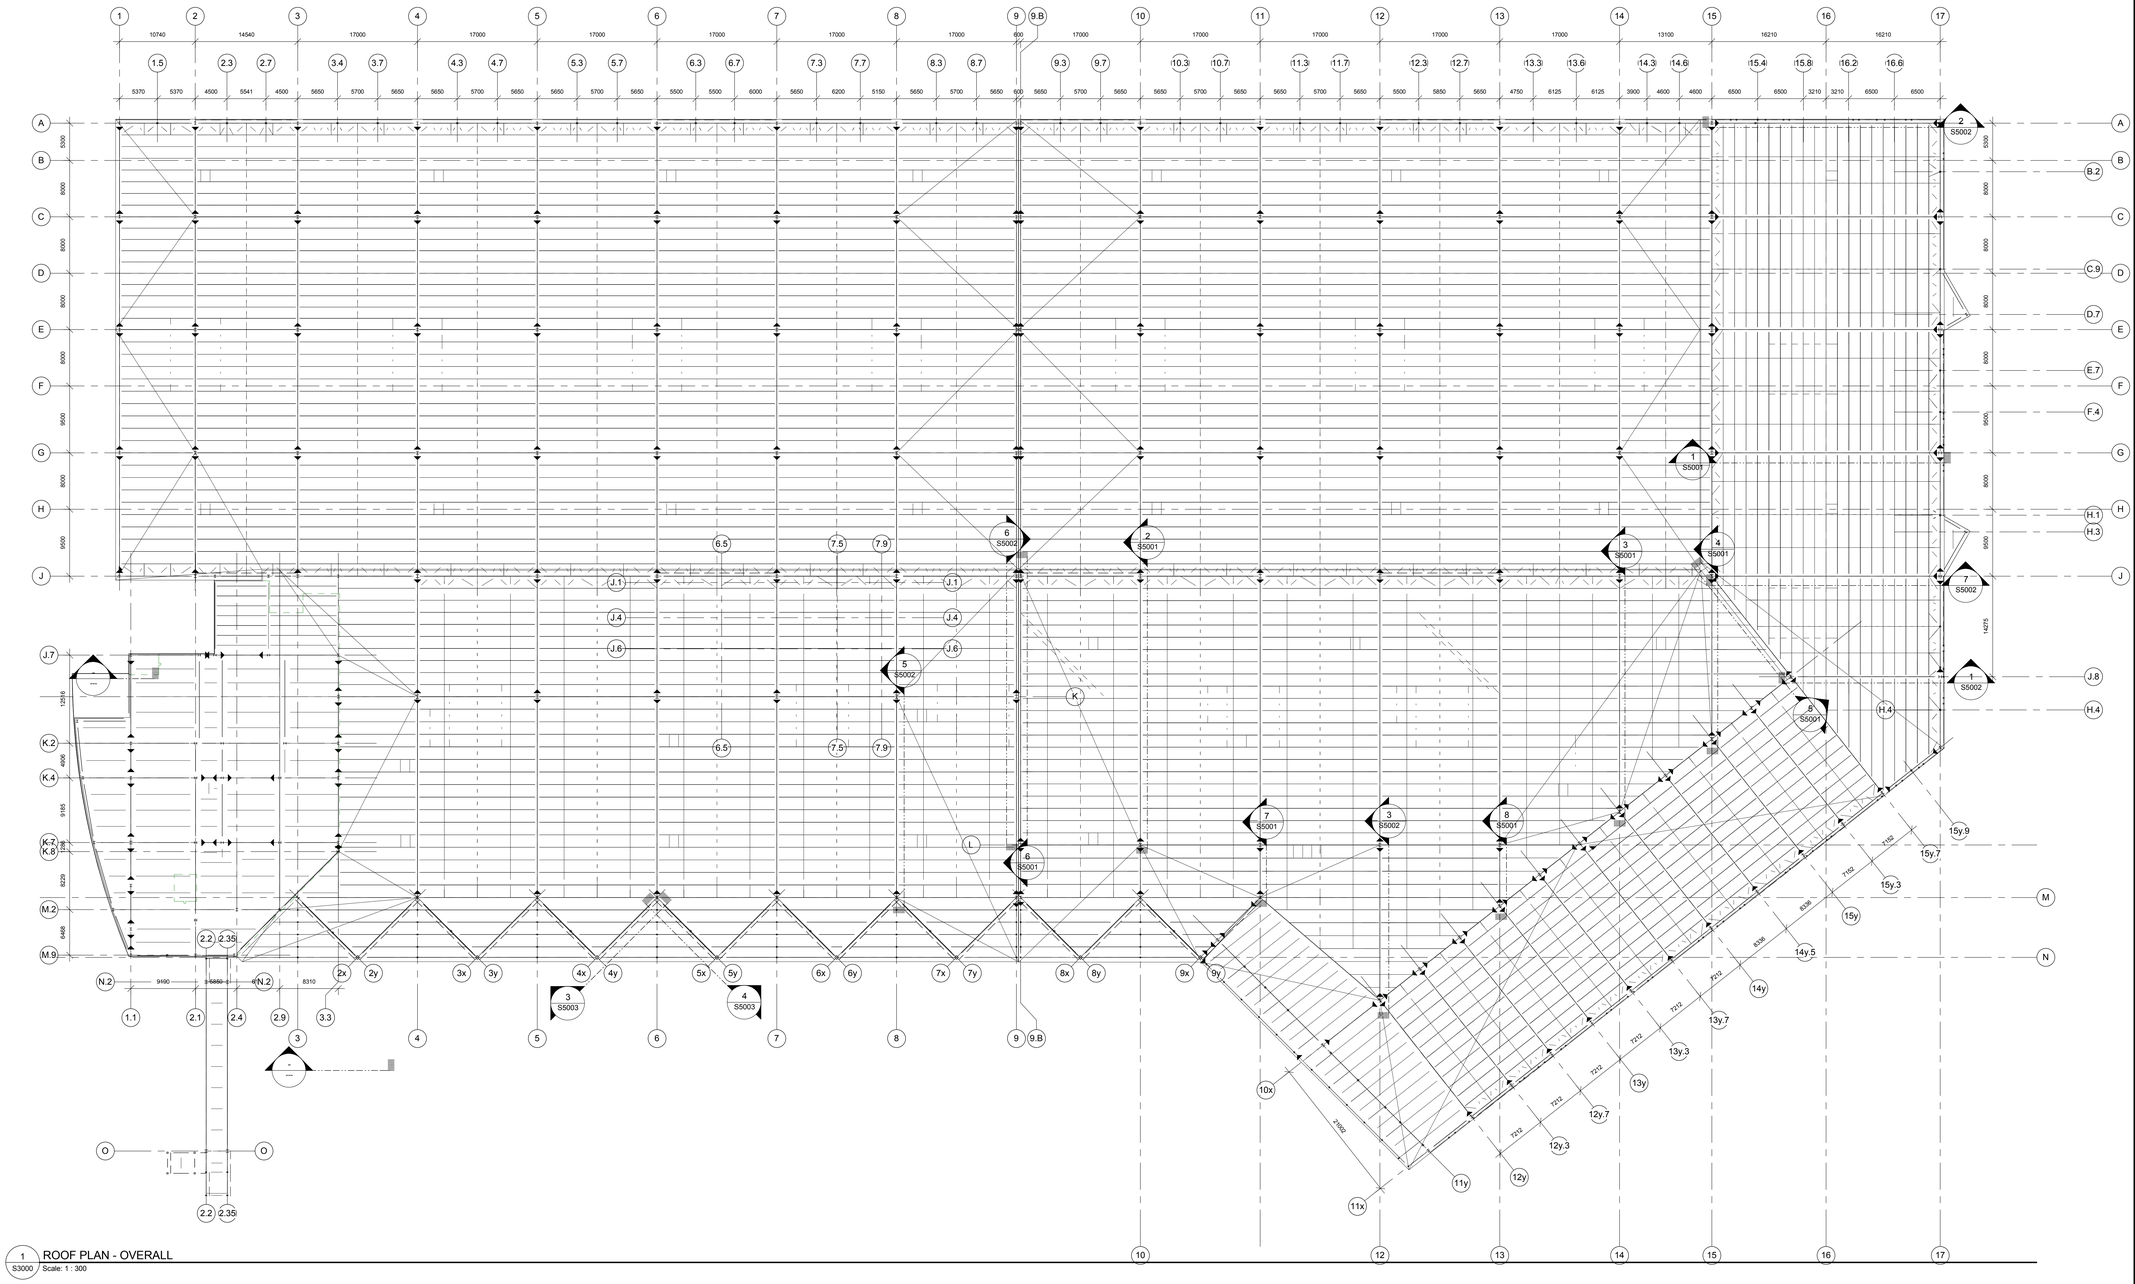


1 S3000 ROOF PLAN - OVERALL
Scale: 1 : 300

JOIST GIRDER SCHEDULE	
TYPE	WEIGHT (kg/m)
J.G.1	375
J.G.2	425
J.G.3	250
J.G.4	300
J.G.5	600


C:\Users\dmitri.raoumov\Documents\REVIT2018\110146-NORTHFIELD-S-16-M_dmitri.raoumov.rvt

06-Dec-17 10:16:02 AM

REVISION SCHEDULE

DATE	ISSUED FOR	REV
SEP 28 2017	60% REVIEW	A

KEY PLAN

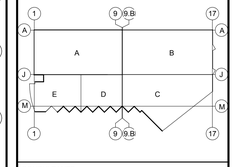

CONSULTANTS

IBI Group
100 - 175 Galaxy Boulevard
Toronto ON M9W 0C9 Canada
tel 416 679 1930 fax 416 675 4620
ibigroup.com

This drawing has been prepared solely for the use of the Region of Waterloo and there are no representations of any kind made by IBI Group to any party with whom IBI Group has not entered into a contract

Seal

North Arrow: Project North

Detail Symbol: DETAIL NUMBER / LOCATION OR DETAIL SHEET

Project Manager: E. CZERNIAK	Architect/Engineer Designer
Project Leader	Drawn: DN
Checker	
Date	Checked / Approver

Client
REGION OF WATERLOO
Region of Waterloo

Project
GRAND RIVER TRANSIT
NORTHFIELD BUS FACILITY

Drawing Title
ROOF PLAN - OVERALL

Check Scale (may be photo-reduced)
0 1 Inch 0 10mm

Project No.	Drawing No.
110146	S3000