


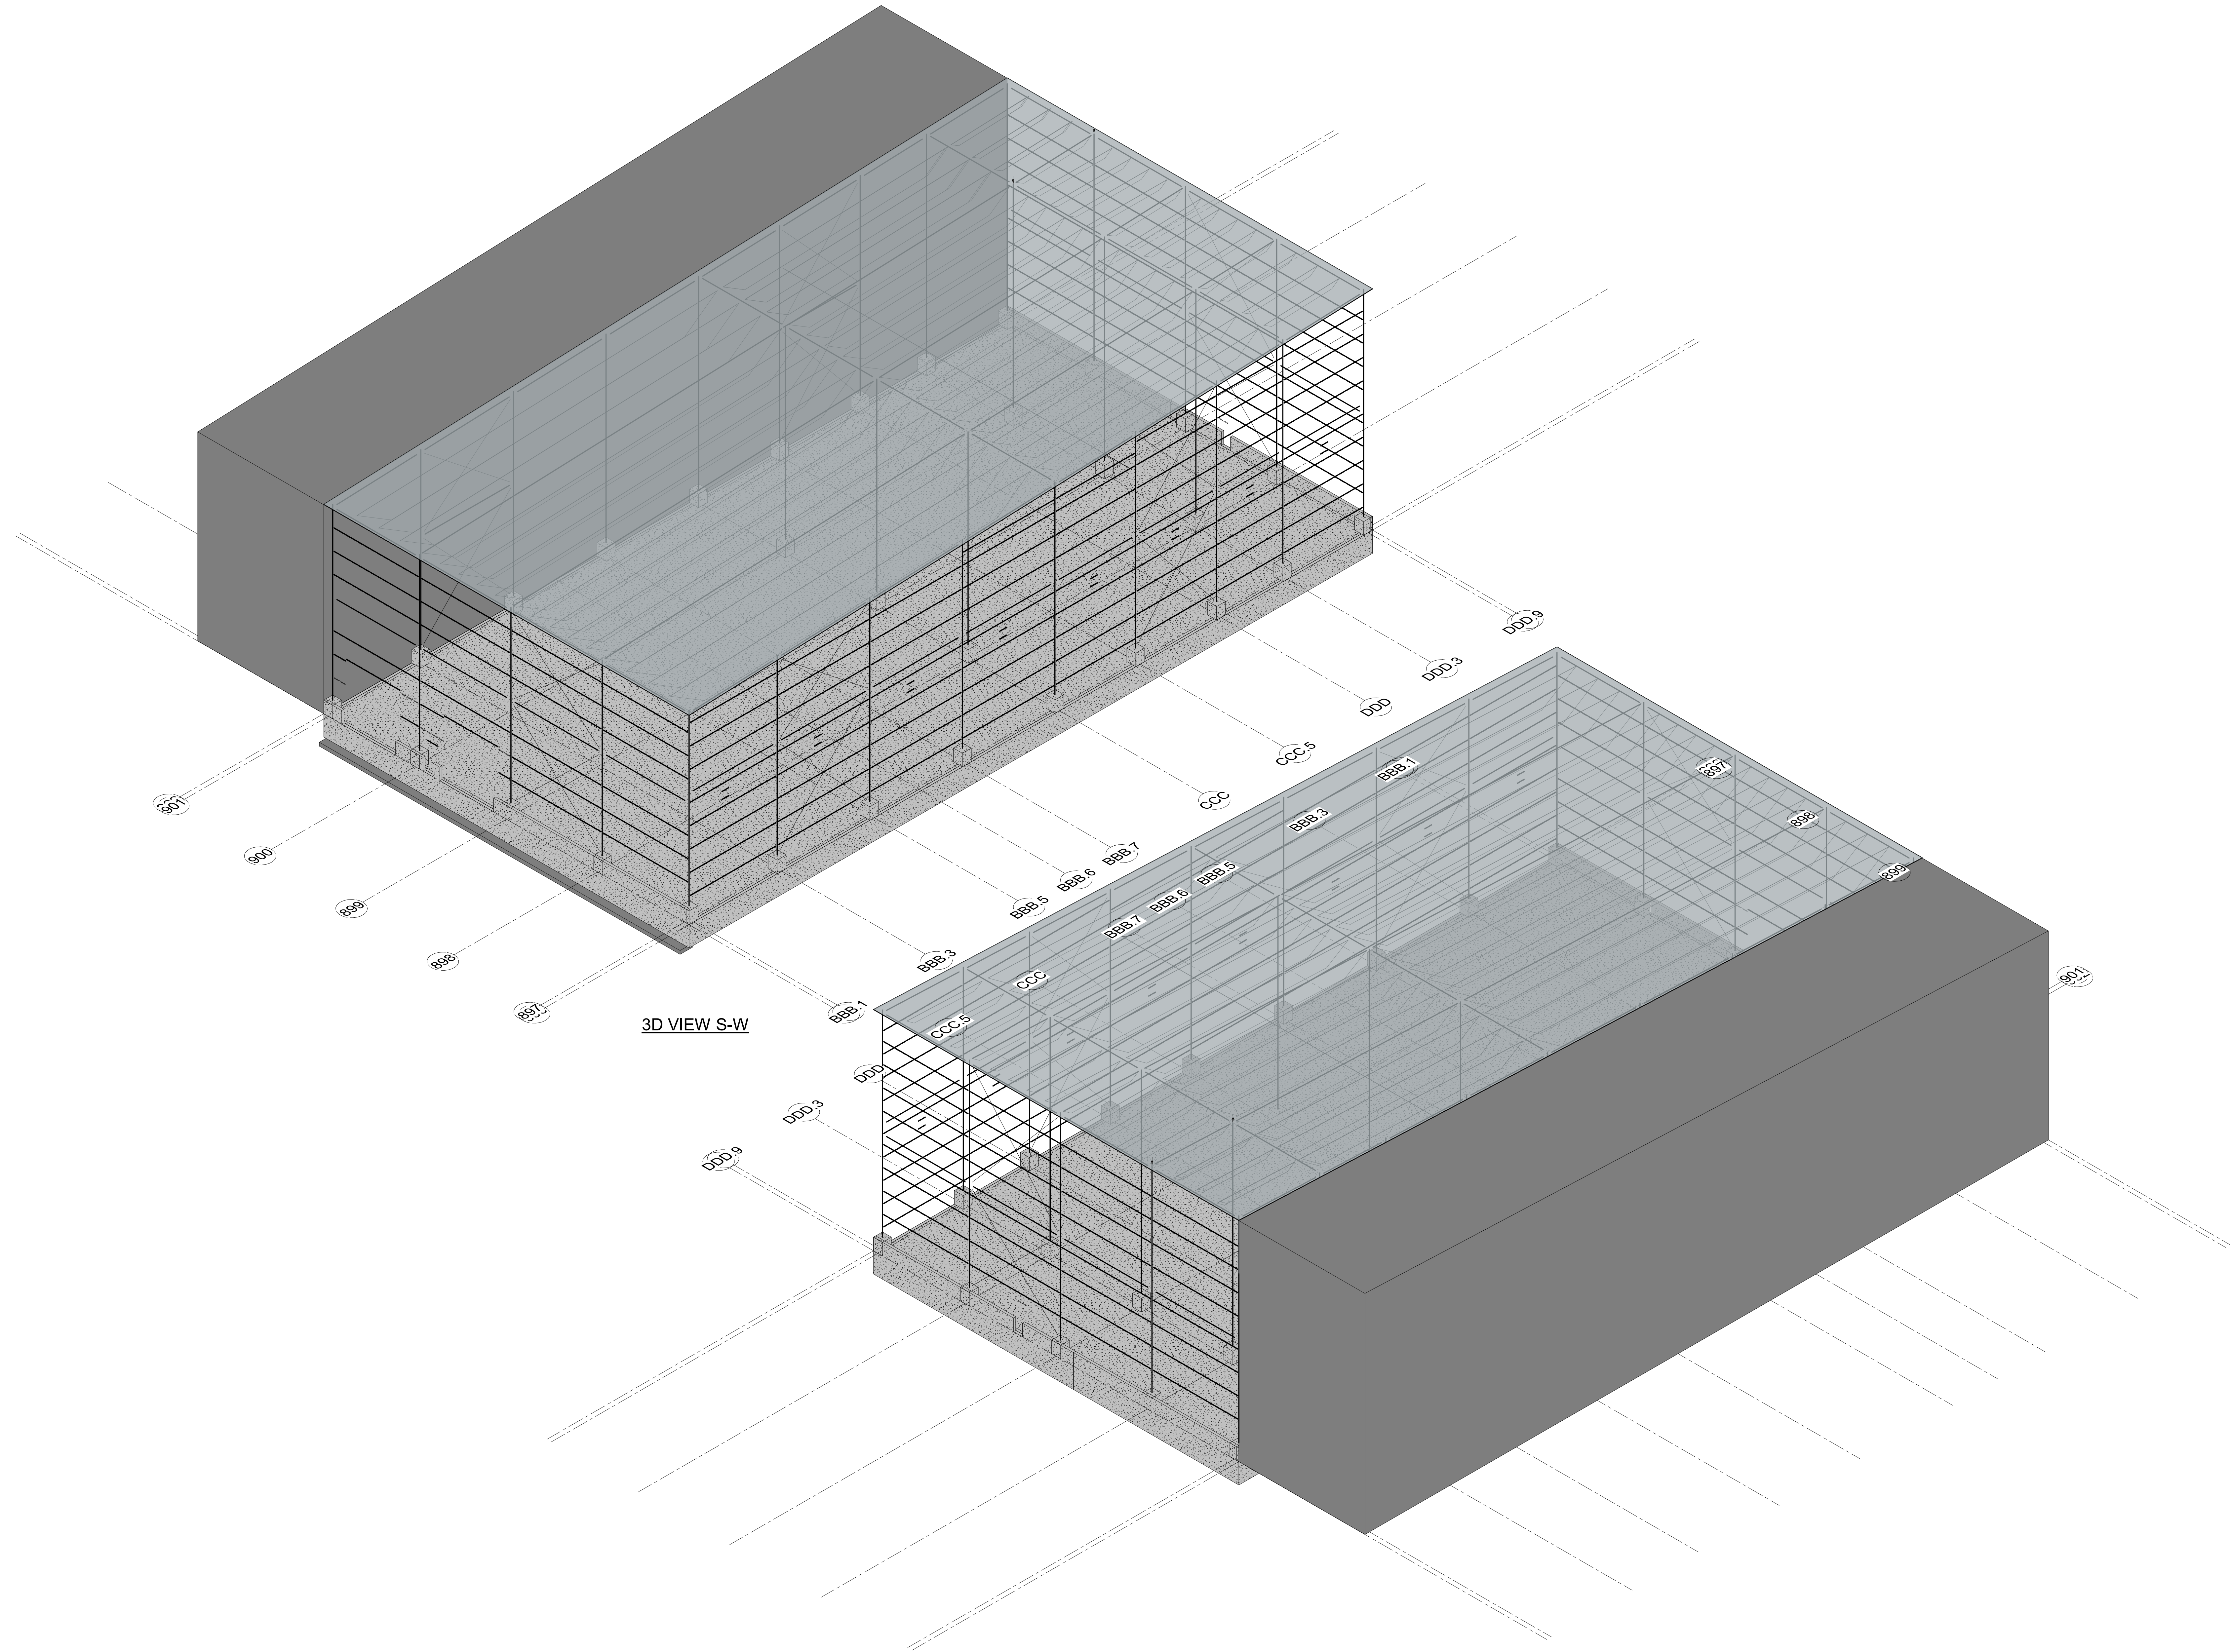

3D VIEW S-W

3D VIEW N-E

CONTRACTOR/RECTOR NOTE:
IT IS PROHIBITED TO MODIFY, COPY, REPRODUCE OR OTHERWISE
DISTRIBUTE THIS DRAWING OR ANY REPRESENTATION OF THIS
DRAWING, OR ANY MEDIA, INCLUDING ELECTRONIC, WITHOUT THE
PRIOR WRITTEN APPROVAL OF CANAM GROUP INC.

PRELIMINARY SHEET LIST	
EsMx001	PRELIMINARY SKETCH - 3D VIEWS
EsMx101	PRELIMINARY SKETCH - ANCHOR PLAN
EsMx201	PRELIMINARY SKETCH - MEZZANINE PLAN
EsMx301	PRELIMINARY SKETCH - BRIDGE CRANE PLAN
EsMx401	PRELIMINARY SKETCH - ROOF PLAN
EsMx501	PRELIMINARY SKETCH - ELEVATIONS
EsMx502	PRELIMINARY SKETCH - ELEVATION, WALL SECTION AND SCHEDULES
EsMx601	PRELIMINARY SKETCH - DETAILS

LEGENDE
NUMEROTATION DES PAGES
Mx001 = GENERAL
Mx101 = ANCRAGE
Mx201 = MEZZANINE
Mx301 = PONT ROULANT
Mx401 = TOIT (INCLURE LE PONT ROULANT SUSPENDU)
Mx501 = ELEVATION + MARQUISE + HIGH & LOW
Mx601 = COUPE DE MUR + DETAILS DE FINITION

[Click here for 3D model](#)

PRELIMINARY

NOT TO BE USED FOR CONSTRUCTION

REVISION	DATE	DESCRIPTION	DESIGN	VER
PROJECT MANAGER				
		-		
		-		
		-		
		-		
		-		
DRAWING				
DRAWN	DESIGNED	PROJECT ENGINEER	SCALE:	
Donald Piché			1/2" = 1'-0"	
CHECKED	CONSULTING ENGINEERS / ARCHITECTS		DATE (yyyy-mm-dd):	
			2025-02-10	
CUSTOMER: Fws Industrial Project Ltd				

**CANAM**

11505, 1re Avenue, bureau 500, Saint-Georges Beauce
Châteauguay, Québec, G5Y 7G5
Phone : (418) 228-8031
Toll free : (877) 499-6049
www.canam.com

PROFESSIONAL SEAL

PROJECT


Strong Pine- Hanson Lake Phase 3
Hanson Lake, SK

DRAWING TITLE

PRELIMINARY SKETCH - 3D VIEWS

CONTRACT NUMBER	DRAWING NUMBER	DIVISION	REVISION
P2029-034	EsMx001		

Initials

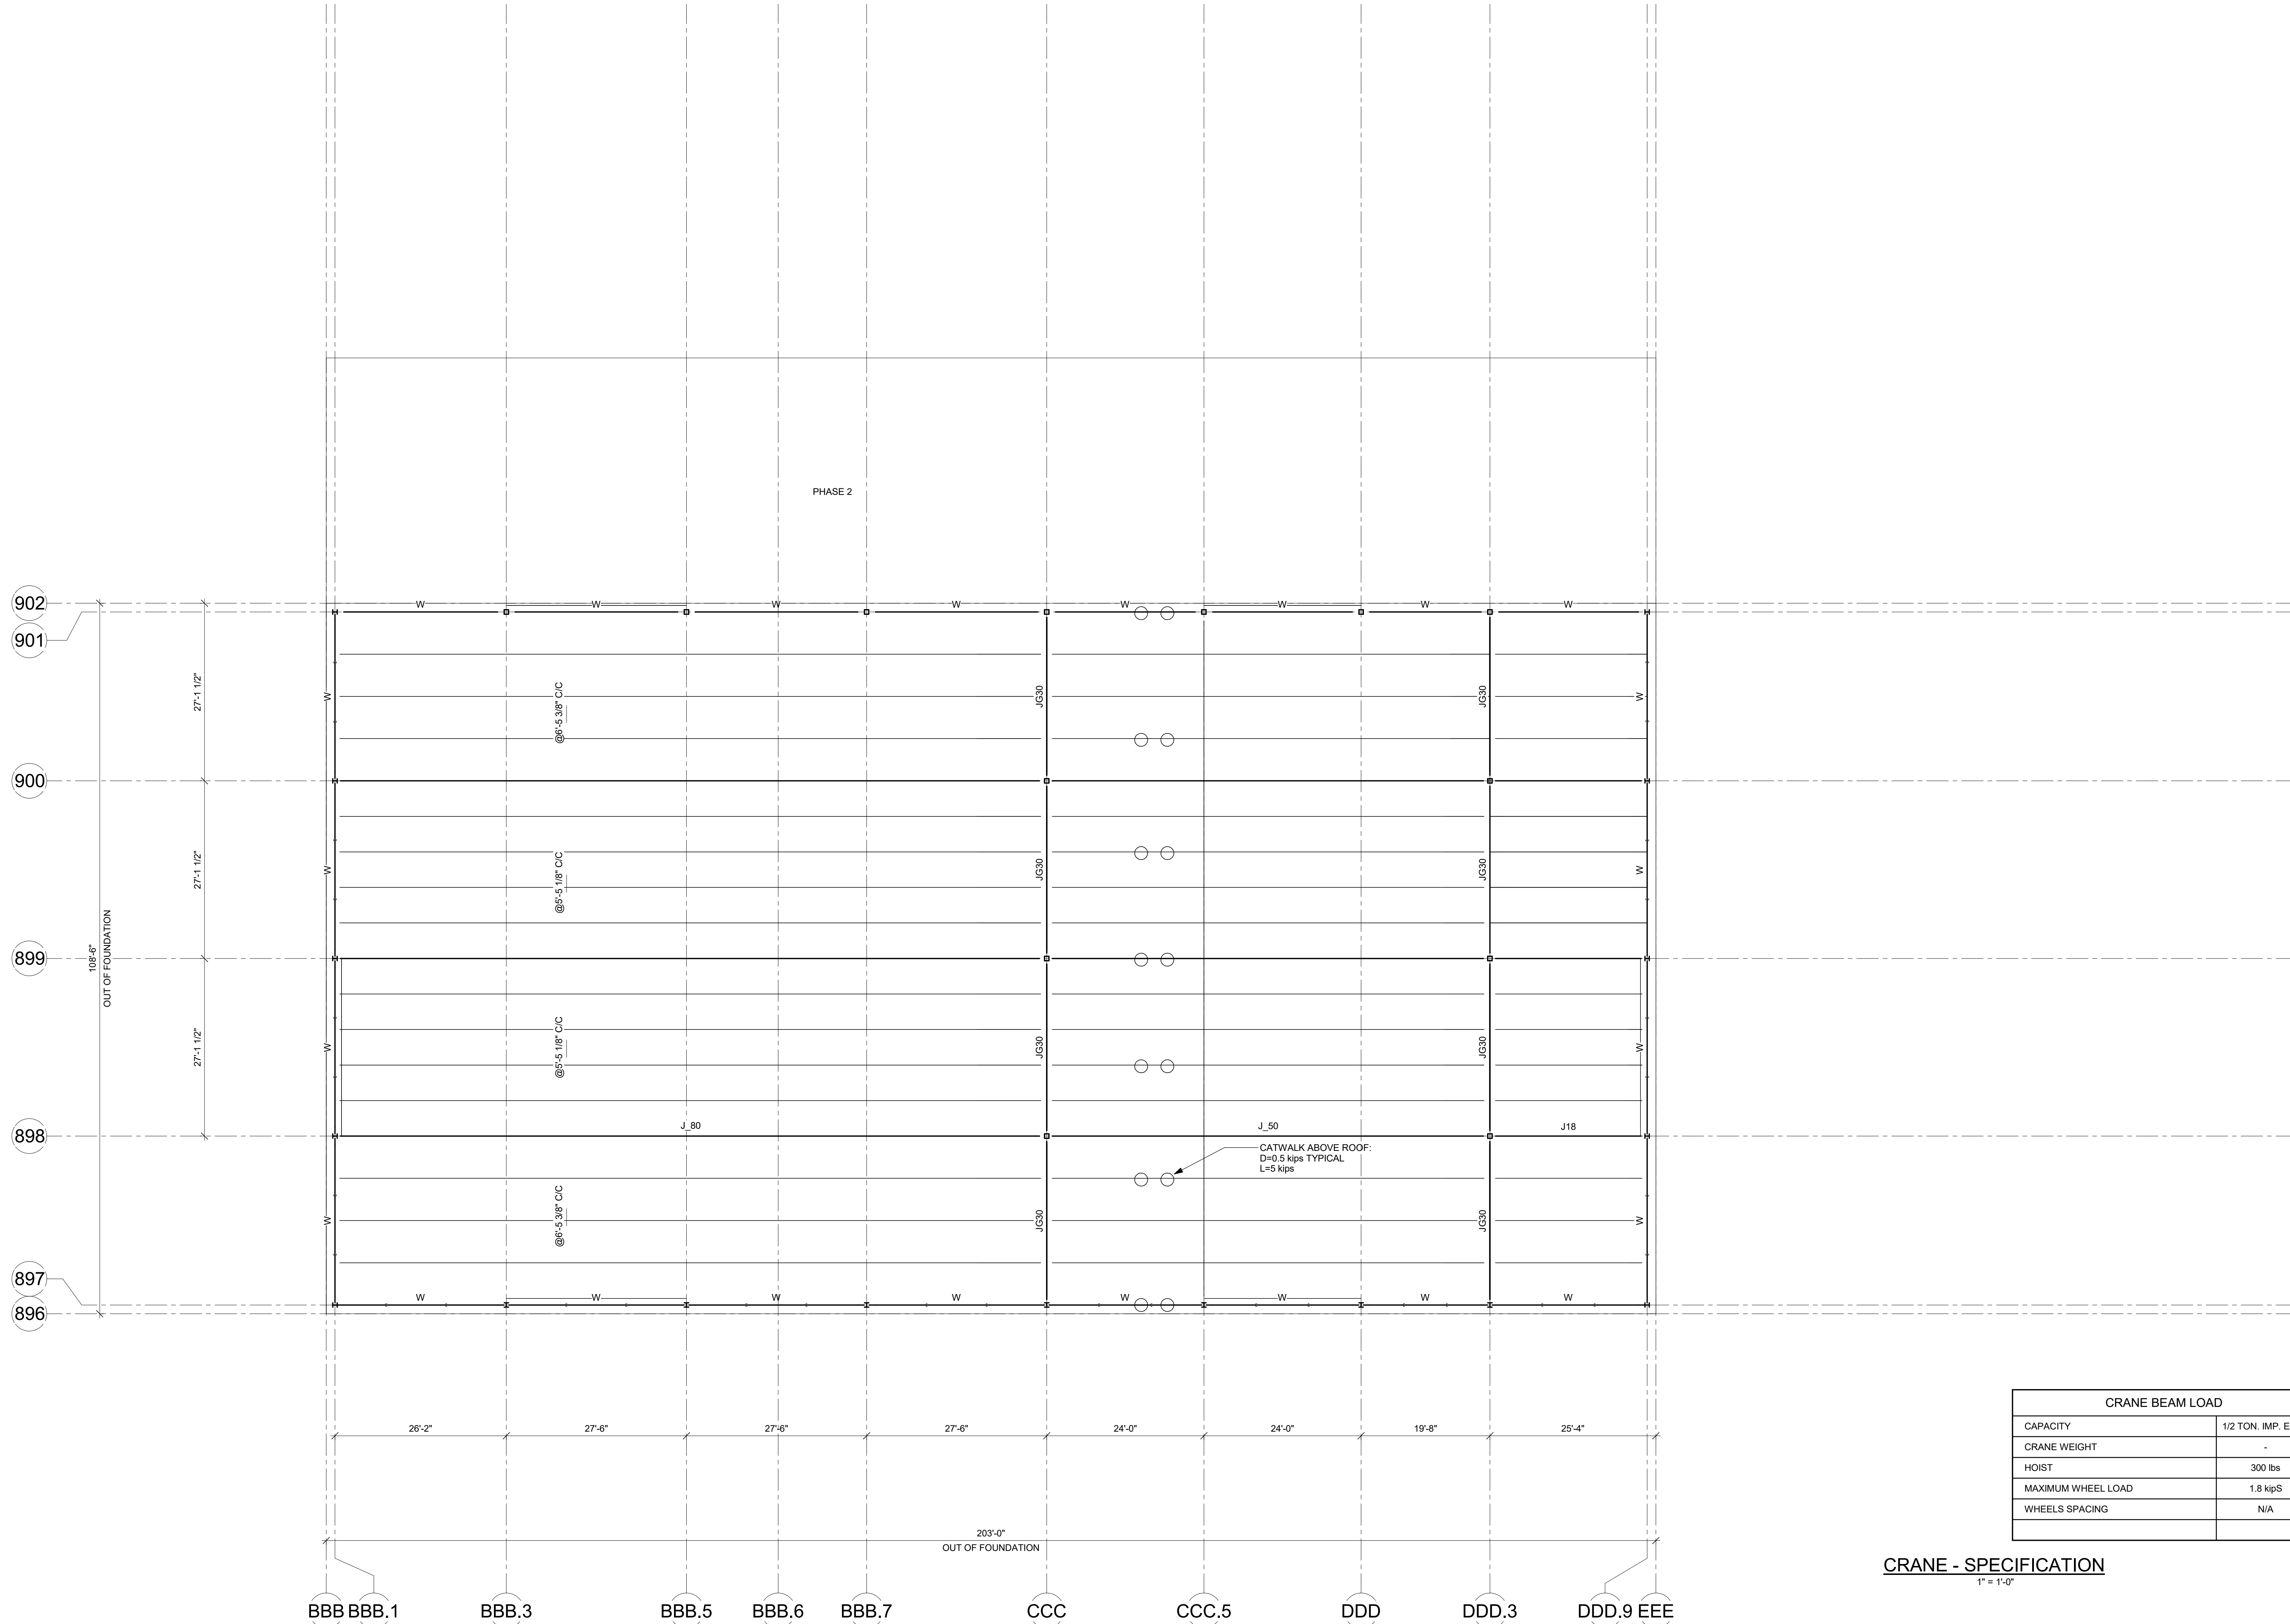


CRANE BEAM LOAD	
CAPACITY	1/2 TON. IMP. EACH
CRANE WEIGHT	-
HOIST	300 lbs
MAXIMUM WHEEL LOAD	1.8 kips
WHEELS SPACING	N/A

CRANE - SPECIFICATION
1" = 1'-0"

ROOF PLAN
3/32" = 1'-0"

GROSS UPLIFT DIAGRAM (UNFACTORED):

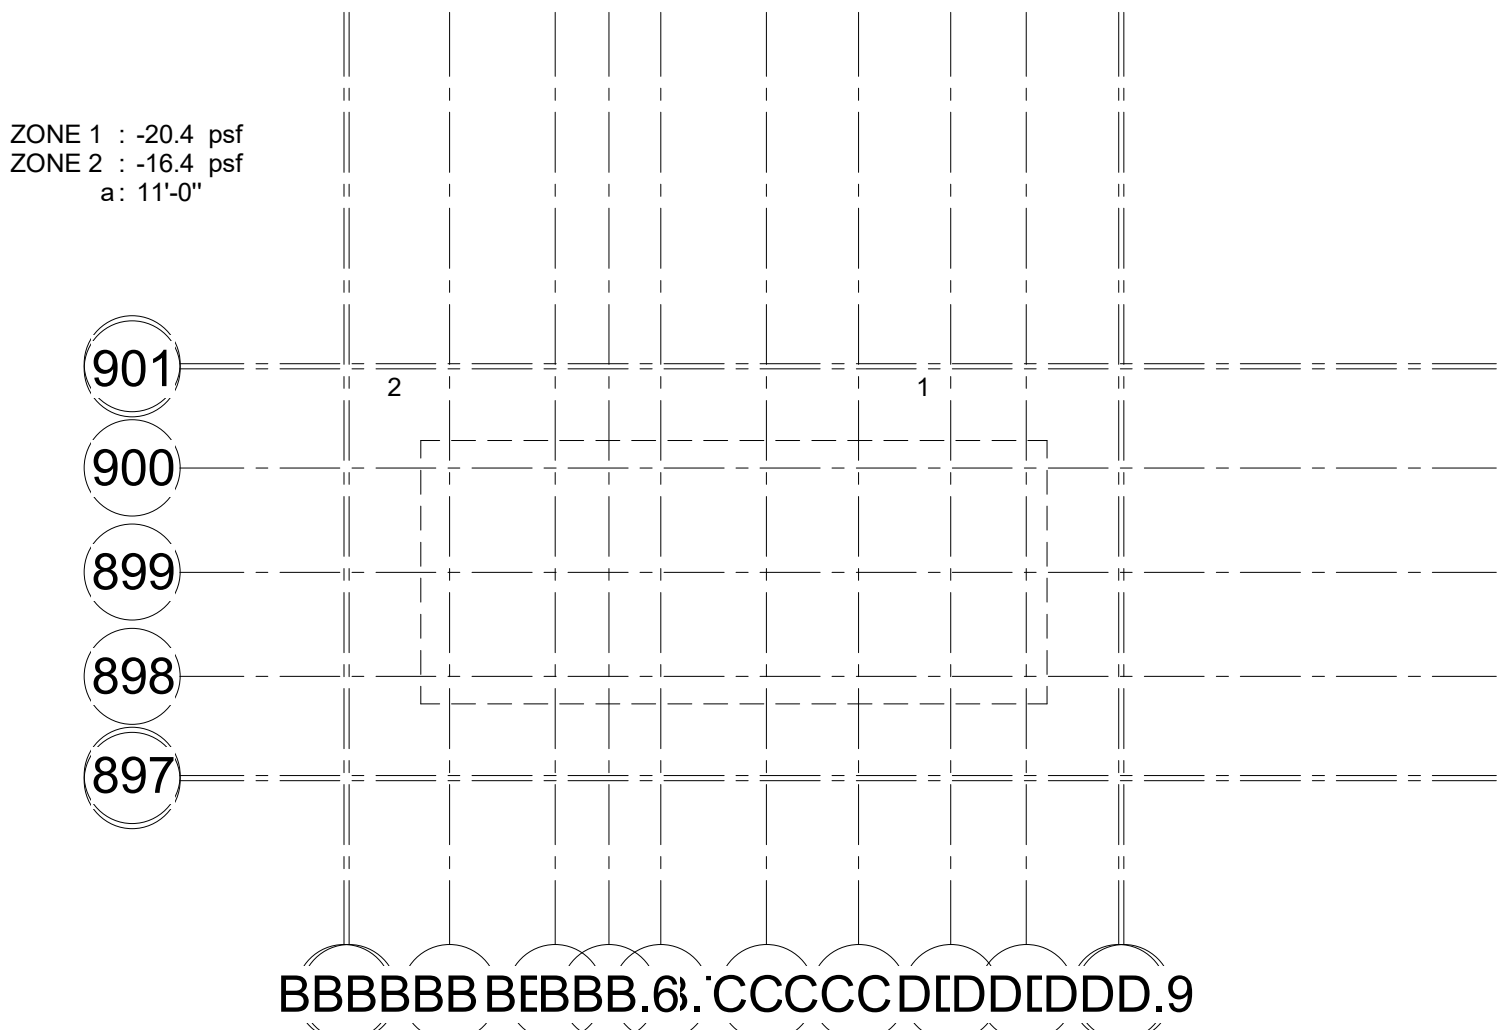

CONTRACTOR/RECTOR NOTE:
IT IS PROHIBITED TO MODIFY, COPY, REPRODUCE OR OTHERWISE DISTRIBUTE THIS DRAWING OR ANY REPRESENTATION OF THIS DRAWING, OR ANY MEDIA, INCLUDING ELECTRONIC, WITHOUT THE PRIOR WRITTEN APPROVAL OF CANAM GROUP INC.

ROOF
TOP OF PLASTER RWL : 98'-0"
TOP OF PLASTER : 99'-0"
TOP OF SLAB : 100'-0"
TOP OF FOUNDATION : 100'-0"
CLEAR HEIGHT : 47'-7 1/4"
TOP OF STEEL GRIDLINE BBB: 104'-3 1/4"
TOP OF STEEL GRIDLINE EEE: 102'-6 1/8"

LOADS
D.L. : 21 psf
C.O.L. : 10.0 psf
Ss : 46.86 psf
Sv : 4.18 psf
Cb x Cw : 0.87
Roof L.L. : 0 psf
Roof L.L. : 1.0
Roof snow load: 44.3 psf
Iv : 1.0
Wind q_z 150 : 7.31 psf

Seismic (Site class: C (Assumed))
I_e : 1.0
S_s (0.2) : 0.0815
S_s (0.5) : 0.0511
S_h (1.0) : 0.0252
S_h (2.0) : 0.0194
S_h (5.0) : 0.00218
S_h (10.0) : 0.00026
PGA : 0.0391
PGV : 0.0275

• Code Applicable : National building Code of Canada
Quebec Building Code, latest adopted editions
Code of Standard Practice CISC.

• Assumed soil site class: C

• NOTE :
1. If, however, the seismic site class is determined to be E or F according to the geotechnical report, the preliminary structural concept (location and geometry of bracing, etc.) must be validated and coordinated by a Canam's engineer.

Position de la colonne HSS et W
- On va conserver 1'-4" pour la majorité des cas.
- Pour la coupe de mur R-20 et 2 heures au feu, on va mettre 1'-6".
- Lorsqu'on va avoir des colonnes de panneau C10 et C12, on va déterminer la localisation de la colonne selon le design. L'idée est de rester avec 1'-4" et 1'-6", mais dans certain cas, on va devoir utiliser 1'-8".

HSS and W column position
- We will keep 1'-4" for the majority of cases.
- For the R-20 and 2-hour fire wall, we will put 1'-6".
- When we have C10 and C12 panel columns, we will determine the location of the column according to the design. The idea is to stay with 1'-4" and 1'-6", but in some cases, we will have to use 1'-8".

PRELIMINARY

NOT TO BE USED FOR CONSTRUCTION

REVISION	DATE	DESCRIPTION	DES	VER
PROJECT MANAGER				
-				
-				
-				
DRAFTING				
DRAWN	DESIGNED	PROJECT ENGINEER	SCALE:	
Donald Piché			Comme indiqué	
CHECKED	CONSULTING ENGINEERS ARCHITECTS		DATE (yyyy/mm/dd)	
			2025-02-10	

CUSTOMER: Fws Industrial Project Ltd




PROFESSIONAL SEAL

PROJECT
Strong Pine- Hanson Lake Phase 3
Hanson Lake, SK


DRAWING TITLE
PRELIMINARY SKETCH - ROOF PLAN

CONTRACT NUMBER	DRAWING NUMBER	DIVISION	REVISION
P2029-034	EsMx401		


Scale

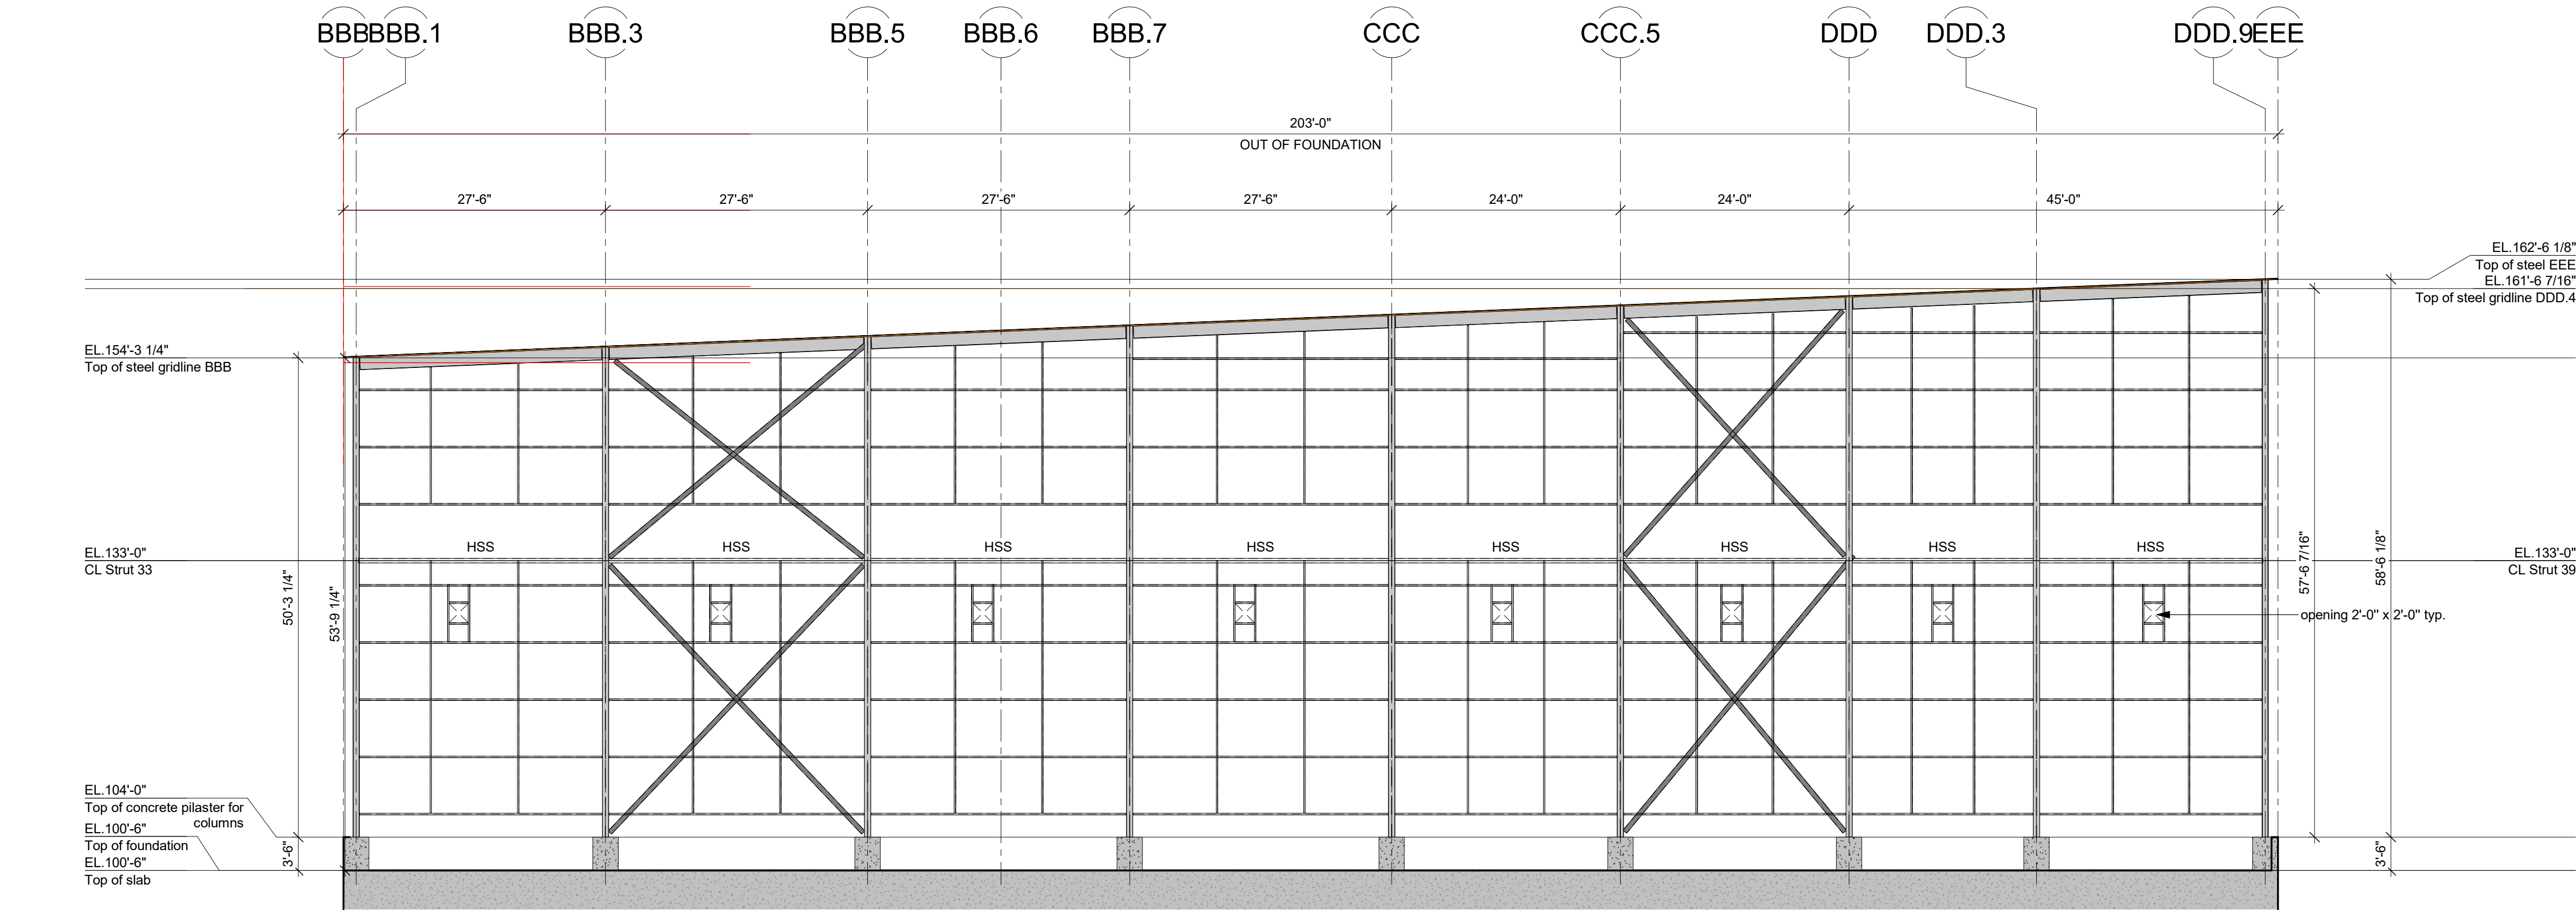


ELEVATION LINE 902 (SOUTH)
3/32" = 1'-0"

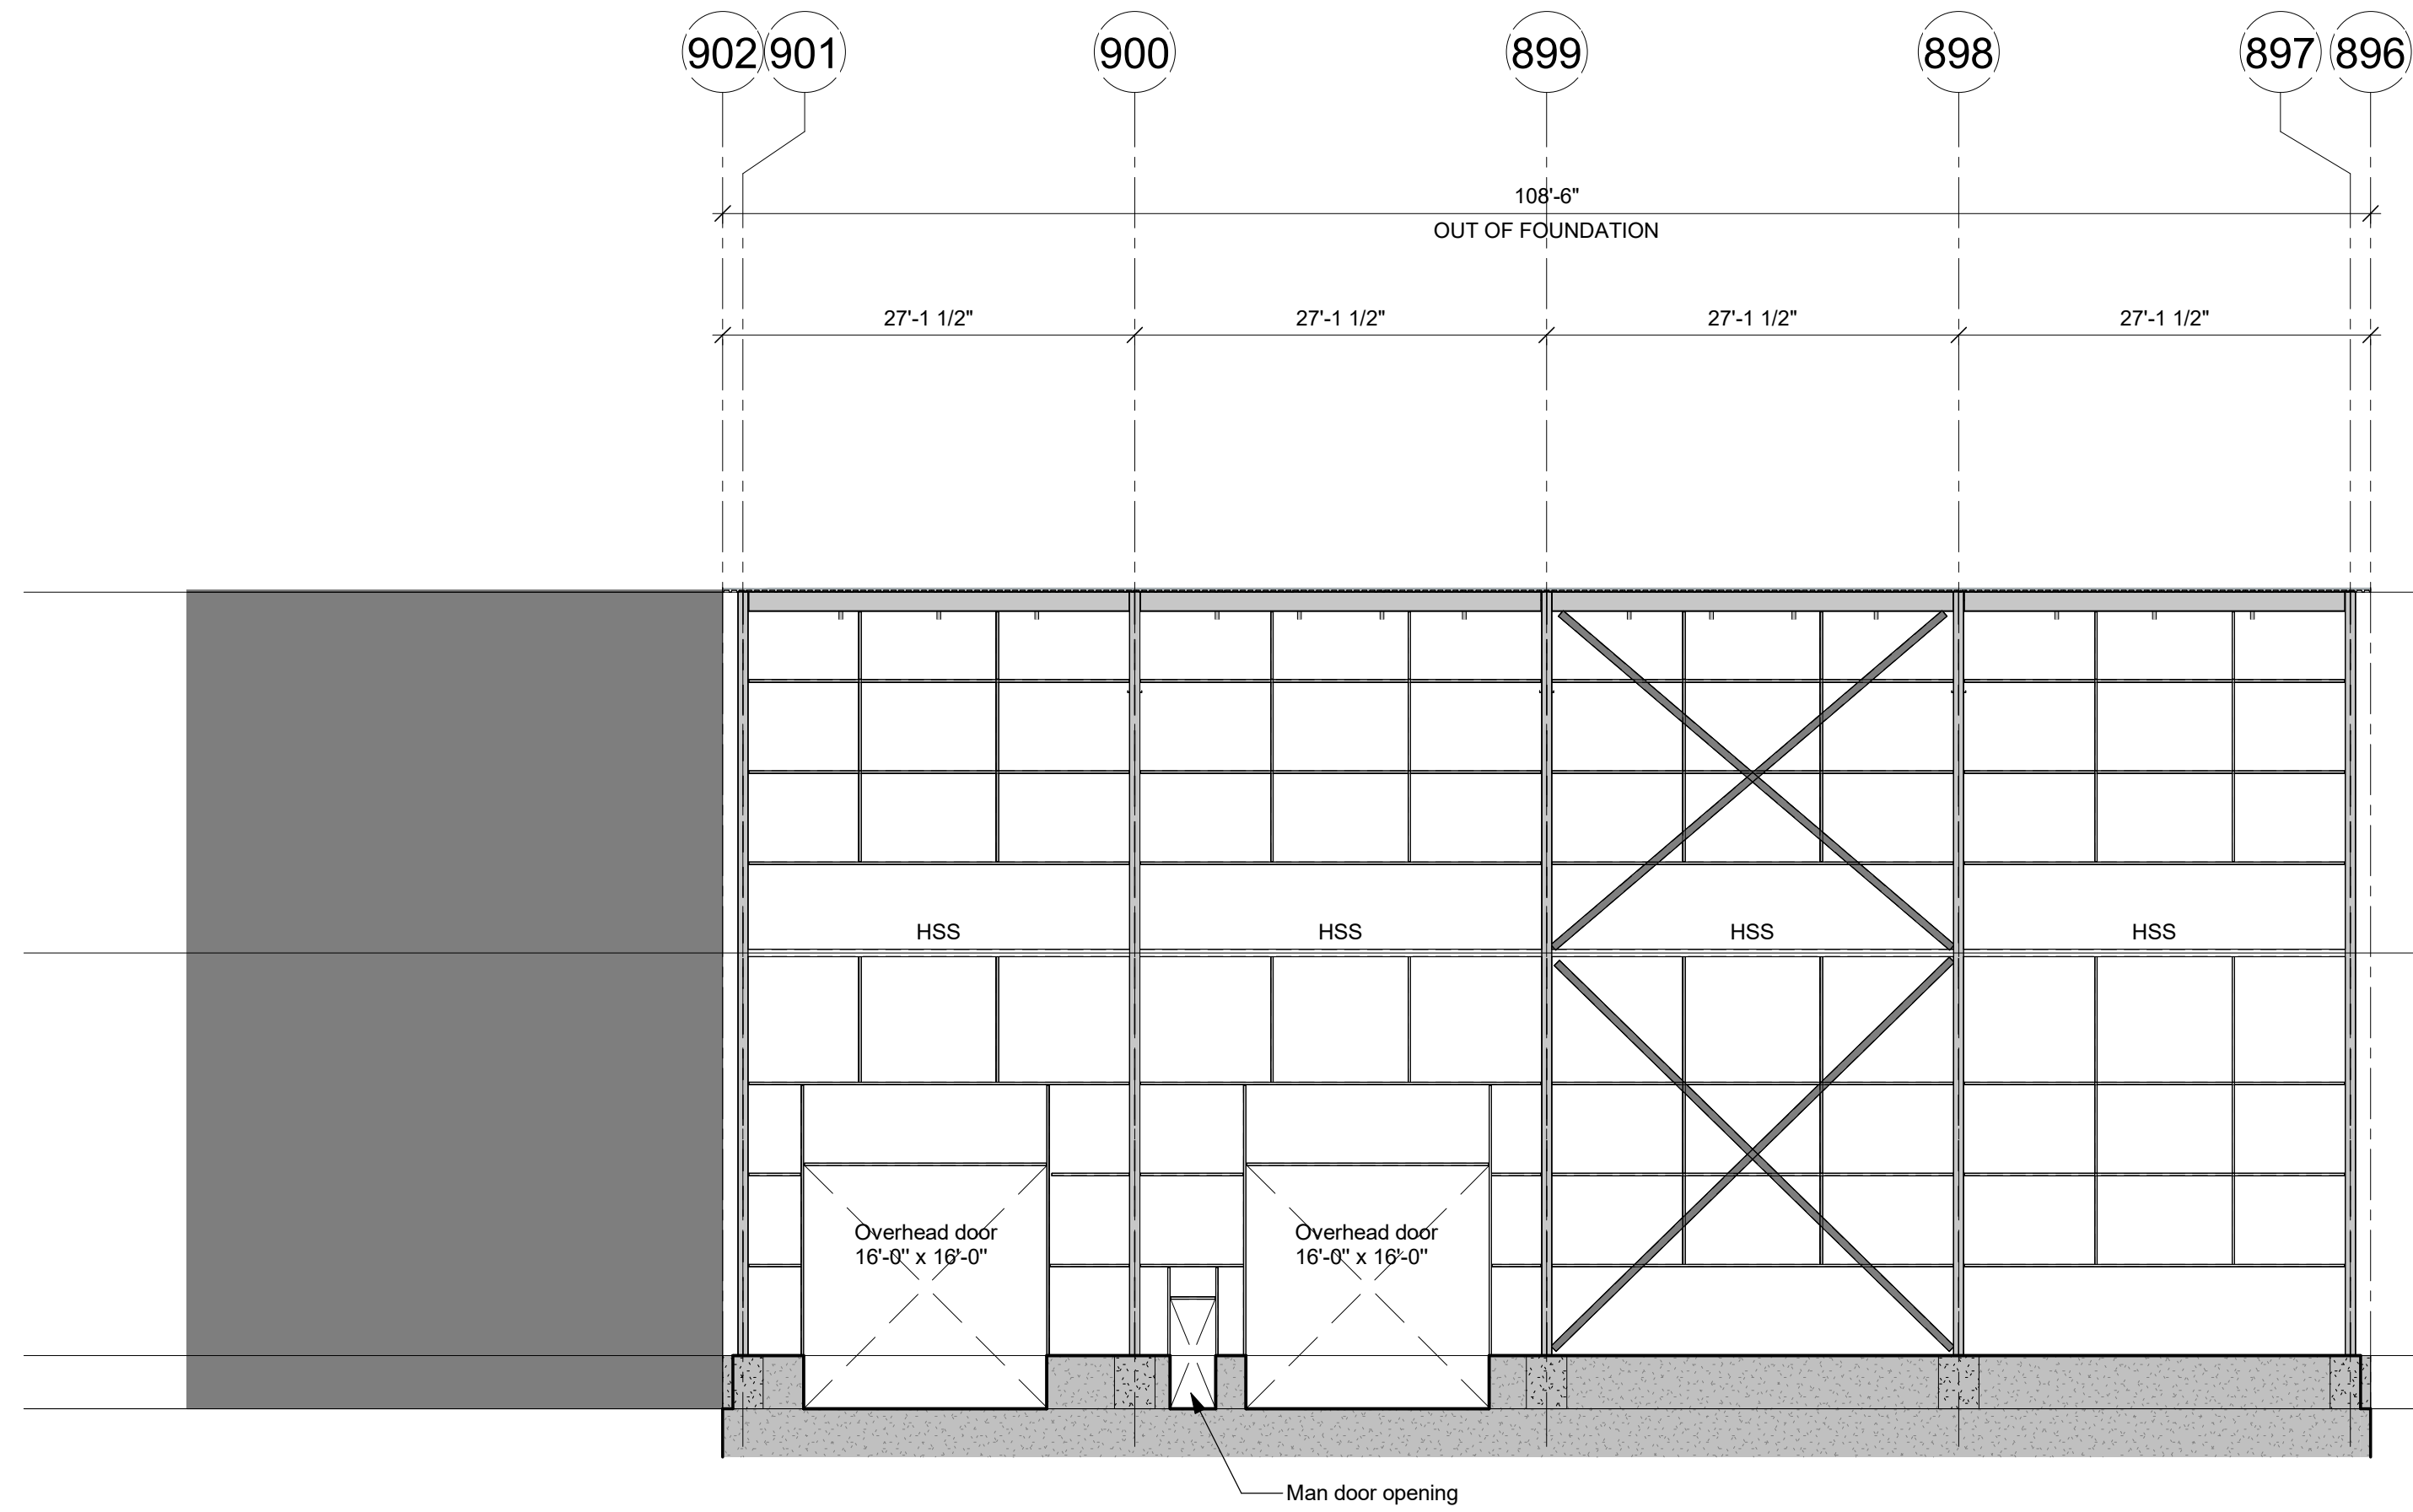

ELEVATION LINE BBB (WEST)
3/32" = 1'-0"

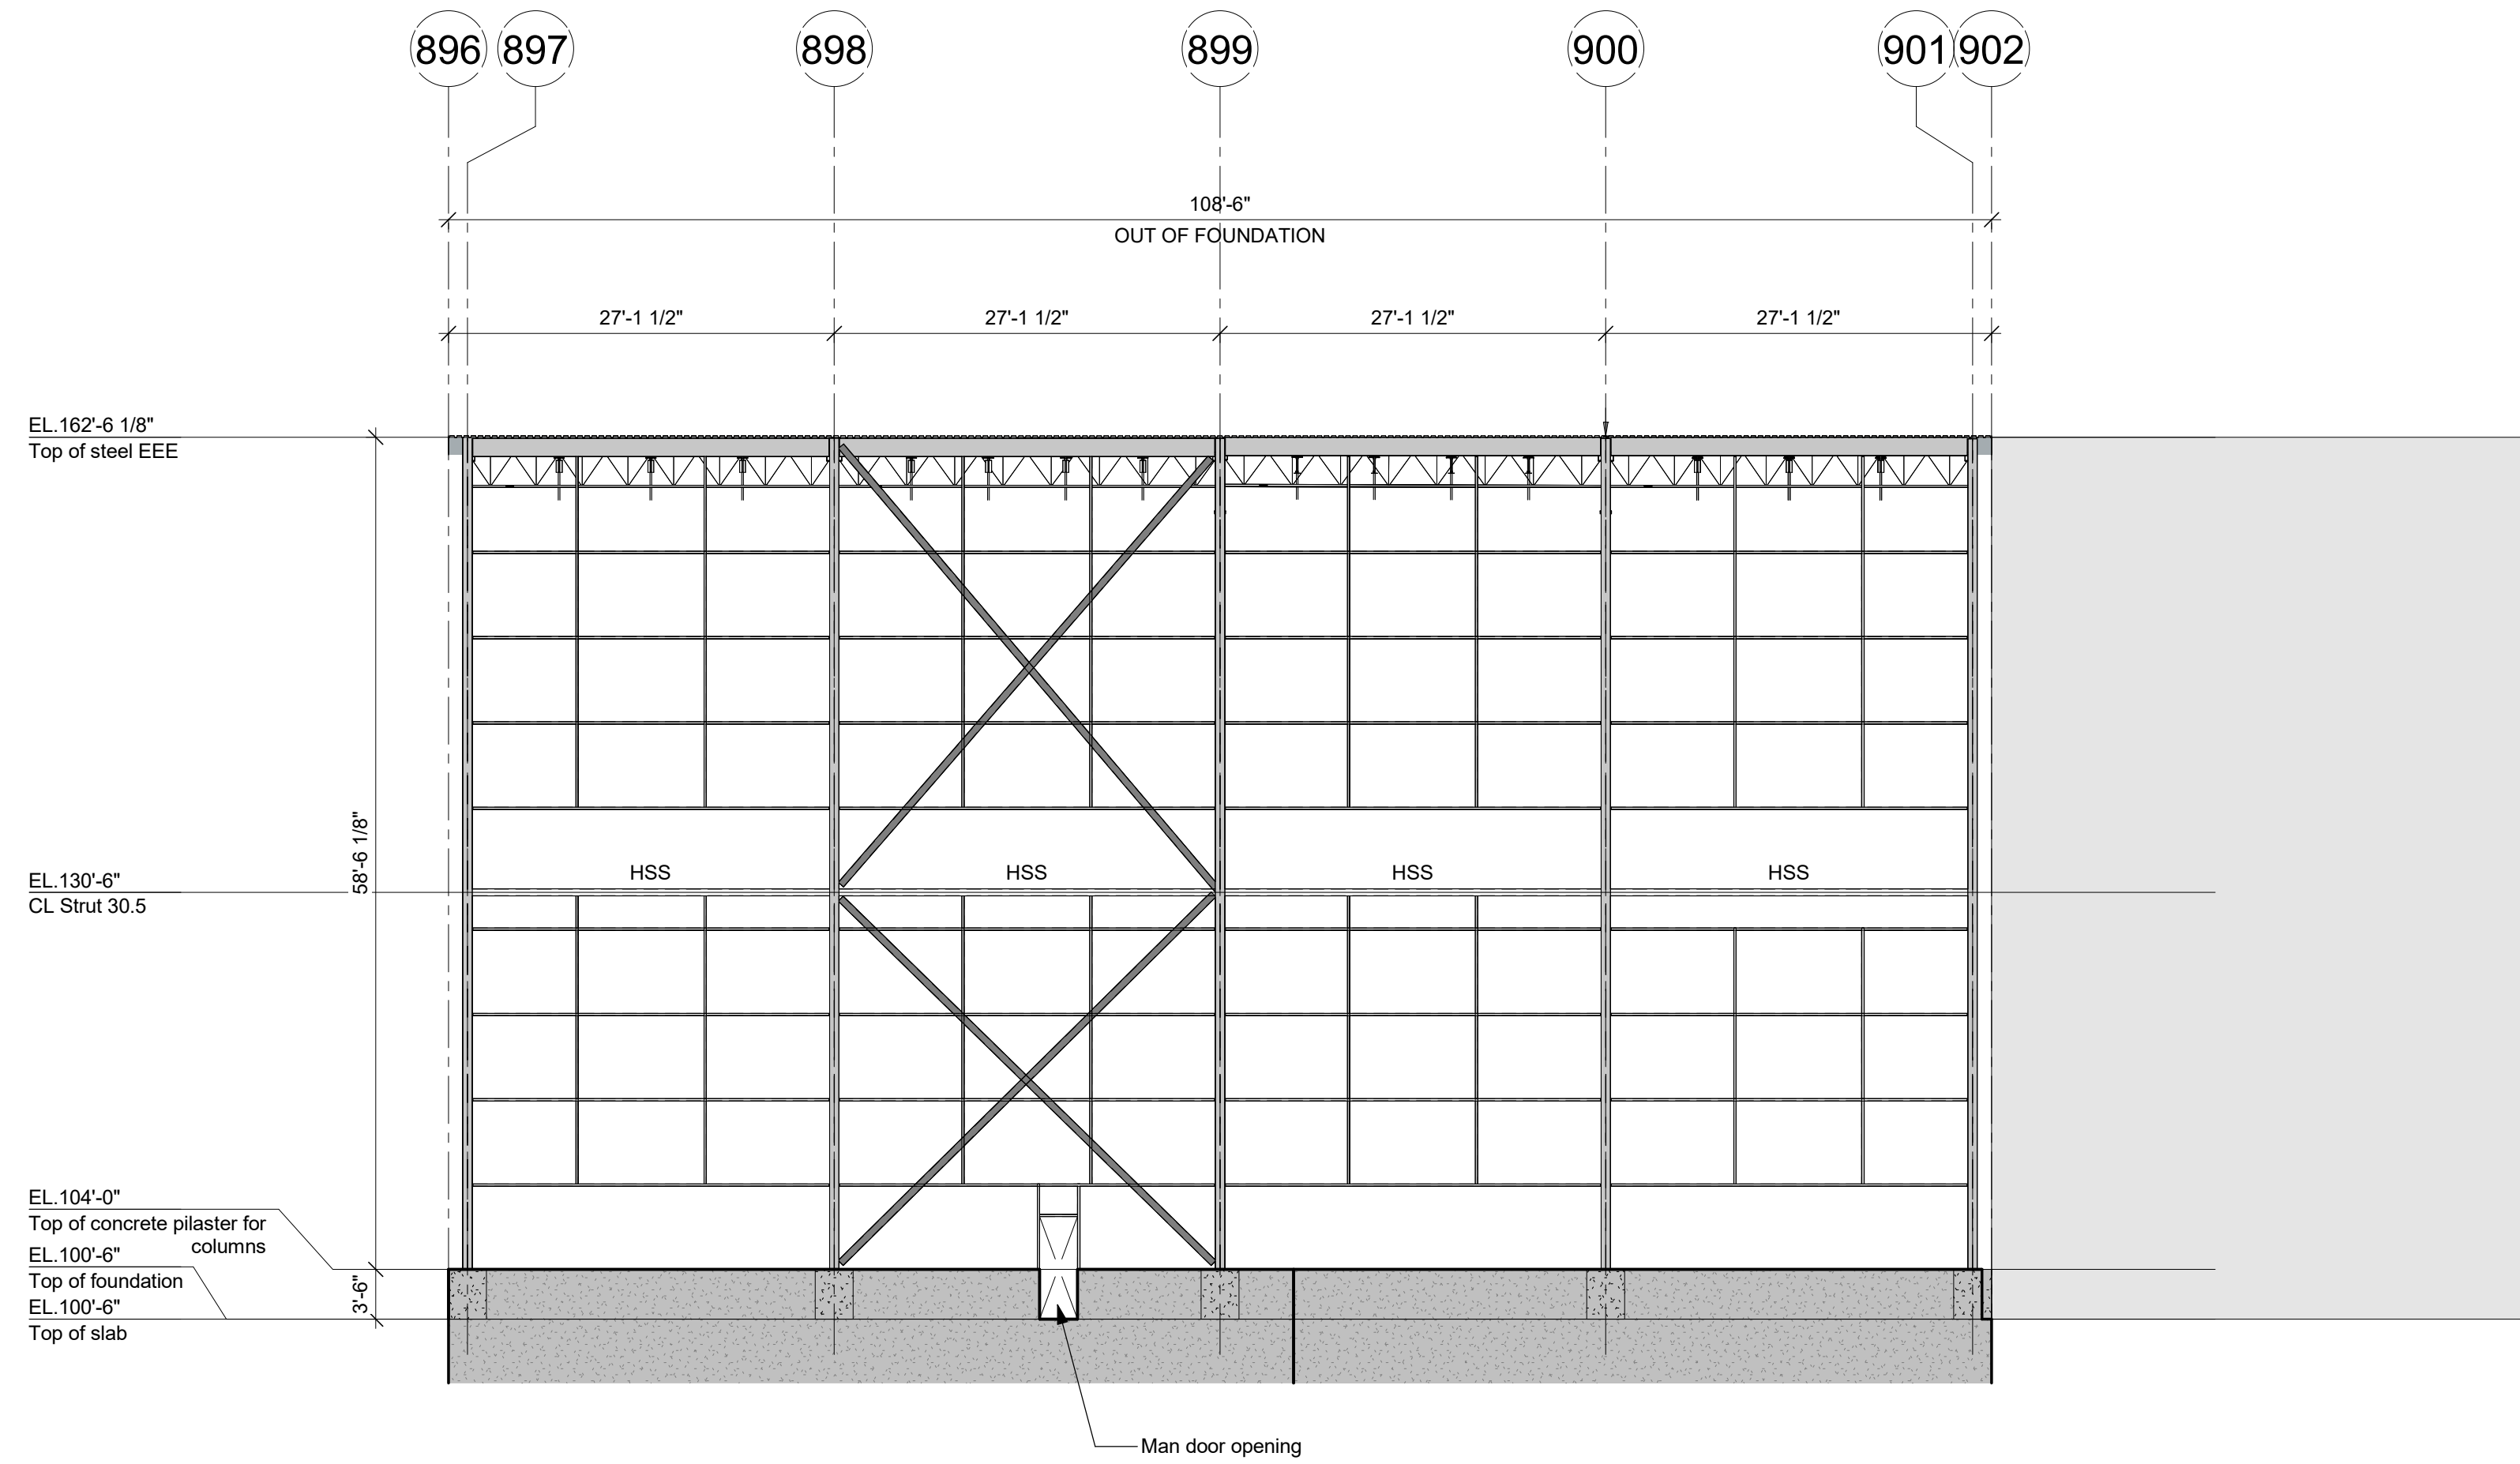

ELEVATION LINE EEE (EAST)
3/32" = 1'-0"

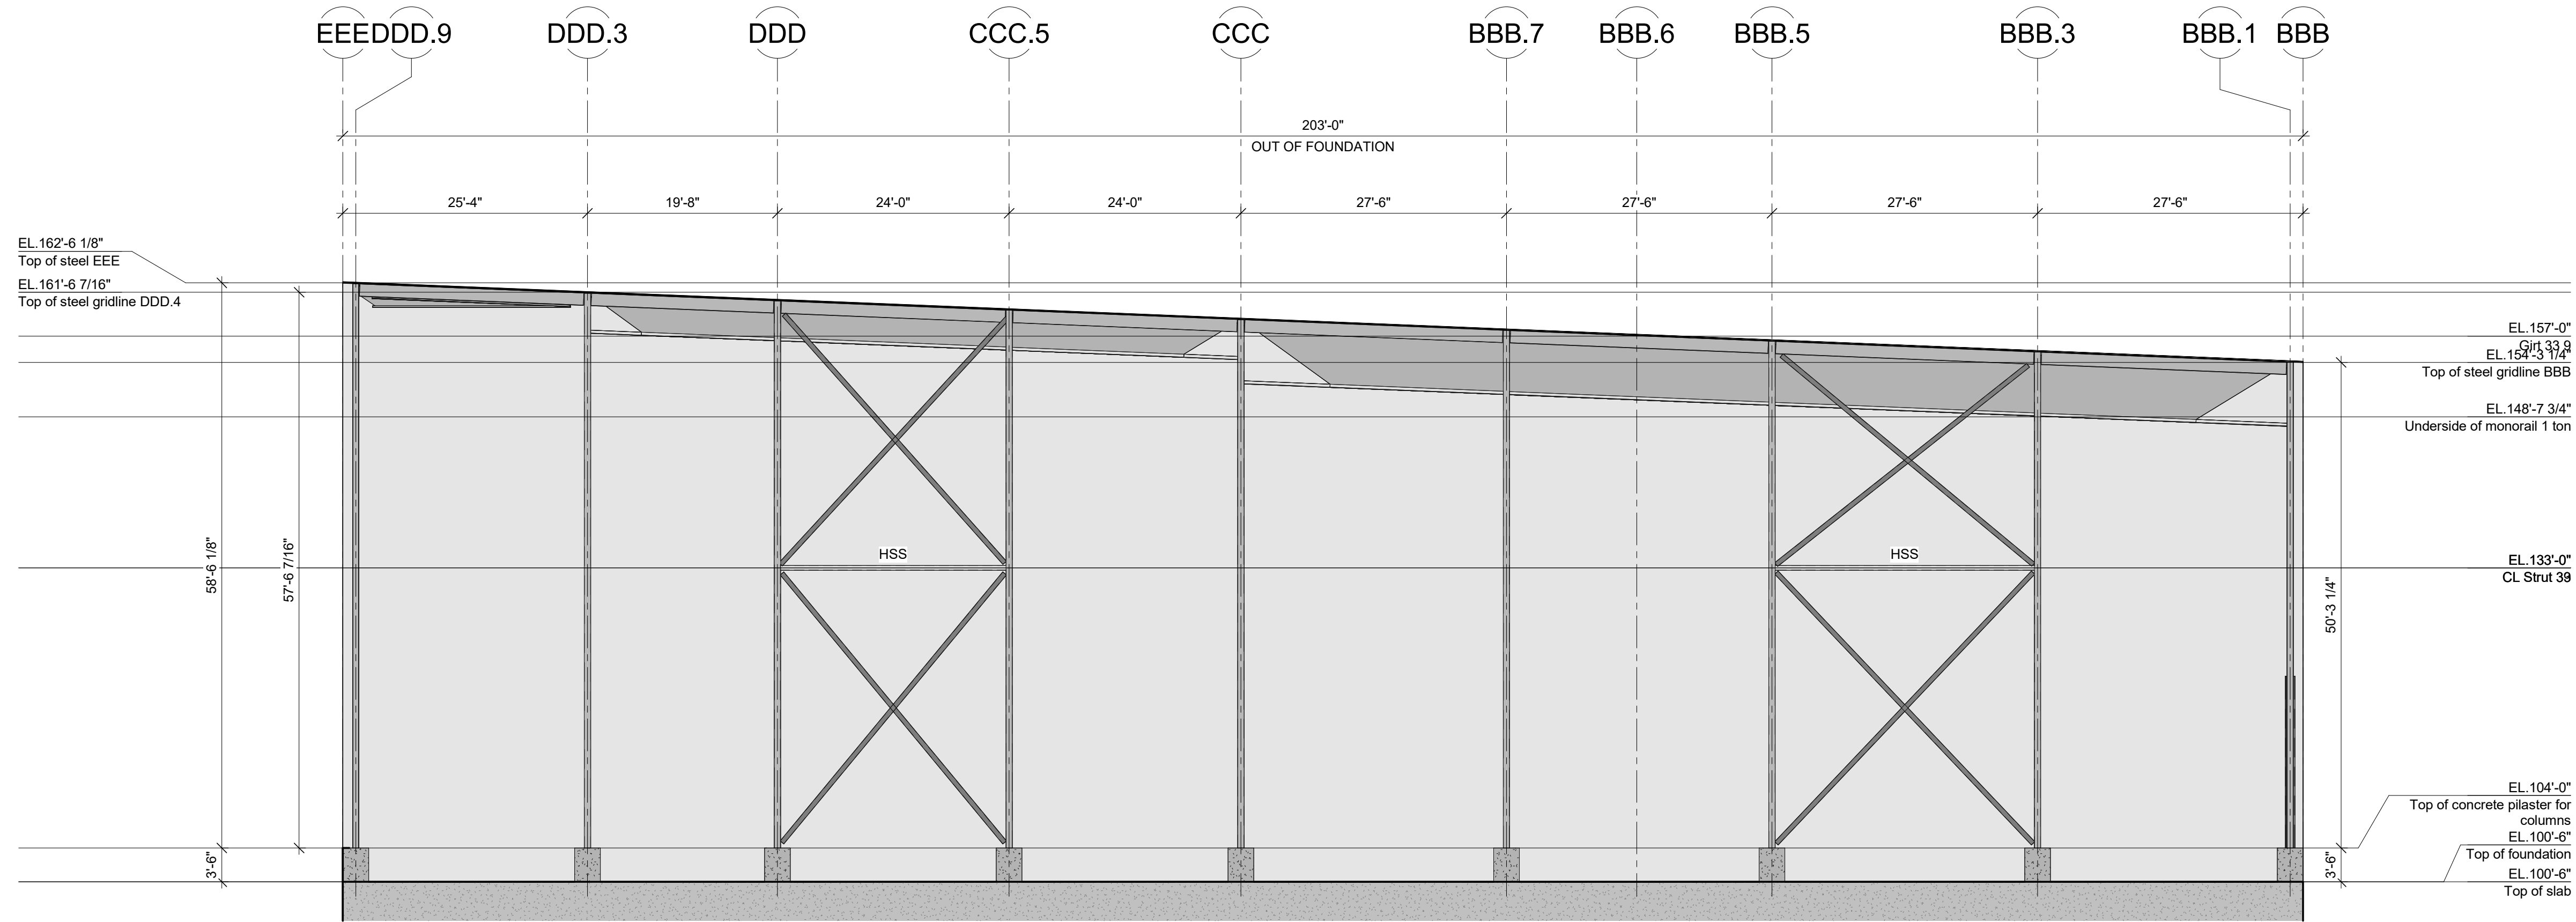

ELEVATION LINE 907 & 910 (NORTH)
3/32" = 1'-0"

CONTRACTOR/RECTOR NOTE:

IT IS PROHIBITED TO MODIFY, COPY, REPRODUCE OR OTHERWISE
DISTRIBUTE THIS DRAWING OR ANY REPRESENTATION OF THIS
DRAWING, OR ANY MEDIA, INCLUDING ELECTRONIC, WITHOUT THE
PRIOR WRITTEN APPROVAL OF CANAM GROUP INC.

PRELIMINARY

NOT TO BE USED FOR CONSTRUCTION

REVISION	DATE	DESCRIPTION	ISS	VER
----------	------	-------------	-----	-----

PROJECT MANAGER	-	-	-	-
	-	-	-	-
	-	-	-	-

DRAFTING

DRAWN	DESIGNED	PROJECT ENGINEER	SCALE
Donald Piché			3/32" = 1'-0"
CHECKED	CONSULTING ENGINEERS ARCHITECTS	DATE (yyyy/mm/dd)	
		2025-02-10	

CUSTOMER: Fws Industrial Project Ltd

CANAM
11505, 1re Avenue, bureau 500, Saint-Georges Beauce
Québec, Canada, G5Y 7X3
Phone : (418) 228-8031
Toll free : (877) 499-6049
www.canam.com

PROFESSIONAL SEAL

PROJECT

Strong Pine- Hanson Lake Phase 3
Hanson Lake, SK

DRAWING TITLE

PRELIMINARY SKETCH - ELEVATIONS

CONTRACT NUMBER	DRAWING NUMBER	DIVISION	REVISION
P2029-034	EsMx501		

Initials

