



CÉDULE DES FENÊTRES				
Identifiant	Qté.	Description	Dimensions ext. cadre largeur X hauteur	Couleur du cadre
F1	2	Fenêtre en aluminium fixe avec bris thermique et verre scellé + Low-E argon clair	9'-0" x 3'-0"	Cadre d'Aluminium (Blanc ext. et int.)
F2	2	Fenêtre en aluminium fixe avec bris thermique et verre scellé + Low-E argon clair	5'-0" x 3'-0"	Cadre d'Aluminium (Blanc ext. et int.)


CÉDULE DES PORTES				
Identifiant	Qté.	Porte 18 ja.	Dimensions	Remarques
P1	4		5'-0" x 7'-0"	
P2	2		12'-0" x 16'-0"	OUVERTURE POUR PORTE MONTANTE
P3	4		6'-0" x 9'-0"	OUVERTURE POUR PORTE MONTANTE+COUSSIN D'TANCHEITE

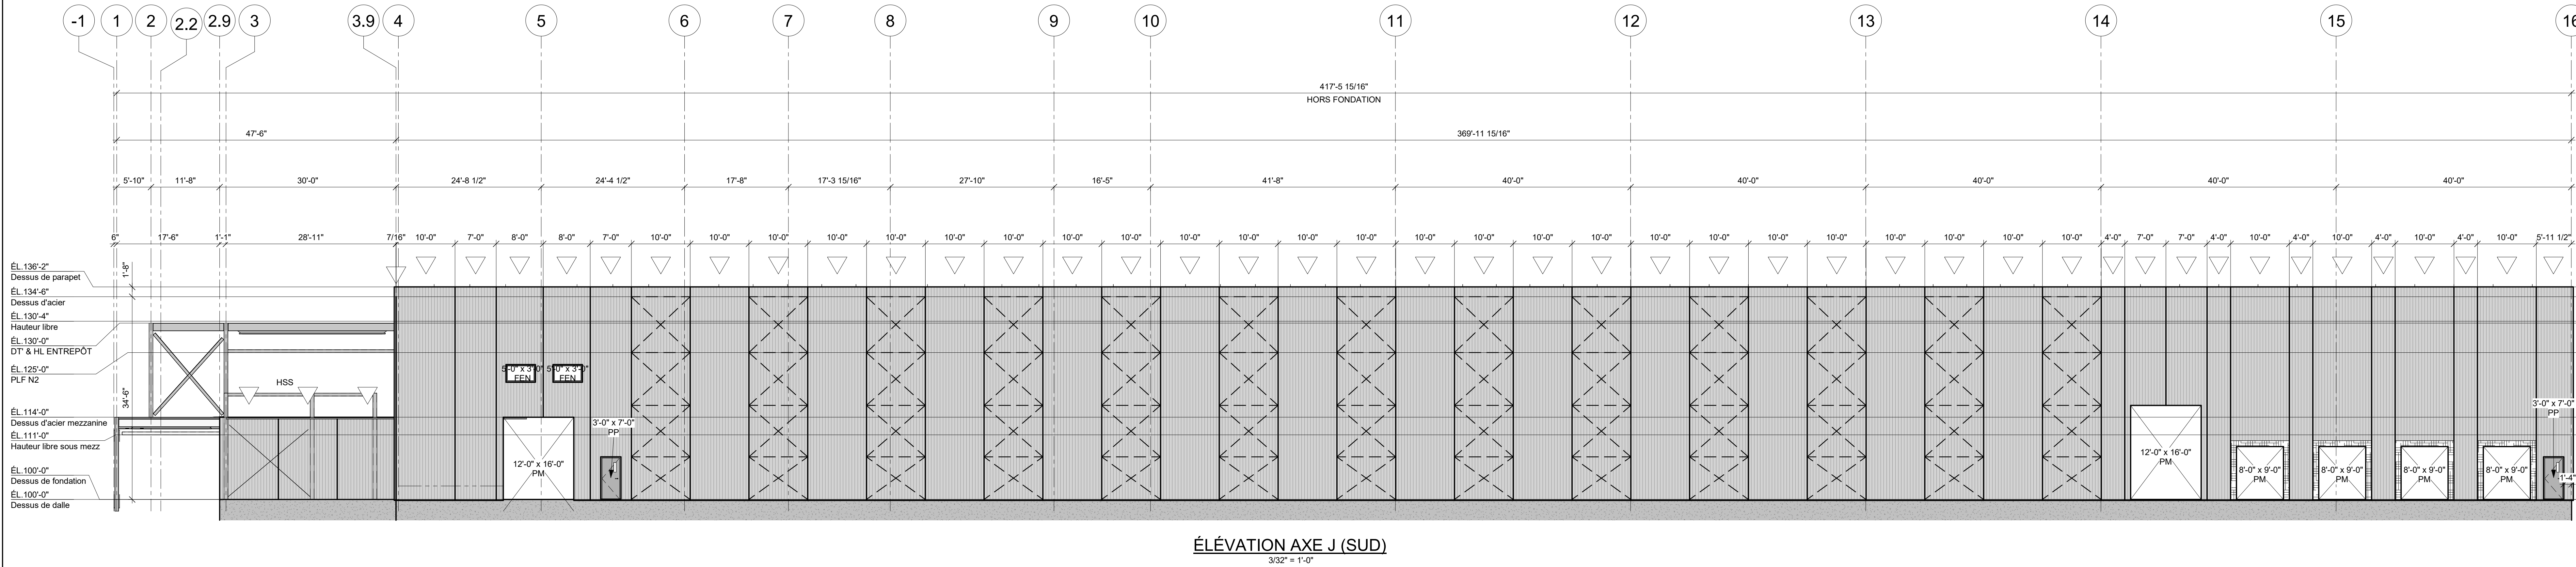


ÉLEVATION AXE J (SUD)
3/32" = 1'-0"

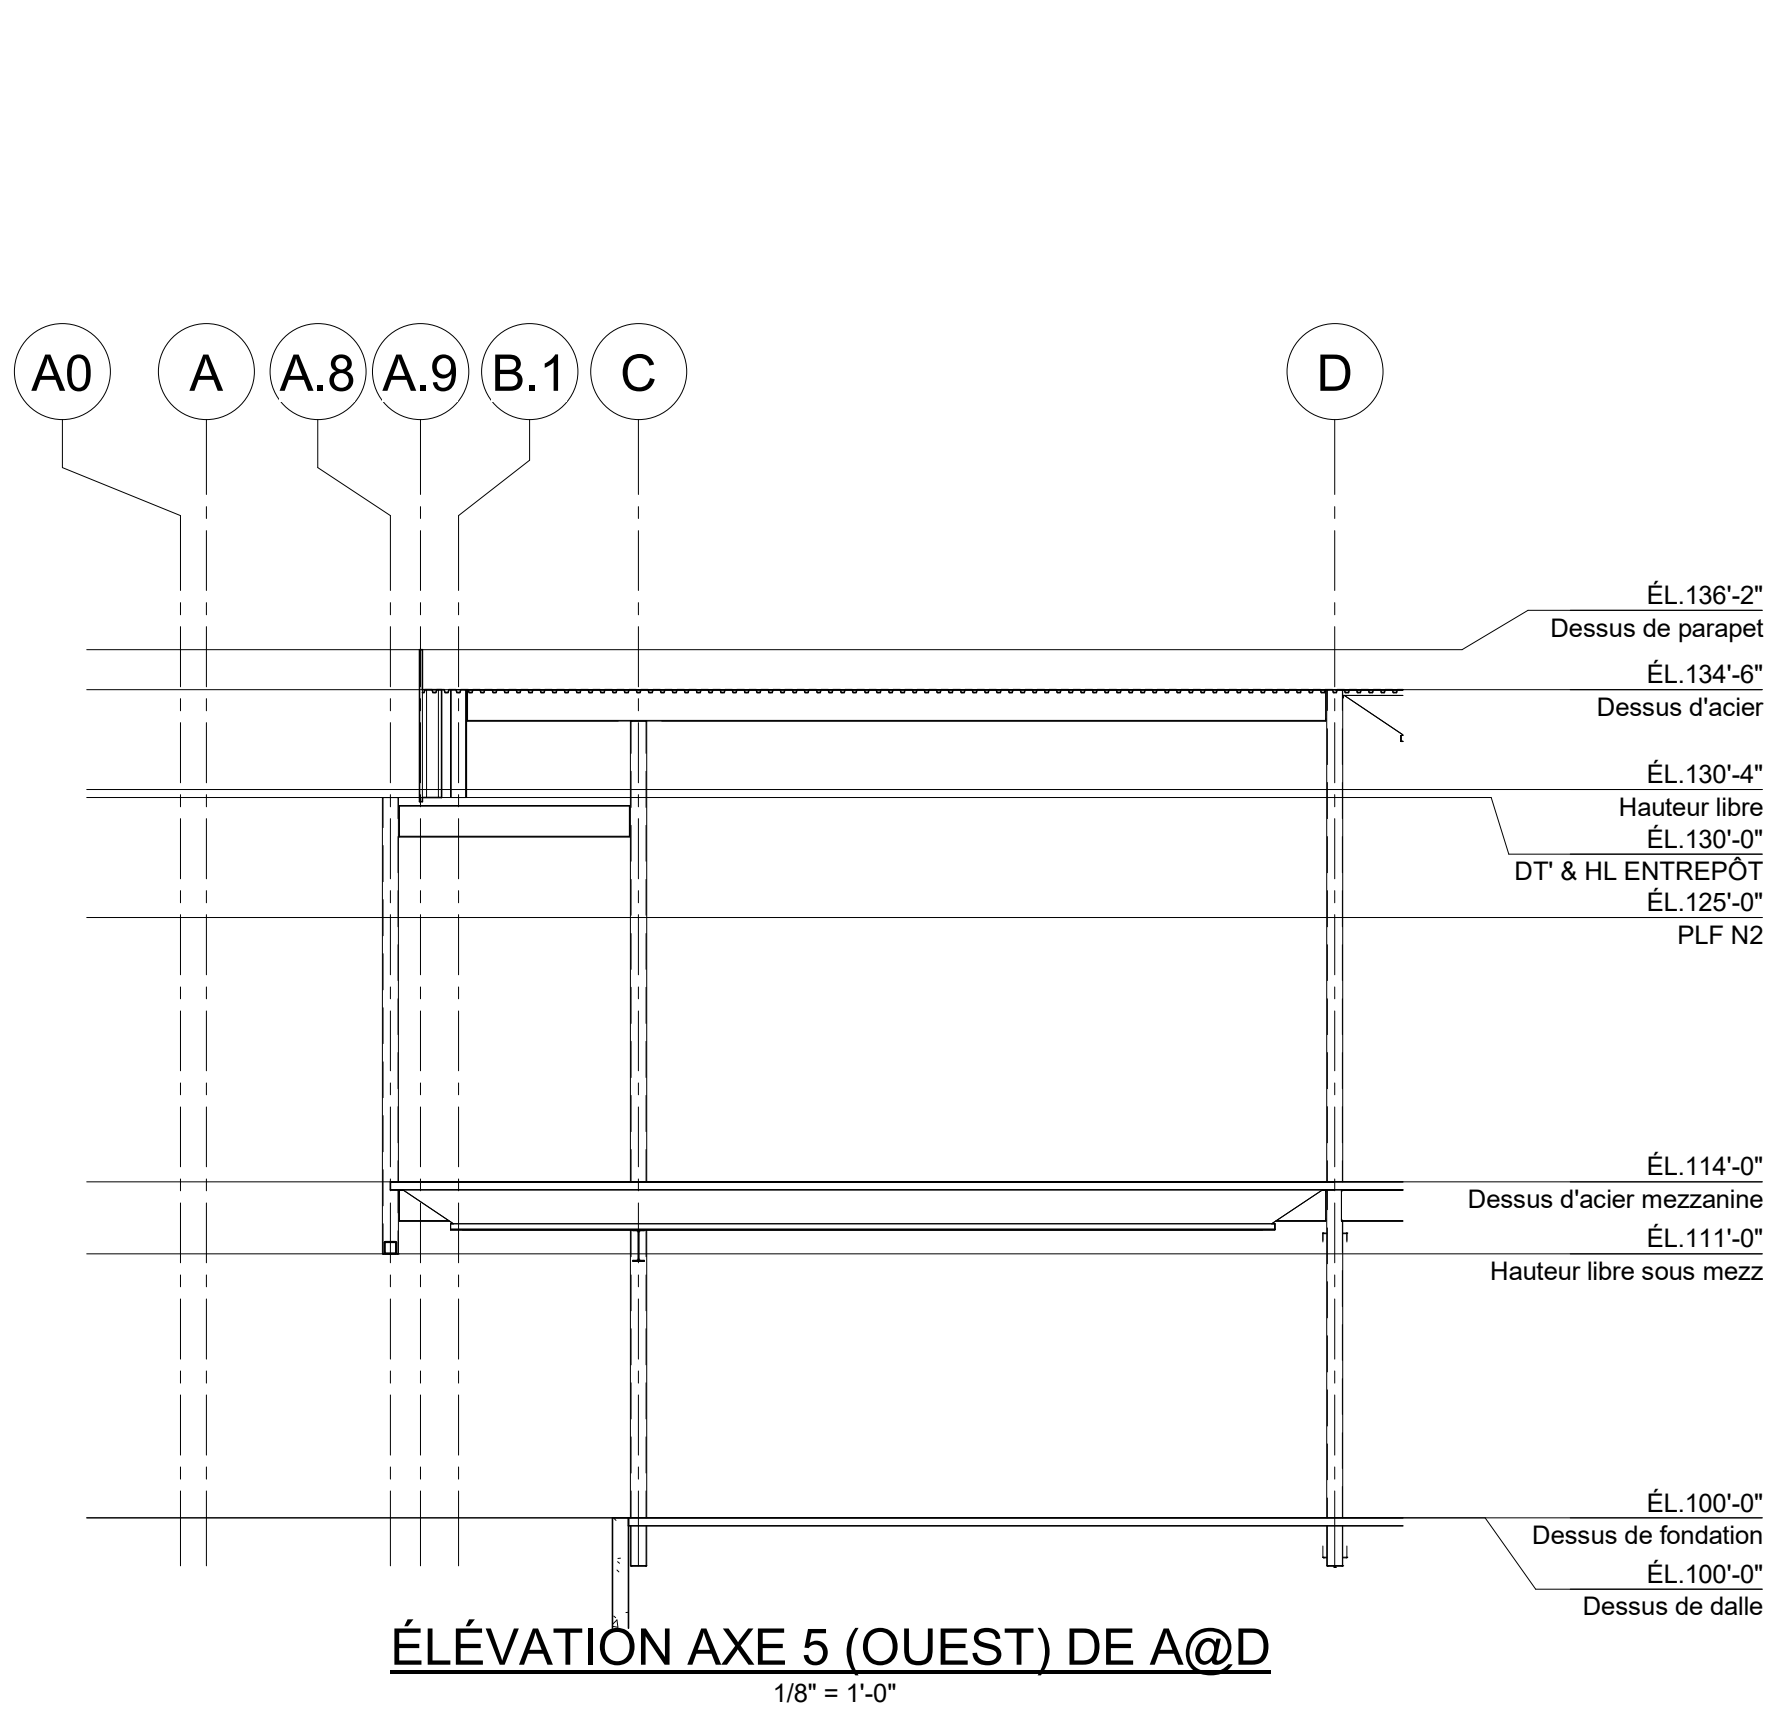


ÉLEVATION AXE 5 (OUEST) DE A@D
1/8" = 1'-0"

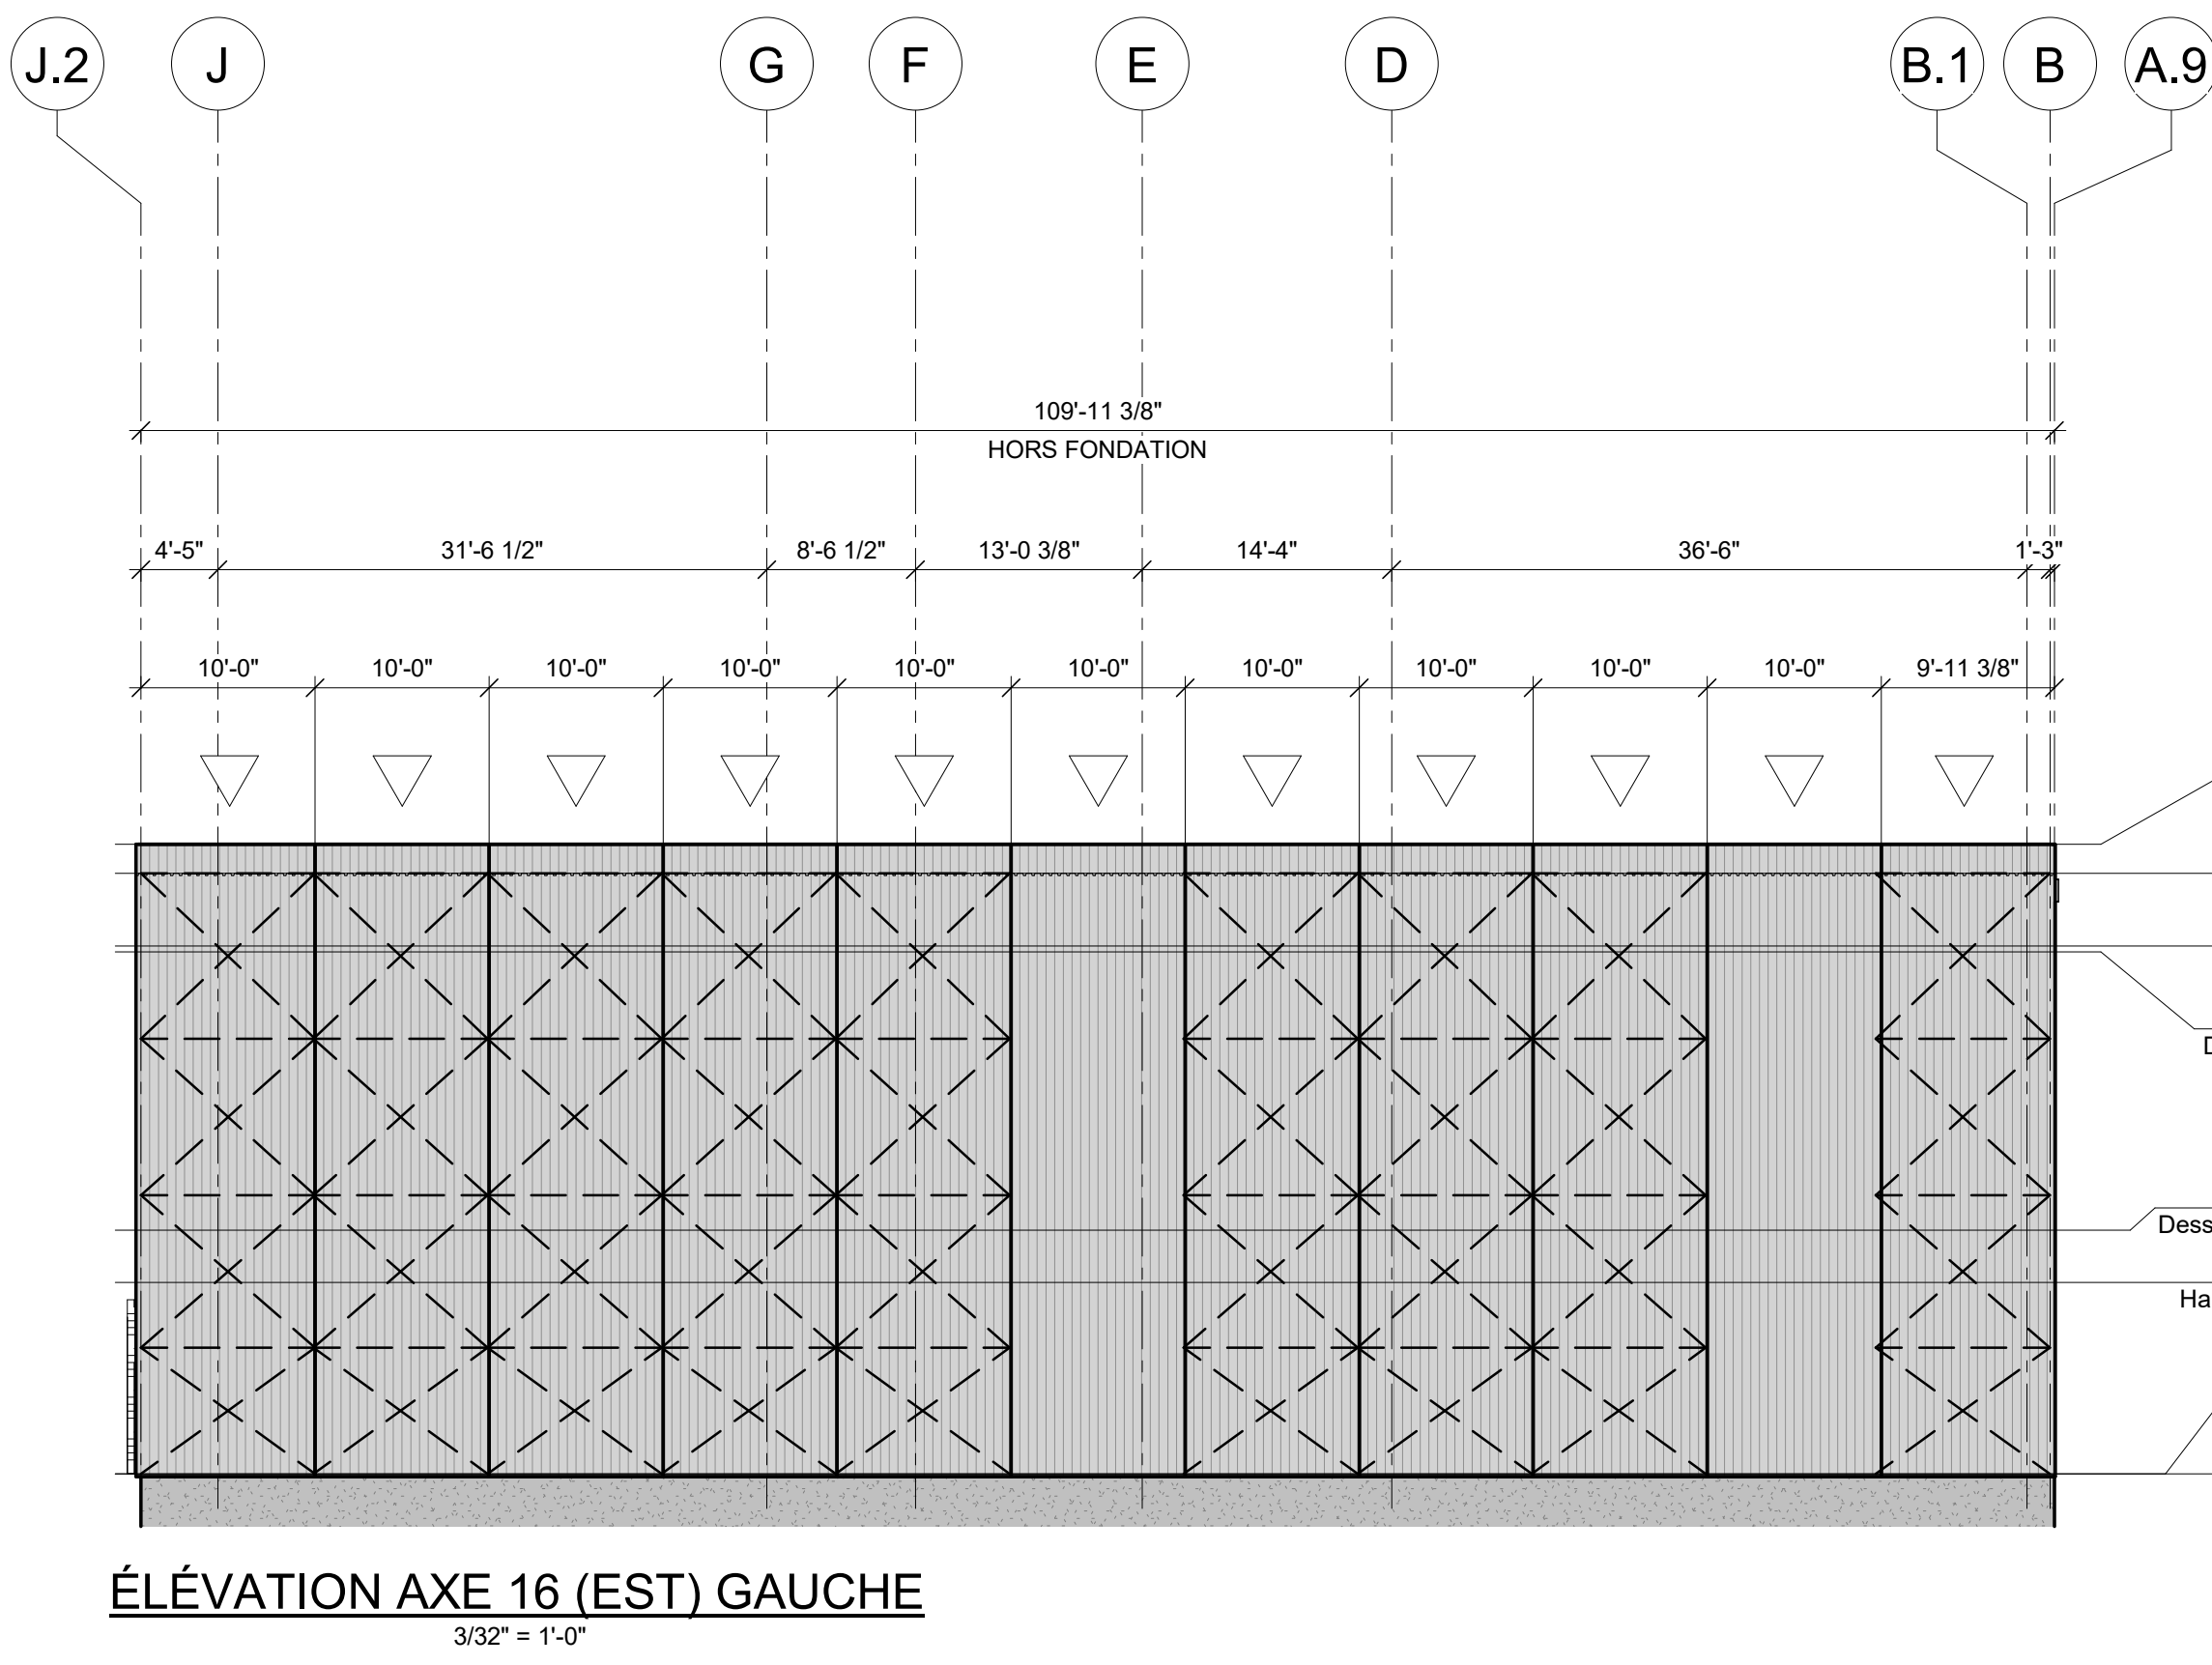

ÉLEVATION AXE 16 (EST) GAUCHE
3/32" = 1'-0"

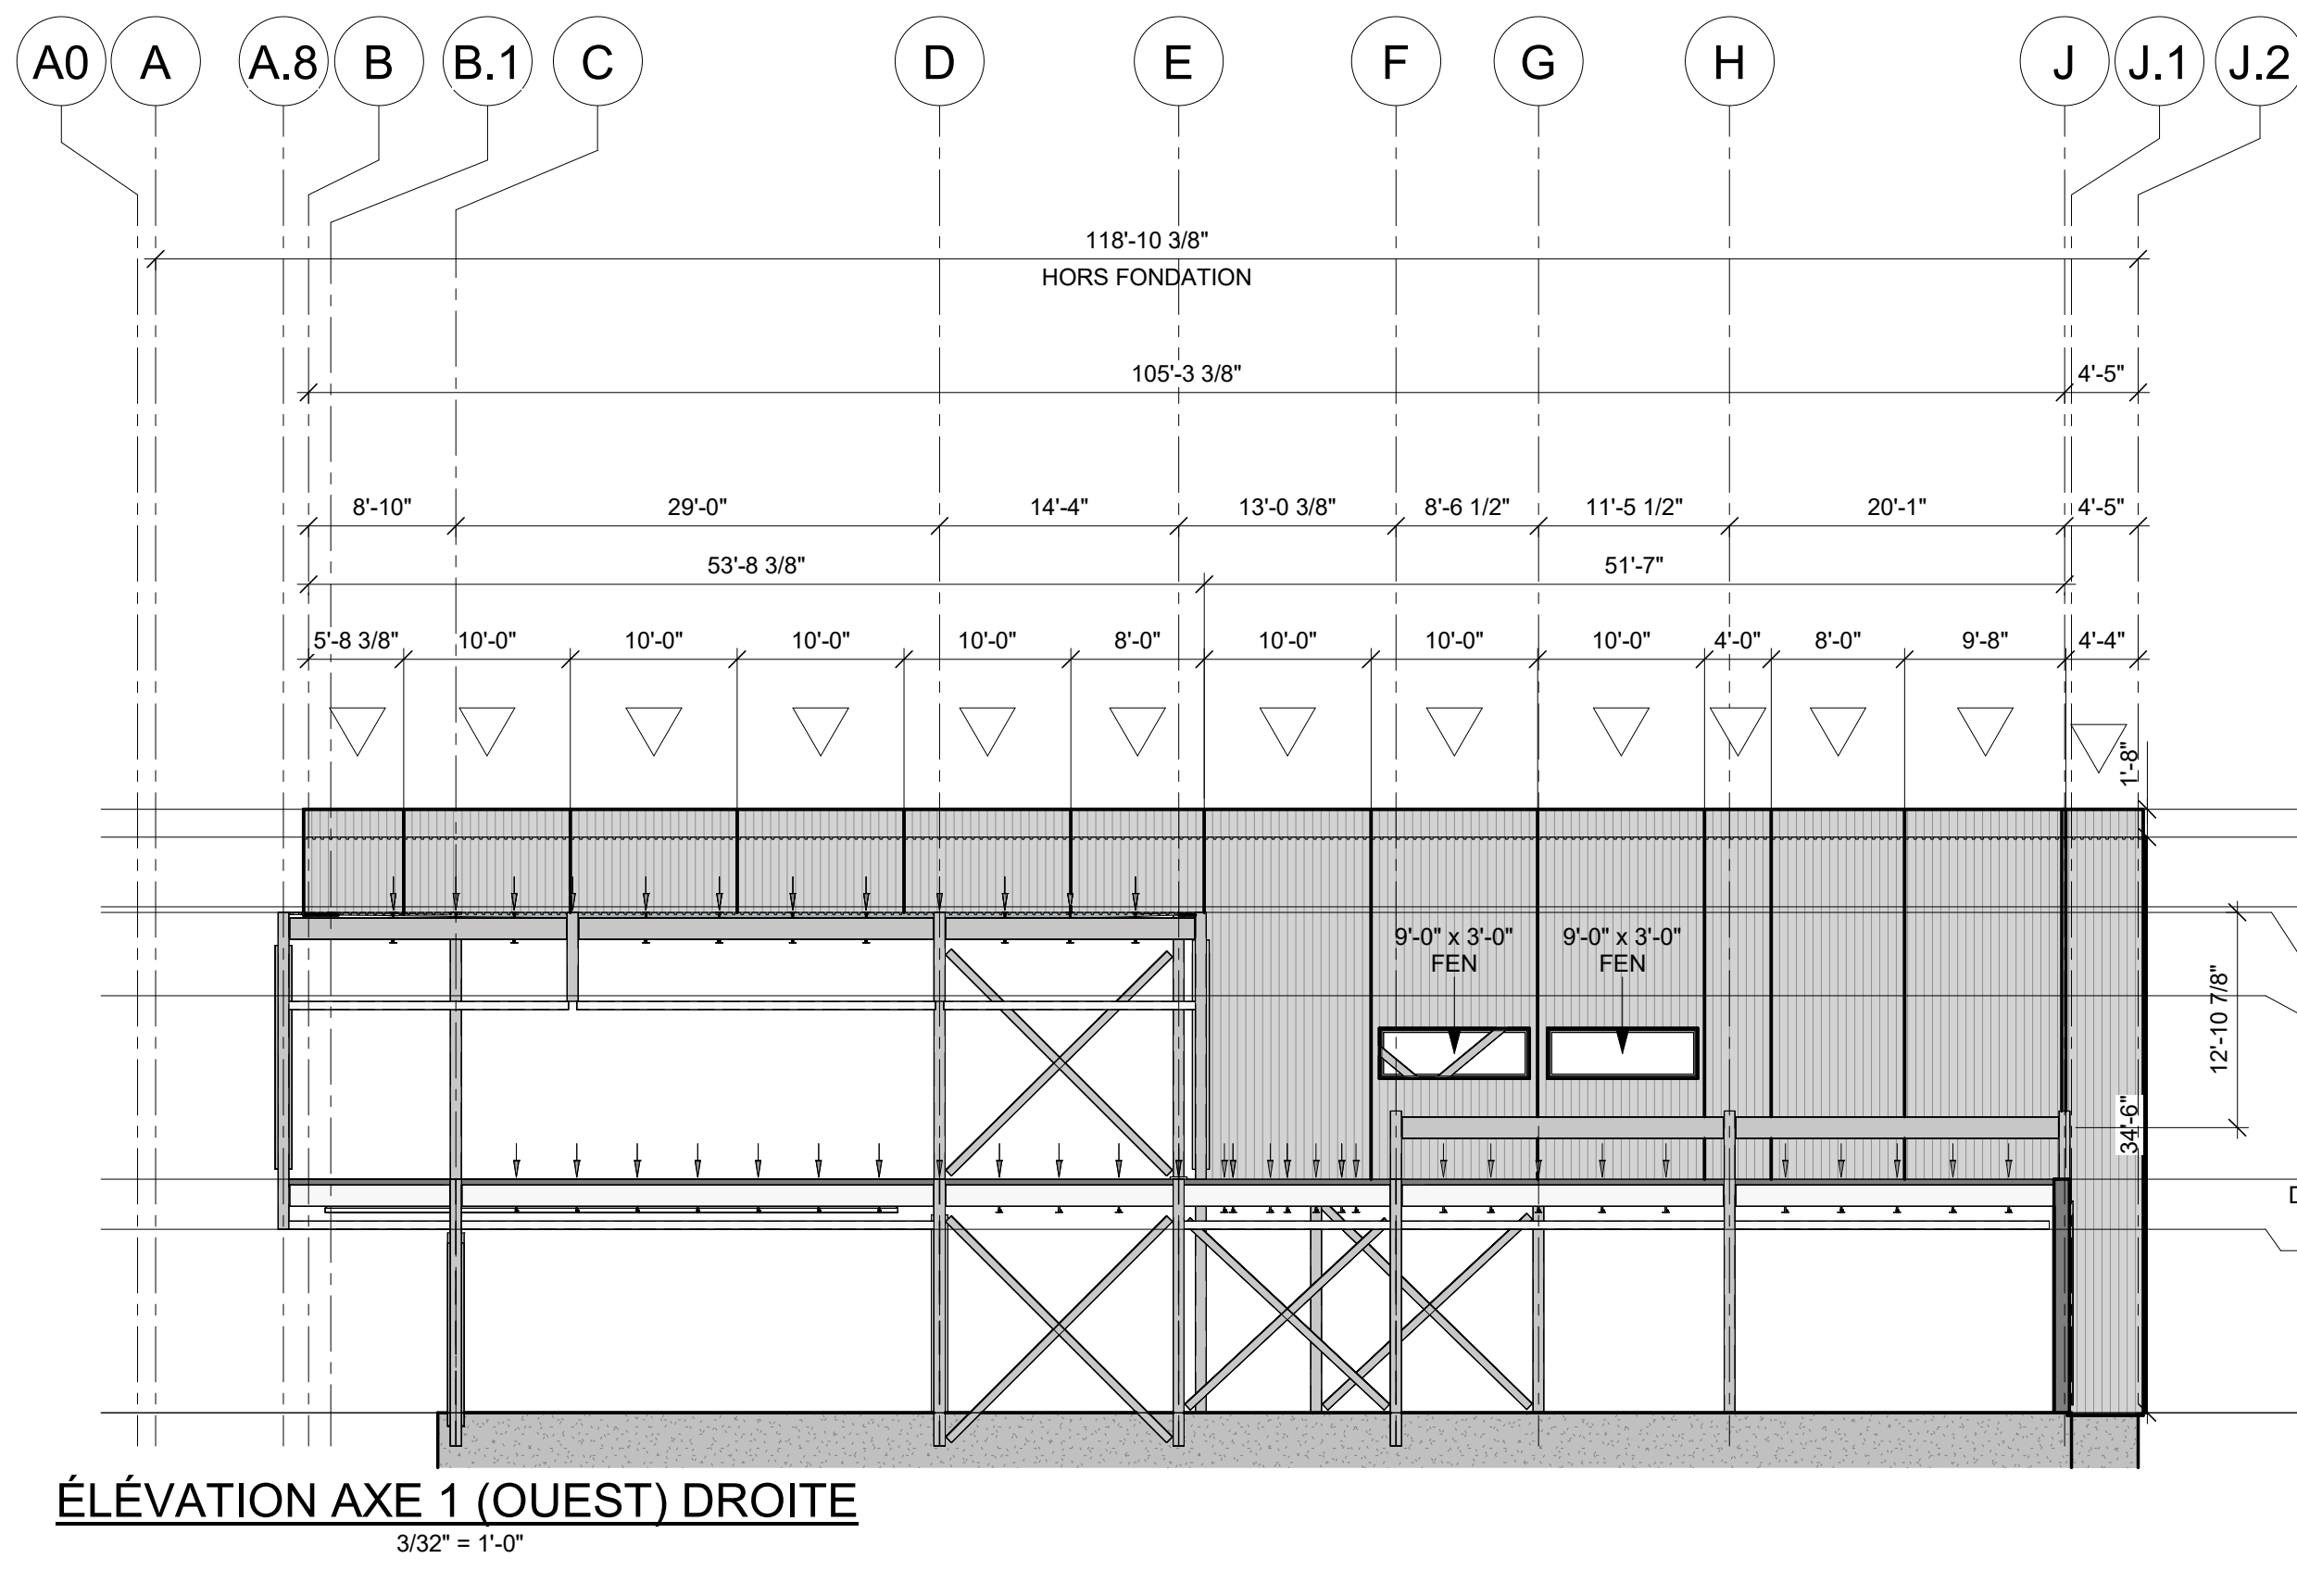

ÉLEVATION AXE 1 (OUEST) DROITE
3/32" = 1'-0"

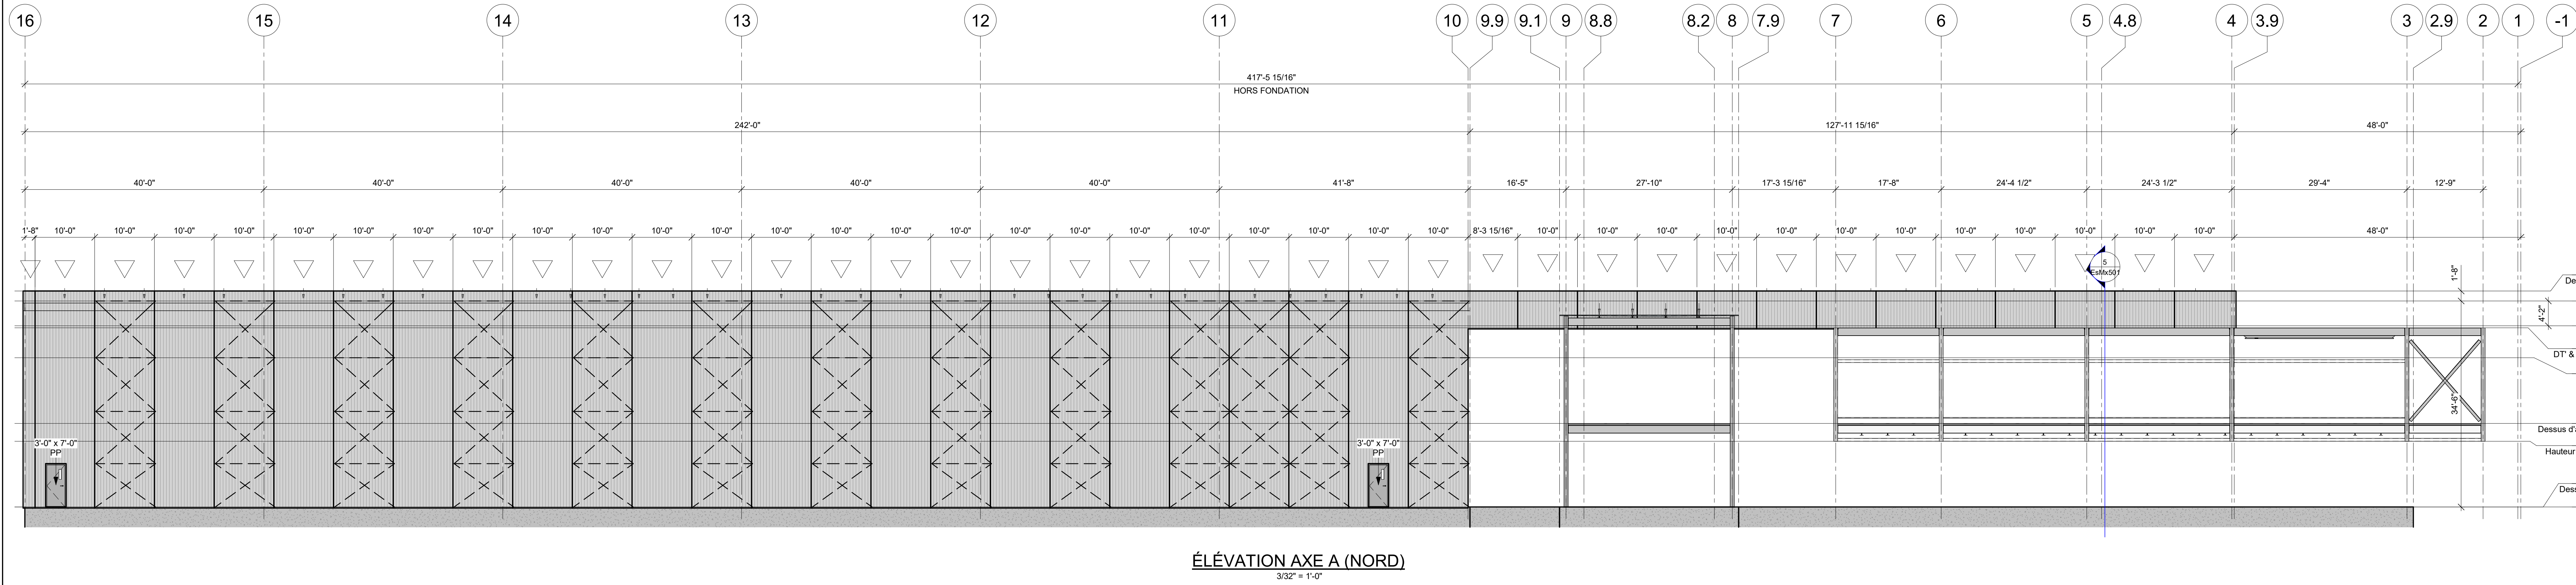

ÉLEVATION AXE A (NORD)
3/32" = 1'-0"

NOTE POUR LE CONTRACTEUR/ÉRECTEUR:
IL EST STRICTEMENT DÉFENDU DE MODIFIER, COPIER, REPRODUIRE OU DE DISTRIBUER CES DESSINS OU QUELQUES REPRÉSENTATIONS DE CES DESSINS, PAR TOUTES SOURCES DE MÉDIA INCLUANT ÉLECTRONIQUEMENT, SANS L'APPROBATION ÉCRITE DE GROUPE CANAM INC.

PRÉLIMINAIRE

NE DOIT PAS SERVIR À LA CONSTRUCTION

REVISION	DATE	DESCRIPTION	DESS	VER
GERANT DE PROJET				
DESSIN				
DESIGNÉ PAR	CONÇU PAR	INGÉNIEUR DU PROJET	ÉCHELLE	
VERIFIÉ PAR	INGÉNIEURS CONSEILS / ARCHITECTES	DATE (mm/aa/aaaa)	Comme indiqué	
CLIENT:	Les constructions Binfet Inc.			

CANAM
11505, 1re Avenue, bureau 500, Saint-Georges Beauport
Québec, Canada G5W 7X3
Téléphone : (418) 228-8031
Sans frais : (877) 459-8049
www.canam.com

SCAUX PROFESSIONNEL	
PROJET	Nouveau Bâtiment CMI Motors St-Georges
TITRE	CROQUIS PRÉLIMINAIRE - ÉLEVATIONS

NUMÉRO CONTRAT	NUMÉRO DESSIN	DIVISION	REVISION
P2026-043	EsMx501		