


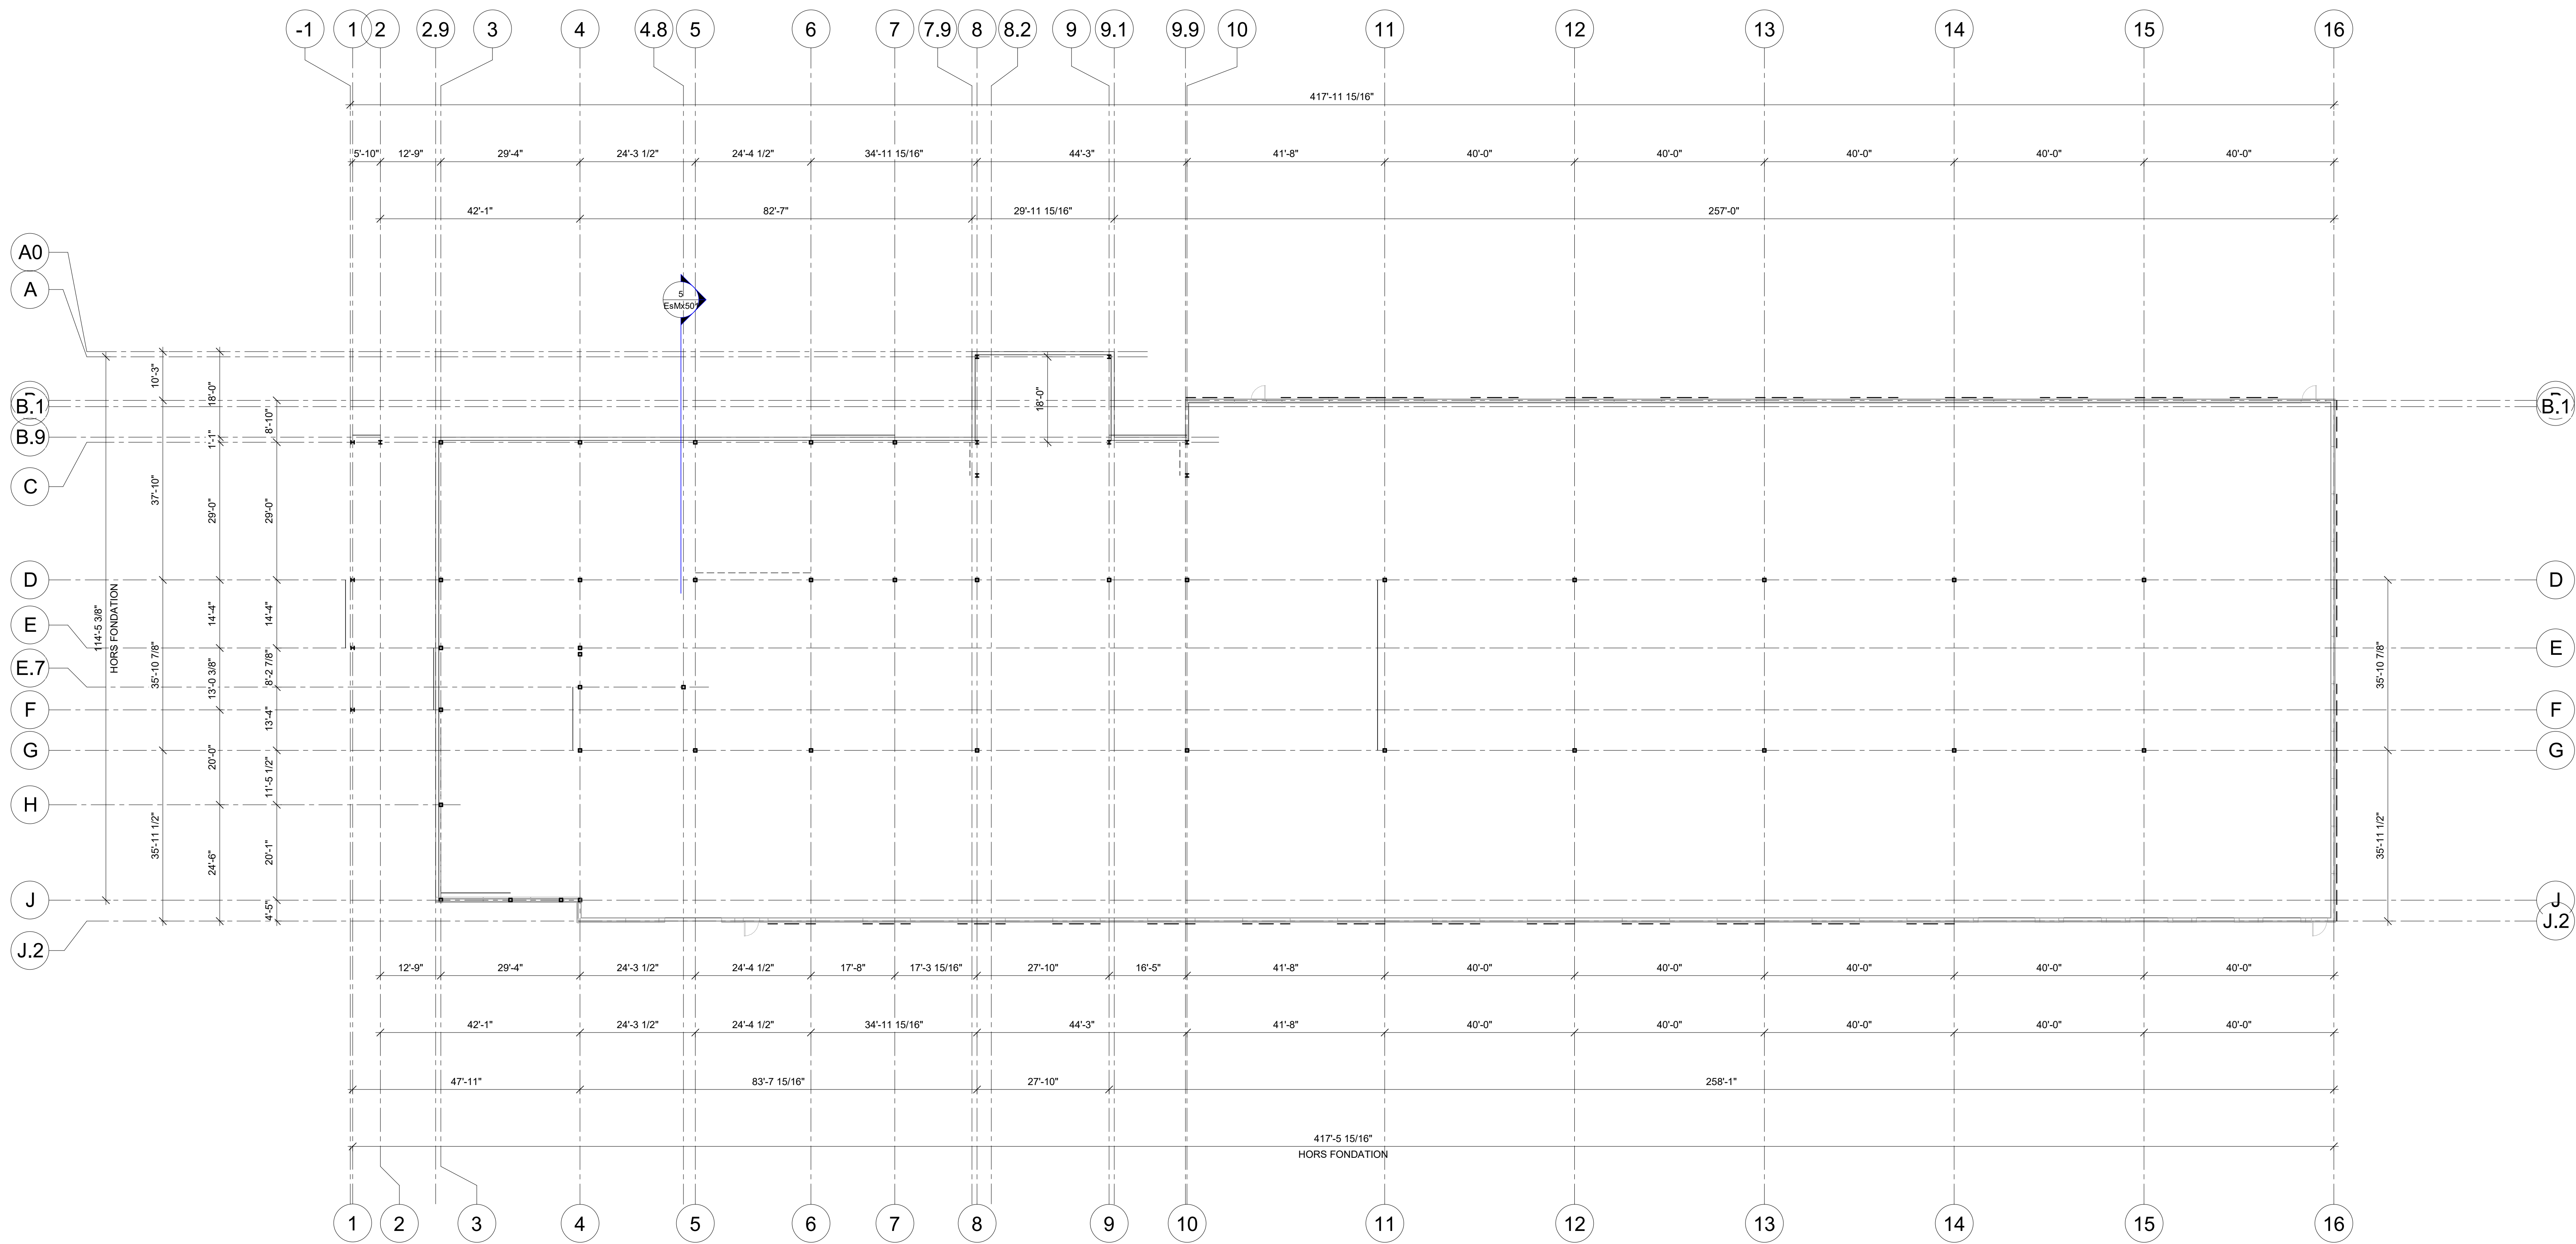

PLAN D'ANCRAGE
1/16" = 1'-0"

PRÉLIMINAIRE

NE DOIT PAS SERVIR À LA
CONSTRUCTION

REVISION	DATE	DESCRIPTION	DESS	VER
----------	------	-------------	------	-----

GERANT DE PROJET	-
	-
	-
	-

DESSIN

DESSINÉ PAR HSC	CONÇU PAR	INGÉNIEUR DU PROJET	ÉCHELLE: 1/16" = 1'-0"
VERIFIÉ PAR	INGÉNIEURS CONSEILS / ARCHITECTES	DATE (mm/aa/aaaa)	02/03/2026

CLIENT: Les constructions Binet Inc.



SCHEAU PROFESSIONNEL

PROJET

Nouveau Bâtiment CMI Motors
St-Georges

TITRE
CROQUIS PRÉLIMINAIRE - PLAN
D'ANCRAGE

NUMERO CONTRAT	NUMERO DESSIN	DIVISION	REVISION
P2026-043	EsMx101		

Initiales

