


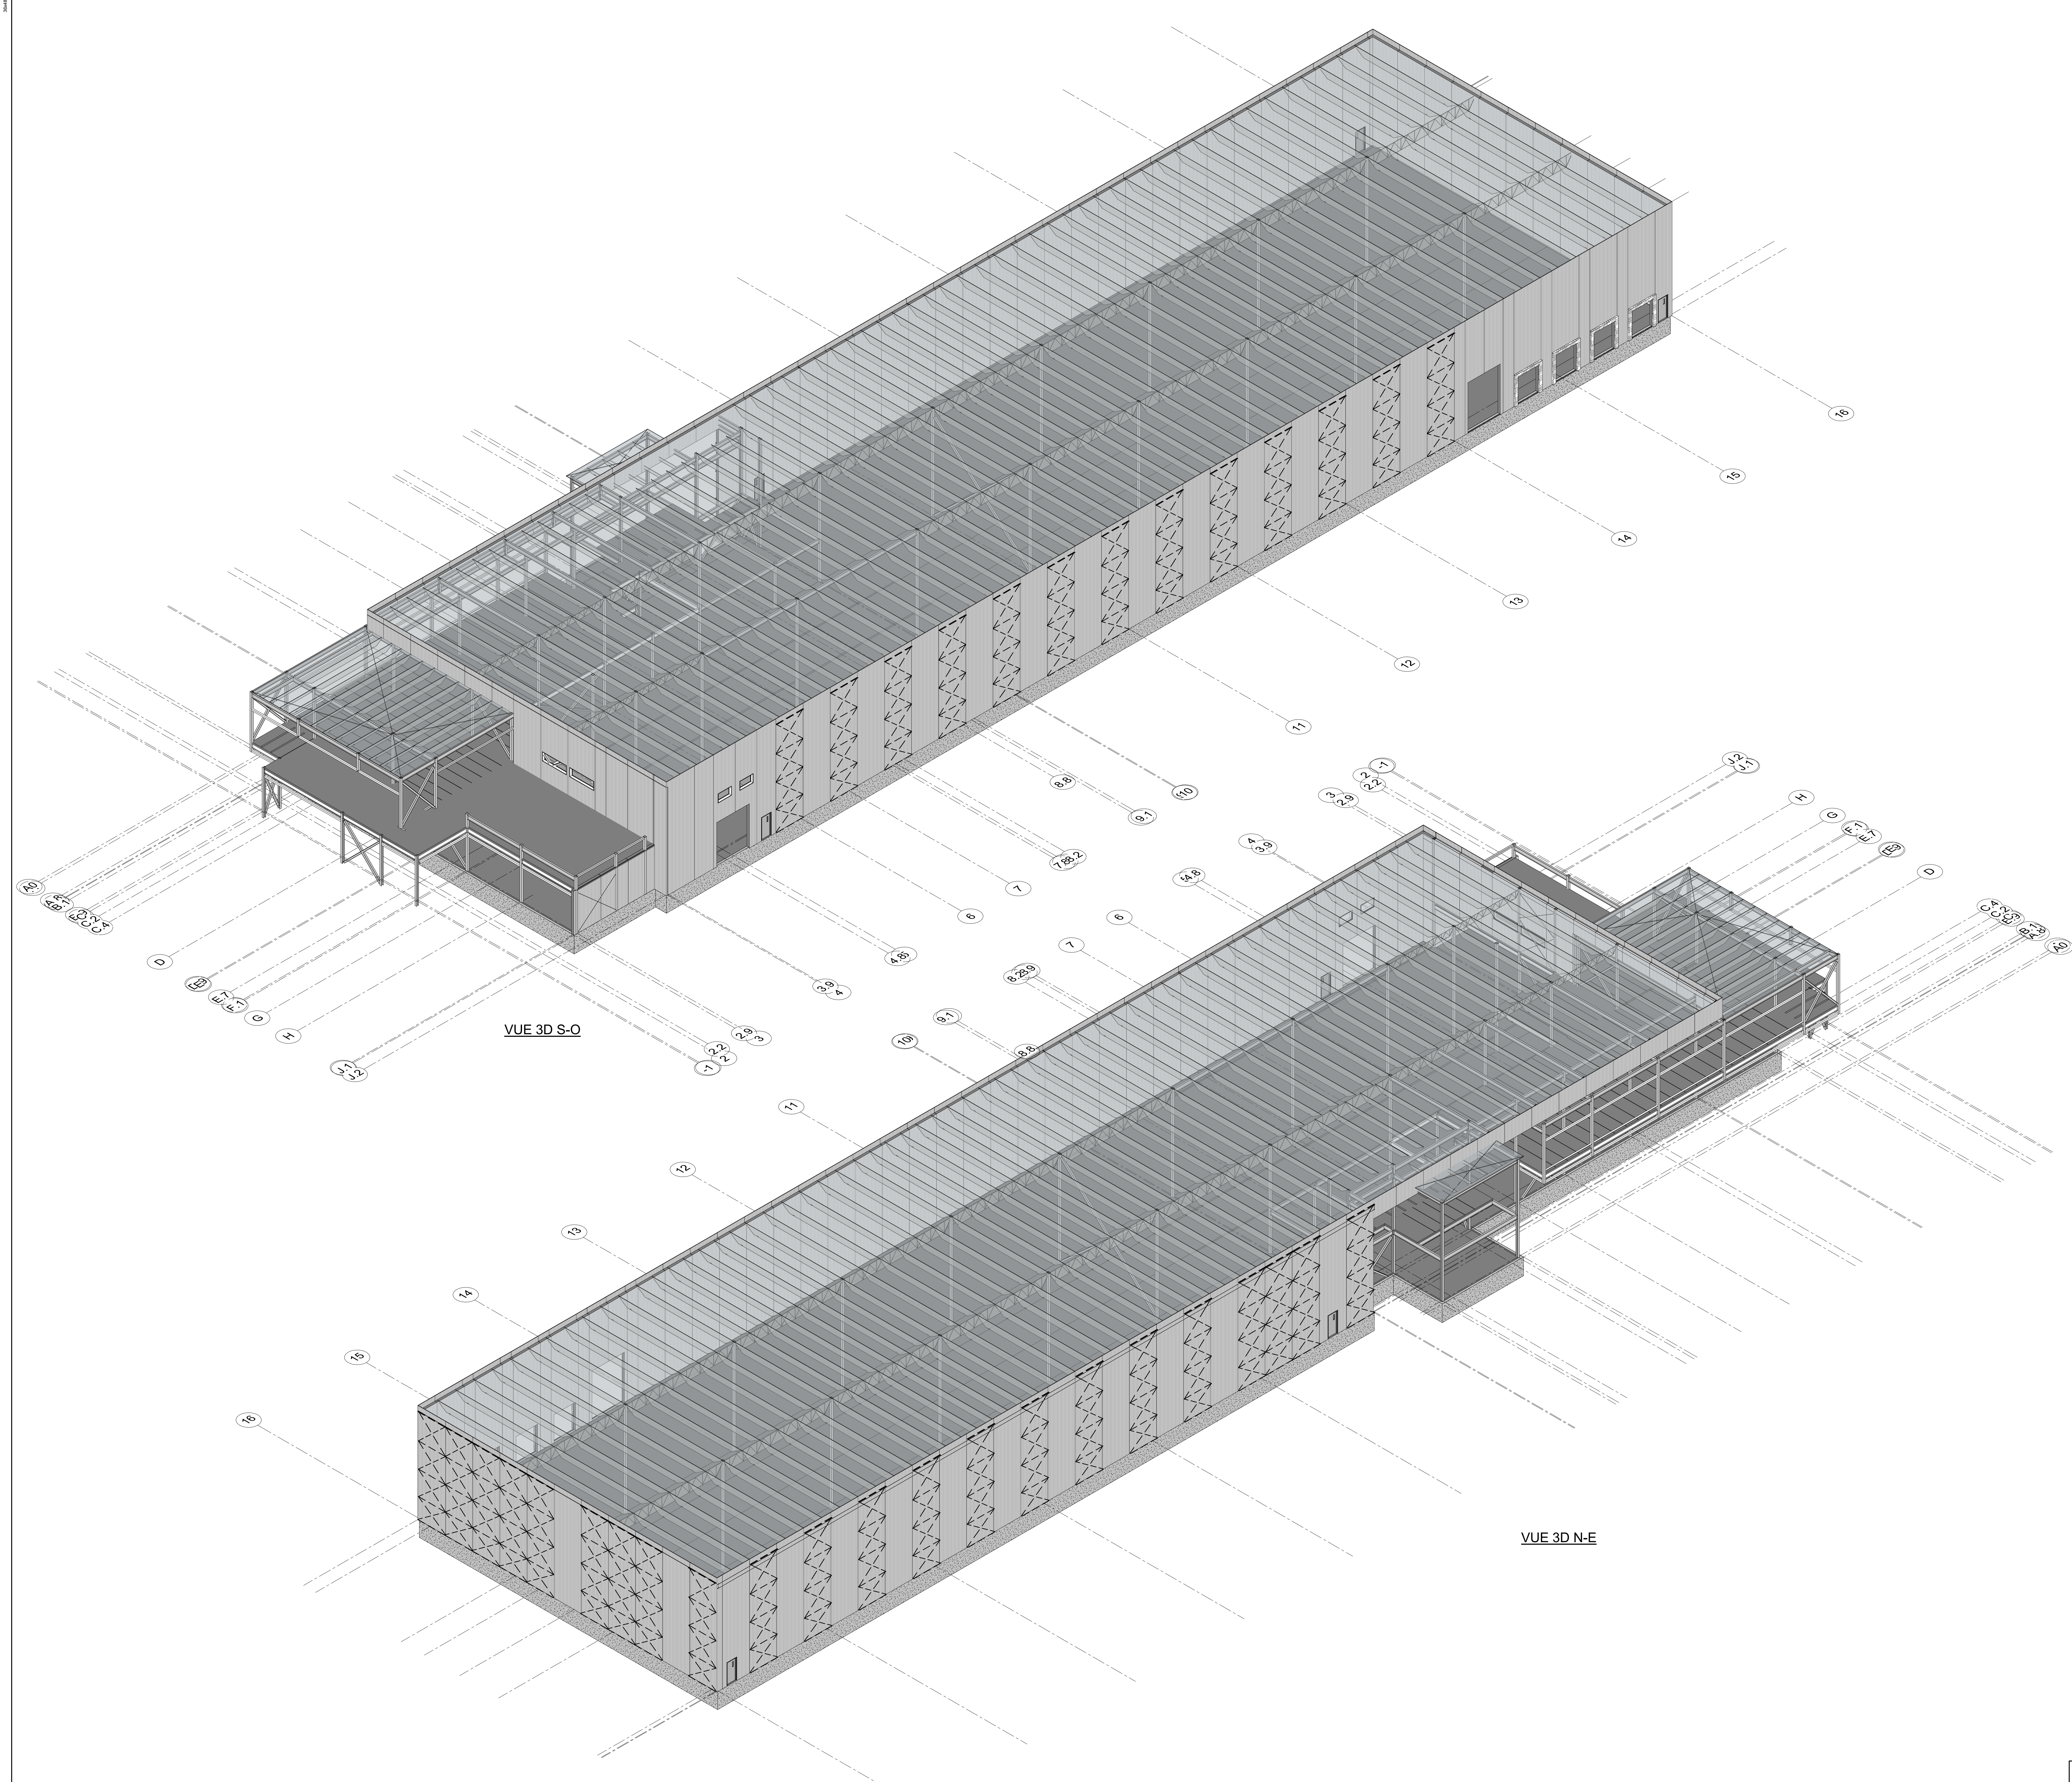

VUE 3D S-O

VUE 3D N-E


NOTE POUR LE CONTRACTEUR/ÉRECTEUR:
IL EST STRICTEMENT DÉFENDU DE MODIFIER, COPIER, REPRODUIRE OU DE DISTRIBUER CES DESSINS OU QUELQUES REPRÉSENTATIONS DE CES DESSINS PAR TOUTES SOURCES DE MÉDIA INCLUANT ÉLECTRONIQUEMENT, SANS L'APPROBATION ÉCRITE DE GROUPE CANAM INC.

LISTE DES FEUILLES PRÉLIMINAIRES	
EsMx001	CROQUIS PRÉLIMINAIRE - VUES 3D
EsMx101	CROQUIS PRÉLIMINAIRE - PLAN D'ANCRAGE
EsMx201	CROQUIS PRÉLIMINAIRE - PLAN DE MEZZANINE
EsMx401	CROQUIS PRÉLIMINAIRE - PLAN DE TOIT
EsMx501	CROQUIS PRÉLIMINAIRE - ÉLEVATIONS
EsMx502	CROQUIS PRÉLIMINAIRE - ÉLEVATION, COUPE DE MUR ET CÉDALES
EsMx601	CROQUIS PRÉLIMINAIRE - DÉTAILS


[Cliquez ici pour modèle 3D](#)

PRÉLIMINAIRE

NE DOIT PAS SERVIR À LA CONSTRUCTION

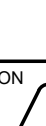REVISION	DATE	DESCRIPTION	DESS	VER
GERANT DE PROJET				
		-		
		-		
		-		
		-		
DESSIN				
DESSINÉ PAR	CONÇU PAR	INGÉNIEUR DU PROJET	ÉCHELLE:	
HSC			12" = 1'-0"	
VÉRIFIÉ PAR	INGÉNIEURS CONSEILS / ARCHITECTES		DATE (jj/mm/aaaa)	
			02/03/2026	
CLIENT:	Les constructions Binet Inc.			
 CANAM 11505, 1re Avenue, bureau 500, Saint-Georges Beauce Québec, Canada, G5Y 7G5 Téléphone : (418) 228-8031 Sans frais : (877) 459-8049 www.canam.com				
SCÉAU PROFESSIONNEL				
PROJET				
Nouveau Bâtiment CMI Motors St-Georges				
TITRE				
CROQUIS PRÉLIMINAIRE - VUES 3D				
NUMÉRO CONTRAT P2026-043	NUMÉRO DESSIN EsMx001	DIVISION	REVISION	
				

Initiales

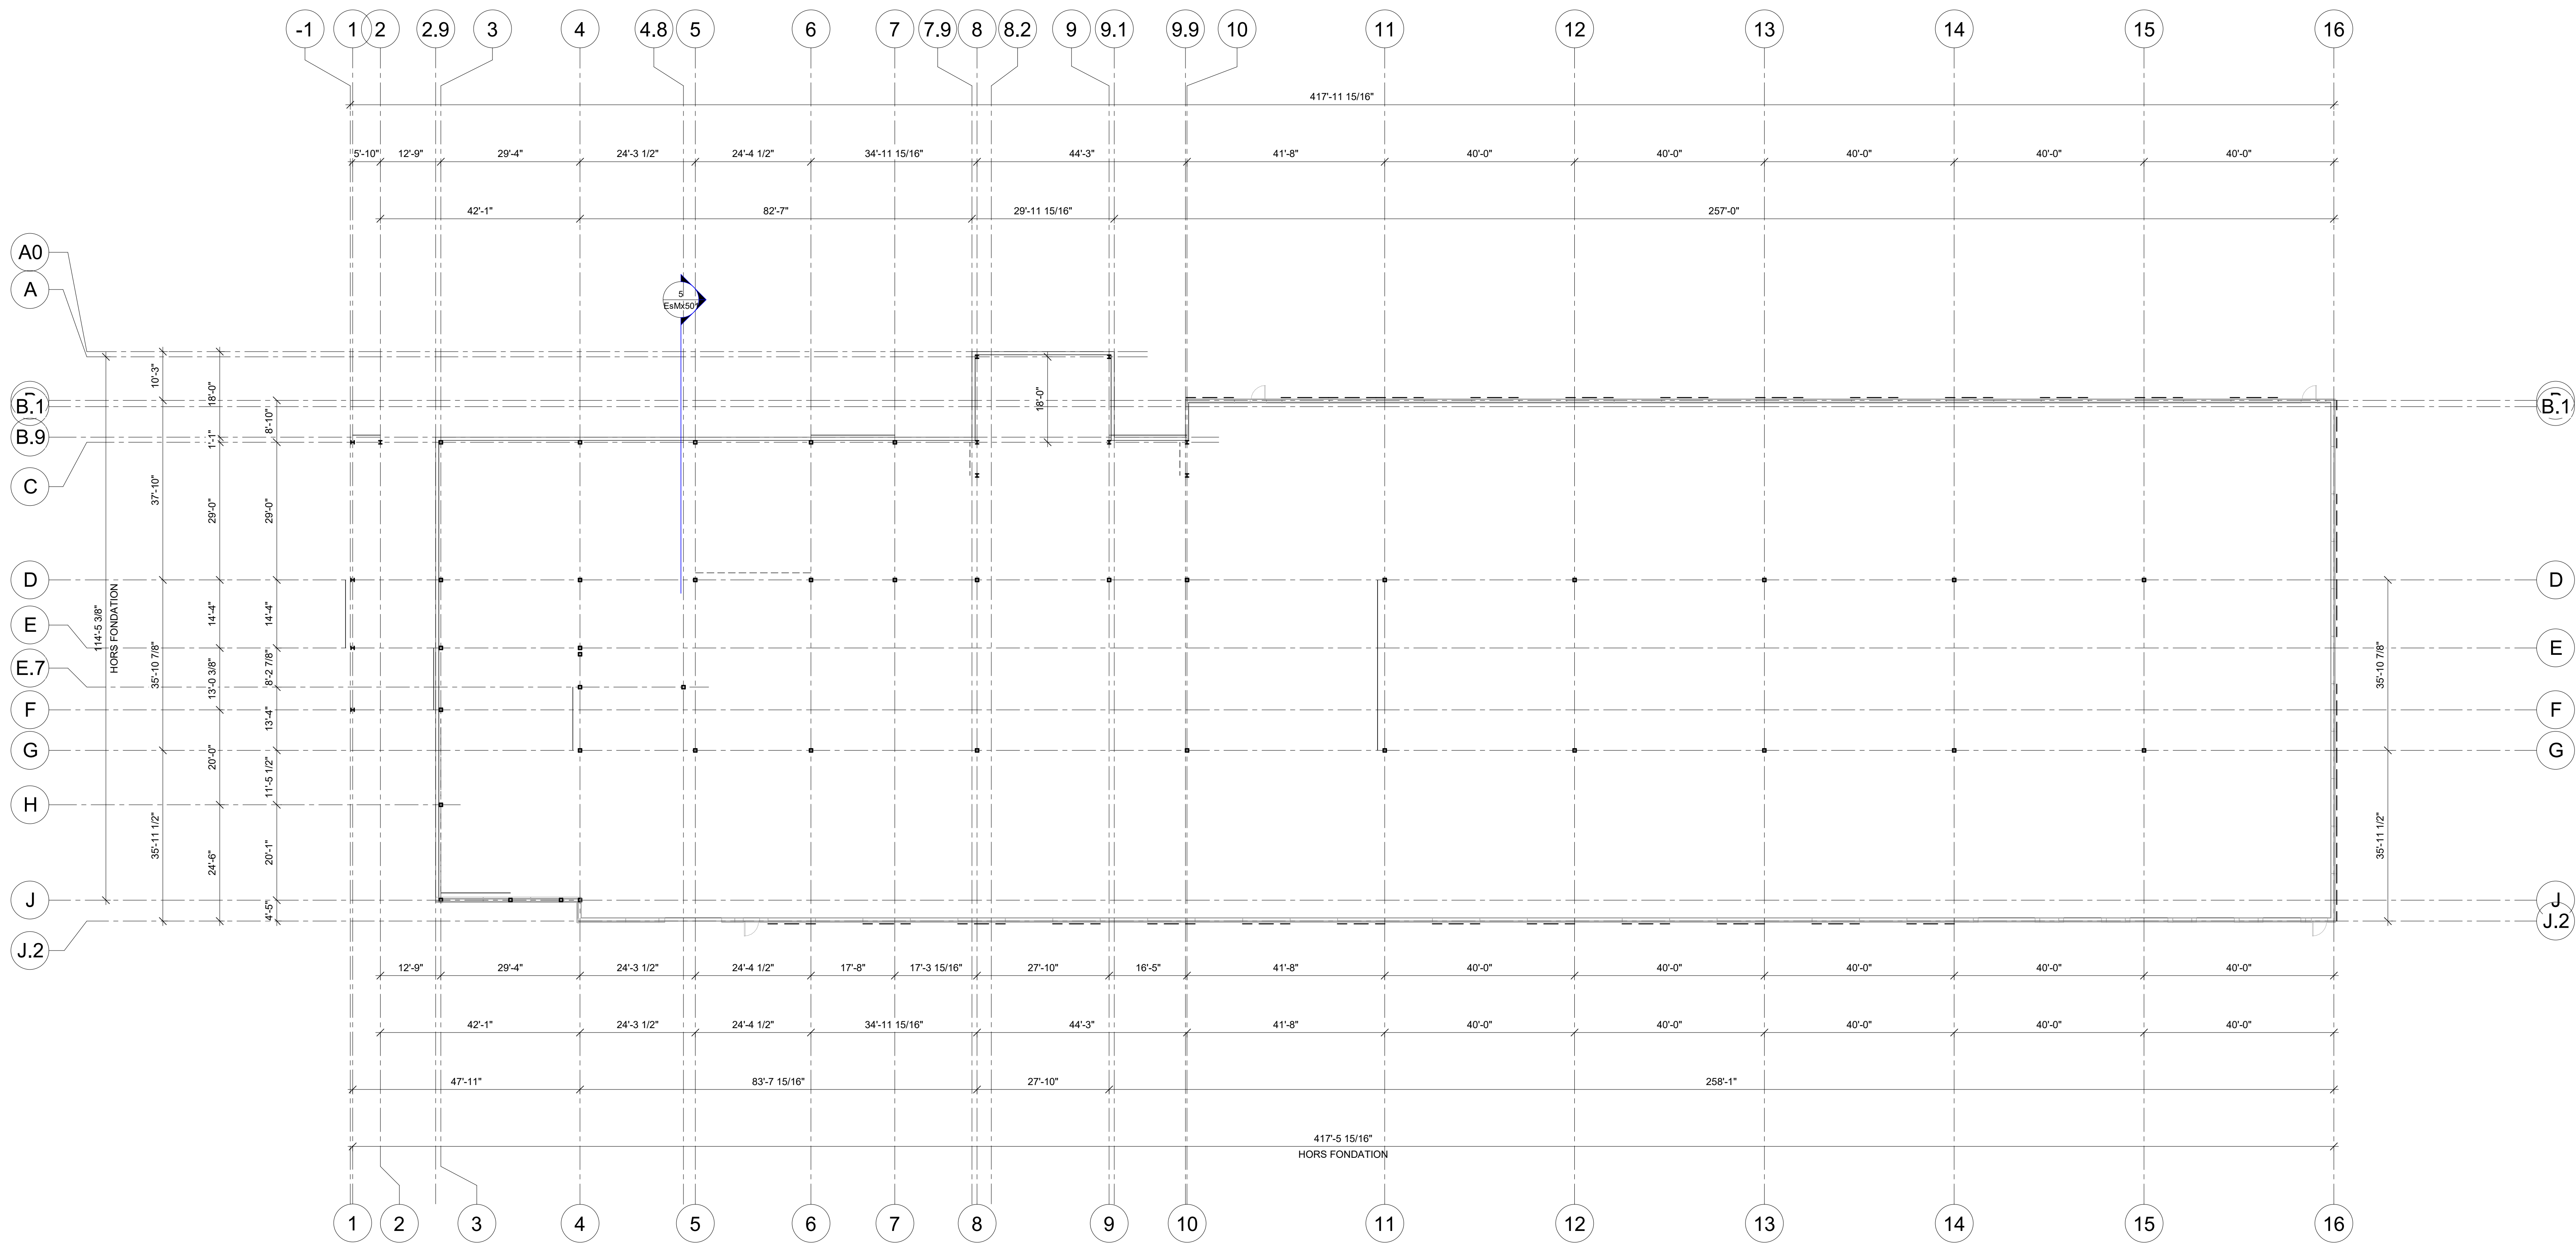

PLAN D'ANCRAGE
1/16" = 1'-0"

PRÉLIMINAIRE

NE DOIT PAS SERVIR À LA
CONSTRUCTION

REVISION	DATE	DESCRIPTION	DESS	VER
----------	------	-------------	------	-----

GERANT DE PROJET	-
-	-
-	-
-	-

DESSIN

DESSINÉ PAR HSC	CONÇU PAR	INGÉNIEUR DU PROJET	ÉCHELLE: 1/16" = 1'-0"
VERIFIÉ PAR	INGÉNIEURS CONSEILS / ARCHITECTES	DATE (mm/aaaa)	02/03/2026

CLIENT: Les constructions Binet Inc.



SCHEAU PROFESSIONNEL


PROJET


Nouveau Bâtiment CMI Motors
St-Georges

TITRE
CROQUIS PRÉLIMINAIRE - PLAN
D'ANCRAGE

NUMERO CONTRAT	NUMERO DESSIN	DIVISION	REVISION
P2026-043	EsMx101		

Initiales

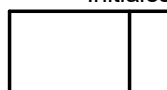

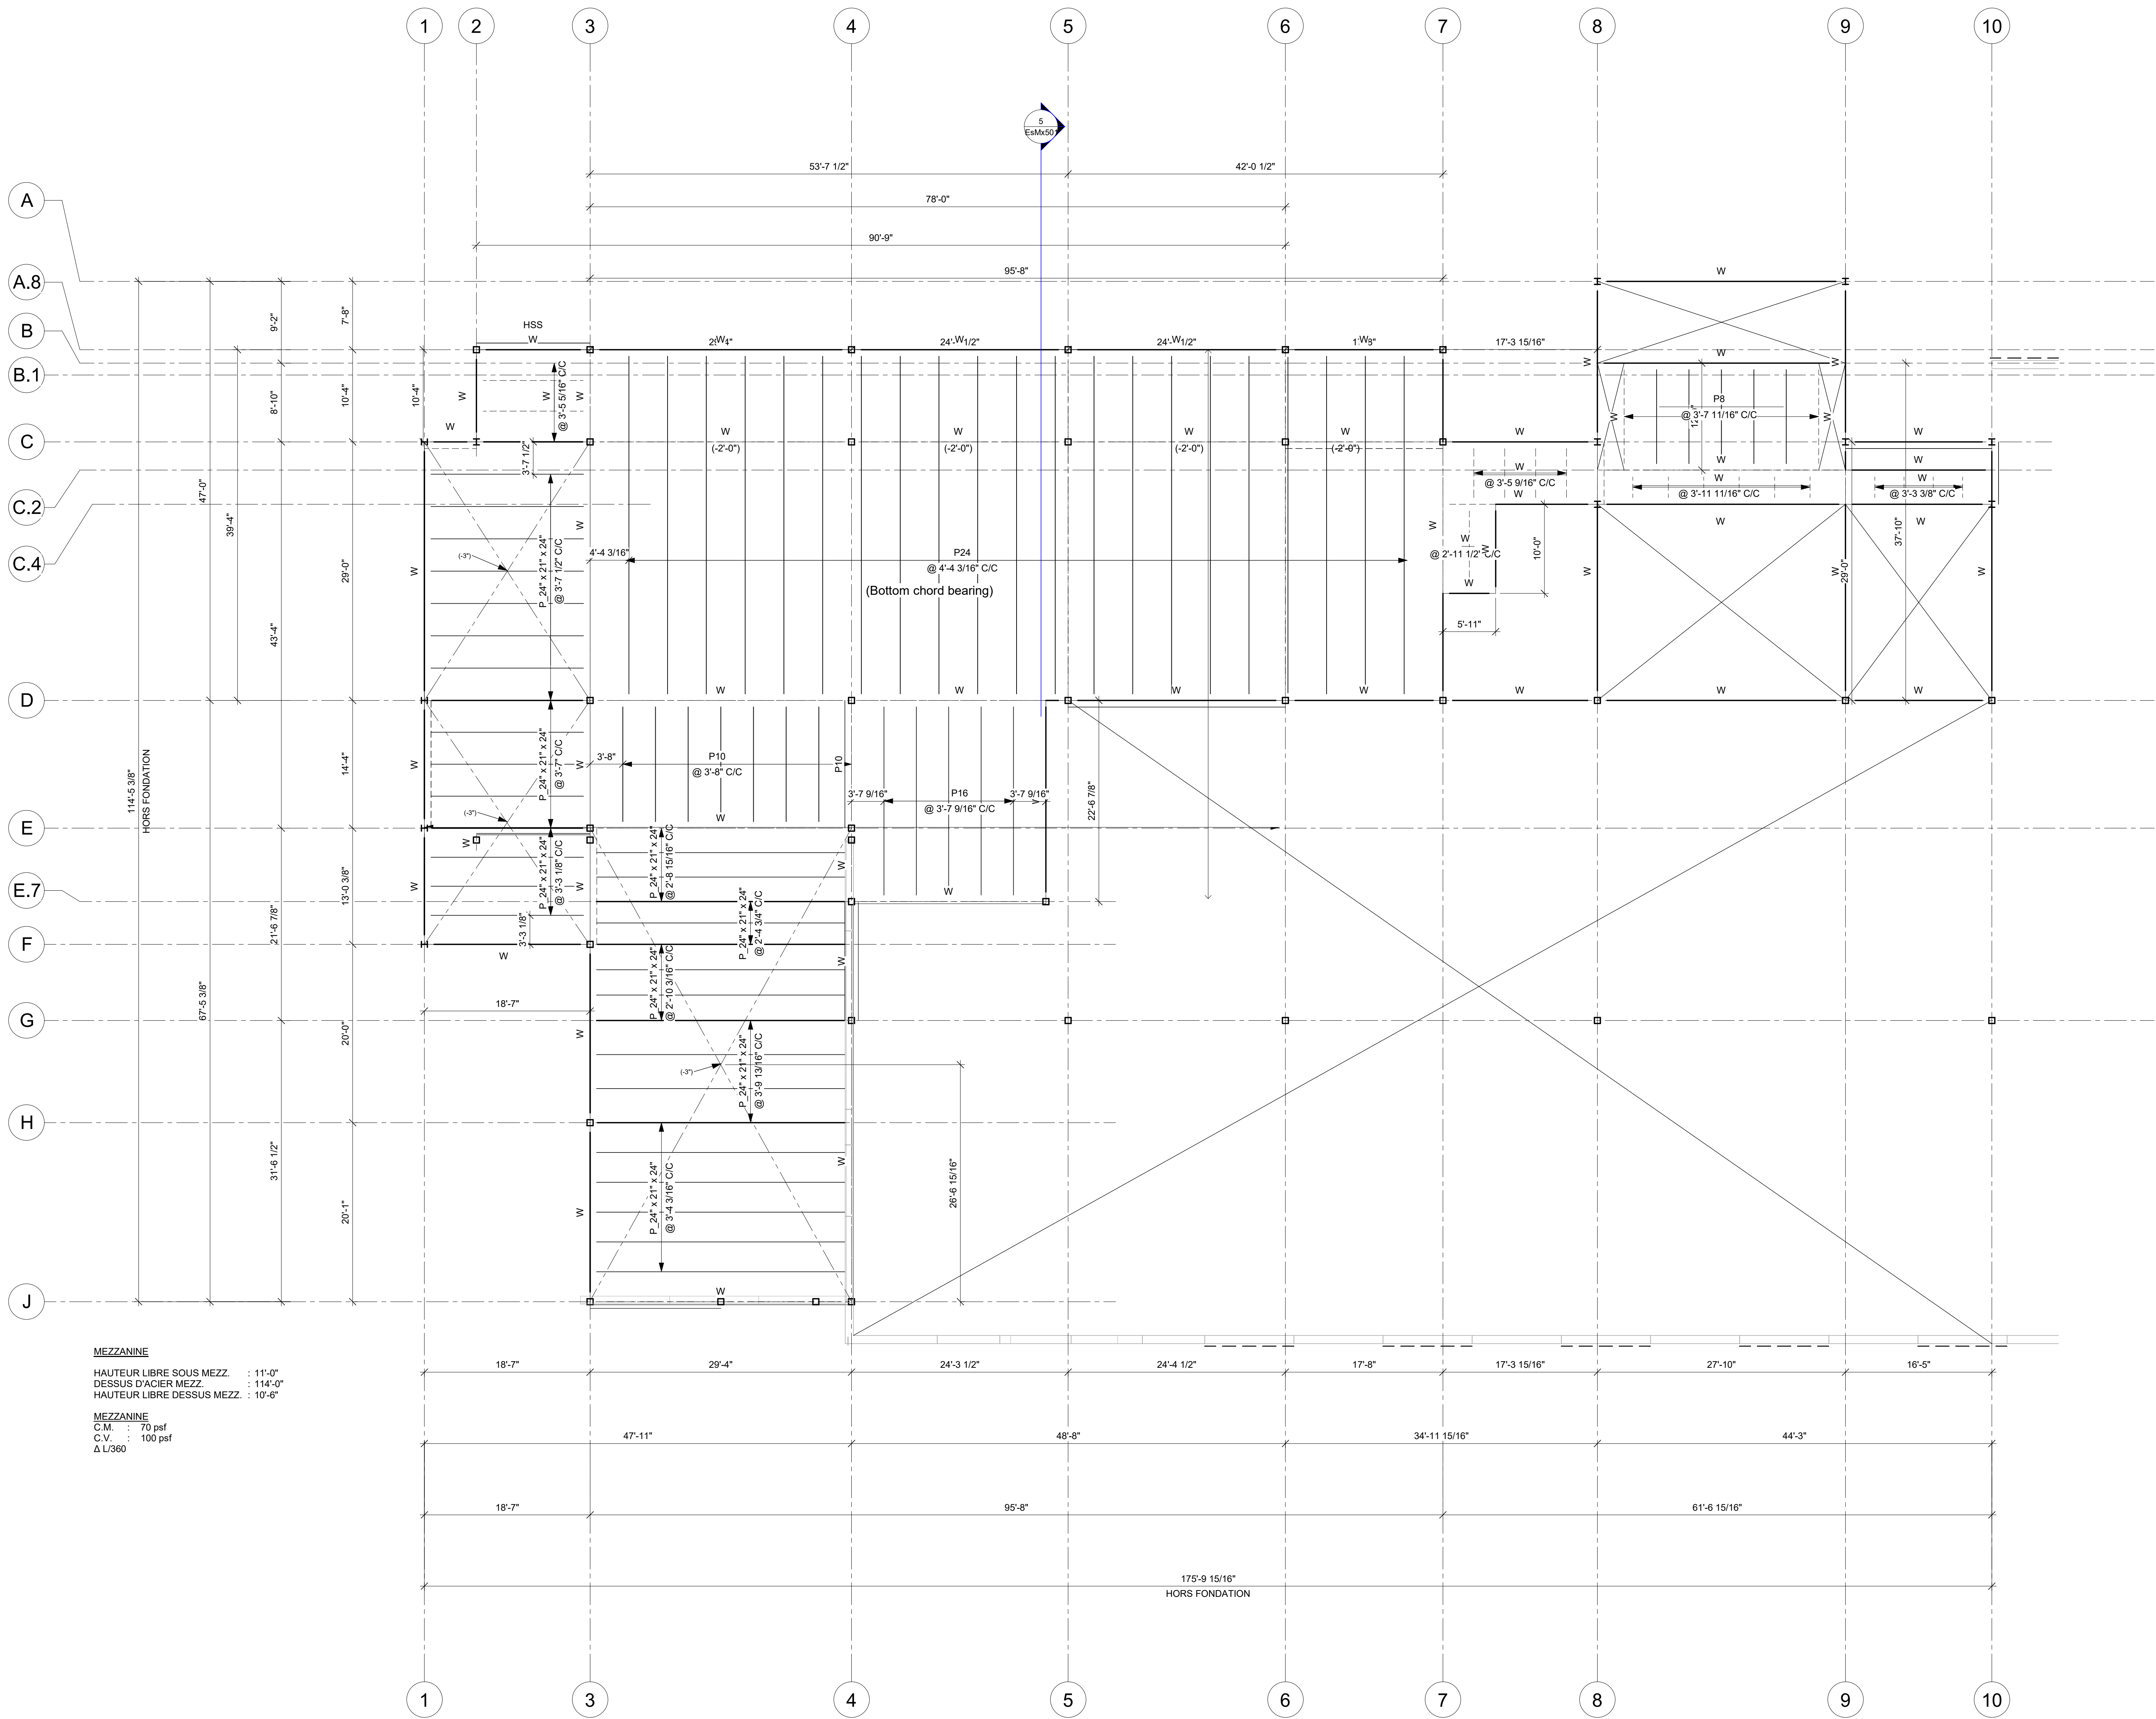

MEZZANINE
HAUTEUR LIBRE SOUS MEZZ. : 11'-0"
DESSUS D'ACIER MEZZ. : 114'-0"
HAUTEUR LIBRE DESSUS MEZZ. : 10'-8"
MEZZANINE
C.M. : 70 psf
C.V. : 100 psf
Δ U080

PLAN DE MEZZANINE
1/8" = 1'-0"

NOTE POUR LE CONTRACTEUR/ÉRECTEUR:
IL EST STRICTEMENT DÉFENDU DE MODIFIER, COPIER, REPRODUIRE OU
DE DISTRIBUER CES DESSINS OU QUELQUES REPRÉSENTATIONS DE
CES DESSINS, PAR TOUTES SOURCES DE MÉDIA INCLUANT
ÉLECTRONIQUEMENT, SANS L'APPROBATION ÉCRITE DE GROUPE
CANAM INC.

PRÉLIMINAIRE

NE DOIT PAS SERVIR À LA
CONSTRUCTION

REVISION	DATE	DESCRIPTION	DESS	VER
GERANT DE PROJET				
		.		
		.		
		.		
		.		
		.		
DESSIN:				
DESSINÉ PAR		CONÇU PAR	INGÉNIEUR DU PROJET	ECHELLE:
HSC				1/8" = 1'-0"
VÉRIFIÉ PAR		INGÉNIEURS CONSEILS / ARCHITECTES		DATE (mm/aa/aaaa):
				02/03/2026
CLIENT: Les constructions Binet Inc.				

CANAM
11505, 1re Avenue, bureau 500, Saint-Georges Beauce
Québec, Canada, G5Y 7X5
Téléphone : (418) 228-8031
Sans frais : (877) 459-8049
www.canam.com

SCAUX PROFESSIONNEL

PROJET

Nouveau Bâtiment CMI Motors
St-Georges

TITRE


CROQUIS PRÉLIMINAIRE - PLAN DE
MEZZANINE

Initiales


NUMÉRO CONTRAT	NUMÉRO DESSIN	DIVISION	REVISION
P2026-043	EsMx201		




ACCUMULATION DE NEIGE

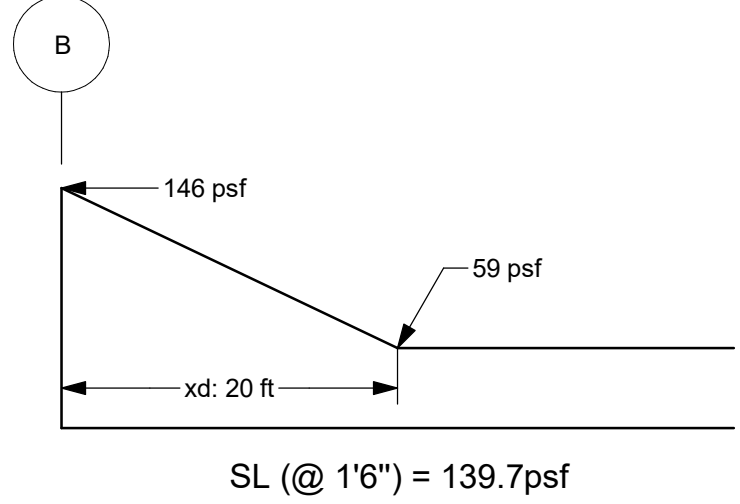

ACCUMULATION DE NEIGE

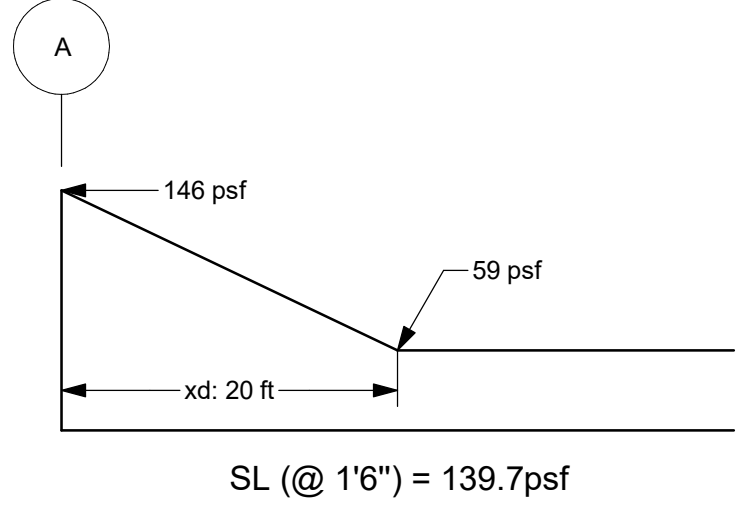

ACCUMULATION DE NEIGE

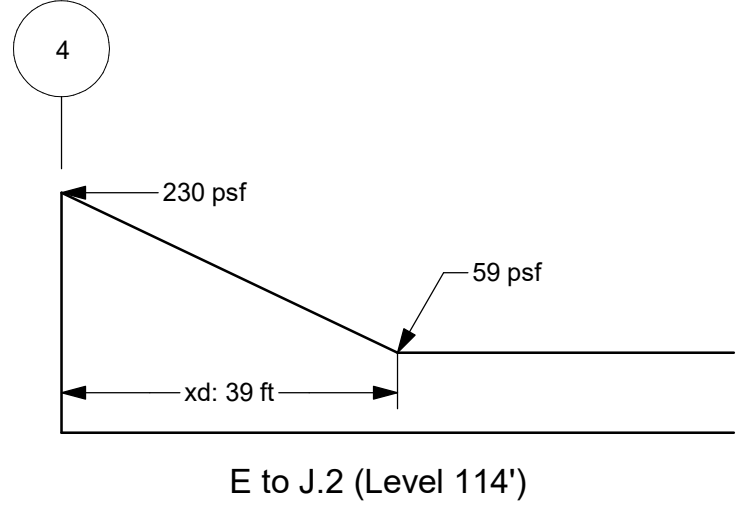

CHARGE DE PLUIE + CHARGE VIVE ADDITIONNEL


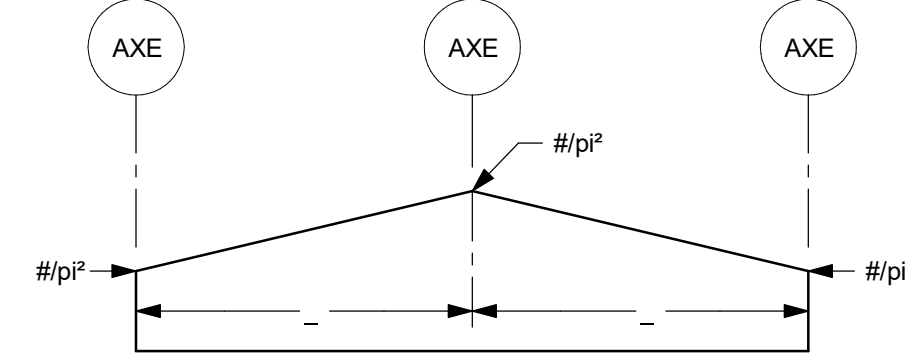


DIAGRAMME DE SOULEVEMENT BRUT (NON PONDERÉ)

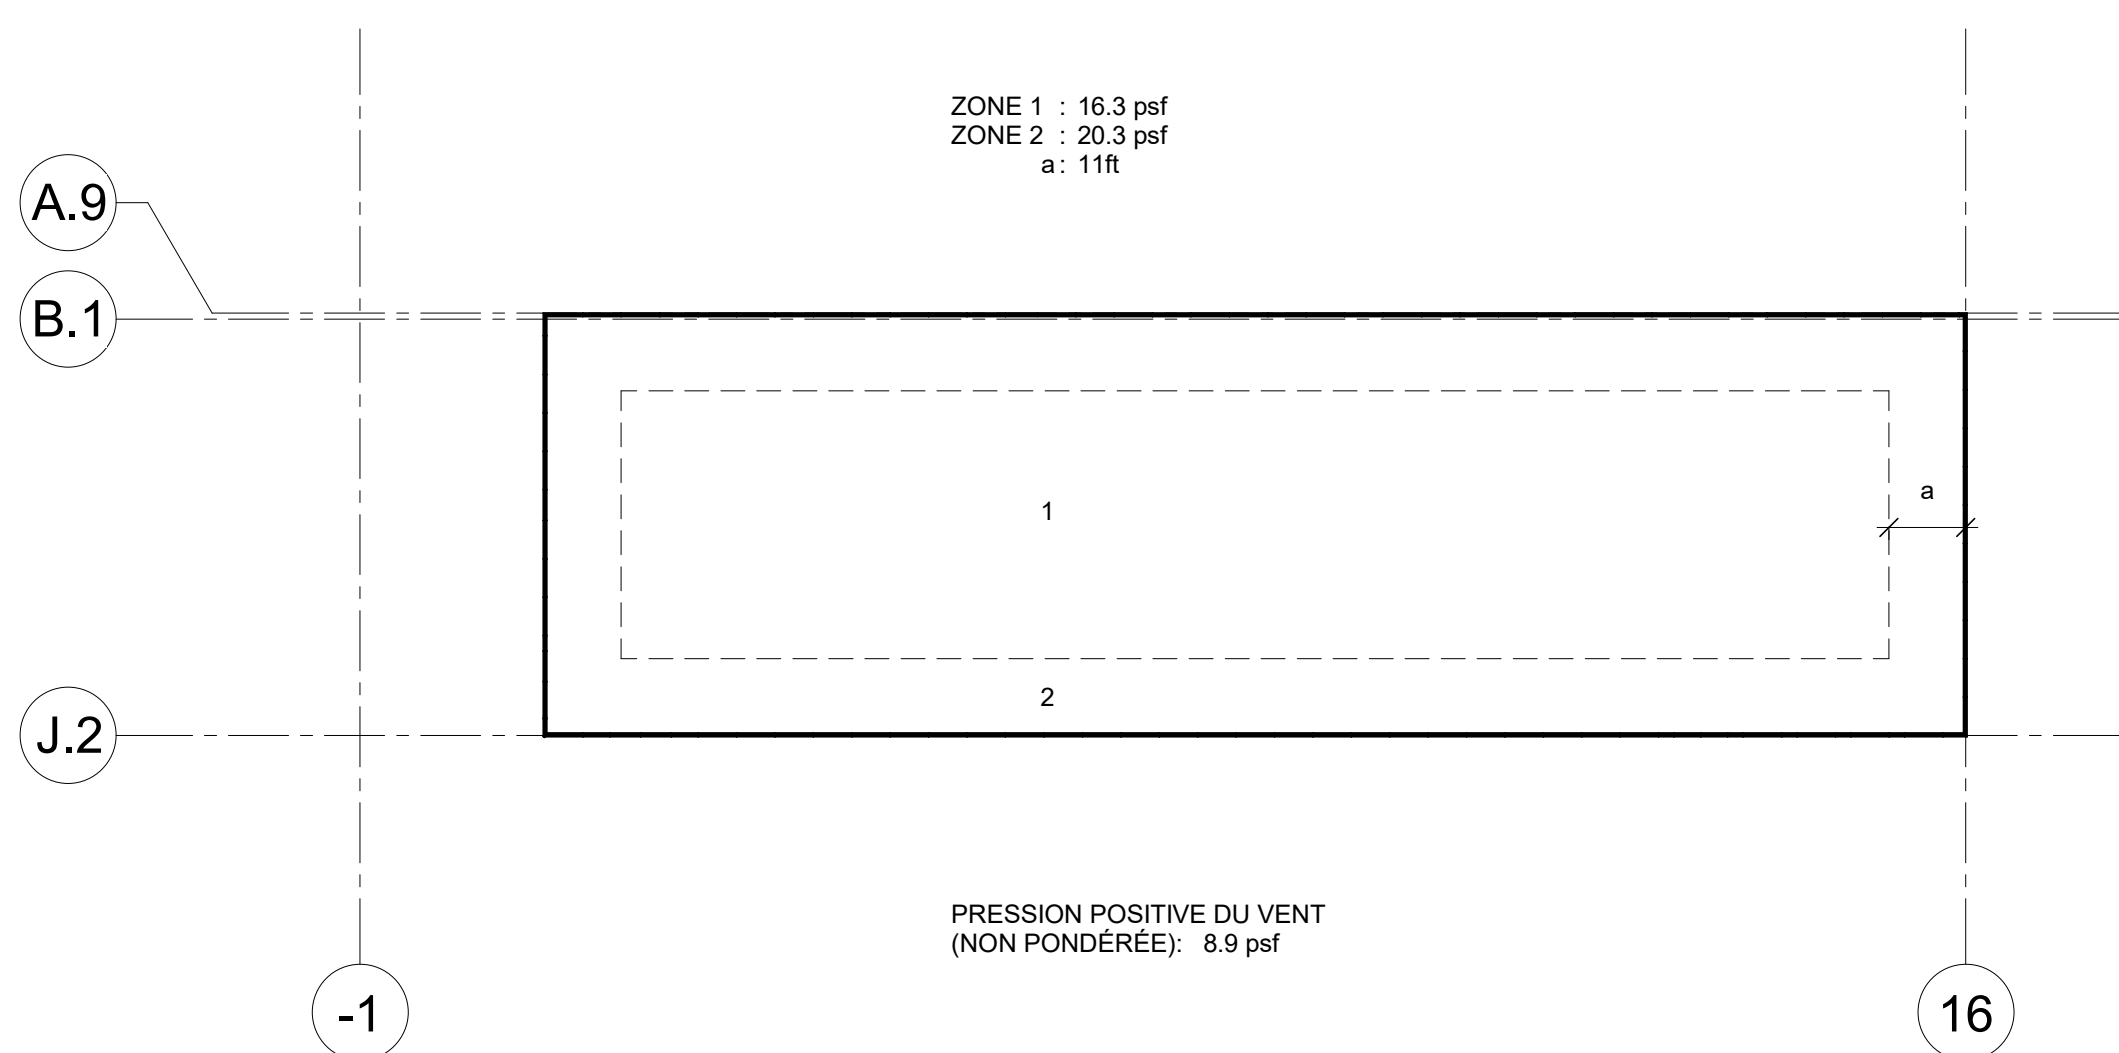

NOTE POUR LE CONTRACTEUR/ÉRECTEUR:
 IL EST STRICTEMENT DEFENDU DE MODIFIER, COPIER, REPRODUIRE OU DE DISTRIBUER CES DESSINS OU QUELQUES REPRÉSENTATIONS DE CES DESSINS, PAR TOUTES SOURCES DE MÉDIA INCLUANT ÉLECTRONIQUEMENT, SANS L'APPROBATION ÉCRITE DE GROUPE CANAM INC.

TOIT
 DESSUS DE PILASTRE DOP : 98'-0"
 DESSUS DE PLASTRE : 99'-0"
 DESSUS DE LA DALLE : 100'-0"
 DESSUS DE LA FONDATION : 102'-0"
 HAUTEUR LIBRE : 30'-4"
 DESSUS D'ACIER : 134'-8"
 DT & HL ENTREPÔT : 130'-0"
 HAUTEUR DE PARAPET : 1'-8"
 DESSUS DE PARAPET : 136'-2"

CHARGES
 C.M. : 16.0 psf
 C.M. : 5.0 psf
 S_u : 58.49 psf
 S_v : 12.53 psf
 C_b x C_w : 0.8
 C.V. au toit : 0.0 psf
 I_t : 1.0 psf
 Charge de neige au toit : 59.51 psf
 Vent q = 1/50 : 1.0 psf
 Vent q = 1/50 : 7.94 psf


Seisme (Sol de classe D assumé)
 I_e : 1.0
 S_u (0.2) : 0.482
 S_u (0.5) : 0.478
 S_u (1.0) : 0.294
 S_u (2.0) : 0.143
 S_u (5.0) : 0.0425
 S_u (10.0) : 0.0128
 PGA : 0.267
 PGV : 0.326

CHARGES
 • Charge morte au toit (excluant charge collatérale) : I_{ts}/psf
 • Charge collatérale : I_{ts}/psf (incluant éclairage et/ou mécanique et gicleurs plus petits que 4" de diamètre)
 • Charge de neige au toit : I_{ts}/psf
 • Charge vive au toit : I_{ts}/psf
 • Charge de vent q 1/50 : I_{ts}/psf
 • Charge de neige au sol : S_u = I_{ts}/psf
 normal
 • Catégorie de risque : normal
 • Coefficient de surcharge de neige : C_b = 0.8
 • Coefficient de surcharge de neige : C_w = 1.0

• Code Applicable : Code National du Bâtiment du Canada
 Code du bâtiment du Québec, dernières éditions adoptées
 Code de Pratique Standard ICCA.

• Type de sol assumé : classe D

NOTE
 1. Si toutefois la catégorie d'emplacement devient E ou F selon le rapport géotechnique, le concept structural préliminaire (localisation et géométrie des contreventements, etc.) devra être validé et coordonné par l'ingénieur de Canam.

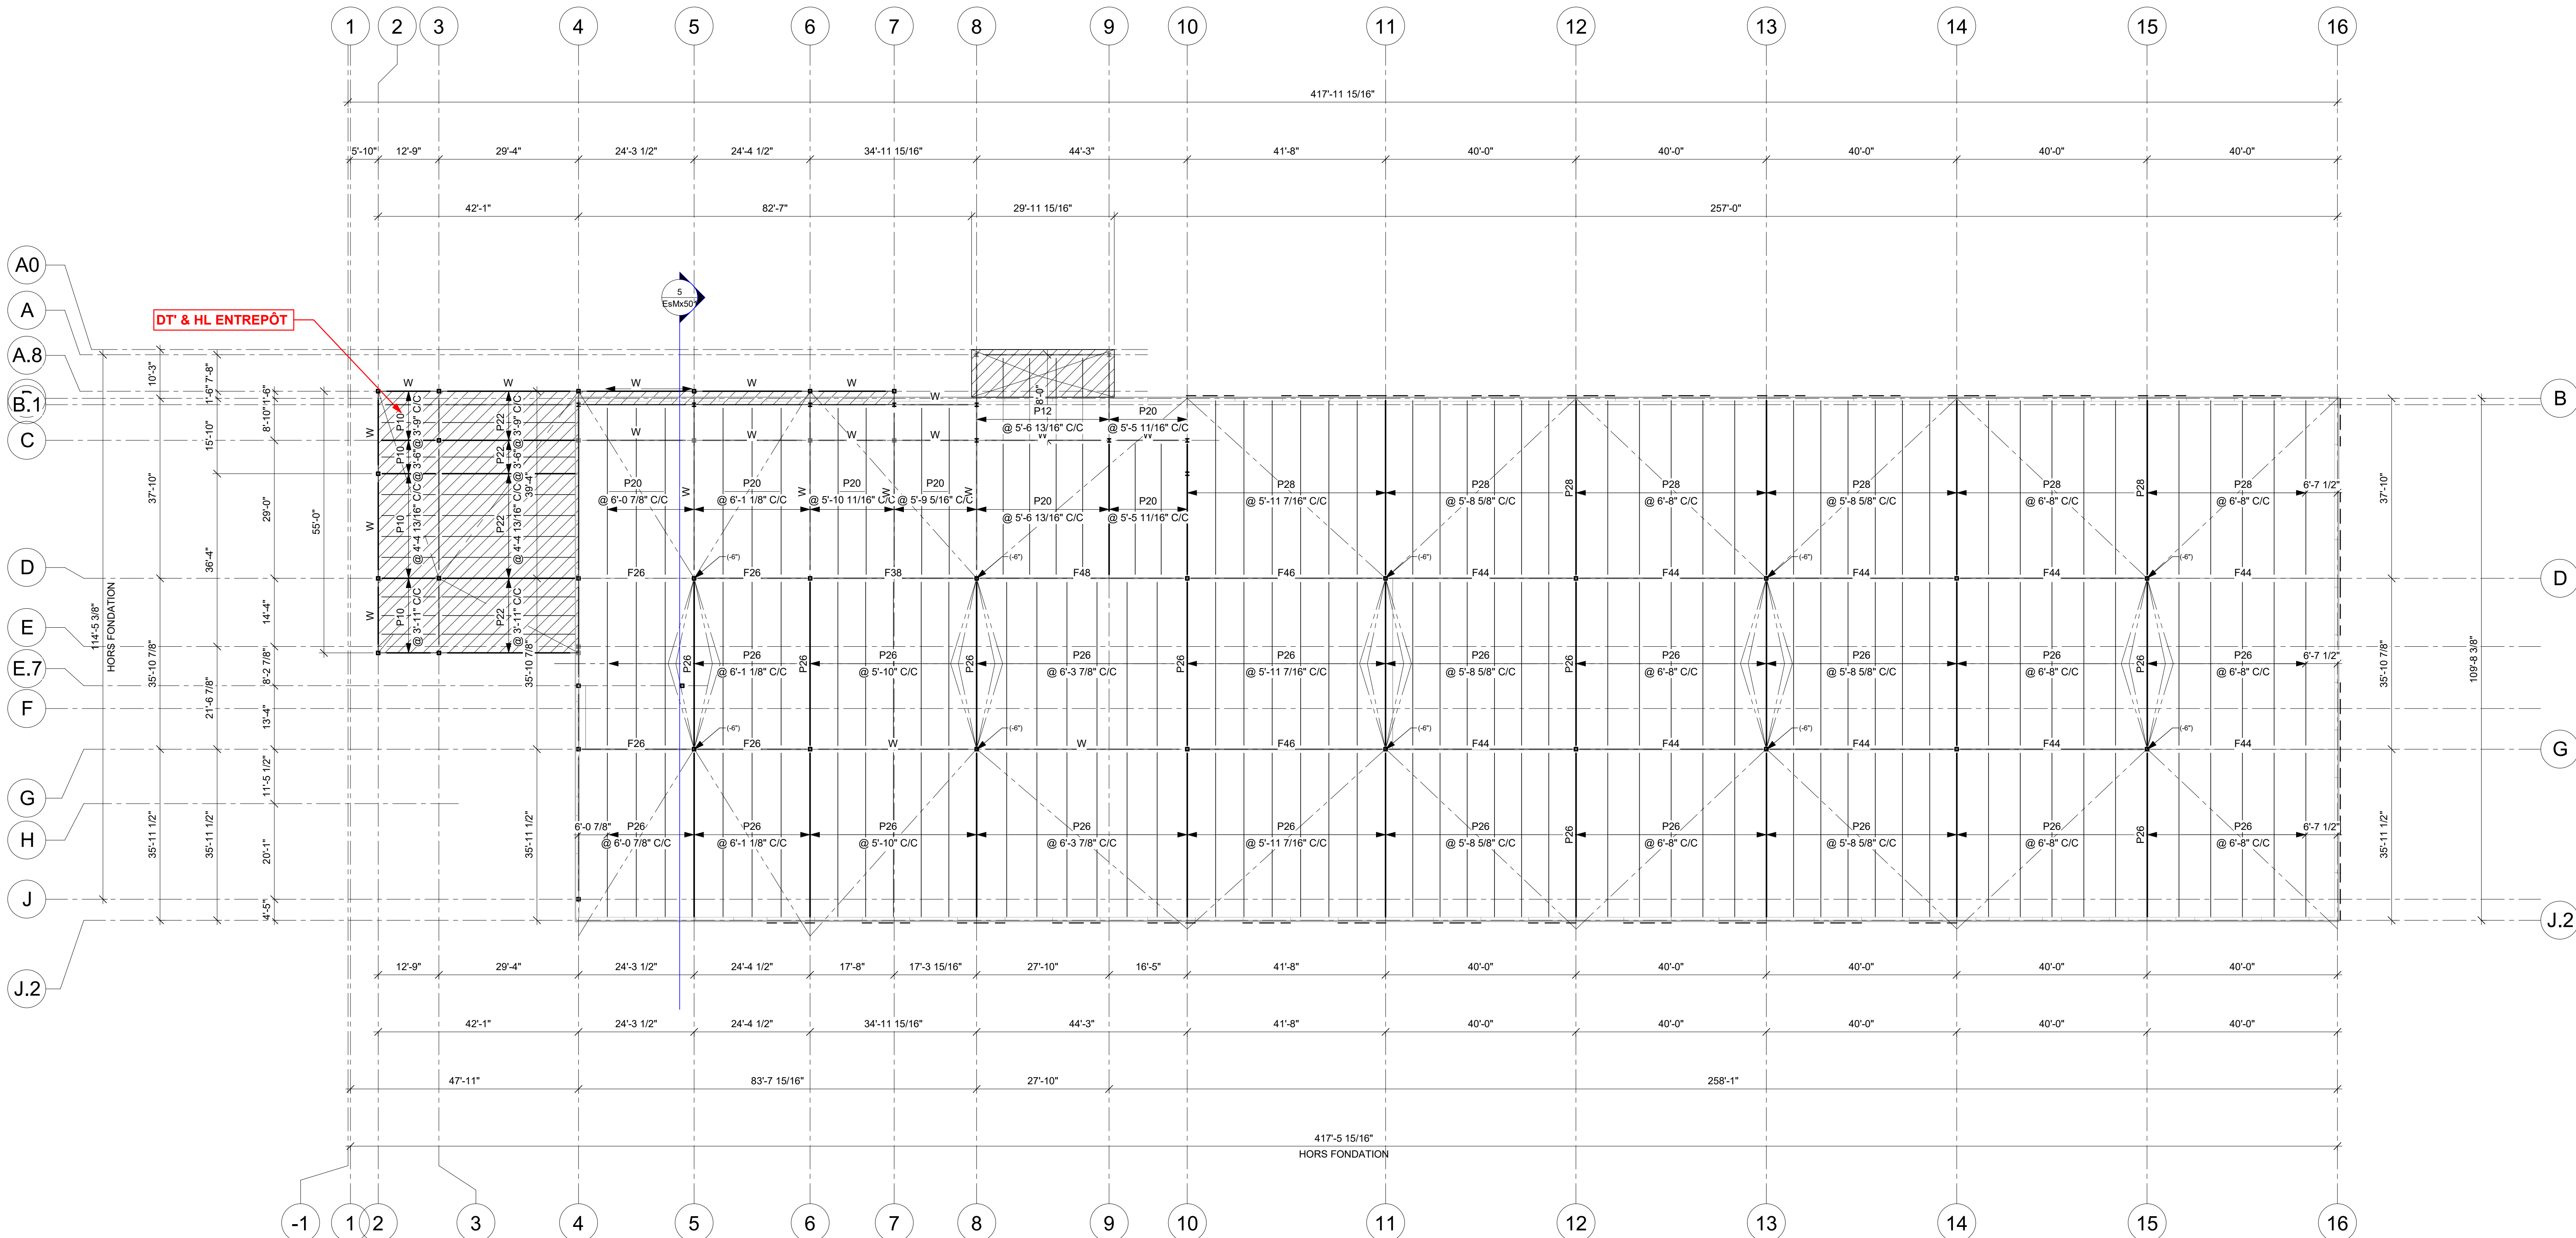

PRÉLIMINAIRE

NE DOIT PAS SERVIR À LA CONSTRUCTION



Nouveau Bâtiment CMI Motors
 St-Georges


CROQUIS PRÉLIMINAIRE - PLAN DE TOIT

NUMÉRO CONTRAT	NUMÉRO DESSIN	DIVISION	REVISION
P2026-043	EsMx401		


PLAN DE TOIT
 1/16" = 1'-0"
 Pontage métallique au toit: 1.5B, gage 22, double span
 1.5B, gage 20 & 22 (Roof Level 130')
 Angle de périmètre: +/- 961'-0"

CÉDULE DES FENÊTRES				
Identifiant	Qté.	Description	Dimensions ext. cadre largeur X hauteur	Couleur du cadre
F1	2	Fenêtre en aluminium fixe avec bris thermique et verre scellé + Low-E argon clair	9'-0" x 3'-0"	Cadre d'Aluminium (Blanc ext. et int.)
F2	2	Fenêtre en aluminium fixe avec bris thermique et verre scellé + Low-E argon clair	5'-0" x 3'-0"	Cadre d'Aluminium (Blanc ext. et int.)


CÉDULE DES PORTES				
Identifiant	Qté.	Porte 18 ja.	Dimensions	Remarques
P1	4		5'-0" x 7'-0"	
P2	2		12'-0" x 16'-0"	OUVERTURE POUR PORTE MONTANTE
P3	4		6'-0" x 9'-0"	OUVERTURE POUR PORTE MONTANTE+COUSSIN D'TANCHEÏTE

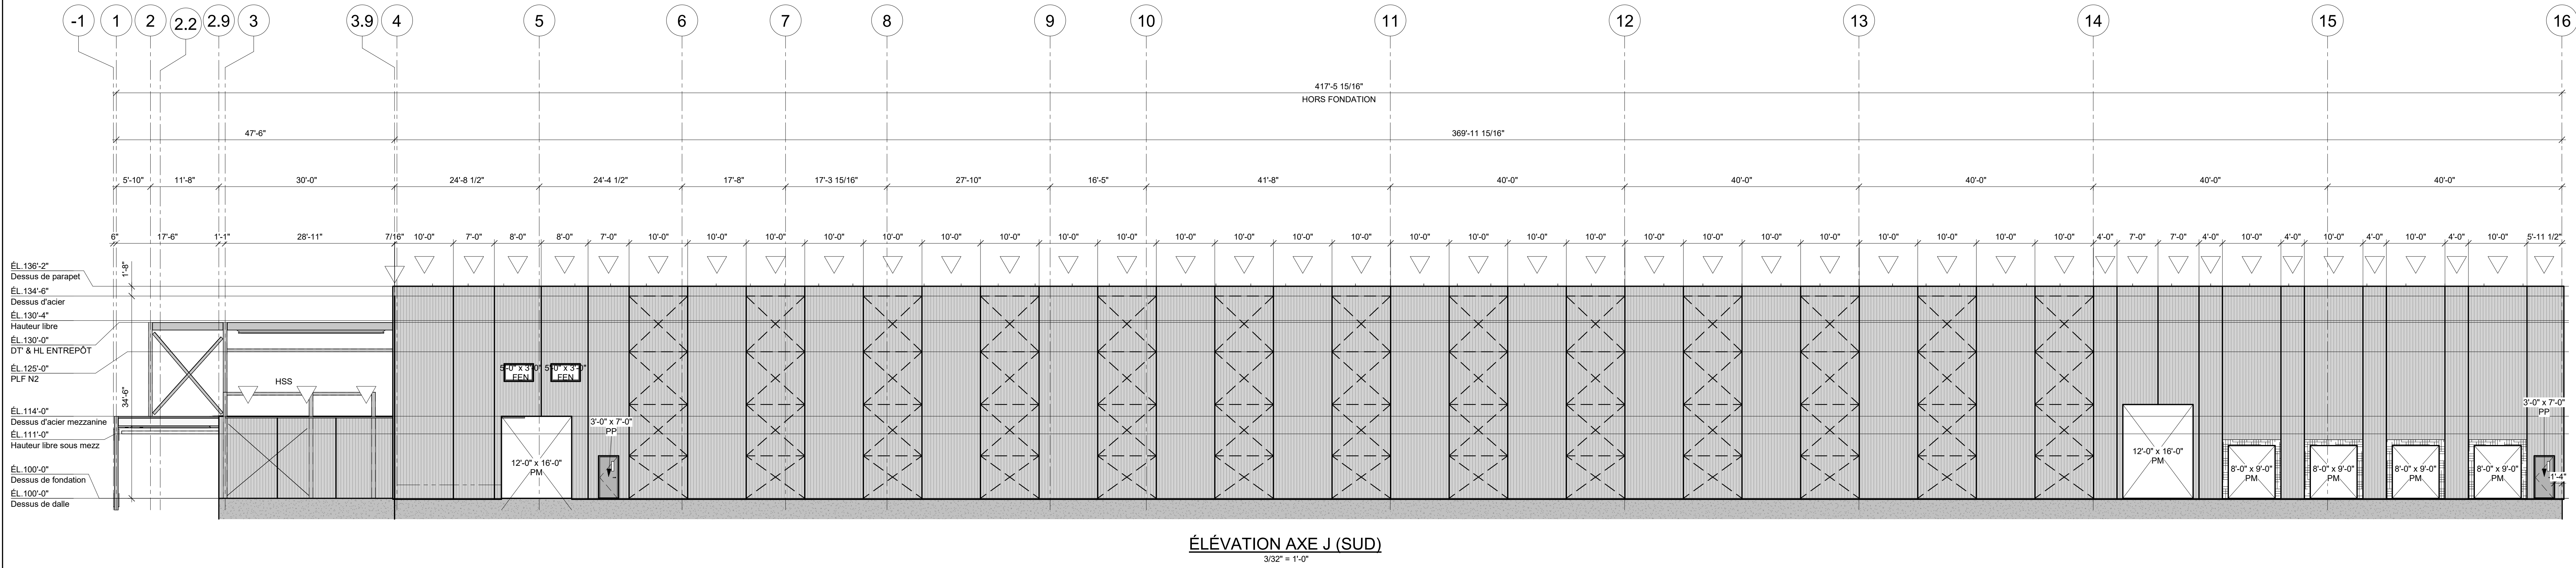


ÉLEVATION AXE J (SUD)
3/32" = 1'-0"

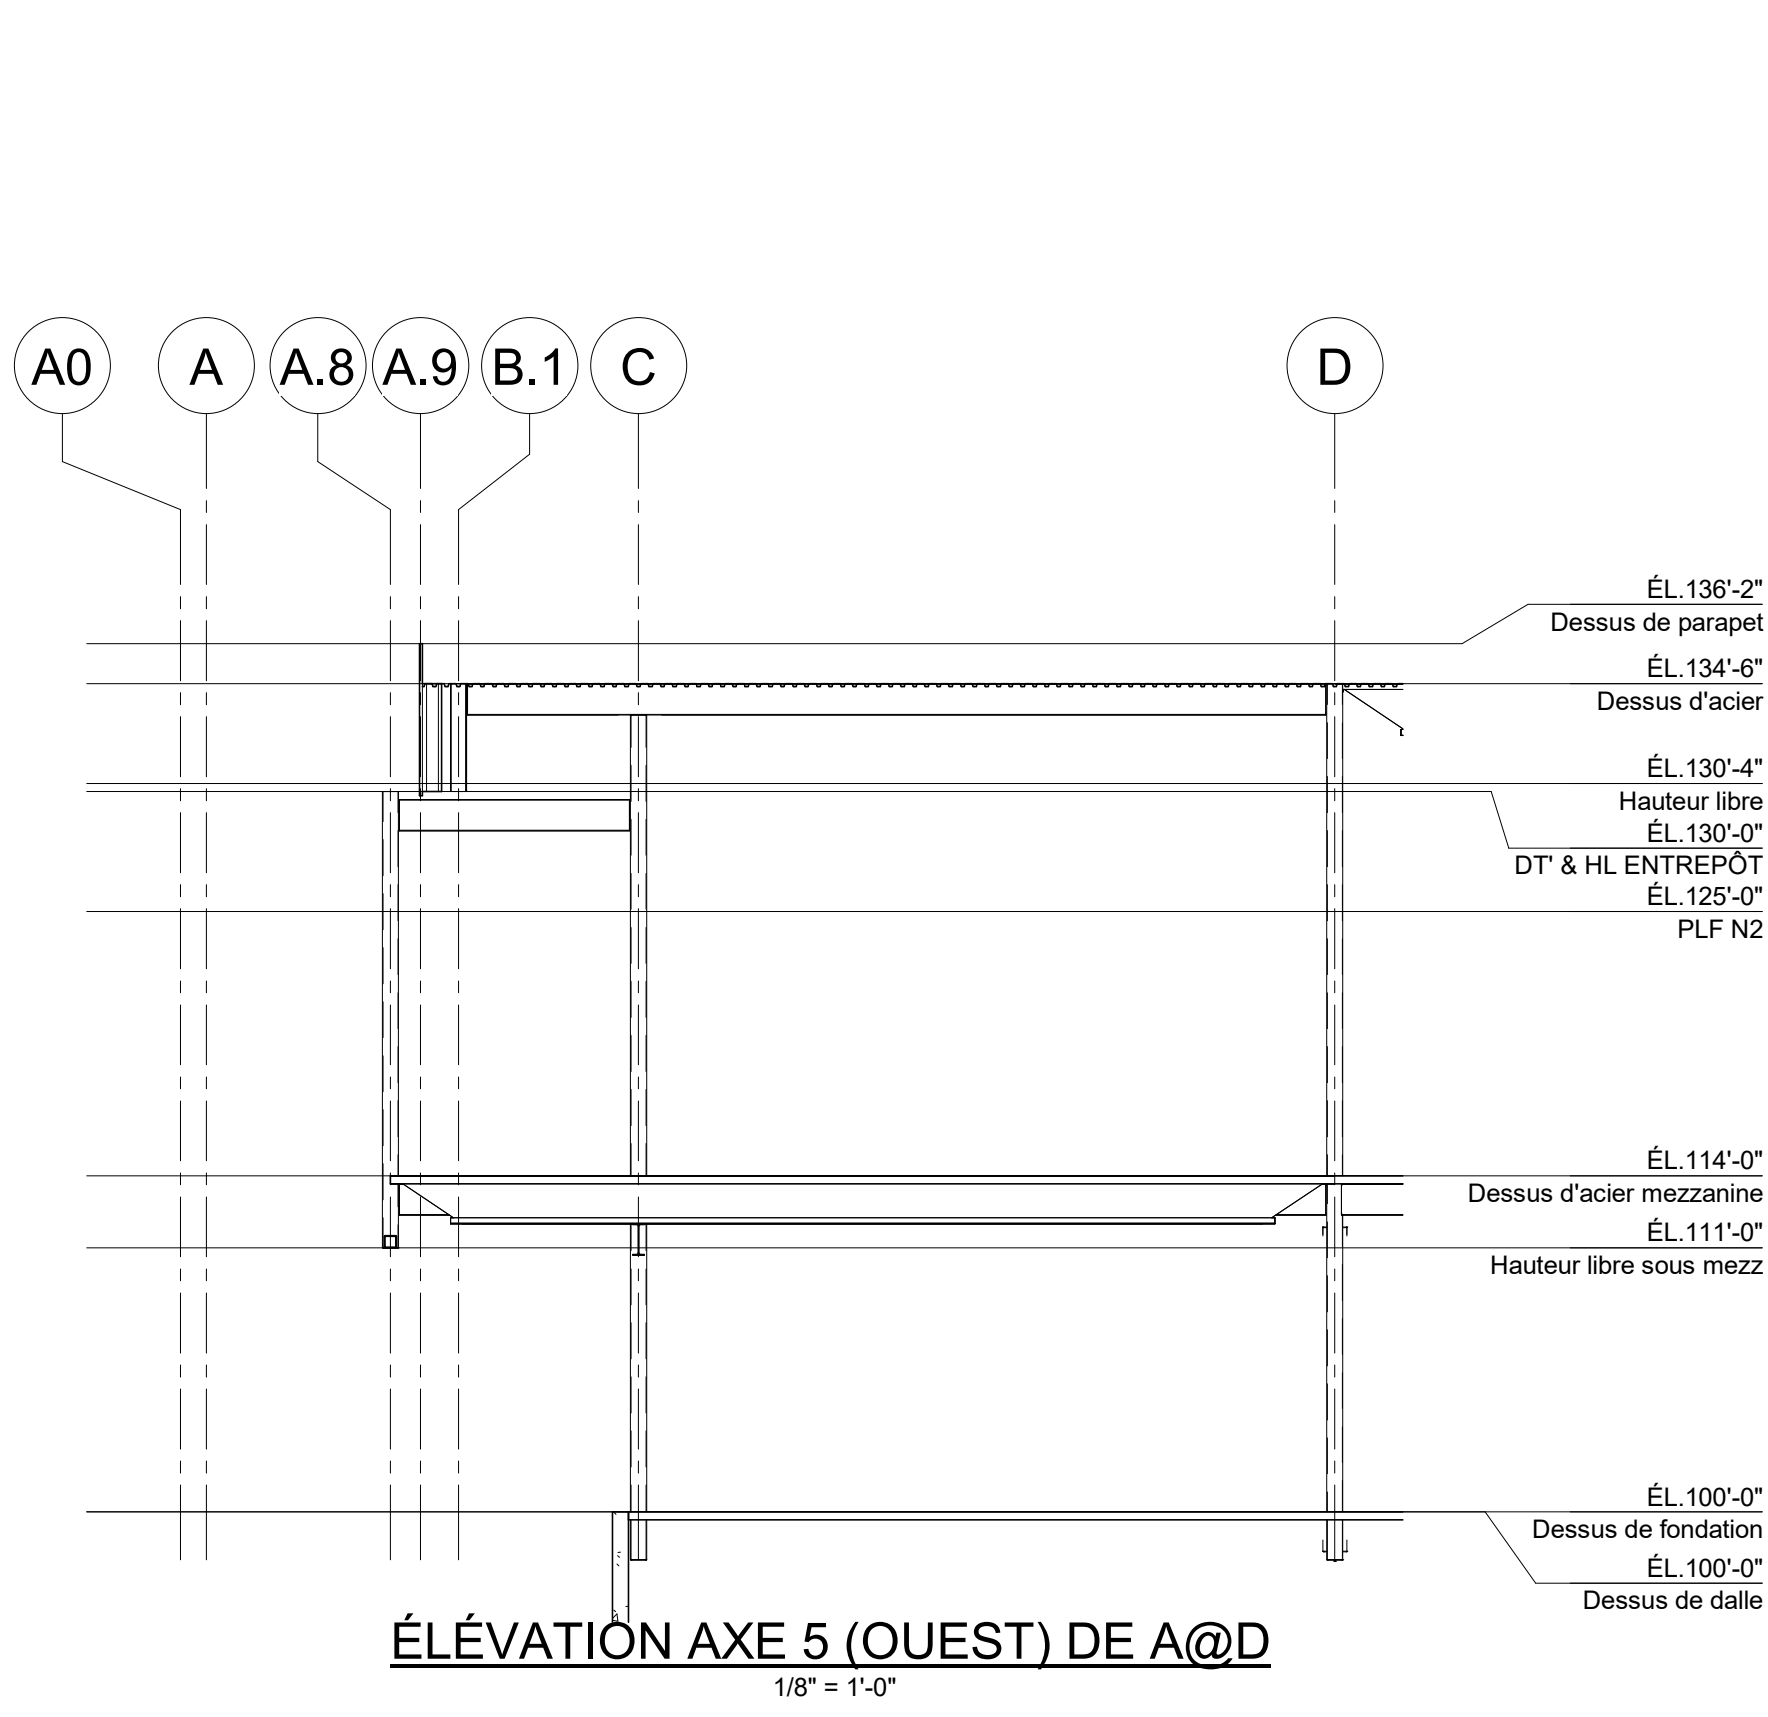


ÉLEVATION AXE 5 (OUEST) DE A@D
1/8" = 1'-0"

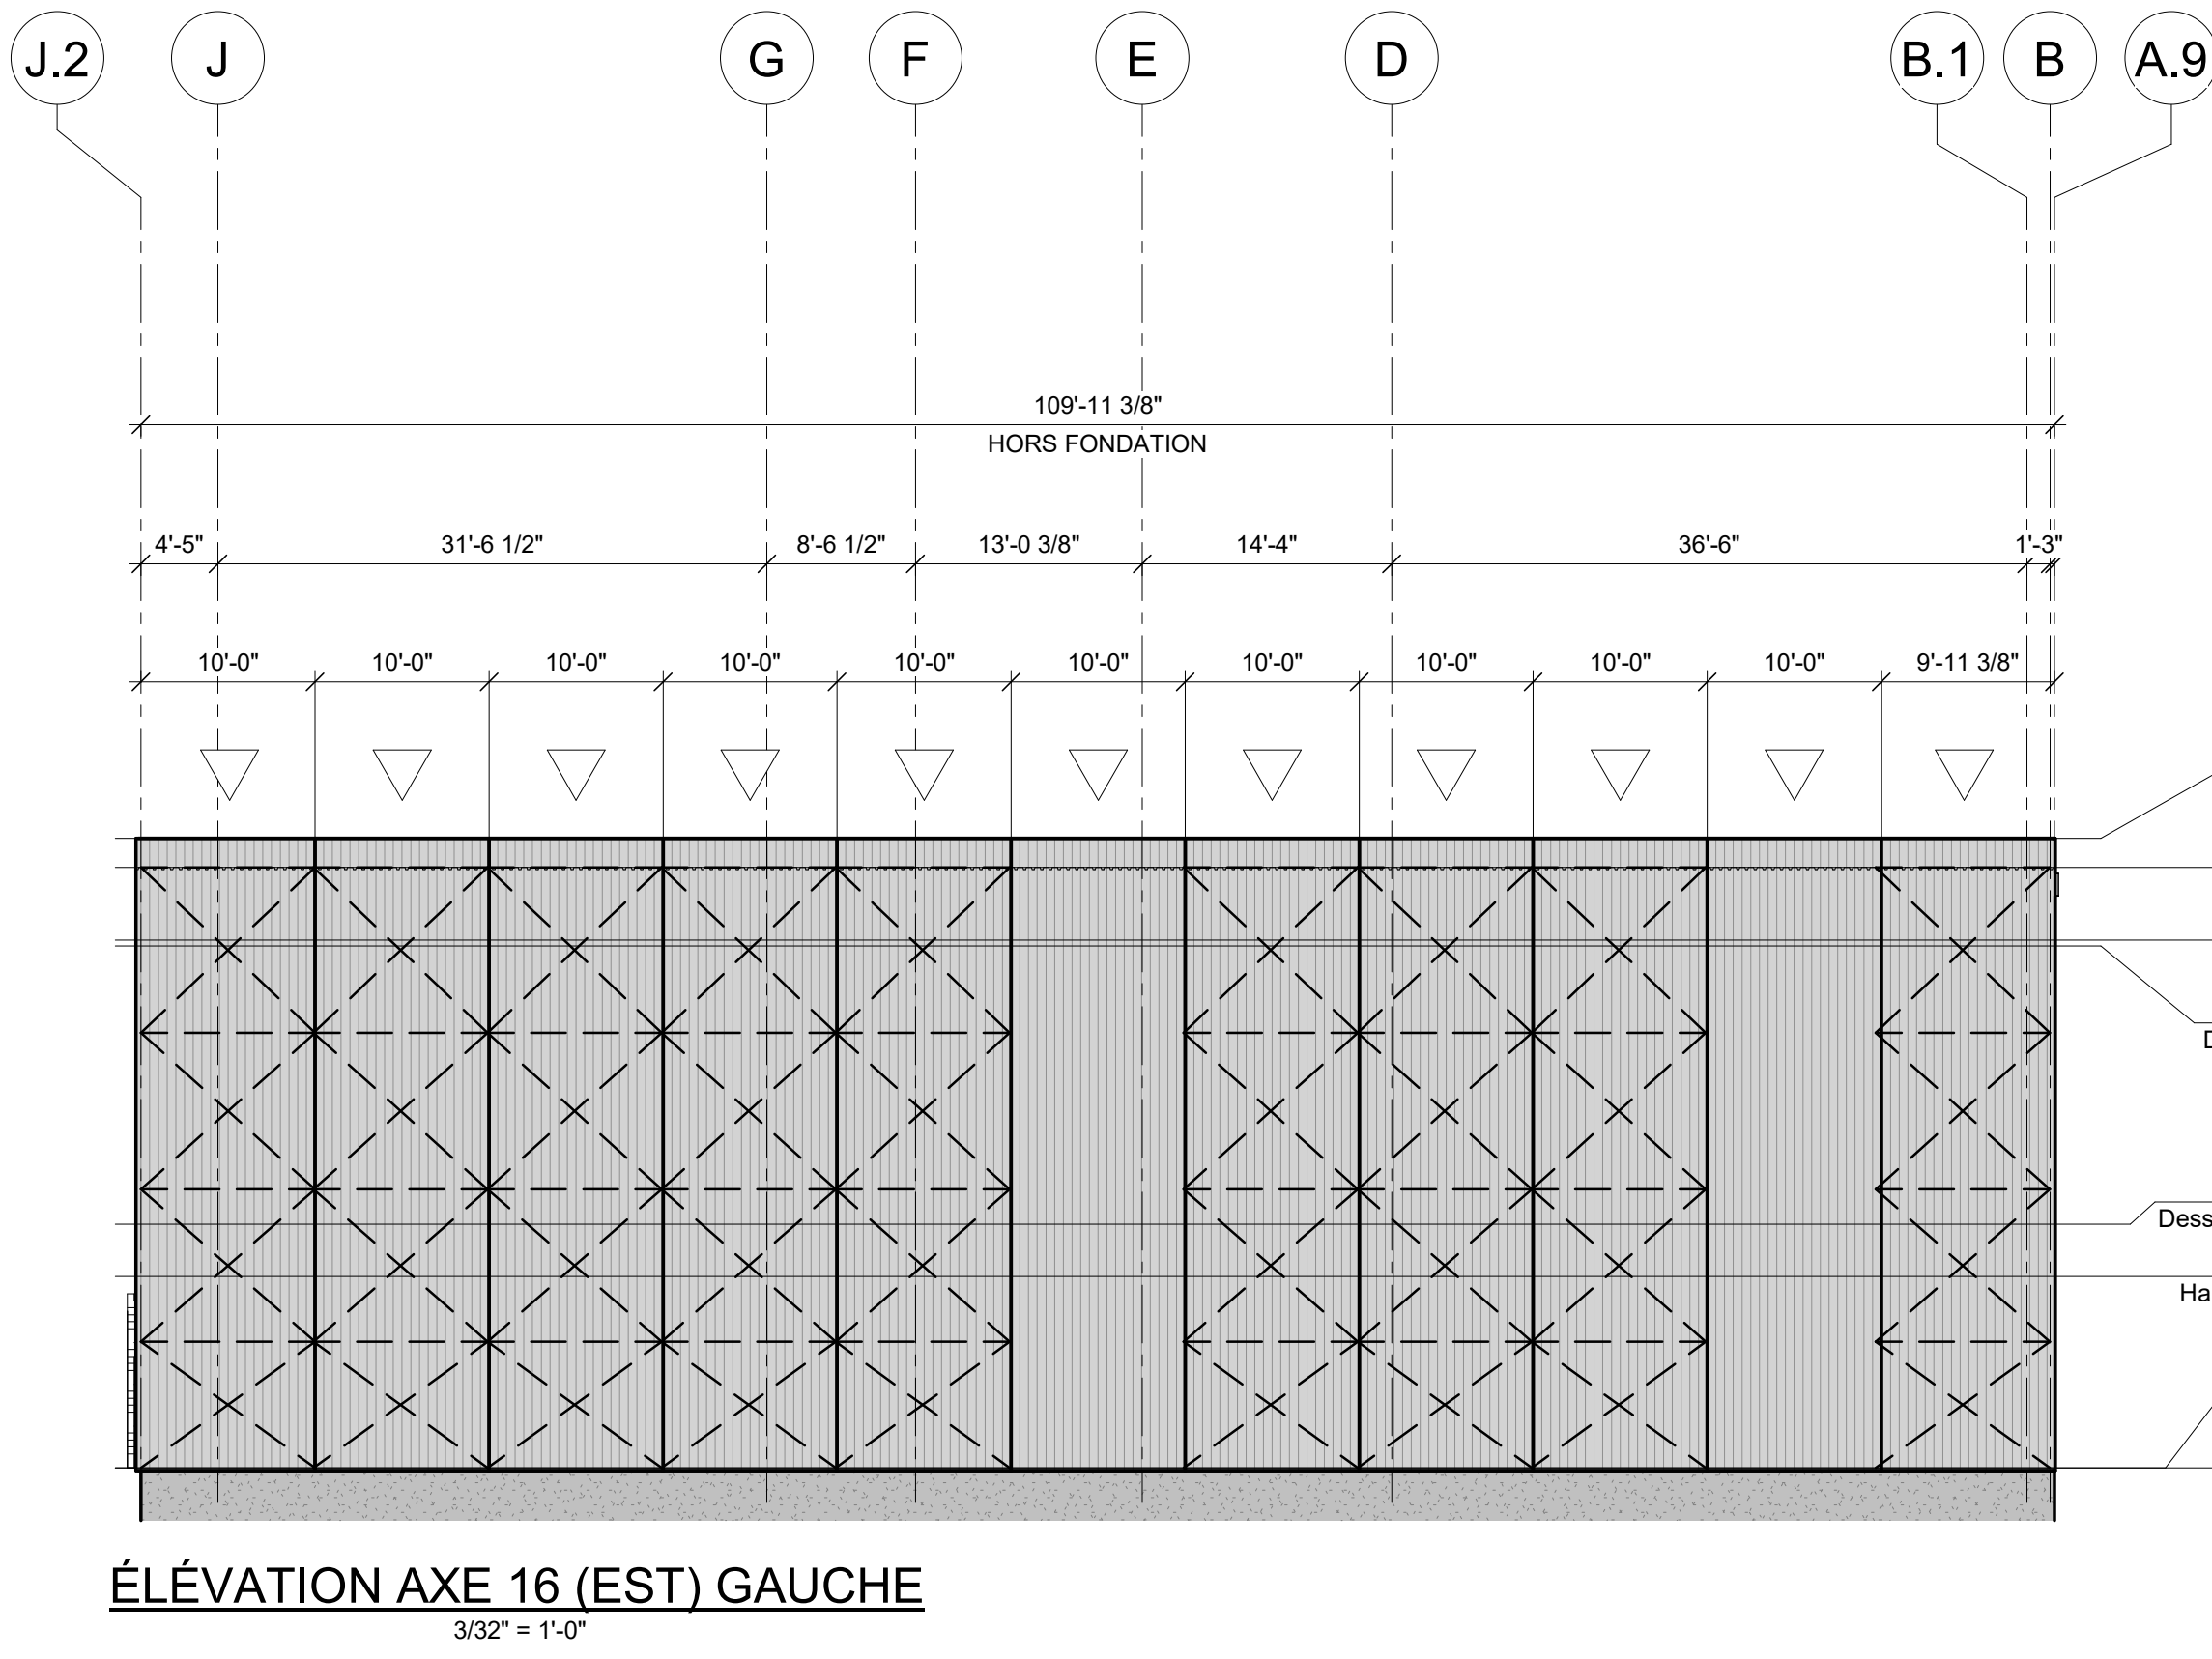

ÉLEVATION AXE 16 (EST) GAUCHE
3/32" = 1'-0"

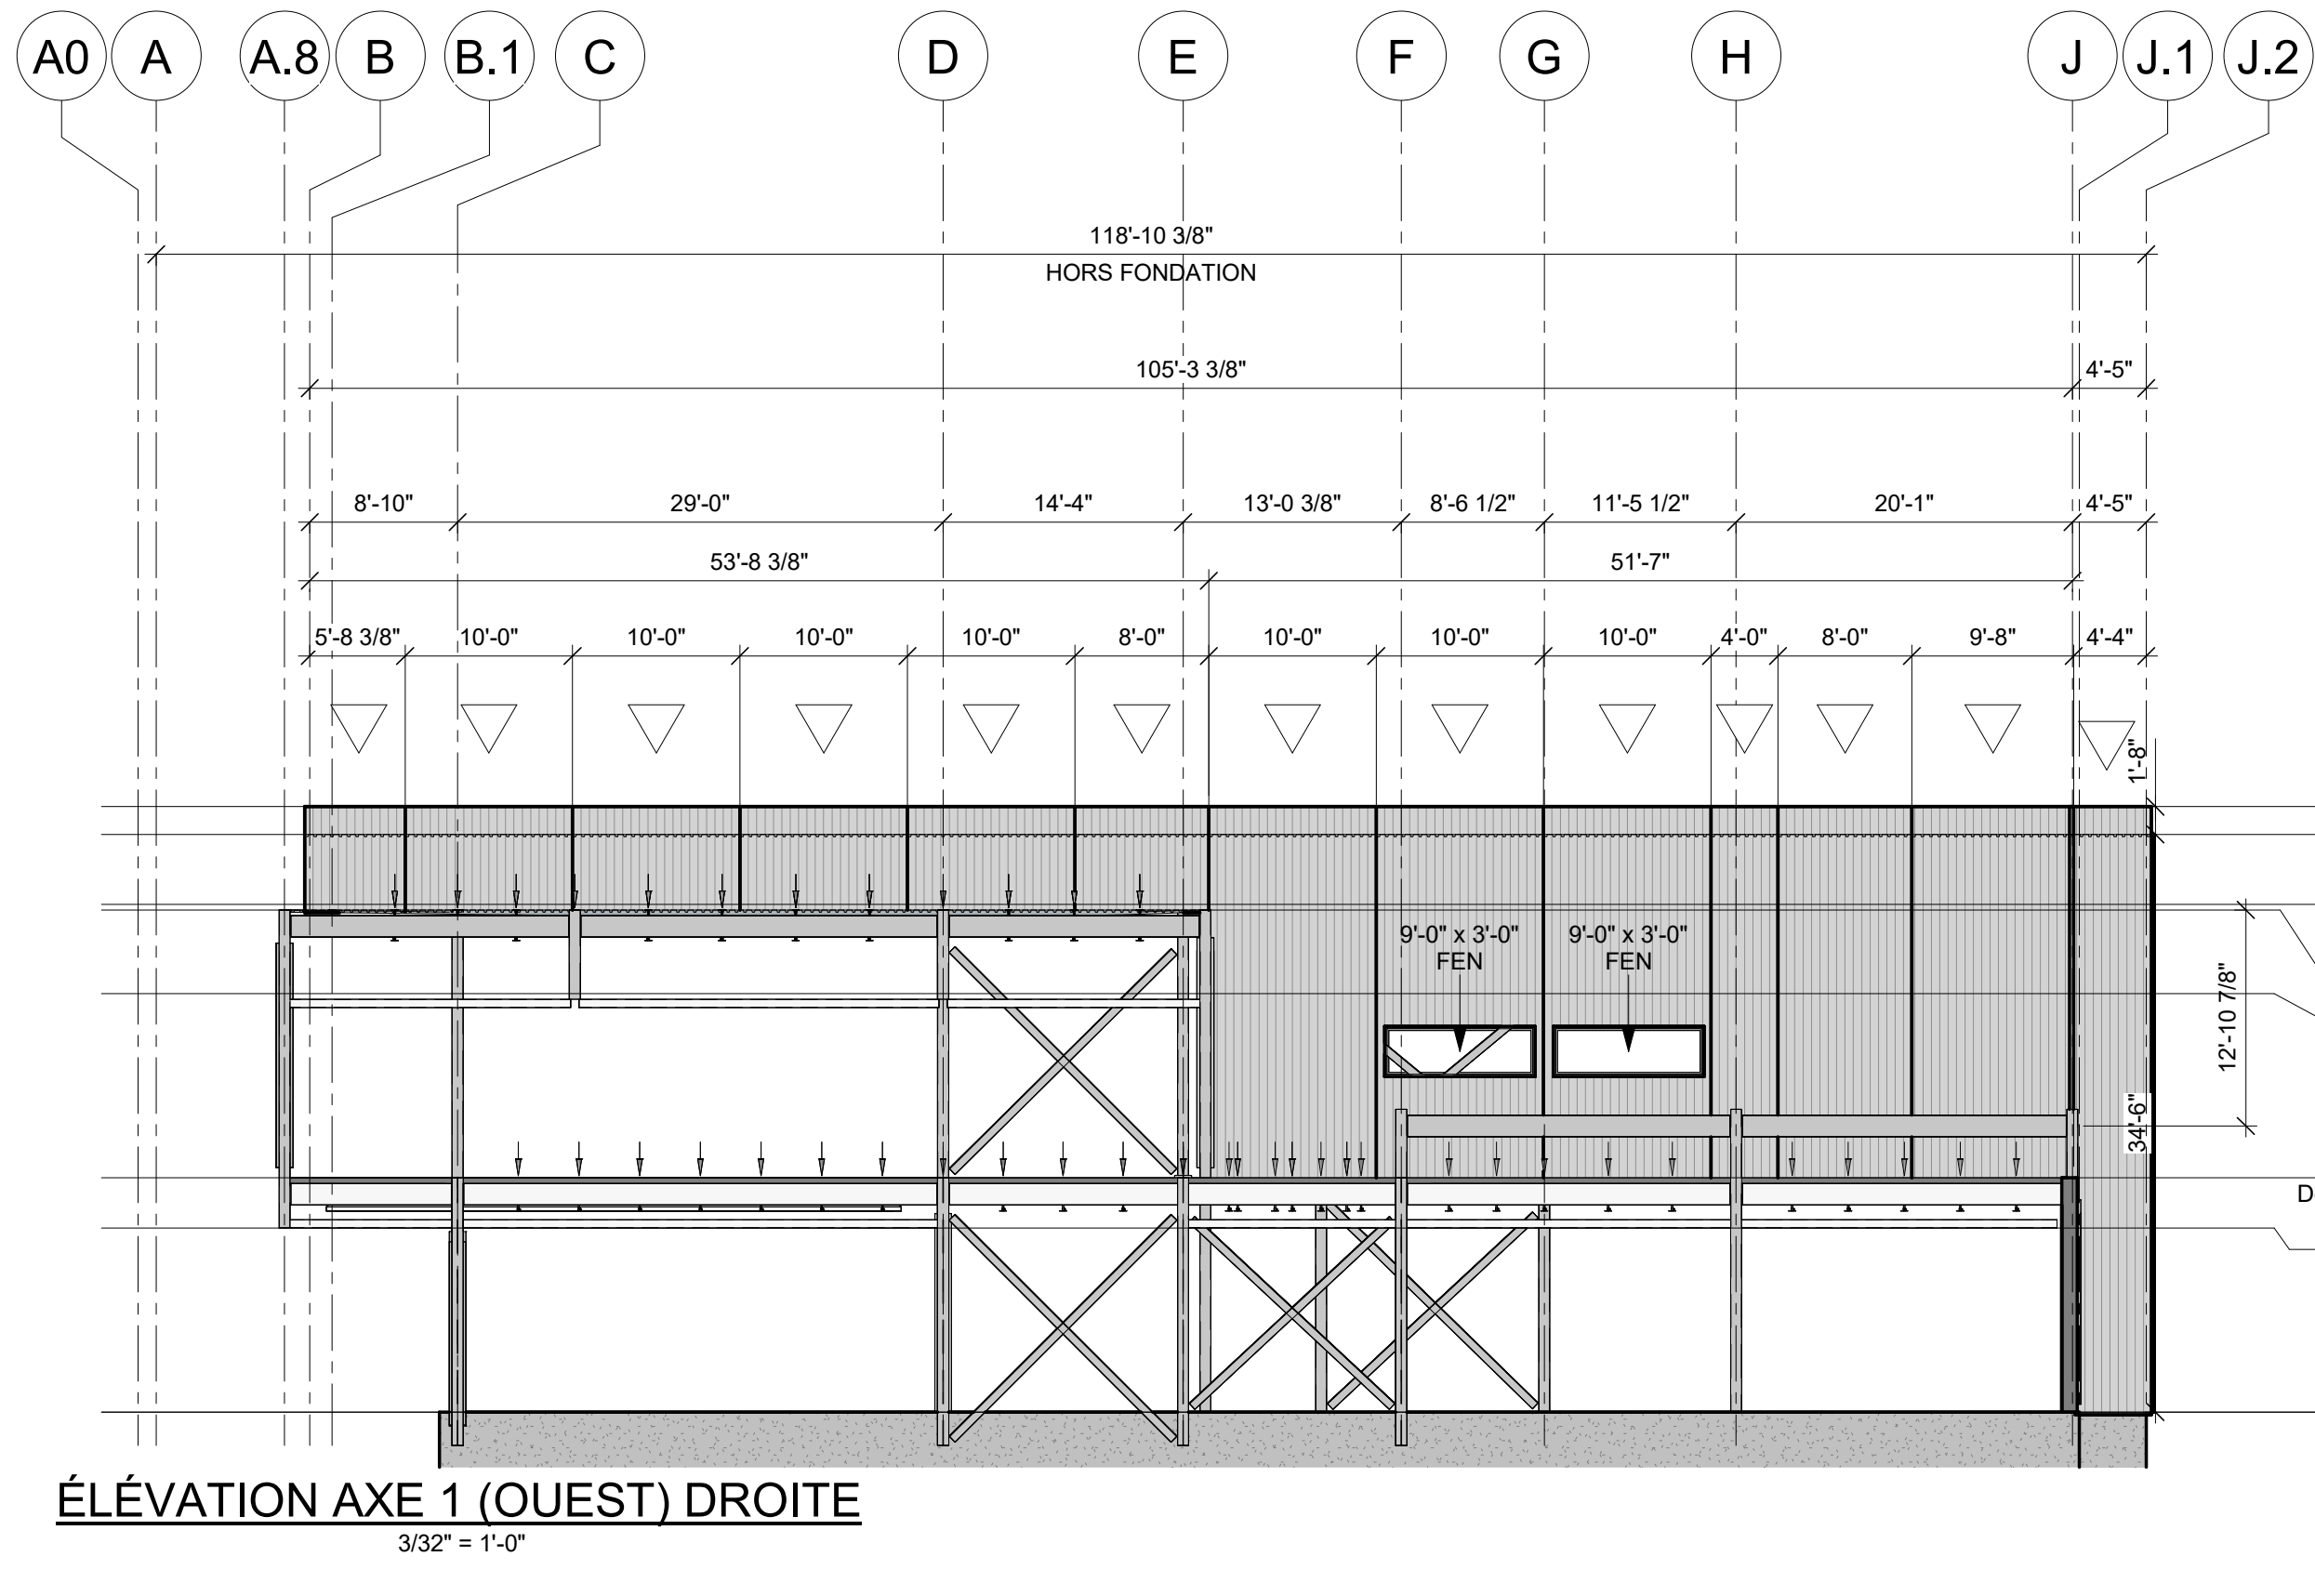

ÉLEVATION AXE 1 (OUEST) DROITE
3/32" = 1'-0"

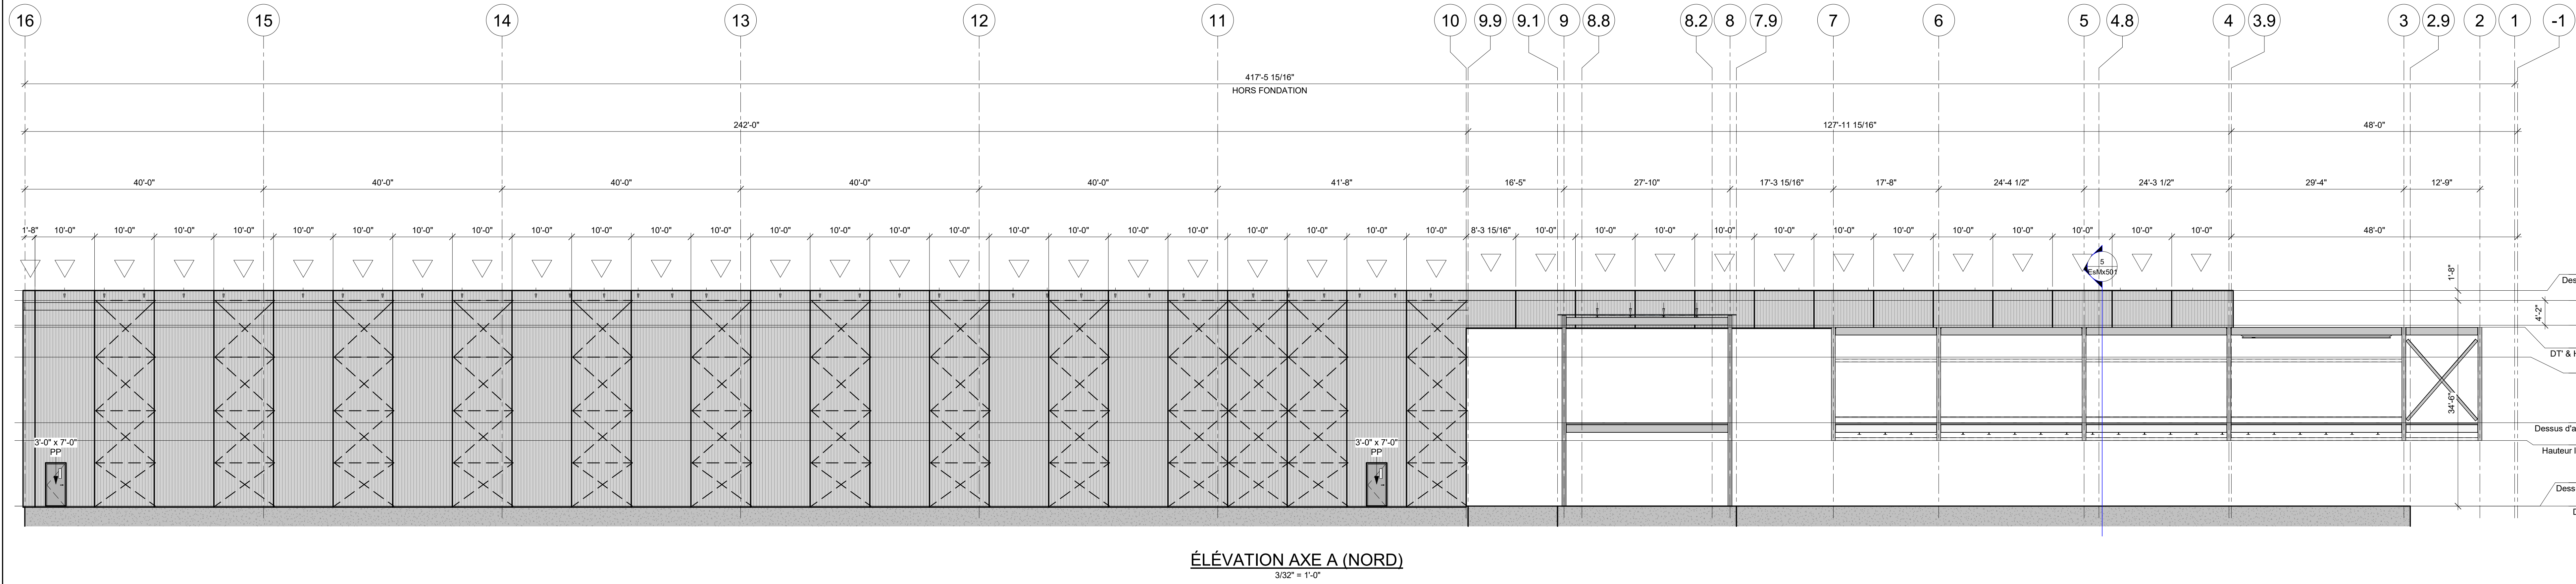

ÉLEVATION AXE A (NORD)
3/32" = 1'-0"

NOTE POUR LE CONTRACTEUR/ÉRECTEUR:
IL EST STRICTEMENT DÉFENDU DE MODIFIER, COPIER, REPRODUIRE OU DE DISTRIBUER CES DESSINS OU QUELQUES REPRÉSENTATIONS DE CES DESSINS, PAR TOUTES SOURCES DE MÉDIA INCLUANT ÉLECTRONIQUEMENT, SANS L'APPROBATION ÉCRITE DE GROUPE CANAM INC.

PRÉLIMINAIRE

NE DOIT PAS SERVIR À LA CONSTRUCTION

REVISION	DATE	DESCRIPTION	DESS	VER
GERANT DE PROJET				
-				
-				
