


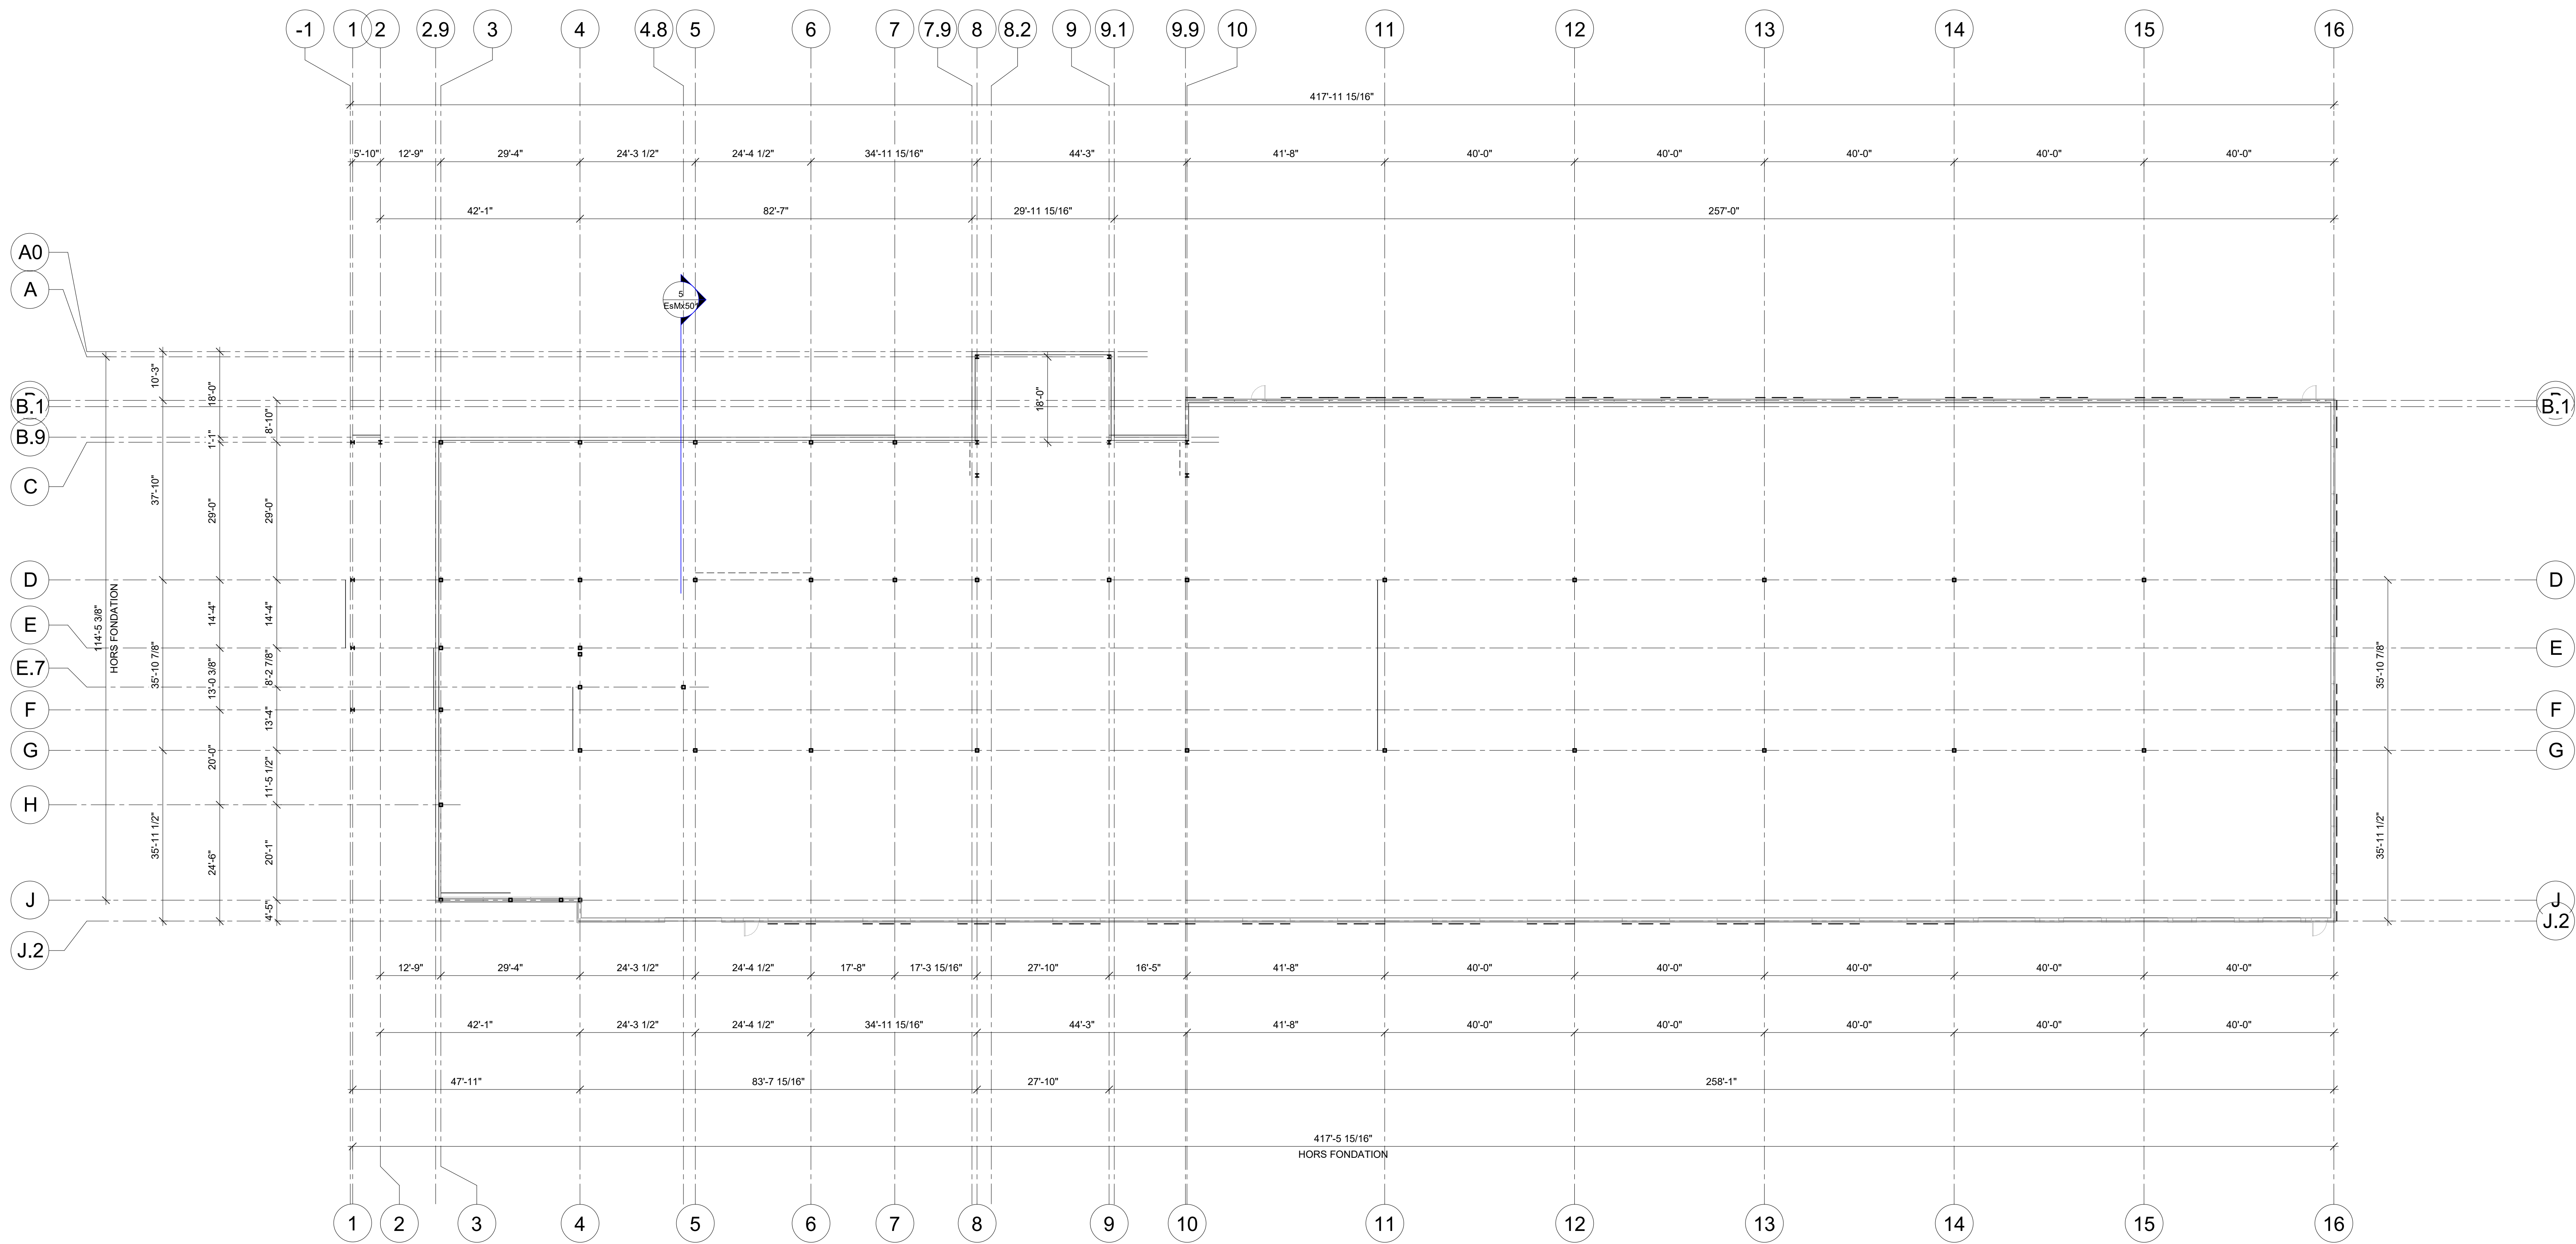

PLAN D'ANCRAGE
1/16\" = 1'-0"

PRÉLIMINAIRE

NE DOIT PAS SERVIR À LA
CONSTRUCTION

REVISION	DATE	DESCRIPTION	DESS	VER
----------	------	-------------	------	-----

GERANT DE PROJET	-
	-
	-
	-

DESSIN

DESSINÉ PAR	CONÇU PAR	INGÉNIEUR DU PROJET	ÉCHELLE:
HSC			1/16\" = 1'-0"
VERIFIÉ PAR	INGÉNIEURS CONSEILS / ARCHITECTES	DATE (mm/aaaa)	
		02/03/2026	

CLIENT: Les constructions Binet Inc.



SCAUX PROFESSIONNEL

PROJET

Nouveau Bâtiment CMI Motors
St-Georges

TITRE
CROQUIS PRÉLIMINAIRE - PLAN
D'ANCRAGE

NUMERO CONTRAT	NUMERO DESSIN	DIVISION	REVISION
P2026-043	EsMx101		

Initiales

