


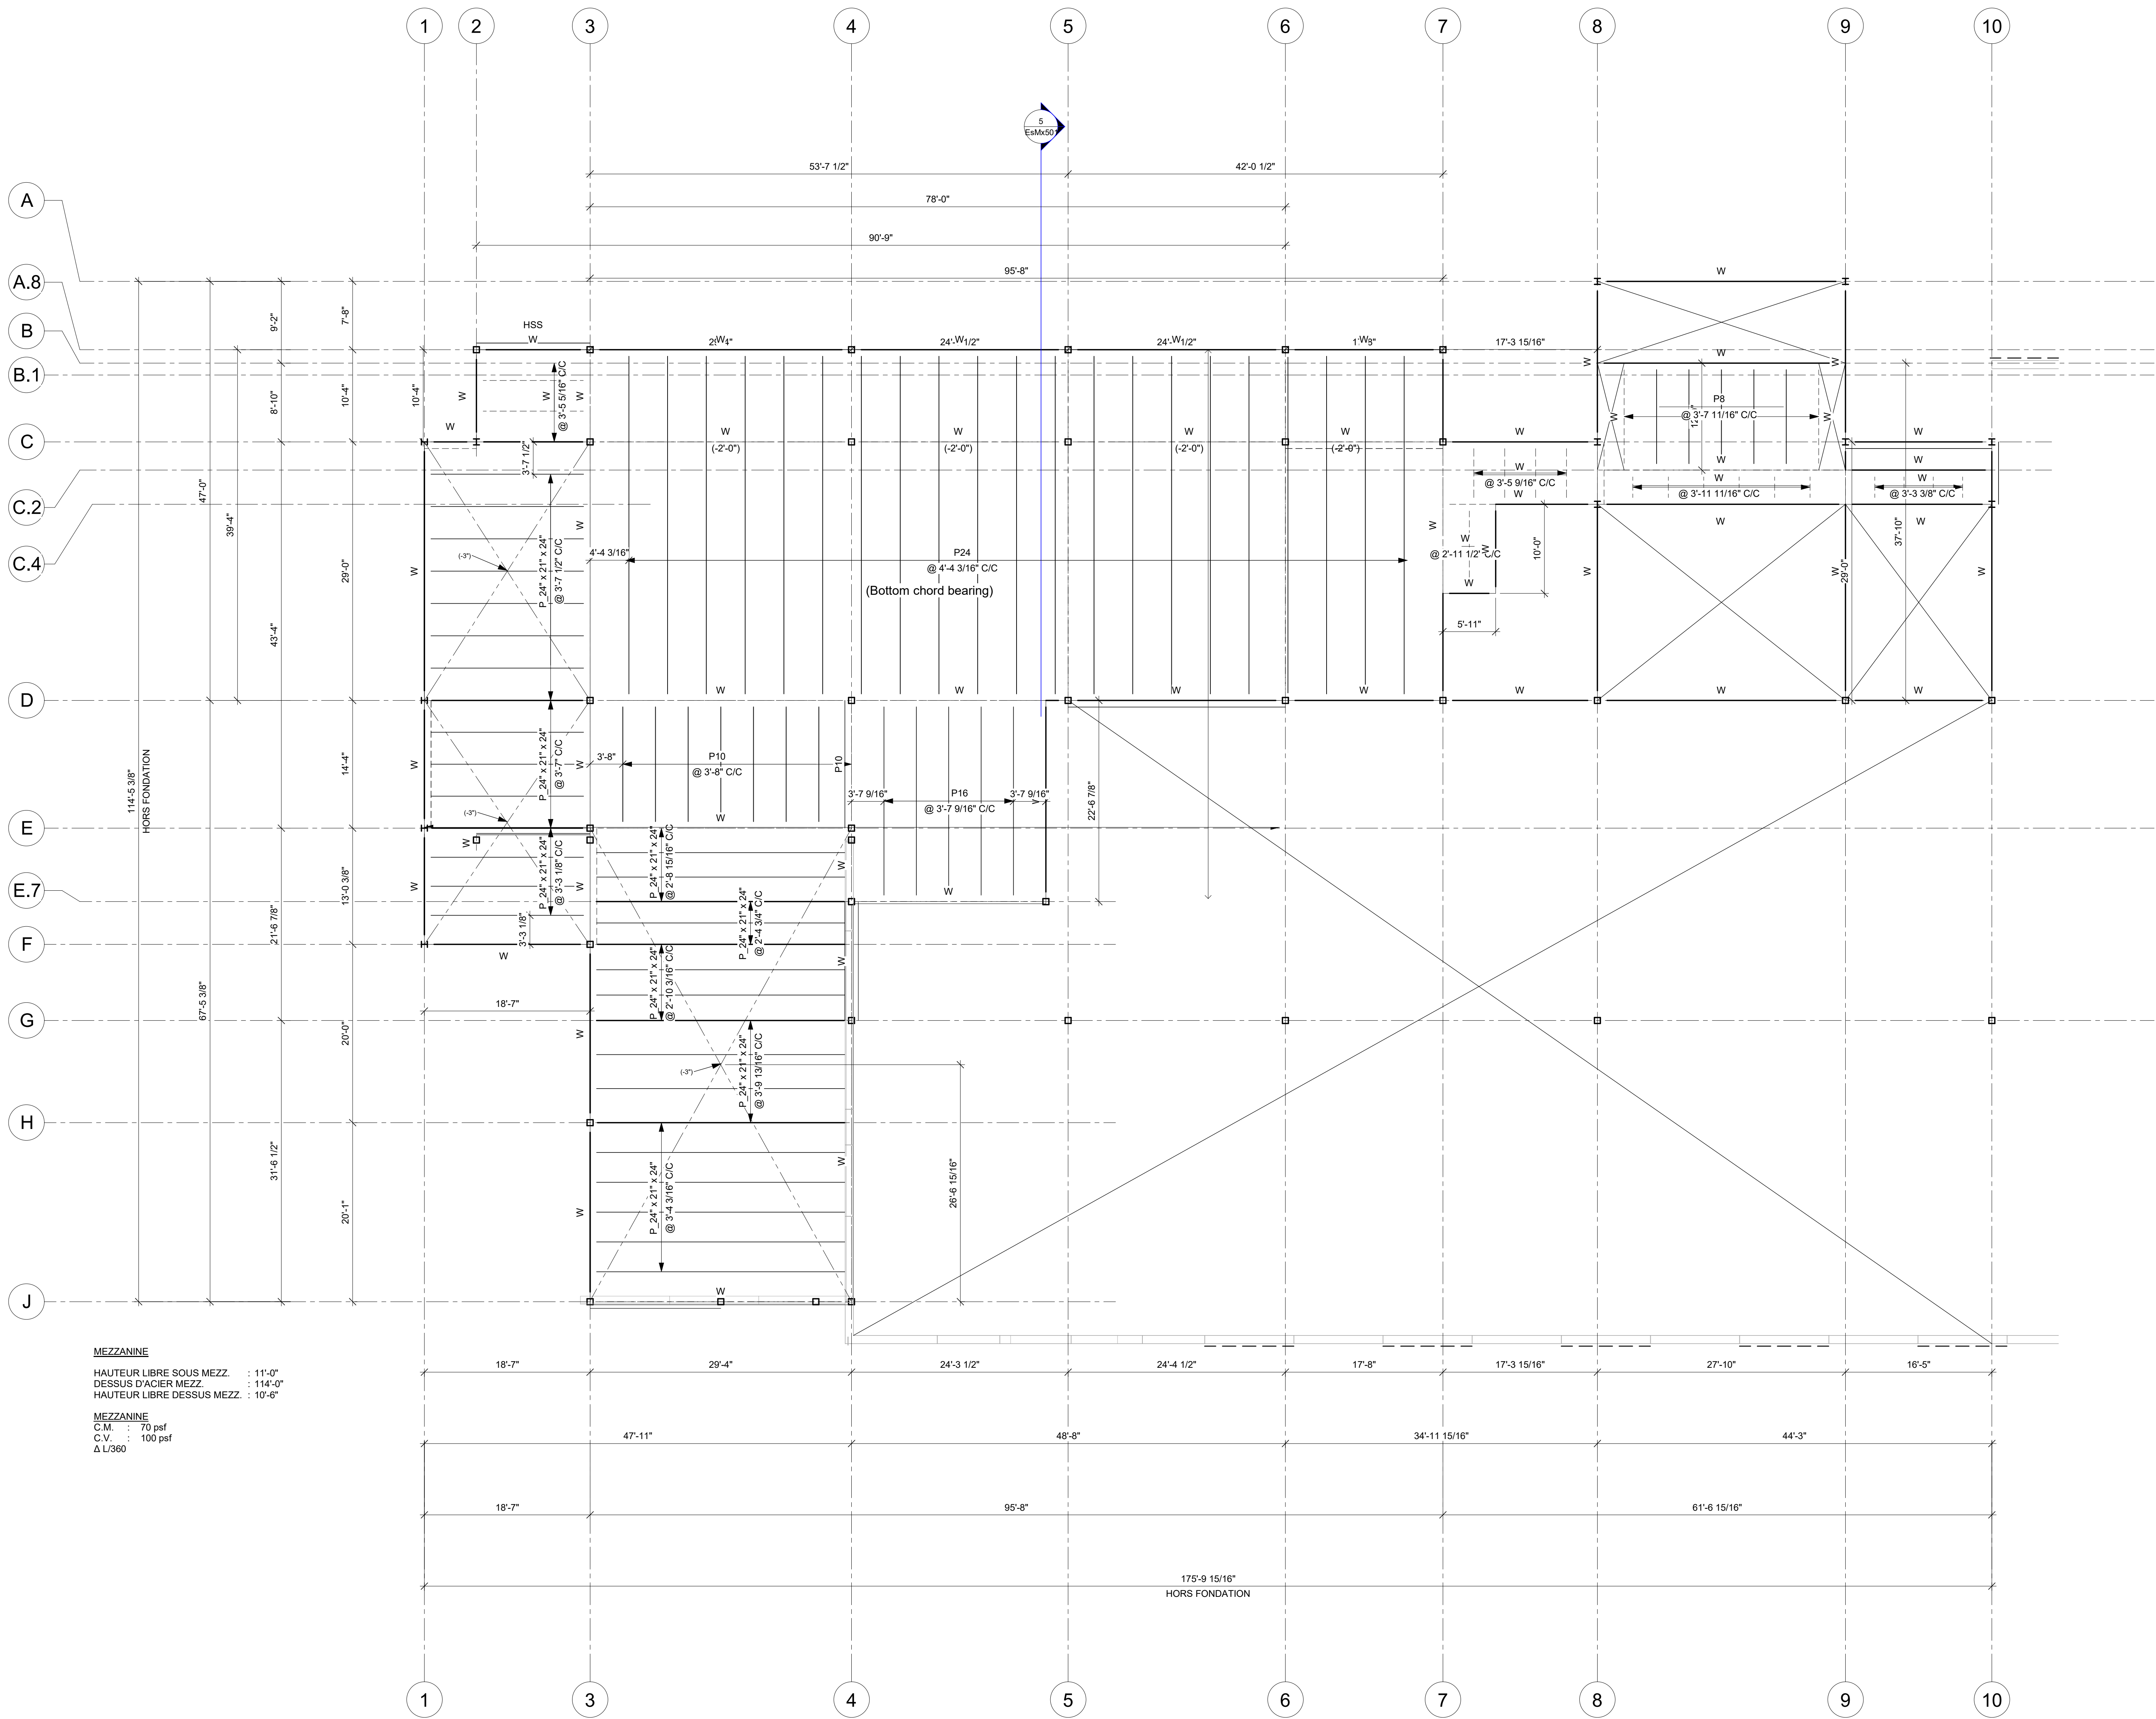

MEZZANINE
HAUTEUR LIBRE SOUS MEZZ. : 11'-0"
DESSUS D'ACIER MEZZ. : 114'-0"
HAUTEUR LIBRE DESSUS MEZZ. : 10'-8"
MEZZANINE
C.M. : 70 psf
C.V. : 100 psf
Δ U080


PLAN DE MEZZANINE
1/8" = 1'-0"

NOTE POUR LE CONTRACTEUR/ÉRECTEUR:
IL EST STRICTEMENT DÉFENDU DE MODIFIER, COPIER, REPRODUIRE OU
DE DISTRIBUER CES DESSINS OU QUELQUES REPRÉSENTATIONS DE
CES DESSINS, PAR TOUTES SOURCES DE MÉDIA INCLUANT
ÉLECTRONIQUEMENT, SANS L'APPROBATION ÉCRITE DE GROUPE
CANAM INC.

PRÉLIMINAIRE

NE DOIT PAS SERVIR À LA
CONSTRUCTION

REVISION	DATE	DESCRIPTION	DESS	VER
GERANT DE PROJET				
-				
-				
-				
-				
-				
DESSIN				
DESSINÉ PAR	CONÇU PAR	INGÉNIEUR DU PROJET	ECHELLE:	
HSC			1/8" = 1'-0"	
VERIFIÉ PAR	INGÉNIEURS CONSEILS / ARCHITECTES		DATE (mm/aa/aaaa):	
			02/03/2026	
CLIENT:	Les constructions Binet Inc.			

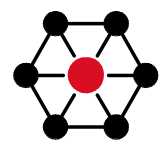 **CANAM**
11505, 1re Avenue, bureau 500, Saint-Georges Beauce
Québec, Canada, G5Y 7X5
Téléphone : (418) 228-8031
Sans frais : (877) 459-8049
www.canam.com

SCAUX PROFESSIONNEL

PROJET

Nouveau Bâtiment CMI Motors
St-Georges

TITRE

CROQUIS PRÉLIMINAIRE - PLAN DE
MEZZANINE

Initiales

NUMÉRO CONTRAT	NUMÉRO DESSIN	DIVISION	REVISION
P2026-043	EsMx201		