



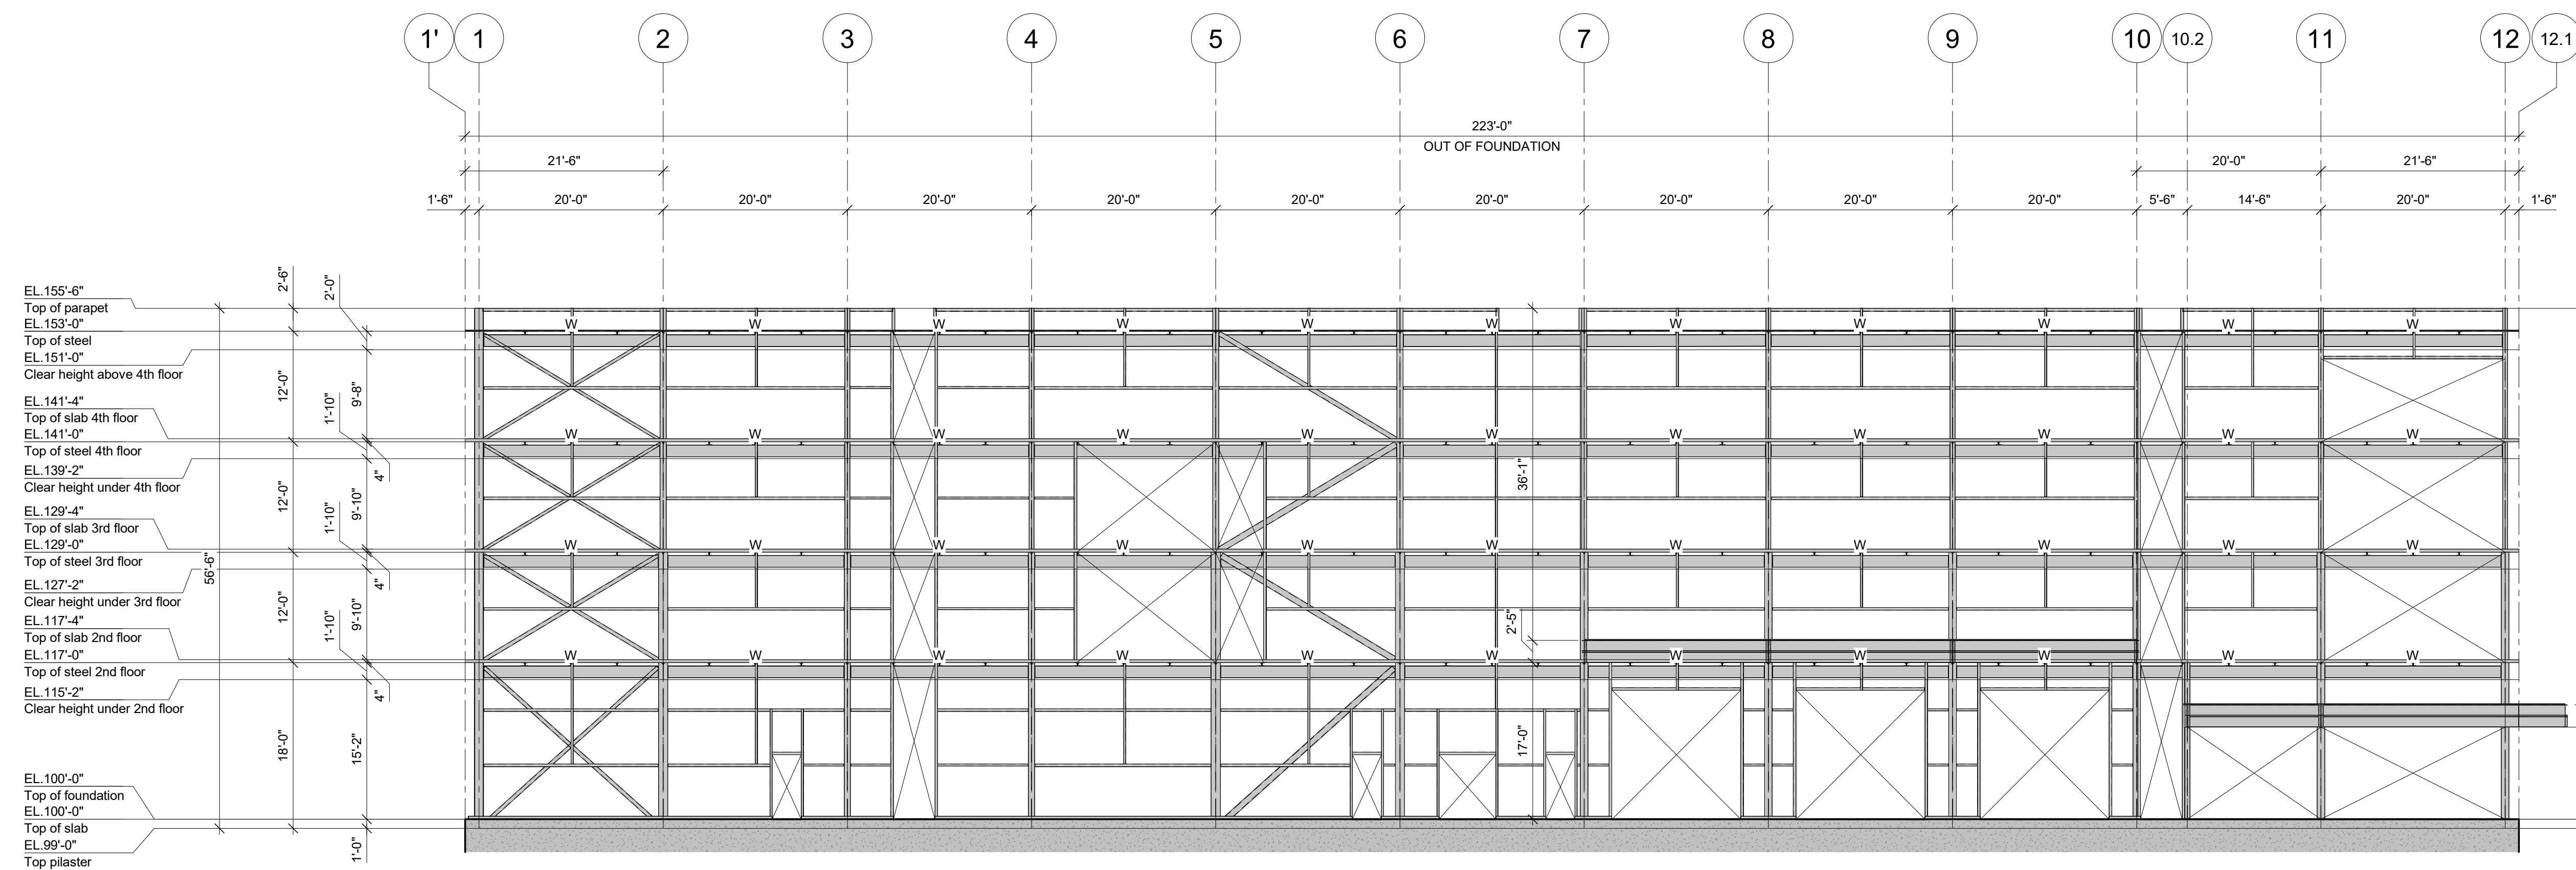


ELEVATION LINE H (EAST)

3/32" = 1'-0"

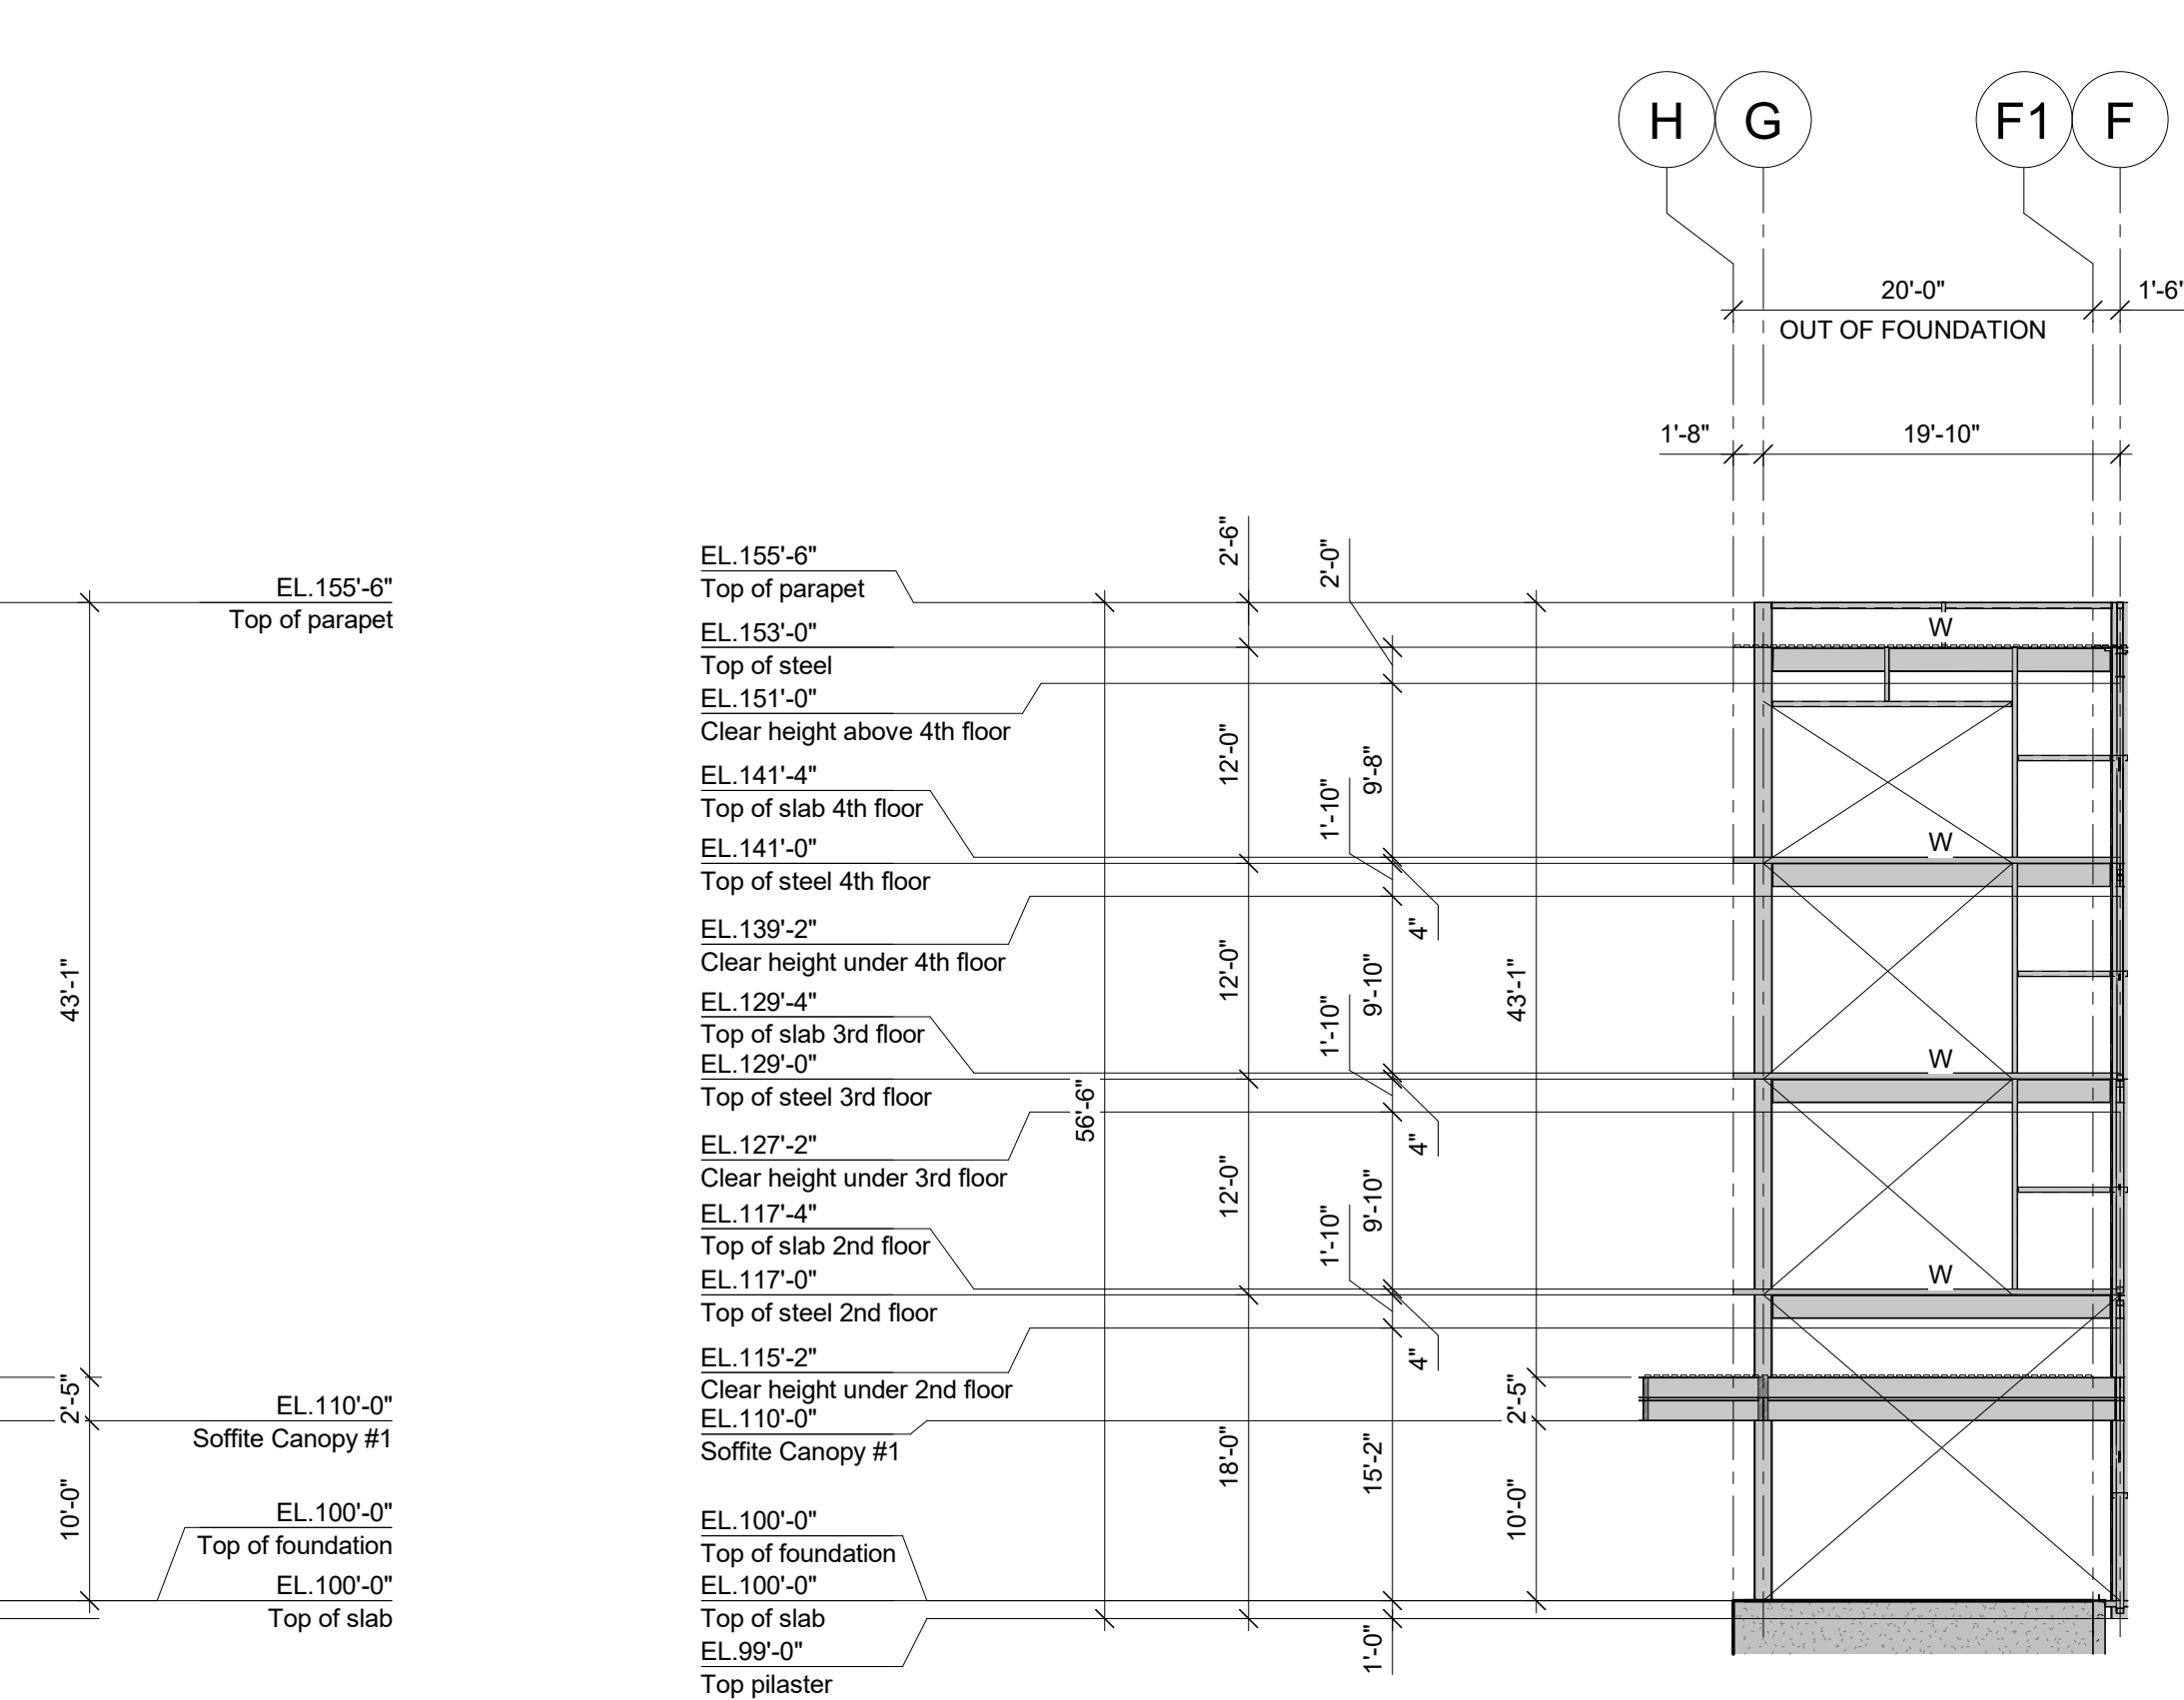


ELEVATION LINE 12.1 (NORTH)

3/32" = 1'-0"

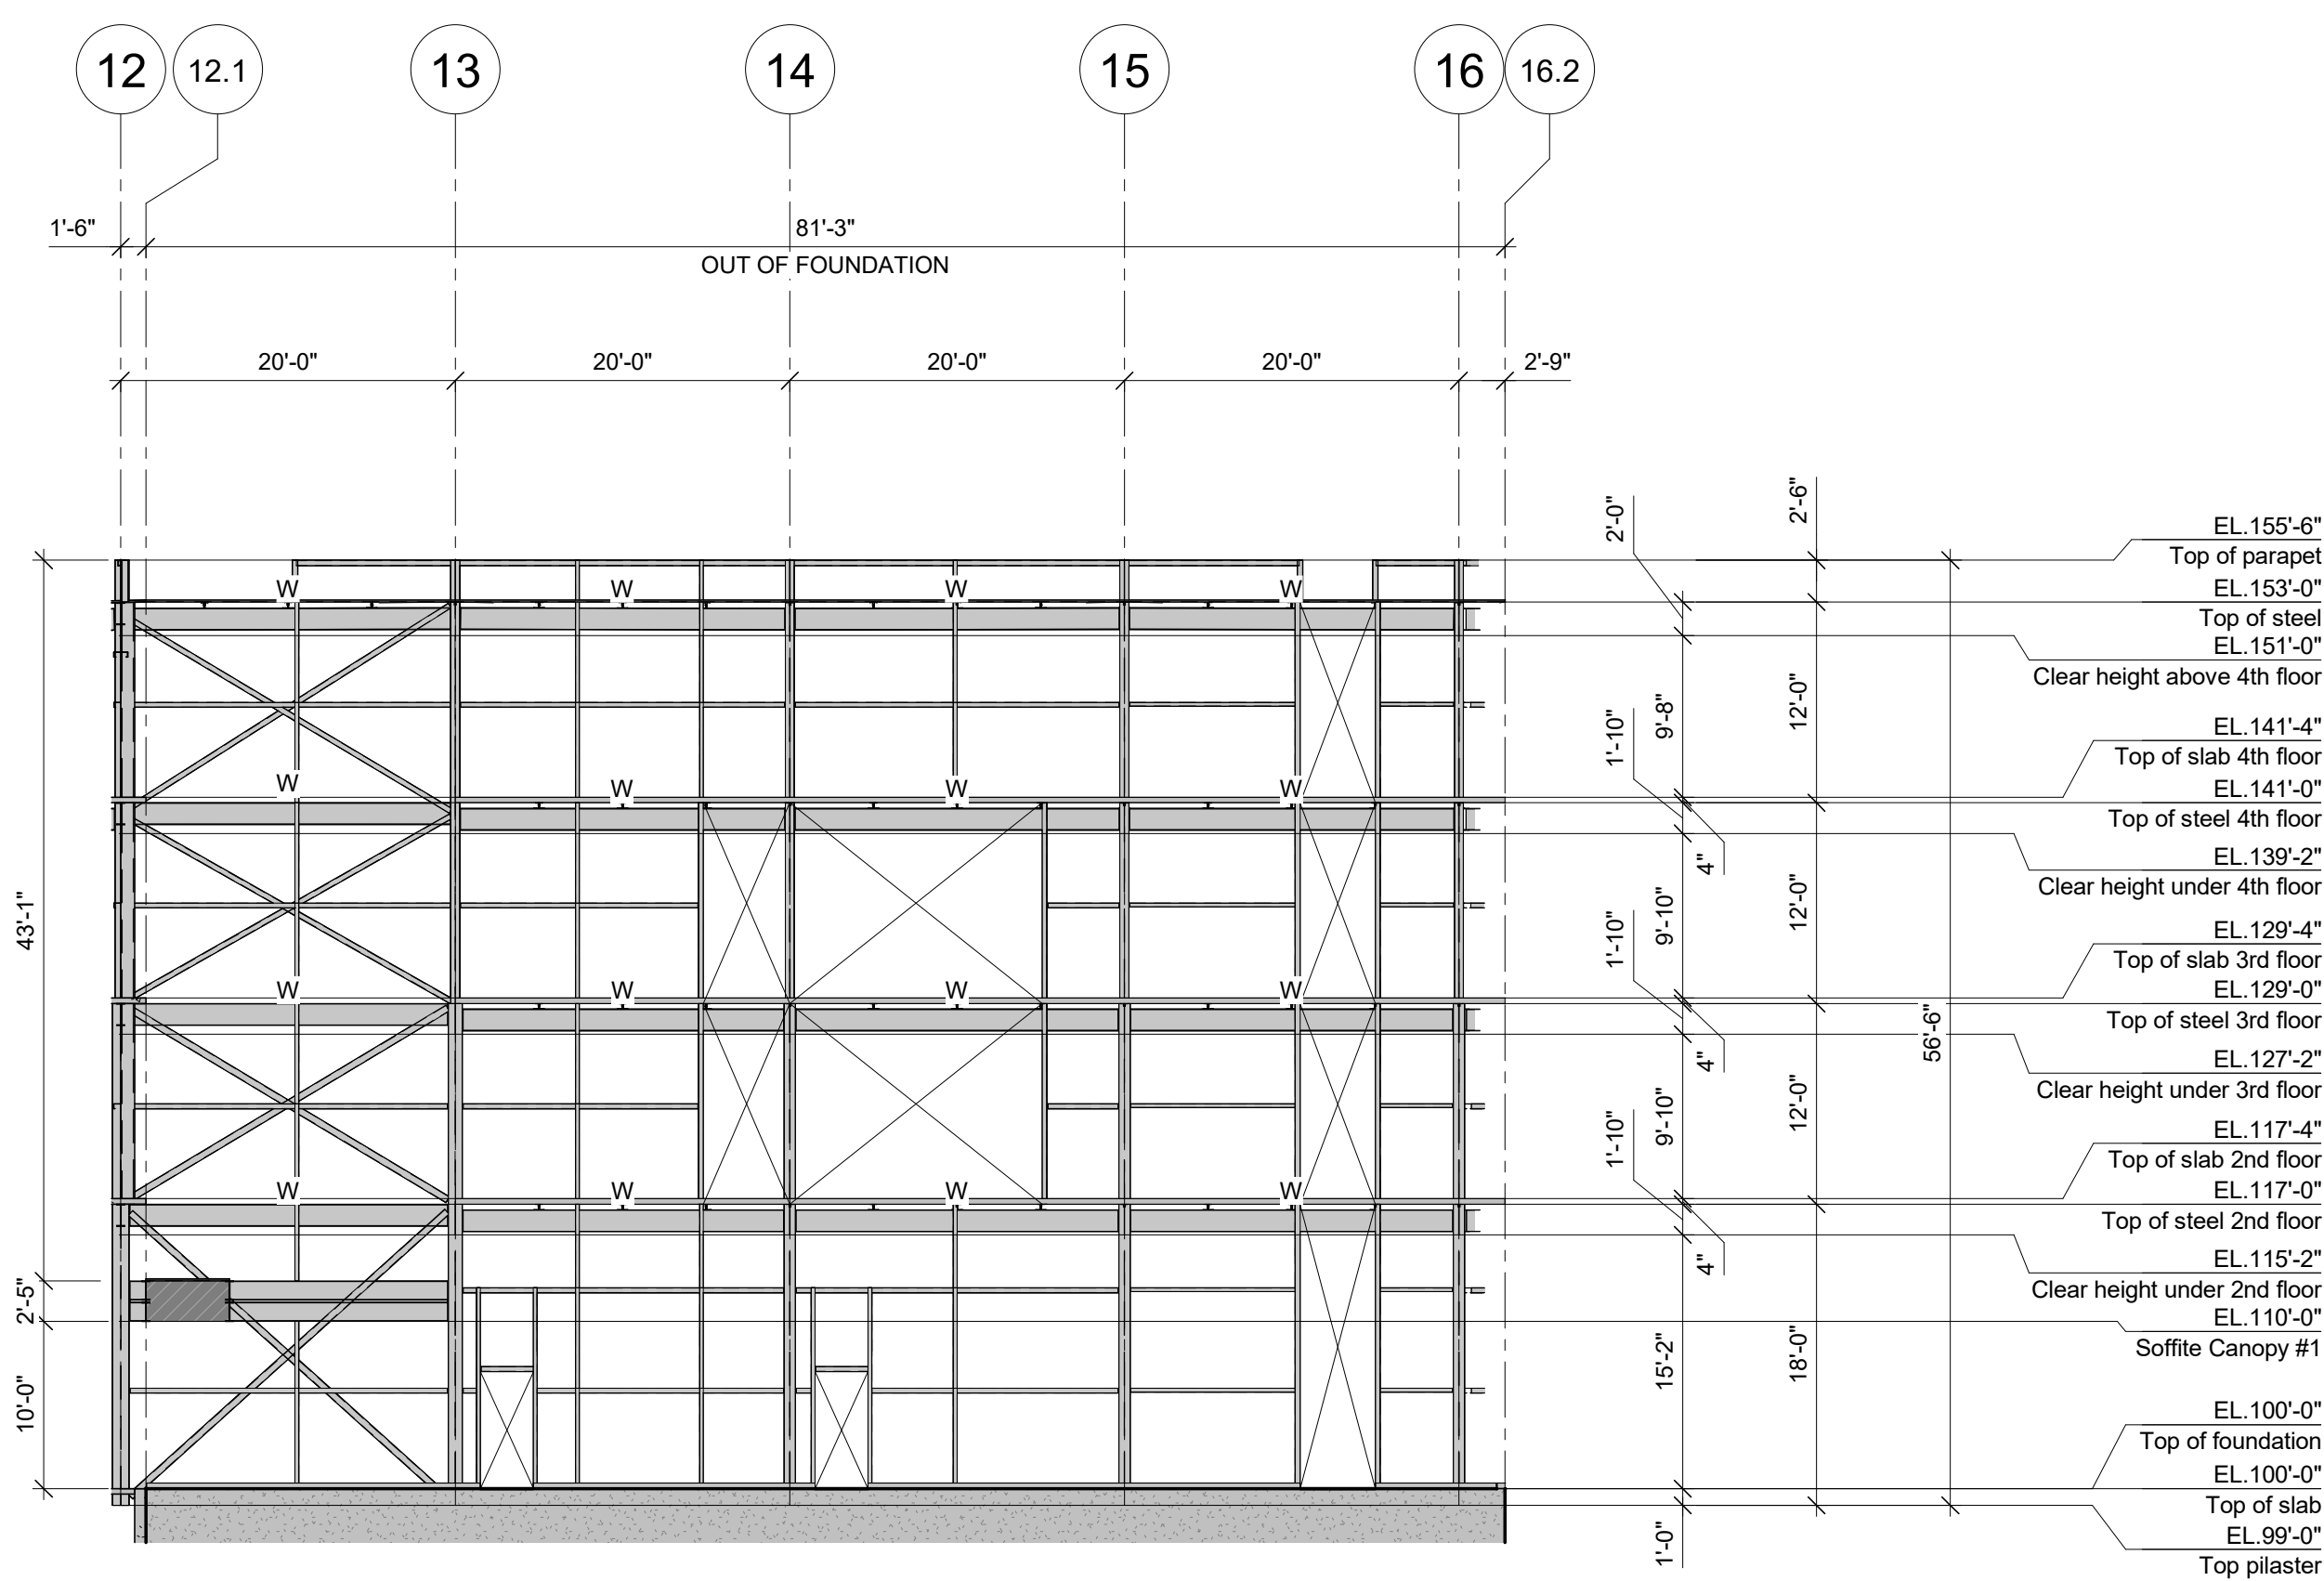


ELEVATION LINE F1 (EAST)

3/32" = 1'-0"

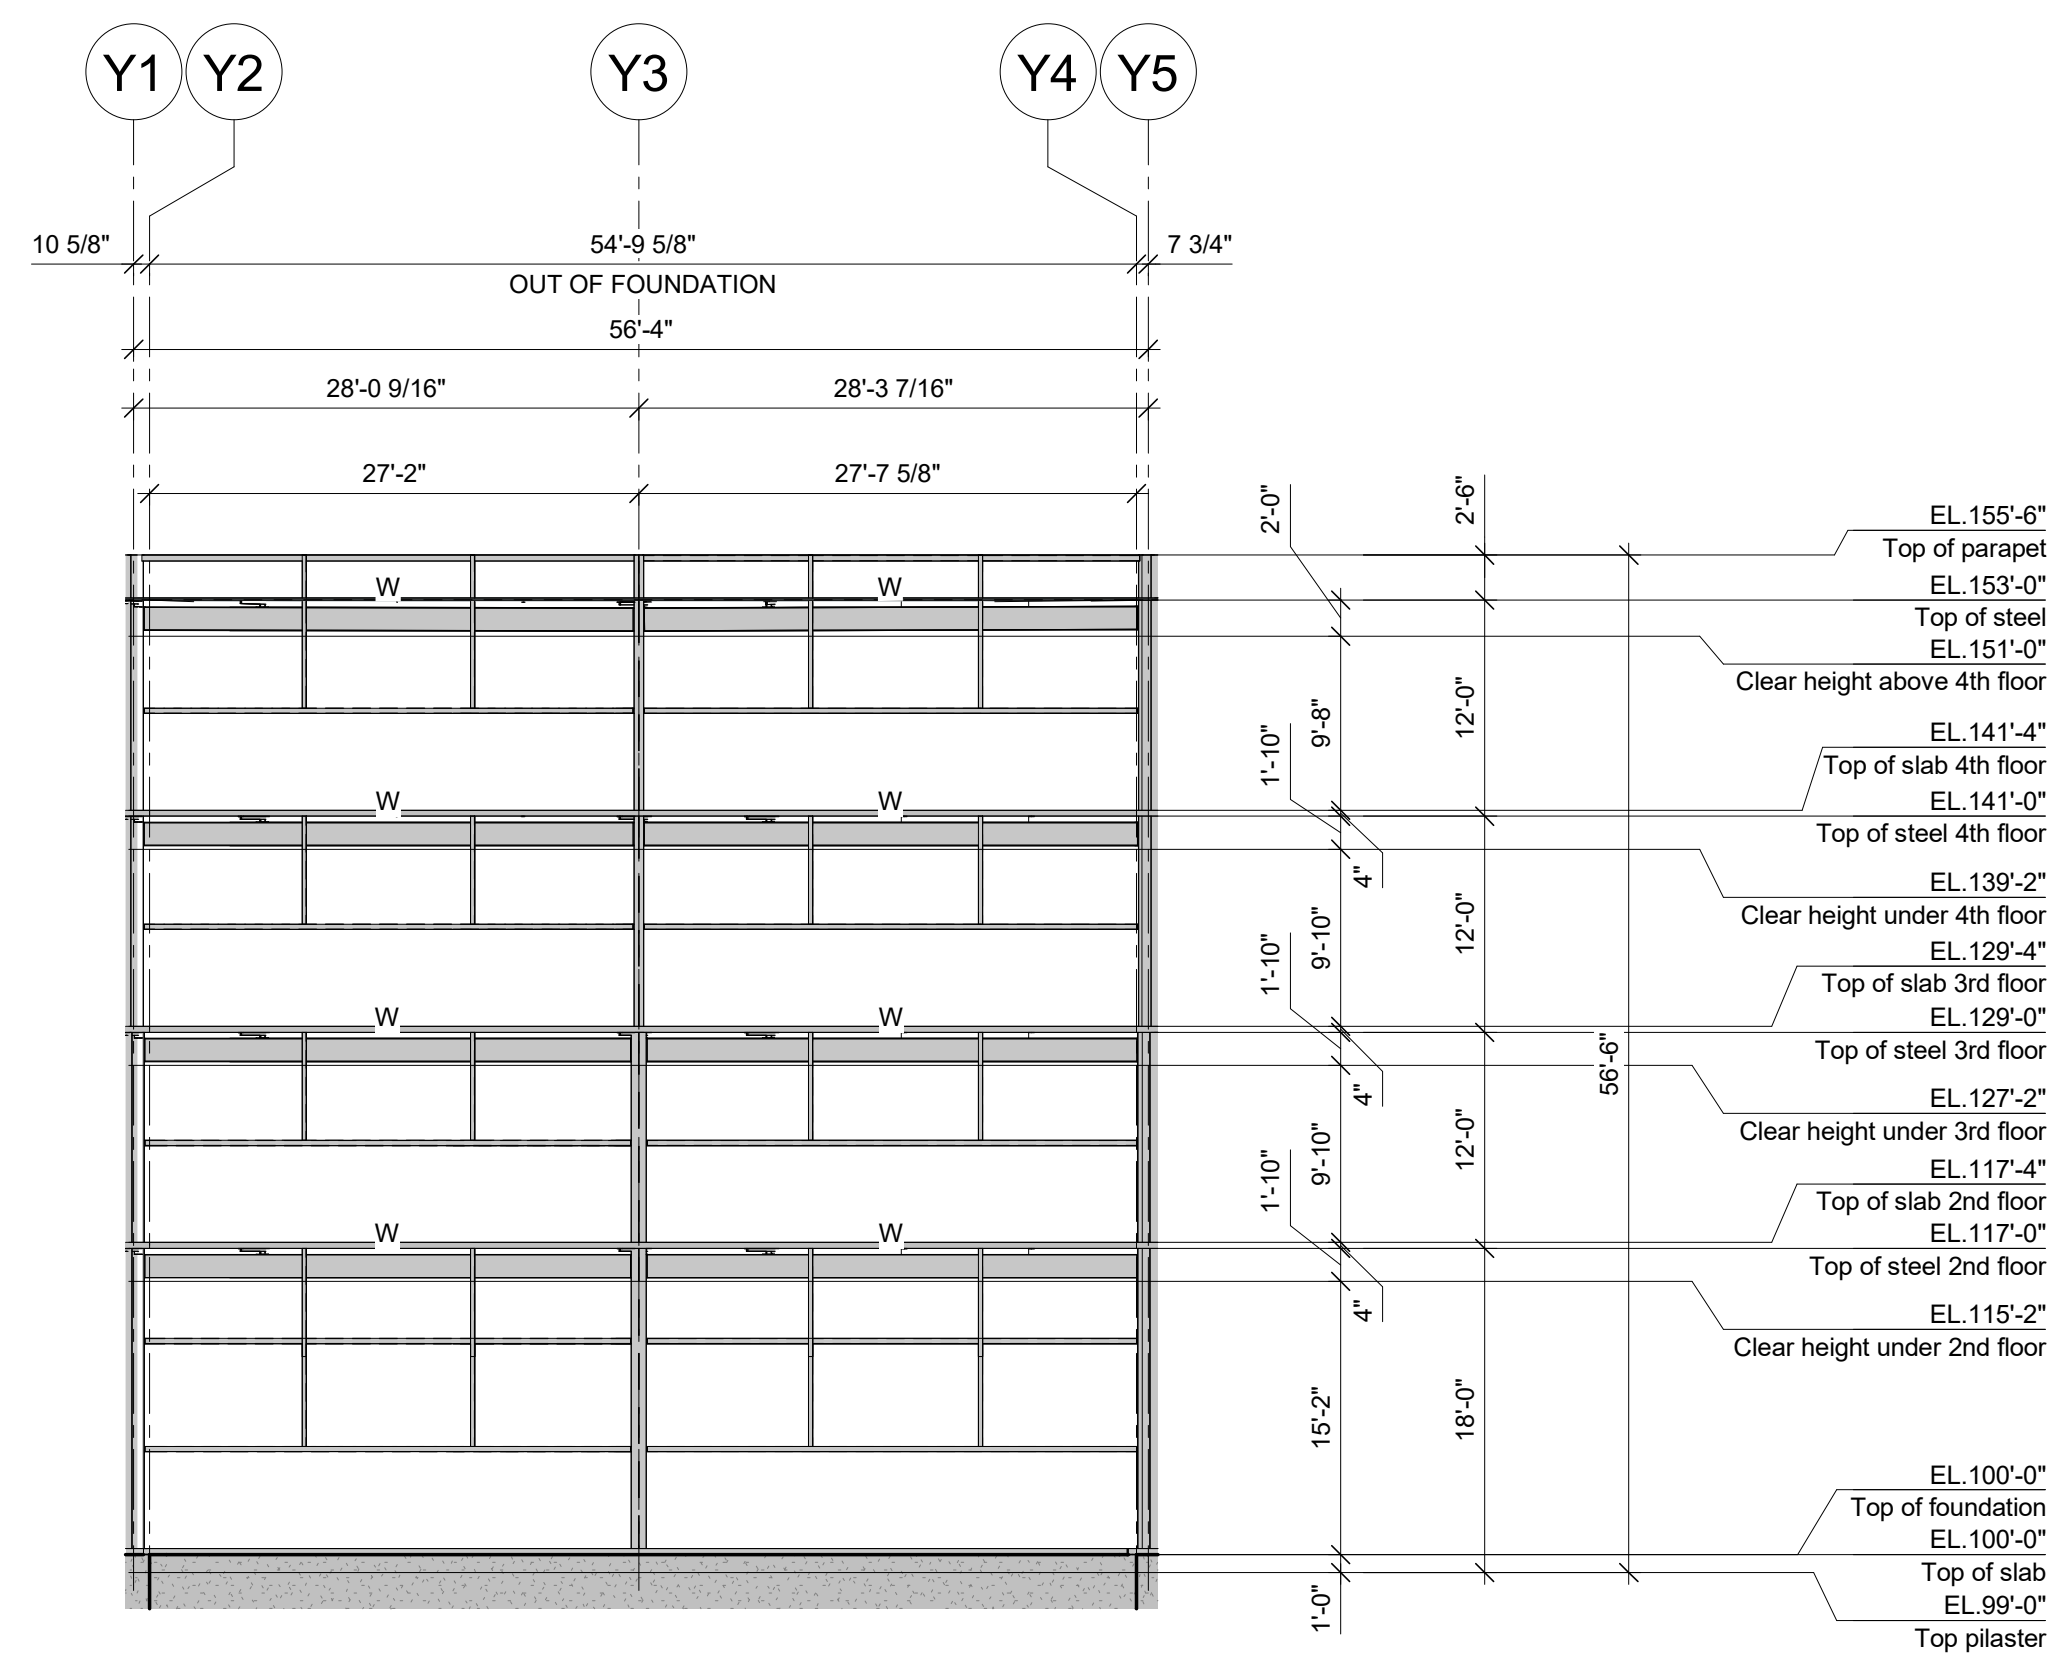


ELEVATION LINE Z1 (NORTH-EAST)

3/32" = 1'-0"

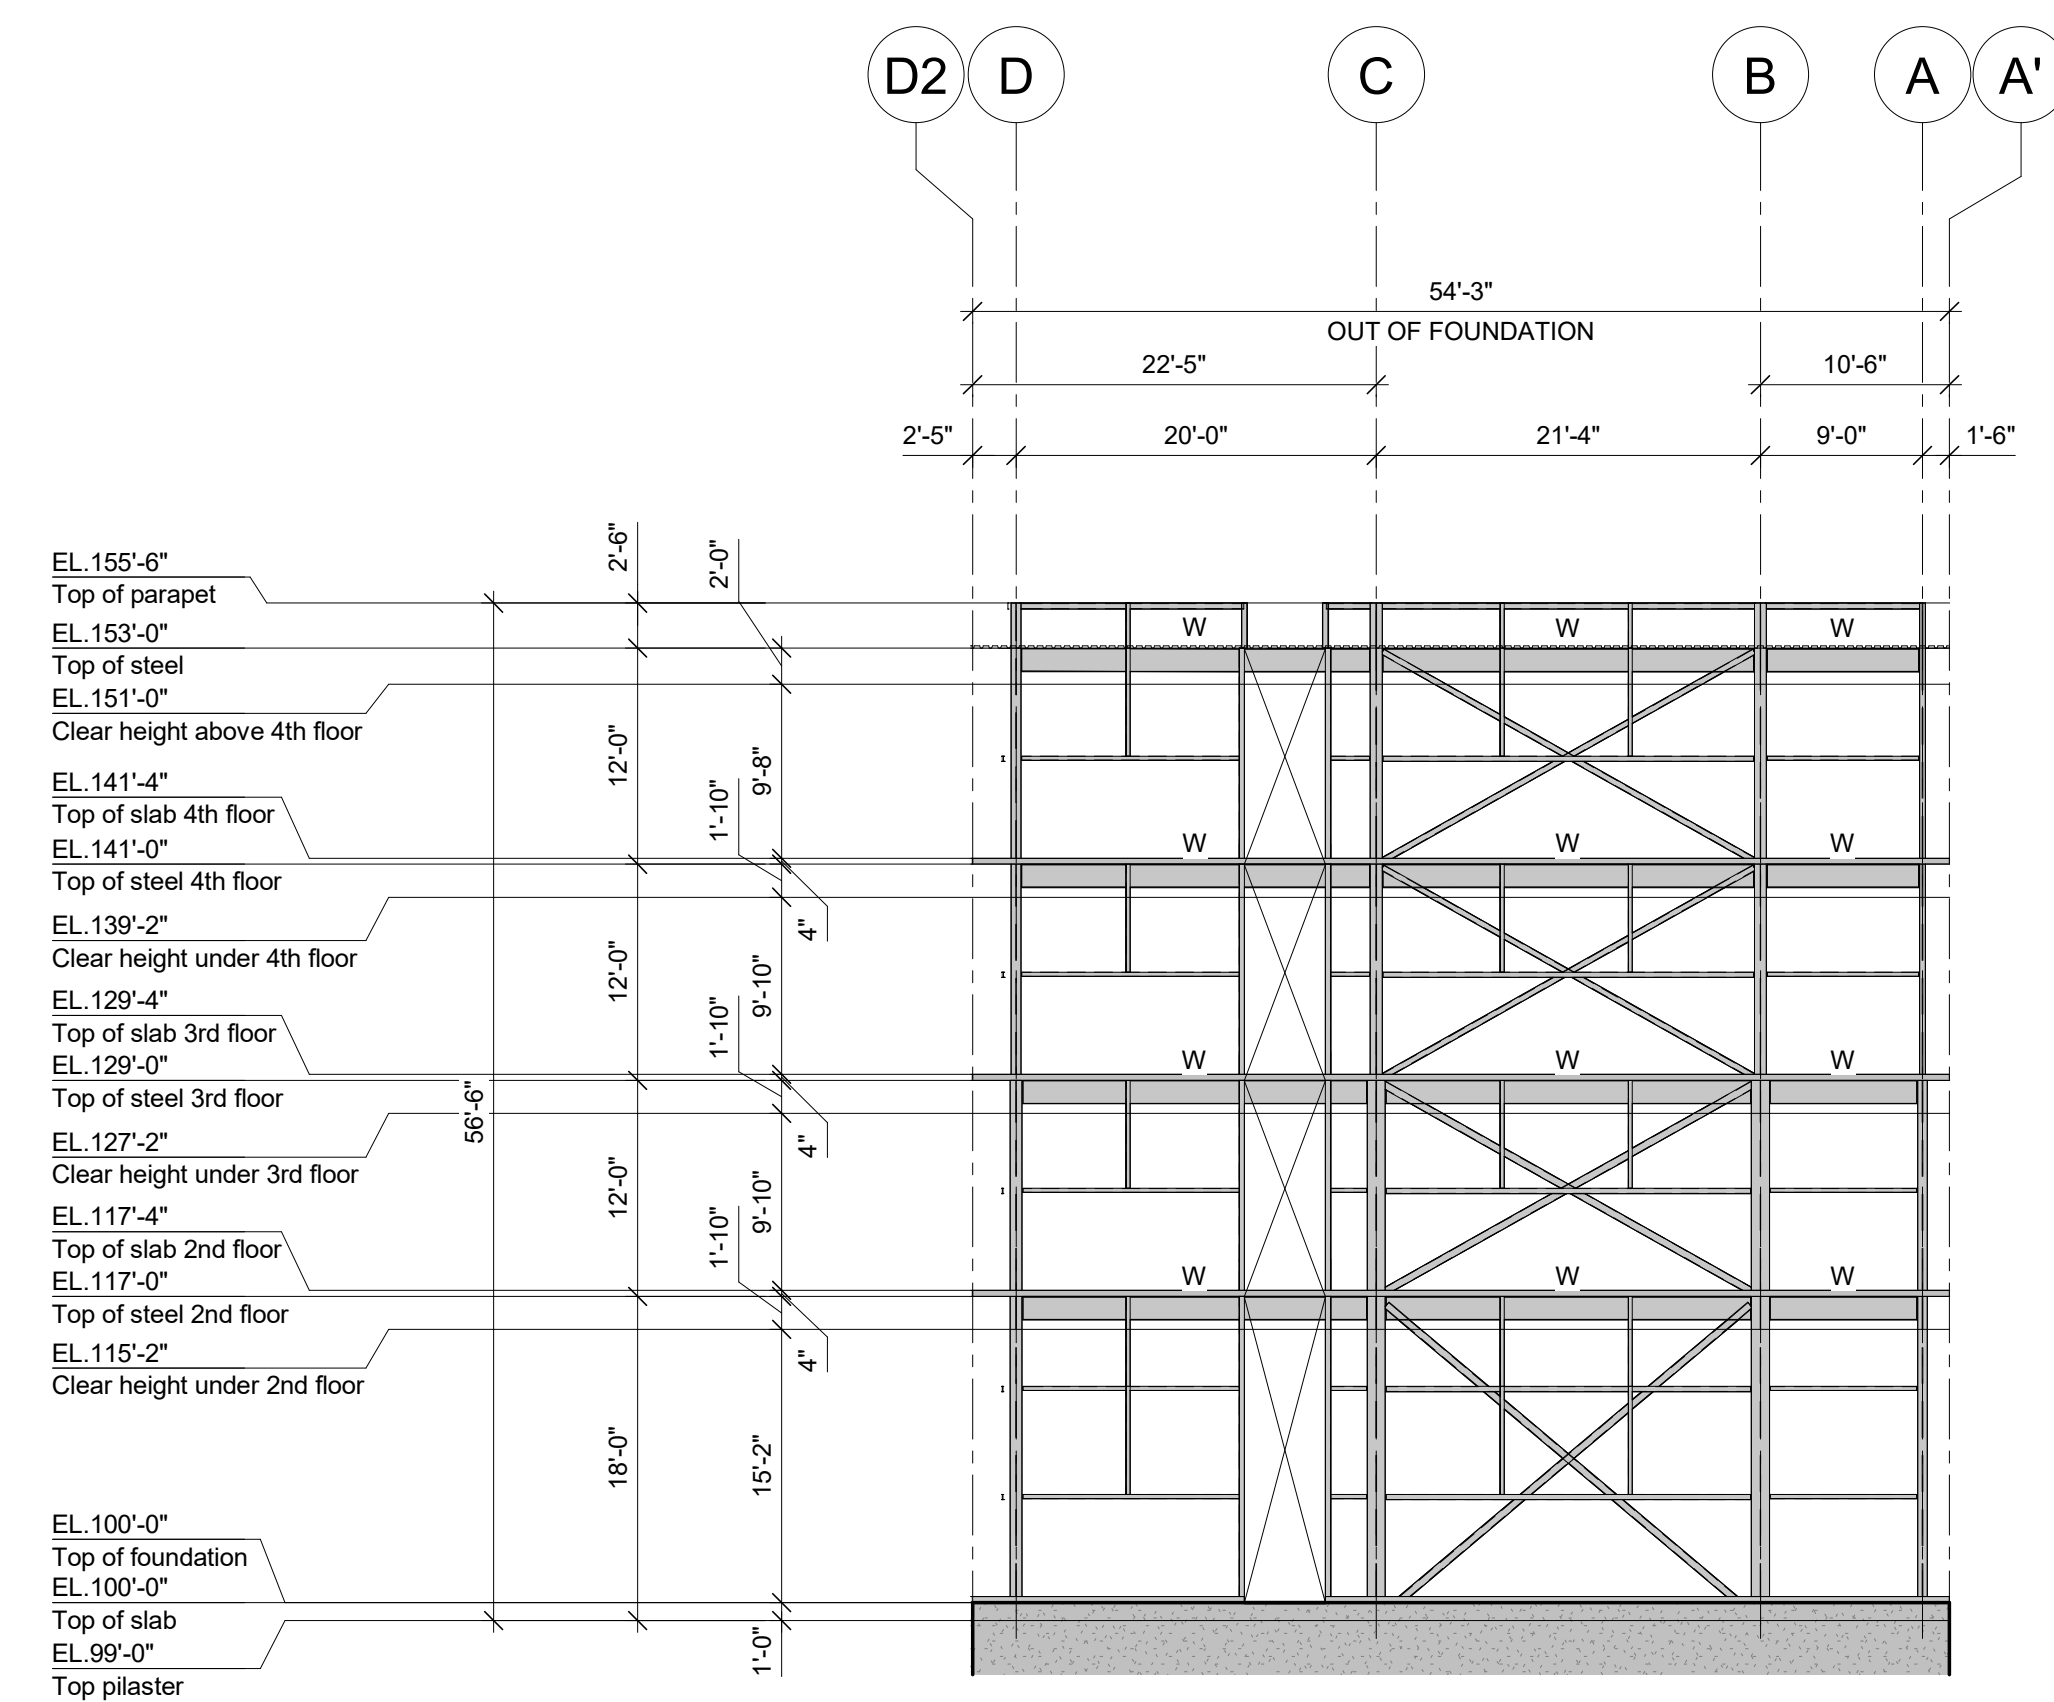

ELEVATION LINE 19 (NORTH)

3/32" = 1'-0"

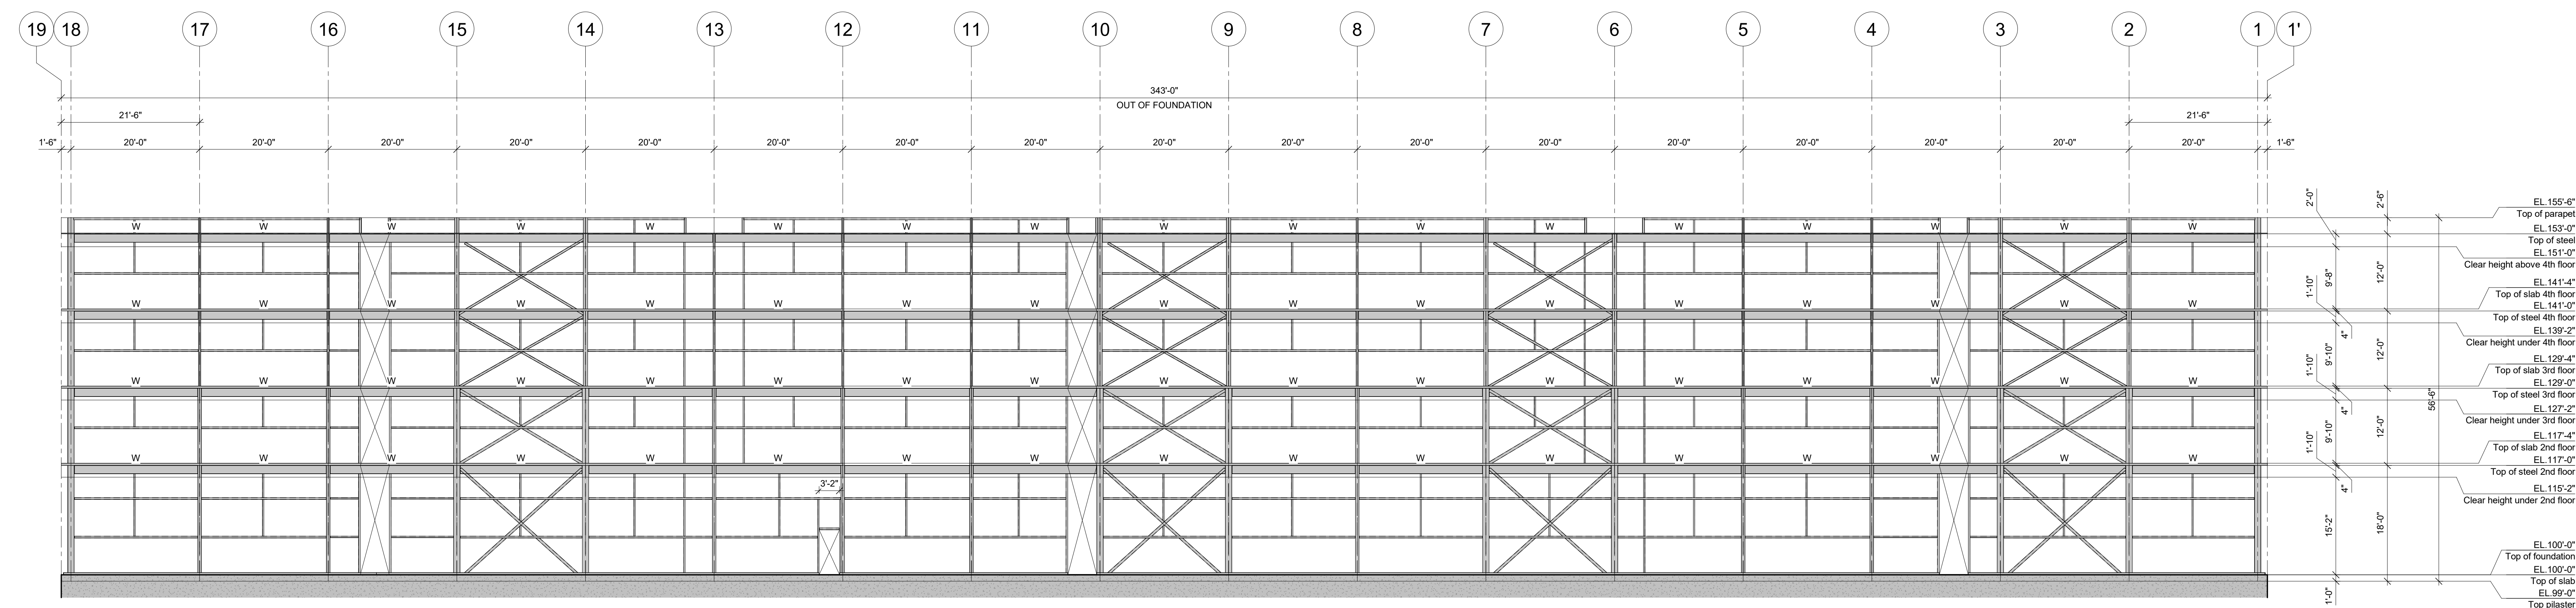

ELEVATION LINE A' (WEST)

3/32" = 1'-0"