




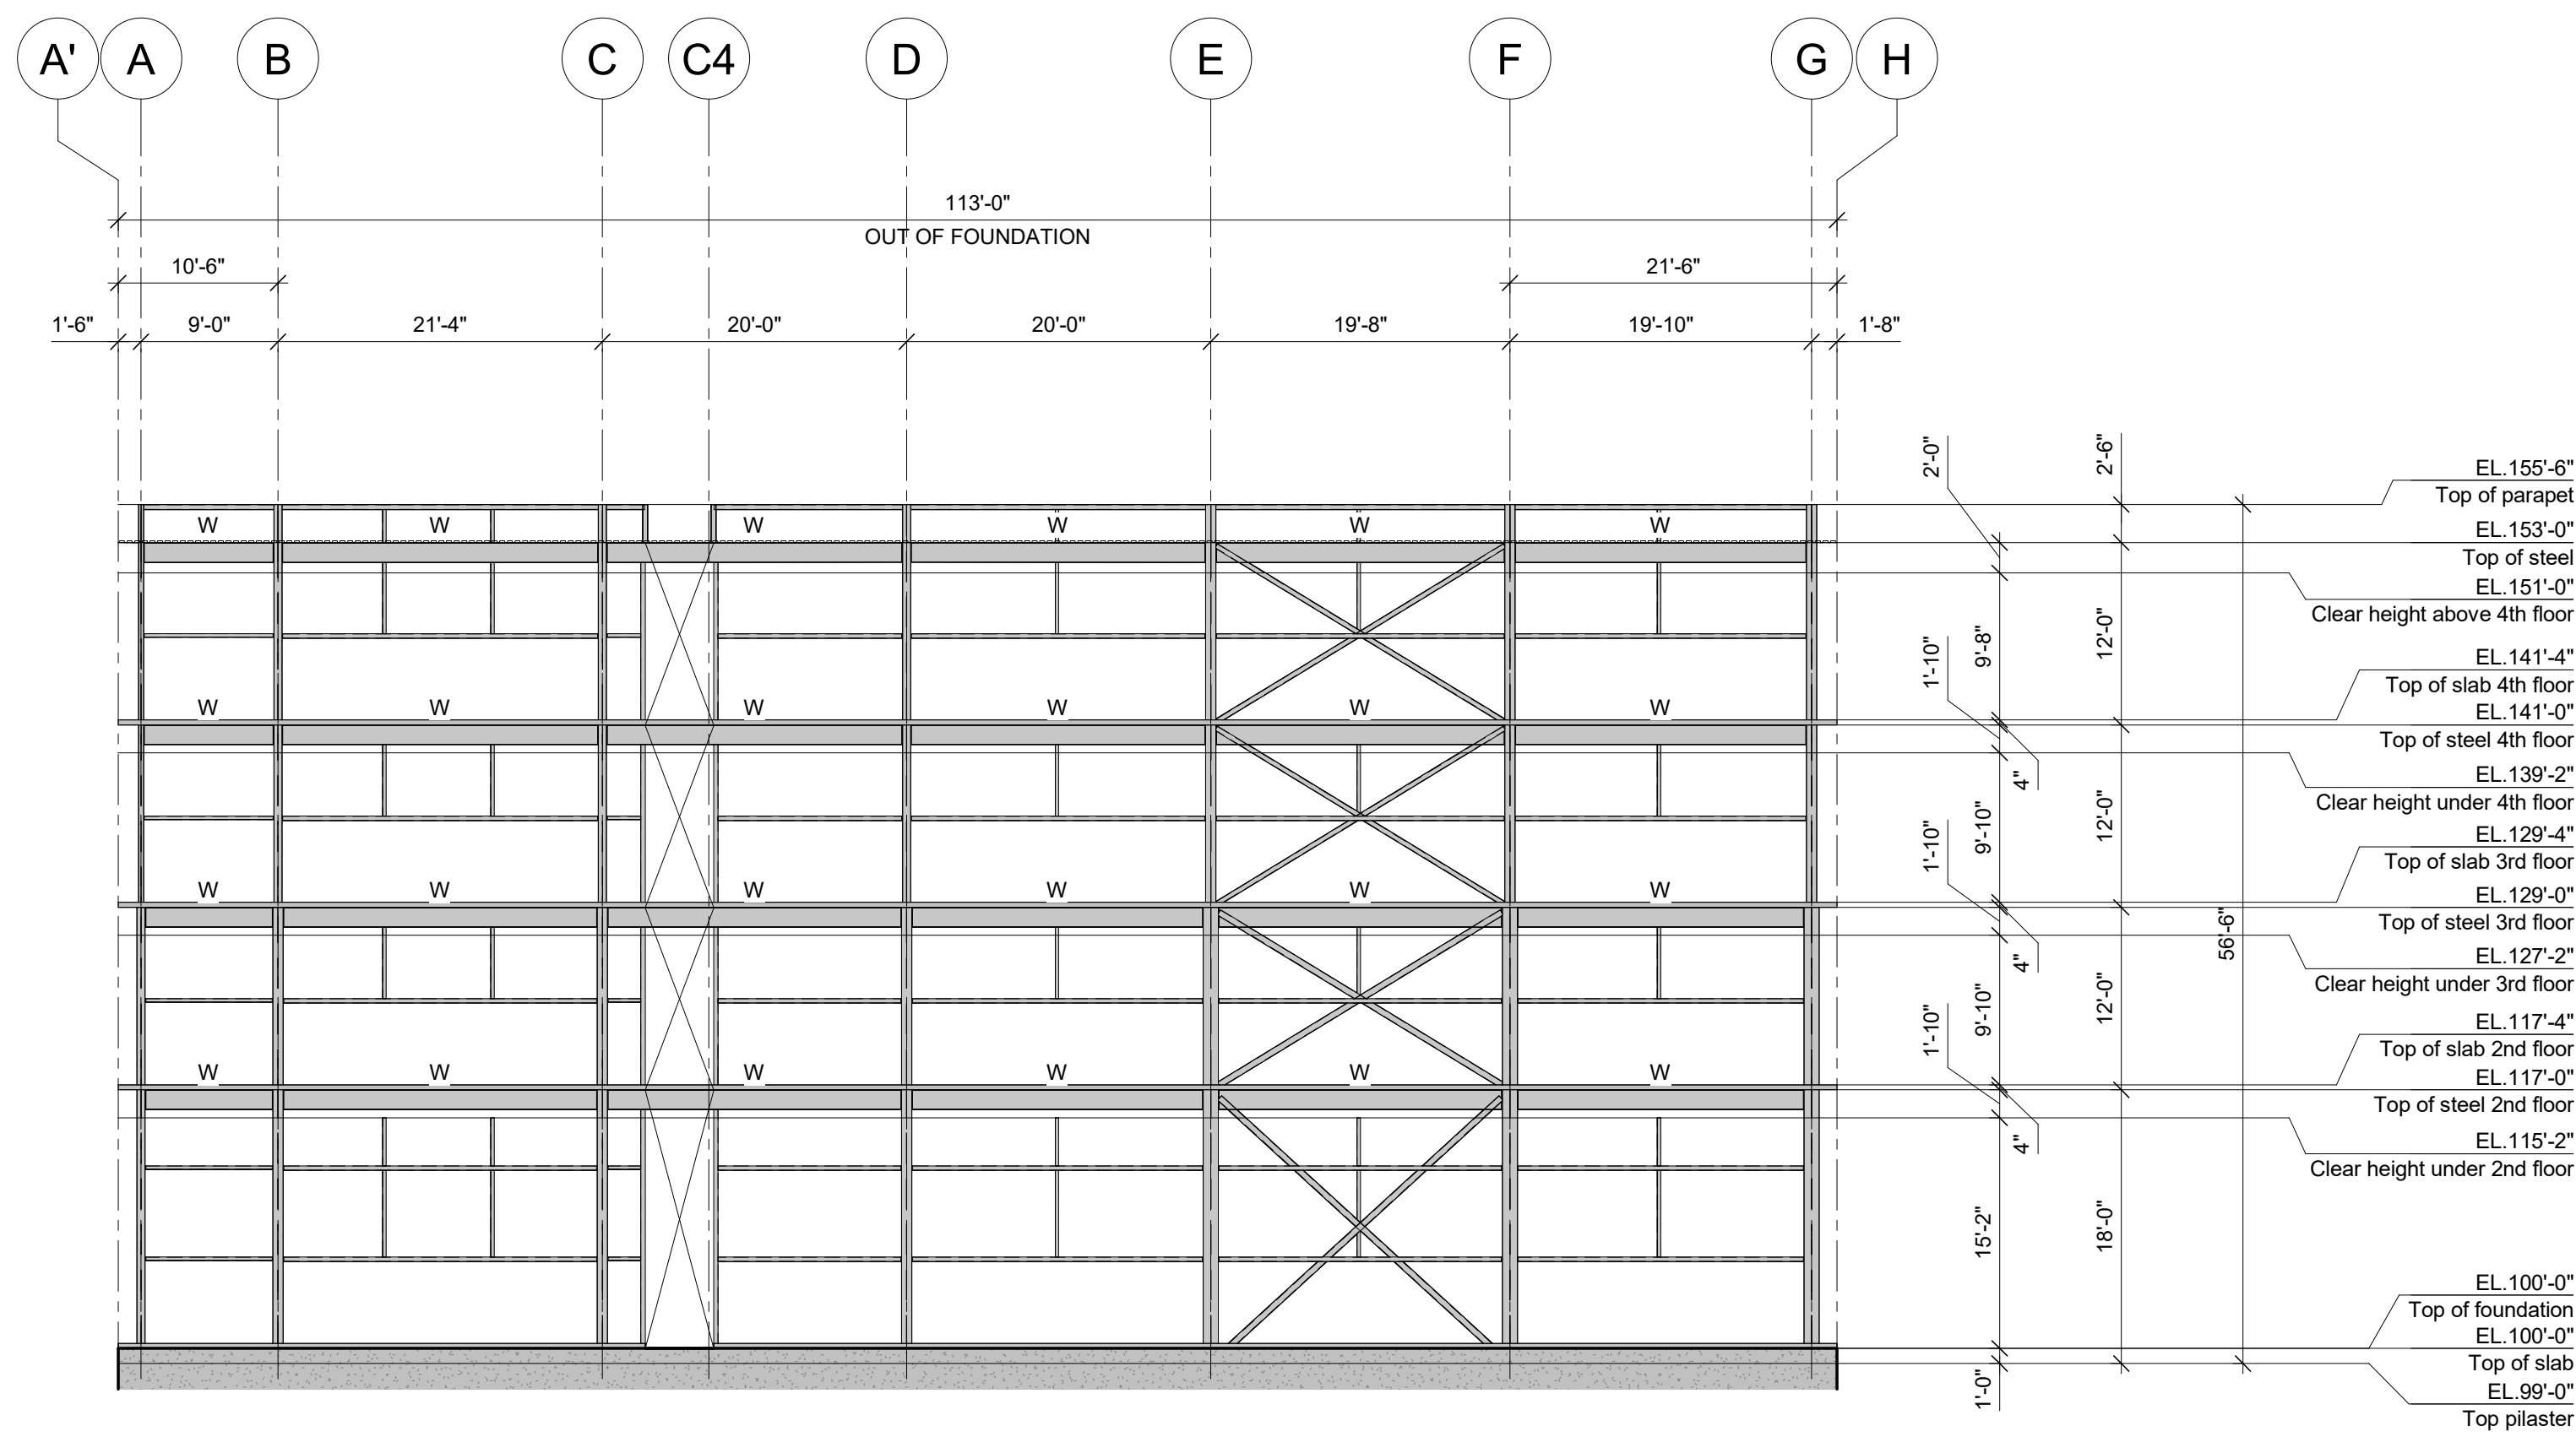


ELEVATION LINE 1' (SOUTH)
3/32" = 1'-0"

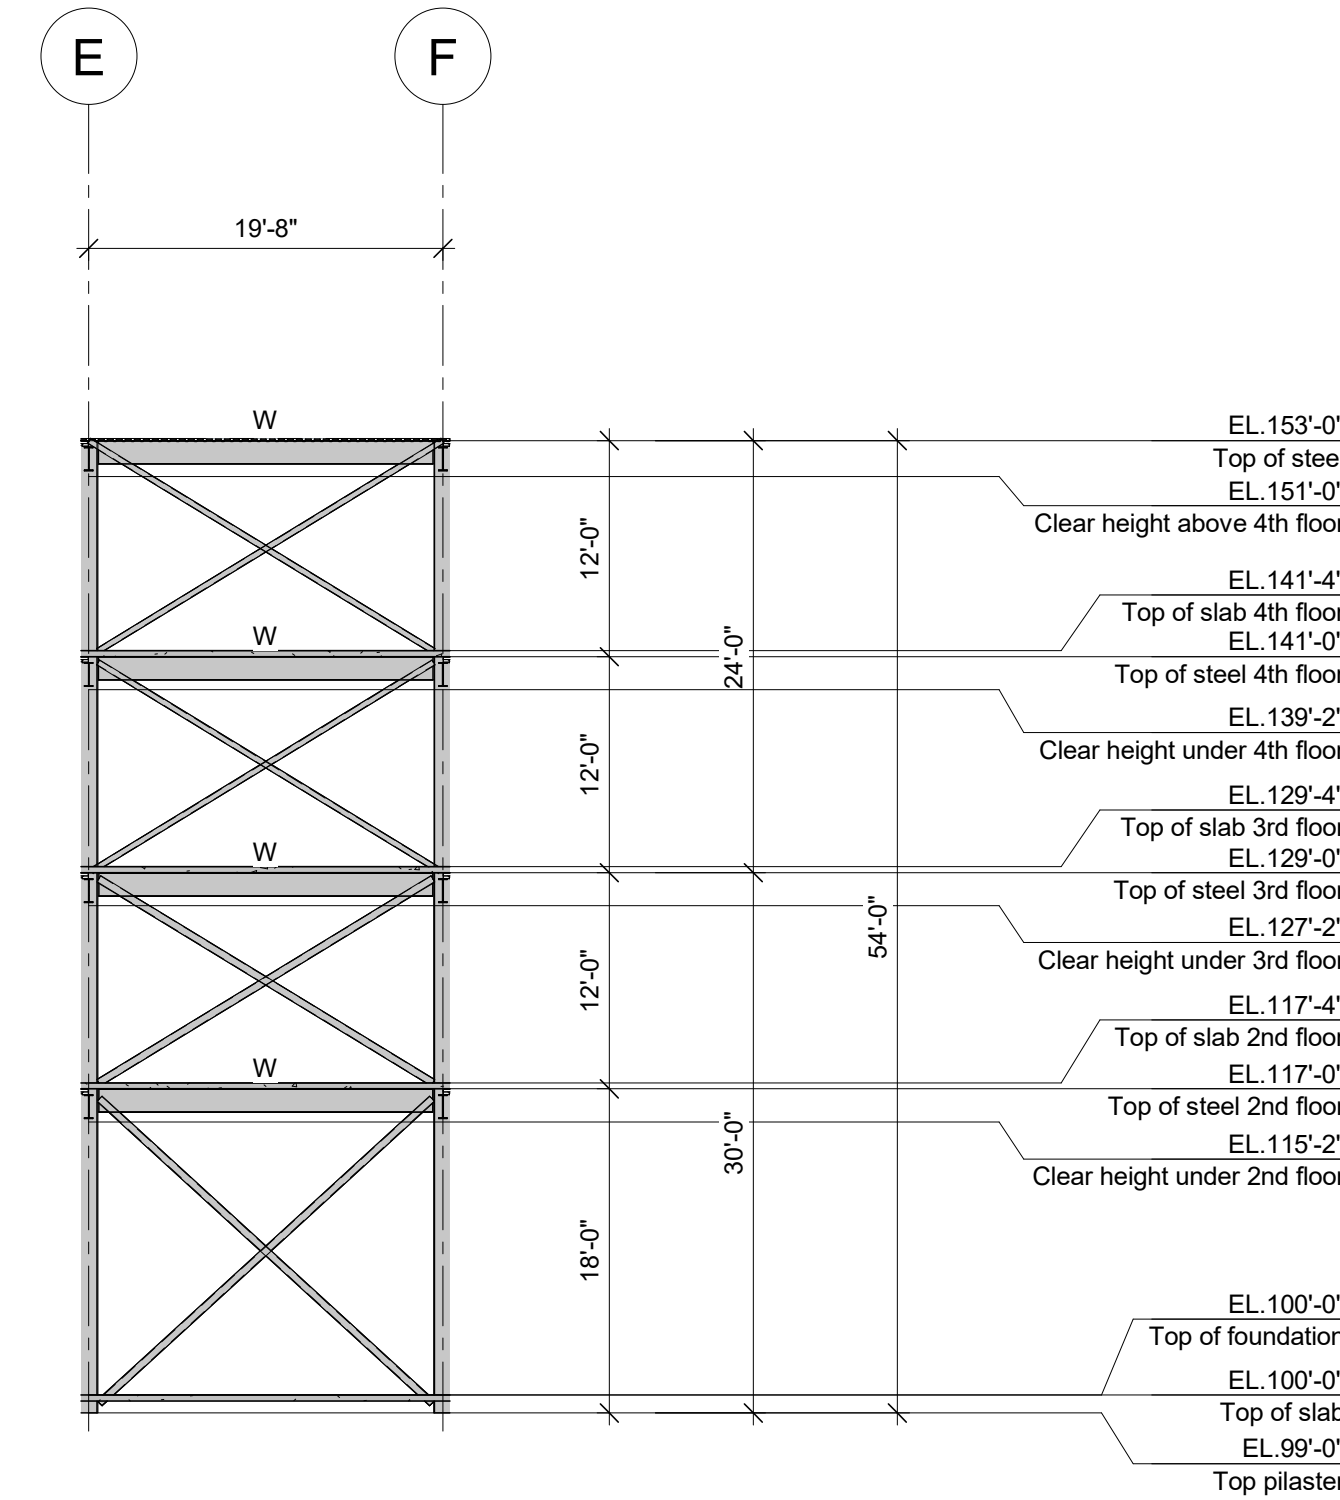


2 BRACING SECTION LINE 5 (WEST)
3/32" = 1'-0"

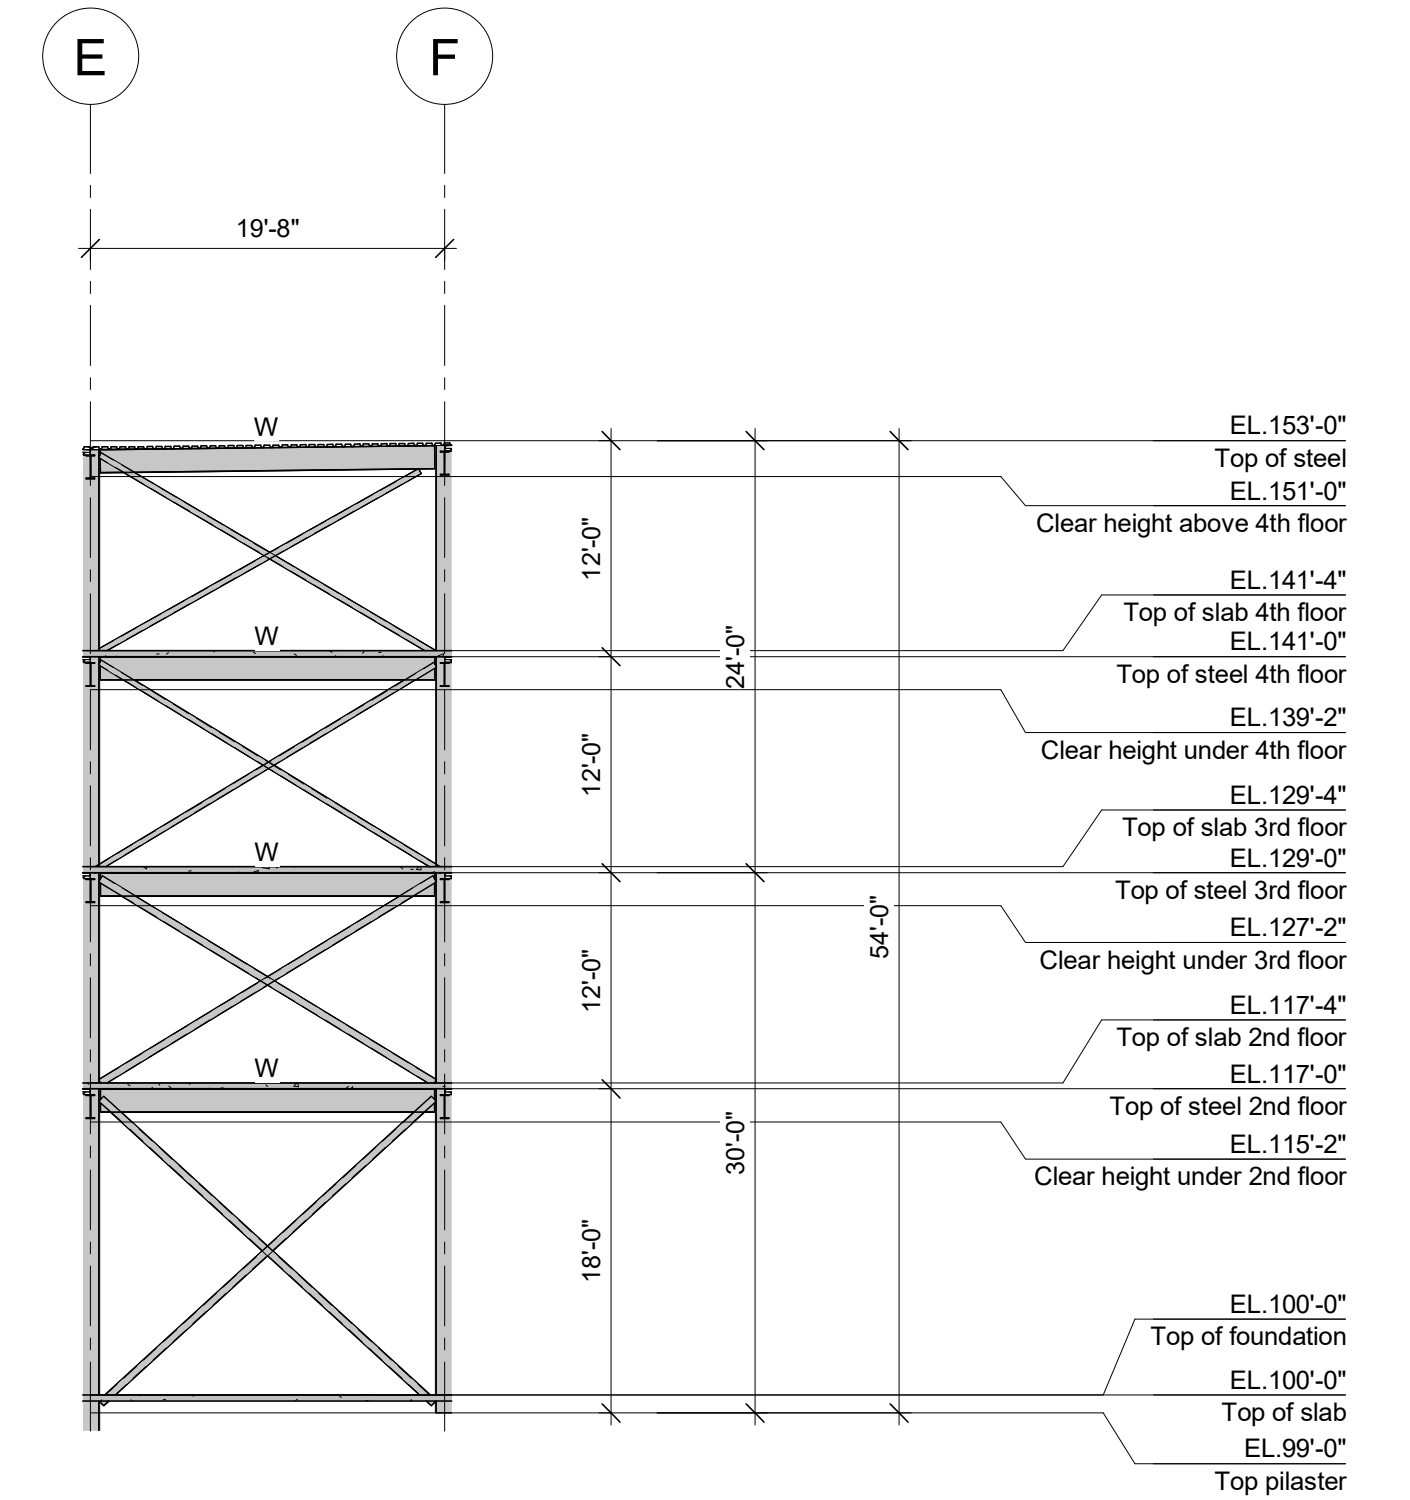


3 BRACING SECTION LINE 7 (WEST)
3/32" = 1'-0"

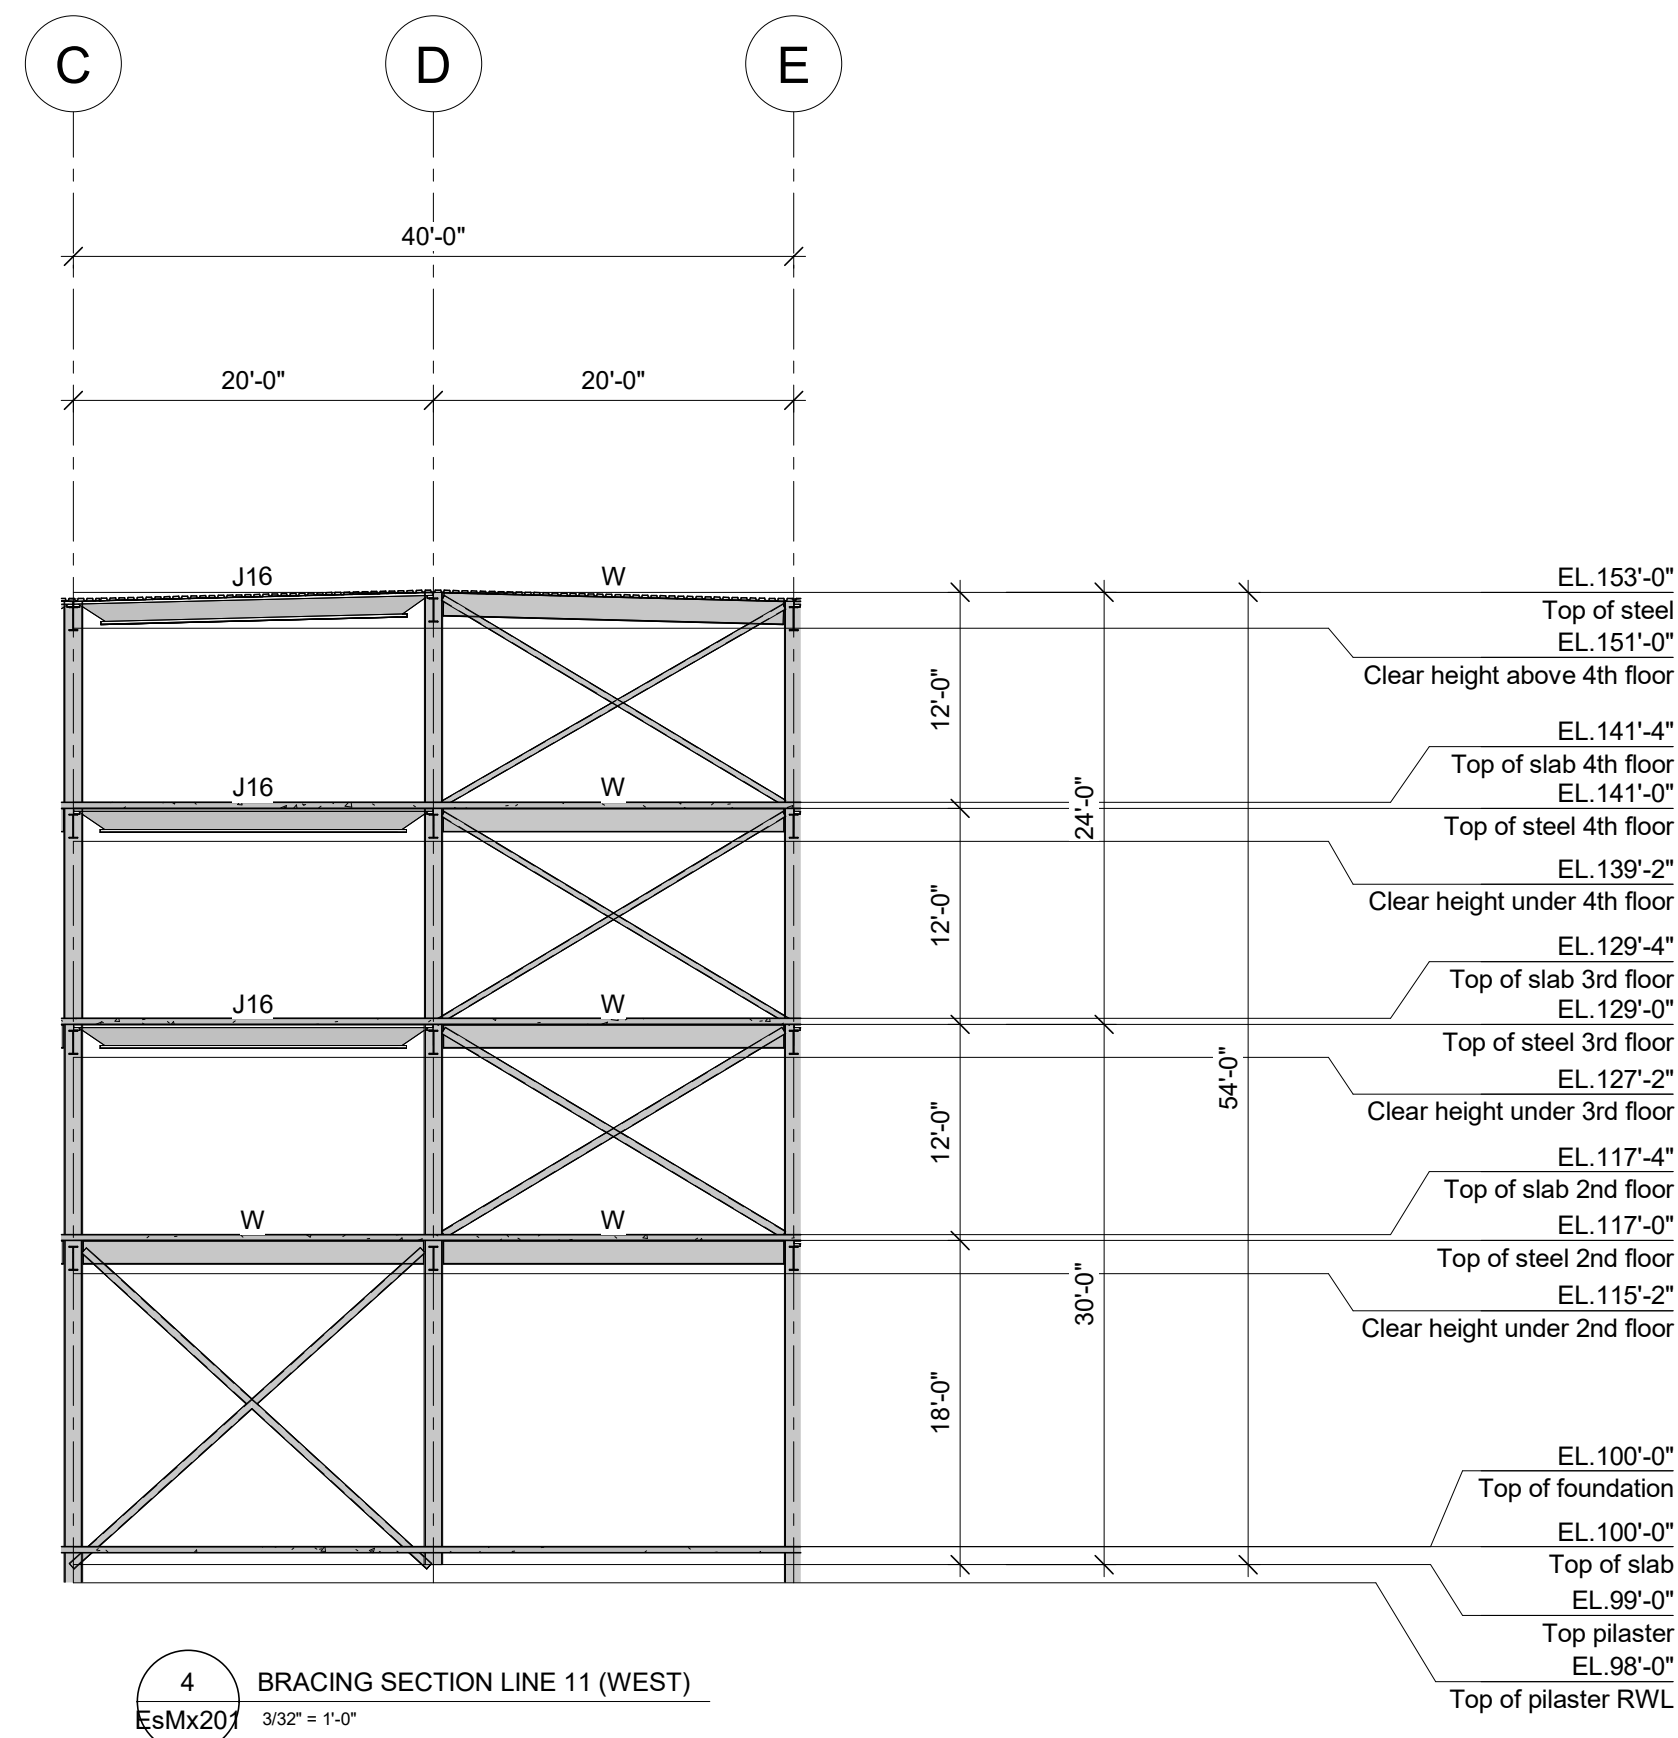


4 BRACING SECTION LINE 11 (WEST)
3/32" = 1'-0"

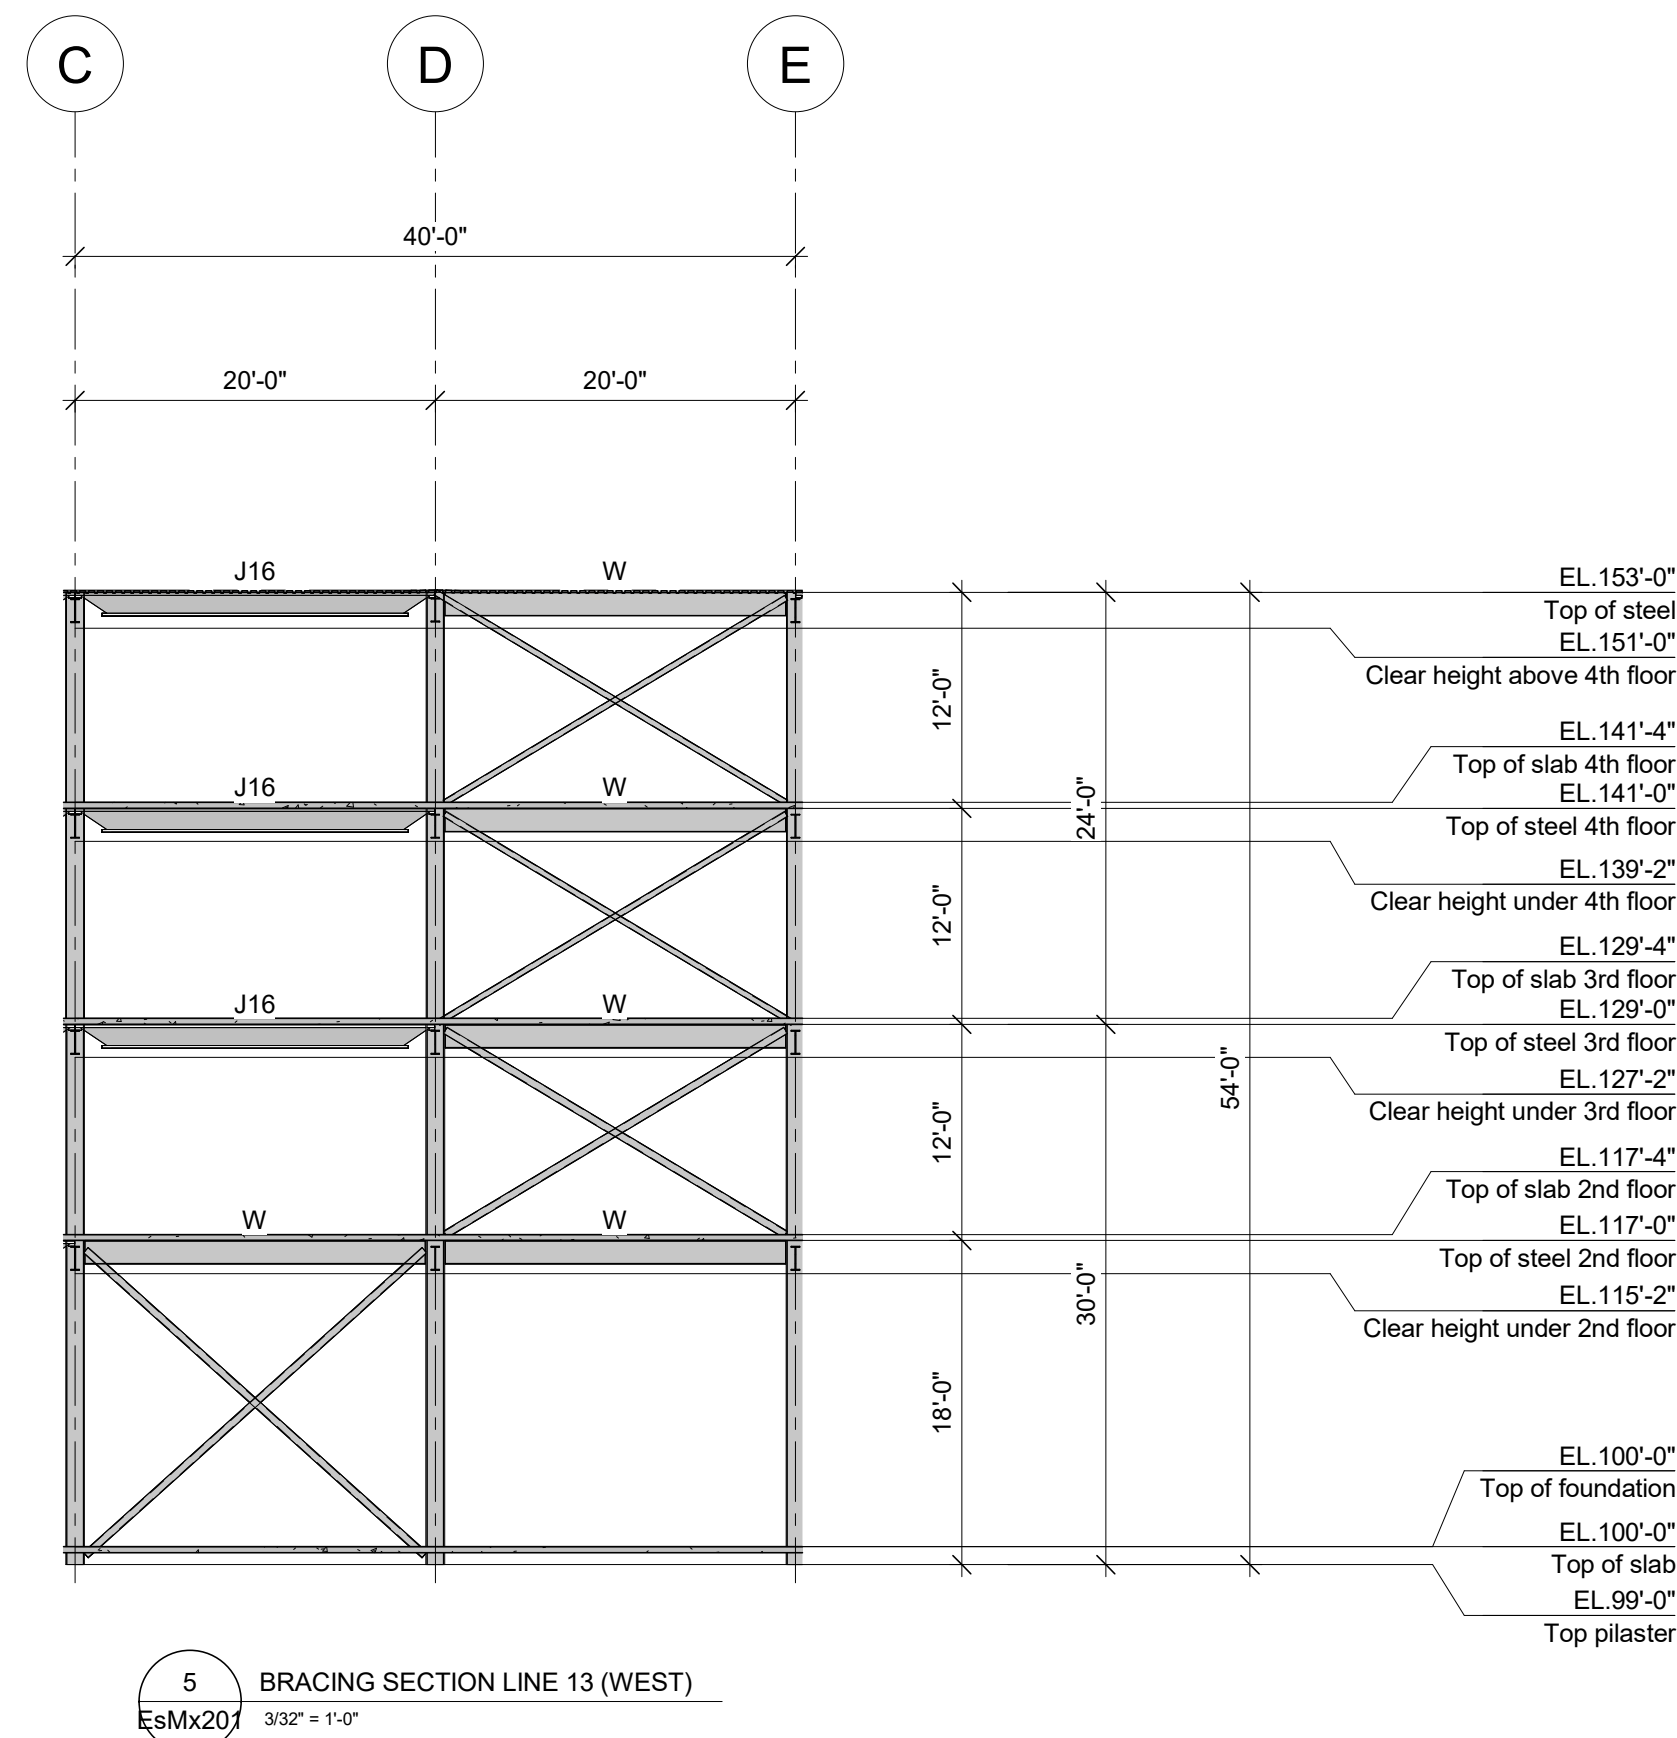

5 BRACING SECTION LINE 13 (WEST)
3/32" = 1'-0"

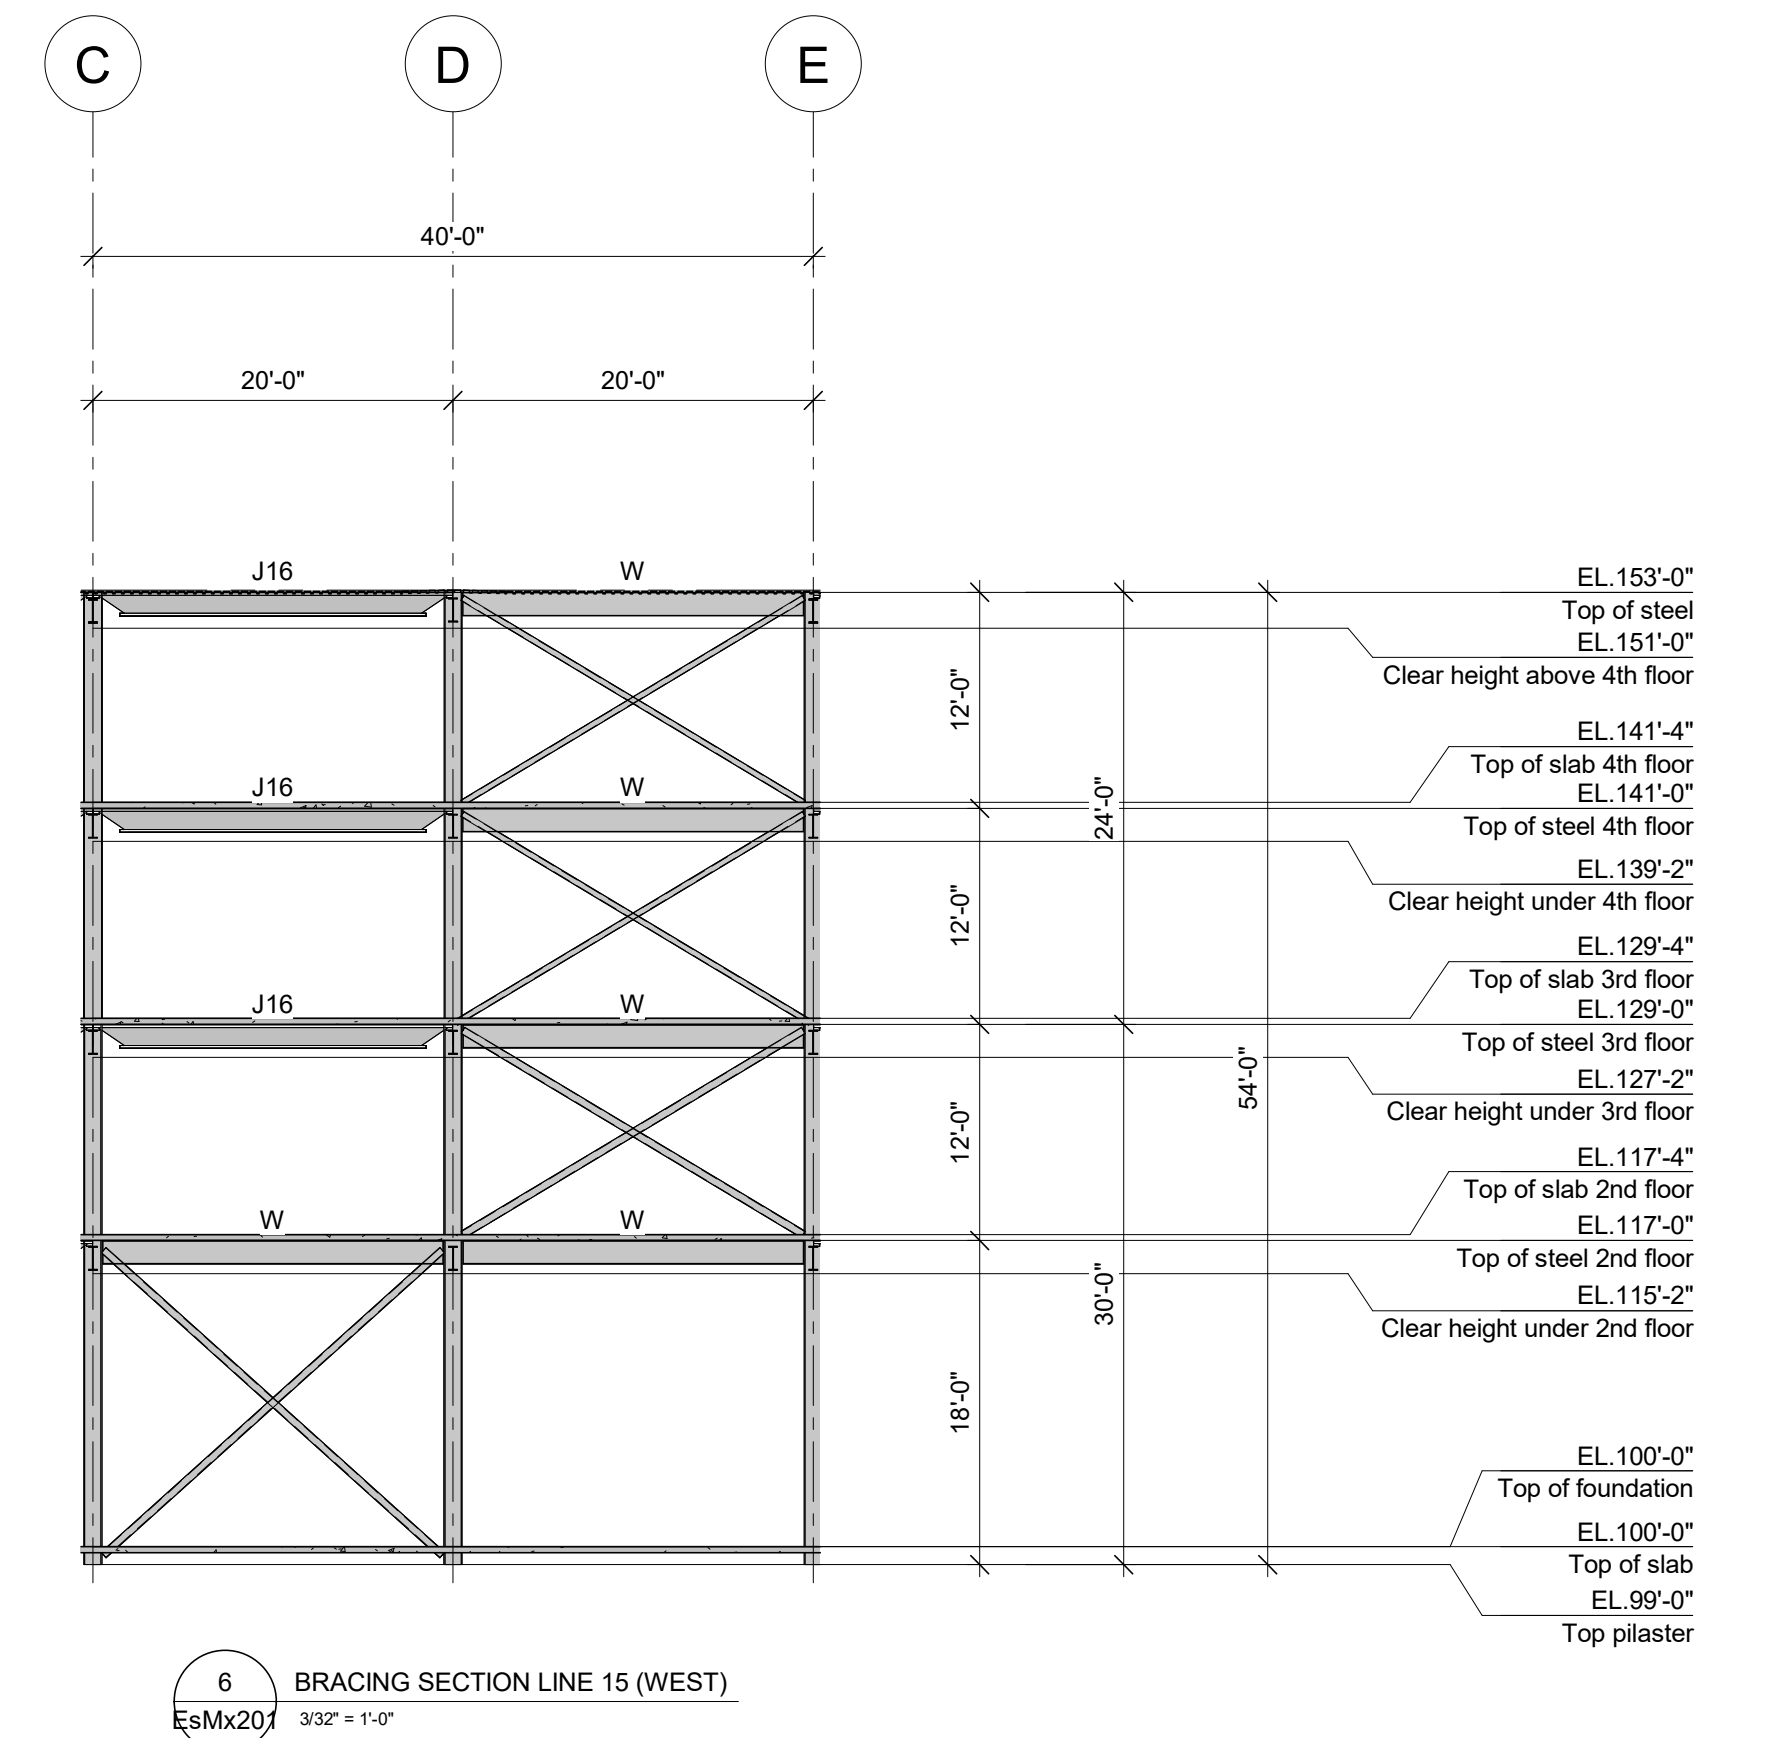

6 BRACING SECTION LINE 15 (WEST)
3/32" = 1'-0"

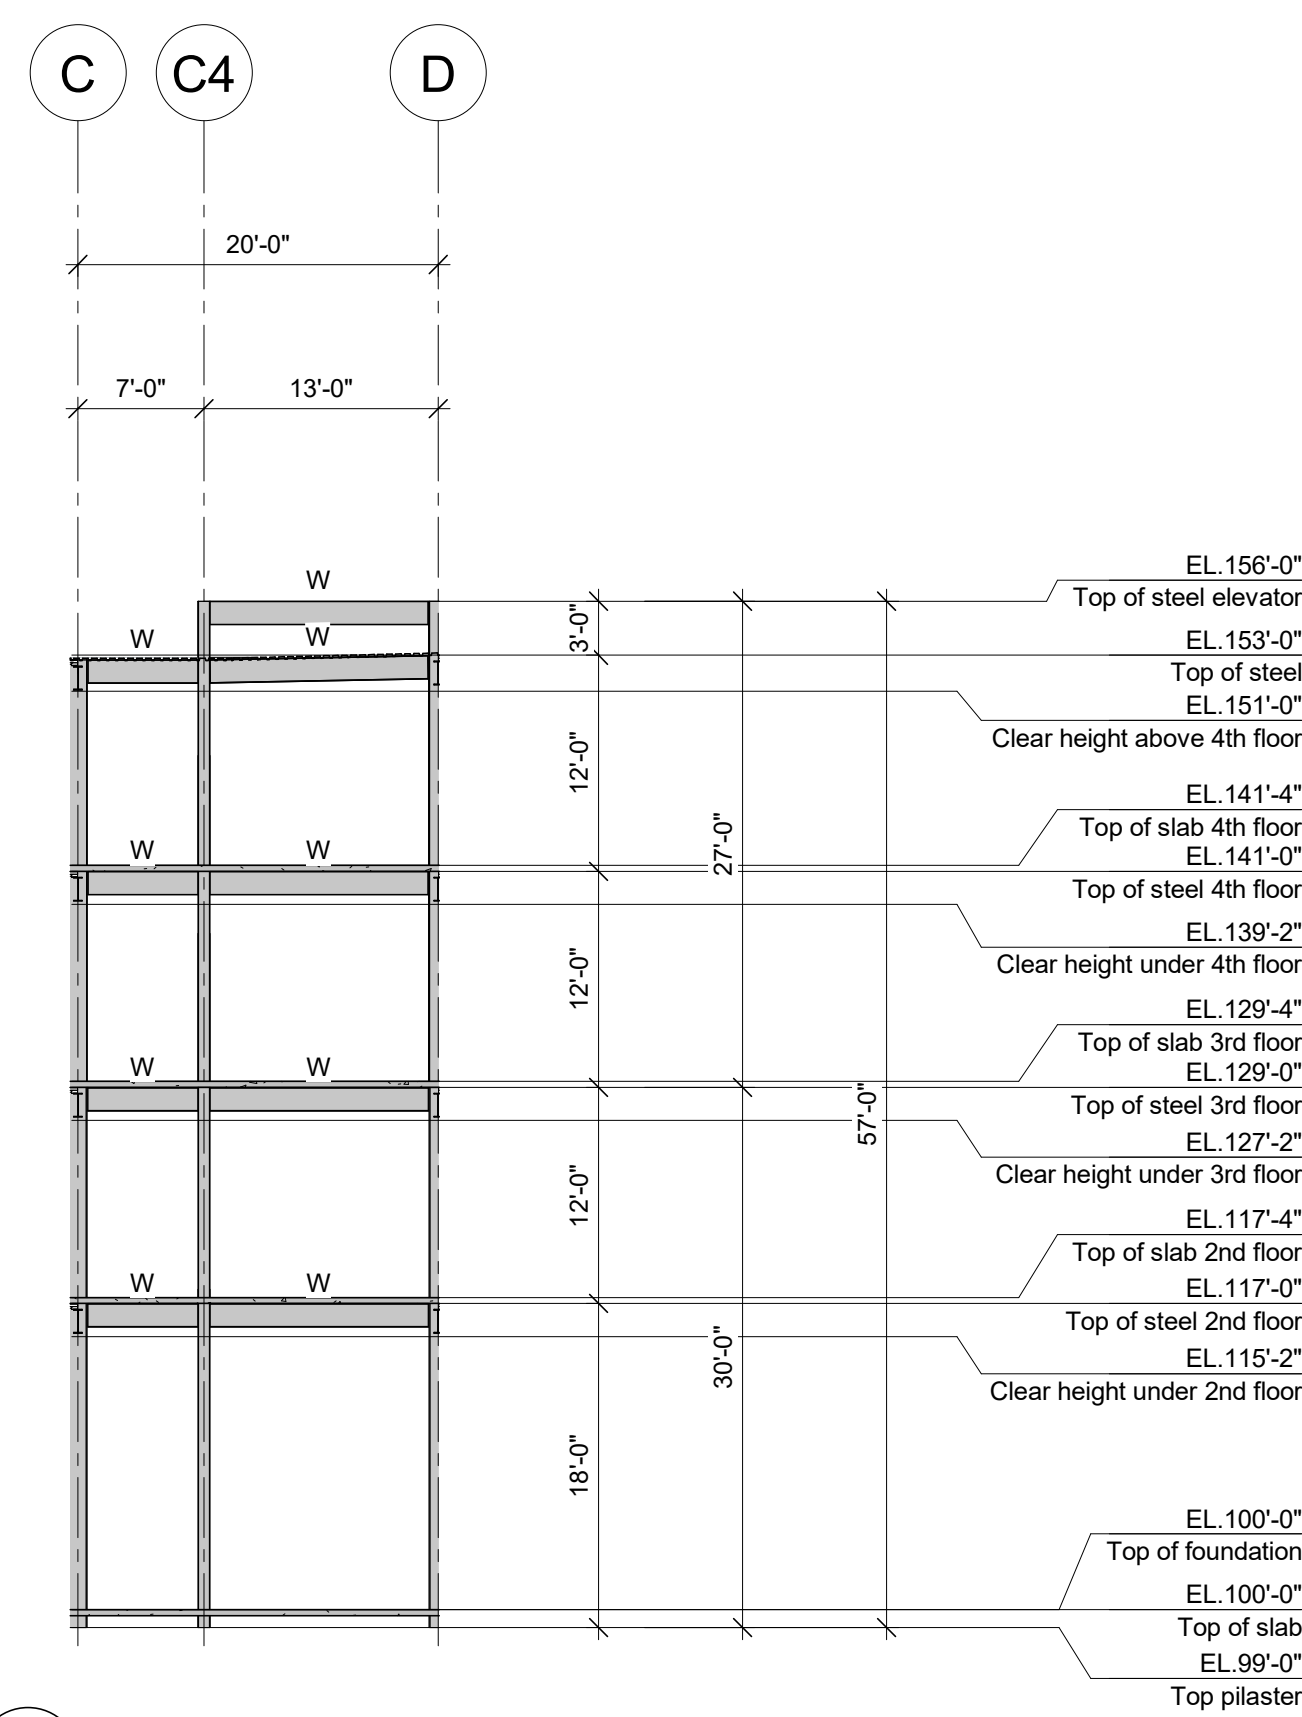

7 ELEVATOR SECTION LINE 8 (WEST)
3/32" = 1'-0"