


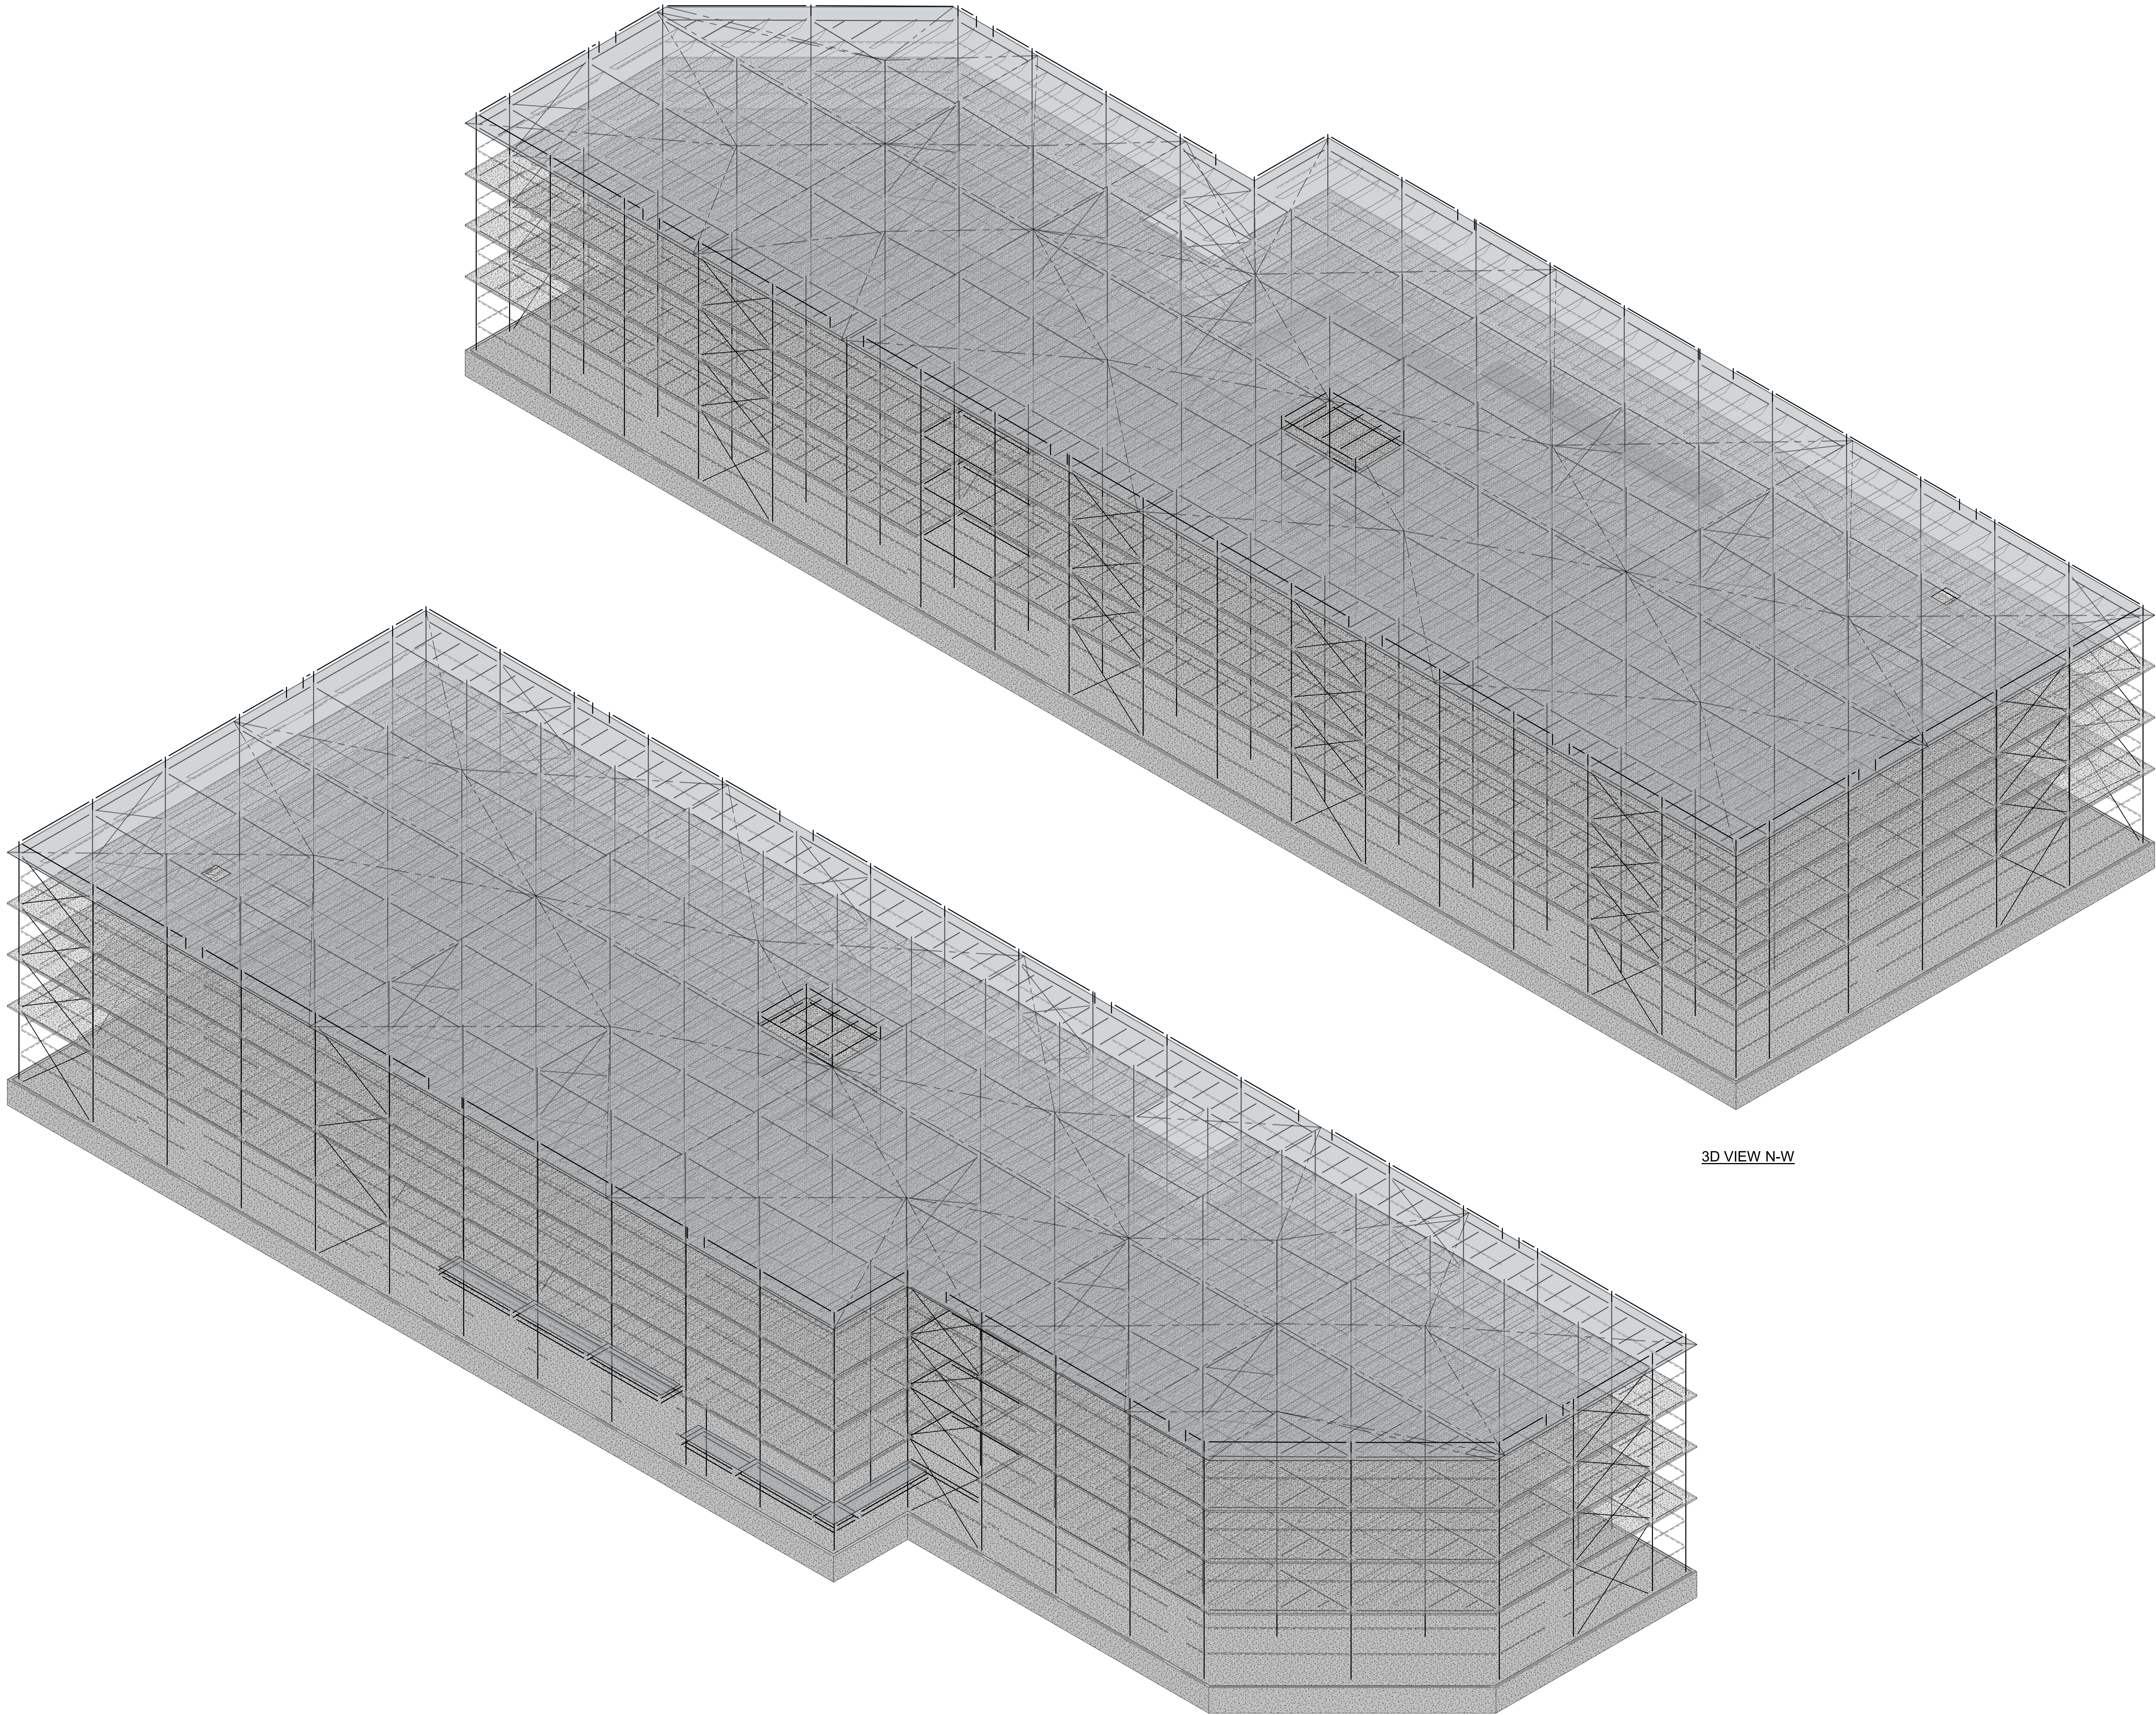

3D VIEW N-W

3D VIEW S-E

CONTRACTOR/RECTOR NOTE:
IT IS PROHIBITED TO MODIFY, COPY, REPRODUCE OR OTHERWISE
DISTRIBUTE THIS DRAWING OR ANY REPRESENTATION OF THIS
DRAWING, OR ANY MEDIA, INCLUDING ELECTRONIC, WITHOUT THE
PRIOR WRITTEN APPROVAL OF CANAM GROUP INC.

PRELIMINARY SHEET LIST	
EaMx001	PRELIMINARY SKETCH - 3D VIEWS
EaMx001	PRELIMINARY SKETCH - 2ND FLOOR AND CANOPIES PLAN
EaMx002	PRELIMINARY SKETCH - 3RD & 4TH FLOOR PLAN
EaMx001	PRELIMINARY SKETCH - ROOF PLAN
EaMx001	PRELIMINARY SKETCH - ELEVATIONS
EaMx002	PRELIMINARY SKETCH - ELEVATIONS & SECTIONS


[Click here for 3D model](#)

PRELIMINARY

NOT TO BE USED FOR CONSTRUCTION

REVISION	DATE	DESCRIPTION	ISSUE	VER
PROJECT MANAGER				
-				
-				
-				
-				
DRAFTING				
DRAWN	DESIGNED	PROJECT ENGINEER	SCALE:	
J.P.				
CHECKED	CONSULTING ENGINEERS - ARCHITECTS		DATE (yyyy/mm/dd)	
			2026/02/025	

CUSTOMER: Pretium Projects Ltd

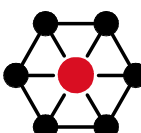

CANAM

11505, 1re Avenue, bureau 500, Saint-Georges Beauce
Châteauguay, Québec, G5Y 7G3
Phone : (418) 228-8031
Toll free : (877) 499-6049
www.canam.com

PROFESSIONAL SEAL

PROJECT

SmartStop Self Storage - Building 1
Edmonton, Alberta


DRAWING TITLE

PRELIMINARY SKETCH - 3D VIEWS


Initials

CONTRACT NUMBER	DRAWING NUMBER	DIVISION	REVISION
P2026-045	EaMx001		




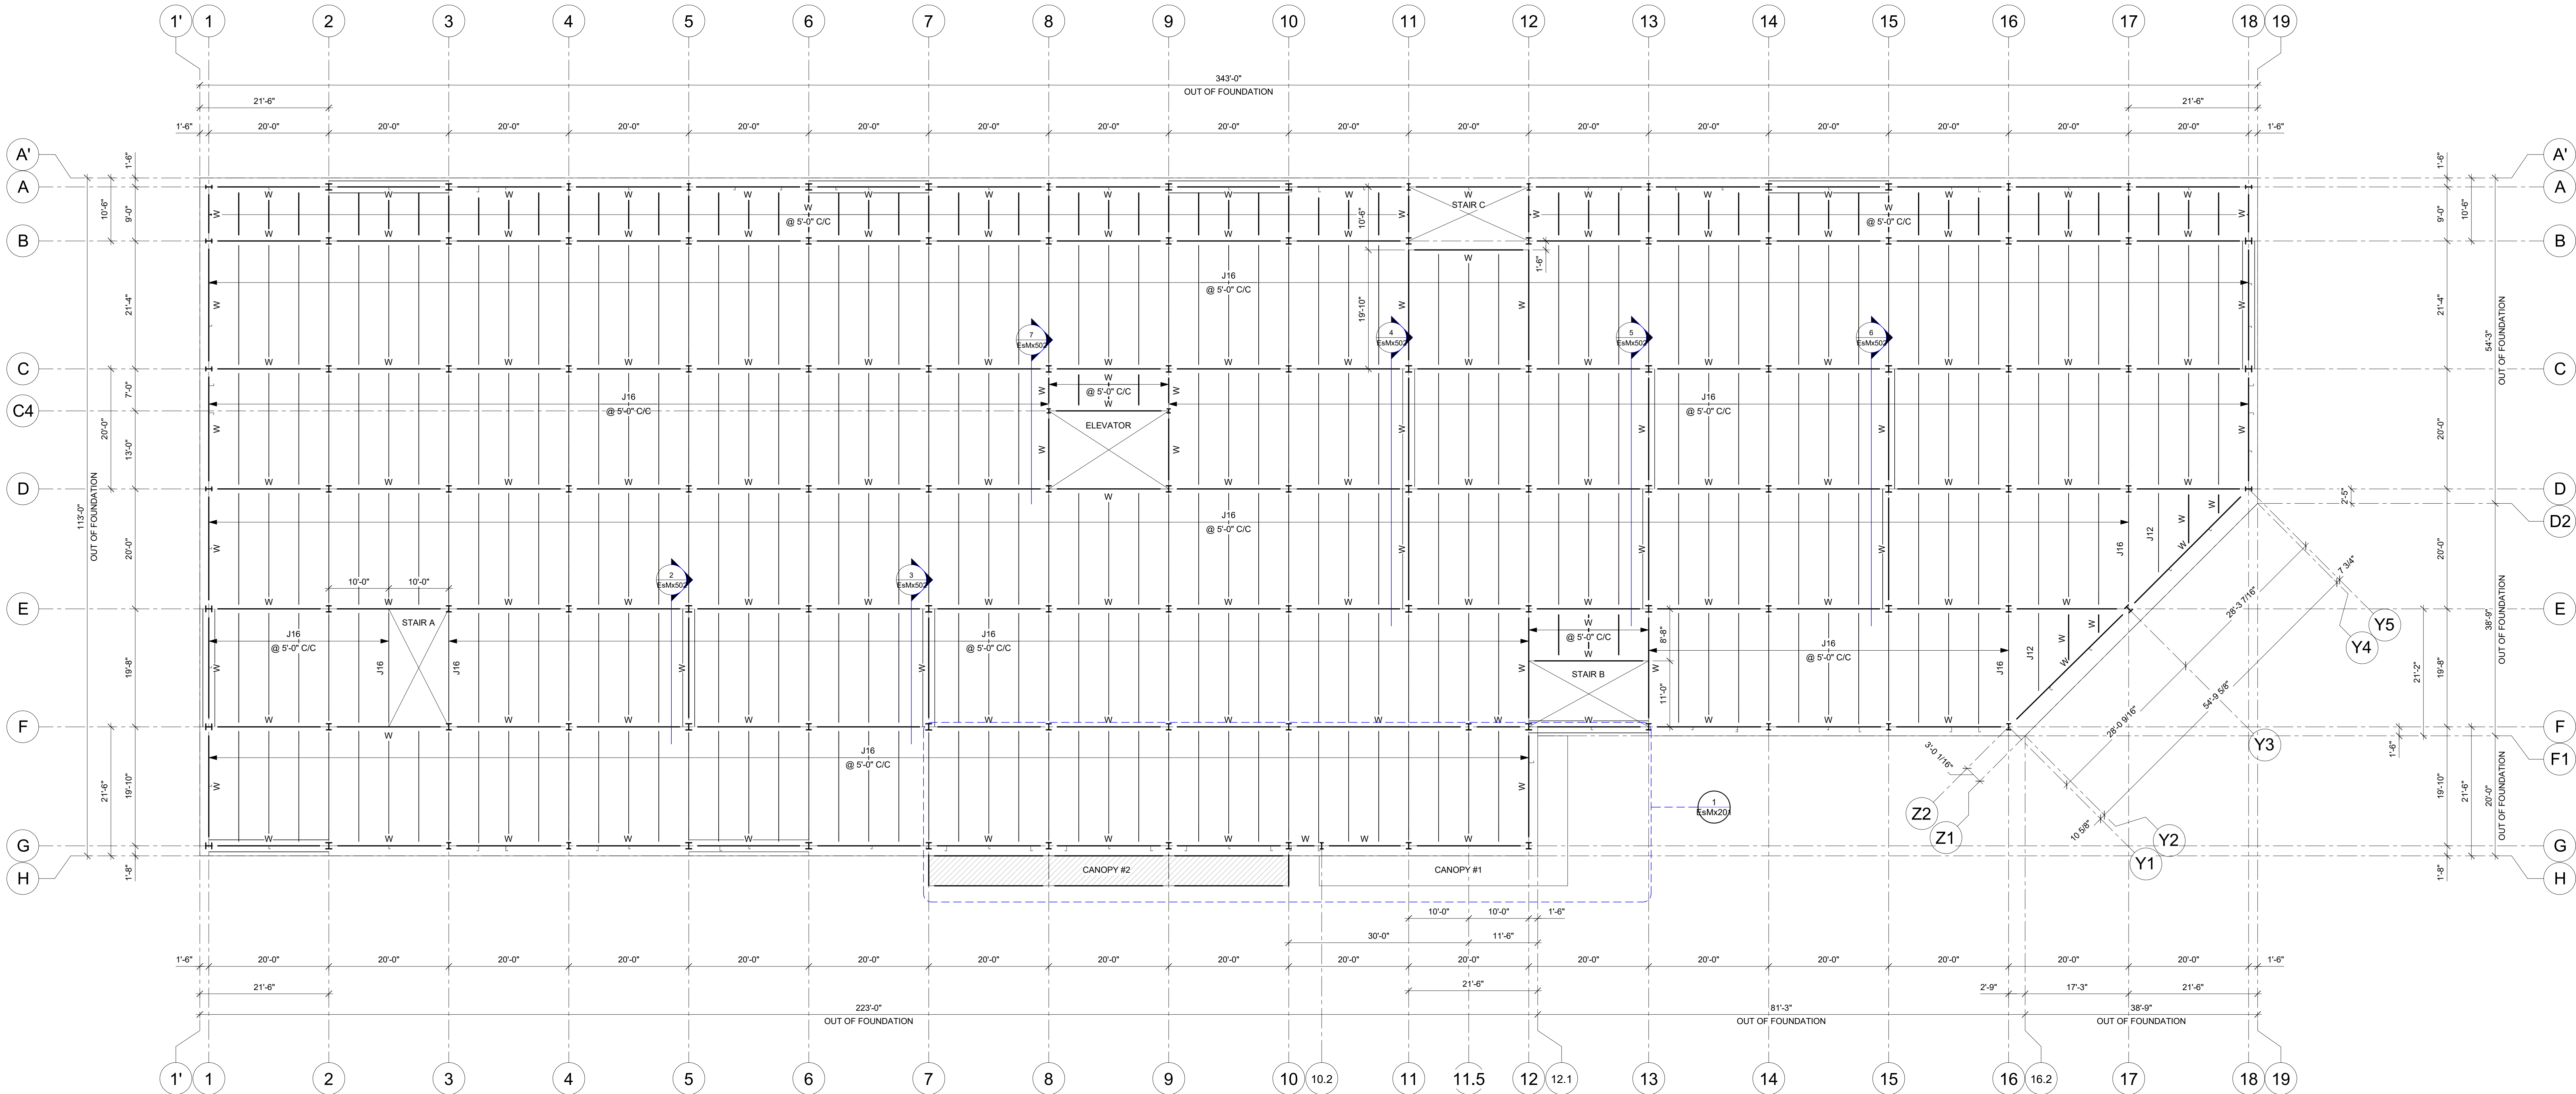

2ND FLOOR PLAN
3/32" = 1'-0"

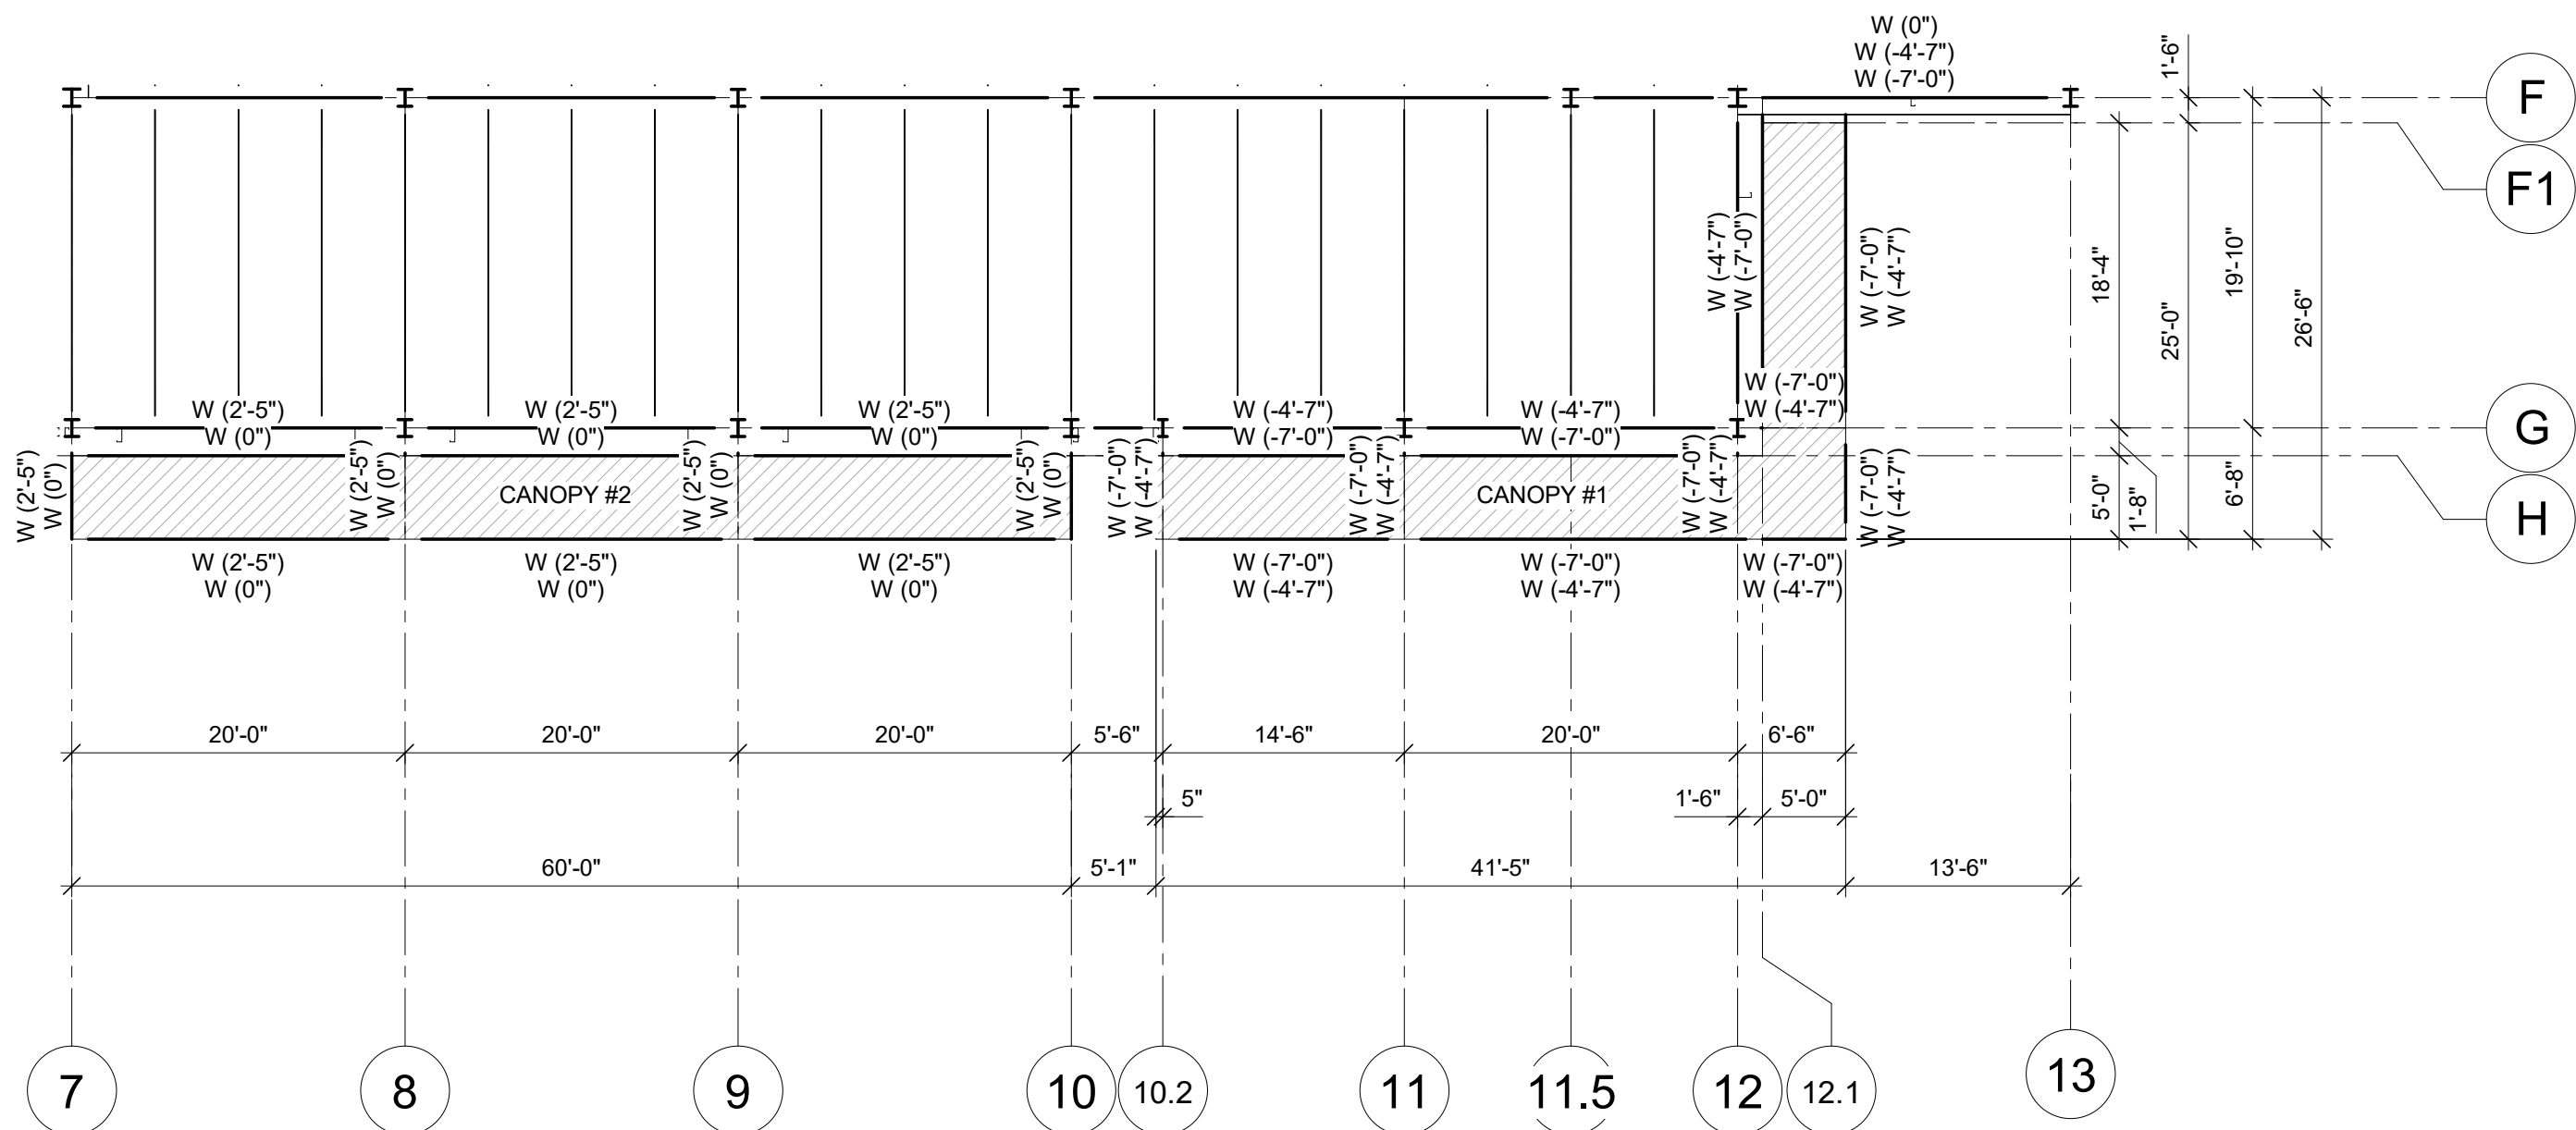

1 CANOPIES PLAN
3/32" = 1'-0"

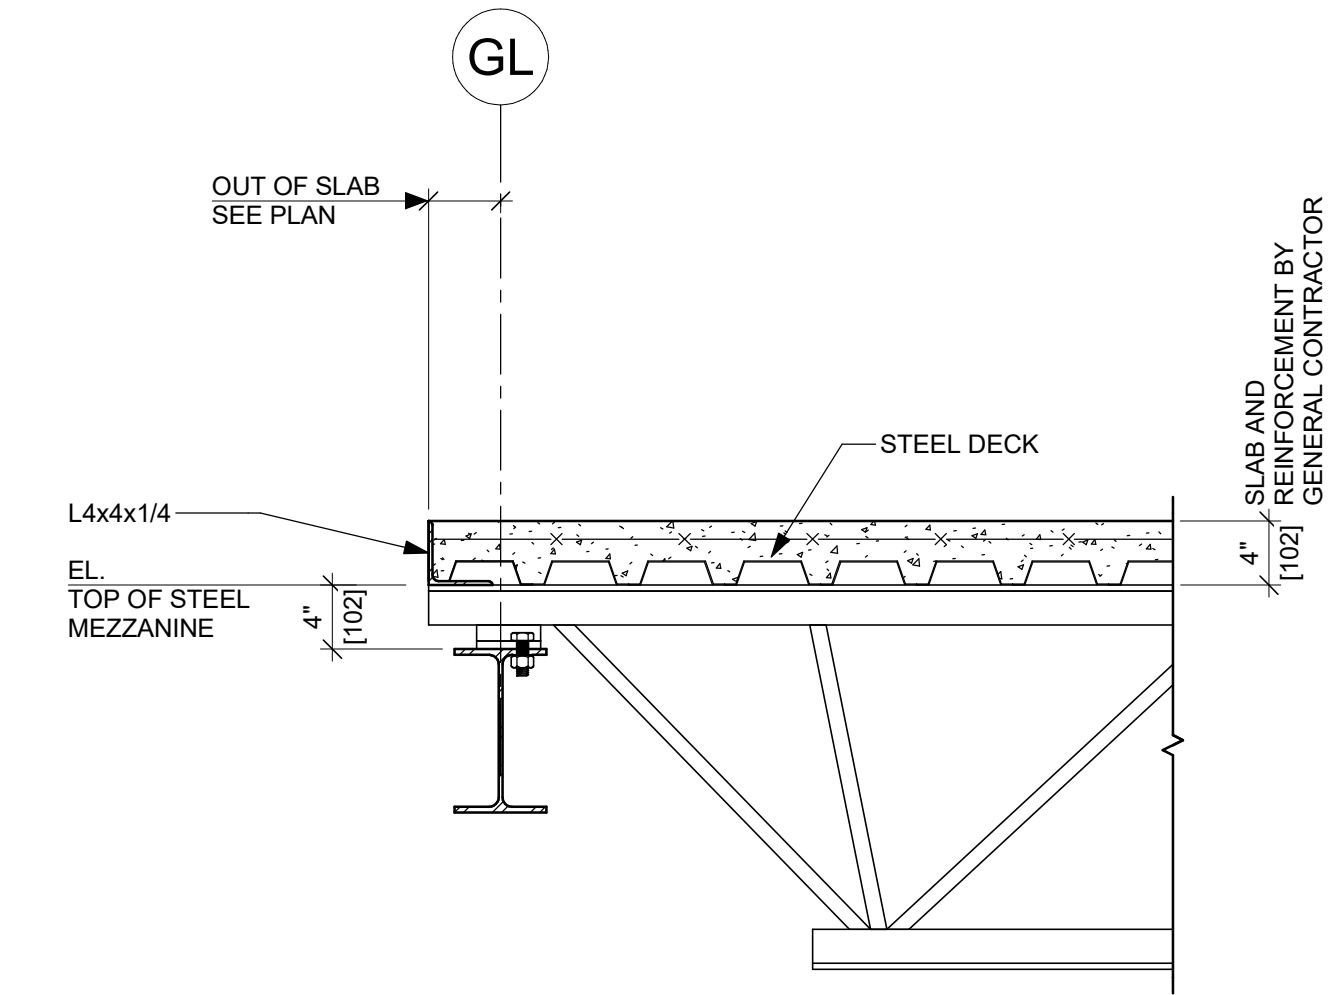

PRELIMINARY SLAB DESIGN
1" = 1'-0"

GENERAL NOTES FOR CONCRETE SLAB ON STEEL DECK (BY OTHERS)

1. USE NORMAL WEIGHT CONCRETE WITH A MINIMUM COMPRESSIVE RESISTANCE (FCI) OF 3600 PSI AT 28 DAYS.
2. MINIMUM REQUIRED WIRE MESH: 1 ROW OF 6X6 6/6 (TYP. U.S.) BETWEEN 3/4" AND 1 1/2".
3. MINIMUM CONCRETE COVER OVER WIRE MESH SHOULD BE BETWEEN 3/4" AND 1 1/2".
4. CONCRETE HUMID CURE: 7 DAYS MINIMUM FOR NON-EXPOSED CONCRETE. (EXAMPLE: POLISHED CONCRETE).

CONTRACTOR/RECTOR NOTE:
IT IS PROHIBITED TO MODIFY, COPY, REPRODUCE OR OTHERWISE DISTRIBUTE THIS DRAWING OR ANY REPRESENTATION OF THIS DRAWING, OR ANY MEDIA, INCLUDING ELECTRONIC, WITHOUT THE PRIOR WRITTEN APPROVAL OF CANAM GROUP INC.

2ND FLOOR

CLEAR HEIGHT UNDER 2ND FLOOR : 15'-2"
TOP OF STEEL 2ND FLOOR : 11'-0"
CLEAR HEIGHT ABOVE 2ND FLOOR : 9'-10"

3RD FLOOR

CLEAR HEIGHT UNDER 3RD FLOOR : 9'-10"
TOP OF STEEL 3RD FLOOR : 12'-0"
CLEAR HEIGHT ABOVE 3RD FLOOR : 9'-10"

4TH FLOOR

CLEAR HEIGHT UNDER 4TH FLOOR : 9'-10"
TOP OF STEEL 4TH FLOOR : 14'-0"
CLEAR HEIGHT ABOVE 4TH FLOOR AT RWL : 9'-8"

LOADS

D.L. : 70 psf
L.L. : 100 psf (Storage)
Δ L/360

PRELIMINARY

NOT TO BE USED FOR CONSTRUCTION

REVISION DATE DESCRIPTION DESI VER

PROJECT MANAGER

DESIGNED PROJECT ENGINEER SCALE

CHECKED CONSULTING ENGINEERS ARCHITECTS DATE (YYYYMMDD)

CUSTOMER: Pretium Projects Ltd

DRAWING TITLE

CONTRACT NUMBER DRAWING NUMBER DIVISION REVISION

PROJECT

SmartStop Self Storage - Building 1

Edmonton, Alberta

PRELIMINARY SKETCH - 2ND FLOOR AND CANOPIES PLAN

Initials

CONTRACT NUMBER DRAWING NUMBER DIVISION REVISION

P2026-045 EsMx201

REVISION

1

2

3

4

5

6

7

8

9

10

11

12

13

14

15

16

17

18

19

20

21


22

23

24

25

26

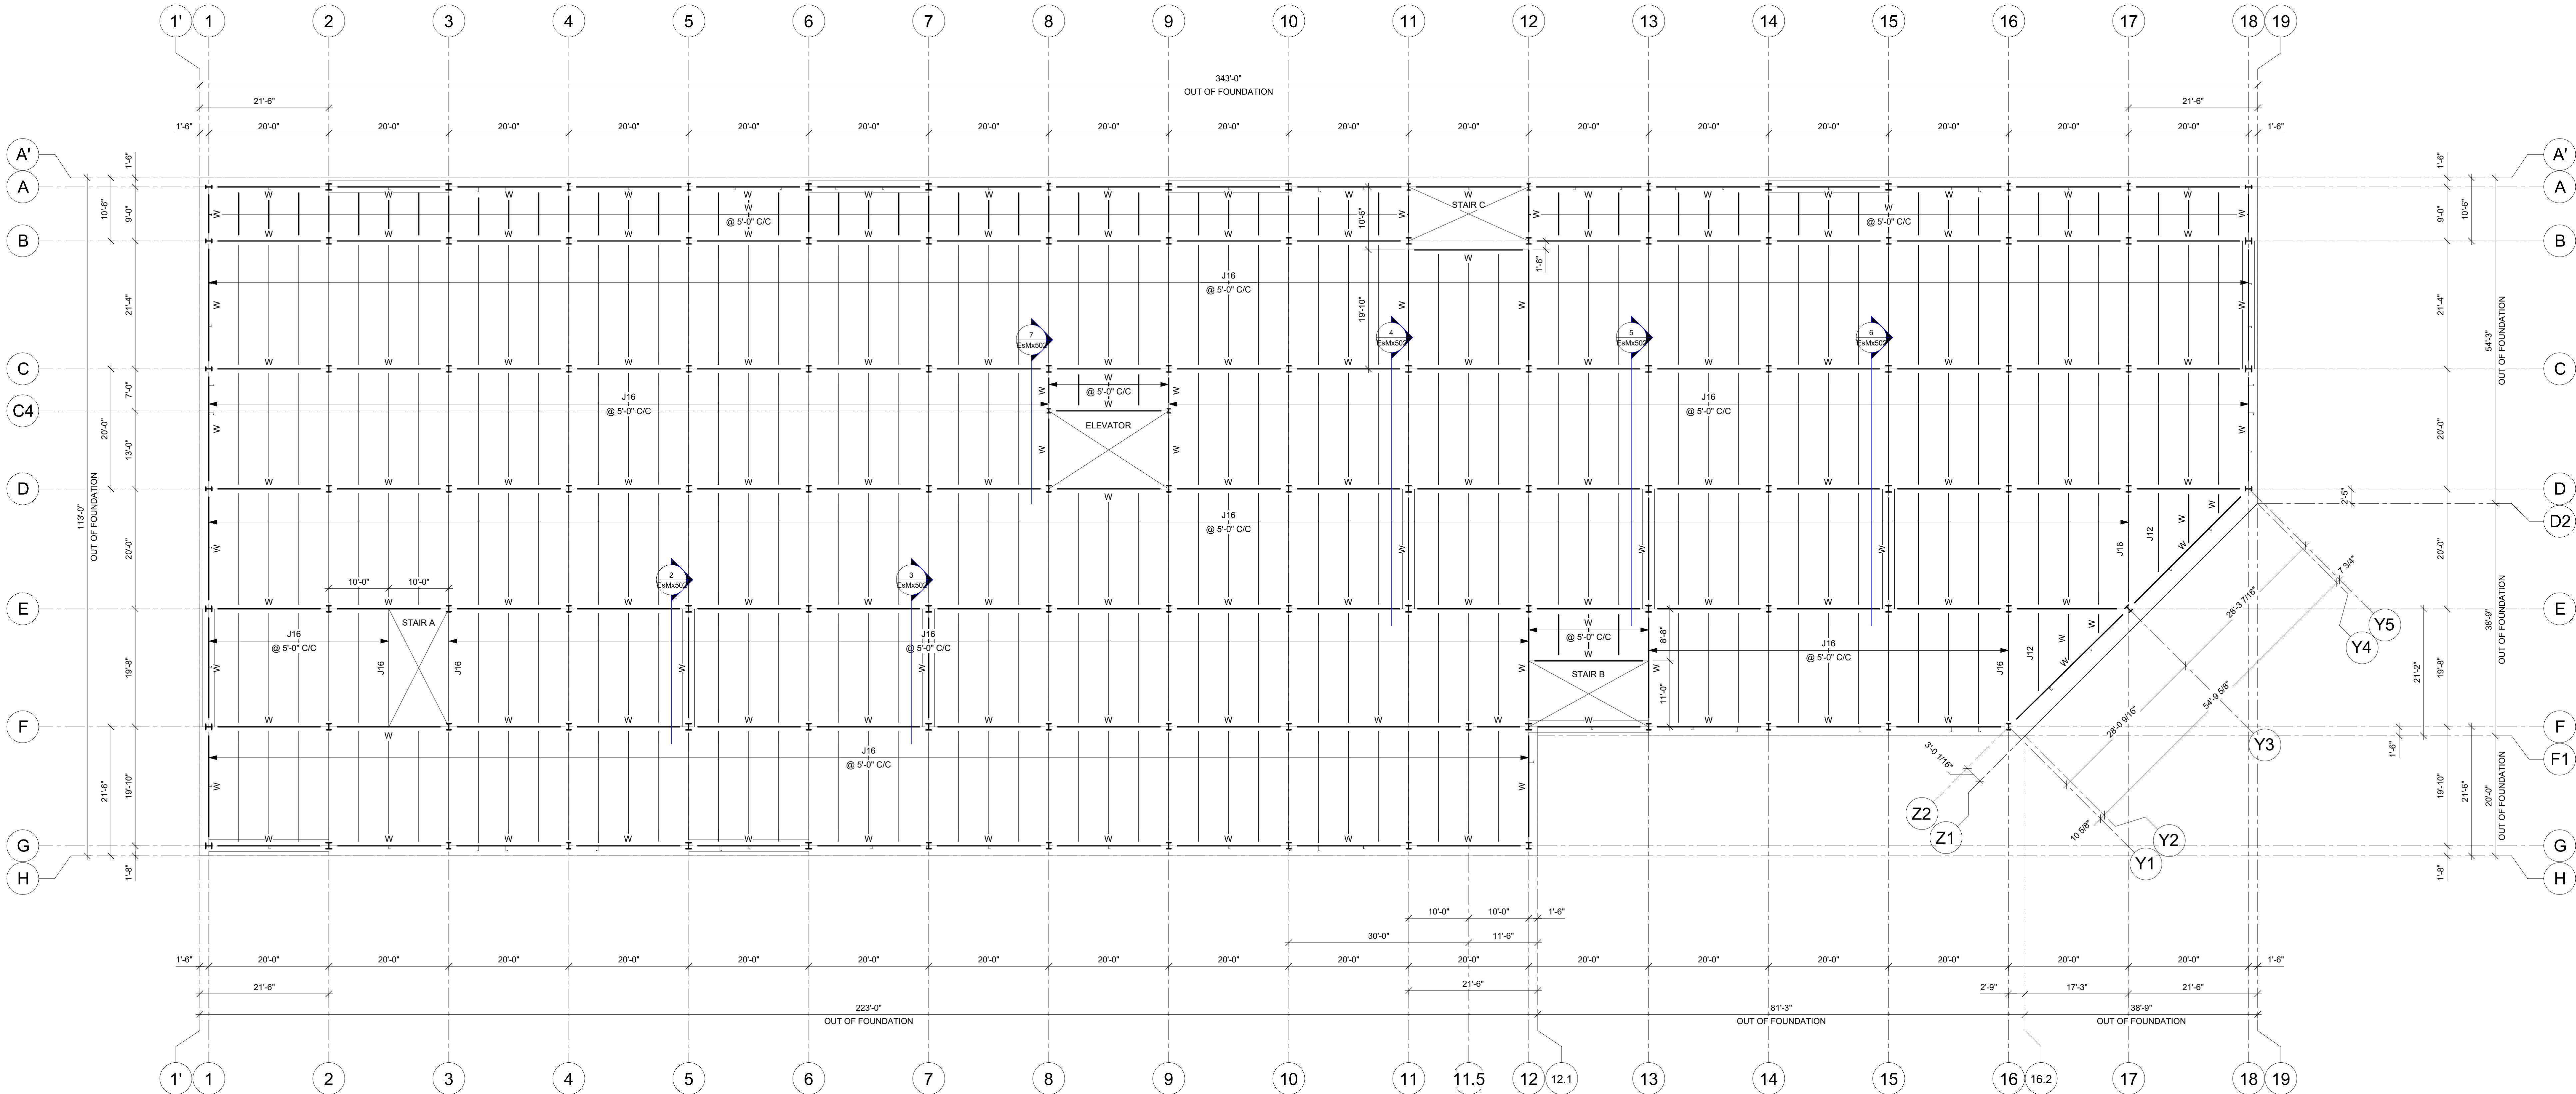

3RD & 4TH FLOOR PLAN
3/32" = 1'-0"

CONTRACTOR/RECTOR NOTE:
IT IS PROHIBITED TO MODIFY, COPY, REPRODUCE OR OTHERWISE
DISTRIBUTE THIS DRAWING OR ANY REPRESENTATION OF THIS
DRAWING, OR ANY MEDIA, INCLUDING ELECTRONIC, WITHOUT THE
PRIOR WRITTEN APPROVAL OF CANAM GROUP INC.

2ND FLOOR

CLEAR HEIGHT UNDER 2ND FLOOR : 15'-2"
TOP OF STEEL 2ND FLOOR : 117'-0"
CLEAR HEIGHT ABOVE 2ND FLOOR : 9'-10"

3RD FLOOR

CLEAR HEIGHT UNDER 3RD FLOOR : 9'-10"
TOP OF STEEL 3RD FLOOR : 129'-0"
CLEAR HEIGHT ABOVE 3RD FLOOR : 9'-10"

4TH FLOOR

CLEAR HEIGHT UNDER 4TH FLOOR : 9'-10"
TOP OF STEEL 4TH FLOOR : 141'-0"
CLEAR HEIGHT ABOVE 4TH FLOOR AT RWL : 9'-8"

LOADS

D.L. : 70 psf
L.L. : 100 psf (Storage)
Δ L/360

PRELIMINARY

NOT TO BE USED FOR CONSTRUCTION

REVISION	DATE	DESCRIPTION	ISS	VER
PROJECT MANAGER				
DRAFTING				
DRAWN	J.P.	DESIGNED	PROJECT ENGINEER	SCALE: 3/32" = 1'-0"
CHECKED		CONSULTING ENGINEERS ARCHITECTS	DATE (yyyy/mm/dd)	2026/02/05

CUSTOMER: Pretium Projects Ltd



PROFESSIONAL SEAL




PROJECT

SmartStop Self Storage - Building 1
Edmonton, Alberta

DRAWING TITLE

PRELIMINARY SKETCH - 3RD & 4TH
FLOOR PLAN

CONTRACT NUMBER	DRAWING NUMBER	DIVISION	REVISION
P2026-045	EsMx202		

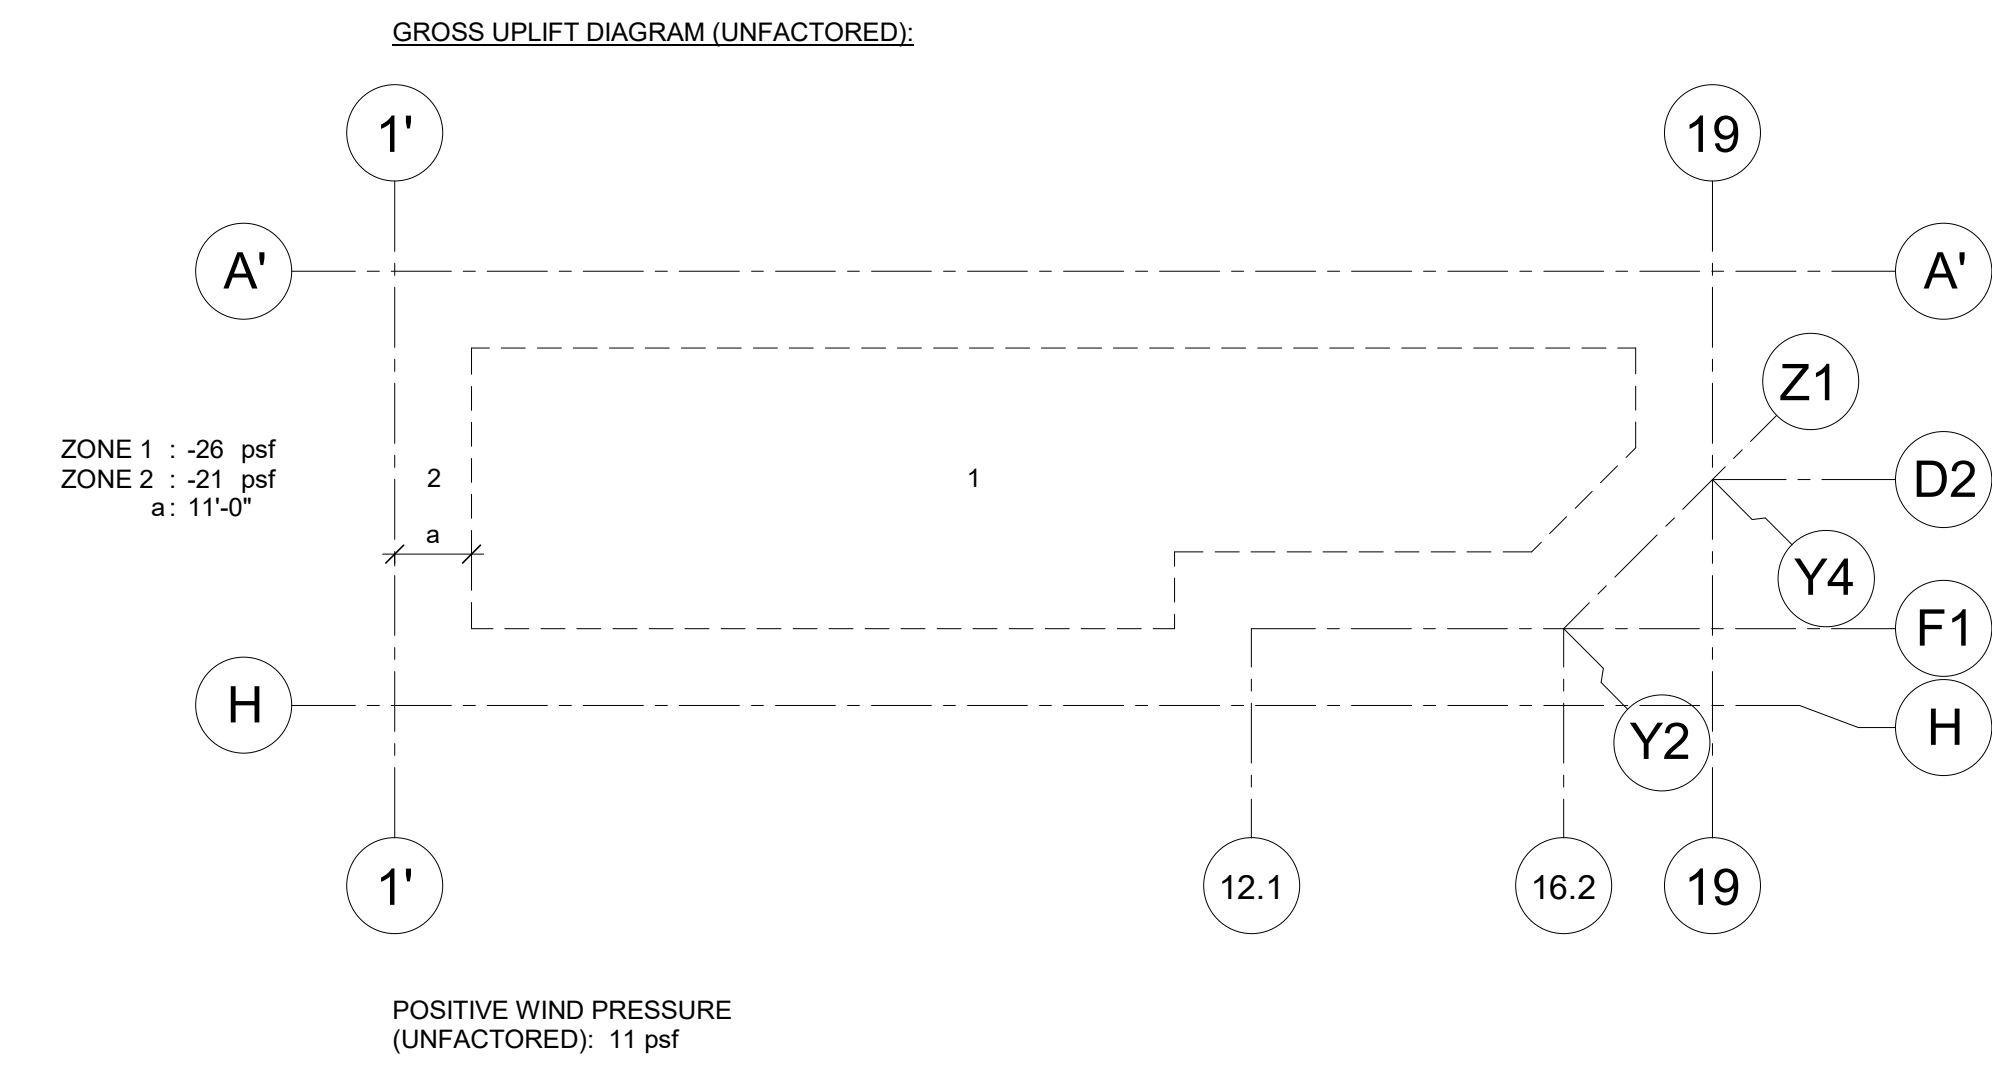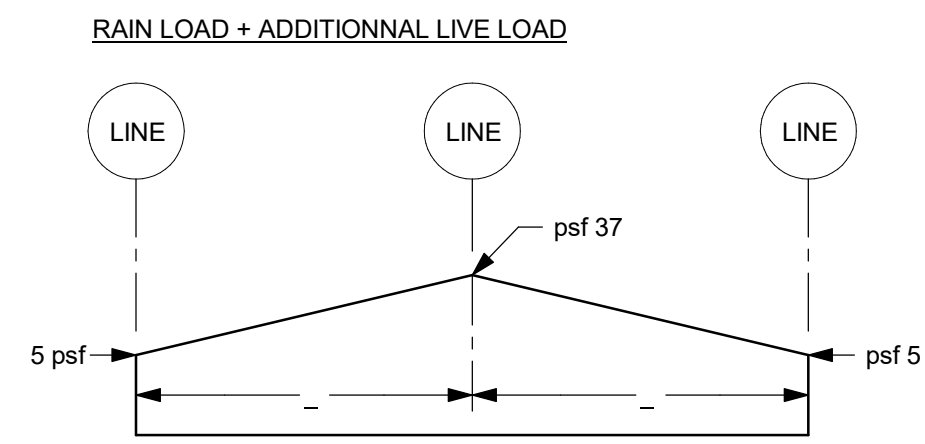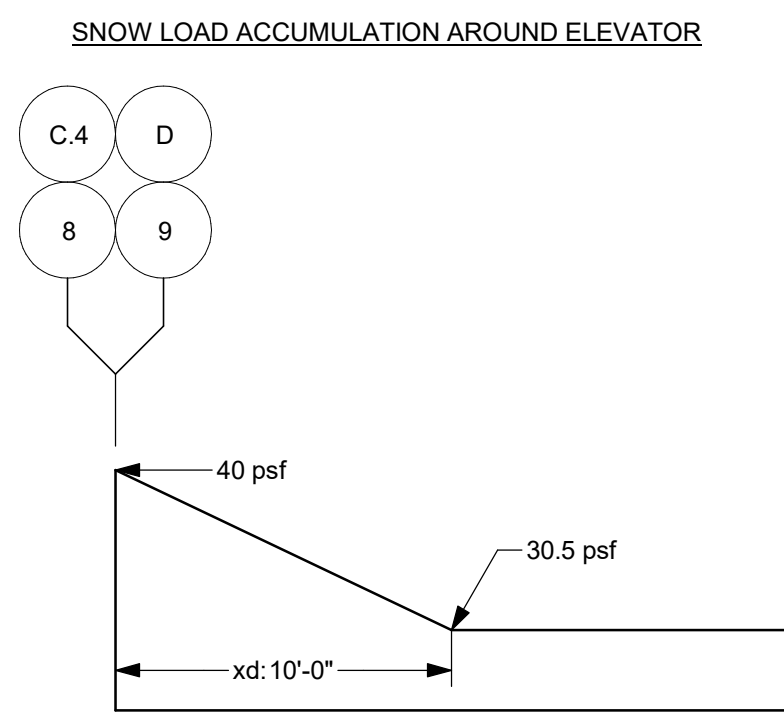


CONTRACTOR/RECTOR NOTE:
IT IS PROHIBITED TO MODIFY, COPY, REPRODUCE OR OTHERWISE
DISTRIBUTE THIS DRAWING OR ANY REPRESENTATION OF THIS
DRAWING, OR ANY MEDIA, INCLUDING ELECTRONIC, WITHOUT THE
PRIOR WRITTEN APPROVAL OF CANAM GROUP INC.

ROOF
TOP OF PLASTER RWL : 98'-0"
TOP OF PLASTER : 98'-0"
TOP OF SLAB : 100'-0"
TOP OF FOUNDATION : 100'-0"
CLEAR HEIGHT : SEE EAMx01 & 502
TOP OF STEEL : 153'-0"
PARAPET HEIGHT : 2'-6"
TOP OF PARAPET : 155'-6"
TOP OF STEEL ELEVATOR : 156'-0"

LOADS
D.L. : 18 psf
C.W. : 0 psf
S.W. : 35.5 psf
S.R. : 2.1 psf
C.W. x C.W. : 0.8
Roof L.L. : 0 psf
Roof snow load : 30.5 psf
W. : 1.0
Wind q = 150 : 9.4 psf
Seismic (Site class: D (Assumed))
I_e : 1.0
S_u(0.2) : 0.201
S_u(0.5) : 0.168
S_u(1.0) : 0.0922
S_u(2.0) : 0.0483
S_u(5.0) : 0.0242
S_u(10.0) : 0.0147
PGA : 0.127
RCV : 0.105

LOADINGS:
• Code Applicable : National building Code of Canada
Alberta Building Code, latest adopted editions
Code of Standard Practice CISC.
• Assumed soil site class: D

NOTE:
1. If, however, the seismic site class is determined to be E or F according to the
geotechnical report, the preliminary structural concept (location and geometry
of bracings, etc.) must be validated and coordinated by a Canam's engineer.

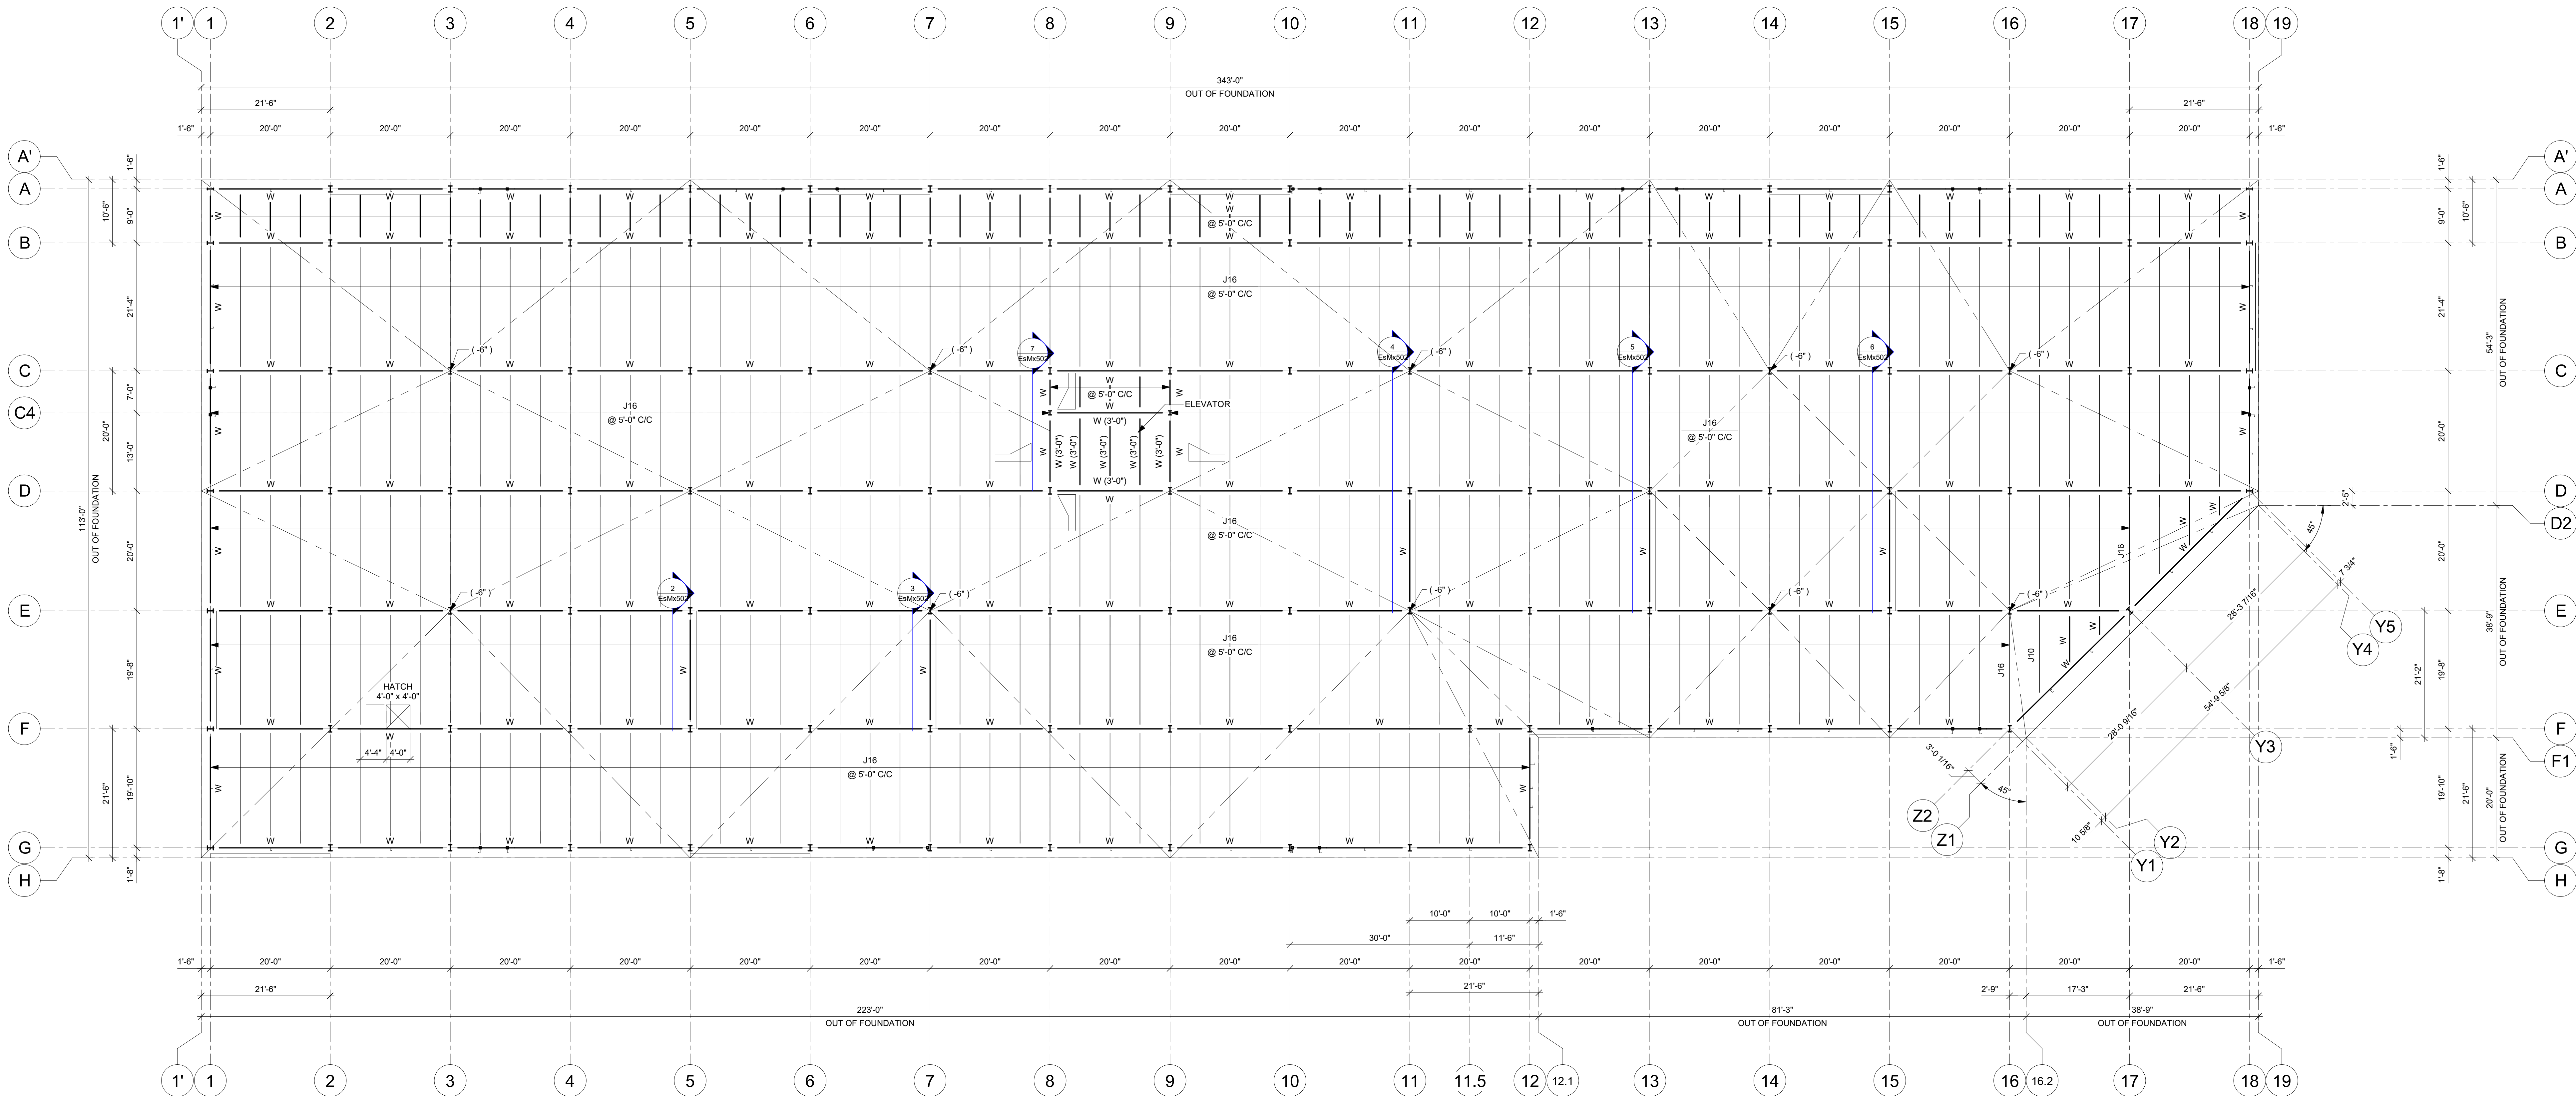

ROOF PLAN
3/32" = 1'-0"

PRELIMINARY
NOT TO BE USED FOR CONSTRUCTION

REVISION	DATE	DESCRIPTION	DESIGN	USER
PROJECT MANAGER				
DRAFTING				
DRAWN	J.P.	DESIGNED	PROJECT ENGINEER	SCALE: Comme indiqué
CHECKED		CONSULTING ENGINEERS ARCHITECTS		DATE: 2026/02/25

CUSTOMER: Premium Projects Ltd




PROFESSIONAL SEAL

PROJECT





SmartStop Self Storage - Building 1
Edmonton, Alberta

DRAWING TITLE
PRELIMINARY SKETCH - ROOF PLAN

CONTRACT NUMBER	DRAWING NUMBER	DIVISION	REVISION
P2026-045	EsMx401		

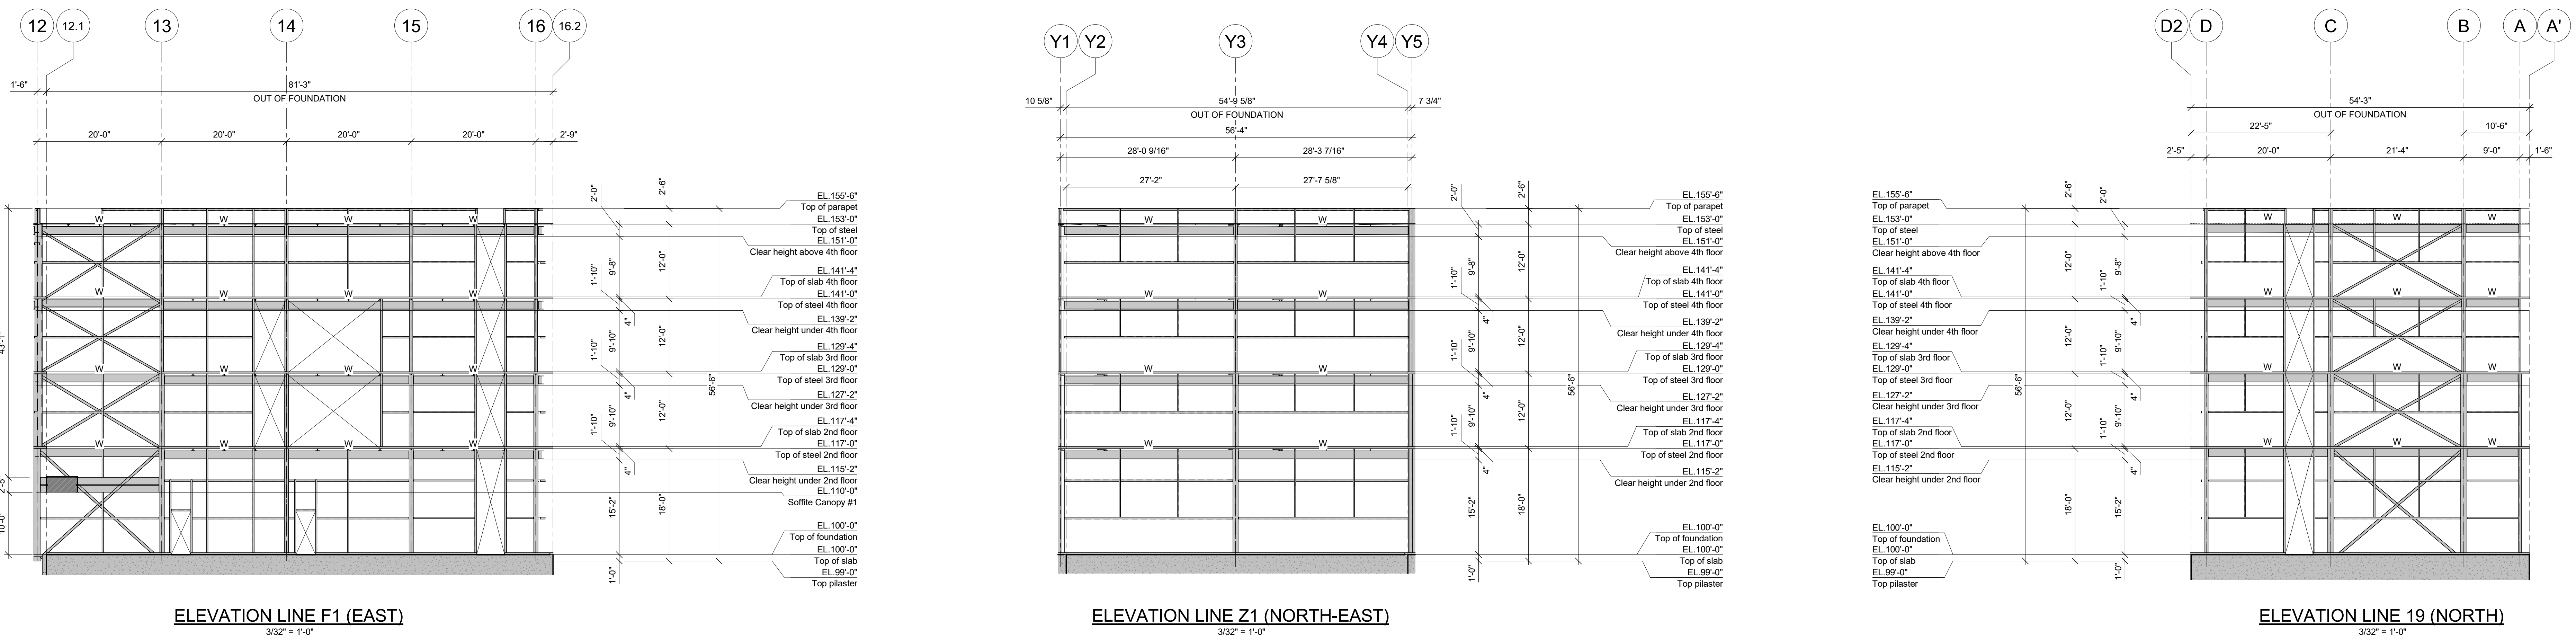

CONTRACT NUMBER P2026-045	DRAWING NUMBER EsMx501	DIVISION	REVISION 
------------------------------	---------------------------	----------	---

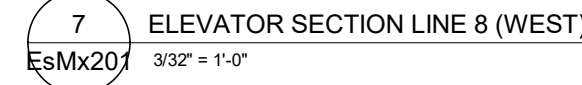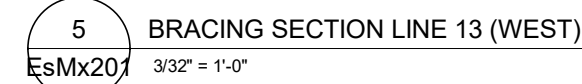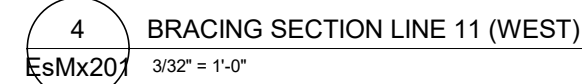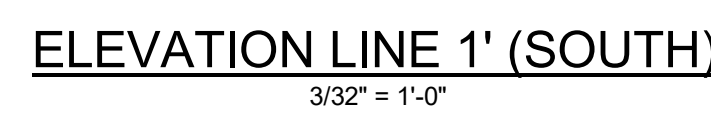

NOT TO BE USED FOR CONSTRUCTION

REVISION	DATE	DESCRIPTION	DESS.	VER.
----------	------	-------------	-------	------

PROJECT MANAGER	-
	-
	-
	-
	-

DRAFTING

DRAWN J.P.	DESIGNED	PROJECT ENGINEER	SCALE: 3/32" = 1'-0"
-------------------	----------	------------------	-----------------------------

CHECKED	CONSULTING ENGINEERS / ARCHITECTS	DATE (yyyy/mm/dd) :
		2026/02/025

CUSTOMER: Pretium Projects Ltd



11505, 1re Avenue, bureau 500, Saint-Georges Beauce
Quebec, Canada, G5Y 7X3
Phone : (418) 228-8031
Toll free : (877) 499-6049
www.canam.com

PROFESSIONAL SEAL

PROJECT

SmartStop Self Storage - Building 1
Edmonton, Alberta

DRAWING TITLE

PRELIMINARY SKETCH - ELEVATIONS & SECTIONS

CONTRACT NUMBER	DRAWING NUMBER	DIVISION	REVISION
-----------------	----------------	----------	----------

lattice

