



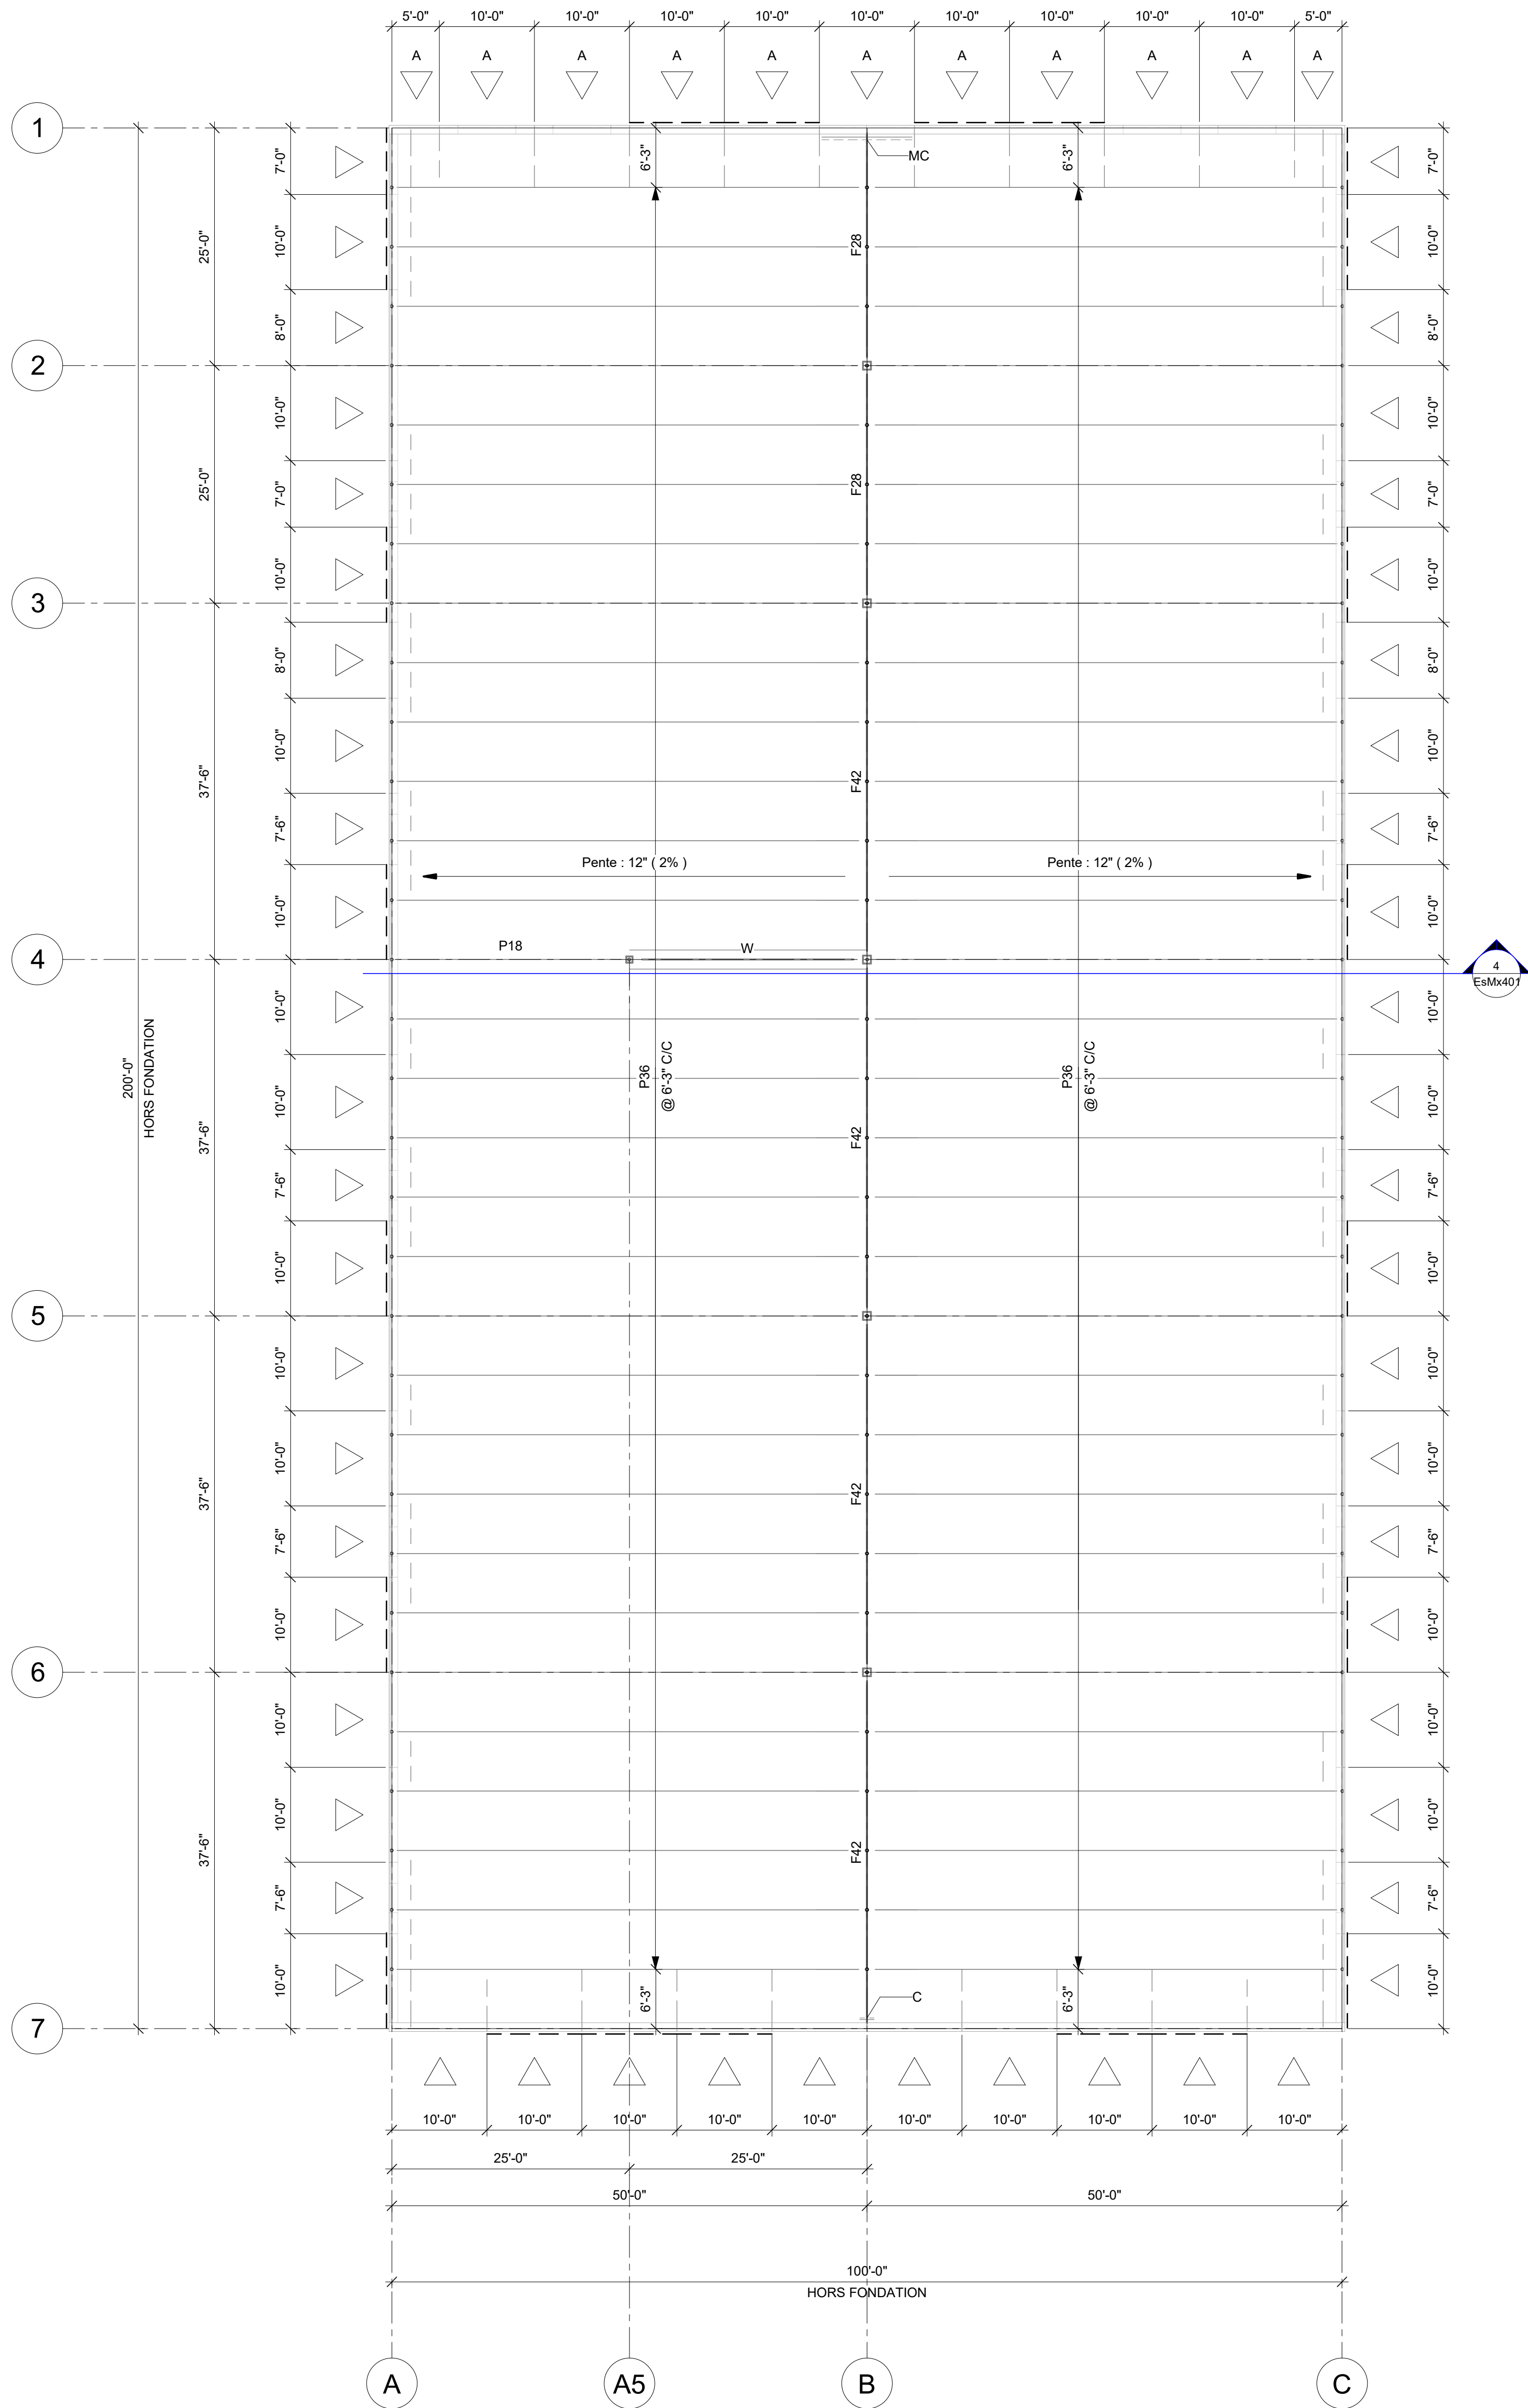

PLAN DE TOIT
3/32" x 1'-0"

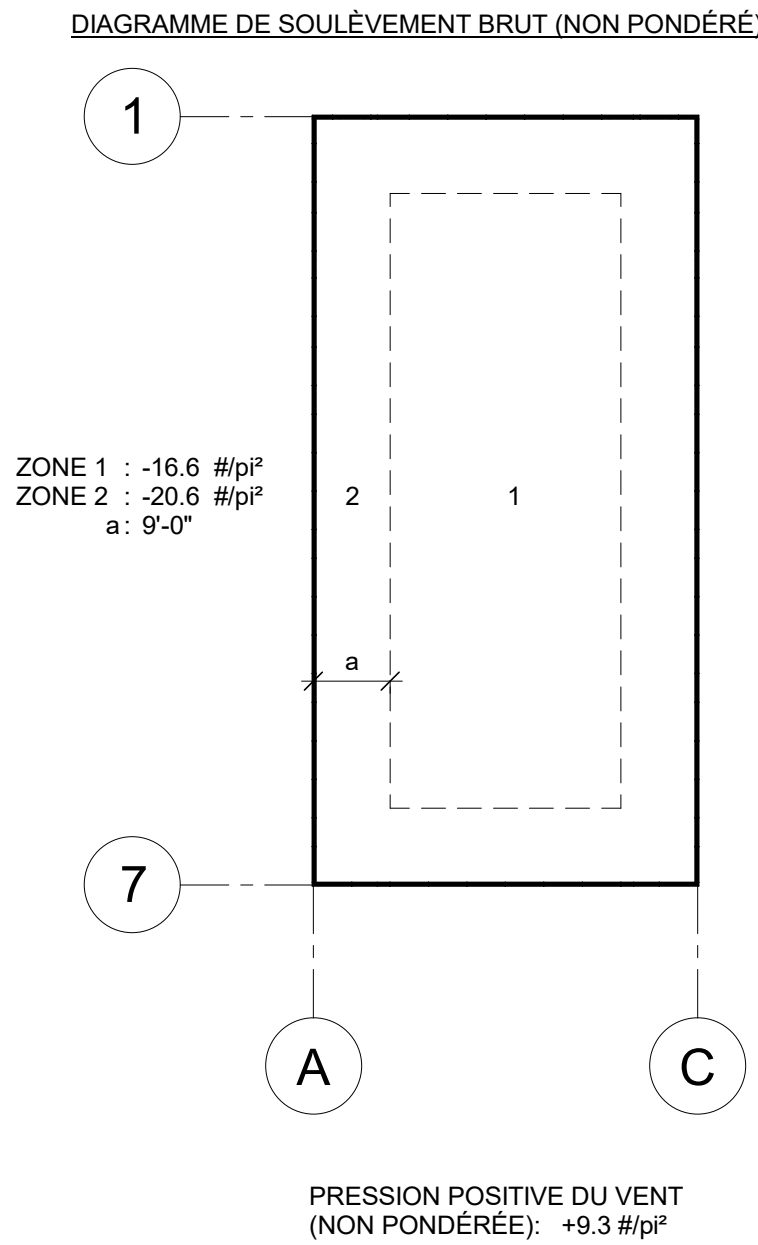

NOTE POUR LE CONTRACTEUR/ÉRECTEUR:

IL EST STRICTEMENT DÉFENDU DE MODIFIER, COPIER, REPRODUIRE OU DE DISTRIBUER CES DESSINS OU QUELQUES REPRÉSENTATIONS DE CES DESSINS, PAR TOUTES SOURCES DE MÉDIA INCLUANT ÉLECTRONIQUEMENT, SANS L'APPROBATION ÉCRITE DE GROUPE CANAM INC.

TOIT

DESSUS DE PILASTRE DDP	: 98'-0"
DESSUS DE PILASTRE	: 99'-0"
DESSUS DE LA DALLE	: 100'-0"
DESSUS DE LA FONDATION	: 100'-0"
HAUTEUR LIBRE AXE A & C	: 122'-10"
HAUTEUR LIBRE AXE B	: 123'-10"
DESSUS D'ACIER AXE A & C	: 123'-10"
DESSUS D'ACIER AXE B	: 123'-10"
HAUTEUR DE PARAPET AXE A & C	: 0'-0"
HAUTEUR DE PARAPET AXE 1 & 7	: 0'-8"

CHARGES

C.M.	: 16 lbs/p²
C.M.	: 5 lbs/p²
S _u	: 75.2 lbs/p²
S _u	: 8.36 lbs/p²
C _p x C _w	: 0.8
C.V. au toit	: 0 lbs/p²
I _u	: 1.0
Charge de neige au toit	: 68.5 lbs/p²
I _u	: 1.0
Vent q = 150	: 8.56 lbs/p²

Séisme (Sol de classe D assumé)

I _e	: 1.0
S _u (0.2)	: 0.625
S _u (0.5)	: 0.547
S _u (1.0)	: 0.331
S _u (2.0)	: 0.160
S _u (5.0)	: 0.0452
S _u (10.0)	: 0.0143
PCA	: 0.355
PGV	: 0.384



CHARGES:

Code Applicable : Code National du Bâtiment du Canada
Code du bâtiment du Québec, dernières éditions adoptées
Code de Pratique Standard ICCA.

Type de sol assumé : classe D

NOTE:

1. Si toutefois la catégorie d'emplacement devient E ou F selon le rapport géotechnique, le concept structural préliminaire (localisation et géométrie des contreventements, etc.) devra être validé et coordonné par l'ingénieur de Canam.

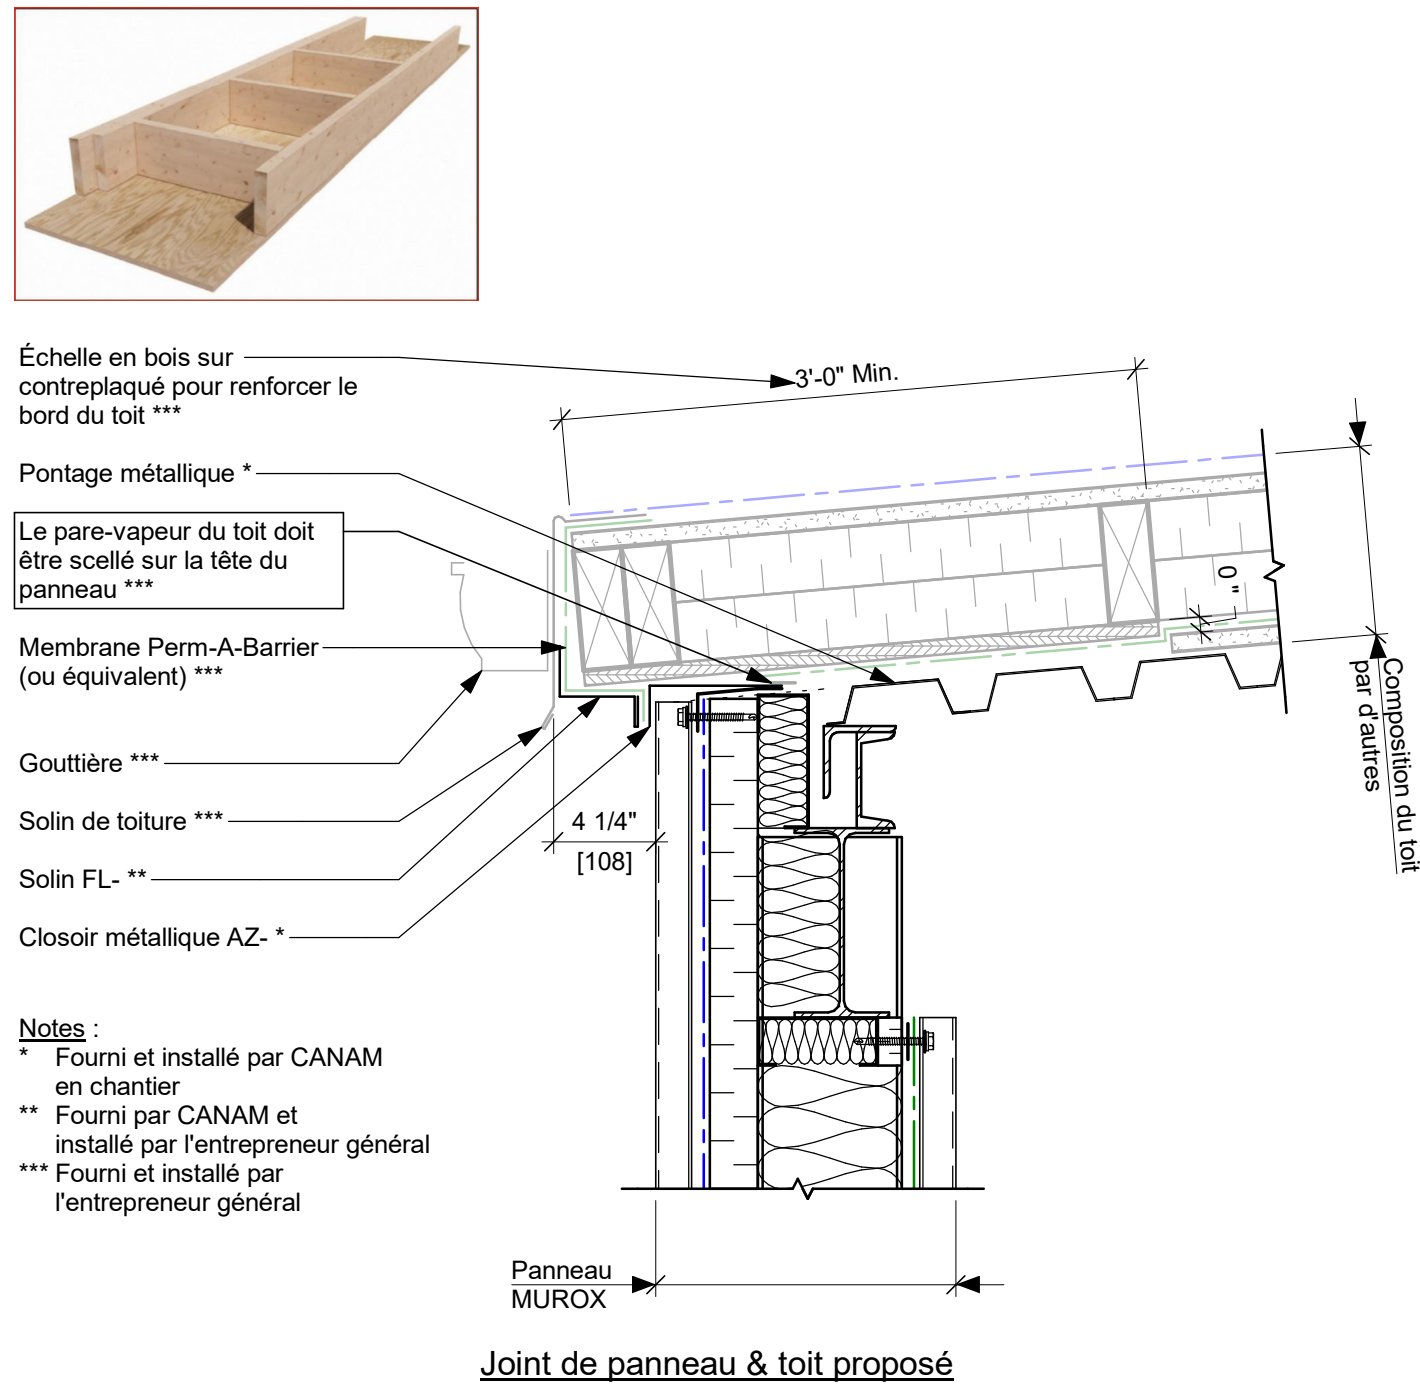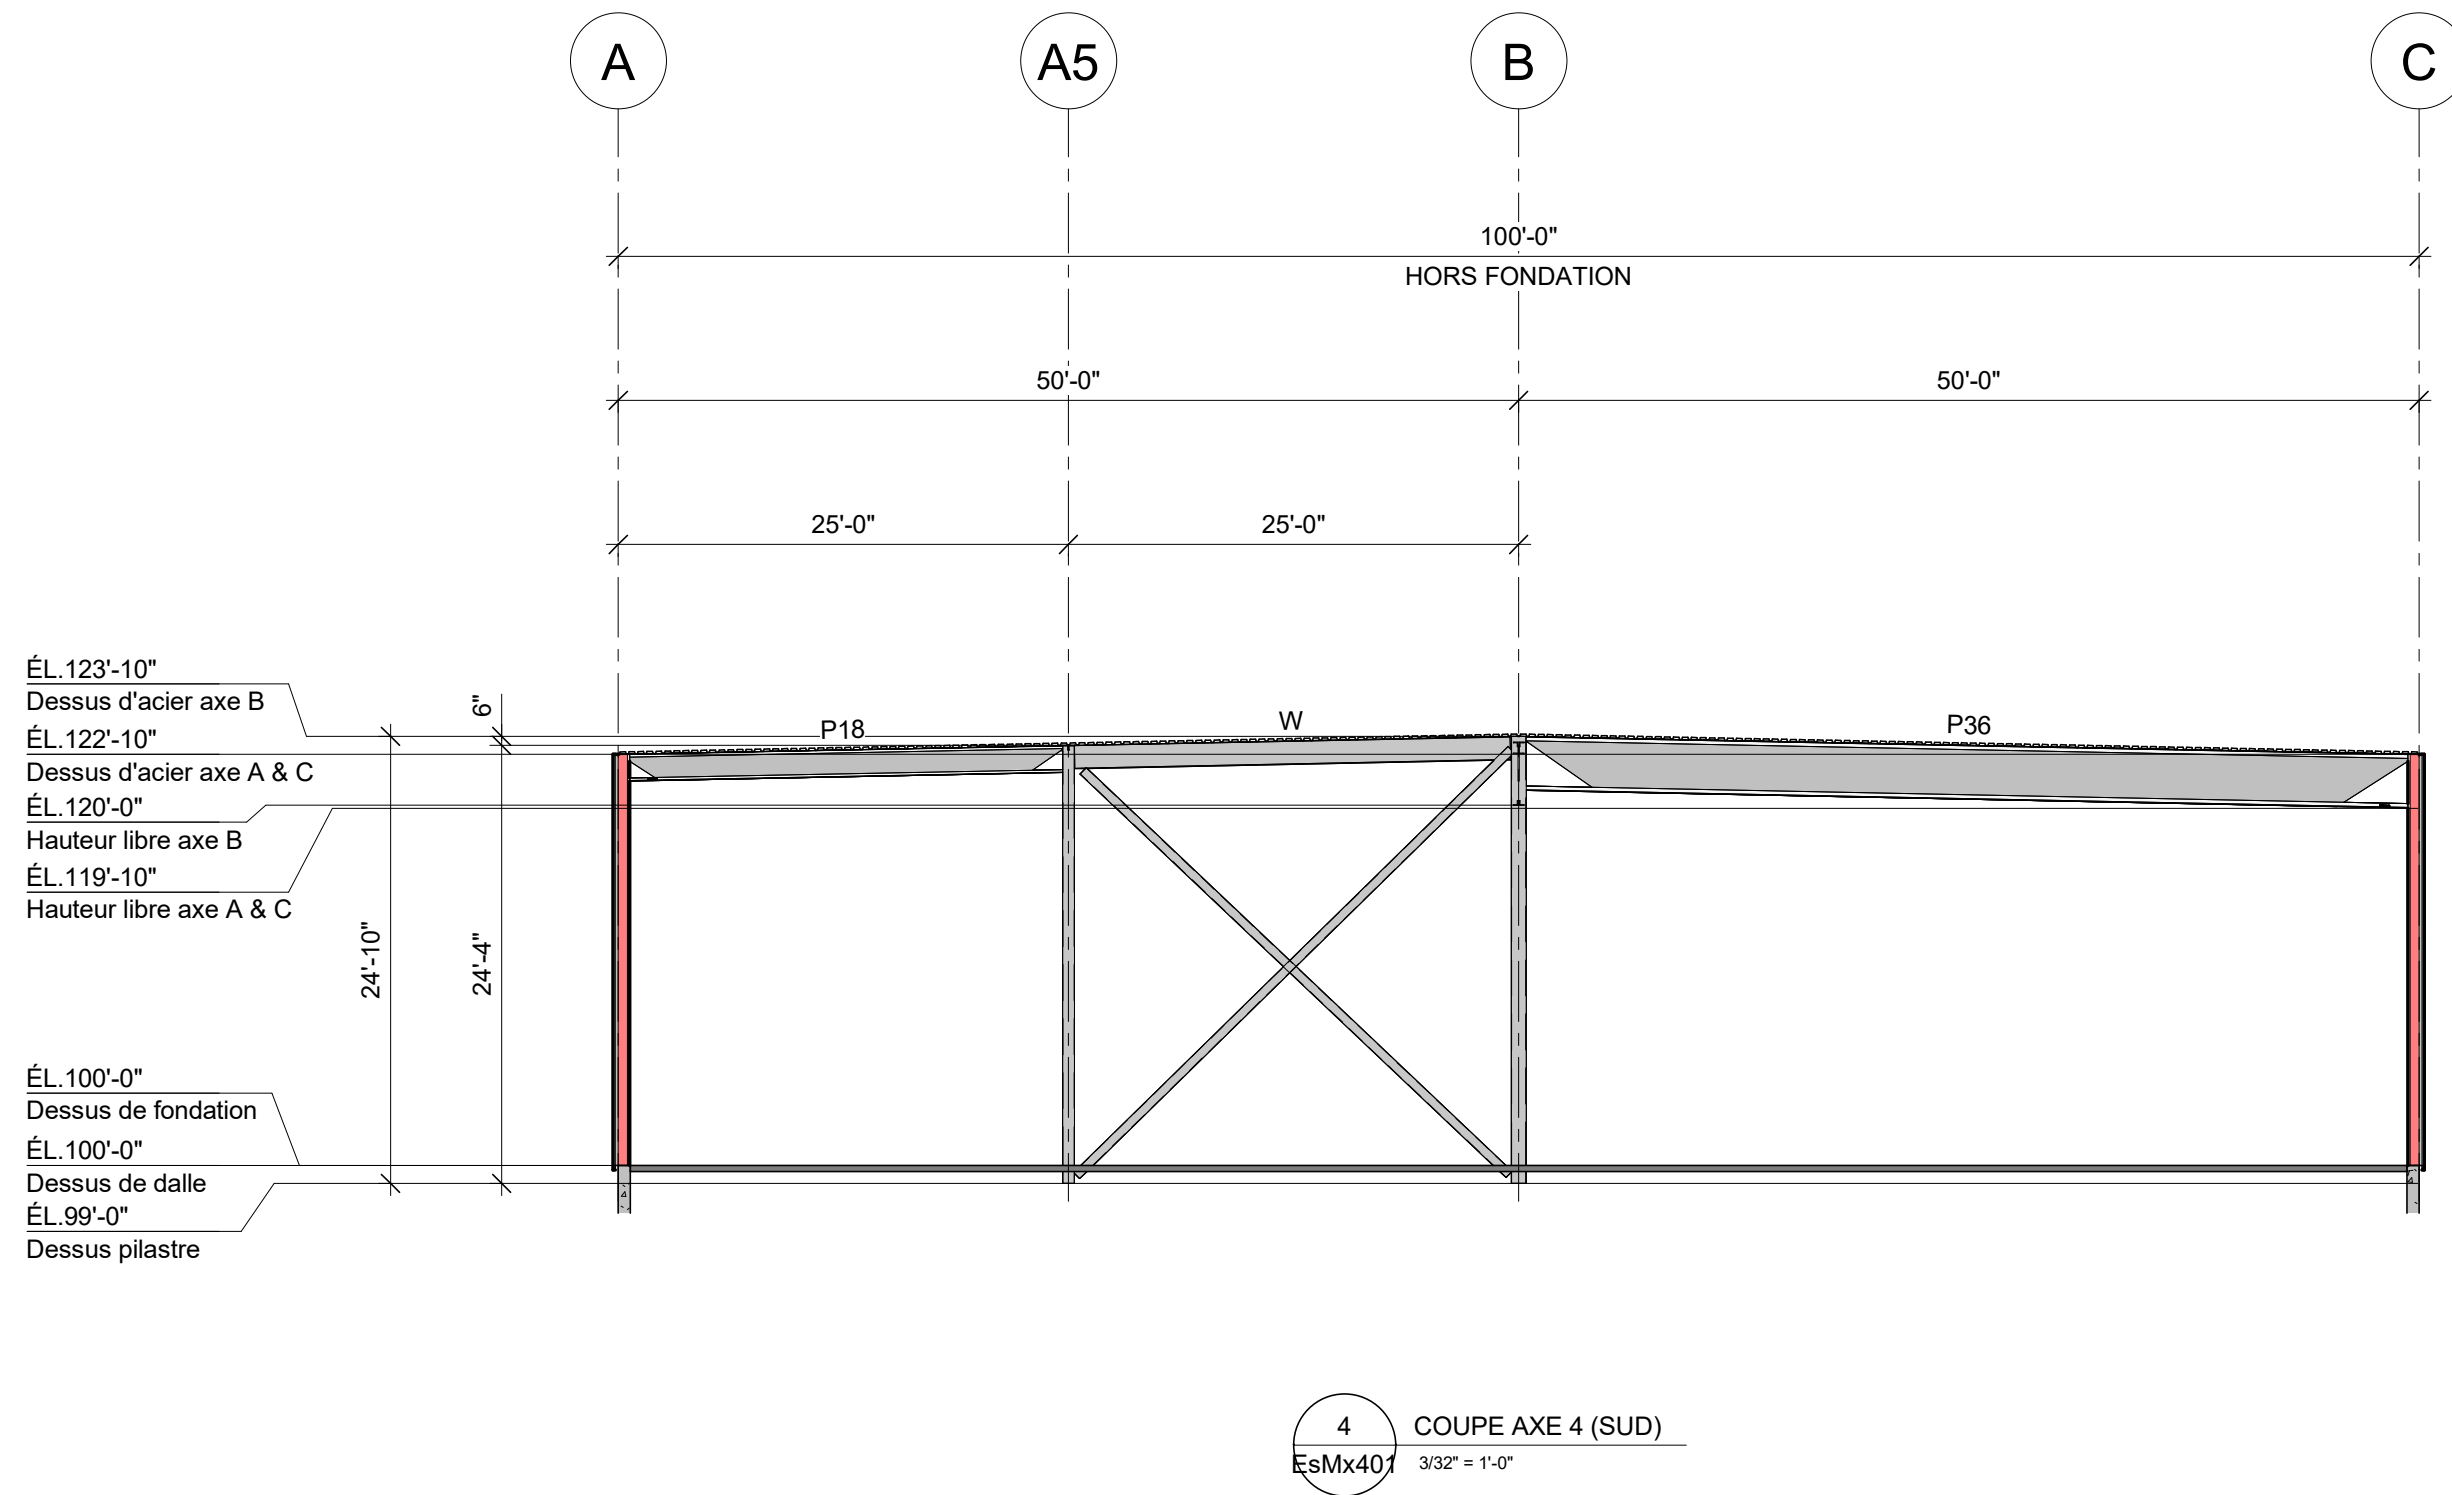

PRÉLIMINAIRE

NE DOIT PAS SERVIR À LA
CONSTRUCTION

REVISION	DATE	DESCRIPTION	DESS	VER
DESSIN DE PROJET				
		-		
		-		
		-		
DESSIN				
DESSINÉ PAR	CONÇU PAR	INGÉNIEUR DU PROJET	ÉCHELLE:	
INITIALE			Comme indiqué	
VERIFIÉ PAR	INGÉNIEURS CONSEILS / ARCHITECTES		DATE (mm/aaaa)	
			27/02/2026	

CLIENT: Toiture Summa



SCAUX PROFESSIONNELS

PROJET

Entrepot E&G
Saint-Lambert de Lauzon, Québec

TITRE

CROQUIS PRÉLIMINAIRE - PLAN DE TOIT

NUMÉRO CONTRAT	NUMÉRO DESSIN	DIVISION	REVISION
P2026-048	EsMx401		