


Quincaillerie standard du fournisseur:
- Chambrés : Stanley FBB179 4.5" x 4"
- Barre panique : Von Duprin 22 x 689 avec poignée extérieure Z30L
- Cylindre permanent : Schlage 2001C 686
- Ferme-porte : LCN 1261 689
- Coupe-froid de tête et des montants : Unique 1650
- Coupe-froid du bas : Unique D54
- Seuil : Voir la remarque dans la "Cédule de porte"

CÉDULE DES FENÊTRES					
Identifiant	Qté	Installation	Description	Dimensions ext. cadre largeur X hauteur	Couleur du cadre
F1	4		Fenêtre en aluminium fixe avec bris thermique et verre scellé + Low-E argon clair	6'-0" x 6'-0"	Cadre d'Aluminium (Blanc ext. et int.)
F2	4		Fenêtre en aluminium fixe avec bris thermique et verre scellé + Low-E argon clair	6'-0" x 4'-0"	Cadre d'Aluminium (Blanc ext. et int.)
F3	10		Fenêtre en aluminium fixe avec bris thermique et verre scellé + Low-E argon clair	5'-0" x 6'-0"	Cadre d'Aluminium (Blanc ext. et int.)


CÉDULE DES PORTES														
Identifiant	Qté	Installation	Porte 18 ja.		Sens ouv.	Vitrage		Cadre d'acier 16 ja. avec bris thermique	(3) Pentures @ type fixe	Poignées seulement	Barre panique sans poignée ext. ZZE0	Quincaillerie Barre panique avec poignée ext. Z30L	Verrou en surface (Porte inactive)	Astragale sur porte inactive
			Isolation (RT2)	Dimensions		Largeur	Hauteur							
P1	10			3'-0" x 7'-0"										

CÉDULE DES P.M. ET DES OUVERTURES			
Total	Type	Tag	Commentaires
1	6'-0" x 7'-0"	OUV	
10	14'-0" x 14'-0"	PM	
Total général: 11			


NOTE POUR LE CONTRACTEUR/ÉRECTEUR:
IL EST STRICTEMENT DÉFENDU DE MODIFIER, COPIER, REPRODUIRE OU DE DISTRIBUER CES DESSINS OU QUELQUES REPRÉSENTATIONS DE CES DESSINS, PAR TOUTES SOURCES DE MÉDIA INCLUANT ÉLECTRONIQUEMENT, SANS L'APPROBATION ÉCRITE DE GROUPE CANAM INC.

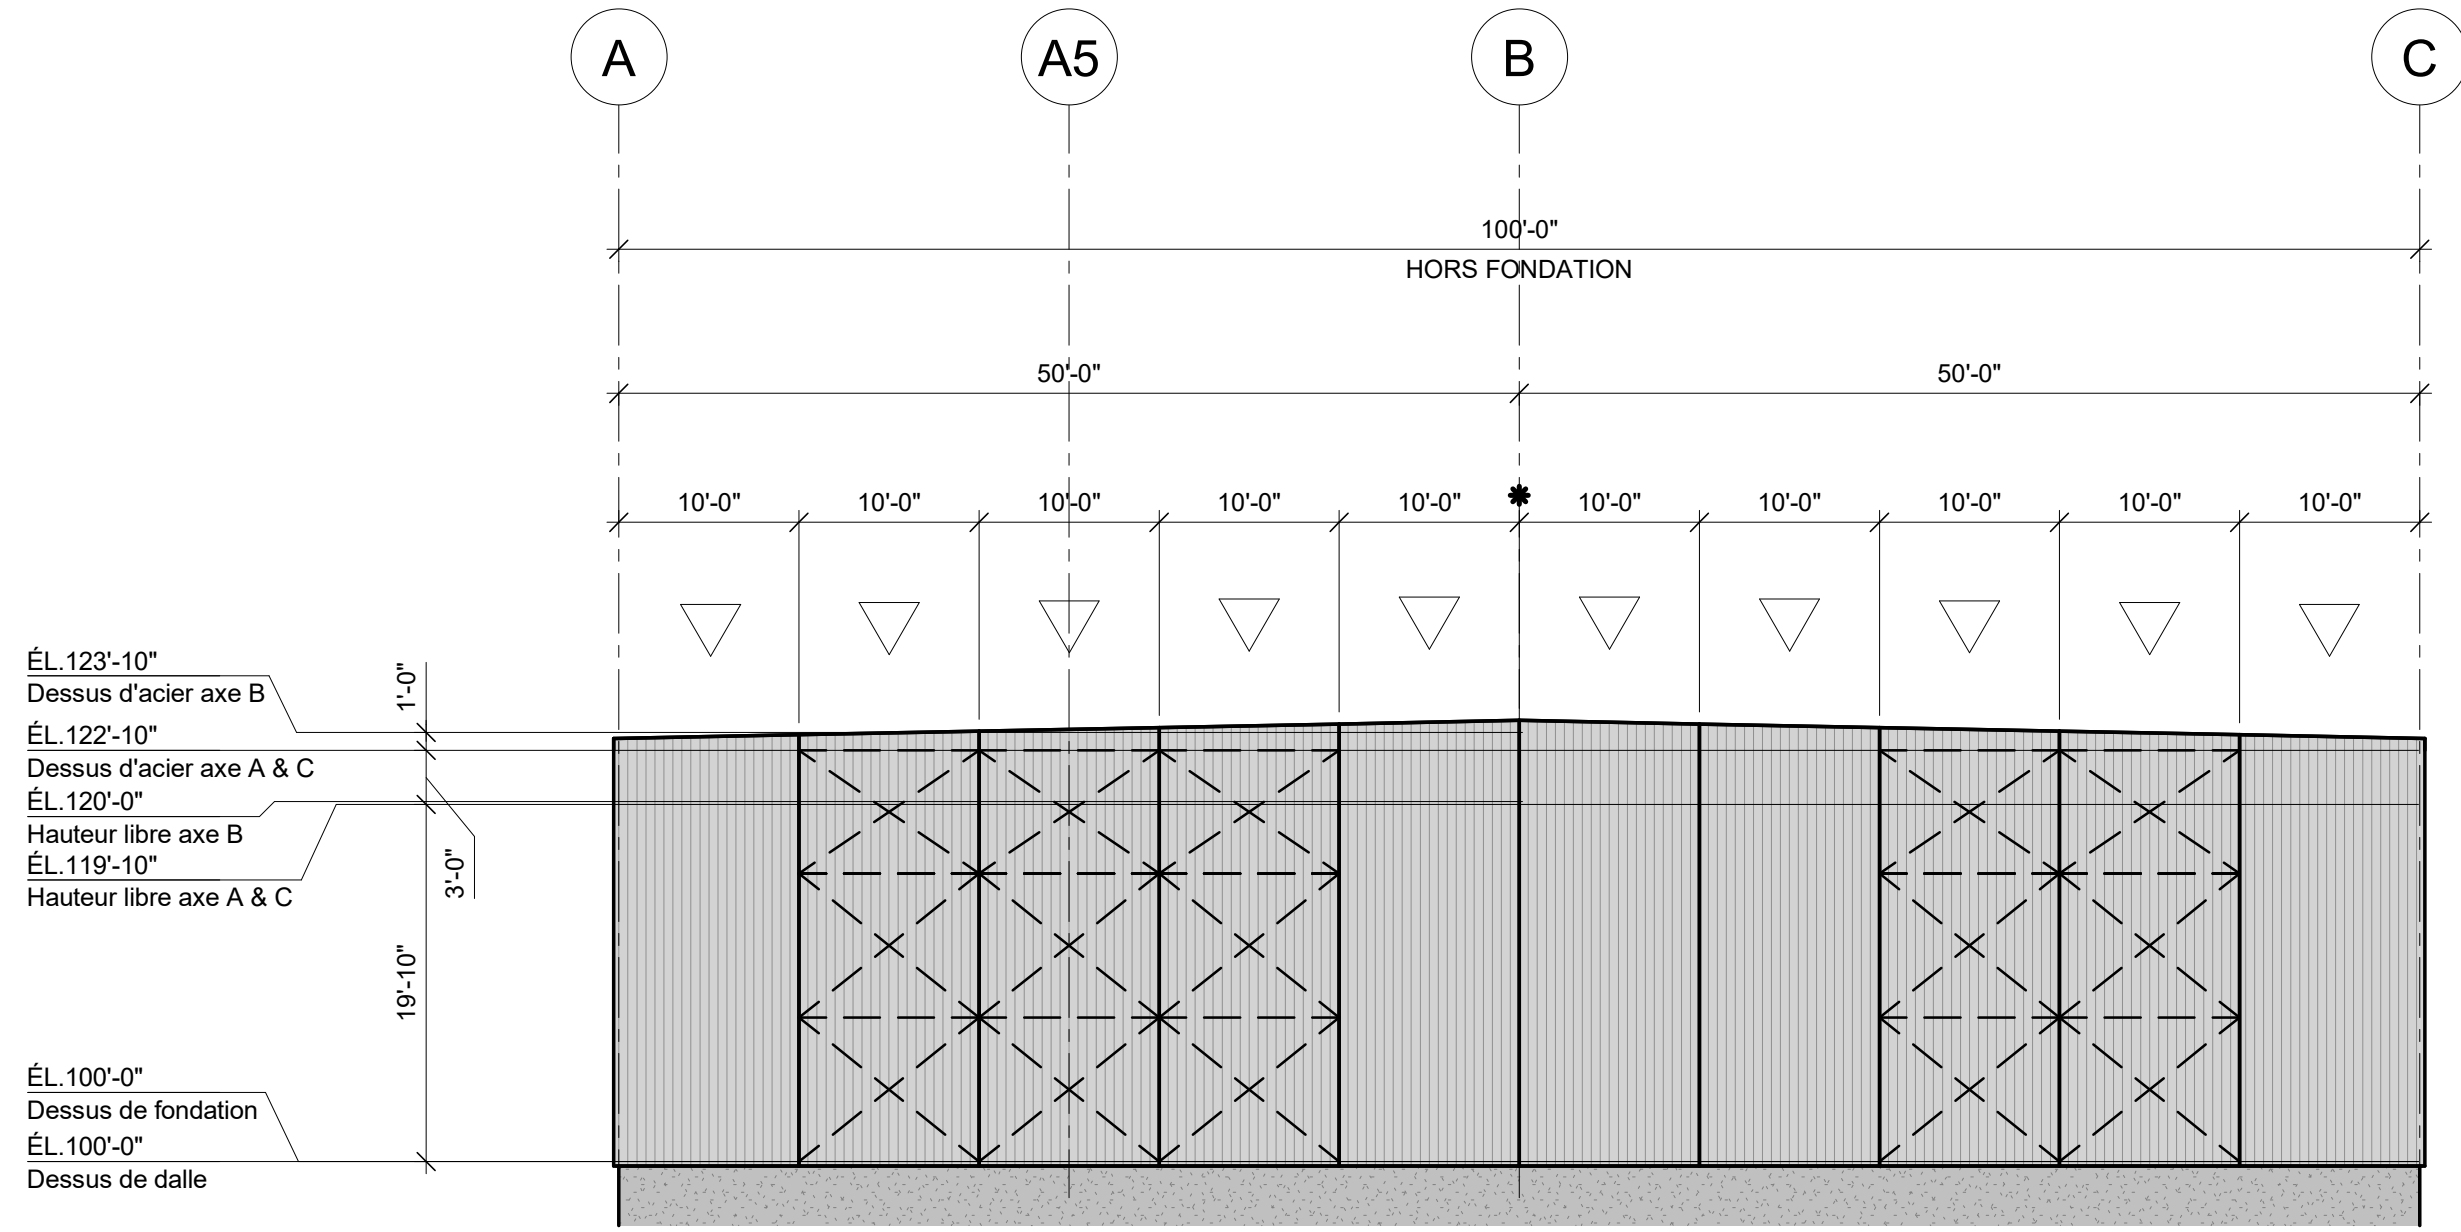


ÉLEVATION AXE 7 (SUD)
3/32" = 1'-0"

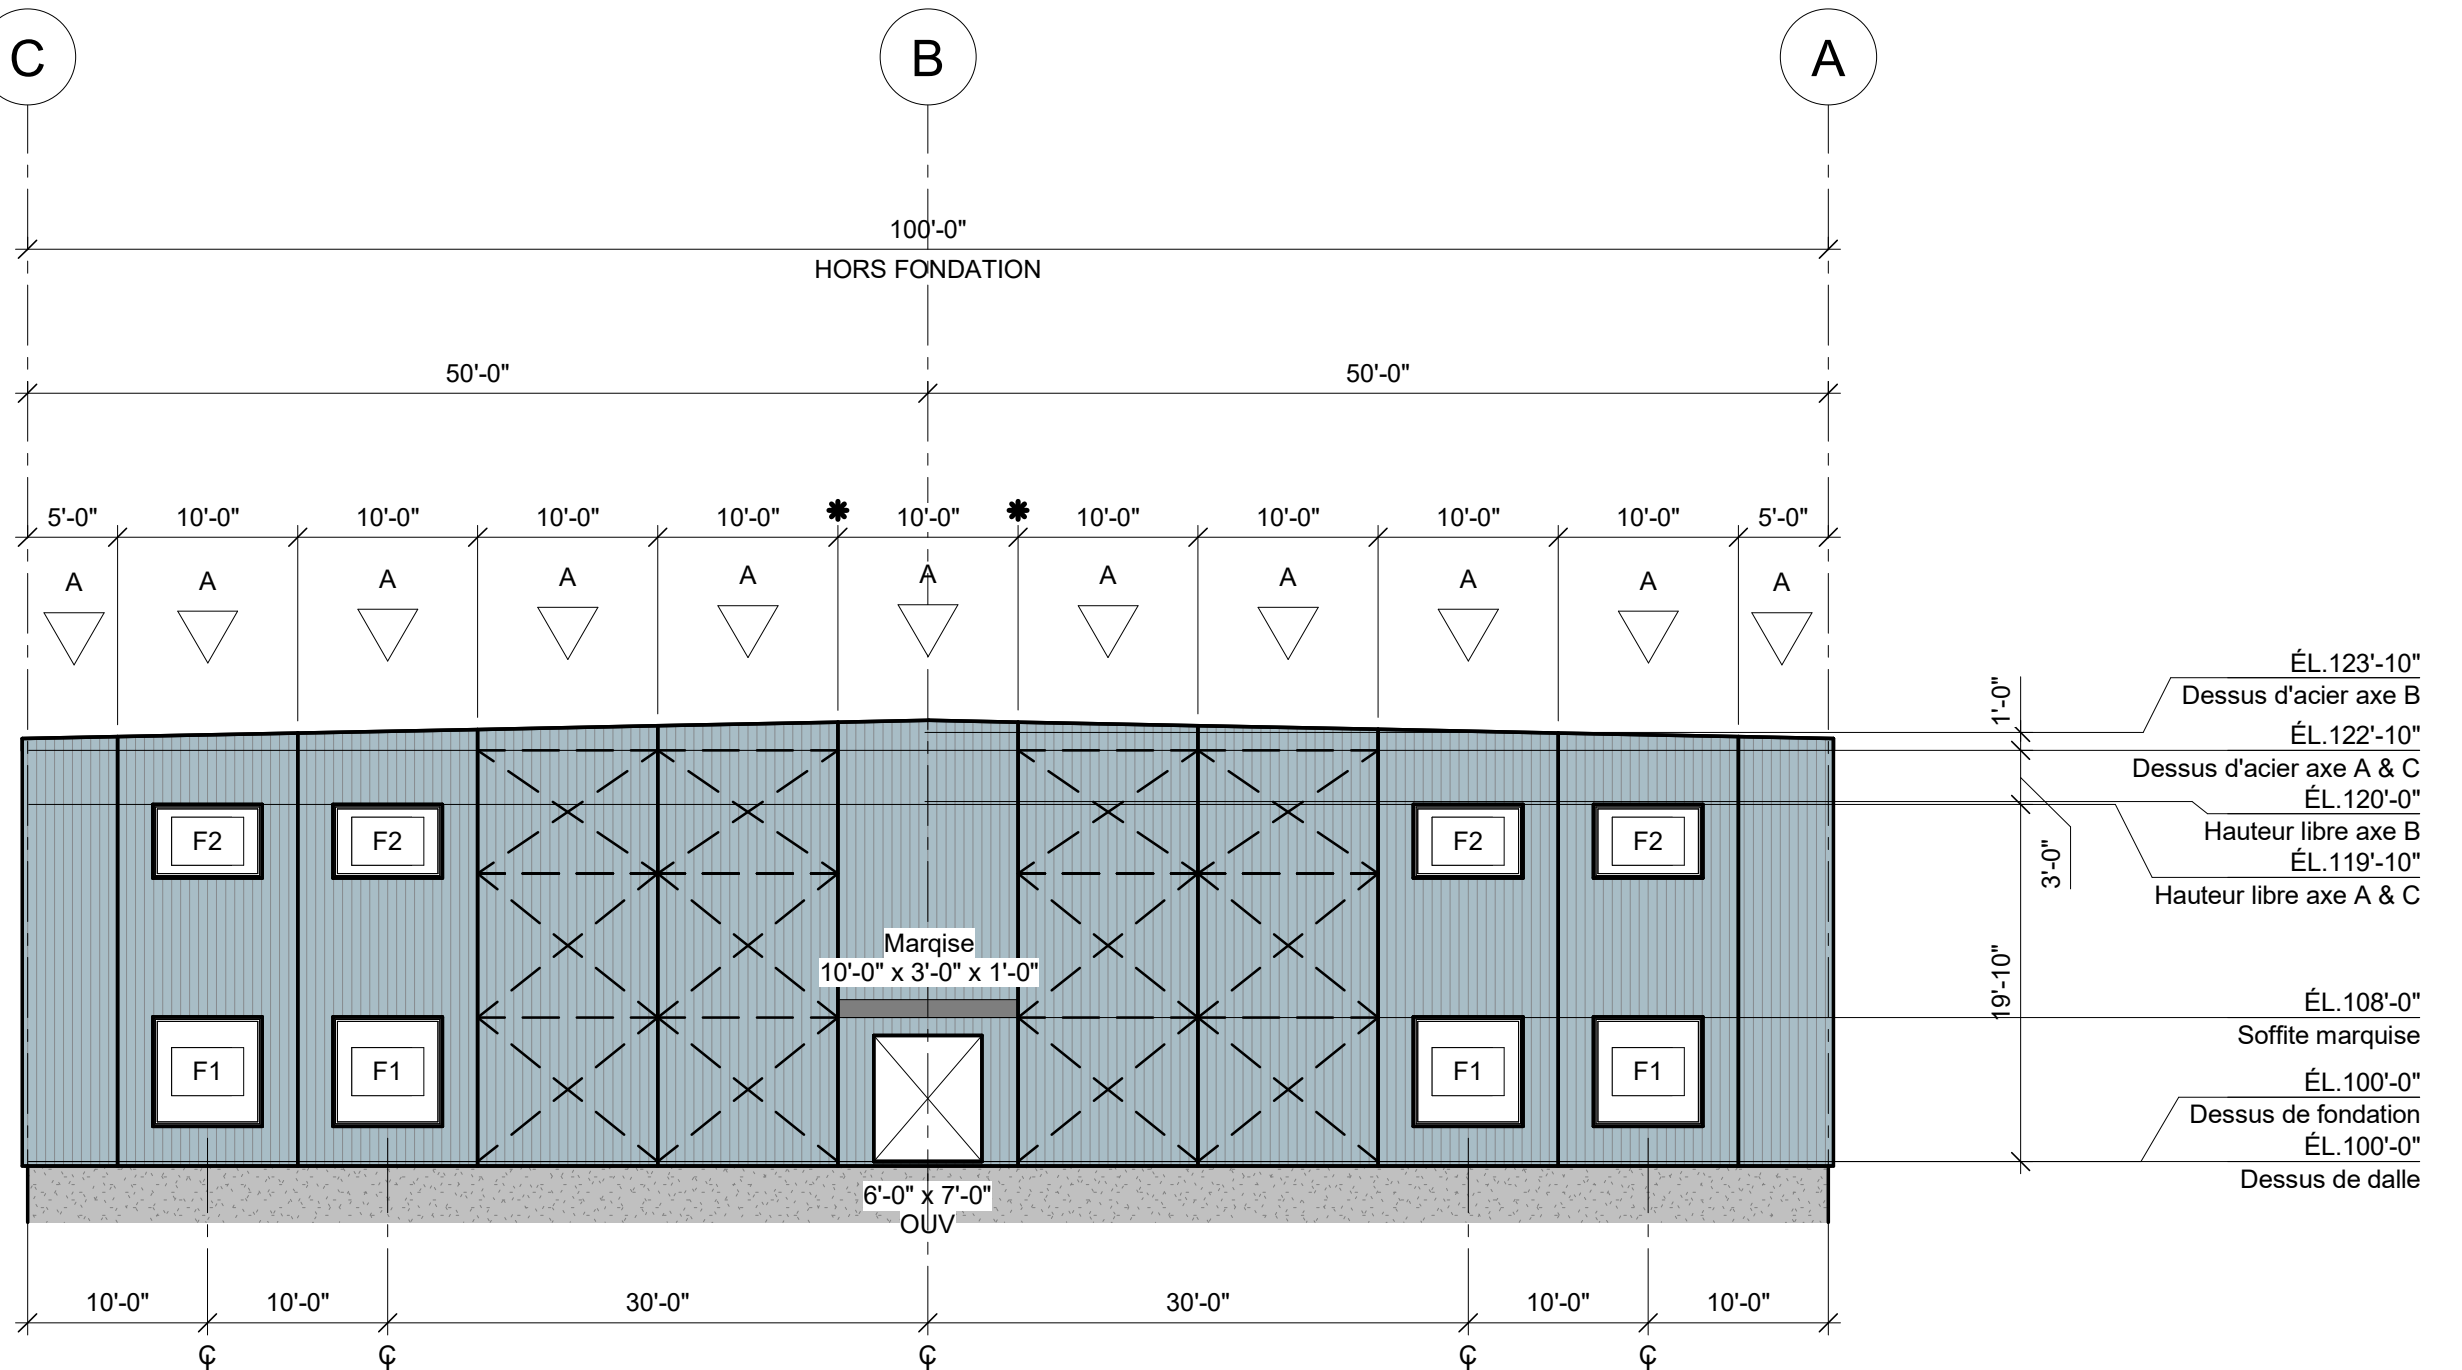



ÉLEVATION AXE 1 (NORD)
3/32" = 1'-0"

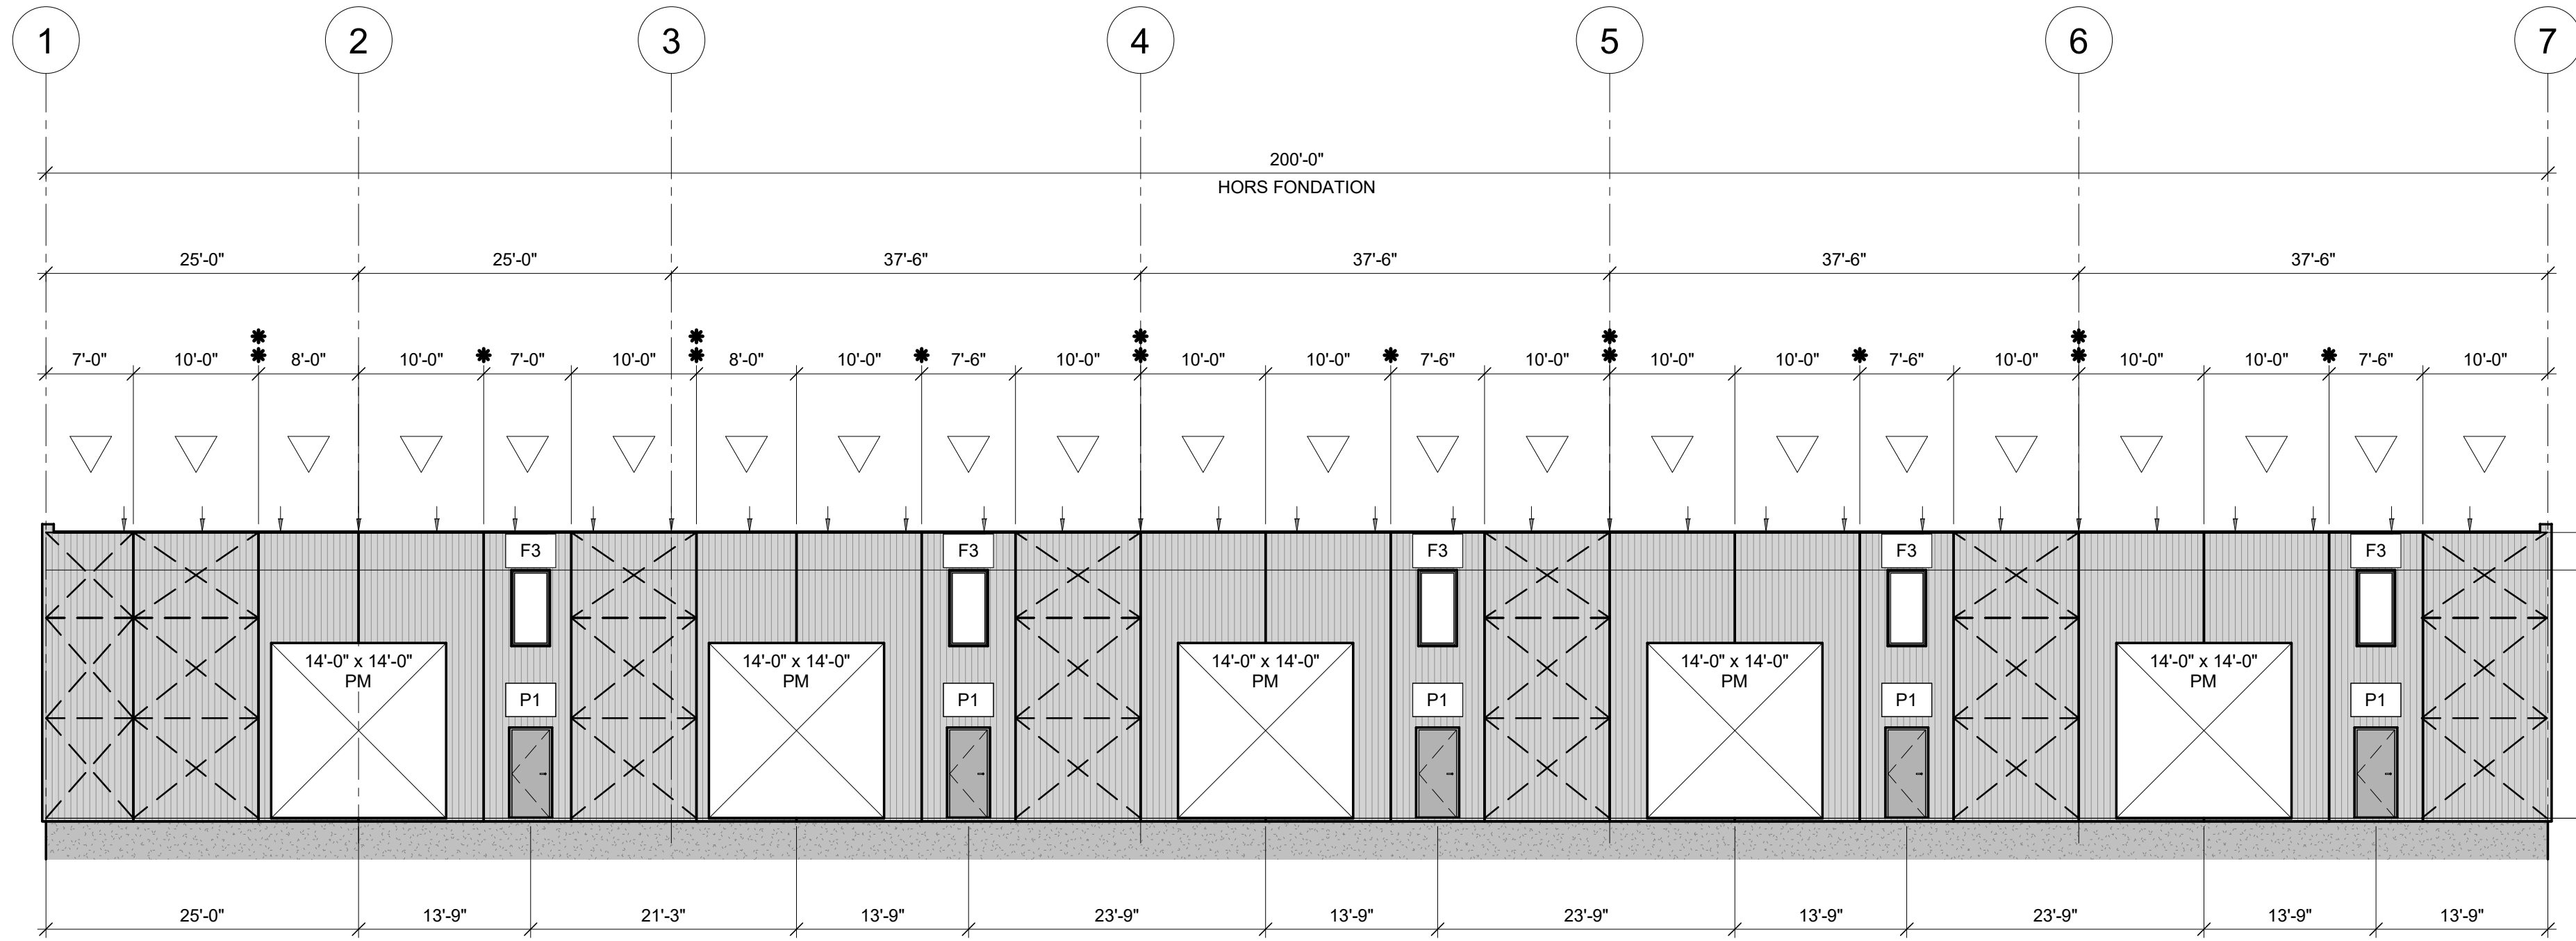

ÉLEVATION AXE A (OUEST)
3/32" = 1'-0"

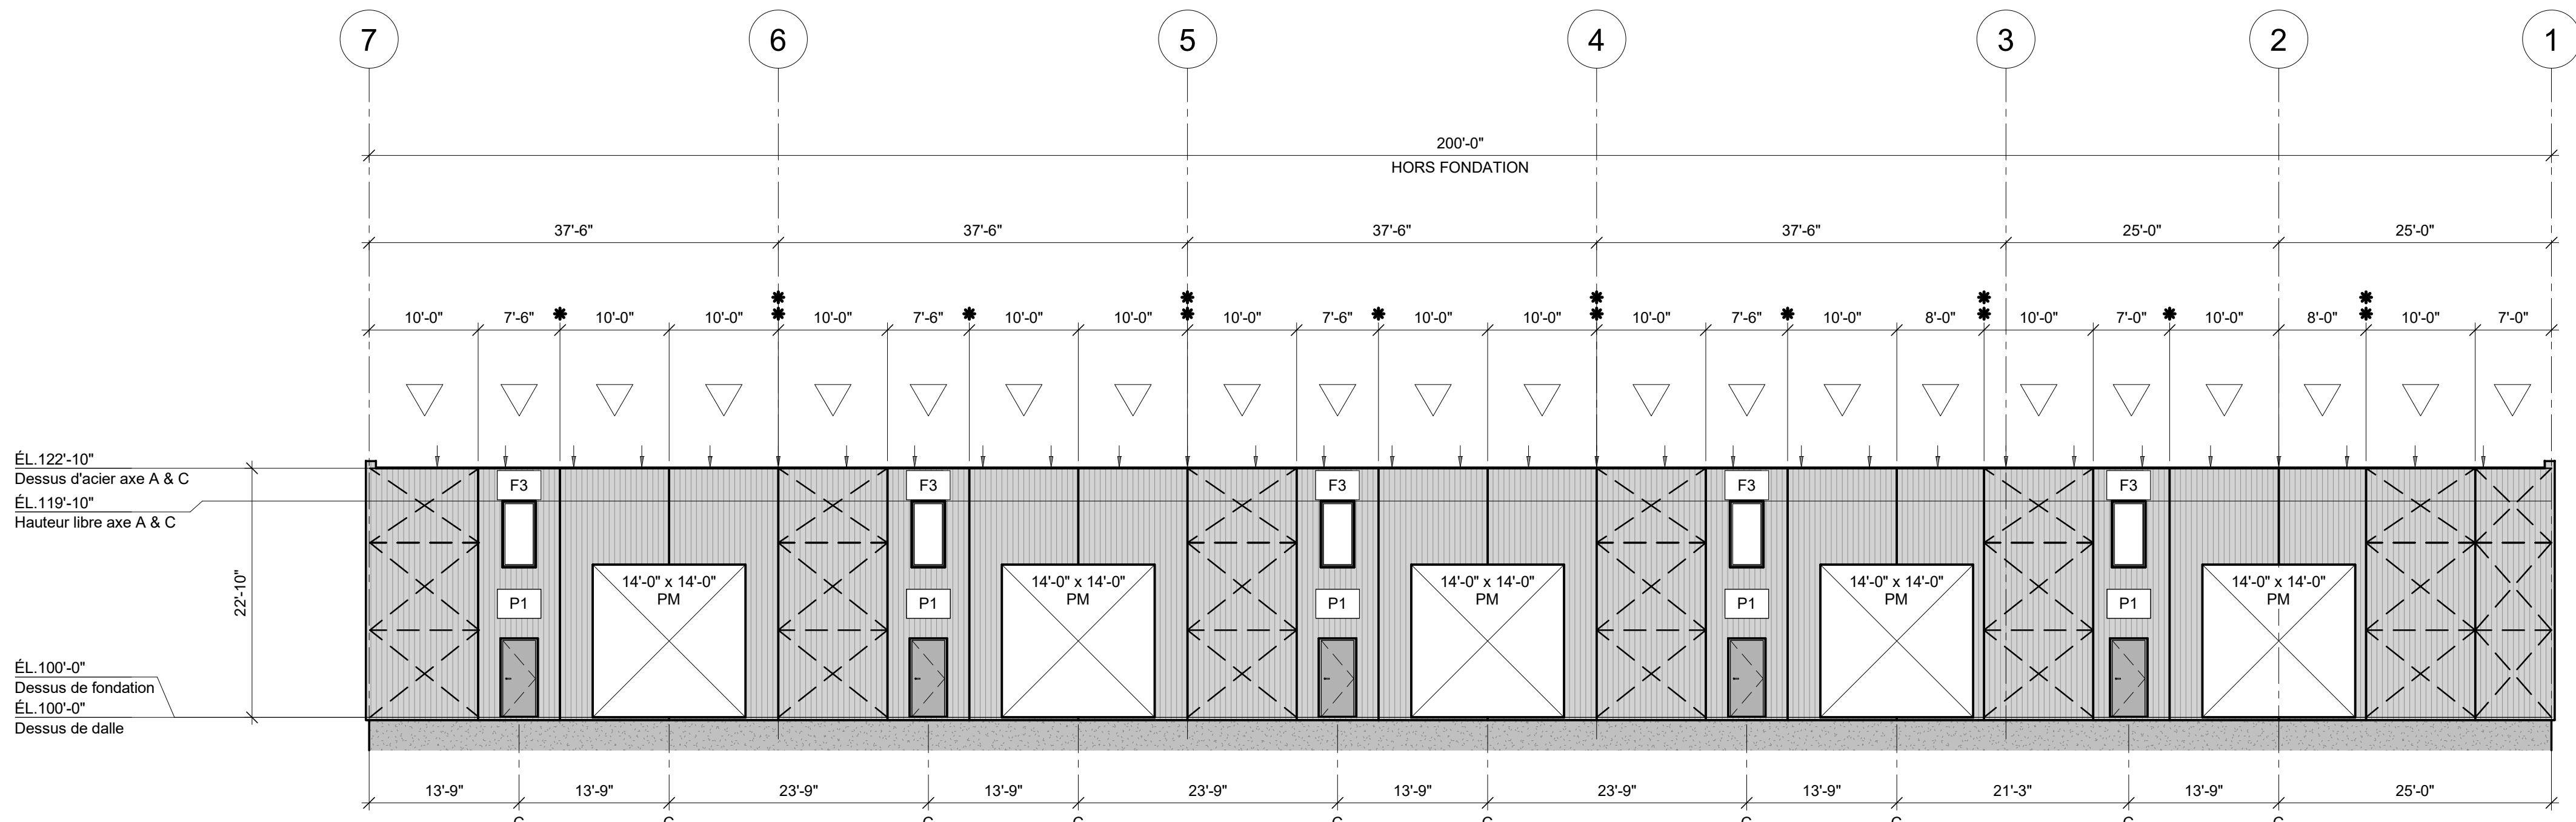


ÉLEVATION AXE C (EST)
3/32" = 1'-0"

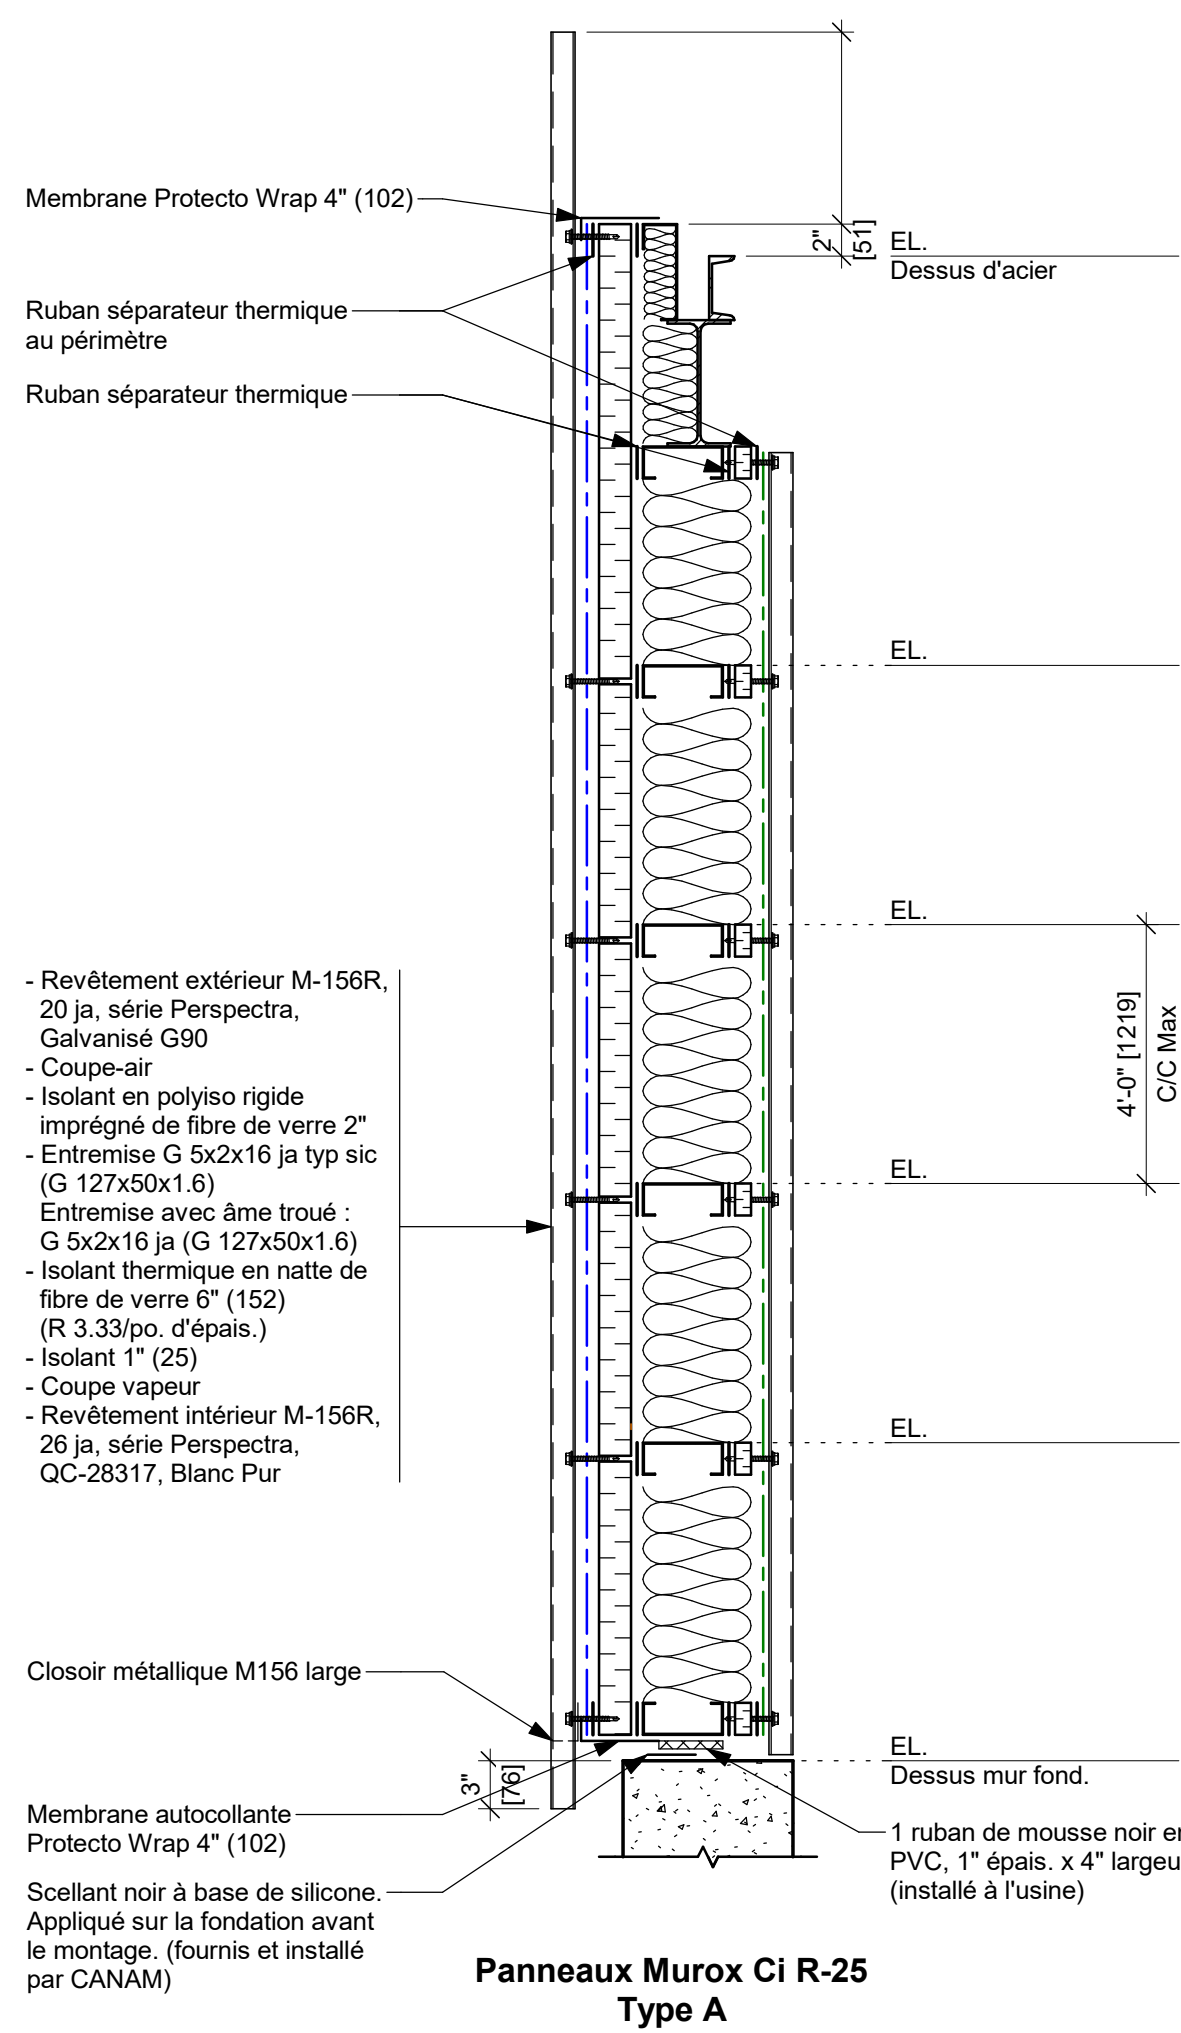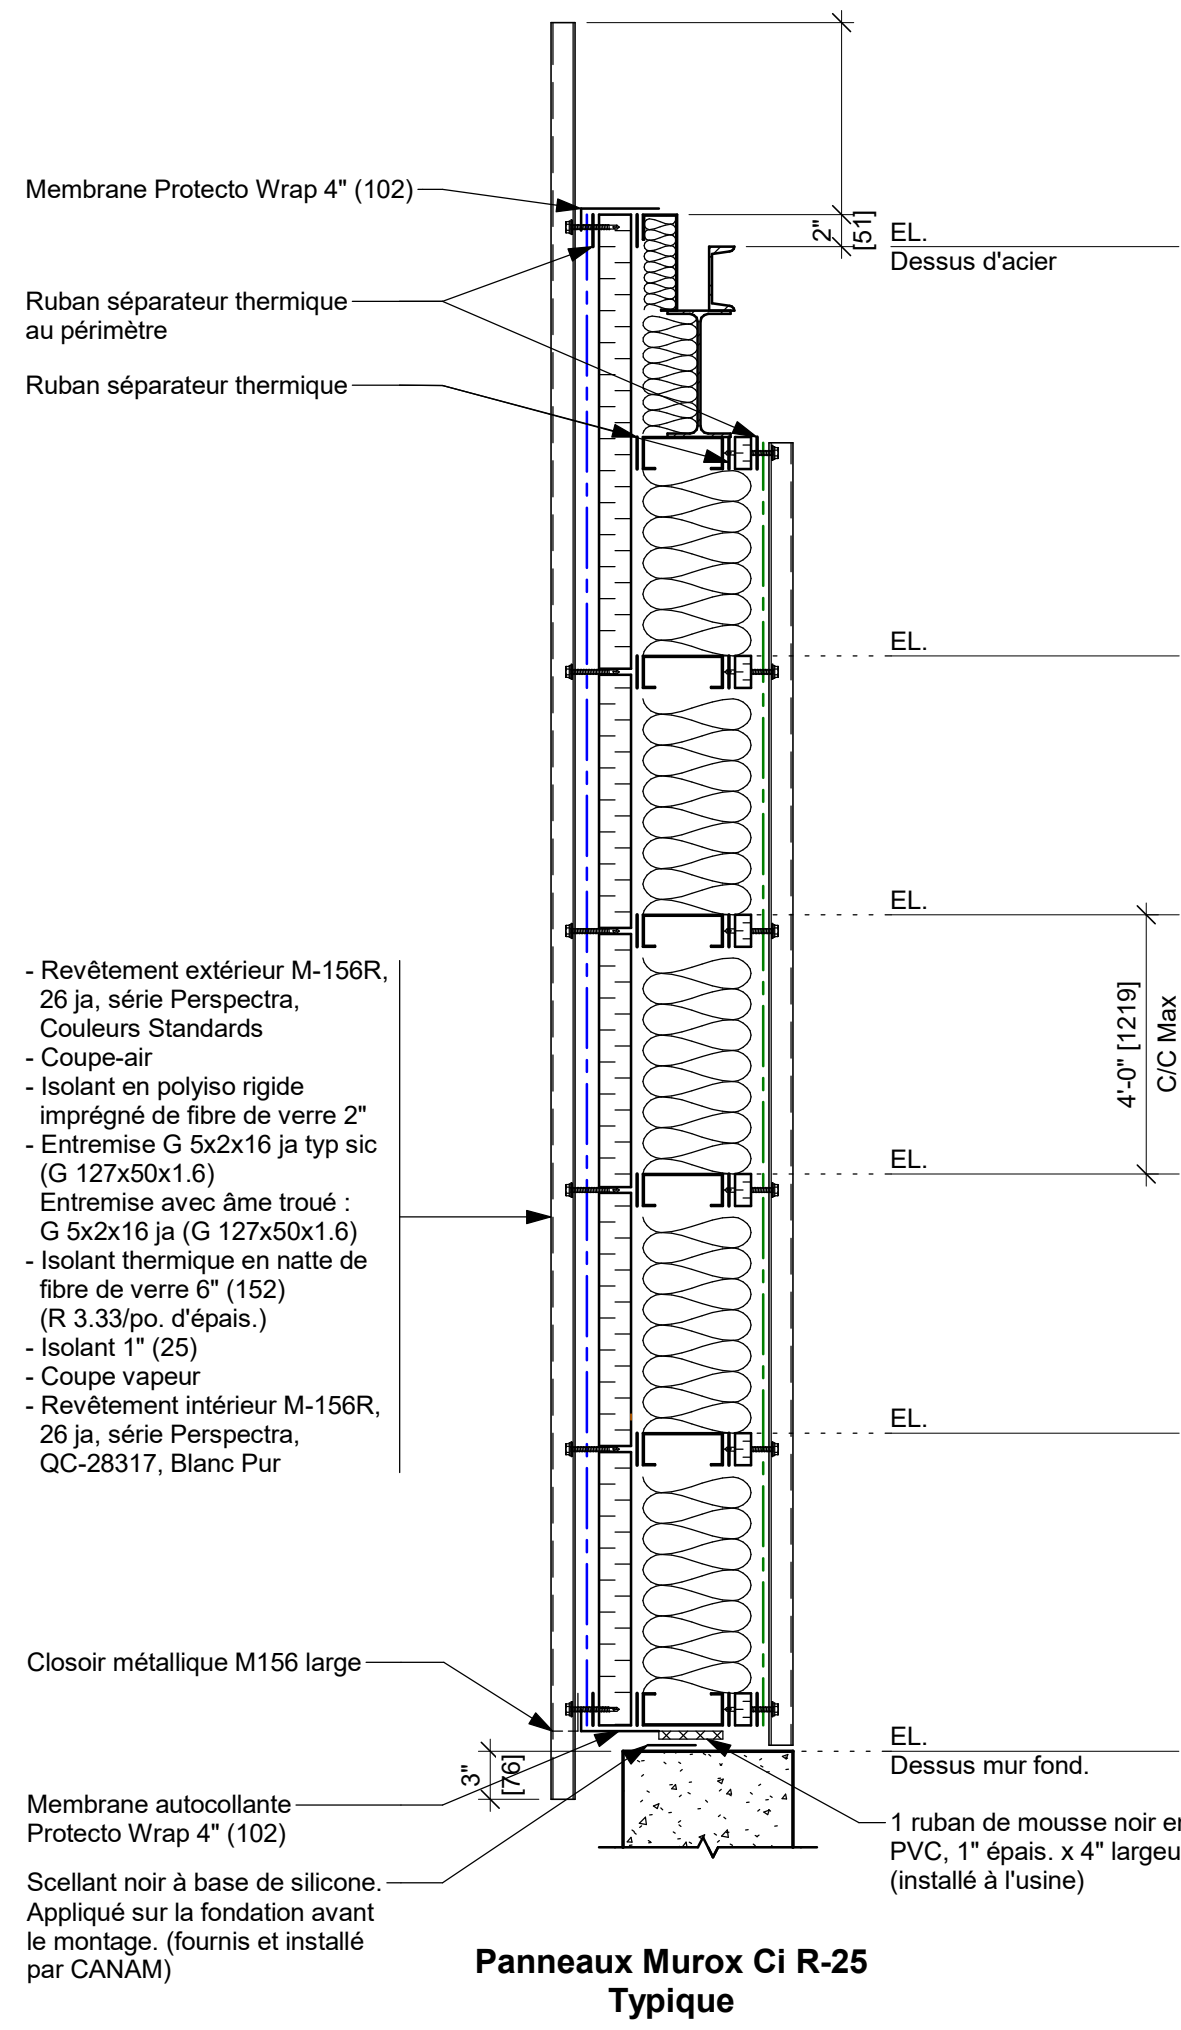

PRÉLIMINAIRE

NE DOIT PAS SERVIR À LA CONSTRUCTION

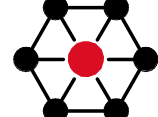REVISION	DATE	DESCRIPTION	DESS	VER		
GERANT DE PROJET						
		-				
		-				
		-				
		-				
DESSIN						
DESSINÉ PAR	CONÇU PAR	INGÉNIEUR DU PROJET	ÉCHELLE:			
INITIALE			Comme indiqué			
VERIFIÉ PAR	INGÉNIEURS CONSEILS / ARCHITECTES		DATE (mm/aaaa)			
			27/02/2026			
CLIENT: Toiture Summa						
CANAM 11505, 1re Avenue, bureau 500, Saint-Georges Beauce Québec, Canada, G5Y 7G3 Téléphone : (418) 228-8031 Sans frais : (877) 499-8049 www.canam.com						
SCAUX PROFESSIONNEL						
PROJET						
Entrepot E&G Saint-Lambert de Lauzon, Québec						
TITRE CROQUIS PRÉLIMINAIRE - ÉLEVATIONS, COUPES DE MUR ET CÉDULES						
NUMERO CONTRAT P2026-048	NUMERO DESSIN EsMx501	DIVISION	REVISION 