



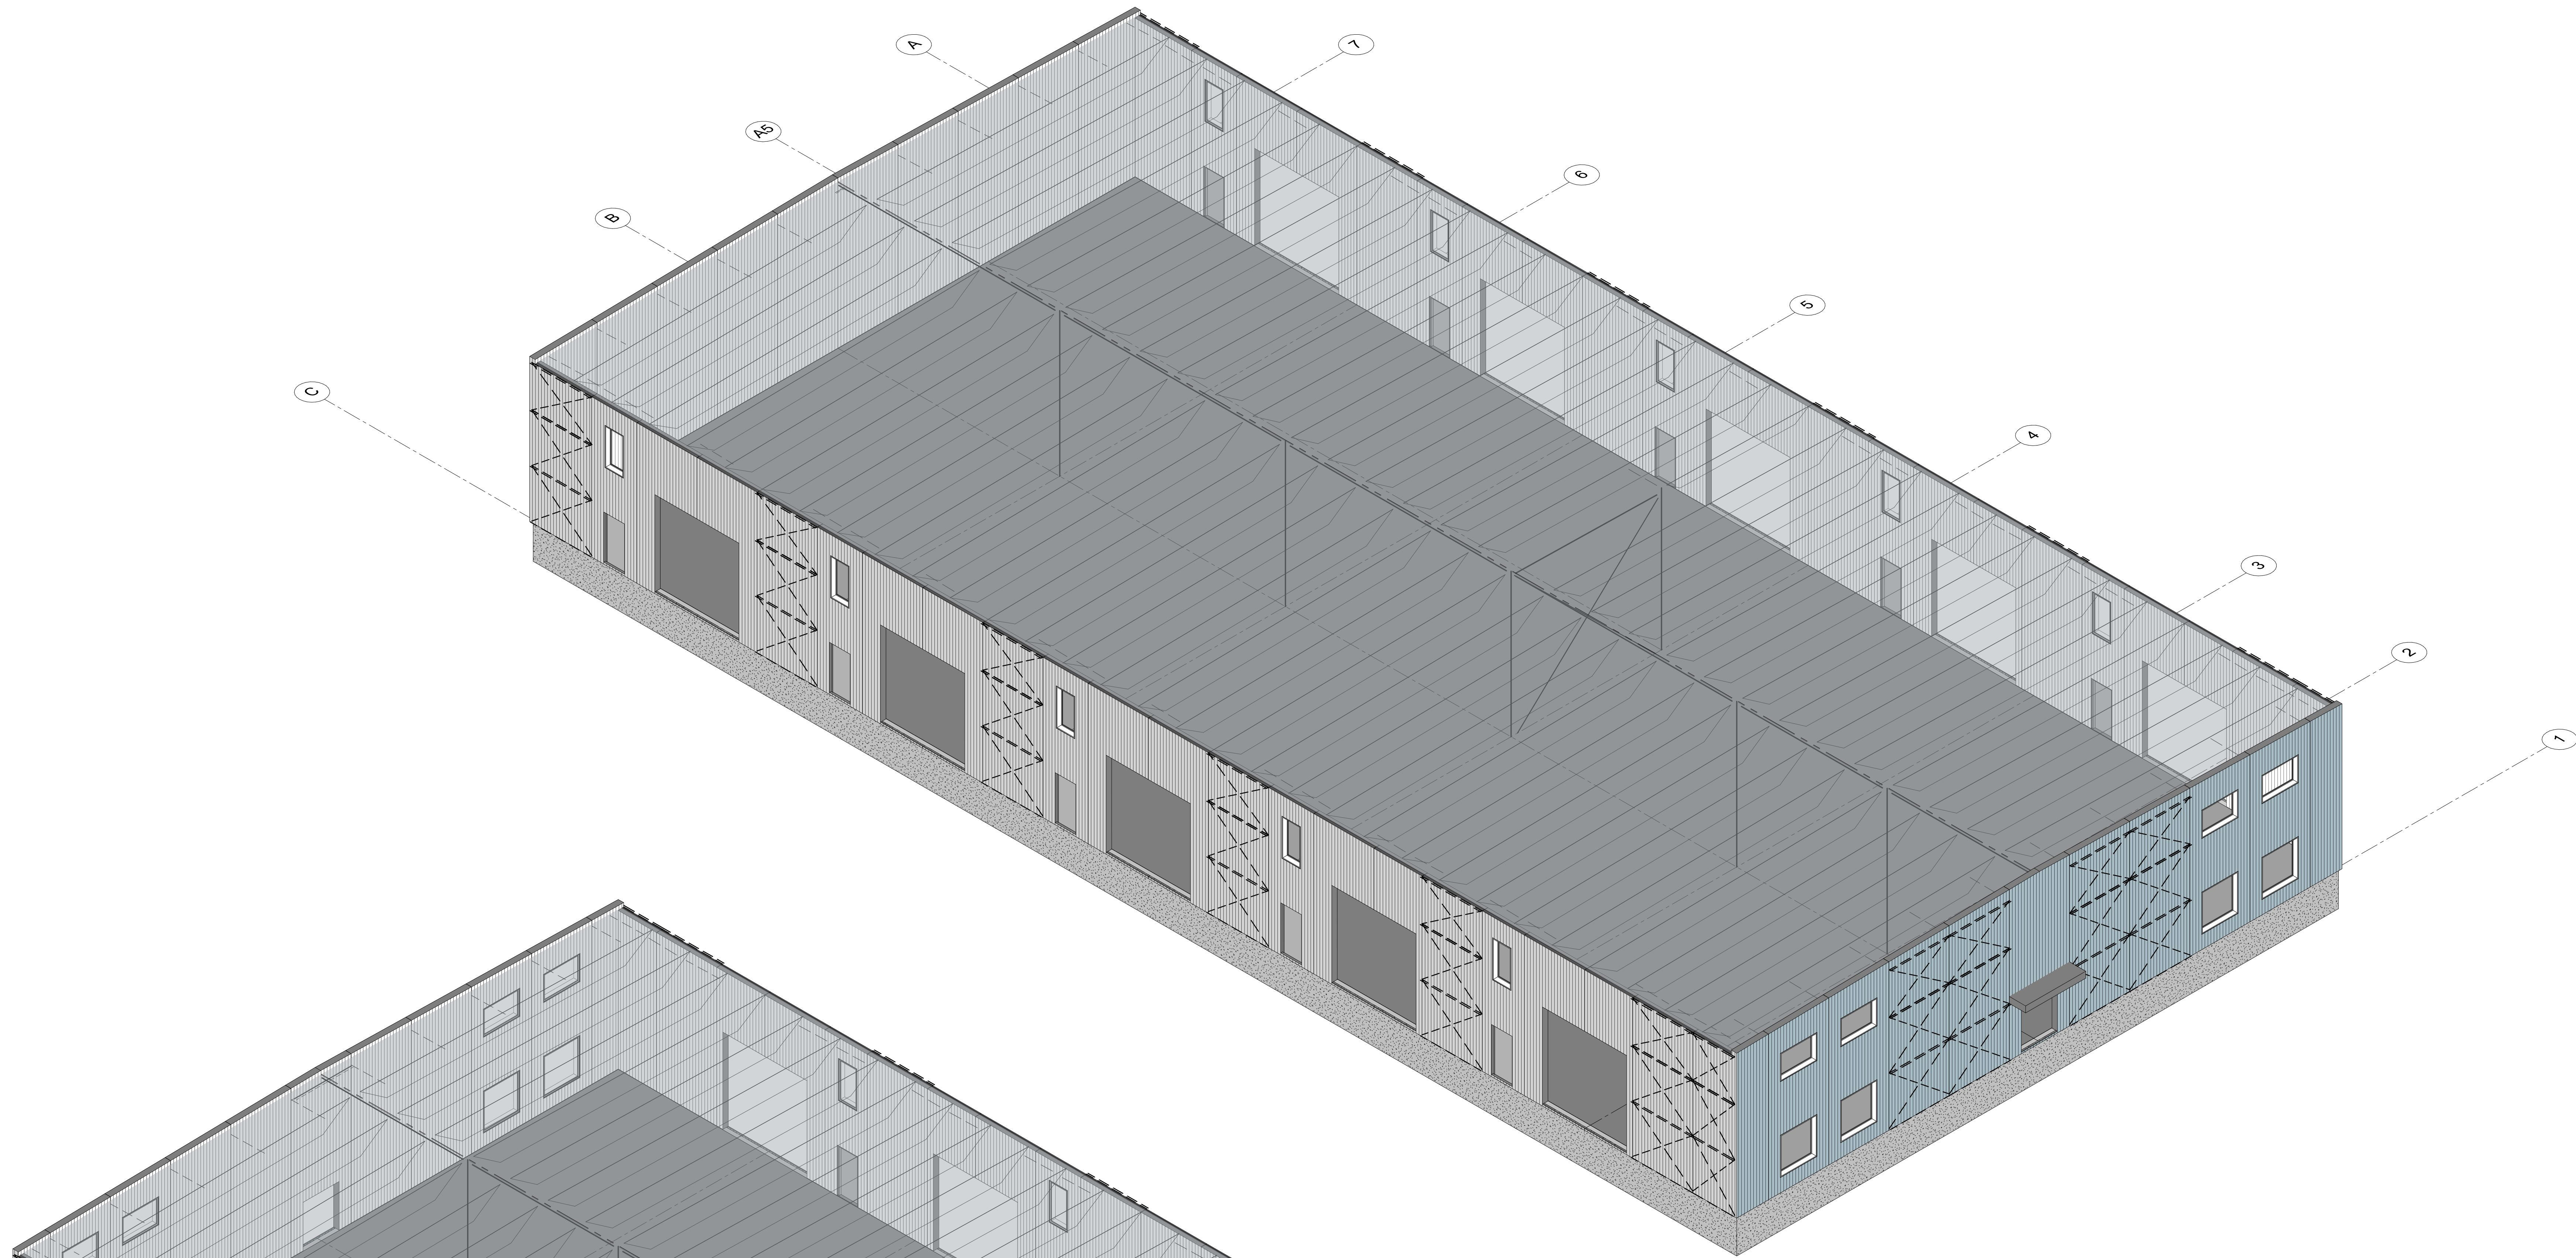

VUE 3D N-E

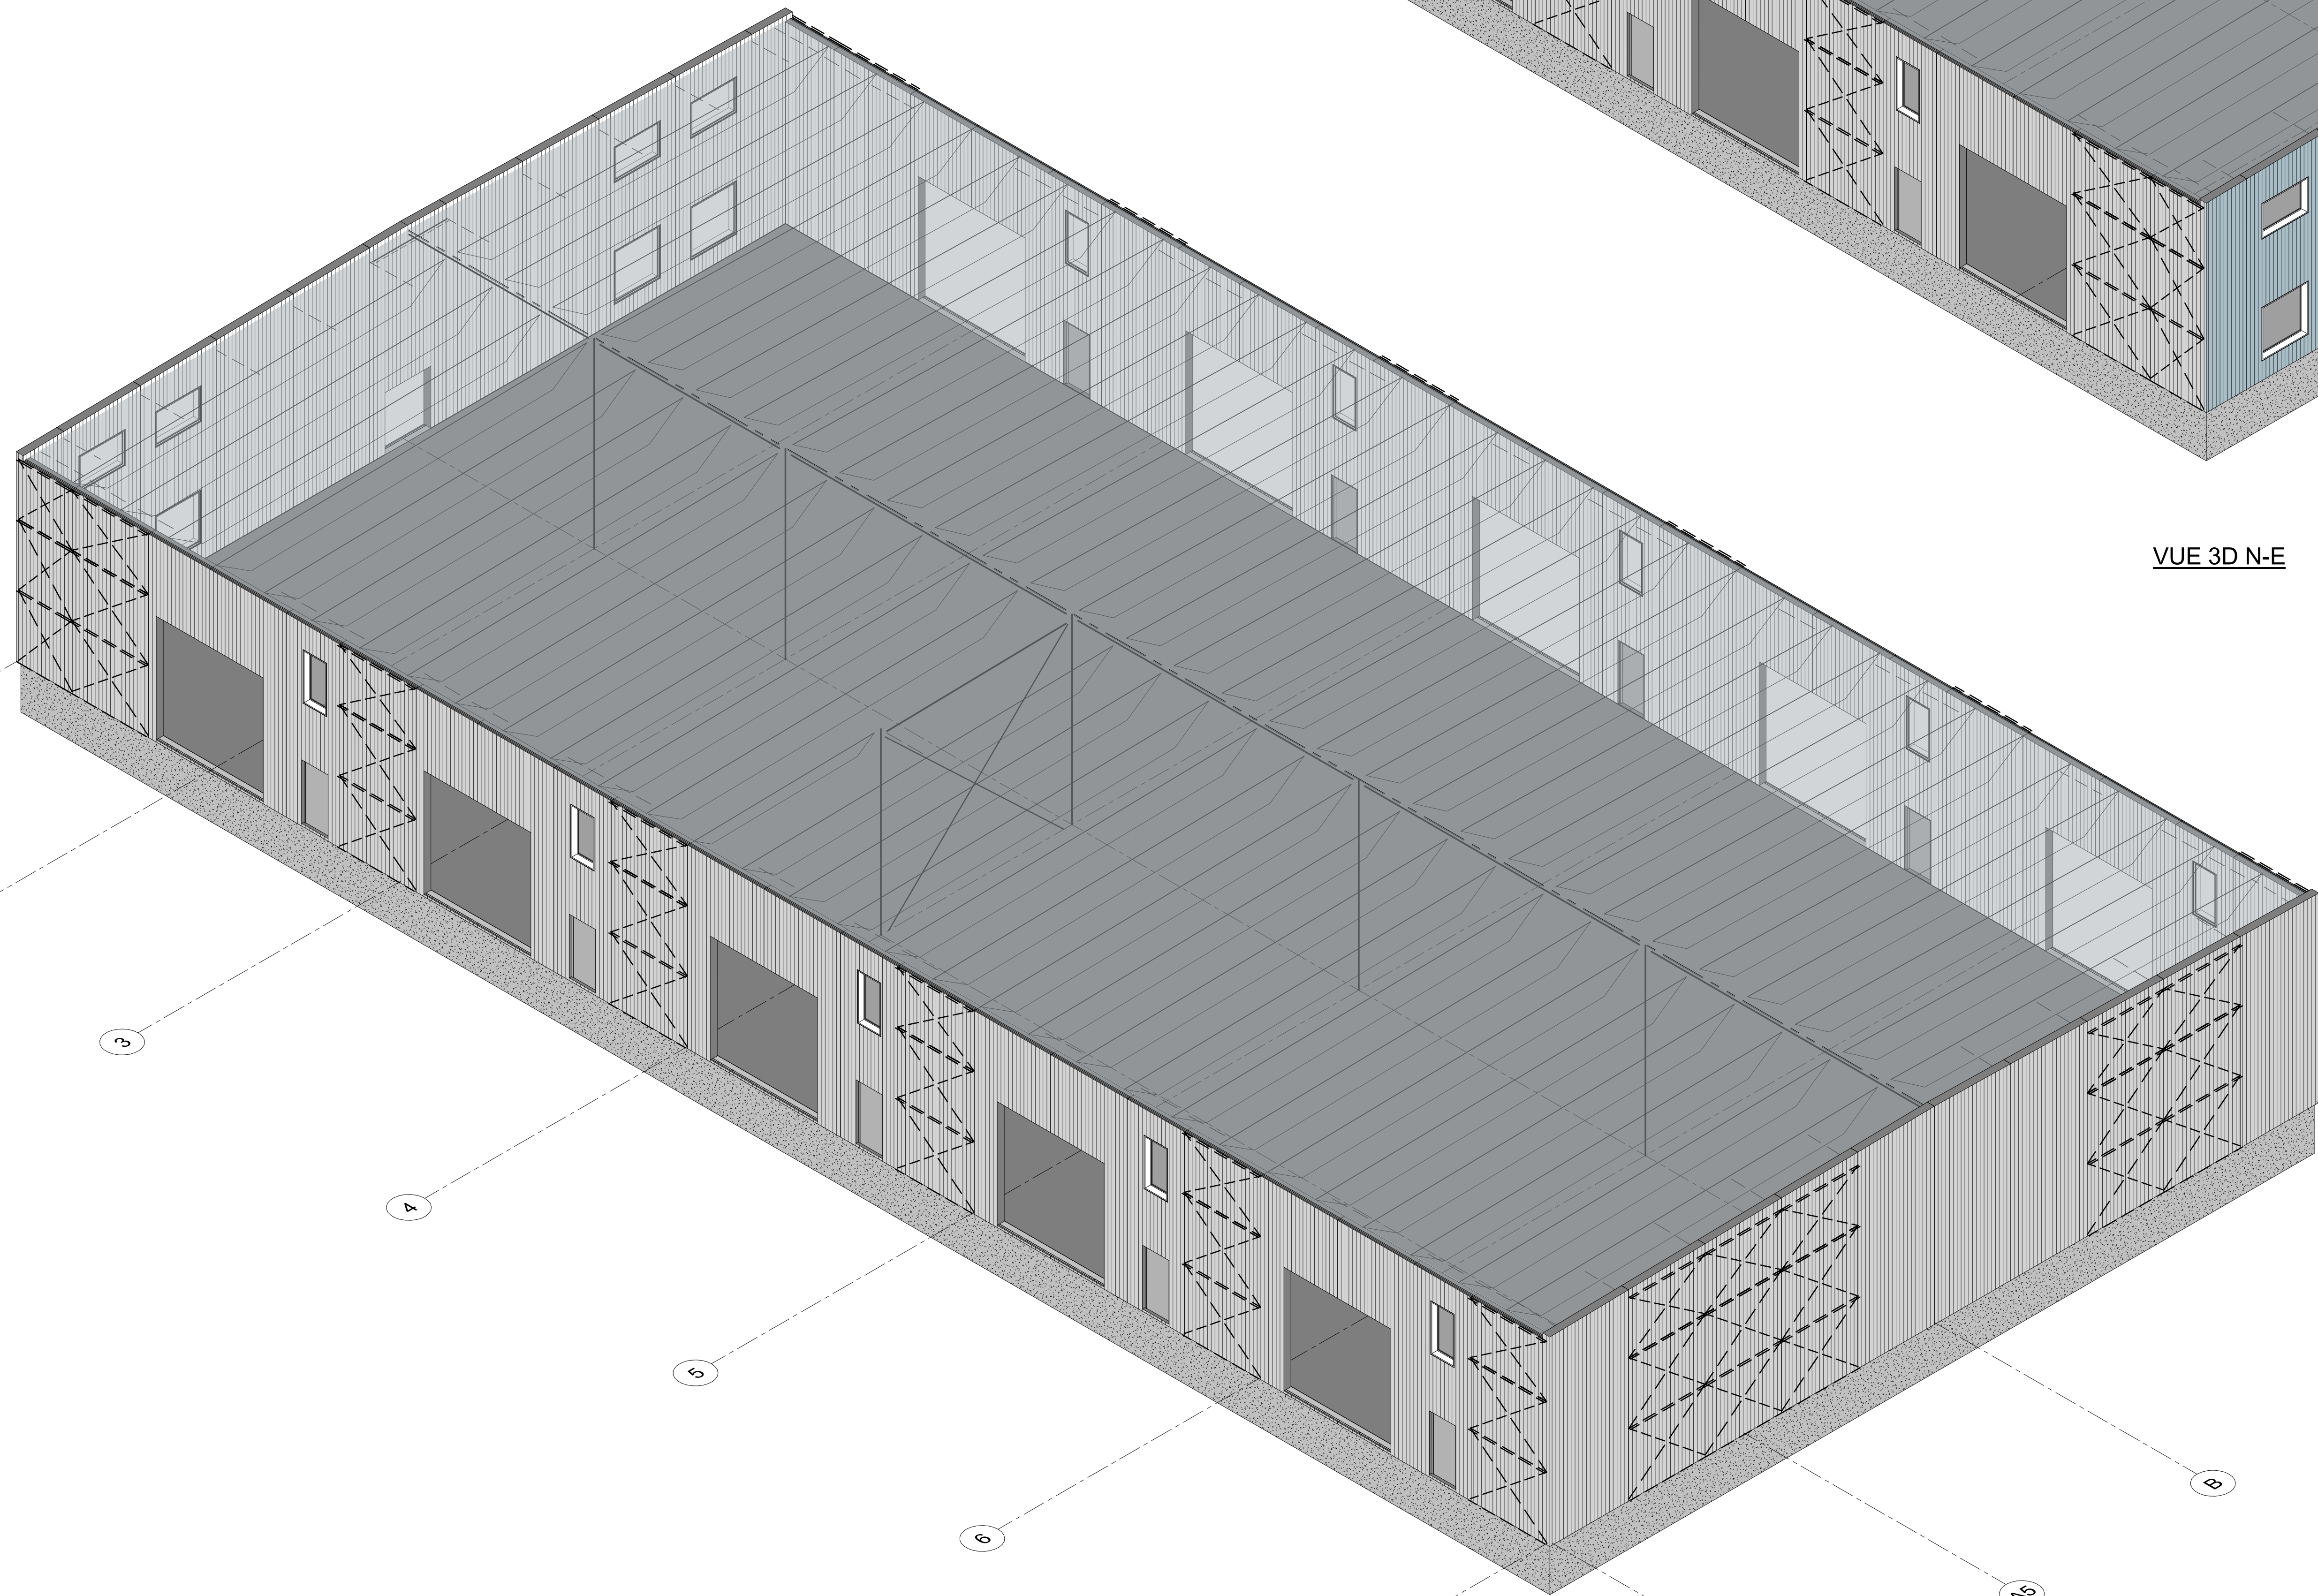

VUE 3D S-O

NOTE POUR LE CONTRACTEUR/ÉRECTEUR:  
IL EST STRICTEMENT DÉFENDU DE MODIFIER, COPIER, REPRODUIRE OU DE DISTRIBUER CES DESSINS OU QUELQUES REPRÉSENTATIONS DE CES DESSINS, PAR TOUTES SOURCES DE MÉDIA INCLUANT ÉLECTRONIQUEMENT, SANS L'APPROBATION ÉCRITE DE GROUPE CANAM INC.

| LISTE DES FEUILLES PRÉLIMINAIRES |                                                             |
|----------------------------------|-------------------------------------------------------------|
| EsMx001                          | CROQUIS PRÉLIMINAIRE - VUES 3D                              |
| EsMx001                          | CROQUIS PRÉLIMINAIRE - PLAN DE TOIT                         |
| EsMx001                          | CROQUIS PRÉLIMINAIRE - ÉLEVATIONS, COUPES DE MUR ET CÉDALES |

Cliquer ici pour modèle 3D

PRÉLIMINAIRE

NE DOIT PAS SERVIR À LA CONSTRUCTION

| REVISION | DATE | DESCRIPTION | DESS | VER |
|----------|------|-------------|------|-----|
|----------|------|-------------|------|-----|

|                  |   |
|------------------|---|
| GERANT DE PROJET | . |
|                  | . |
|                  | . |

DESSIN

| DESSIN PAR  | CONÇU PAR                         | INGÉNIEUR DU PROJET | ÉCHELLE |
|-------------|-----------------------------------|---------------------|---------|
| INITIALE    |                                   |                     |         |
| VERIFIÉ PAR | INGÉNIEURS CONSEILS / ARCHITECTES | DATE (mm/aaaa)      |         |
|             |                                   | 27/02/2026          |         |

CLIENT: Tollure Summa

**CANAM**  
11505, 1re Avenue, bureau 500, Saint-Georges Beaulac  
Québec, Canada, G3Y 7X3  
Téléphone : (418) 228-8031  
Sans frais : (877) 459-8049  
www.canam.com

SCAUX PROFESSIONNEL


PROJET

Entrepot E&G  
Saint-Lambert de Lauzon, Québec


TITRE

CROQUIS PRÉLIMINAIRE - VUES 3D

| NUMÉRO CONTRAT | NUMÉRO DESSIN | DIVISION | REVISION                                                                              |
|----------------|---------------|----------|---------------------------------------------------------------------------------------|
| P2026-048      | EsMx001       |          |  |

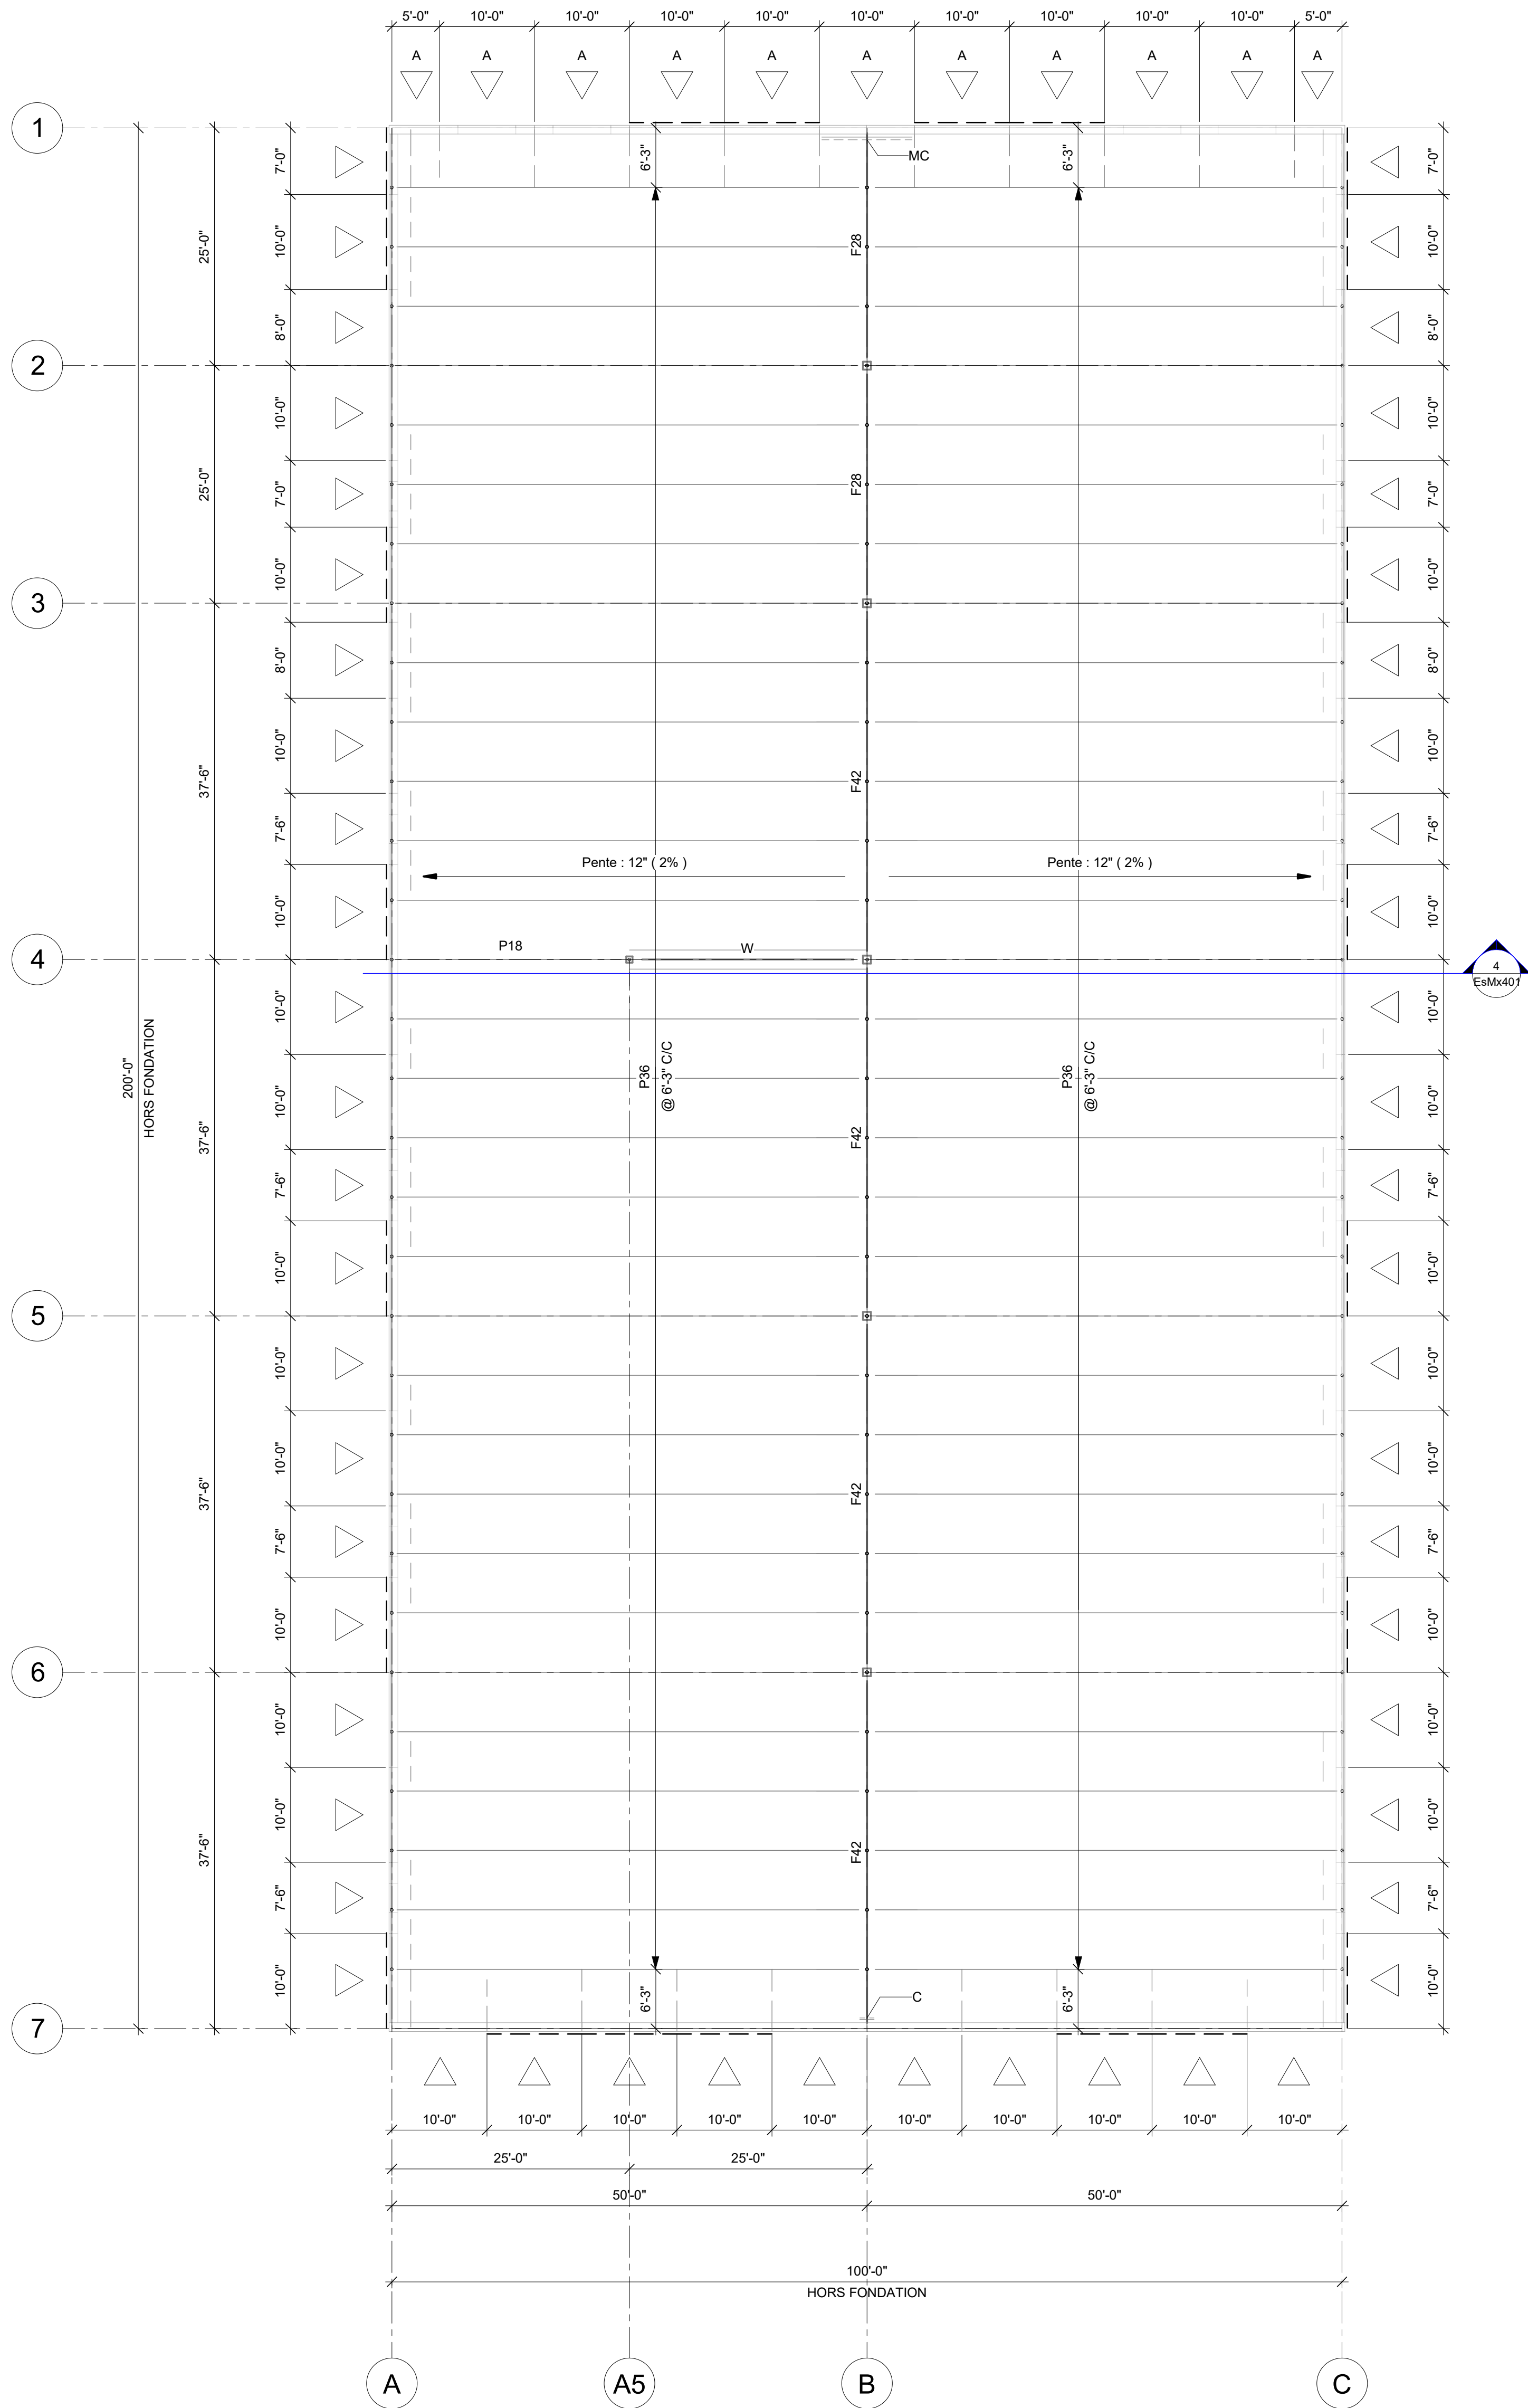

PLAN DE TOIT  
3/32" x 1'-0"

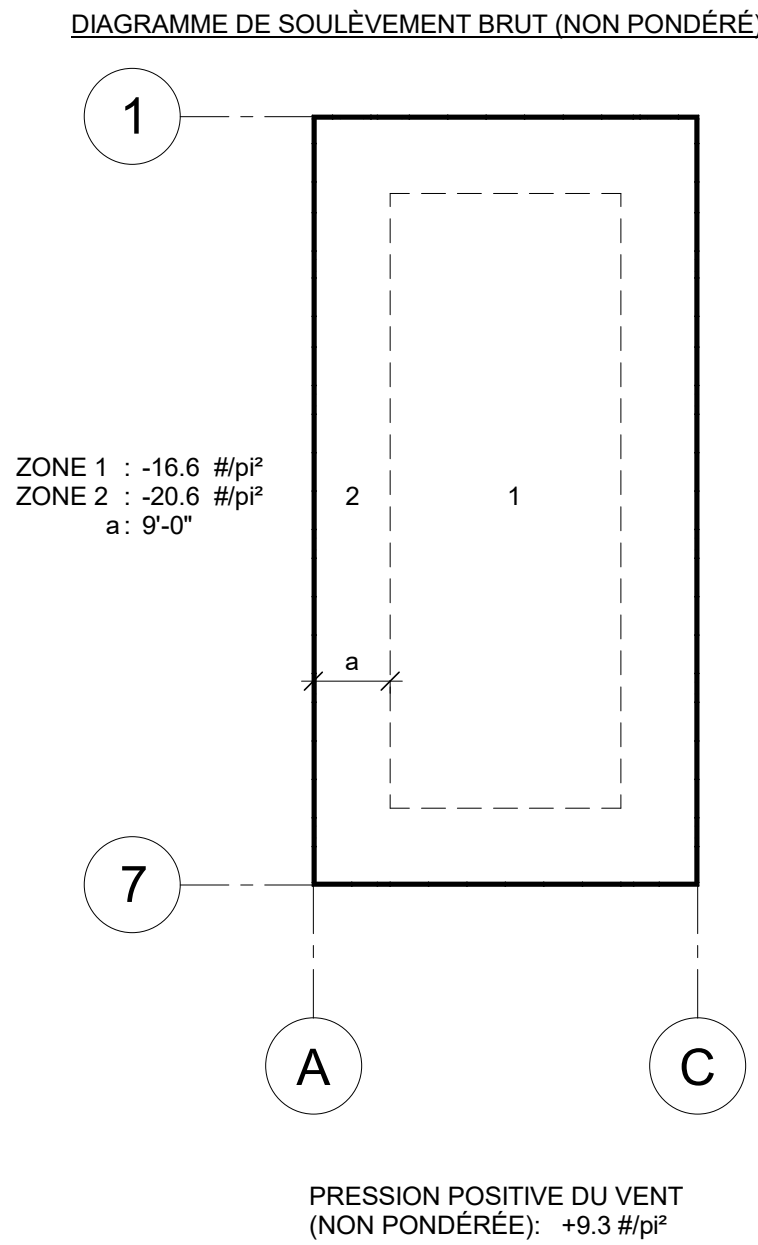

NOTE POUR LE CONTRACTEUR/ÉRECTEUR:

IL EST STRICTEMENT DÉFENDU DE MODIFIER, COPIER, REPRODUIRE OU DE DISTRIBUER CES DESSINS OU QUELQUES REPRÉSENTATIONS DE CES DESSINS, PAR TOUTES SOURCES DE MÉDIA INCLUANT ÉLECTRONIQUEMENT, SANS L'APPROBATION ÉCRITE DE GROUPE CANAM INC.

TOIT

|                              |            |
|------------------------------|------------|
| DESSUS DE PILASTRE DDP       | : 98'-0"   |
| DESSUS DE PILASTRE           | : 99'-0"   |
| DESSUS DE LA DALLE           | : 100'-0"  |
| DESSUS DE LA FONDATION       | : 100'-0"  |
| HAUTEUR LIBRE AXE A & C      | : 122'-10" |
| HAUTEUR LIBRE AXE B          | : 123'-10" |
| DESSUS D'ACIER AXE A & C     | : 123'-10" |
| DESSUS D'ACIER AXE B         | : 123'-10" |
| HAUTEUR DE PARAPET AXE A & C | : 0'-0"    |
| HAUTEUR DE PARAPET AXE 1 & 7 | : 0'-8"    |

CHARGES

|                                 |                           |
|---------------------------------|---------------------------|
| C.M.                            | : 16 lbs/p <sup>2</sup>   |
| C.M.                            | : 5 lbs/p <sup>2</sup>    |
| S <sub>u</sub>                  | : 75.2 lbs/p <sup>2</sup> |
| S <sub>u</sub>                  | : 8.36 lbs/p <sup>2</sup> |
| C <sub>u</sub> x C <sub>w</sub> | : 0.8                     |
| C.V. au toit                    | : 0 lbs/p <sup>2</sup>    |
| I <sub>u</sub>                  | : 1.0                     |
| Charge de neige au toit         | : 68.5 lbs/p <sup>2</sup> |
| I <sub>u</sub>                  | : 1.0                     |
| Vent q = 150                    | : 8.56 lbs/p <sup>2</sup> |

Séisme (Sol de classe D assumé)

|                       |          |
|-----------------------|----------|
| I <sub>e</sub>        | : 1.0    |
| S <sub>u</sub> (0.2)  | : 0.625  |
| S <sub>u</sub> (0.5)  | : 0.547  |
| S <sub>u</sub> (1.0)  | : 0.331  |
| S <sub>u</sub> (2.0)  | : 0.160  |
| S <sub>u</sub> (5.0)  | : 0.0452 |
| S <sub>u</sub> (10.0) | : 0.0143 |
| PGA                   | : 0.355  |
| PGV                   | : 0.384  |



CHARGES:

• Code Applicable : Code National du Bâtiment du Canada  
Code du bâtiment du Québec, dernières éditions adoptées  
Code de Pratique Standard ICCA.

• Type de sol assumé : classe D

• NOTE:

1. Si toutefois la catégorie d'emplacement devient E ou F selon le rapport géotechnique, le concept structural préliminaire (localisation et géométrie des contreventements, etc.) devra être validé et coordonné par l'ingénieur de Canam.

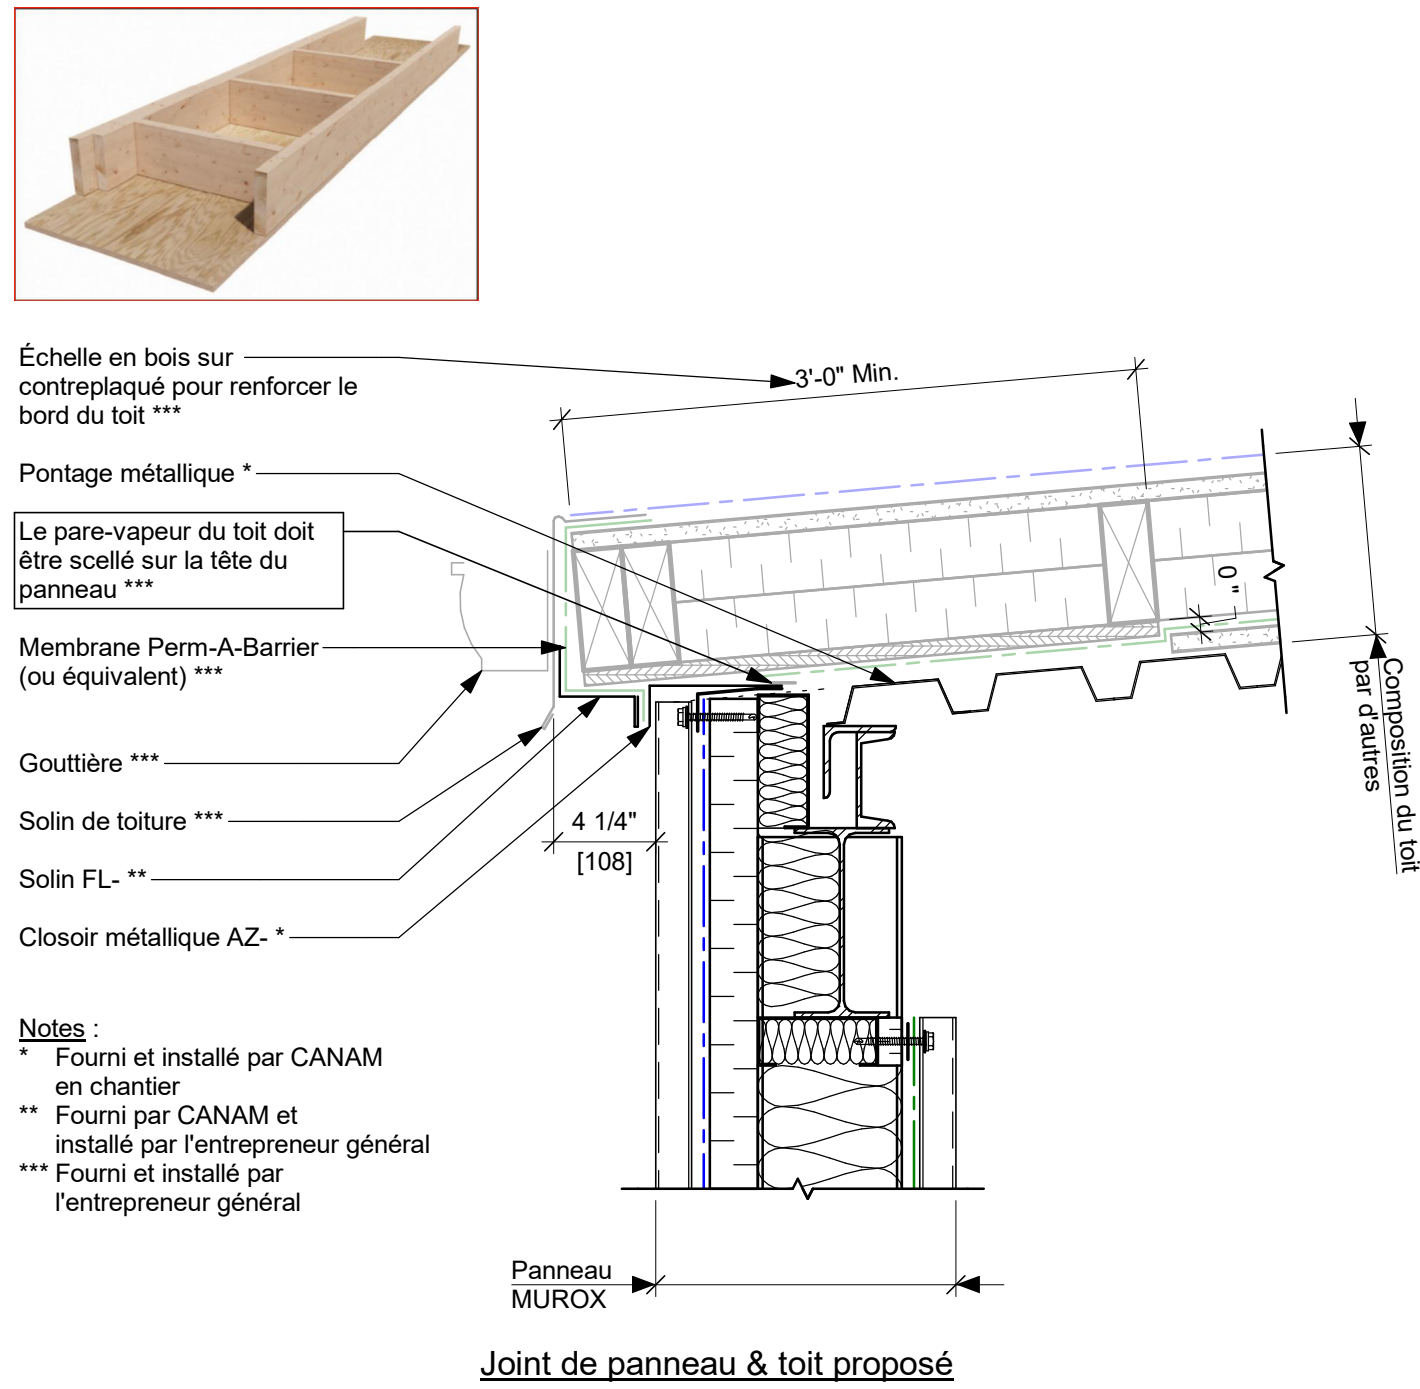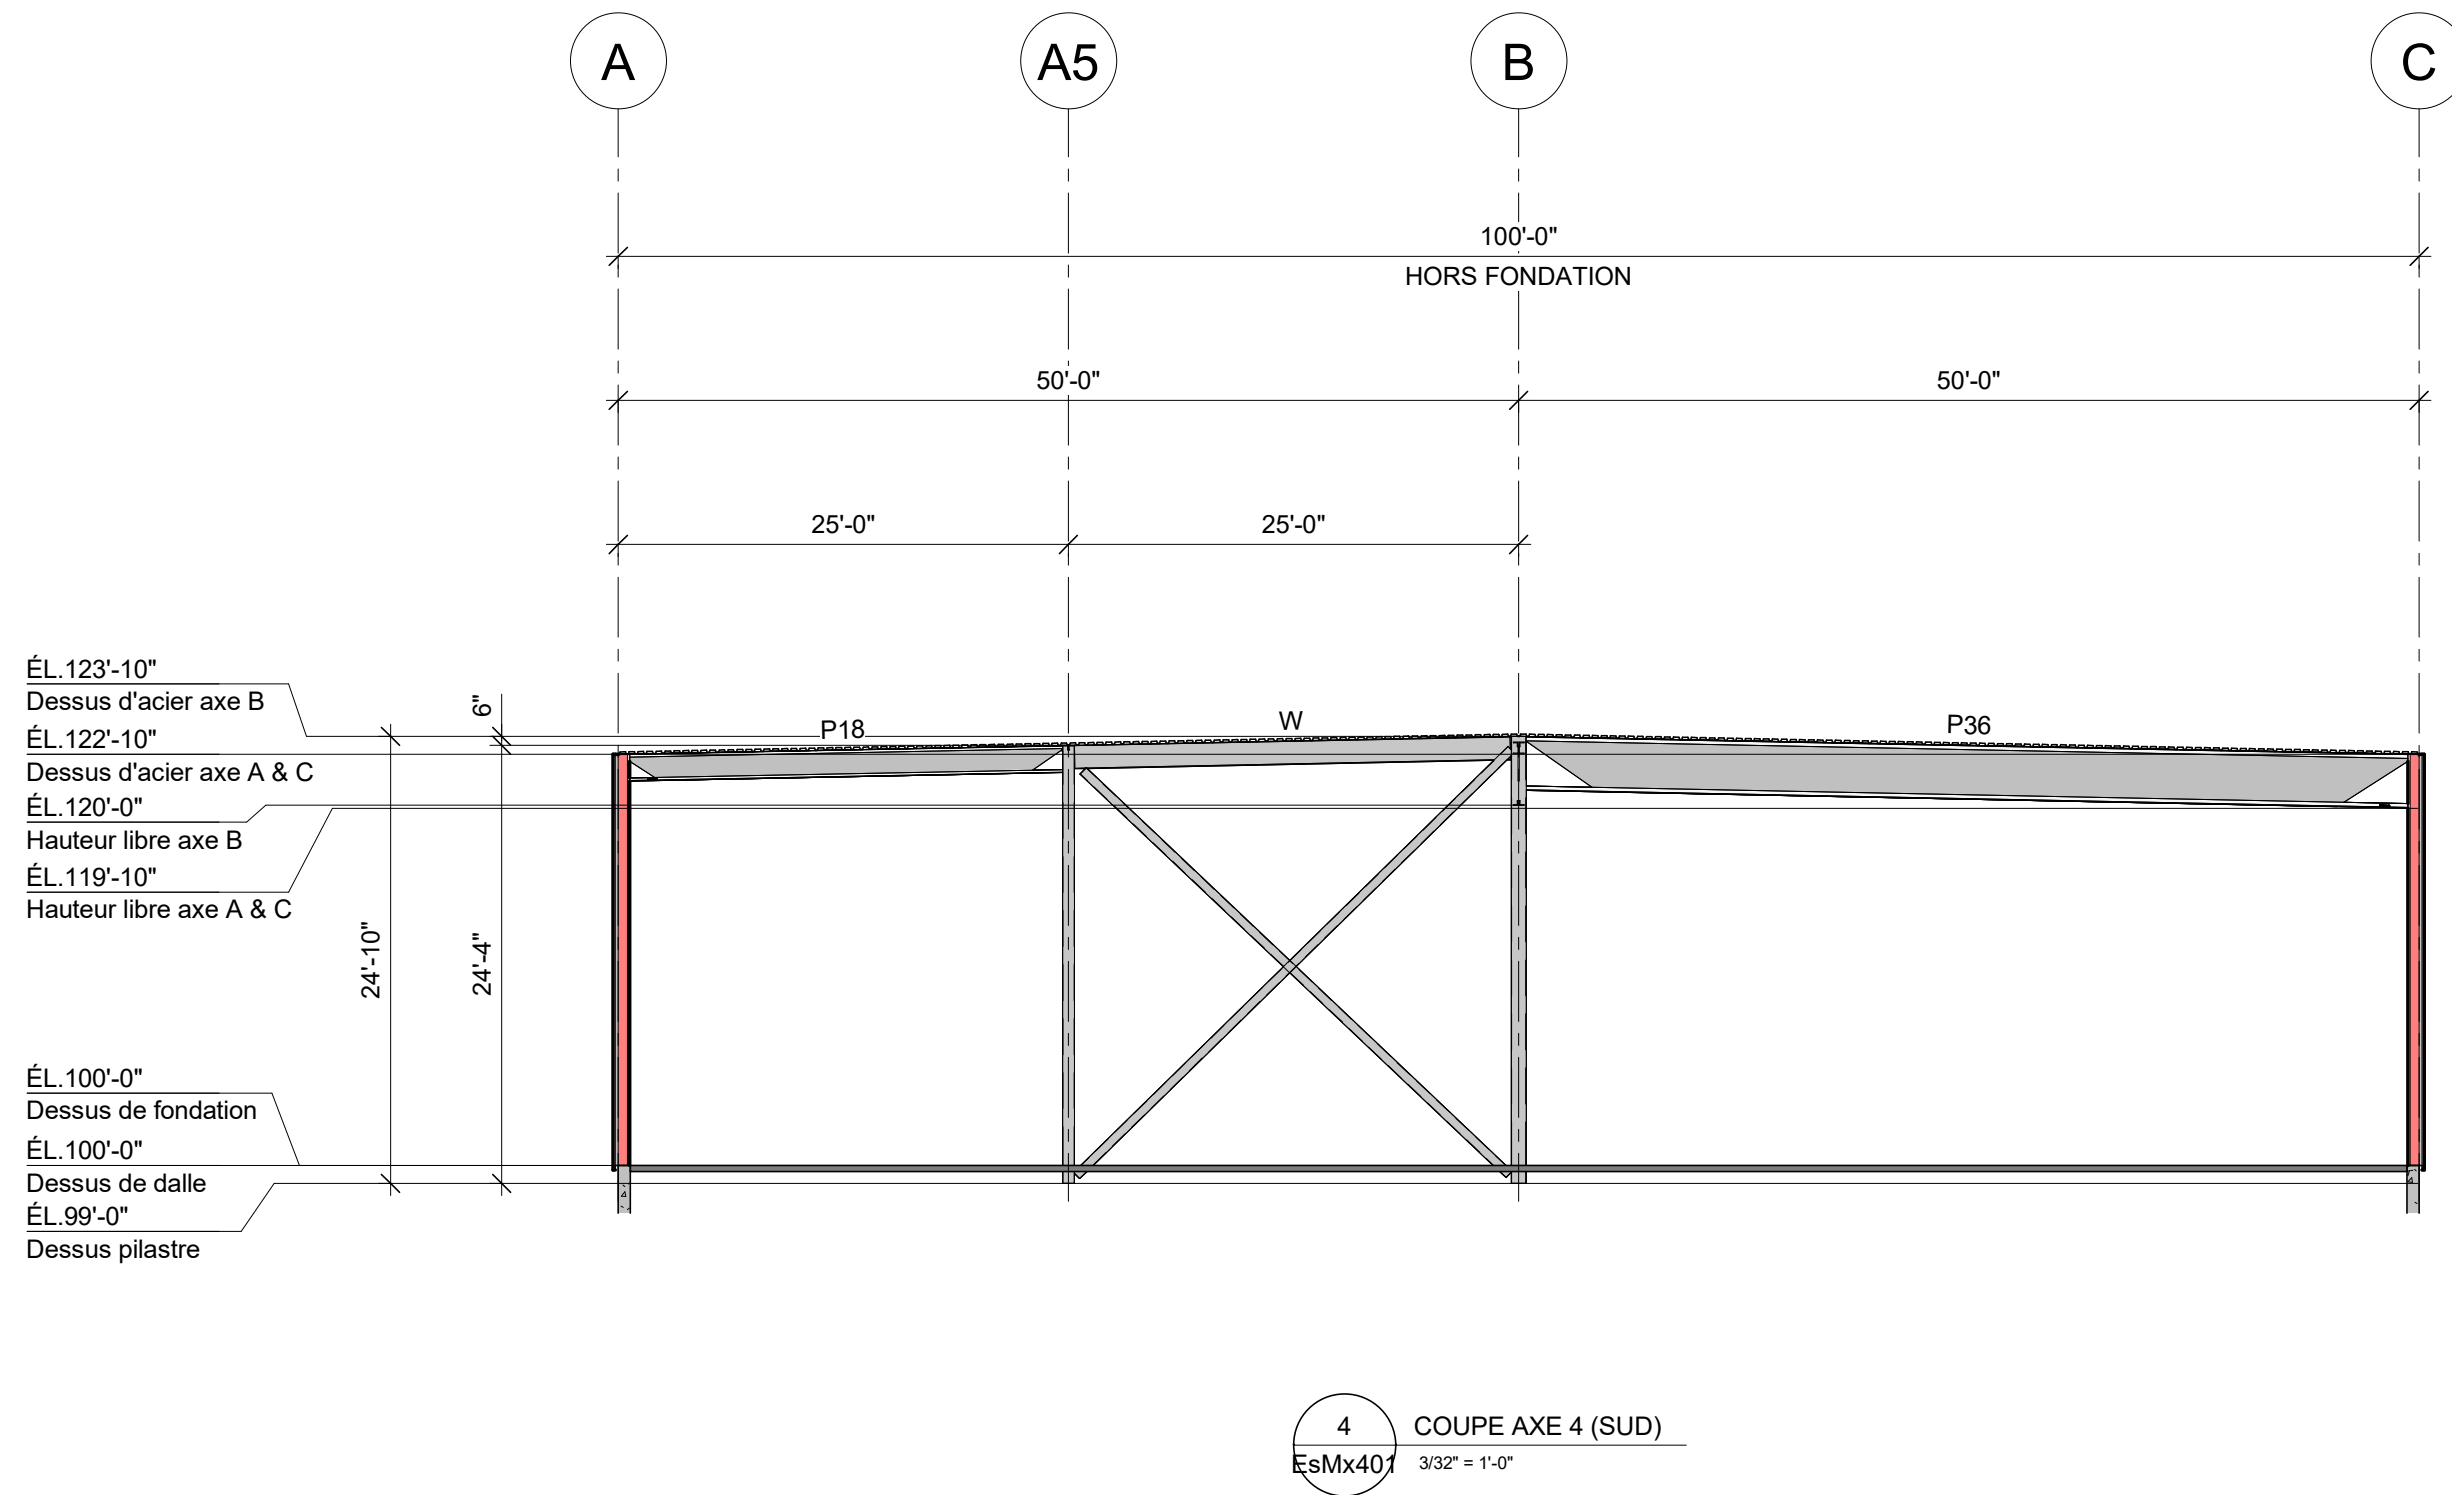

PRÉLIMINAIRE

NE DOIT PAS SERVIR À LA  
CONSTRUCTION

| REVISION         | DATE                              | DESCRIPTION         | DESS            | VER |
|------------------|-----------------------------------|---------------------|-----------------|-----|
| DESSIN DE PROJET |                                   |                     |                 |     |
|                  |                                   | -                   |                 |     |
|                  |                                   | -                   |                 |     |
|                  |                                   | -                   |                 |     |
| DESSIN           |                                   |                     |                 |     |
| DESSINÉ PAR      | CONÇU PAR                         | INGÉNIEUR DU PROJET | ÉCHELLE:        |     |
| INITIALE         |                                   |                     | Comme indiqué   |     |
| VERIFIÉ PAR      | INGÉNIEURS CONSEILS / ARCHITECTES |                     | DATE (mm/aaaa): |     |
|                  |                                   |                     | 27/02/2026      |     |

CLIENT: Toiture Summa



SCAUX PROFESSIONNEL

PROJET

Entrepot E&G  
Saint-Lambert de Lauzon, Québec

TITRE

CROQUIS PRÉLIMINAIRE - PLAN DE TOIT

| NUMÉRO CONTRAT | NUMÉRO DESSIN | DIVISION | REVISION |
|----------------|---------------|----------|----------|
| P2026-048      | EsMx401       |          |          |


Quincaillerie standard du fournisseur:  
- Chambrés : Stanley FBB179 4.5" x 4"  
- Barre panique : Von Duprin 22 x 689 avec poignée extérieure Z30L  
- Cylindre permanent : Schlage 2001C 686  
- Ferme-porte : LCN 1261 689  
- Coupe-froid de tête et des montants : Unique 1650  
- Coupe-froid du bas : Unique D54  
- Seuil : Voir la remarque dans la "Cédule de porte"

| CÉDULE DES FENÊTRES |     |              |                                                                                   |                                            |                                        |
|---------------------|-----|--------------|-----------------------------------------------------------------------------------|--------------------------------------------|----------------------------------------|
| Identifiant         | Qté | Installation | Description                                                                       | Dimensions ext. cadre<br>largeur X hauteur | Couleur du cadre                       |
| F1                  | 4   |              | Fenêtre en aluminium fixe avec bris thermique et verre scellé + Low-E argon clair | 6'-0" x 6'-0"                              | Cadre d'Aluminium (Blanc ext. et int.) |
| F2                  | 4   |              | Fenêtre en aluminium fixe avec bris thermique et verre scellé + Low-E argon clair | 6'-0" x 4'-0"                              | Cadre d'Aluminium (Blanc ext. et int.) |
| F3                  | 10  |              | Fenêtre en aluminium fixe avec bris thermique et verre scellé + Low-E argon clair | 5'-0" x 6'-0"                              | Cadre d'Aluminium (Blanc ext. et int.) |


| CÉDULE DES PORTES |     |              |                 |               |           |         |         |                                          |                          |                    |                                      |                                      |                                    |       |
|-------------------|-----|--------------|-----------------|---------------|-----------|---------|---------|------------------------------------------|--------------------------|--------------------|--------------------------------------|--------------------------------------|------------------------------------|-------|
| Identifiant       | Qté | Installation | Porte 18 ja.    |               | Sens ouv. | Vitrage |         | Cadre d'acier 16 ja. avec bris thermique | (3) Pentures @ type fixe | Poignées seulement | Barre panique sans poignée ext. ZZE0 | Quincaillerie                        |                                    |       |
|                   |     |              | Isolation (RT2) | Dimensions    |           | Largeur | Hauteur |                                          |                          |                    |                                      | Barre panique avec poignée ext. Z30L | Verrou en surface (Porte inactive) | Seuil |
| F1                | 10  |              |                 | 3'-0" x 7'-0" |           |         |         |                                          |                          |                    |                                      |                                      |                                    |       |

| CÉDULE DES P.M. ET DES OUVERTURES |                 |     |              |
|-----------------------------------|-----------------|-----|--------------|
| Total                             | Type            | Tag | Commentaires |
| 1                                 | 6'-0" x 7'-0"   | OUV |              |
| 10                                | 14'-0" x 14'-0" | PM  |              |
| Total général: 11                 |                 |     |              |


NOTE POUR LE CONTRACTEUR/ÉRECTEUR:  
IL EST STRICTEMENT DÉFENDU DE MODIFIER, COPIER, REPRODUIRE OU DE DISTRIBUER CES DESSINS OU QUELQUES REPRÉSENTATIONS DE CES DESSINS, PAR TOUTES SOURCES DE MÉDIA INCLUANT ÉLECTRONIQUEMENT, SANS L'APPROBATION ÉCRITE DE GROUPE CANAM INC.

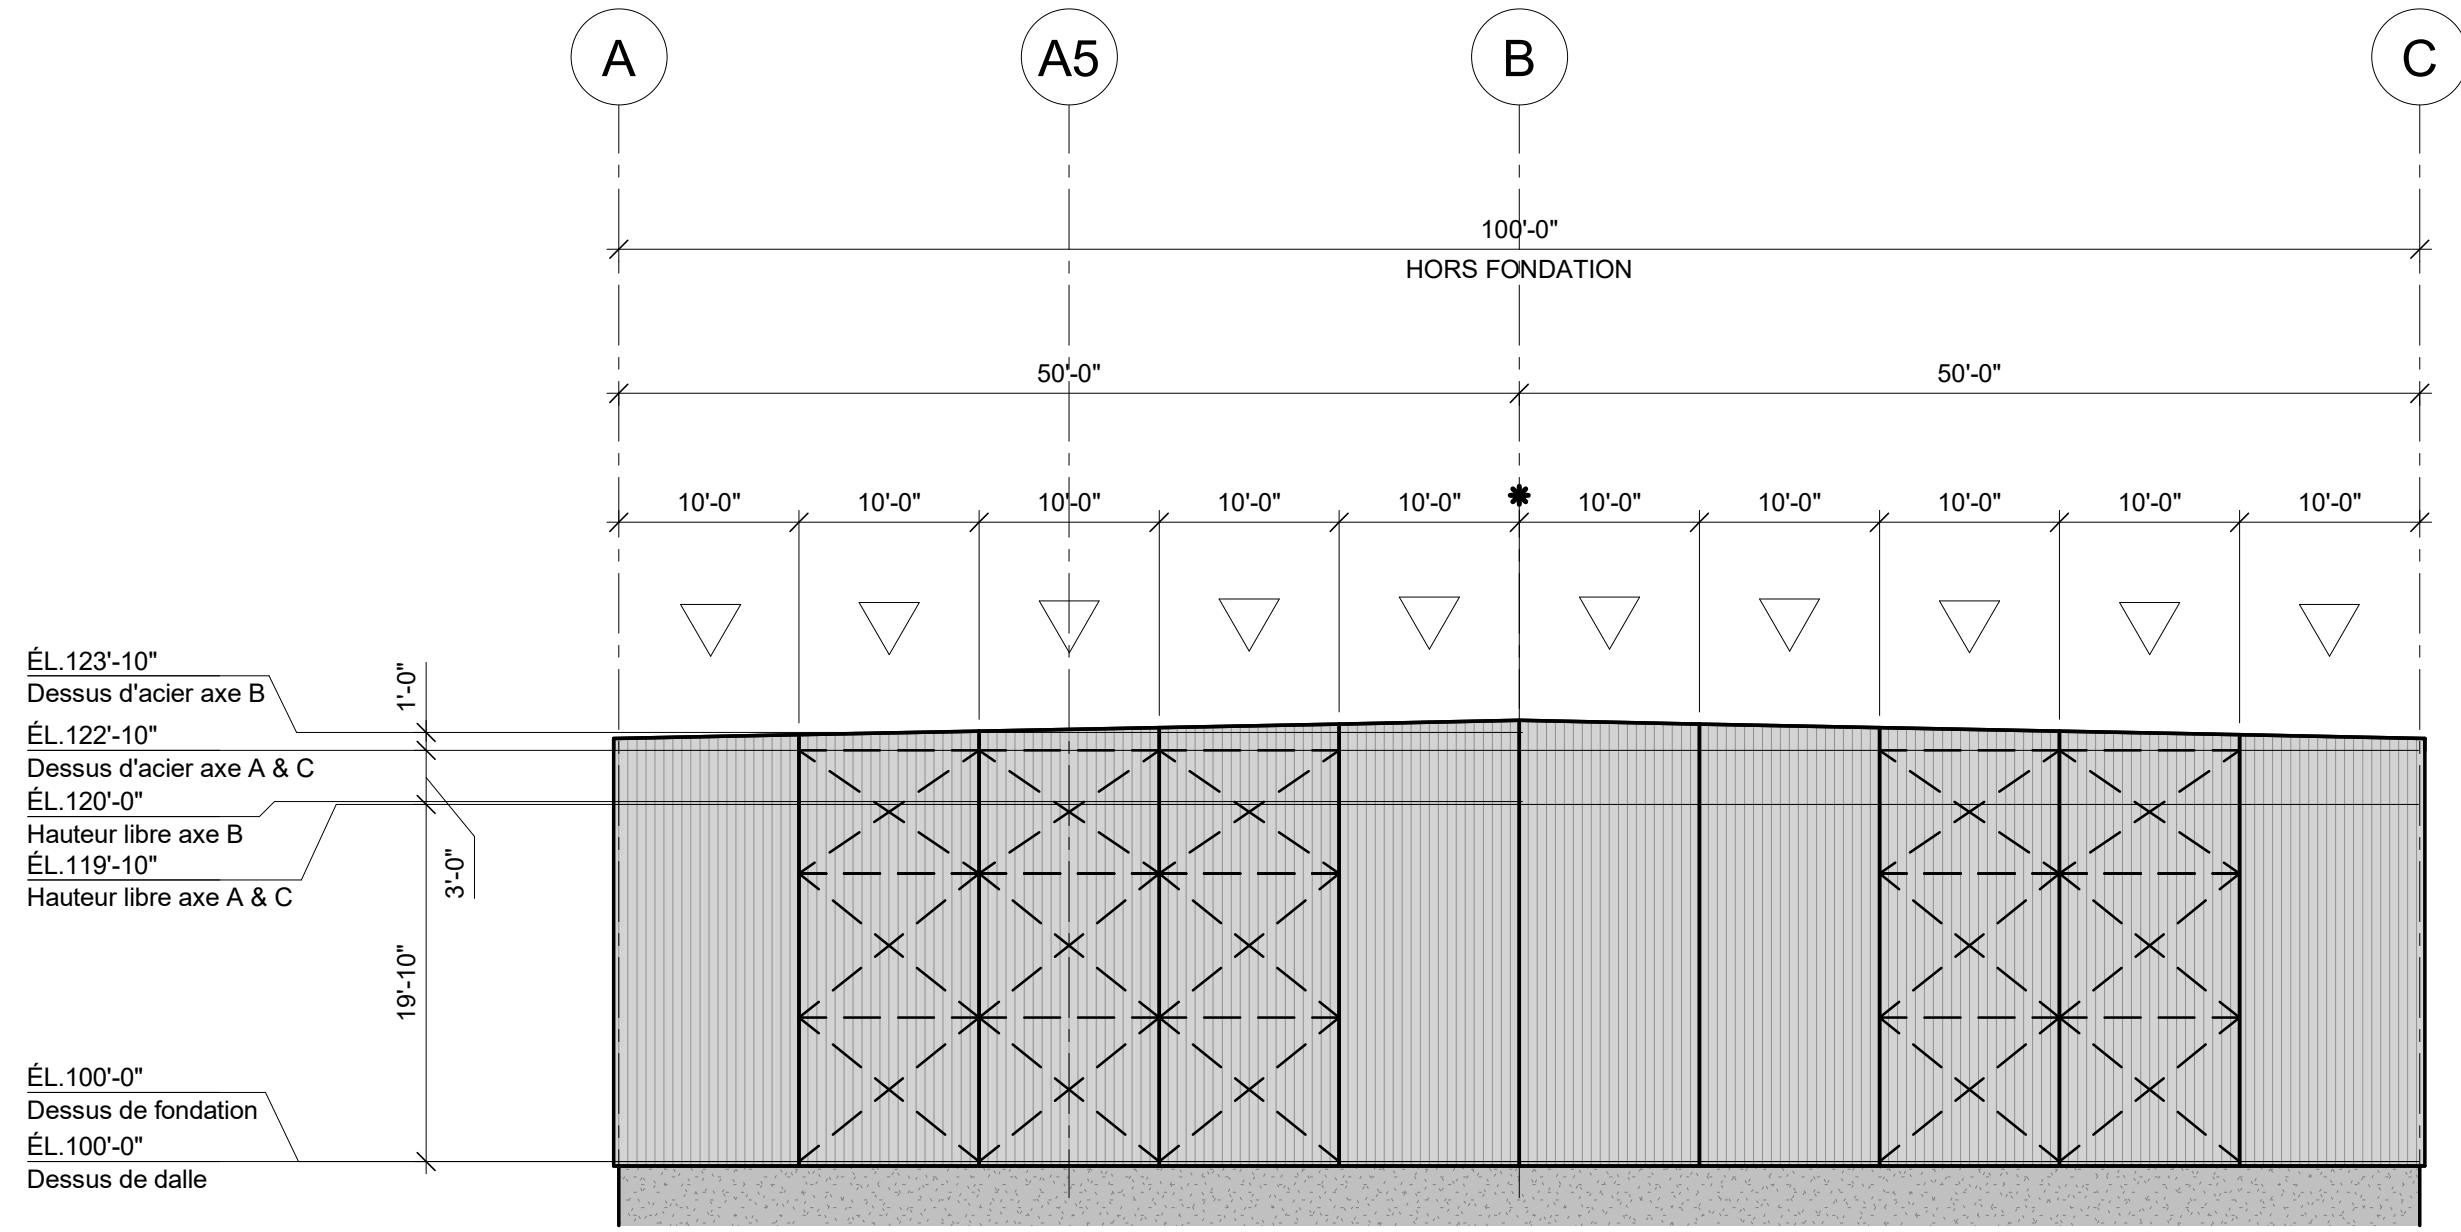


ÉLEVATION AXE 7 (SUD)  
3/32" = 1'-0"

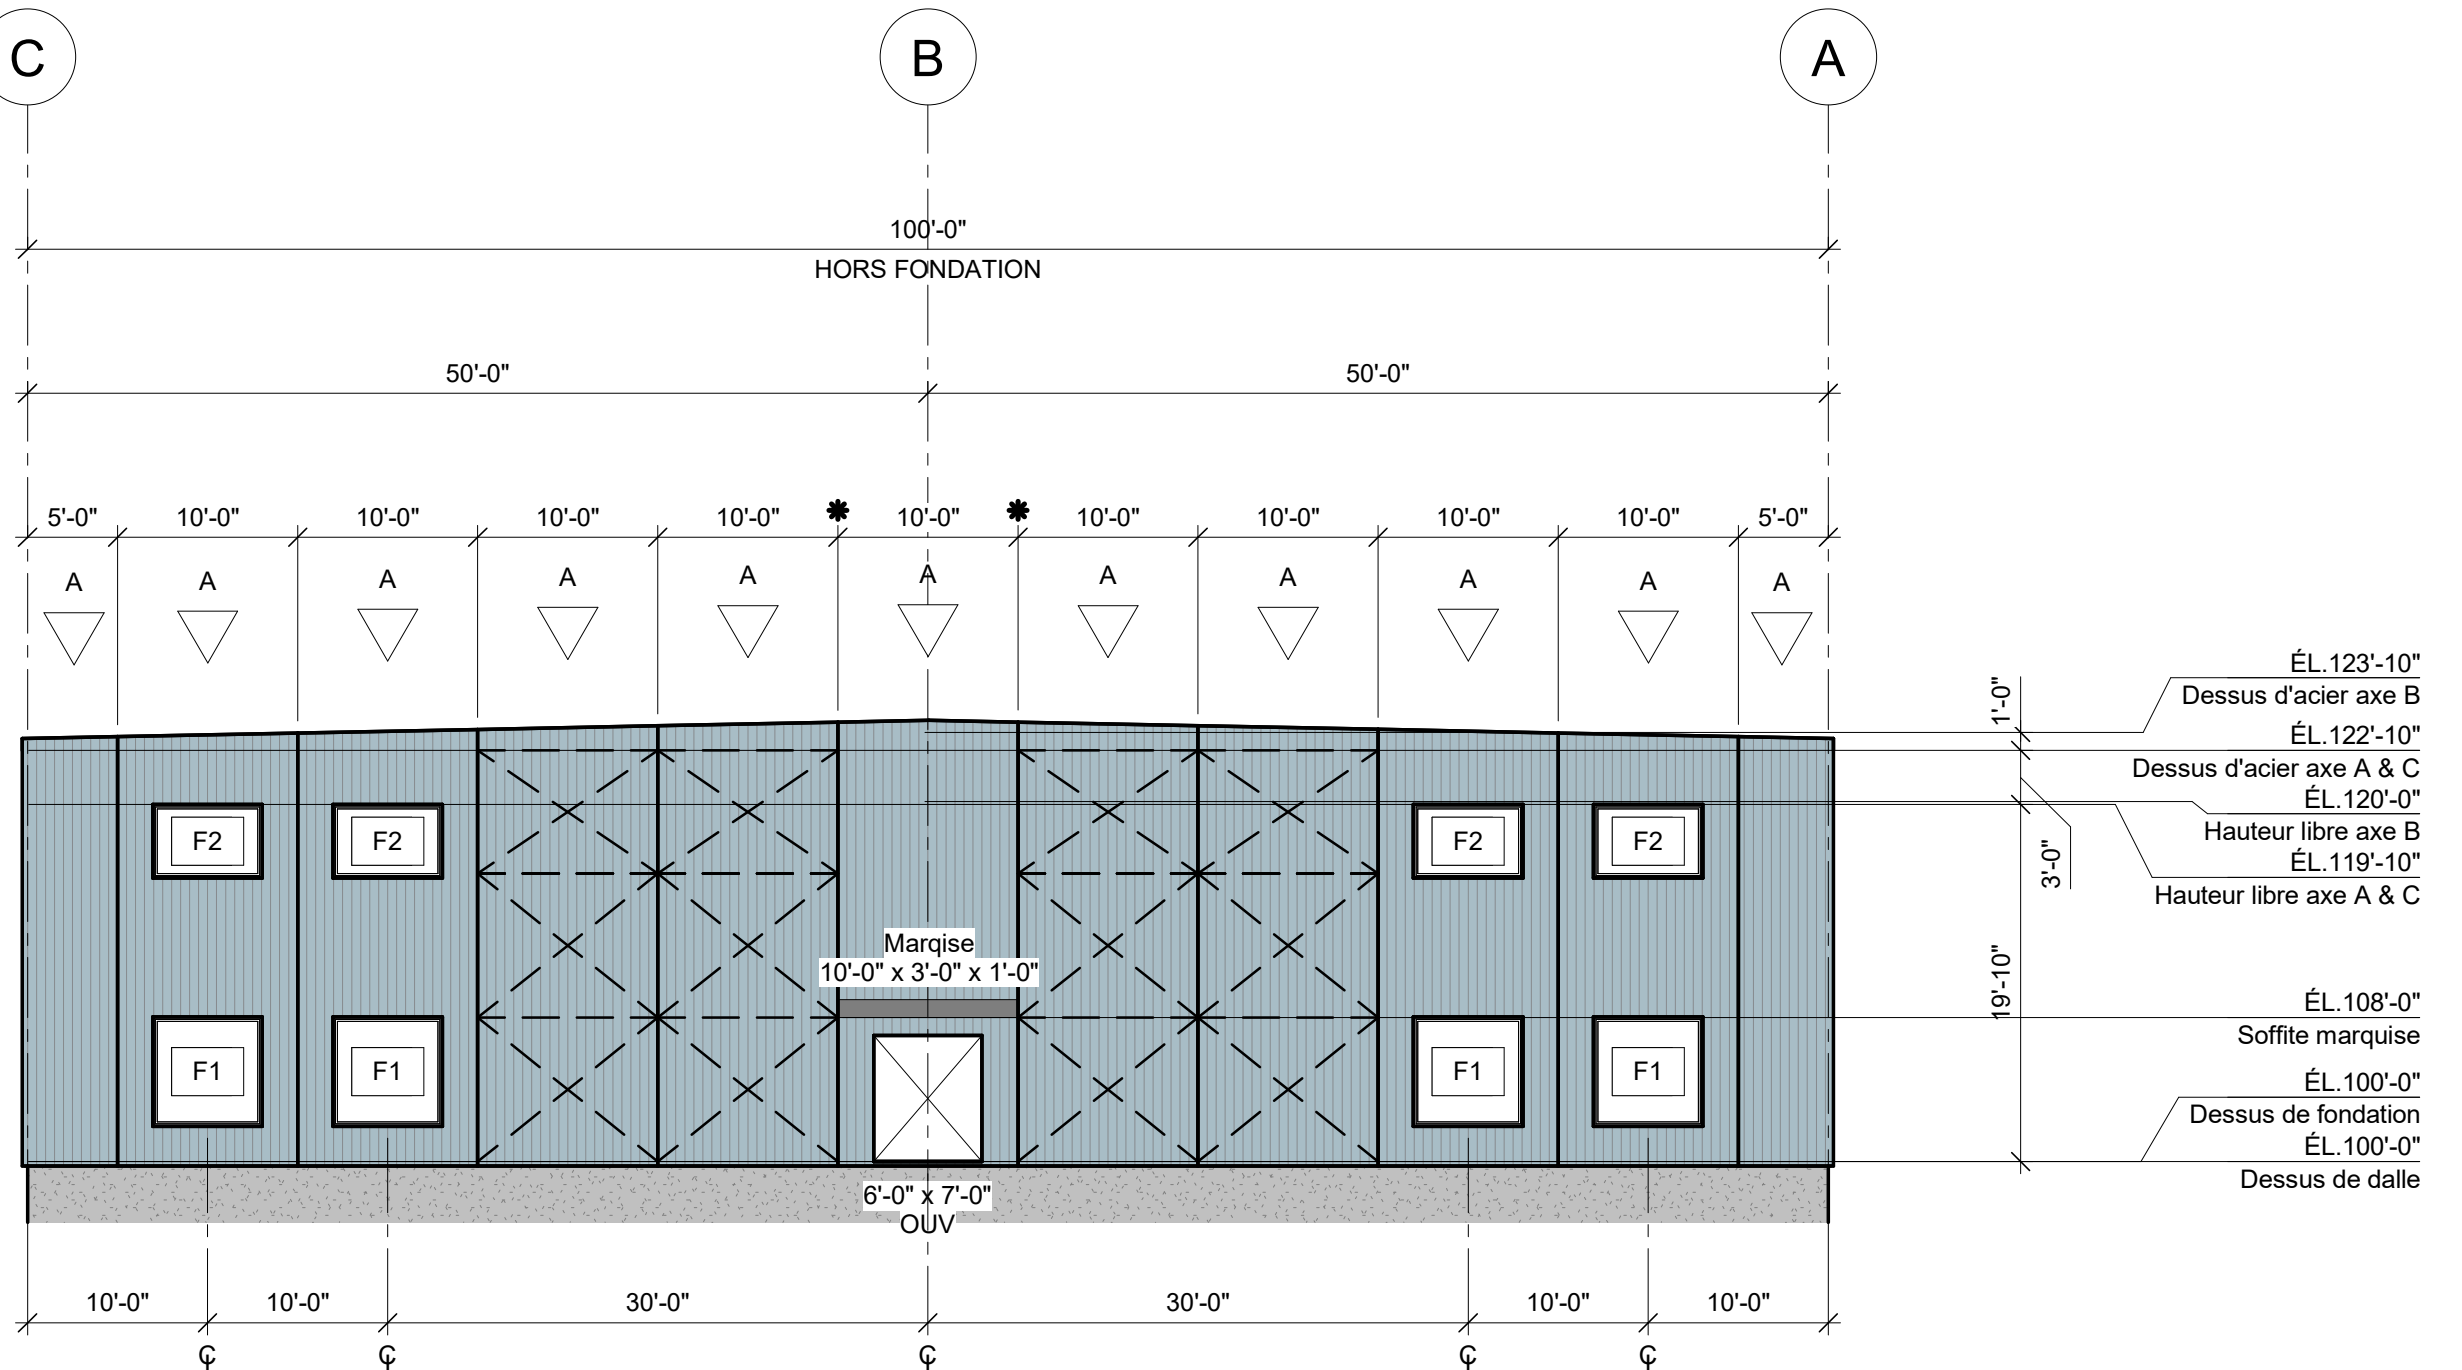



ÉLEVATION AXE 1 (NORD)  
3/32" = 1'-0"

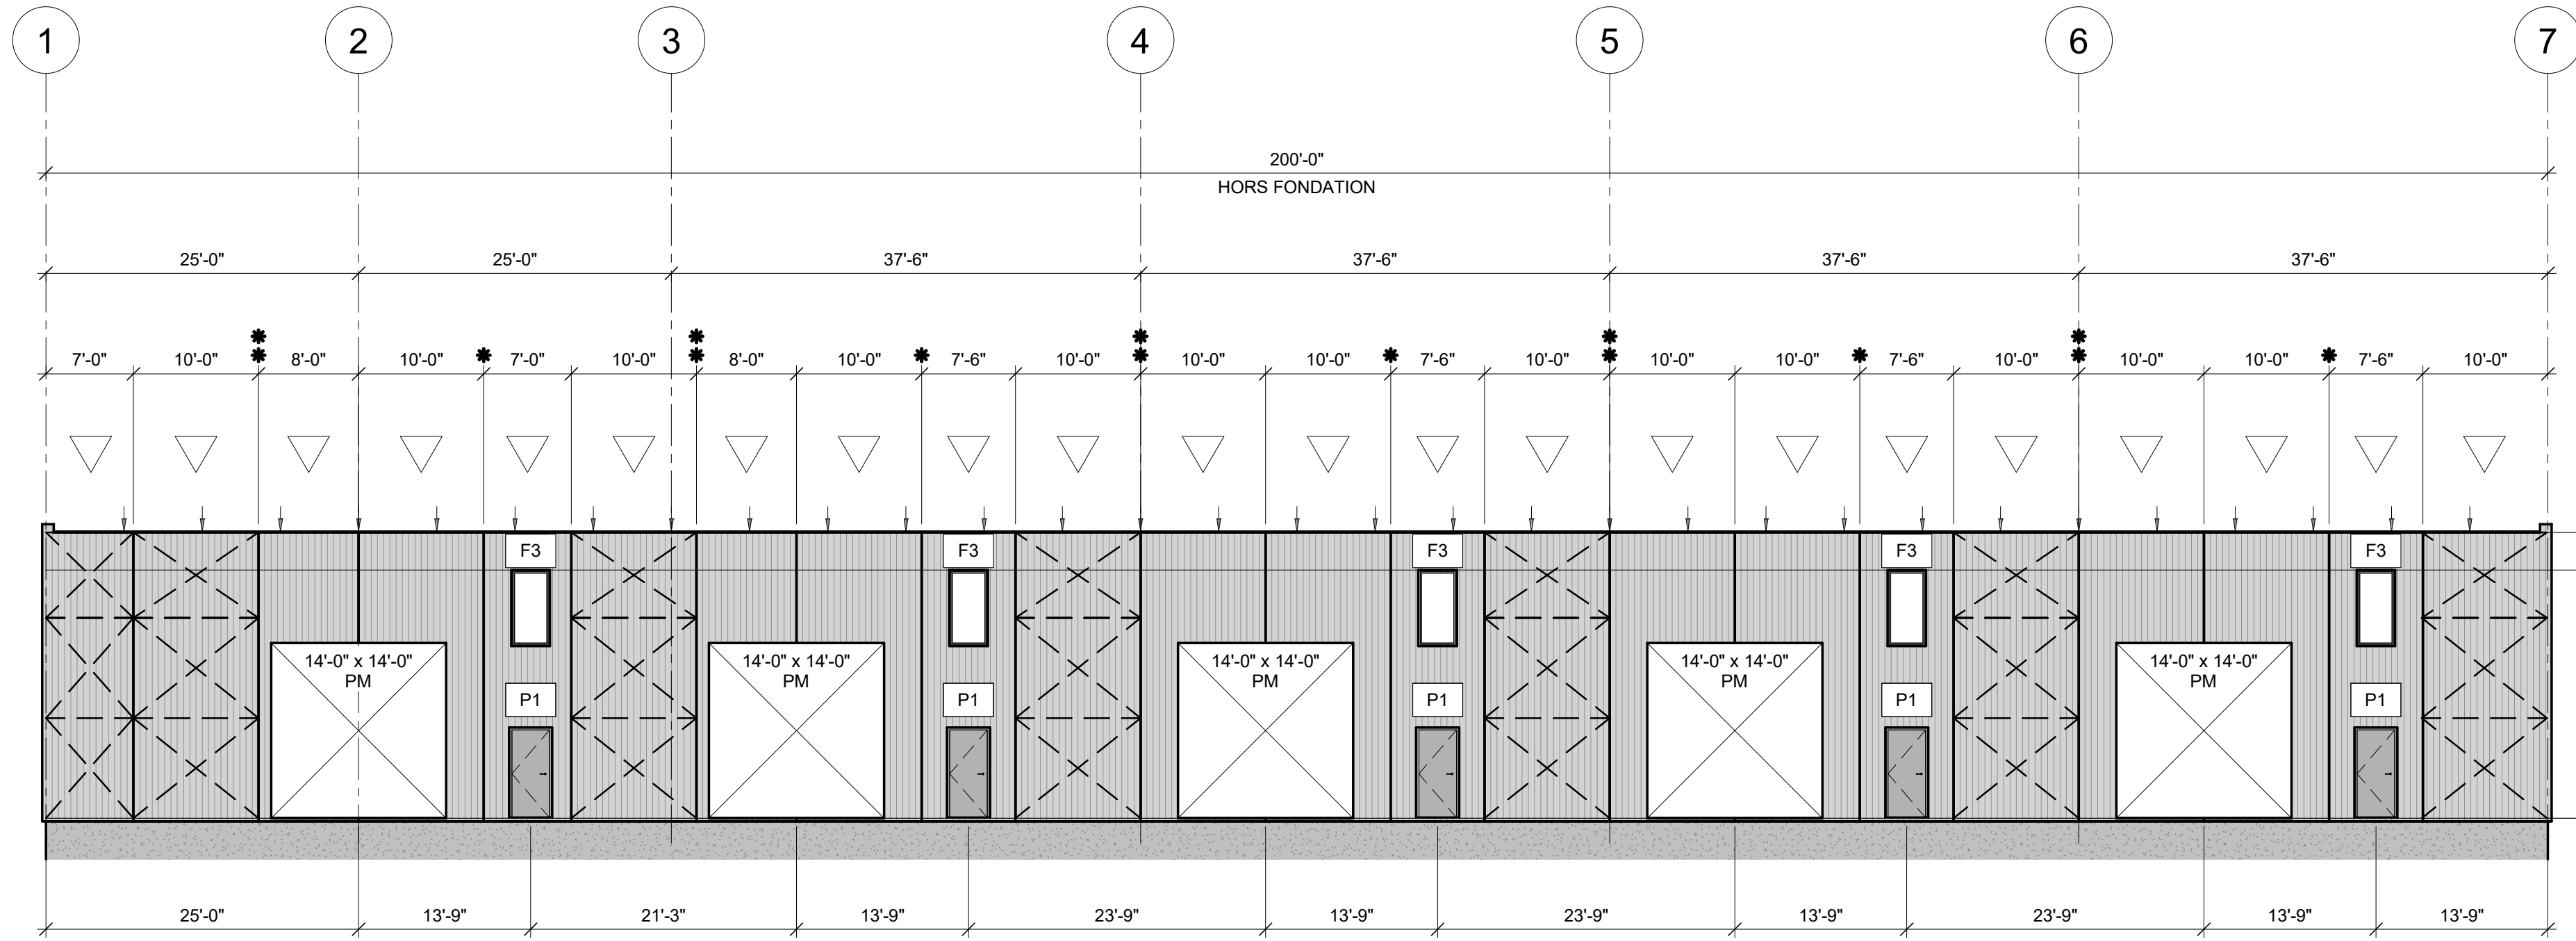

ÉLEVATION AXE A (OUEST)  
3/32" = 1'-0"


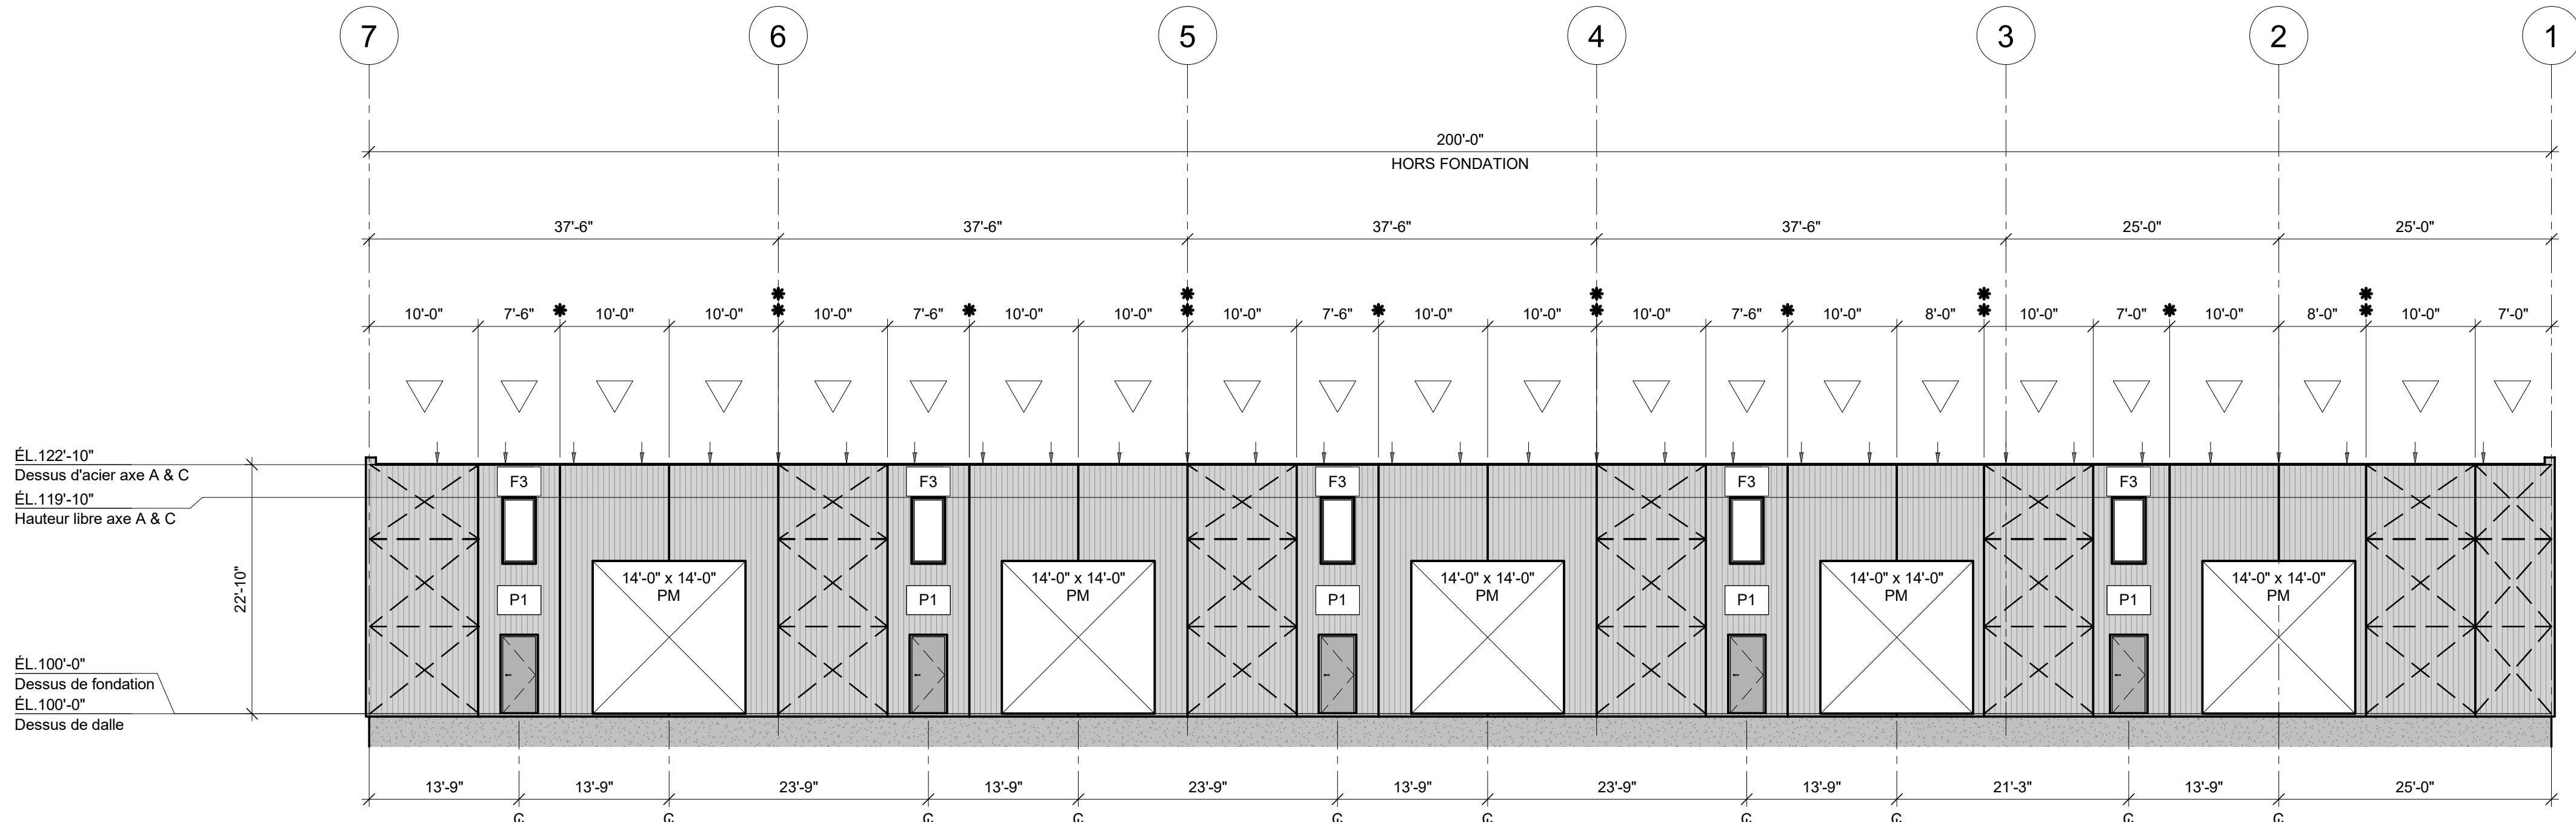


ÉLEVATION AXE C (EST)  
3/32" = 1'-0"

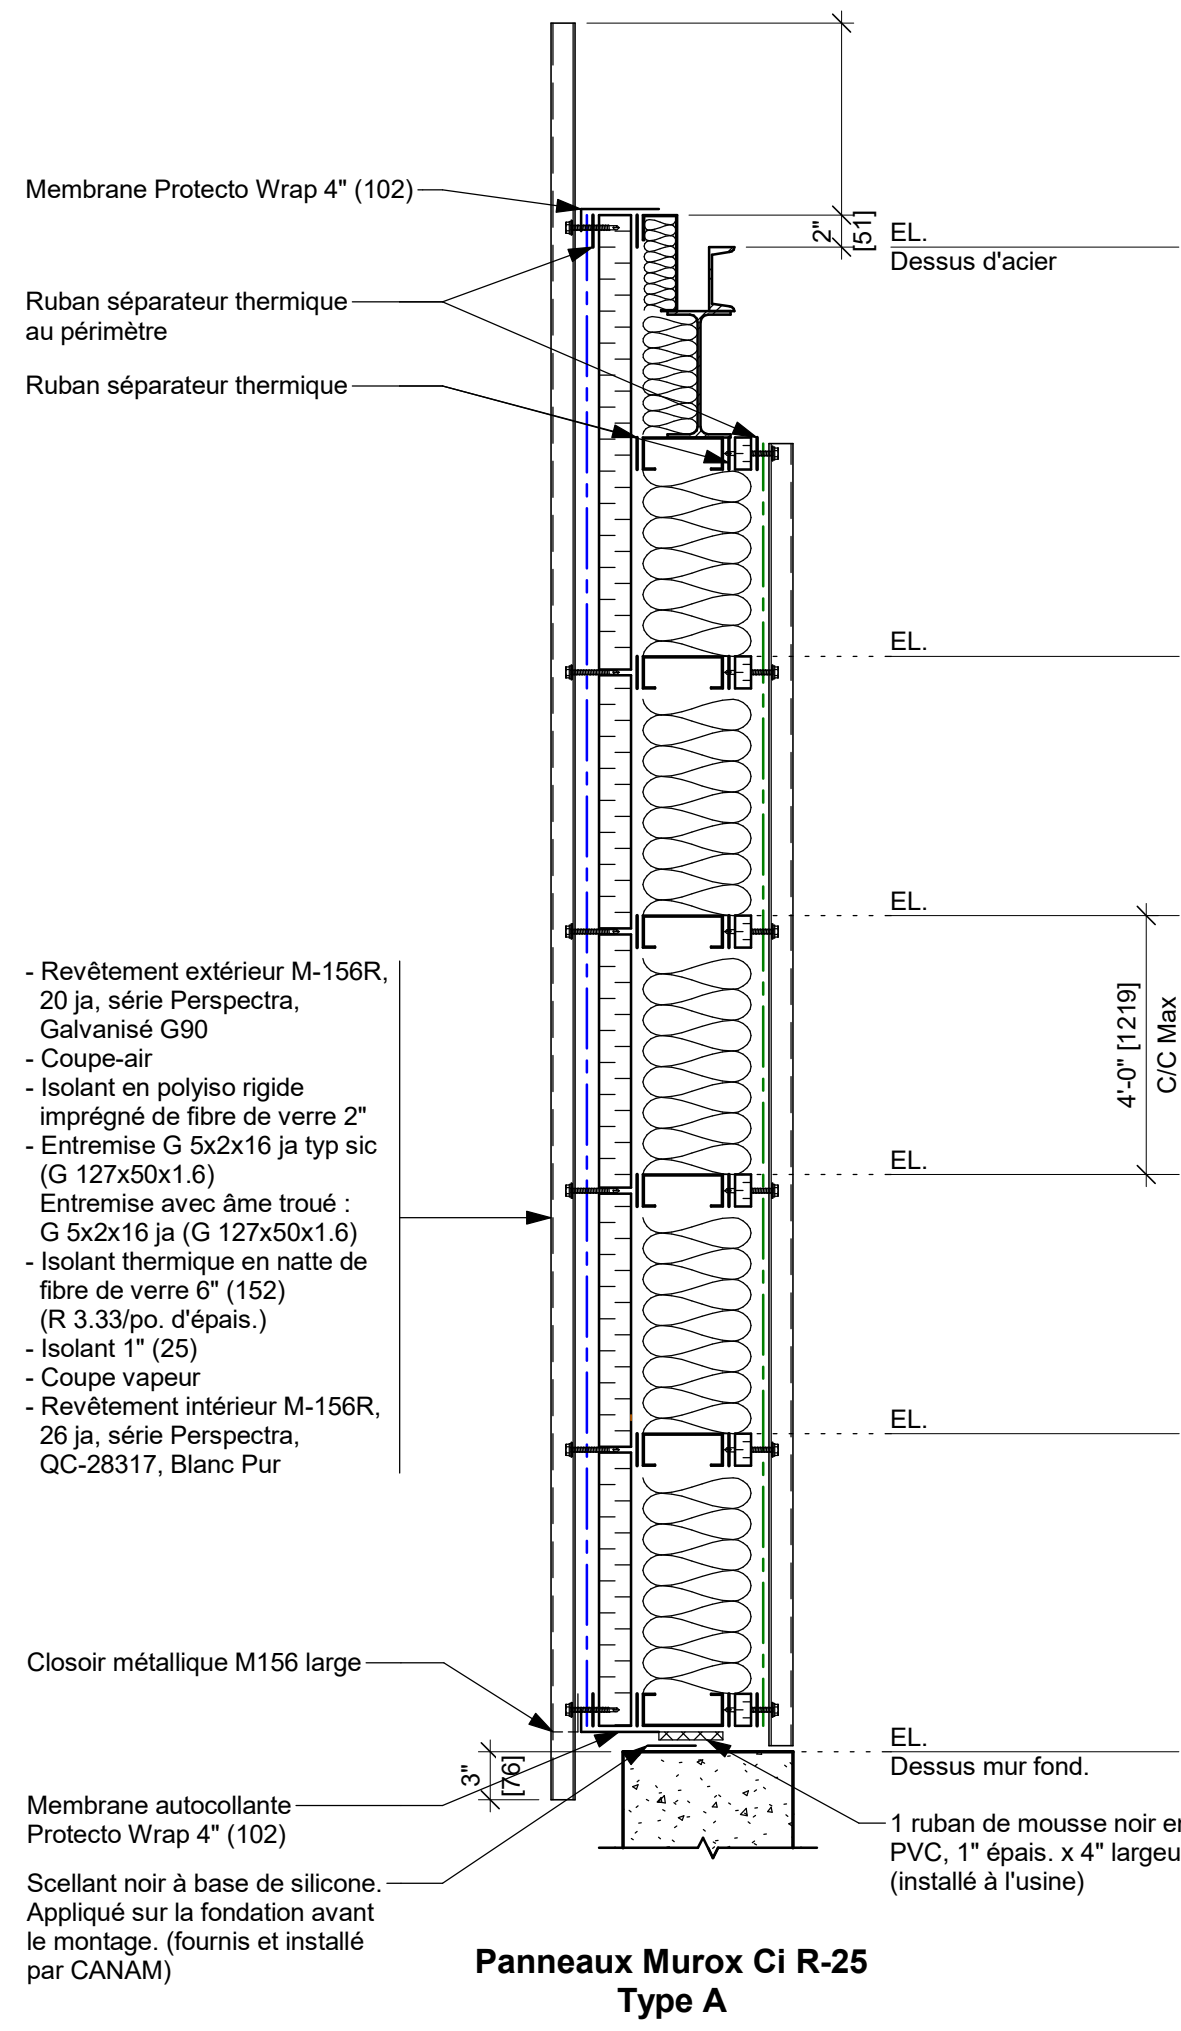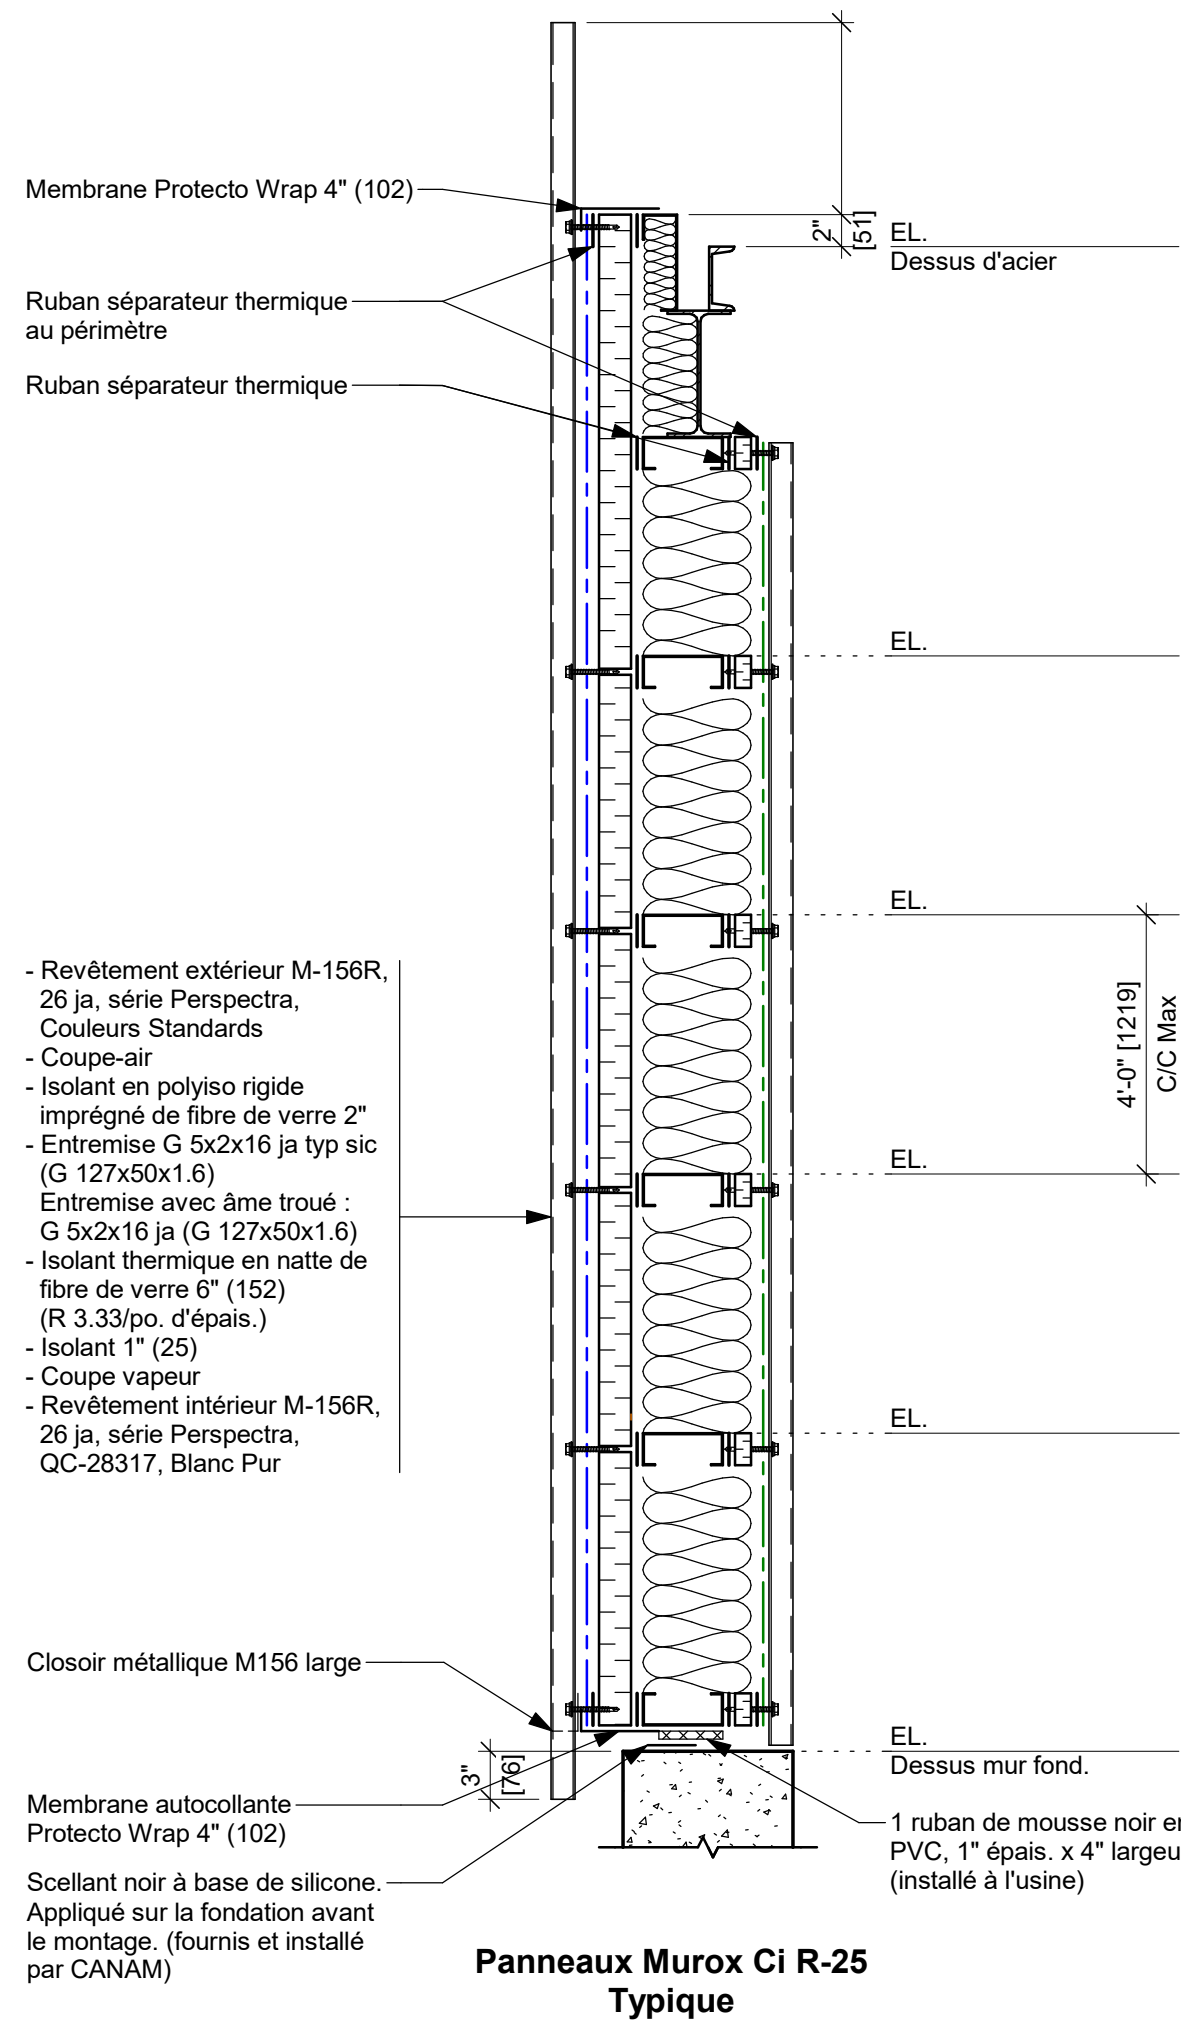

PRÉLIMINAIRE

NE DOIT PAS SERVIR À LA CONSTRUCTION
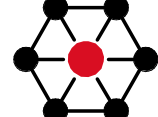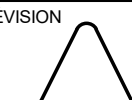
| REVISION   | DATE                              | DESCRIPTION         | DESS                                                                                              | VER |  |  |
|---|-----------------------------------|---------------------|---------------------------------------------------------------------------------------------------|-----|--|--|
| GERANT DE PROJET   |                                   |                     |                                                                                                   |     |  |  |
|   |                                   | -                   |                                                                                                   |     |  |  |
| DESSIN   |                                   |                     |                                                                                                   |     |  |  |
| DESSINÉ PAR   | CONÇU PAR                         | INGÉNIEUR DU PROJET | ÉCHELLE:                                                                                          |     |  |  |
| INITIALE   |                                   |                     | Comme indiqué                                                                                     |     |  |  |
| VERIFIÉ PAR   | INGÉNIEURS CONSEILS / ARCHITECTES |                     | DATE (mm/aaaa)                                                                                    |     |  |  |
|   |                                   |                     | 27/02/2026                                                                                        |     |  |  |
| CLIENT: Toiture Summa   |                                   |                     |                                                                                                   |     |  |  |
| <div><b>CANAM</b></div> <div>11505, 1re Avenue, bureau 500, Saint-Georges Beauce<br/>Québec, Canada, G5Y 7G3<br/>Téléphone : (418) 228-8031<br/>Sans frais : (877) 499-8049<br/>www.canam.com</div> |                                   |                     |                                                                                                   |     |  |  |
| SCAUX PROFESSIONNEL   |                                   |                     |                                                                                                   |     |  |  |
| PROJET   |                                   |                     |                                                                                                   |     |  |  |
| Entrepot E&G<br>Saint-Lambert de Lauzon, Québec   |                                   |                     |                                                                                                   |     |  |  |
| TITRE<br>CROQUIS PRÉLIMINAIRE -<br>ÉLEVATIONS, COUPES DE MUR ET<br>CÉDULES   |                                   |                     |                                                                                                   |     |  |  |
| NUMERO CONTRAT<br>P2026-048   | NUMERO DESSIN<br>EsMx501          | DIVISION            | REVISION<br> |     |  |  |