


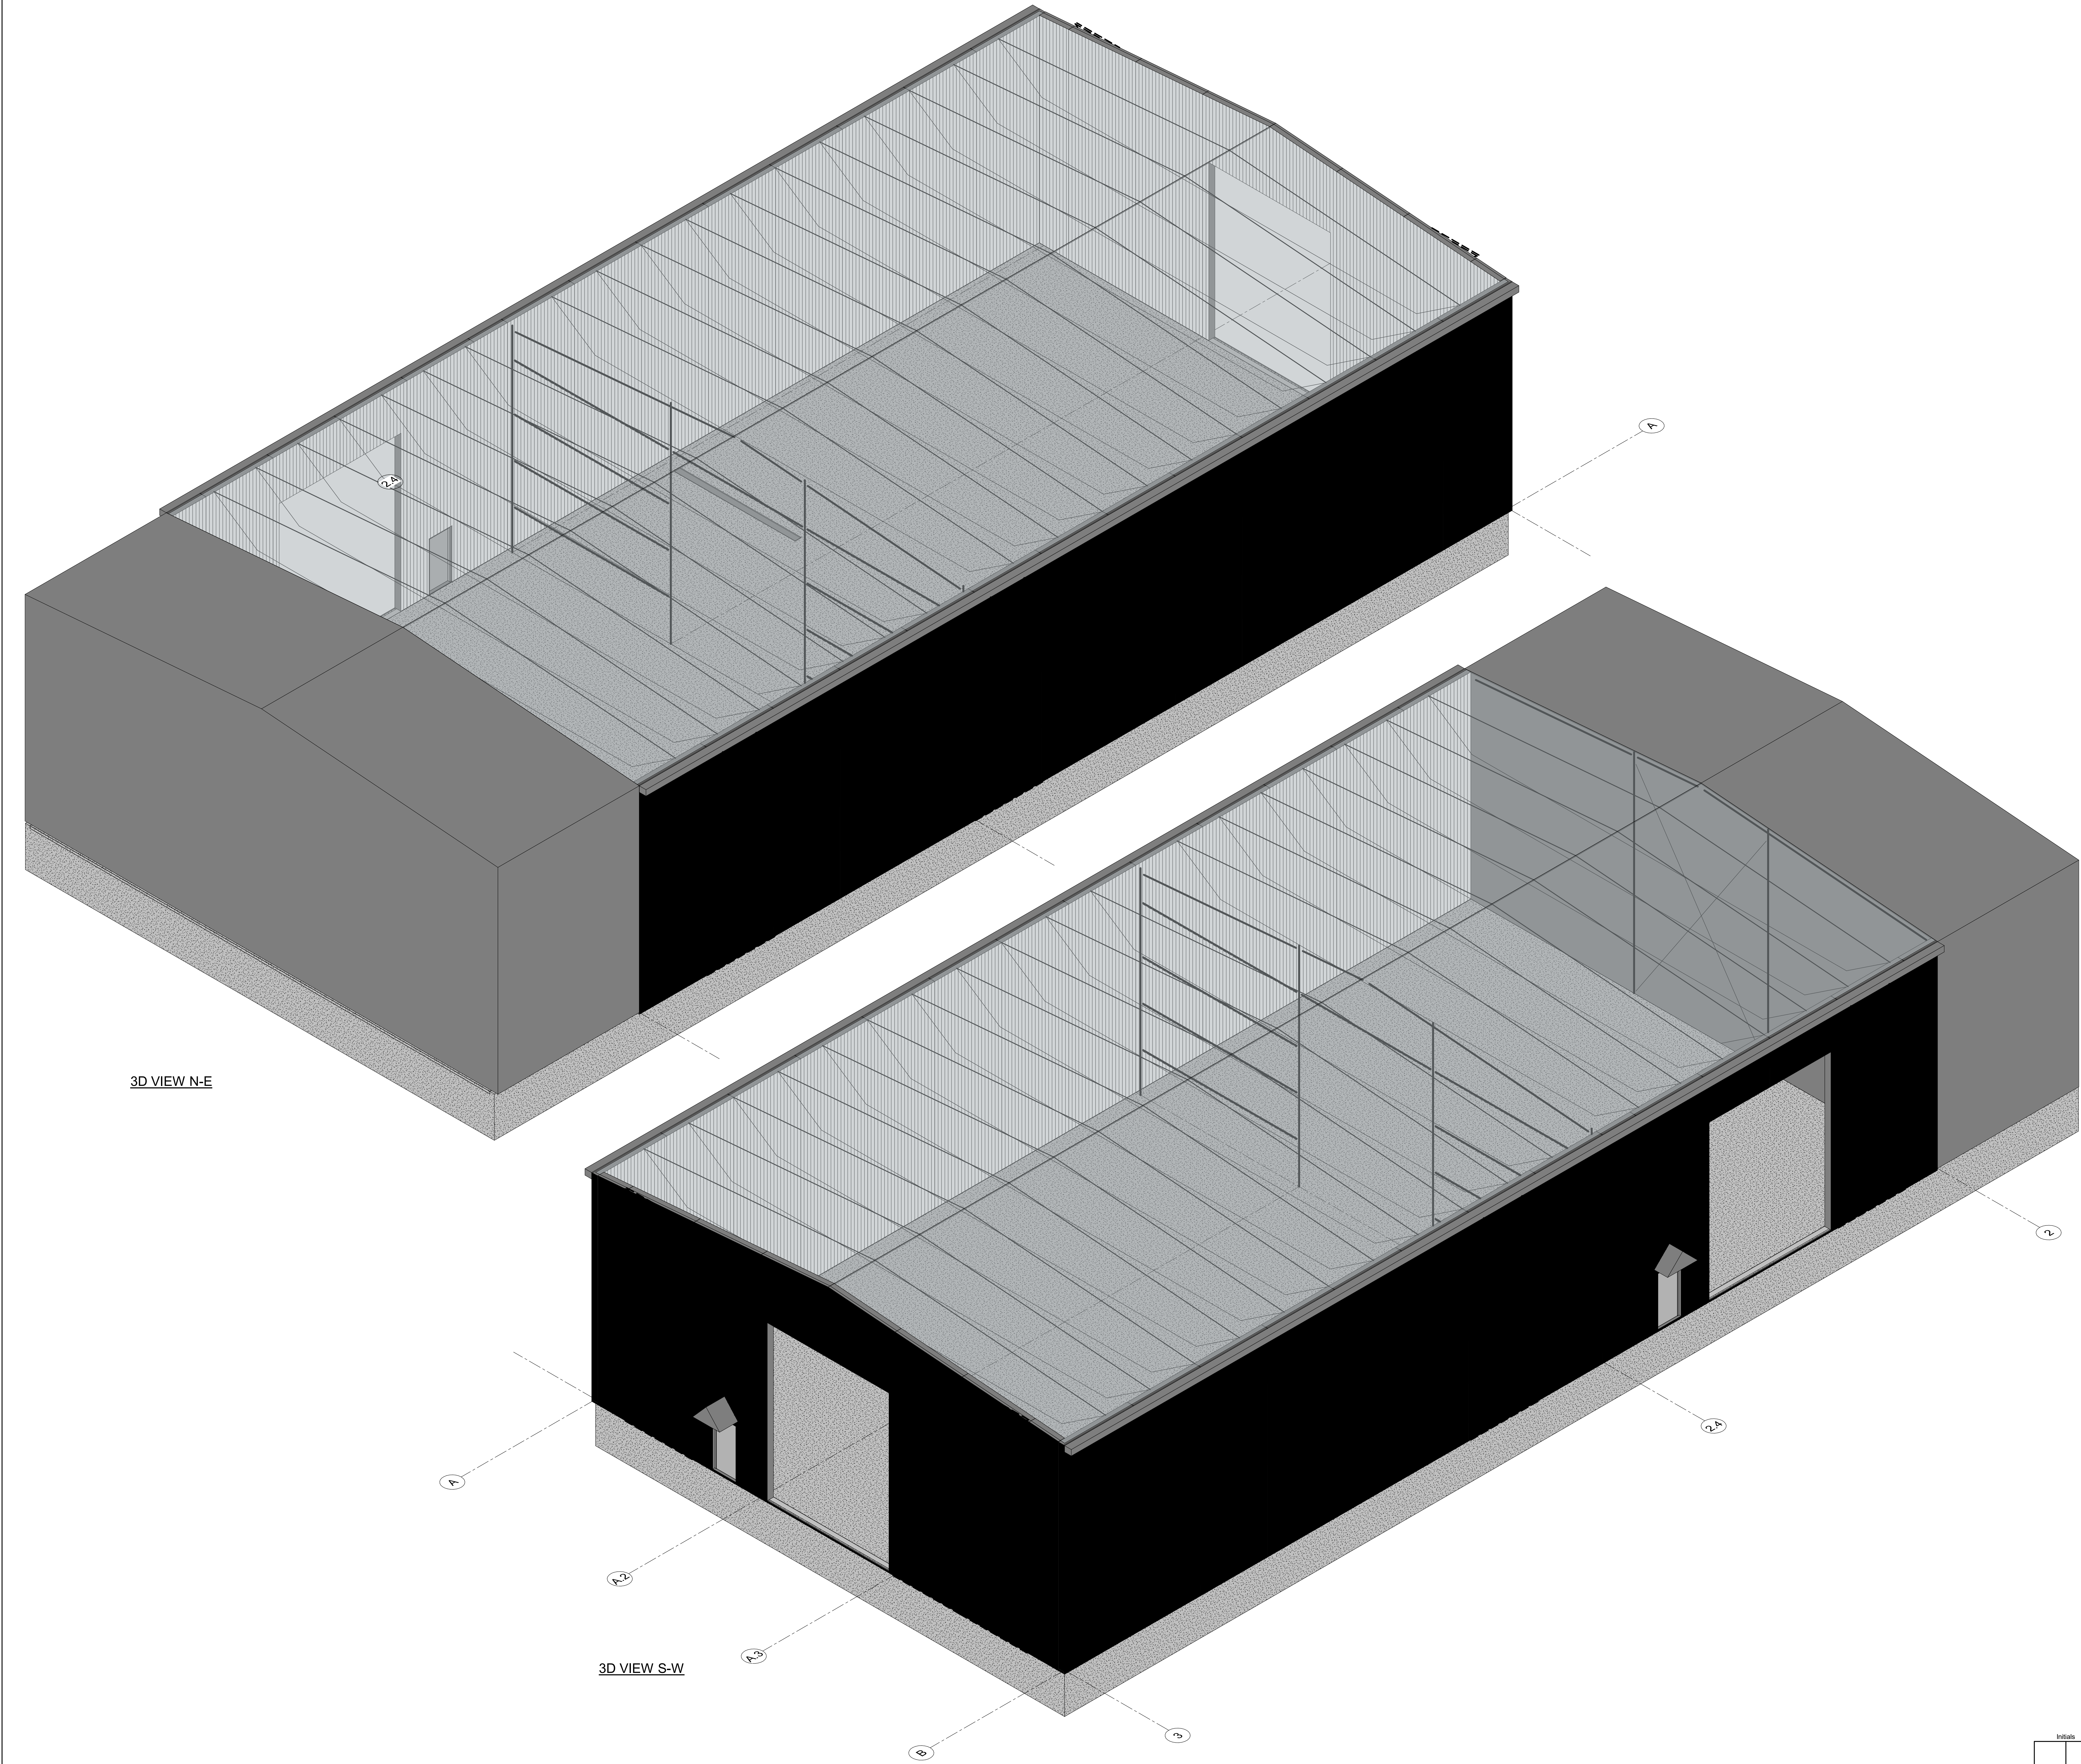

3D VIEW N-E

3D VIEW S-W

CONTRACTOR/RECTOR NOTE:  
IT IS PROHIBITED TO MODIFY, COPY, REPRODUCE OR OTHERWISE  
DISTRIBUTE THIS DRAWING OR ANY REPRESENTATION OF THIS  
DRAWING, OR ANY MEDIA, INCLUDING ELECTRONIC, WITHOUT THE  
PRIOR WRITTEN APPROVAL OF CANAM GROUP INC.

| PRELIMINARY SHEET LIST |                                                            |  |  |
|------------------------|------------------------------------------------------------|--|--|
| EsMx001                | PRELIMINARY SKETCH - 3D VIEWS                              |  |  |
| EsMx001                | PRELIMINARY SKETCH - ROOF PLAN                             |  |  |
| EsMx001                | PRELIMINARY SKETCH - ELEVATIONS                            |  |  |
| EsMx001                | PRELIMINARY SKETCH - ELEVATION, WALL SECTION AND SCHEDULES |  |  |


[Click here for 3D model](#)

PRELIMINARY

NOT TO BE USED FOR CONSTRUCTION

| 1               | 05/04/2025 | Revised bldg dimensions, door and OH/OR quantities | SL                 |        |             |
|-----------------|------------|----------------------------------------------------|--------------------|--------|-------------|
| REVISION        | DATE       | DESCRIPTION                                        | BY                 | CHKD   | APPD        |
| PROJECT MANAGER |            |                                                    |                    |        |             |
|                 |            |                                                    |                    |        |             |
|                 |            |                                                    |                    |        |             |
|                 |            |                                                    |                    |        |             |
|                 |            |                                                    |                    |        |             |
| DRAFTING        |            |                                                    |                    |        |             |
| DRAWN           | SL         | DESIGNED                                           | PROJECT ENGINEER   | SCALE: | 12" = 1'-0" |
| CHECKED         |            | CONSULTING ENGINEERS - ARCHITECTS                  | DATE (yyyy/mm/dd): |        | 2025/04/20  |

CUSTOMER:

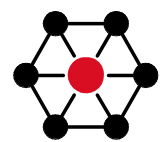**CANAM**

11505, 1re Avenue, bureau 500, Saint-Georges Beauce  
Châteauguay, Québec, G5Y 7Y3  
Phone : (418) 228-8031  
Toll free : (877) 499-6049  
www.canam.com

PROFESSIONAL SEAL

PROJECT

ESTEVAN, SASKATCHEWAN

DRAWING TITLE

PRELIMINARY SKETCH - 3D VIEWS

| CONTRACT NUMBER | DRAWING NUMBER | DIVISION | REVISION |
|-----------------|----------------|----------|----------|
| P2025-079       | EsMx001        |          | 1        |




| DOOR SCHEDULE |      |              |         |
|---------------|------|--------------|---------|
| Identity      | Qty. | Door 18 ga.  | Remarks |
| D1            | 2    | 36" x 84"    |         |
| D2            | 3    | 18'-2" x 23' |         |

Supplier's standard hardware:

- Hinges : Stanley FBB175 4 5" x 4"
- Exit device : Von Duern 22 x 688 with outside trim 230L
- Permanent cylinder : Schlage 20001C 626
- Door closure : LCN 1591 659
- Head and jamb seal : Unique 1650
- Bottom seal : Unique D34
- Threshold : See the remarks in "Door schedule"


SUPPLIER'S STD HARDWARE

1/2" = 1'-0"

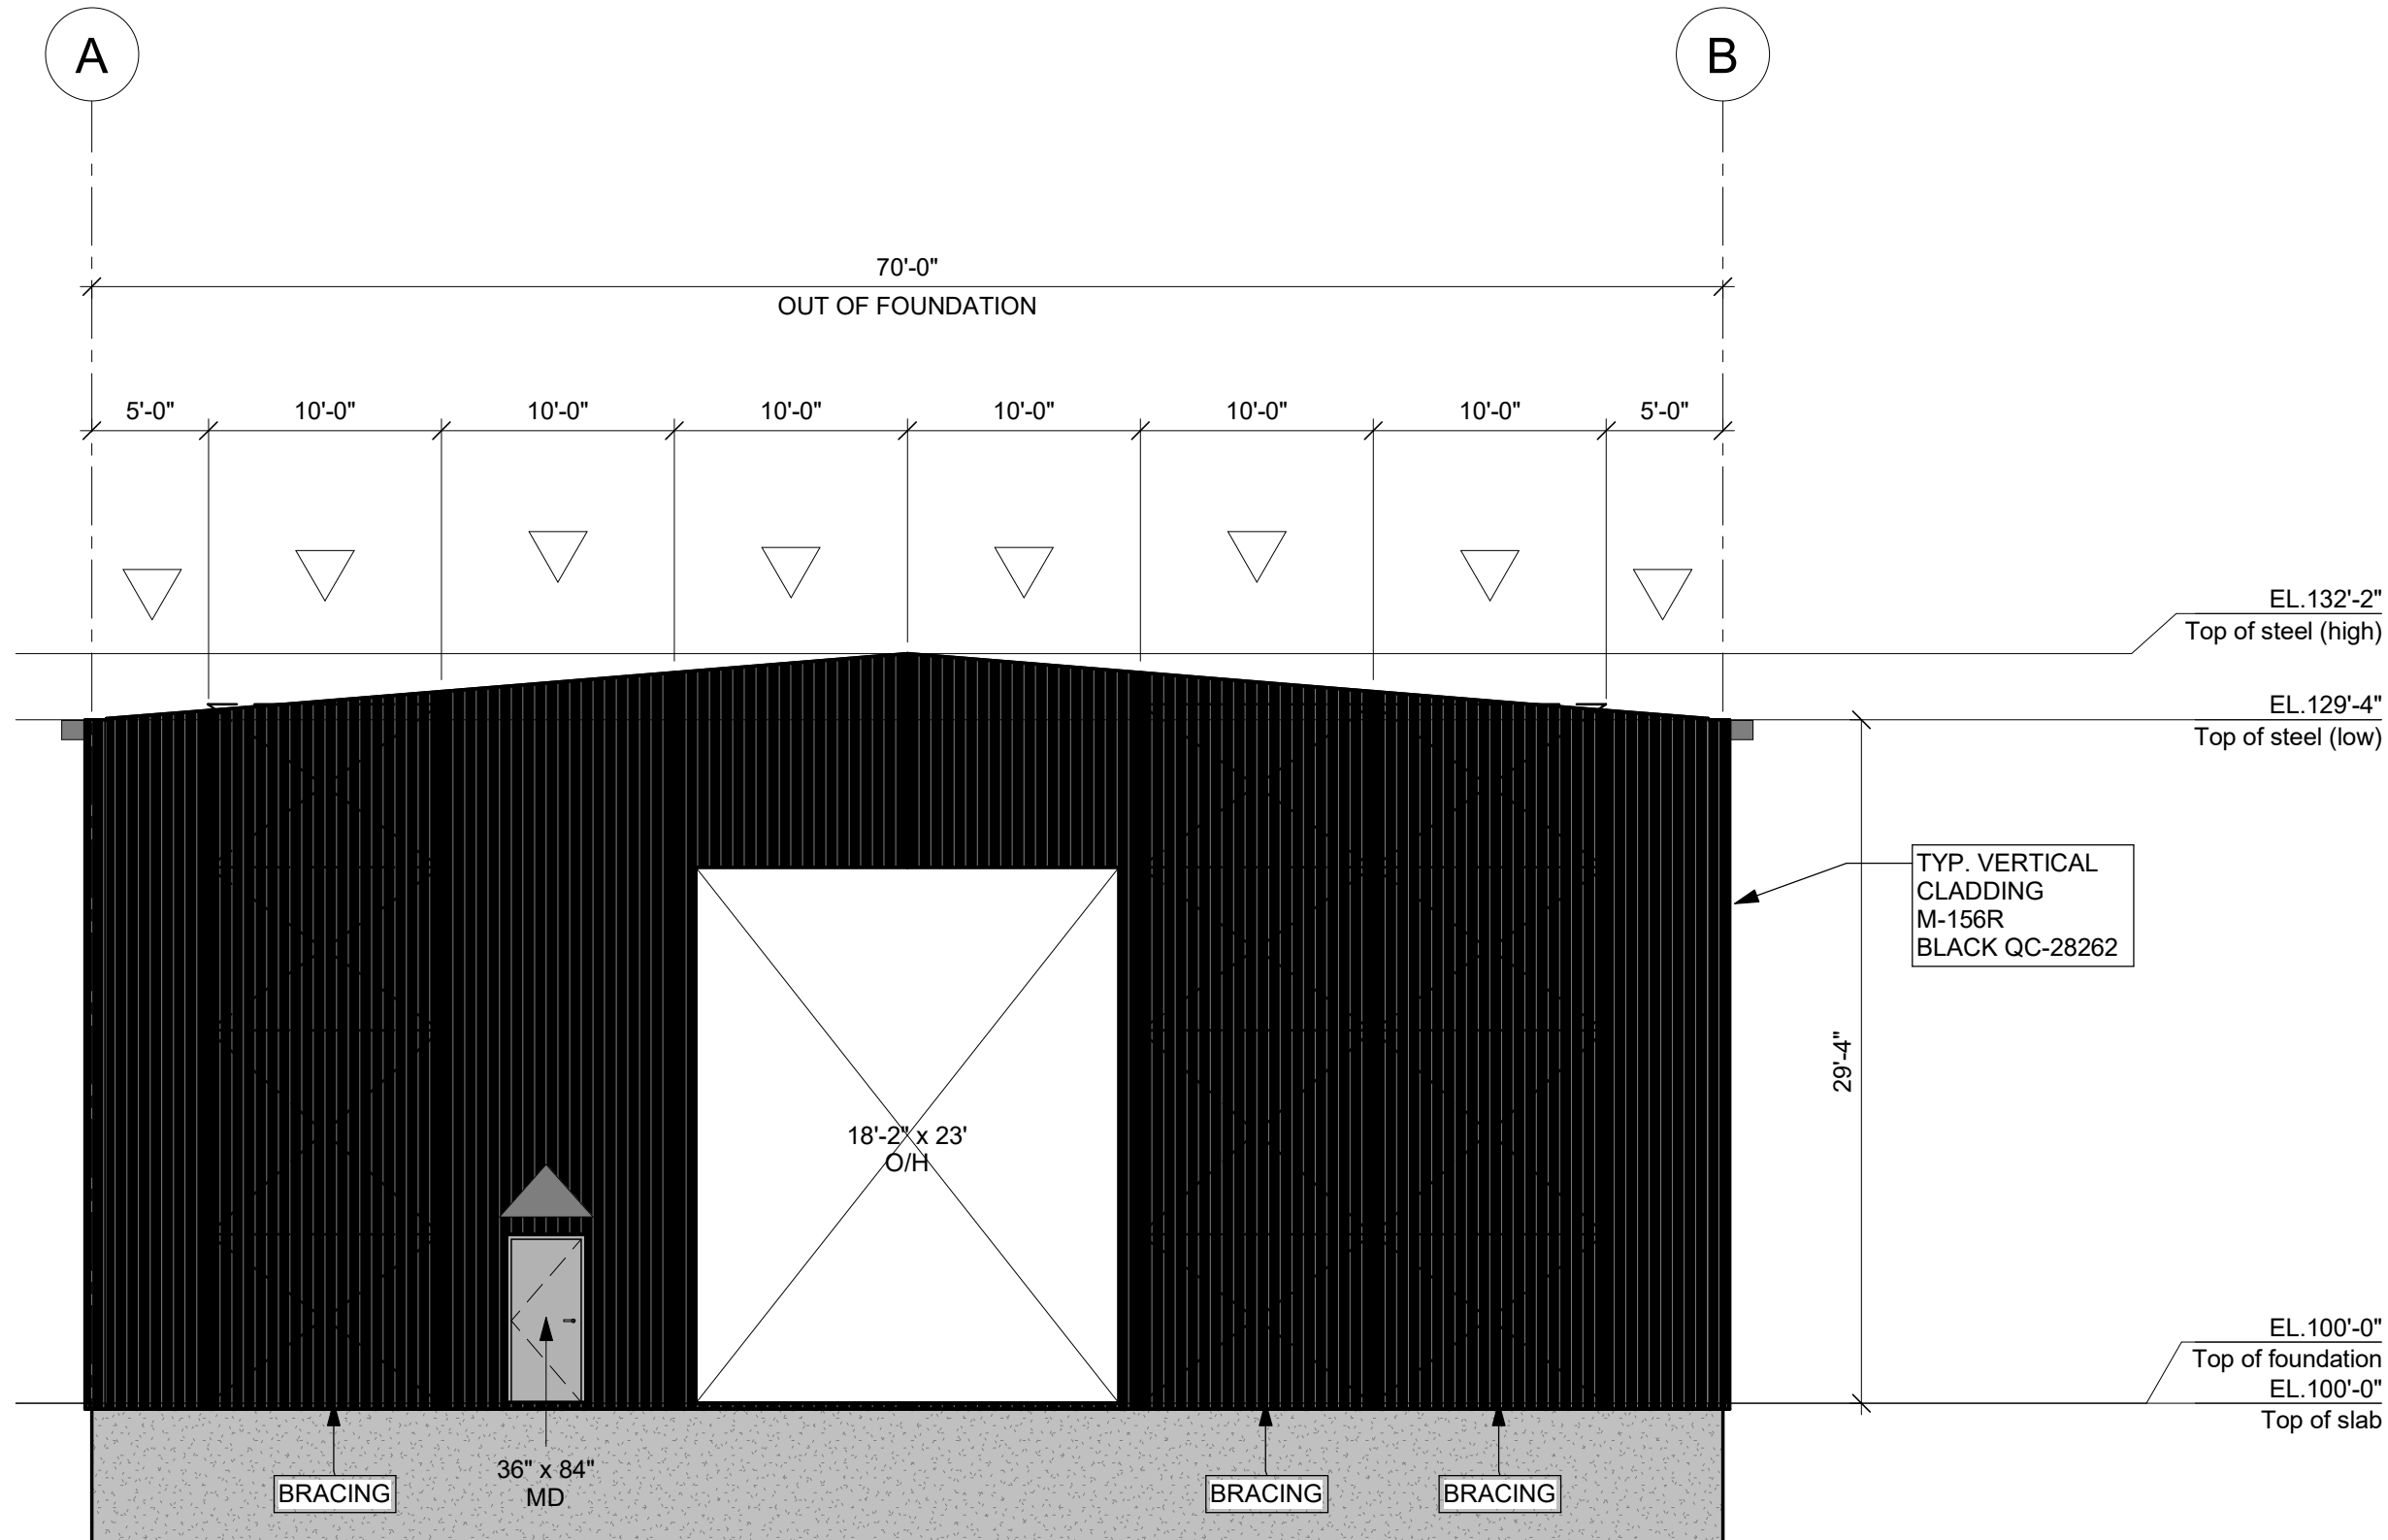


ELEVATION LINE 3 (WEST)

1/8" = 1'-0"

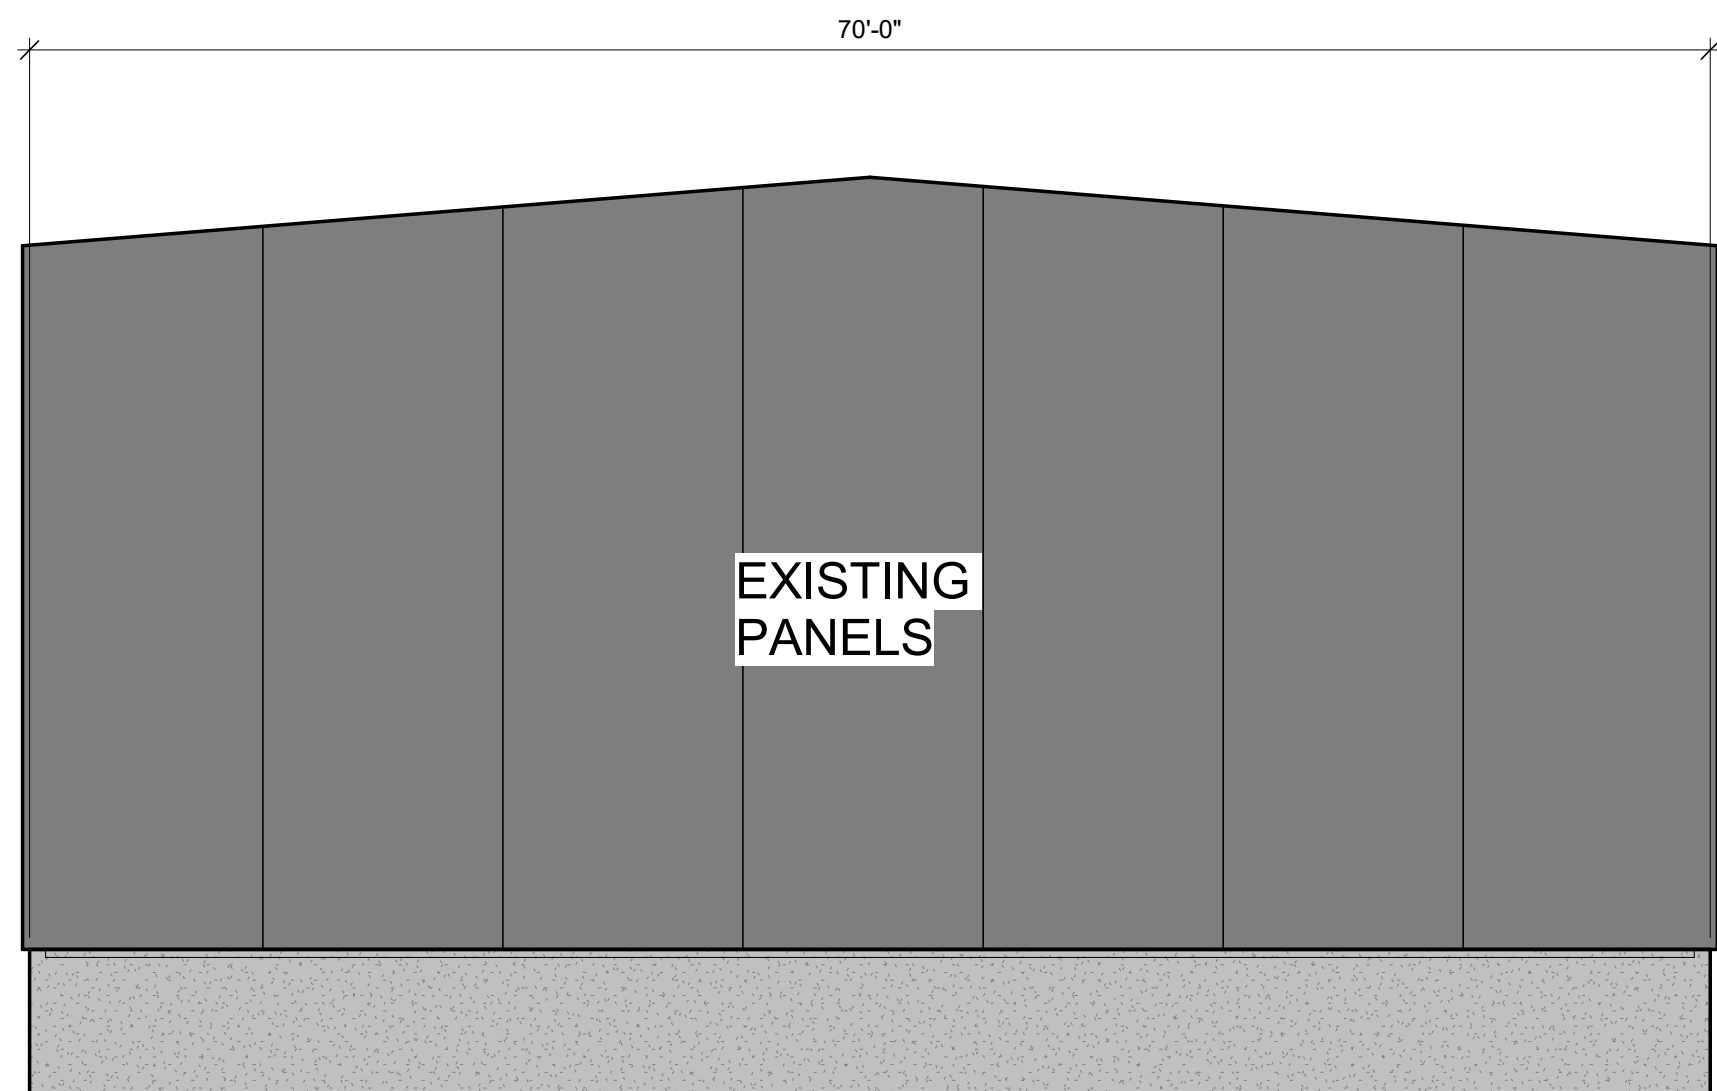


ELEVATION LINE 2 (EAST)(EXISTING)

1/8" = 1'-0"

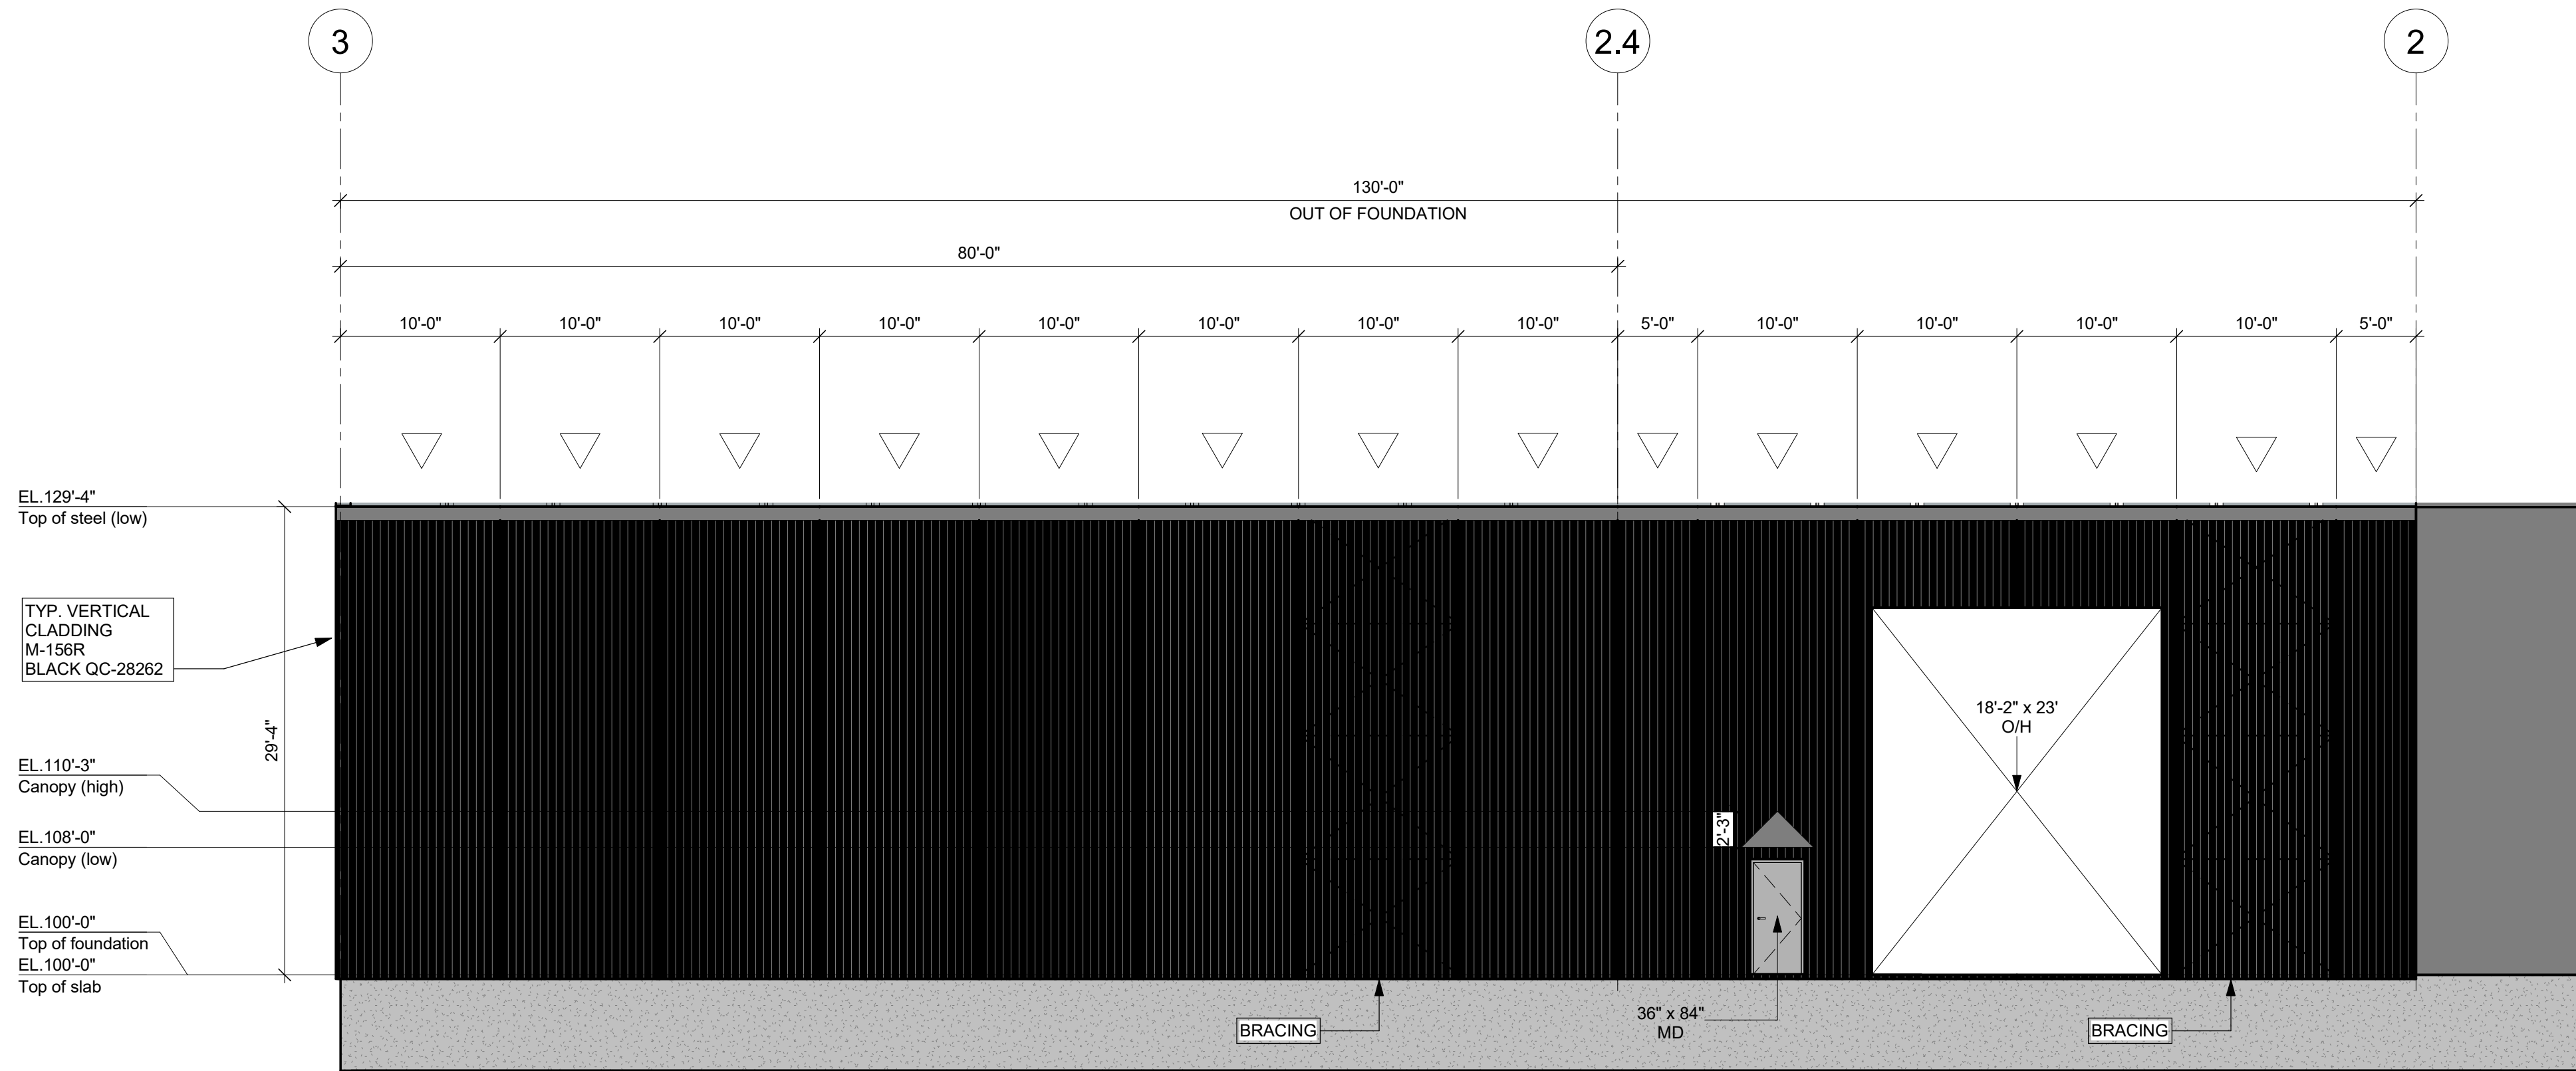


ELEVATION LINE B (SOUTH)

1/8" = 1'-0"

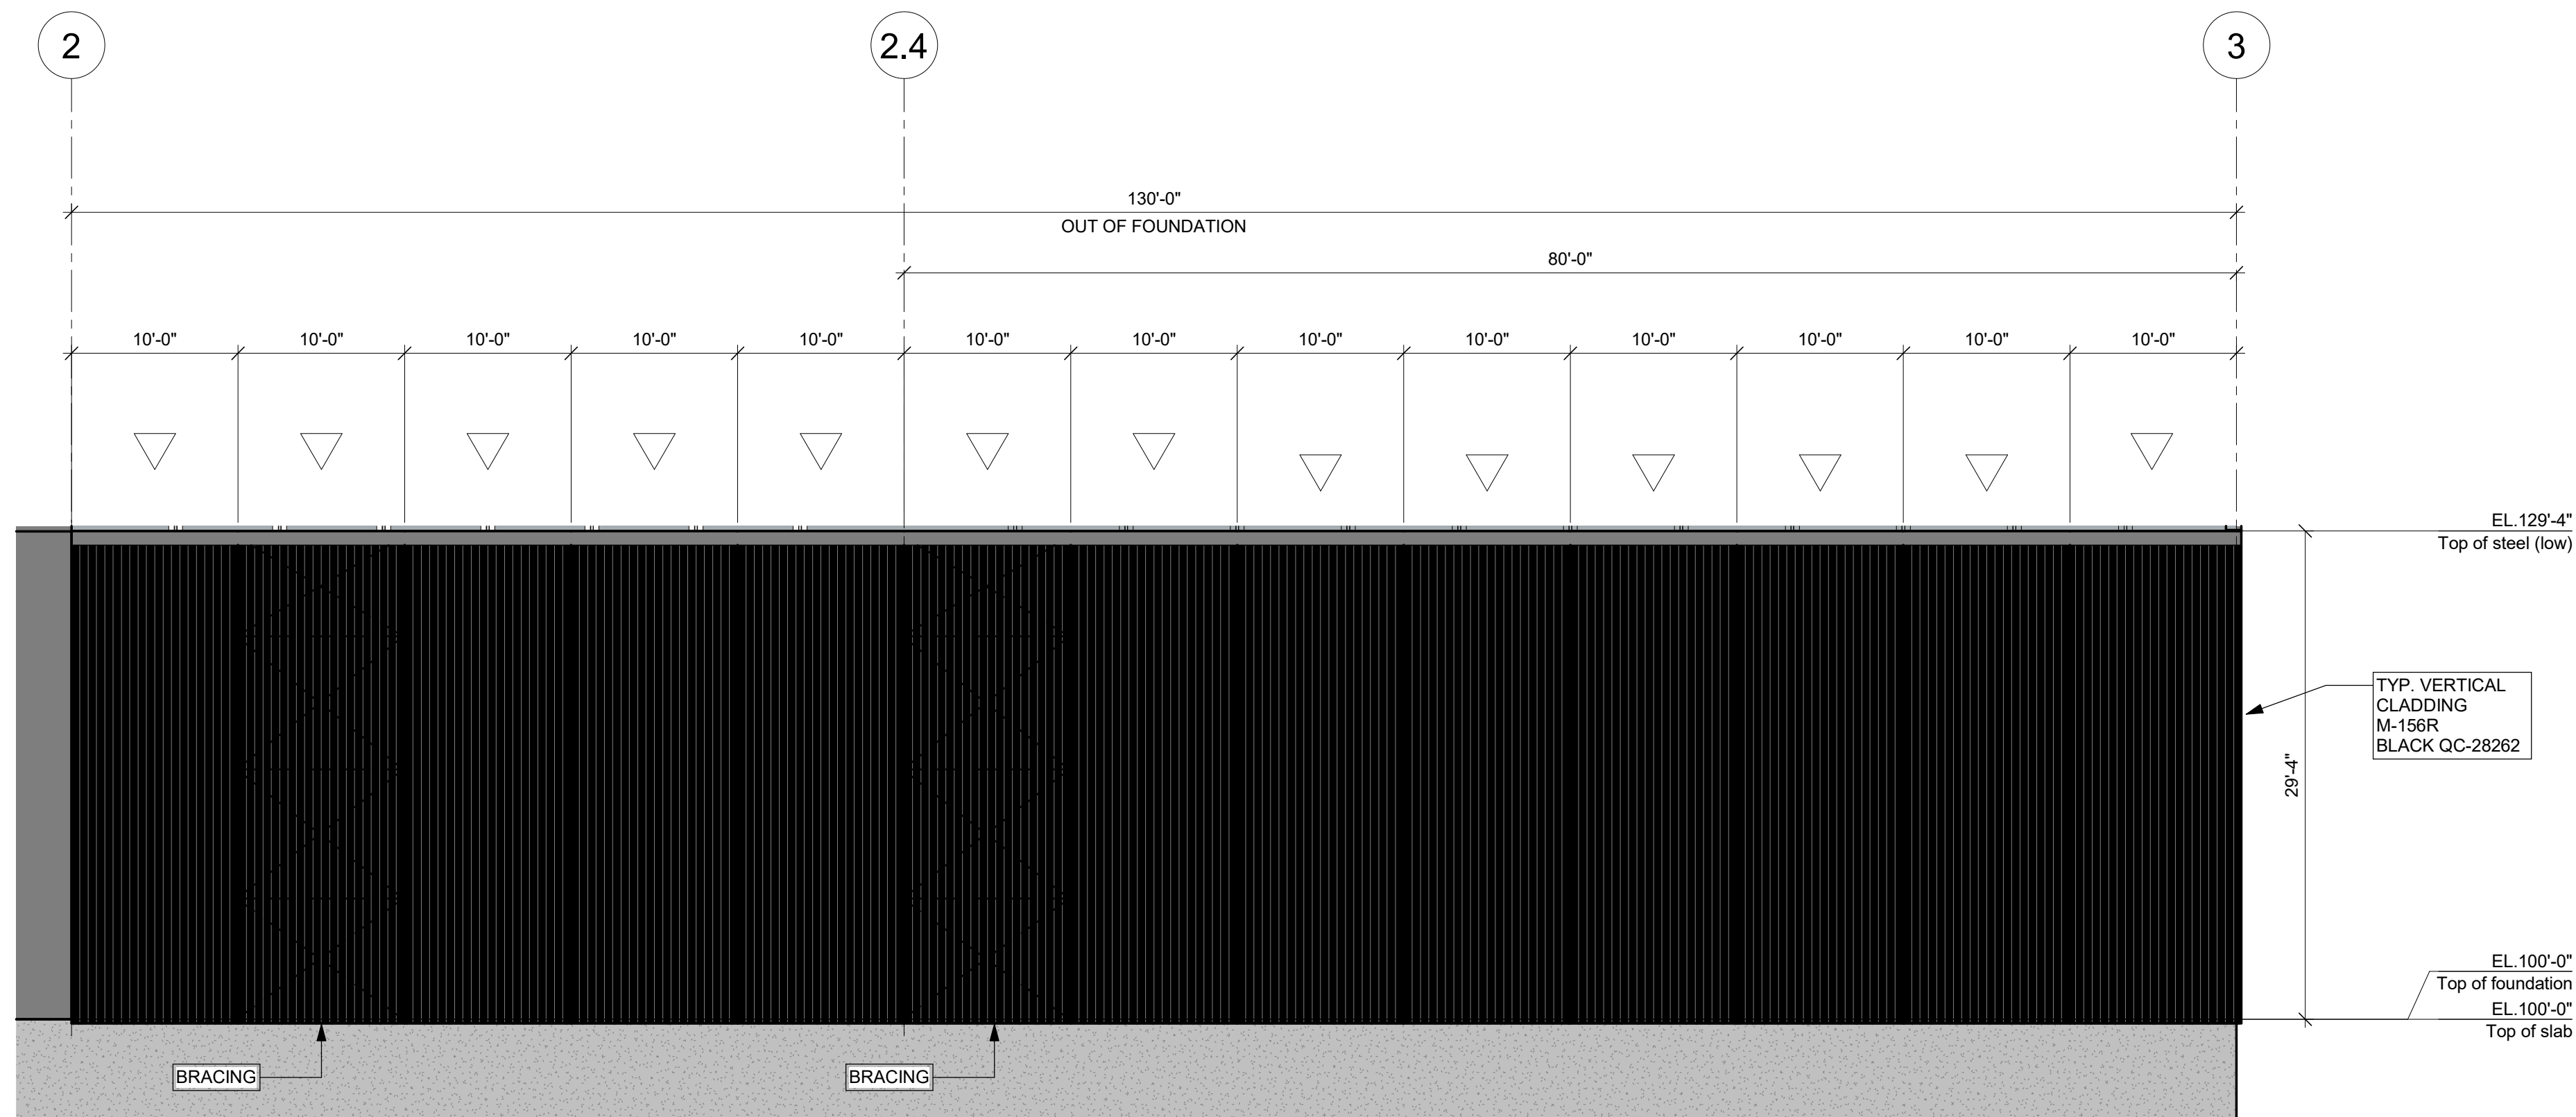

ELEVATION LINE A (NORTH)

1/8" = 1'-0"

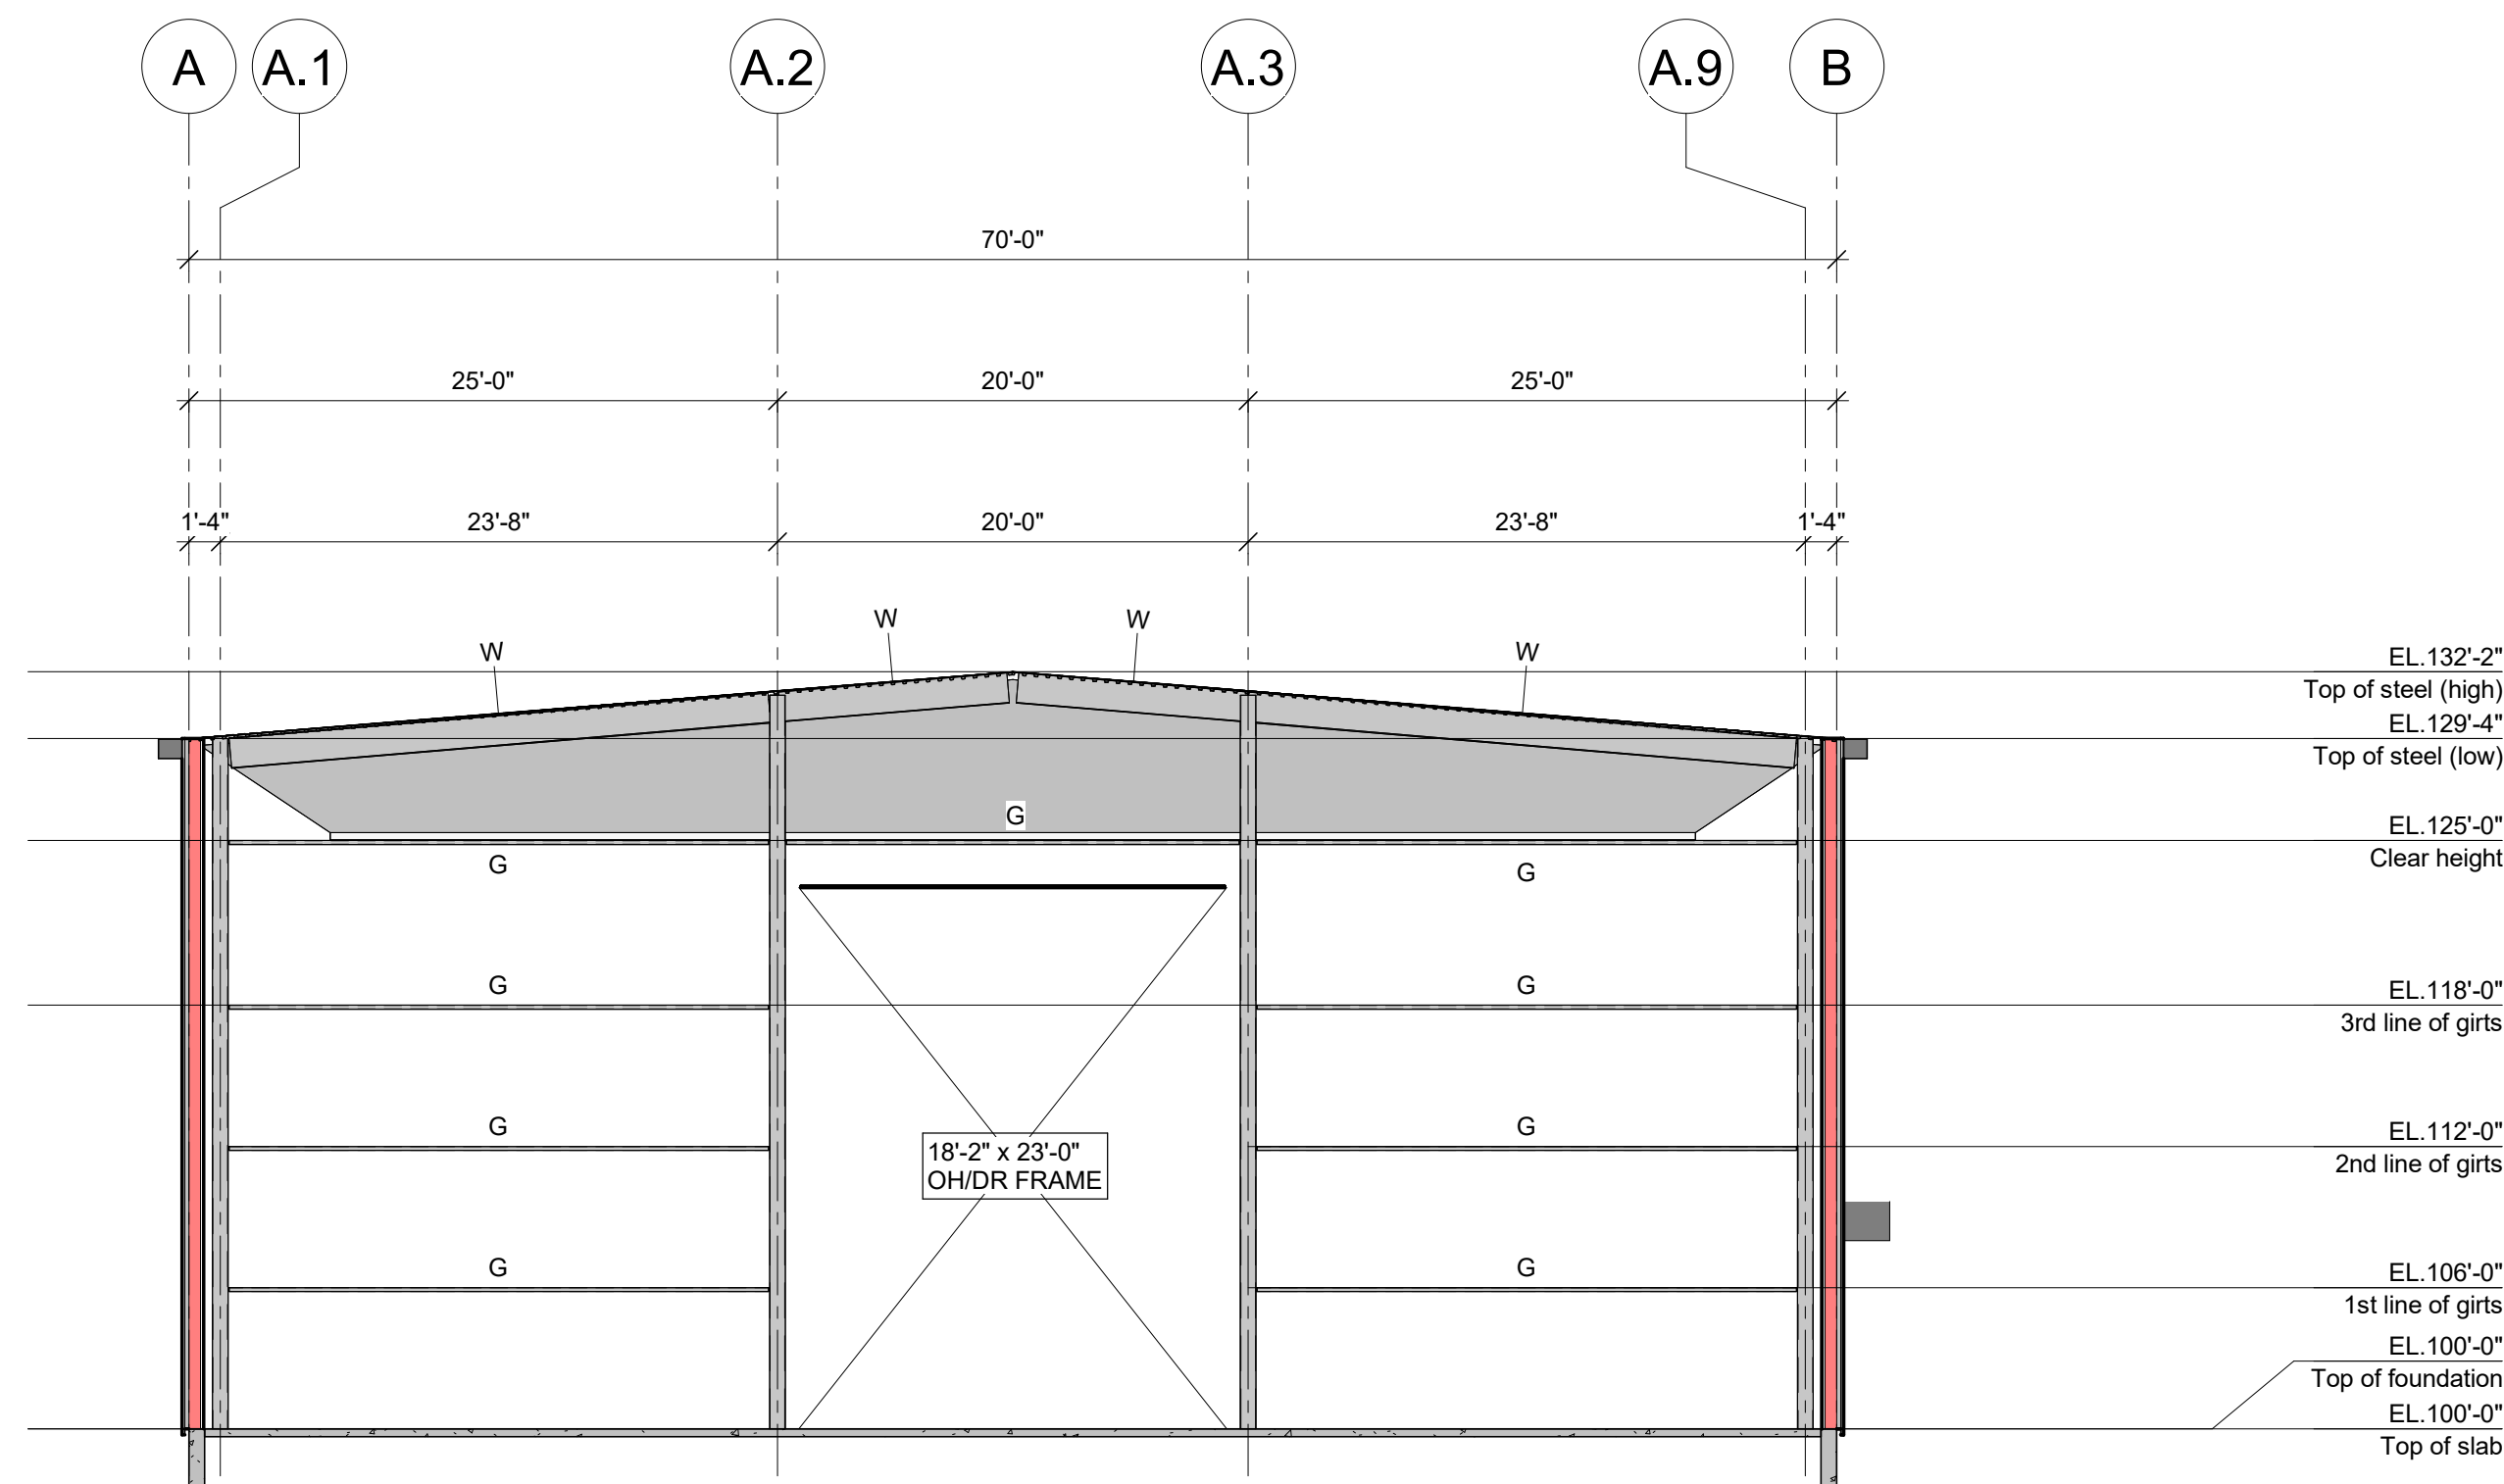

ELEVATION LINE 2.4 (WEST)(STRUCTURE)

1/8" = 1'-0"

CONTRACTOR/RECTOR NOTE:

IT IS PROHIBITED TO MODIFY, COPY, REPRODUCE OR OTHERWISE DISTRIBUTE THIS DRAWING OR ANY REPRESENTATION OF THIS DRAWING OR ANY MEDIA, INCLUDING ELECTRONIC, WITHOUT THE PRIOR WRITTEN APPROVAL OF CANAM GROUP INC.

PRELIMINARY

NOT TO BE USED FOR CONSTRUCTION

|   |            |                                                    |    |     |
|---|------------|----------------------------------------------------|----|-----|
| 1 | 05/04/2025 | Revised bldg dimensions, door and OH/OR quantities | SL | USR |
|---|------------|----------------------------------------------------|----|-----|

| REVISION | DATE | DESCRIPTION | BY | APP |
|----------|------|-------------|----|-----|
|----------|------|-------------|----|-----|

|                 |  |  |  |  |
|-----------------|--|--|--|--|
| PROJECT MANAGER |  |  |  |  |
|-----------------|--|--|--|--|

|          |  |  |  |  |
|----------|--|--|--|--|
| DRAFTING |  |  |  |  |
|----------|--|--|--|--|

|       |          |                  |       |
|-------|----------|------------------|-------|
| DRAWN | DESIGNED | PROJECT ENGINEER | SCALE |
|-------|----------|------------------|-------|

|          |  |  |               |
|----------|--|--|---------------|
| INITIALE |  |  | Comme indiqu  |
|----------|--|--|---------------|

|         |                                   |                   |
|---------|-----------------------------------|-------------------|
| CHECKED | CONSULTING ENGINEERS / ARCHITECTS | DATE (yyyy/mm/dd) |
|---------|-----------------------------------|-------------------|

|          |  |
|----------|--|
| CUSTOMER |  |
|----------|--|



11505, 1re Avenue, bureau 500, Saint-Georges Beauce  
Chabec, Canada, G5Y 7G3  
Phone : (418) 228-8031  
Toll free : (877) 499-6049  
www.canam.com

|                   |  |
|-------------------|--|
| PROFESSIONAL SEAL |  |
|-------------------|--|

|         |  |
|---------|--|
| PROJECT |  |
|---------|--|

ESTEVAN, SASKATCHEWAN

|               |  |
|---------------|--|
| DRAWING TITLE |  |
|---------------|--|

PRELIMINARY SKETCH - ELEVATIONS

|                 |                |          |          |
|-----------------|----------------|----------|----------|
| CONTRACT NUMBER | DRAWING NUMBER | DIVISION | REVISION |
|-----------------|----------------|----------|----------|

P2025-079

EsMx501

1

