



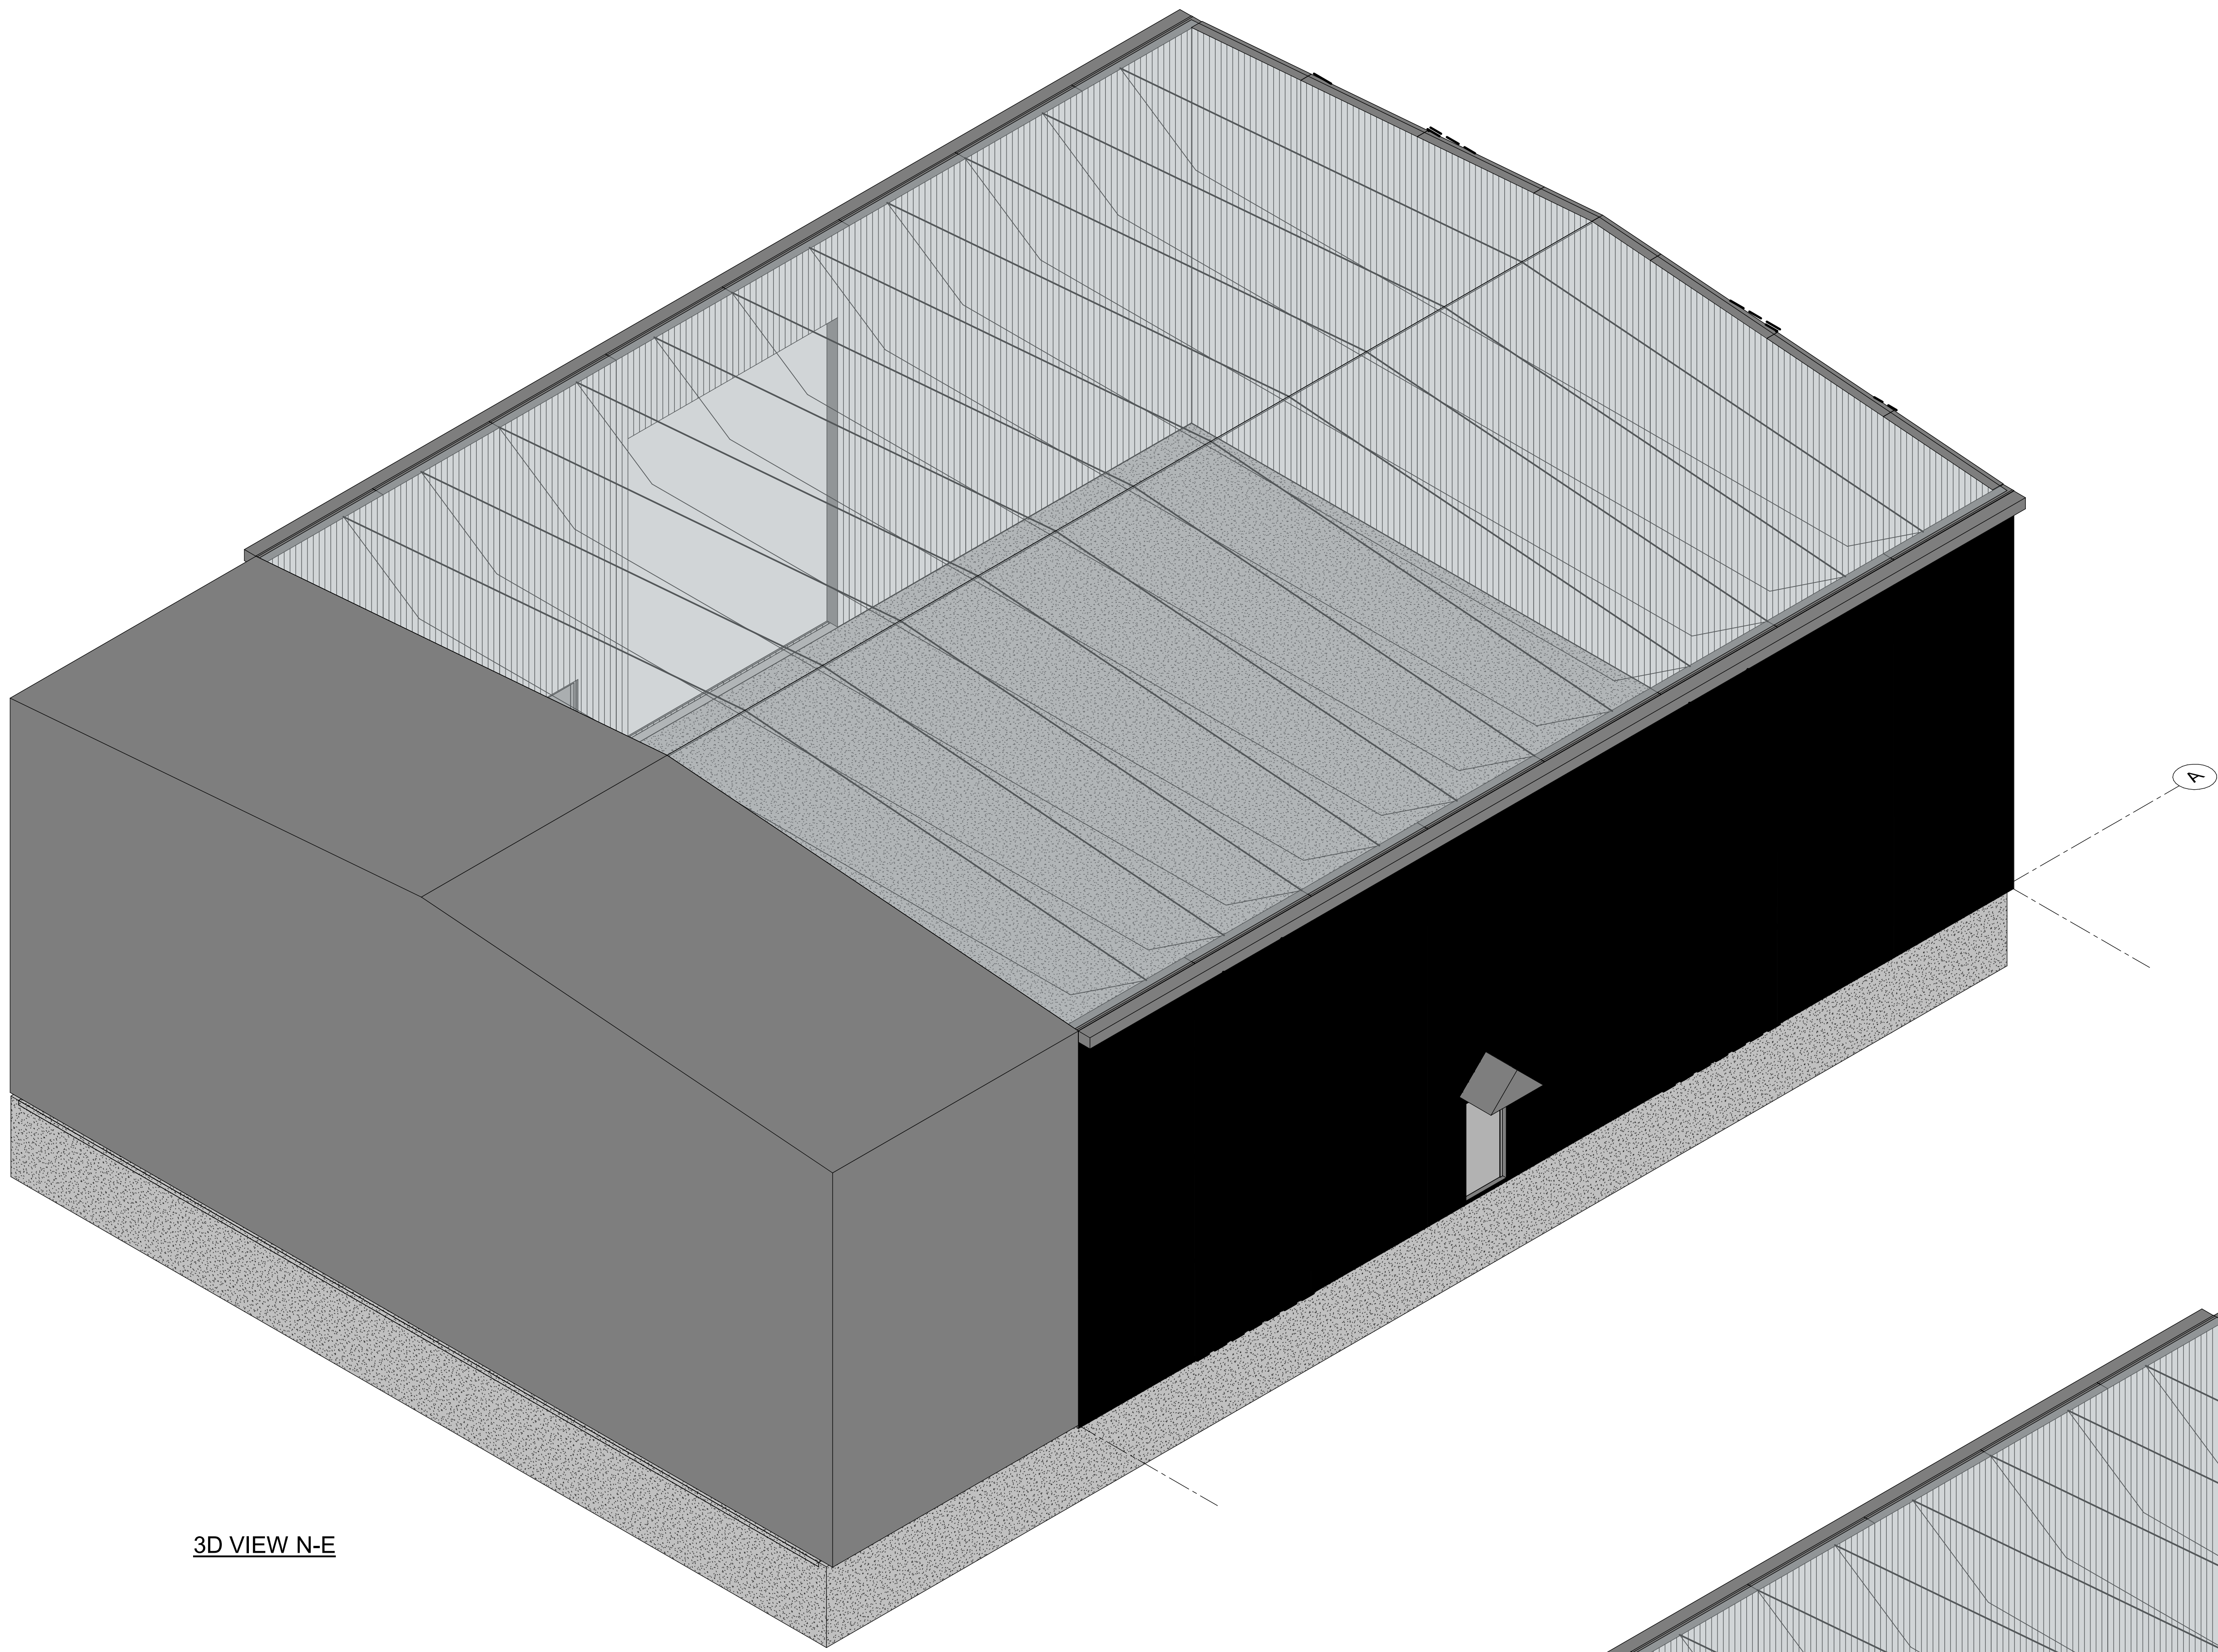

3D VIEW N-E

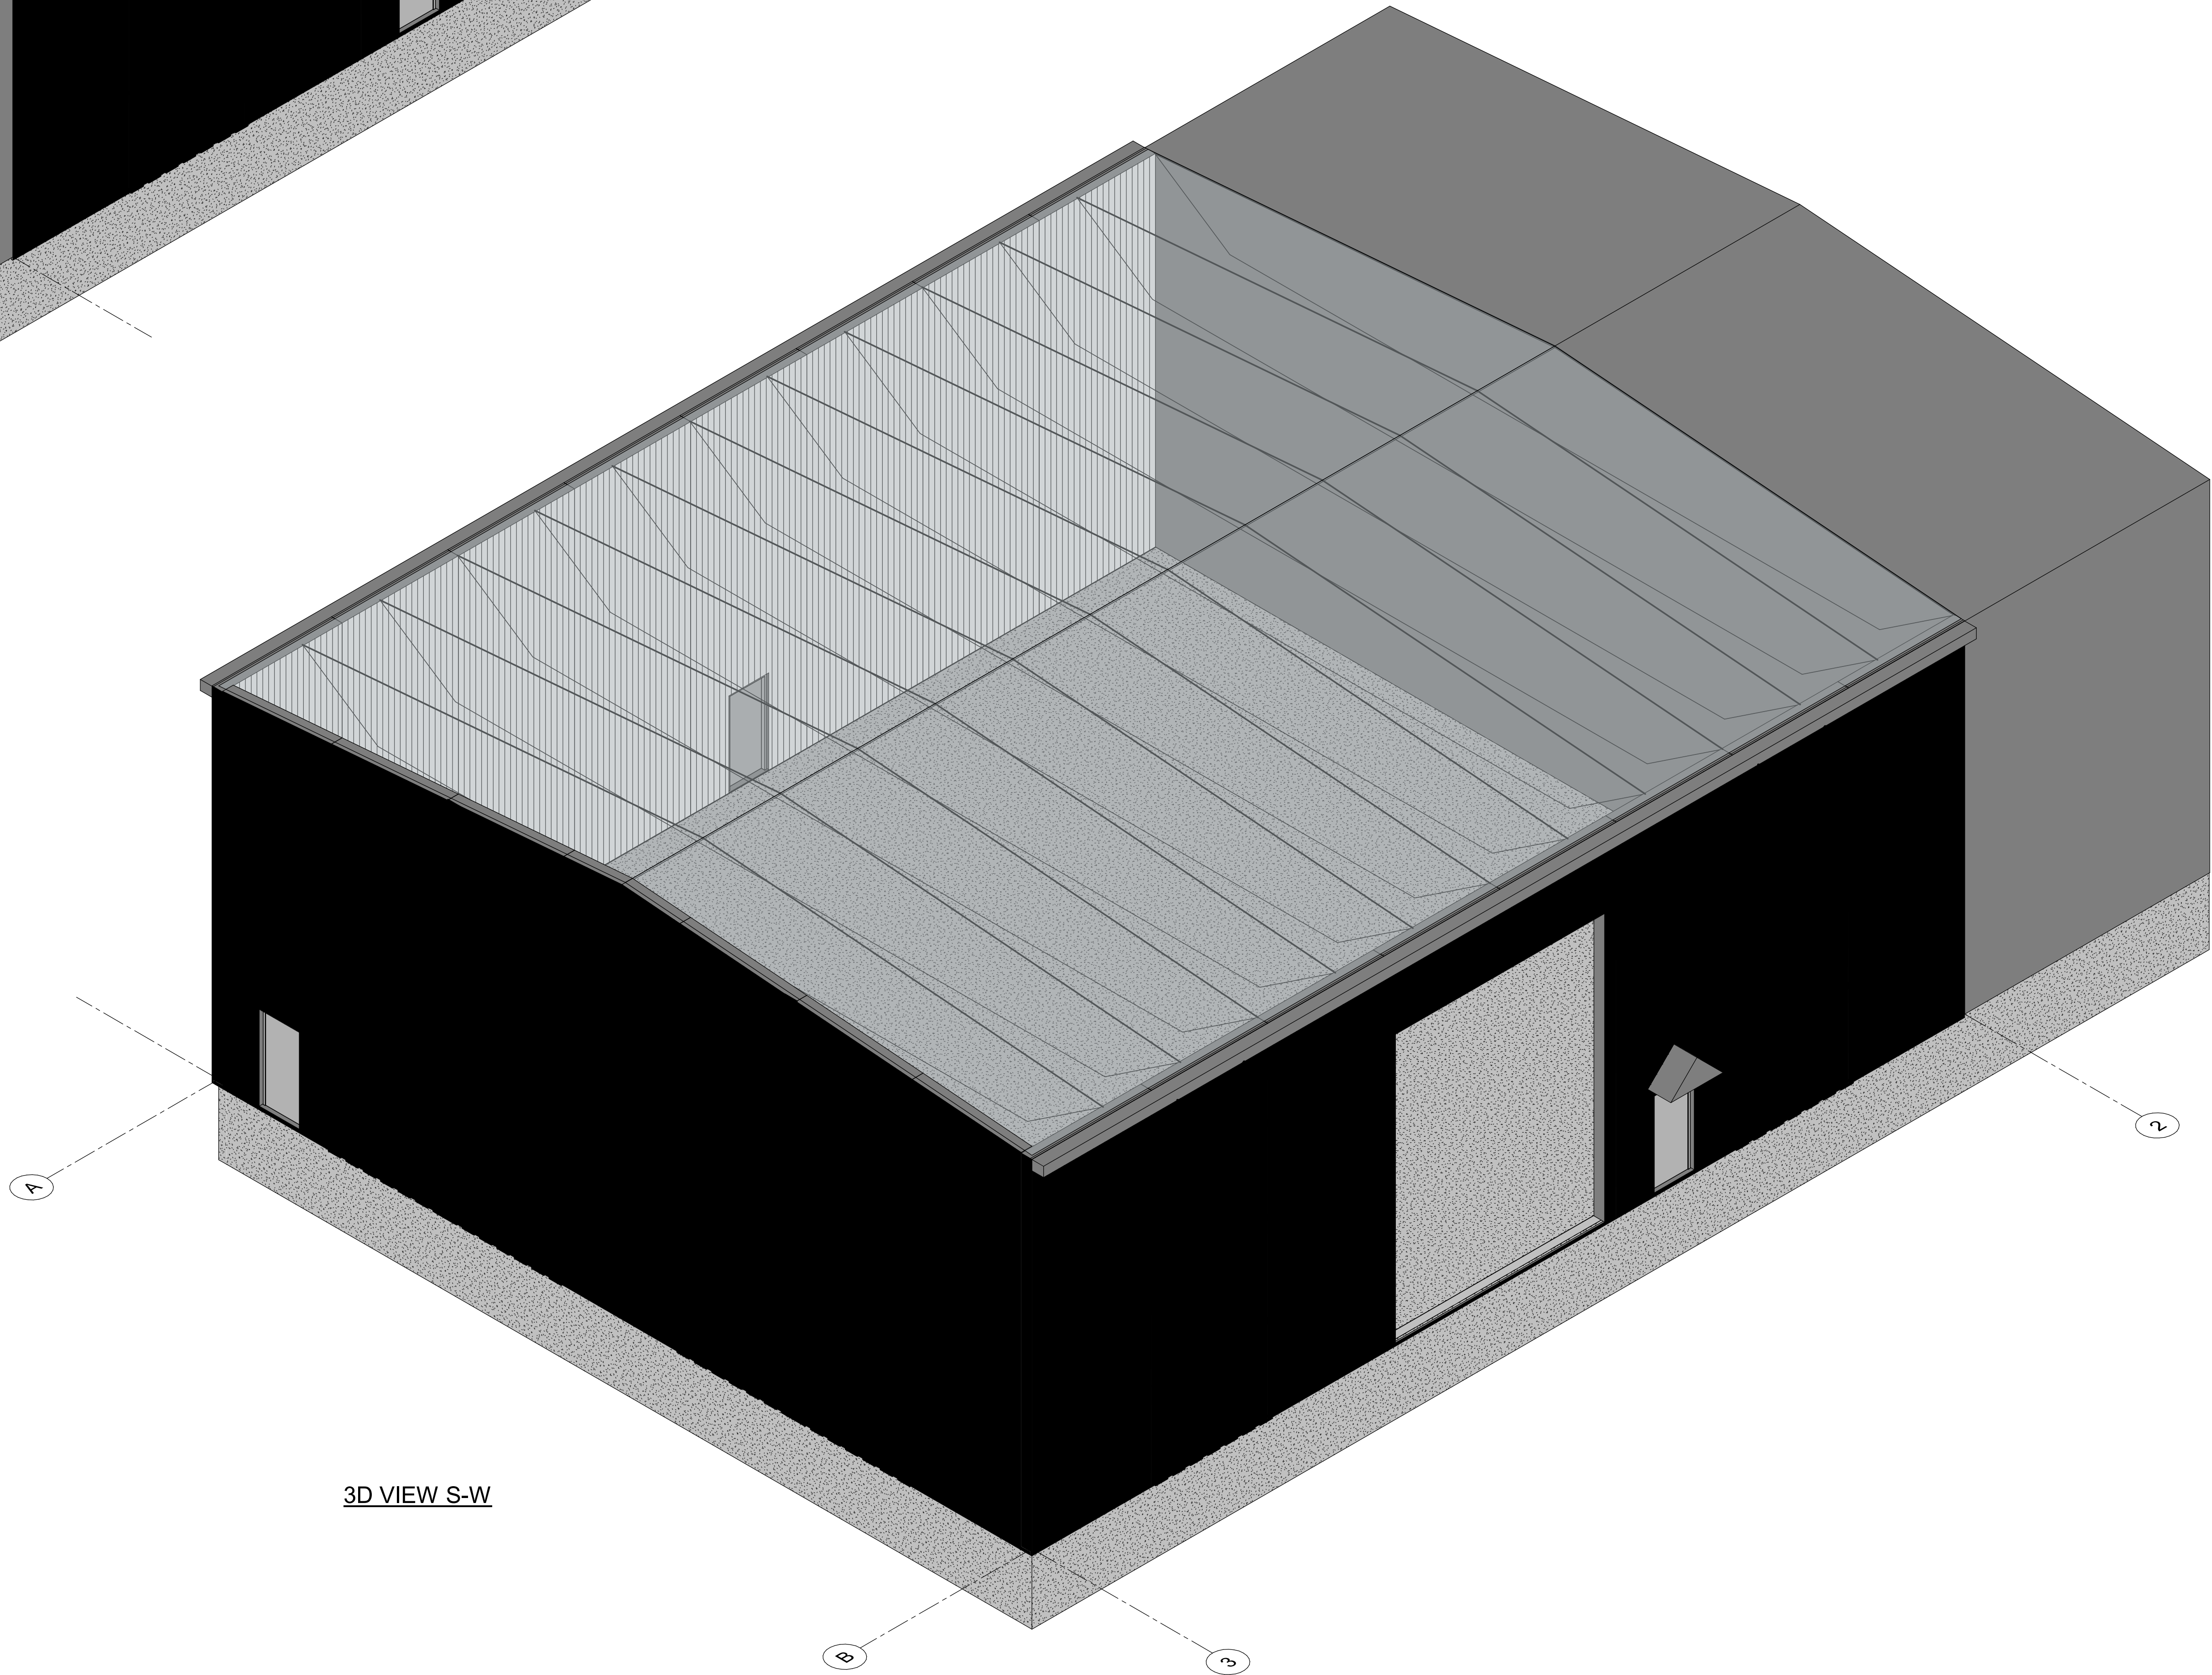

3D VIEW S-W

CONTRACTOR/RECTOR NOTE:
IT IS PROHIBITED TO MODIFY, COPY, REPRODUCE OR OTHERWISE
DISTRIBUTE THIS DRAWING OR ANY REPRESENTATION OF THIS
DRAWING, OR ANY MEDIA, INCLUDING ELECTRONIC, WITHOUT THE
PRIOR WRITTEN APPROVAL OF CANAM GROUP INC.

PRELIMINARY SHEET LIST	
EsMx001	PRELIMINARY SKETCH - 3D VIEWS
EsMx001	PRELIMINARY SKETCH - ROOF PLAN
EsMx001	PRELIMINARY SKETCH - ELEVATIONS
EsMx002	PRELIMINARY SKETCH - ELEVATION, WALL SECTION AND SCHEDULES
EsMx001	PRELIMINARY SKETCH - DETAILS


[Click here for 3D model](#)

PRELIMINARY

NOT TO BE USED FOR CONSTRUCTION

REVISION	DATE	DESCRIPTION	ISSUE	VER
PROJECT MANAGER				
		-		
		-		
		-		
DRAFTING				
		-		
DRAWN	SL	DESIGNED	PROJECT ENGINEER	SCALE: 1/2" = 1'-0"
CHECKED		CONSULTING ENGINEERS / ARCHITECTS	DATE (yyyy/mm/dd): 2028/04/08	

CUSTOMER:

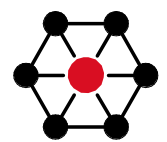**CANAM**
11505, 1re Avenue, bureau 500, Saint-Georges Beauce
Châteauguay, Québec, G5Y 7Y3
Phone : (418) 228-8031
Toll free : (877) 499-6049
www.canam.com

PROFESSIONAL SEAL


PROJECT

ESTEVAN, SASKATCHEWAN

DRAWING TITLE

PRELIMINARY SKETCH - 3D VIEWS

CONTRACT NUMBER	DRAWING NUMBER	DIVISION	REVISION
P2026-079	EsMx001		

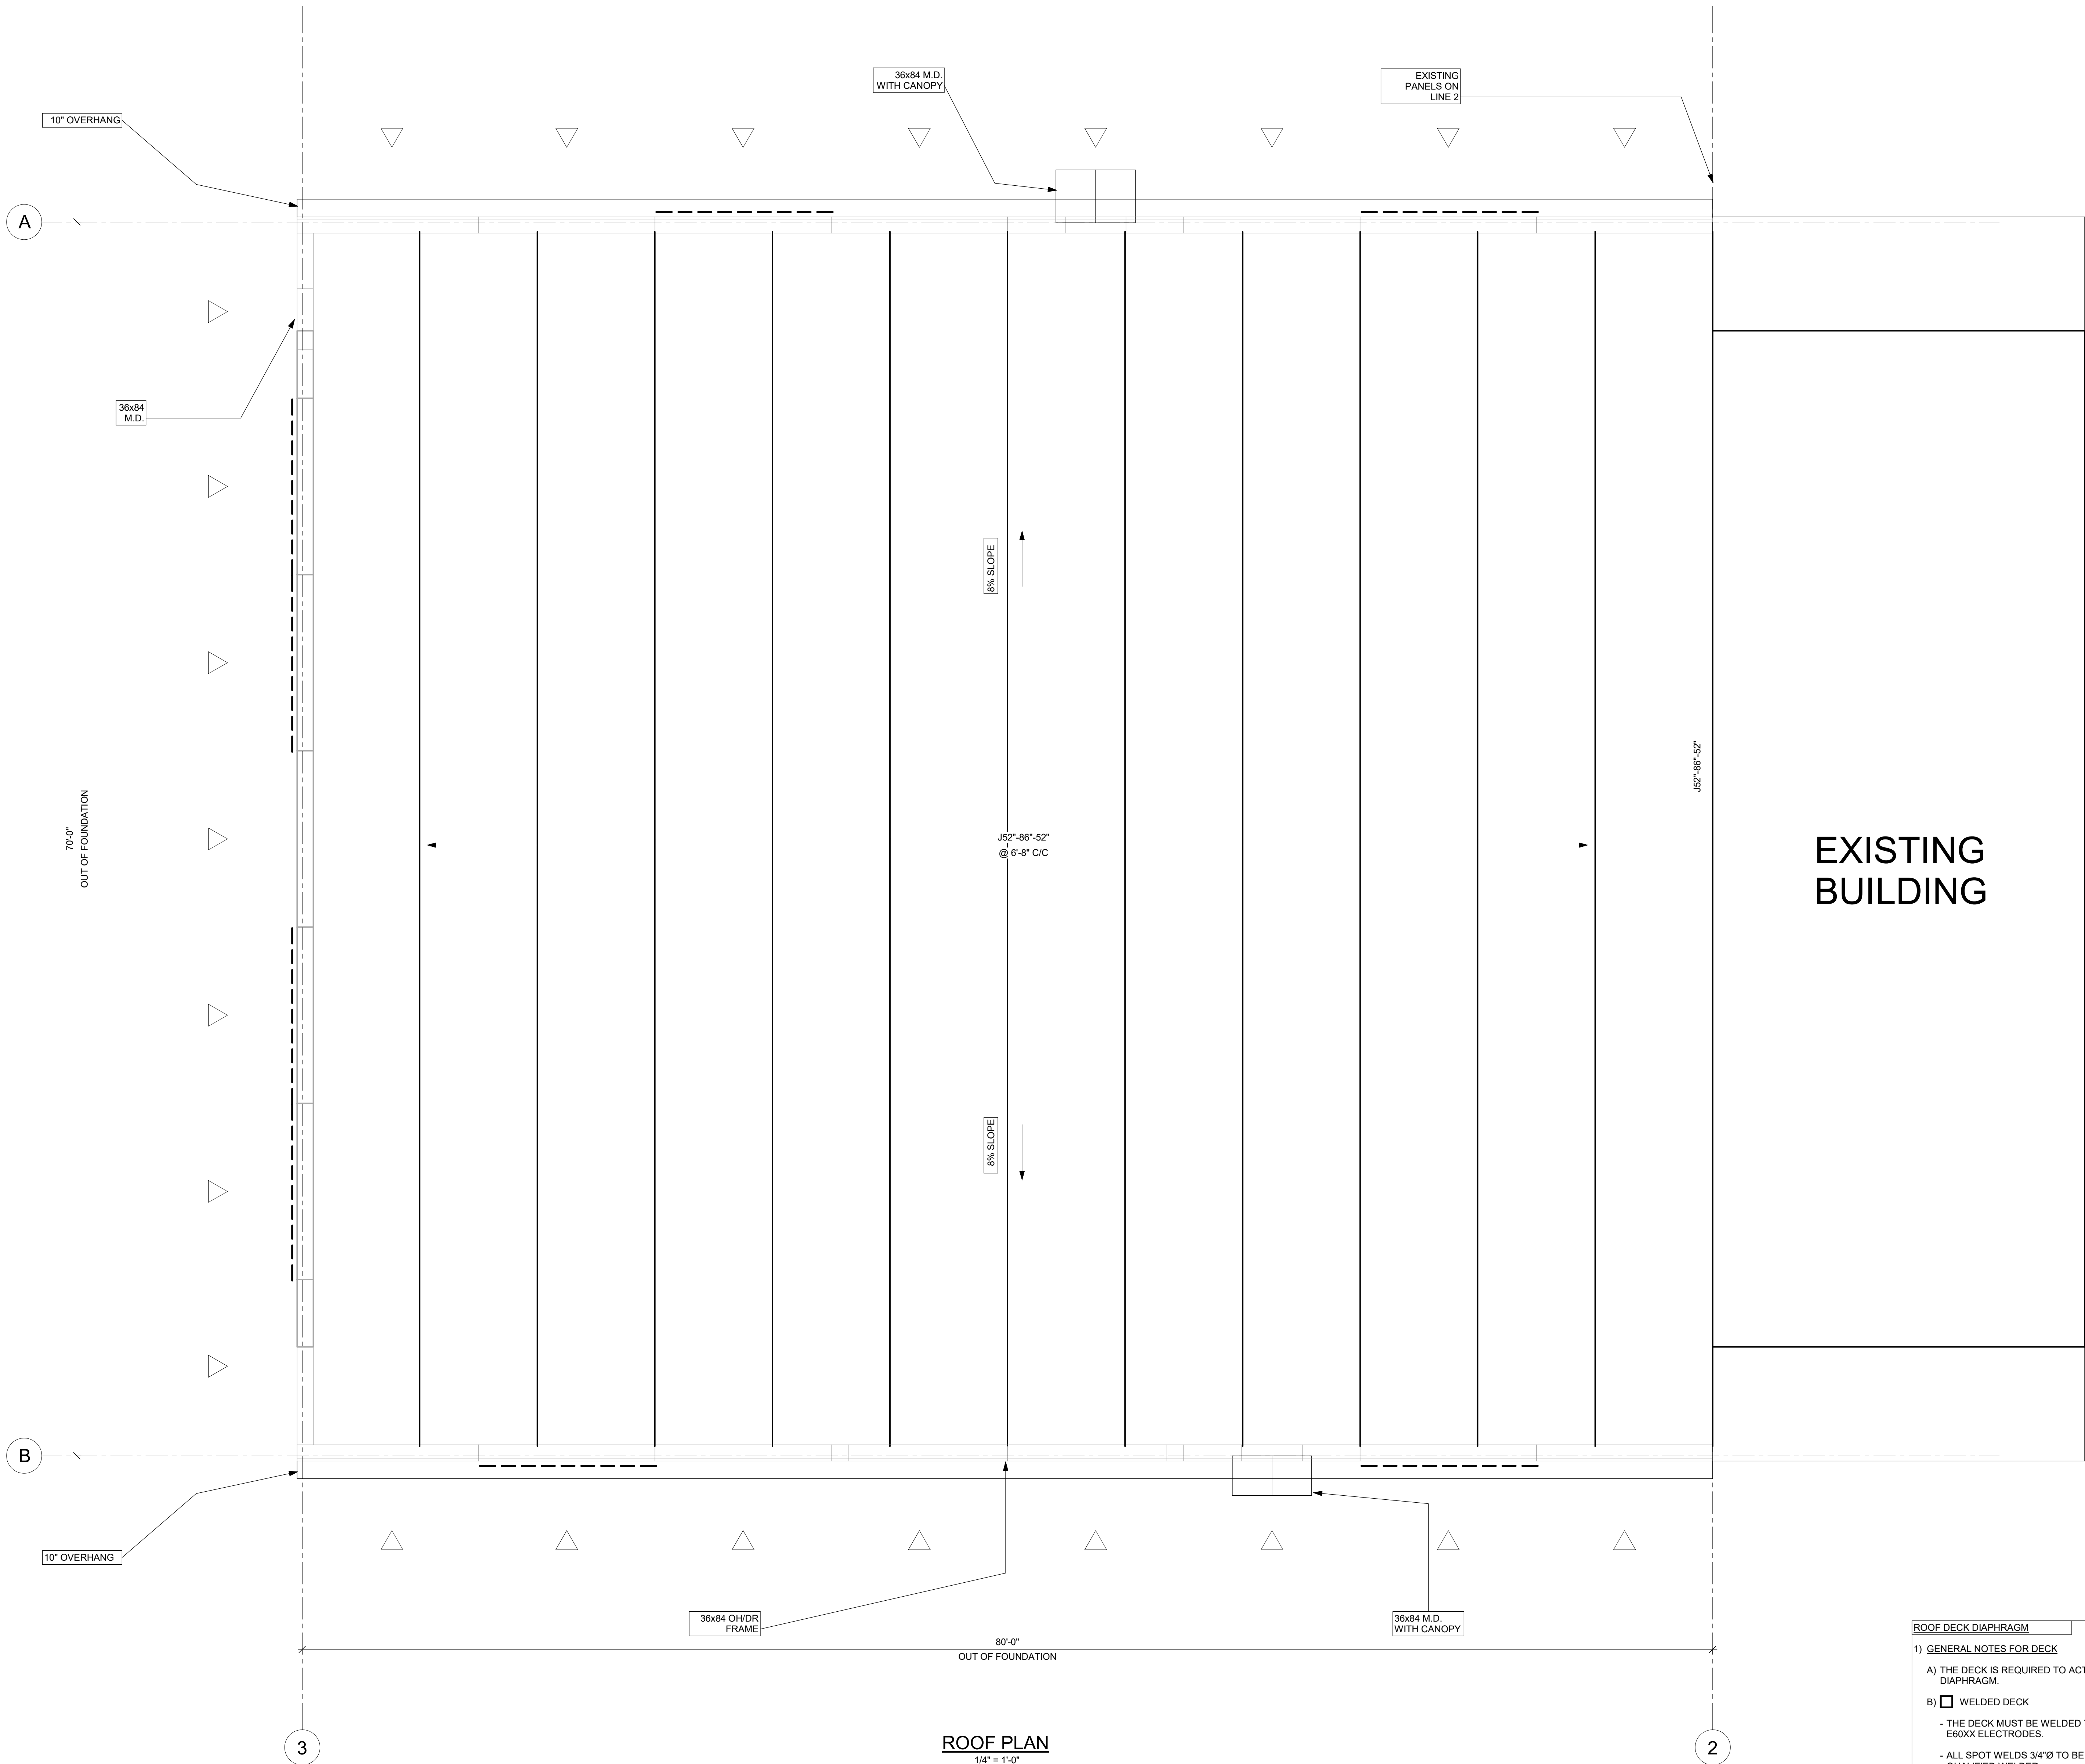


ROOF PLAN
1/4" = 1'-0"


ROOF DECK DIAPHRAGM

1) GENERAL NOTES FOR DECK

- A) THE DECK IS REQUIRED TO ACT AS A LATERAL FORCE DISTRIBUTING DIAPHRAGM.
- B) ☐ WELDED DECK
- THE DECK MUST BE WELDED TO THE STRUCTURAL FRAMING SYSTEM WITH E60XX ELECTRODES.
 - ALL SPOT WELDS 3/4"Ø TO BE DONE BY CANADIAN WELDING BUREAU QUALIFIED WELDER.
 - APPLY A SUITABLE PRIMER, ON EACH BURNED TOPSIDE AREAS.
- ☐ SCREWED DECK
- THE STEEL DECK SHALL BE SCREWED TO STRUCTURAL SUPPORT WITH SCREWS TYPE TEK S #12-24x1 1/2"
- ☐ NAILED
- THE STEEL DECK SHALL BE NAILED TO STRUCTURAL SUPPORT WITH NAILS TYPE HILTI - X-HSN 24 15 x 1 1/4" (3 mm) s1 s 3/8" (10 mm)
 - X-ENP19 L15 1 x 1 1/4" (6 mm)
- THE ERECTOR IS RESPONSIBLE FOR THE FASTENING OF THE DECK TO THE STEEL STRUCTURE AND THE SELECTION OF THE FASTENER, THE TOOL, THE CARTRIDGE AS WELL AS THE POWER REGULATION OF THE TOOL, IN ACCORDANCE WITH THE PRODUCT SPECIFICATIONS.
- C) THE MINIMUM EDGE DISTANCE MEASURED FROM CENTERLINE OF THE FASTENER TO THE END OR BOUNDARY OF THE DECK SHALL NOT BE LESS THAN 1".
- D) ERECTION SHALL BE IN ACCORDANCE WITH CSSBI 10M-2013 PUBLICATIONS, AND ALL OTHER APPLICABLE STANDARDS.

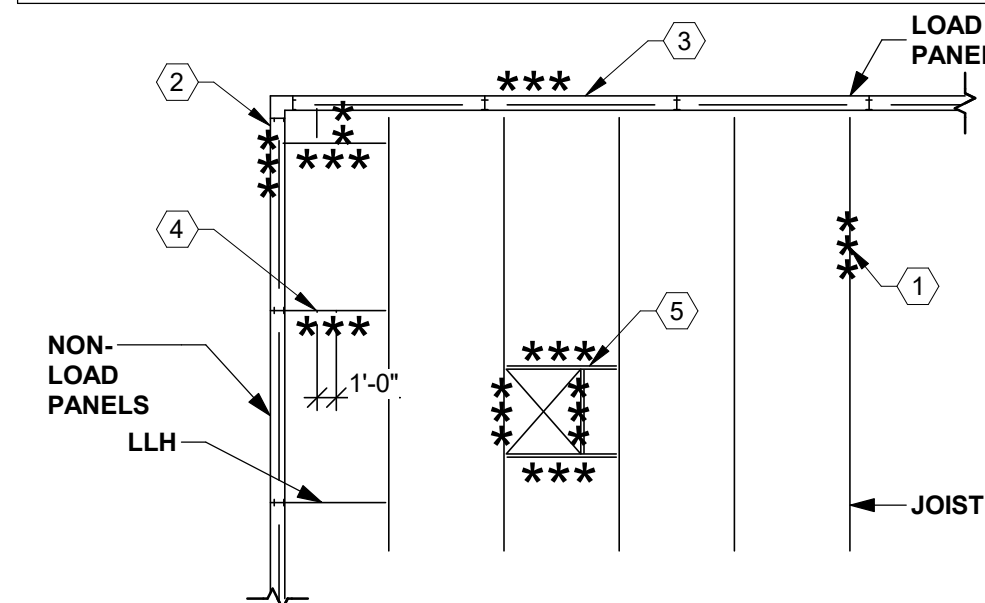



2) FASTENER PATTERN AT SUPPORT

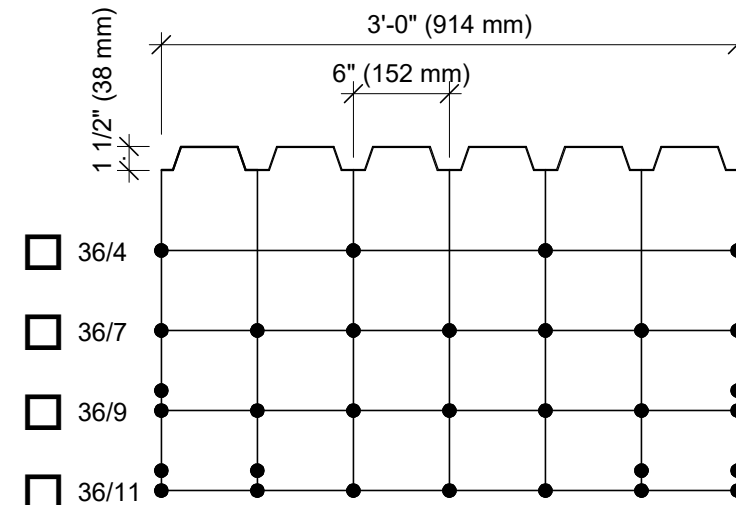

3) SIDE LAP FASTENING

SIDE LAP SHALL BE SCREW:

- ☐ SCREW TEK 2 #10 - 16 x 1/2"

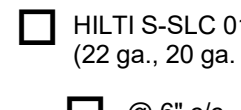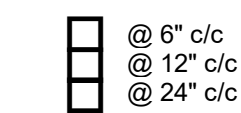

4) PERIMETER FASTENING


- 2) A) ATTACH DECK TO PERIMETER MEMBER AT EACH RIB.
- 3) B) ATTACH DECK TO PERIMETER MEMBER @ 6" c/c.
- 4) C) ATTACH DECK TO LH AND CR @ 12" c/c.
- 5) D) ATTACH DECK TO ROOF OPENING FRAMES @ 6" c/c.

5) SHEAR CONNECTORS FASTENING

A) PROVIDE ATTACHMENT BETWEEN DECK AND EACH SHEAR CONNECTOR WITH:

- ☐ SPOT WELD 3/4" @ 6" c/c TYP. U/N
- ☐ SCREW TEK S #12-24x1" @ 6" c/c TYP. U/N
- ☐ HILTI NAIL X-HSN 24 @ 6" c/c TYP. U/N

GROSS UPLIFT DIAGRAM (UNFACTORED):

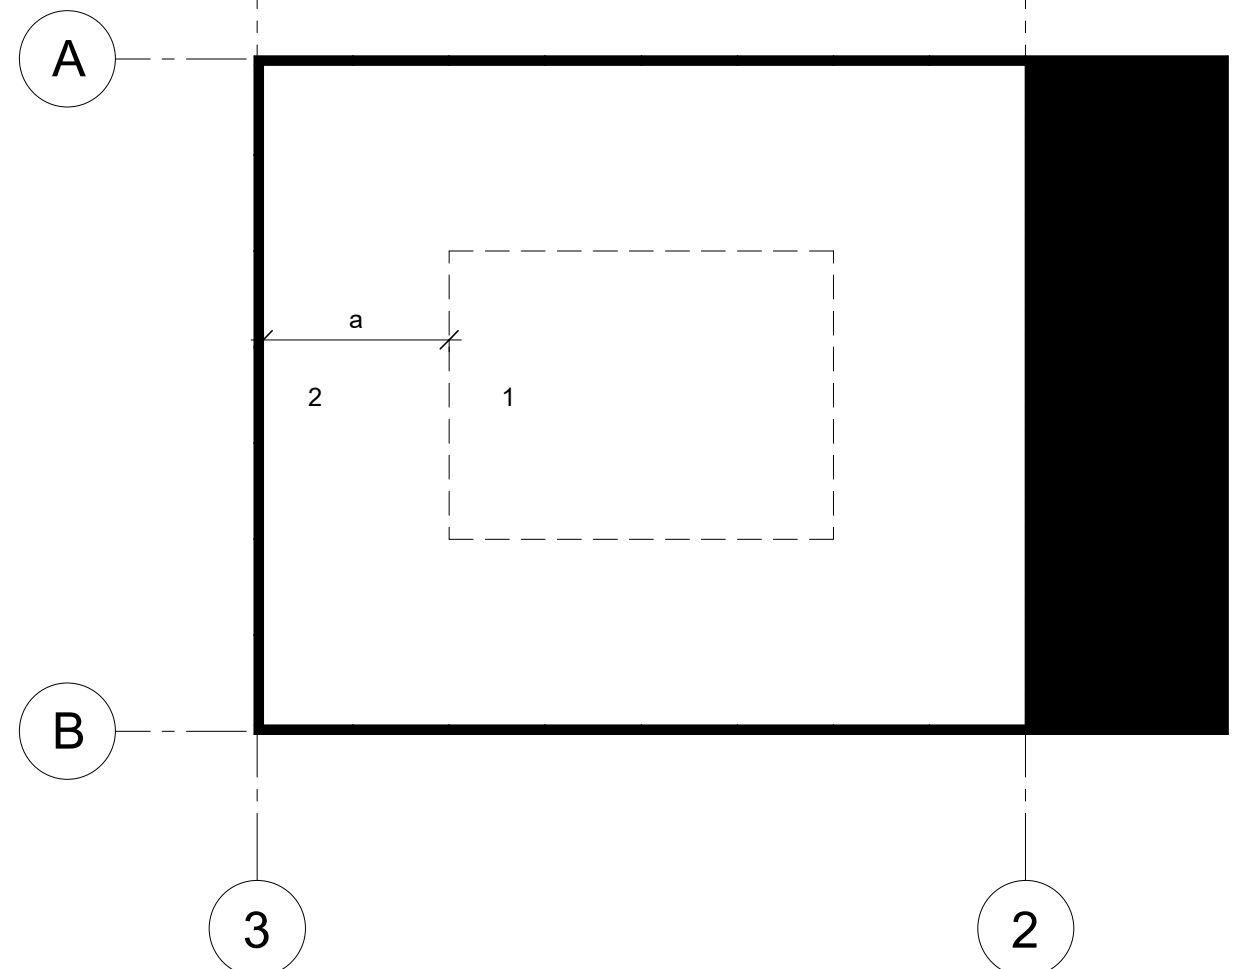

POSITIVE WIND PRESSURE
(UNFACTORED): psf
ZONE 1 : psf
ZONE 2 : psf
a)

CONTRACTOR/ERECTOR NOTE:

IT IS PROHIBITED TO MODIFY, COPY, REPRODUCE OR OTHERWISE DISTRIBUTE THIS DRAWING OR ANY REPRESENTATION OF THIS DRAWING, OR ANY MEDIA, INCLUDING ELECTRONIC, WITHOUT THE PRIOR WRITTEN APPROVAL OF CANAM GROUP INC.

ROOF:

TOP OF PILASTER : 99'-0"
TOP OF SLAB : 100'-0"
TOP OF FOUNDATION : 100'-0"
CLEAR HEIGHT : 25'-0"
TOP OF STEEL (LOW) : 122'-4"
TOP OF STEEL (HIGH) : 132'-2"

LOADS:

D.L. : psf
Coll. : psf
Sl. : psf
Sr. : psf
Cd x Cw : psf
Roof L.L. : psf
Roof snow load : psf
Wind q = 150 : psf

Seismic (Site class: D (Assumed))

ls :
Ss (0.2) :
Ss (0.5) :
Ss (1.0) :
Ss (2.0) :
Ss (5.0) :
Ss (10.0) :
PGA :
PGV :

LOADINGS:

- Roof dead load excluding collateral load : 18 psf
- Collateral load : 5 psf (includes lighting and/or mechanical and sprinklers of 4 inches in diameter and less)
- Roof snow load : psf
- Wind load q 150 : psf
- Roof live load : Ss = psf
- Ground snow load : Ss = psf
- Risk Category : normal
- Snow load factors : Cb = 0.8
- Snow load factors : Cw = 1.0

• Code Applicable : National building Code of Canada
Saskatchewan Building Code, latest adopted editions
Code of Standard Practice CISC.

• Assumed soil site class: D

NOTE:

1. If, however, the seismic site class is determined to be E or F according to the geotechnical report, the preliminary structural concept (location and geometry of bracings, etc.) must be validated and coordinated by a Canam's engineer.

PRELIMINARY

NOT TO BE USED FOR CONSTRUCTION

REVISION	DATE	DESCRIPTION	ISSUE	VER
----------	------	-------------	-------	-----

PROJECT MANAGER	-
-	-
-	-
-	-
-	-

DRAWING	DESIGNED	PROJECT ENGINEER	SCALE:
INITIALE			Comme indiqué
CHECKED	CONSULTING ENGINEERS ARCHITECTS	DATE (yyyy/mm/aa)	
		2028/04/08	

CUSTOMER:



11505, 1re Avenue, bureau 500, Saint-Georges Beauce
Dorval, Québec, G9V 7G3
Phone : (418) 228-8031
Toll free : (877) 499-6049
www.canam.com

PROFESSIONAL SEAL

PROJECT

ESTEVAN, SASKATCHEWAN

DRAWING TITLE

PRELIMINARY SKETCH - ROOF PLAN

NOTES STEEL DECK ROOF EN IMP (CAN)

1" = 1'-0"

Initials

CONTRACT NUMBER	DRAWING NUMBER	DIVISION	REVISION
-----------------	----------------	----------	----------

P2026-079


EsMx401




DOOR SCHEDULE				
Identity	Qty.	Door 18 ga.	Dimensions	Remarks
D1	3		36" x 84"	MAN DOOR
D2	1		18' x 23'	OHDR FRAME OPENING

Supplier's standard hardware:
- Hinges : Stanley FBB170 4.5" x 4"
- Exit device : Van Dupirel 22 x 600 with outside trim 230L
- Permanent cylinder : Schlage 2000IC 826
- Door closure : LCN 1261 669
- Head and jamb seal : Unique 1650
- Bottom seal : Unique DS4
- Threshold : See the remarks in "Door schedule"


SUPPLIER'S STD HARDWARE
1/2" = 1'-0"

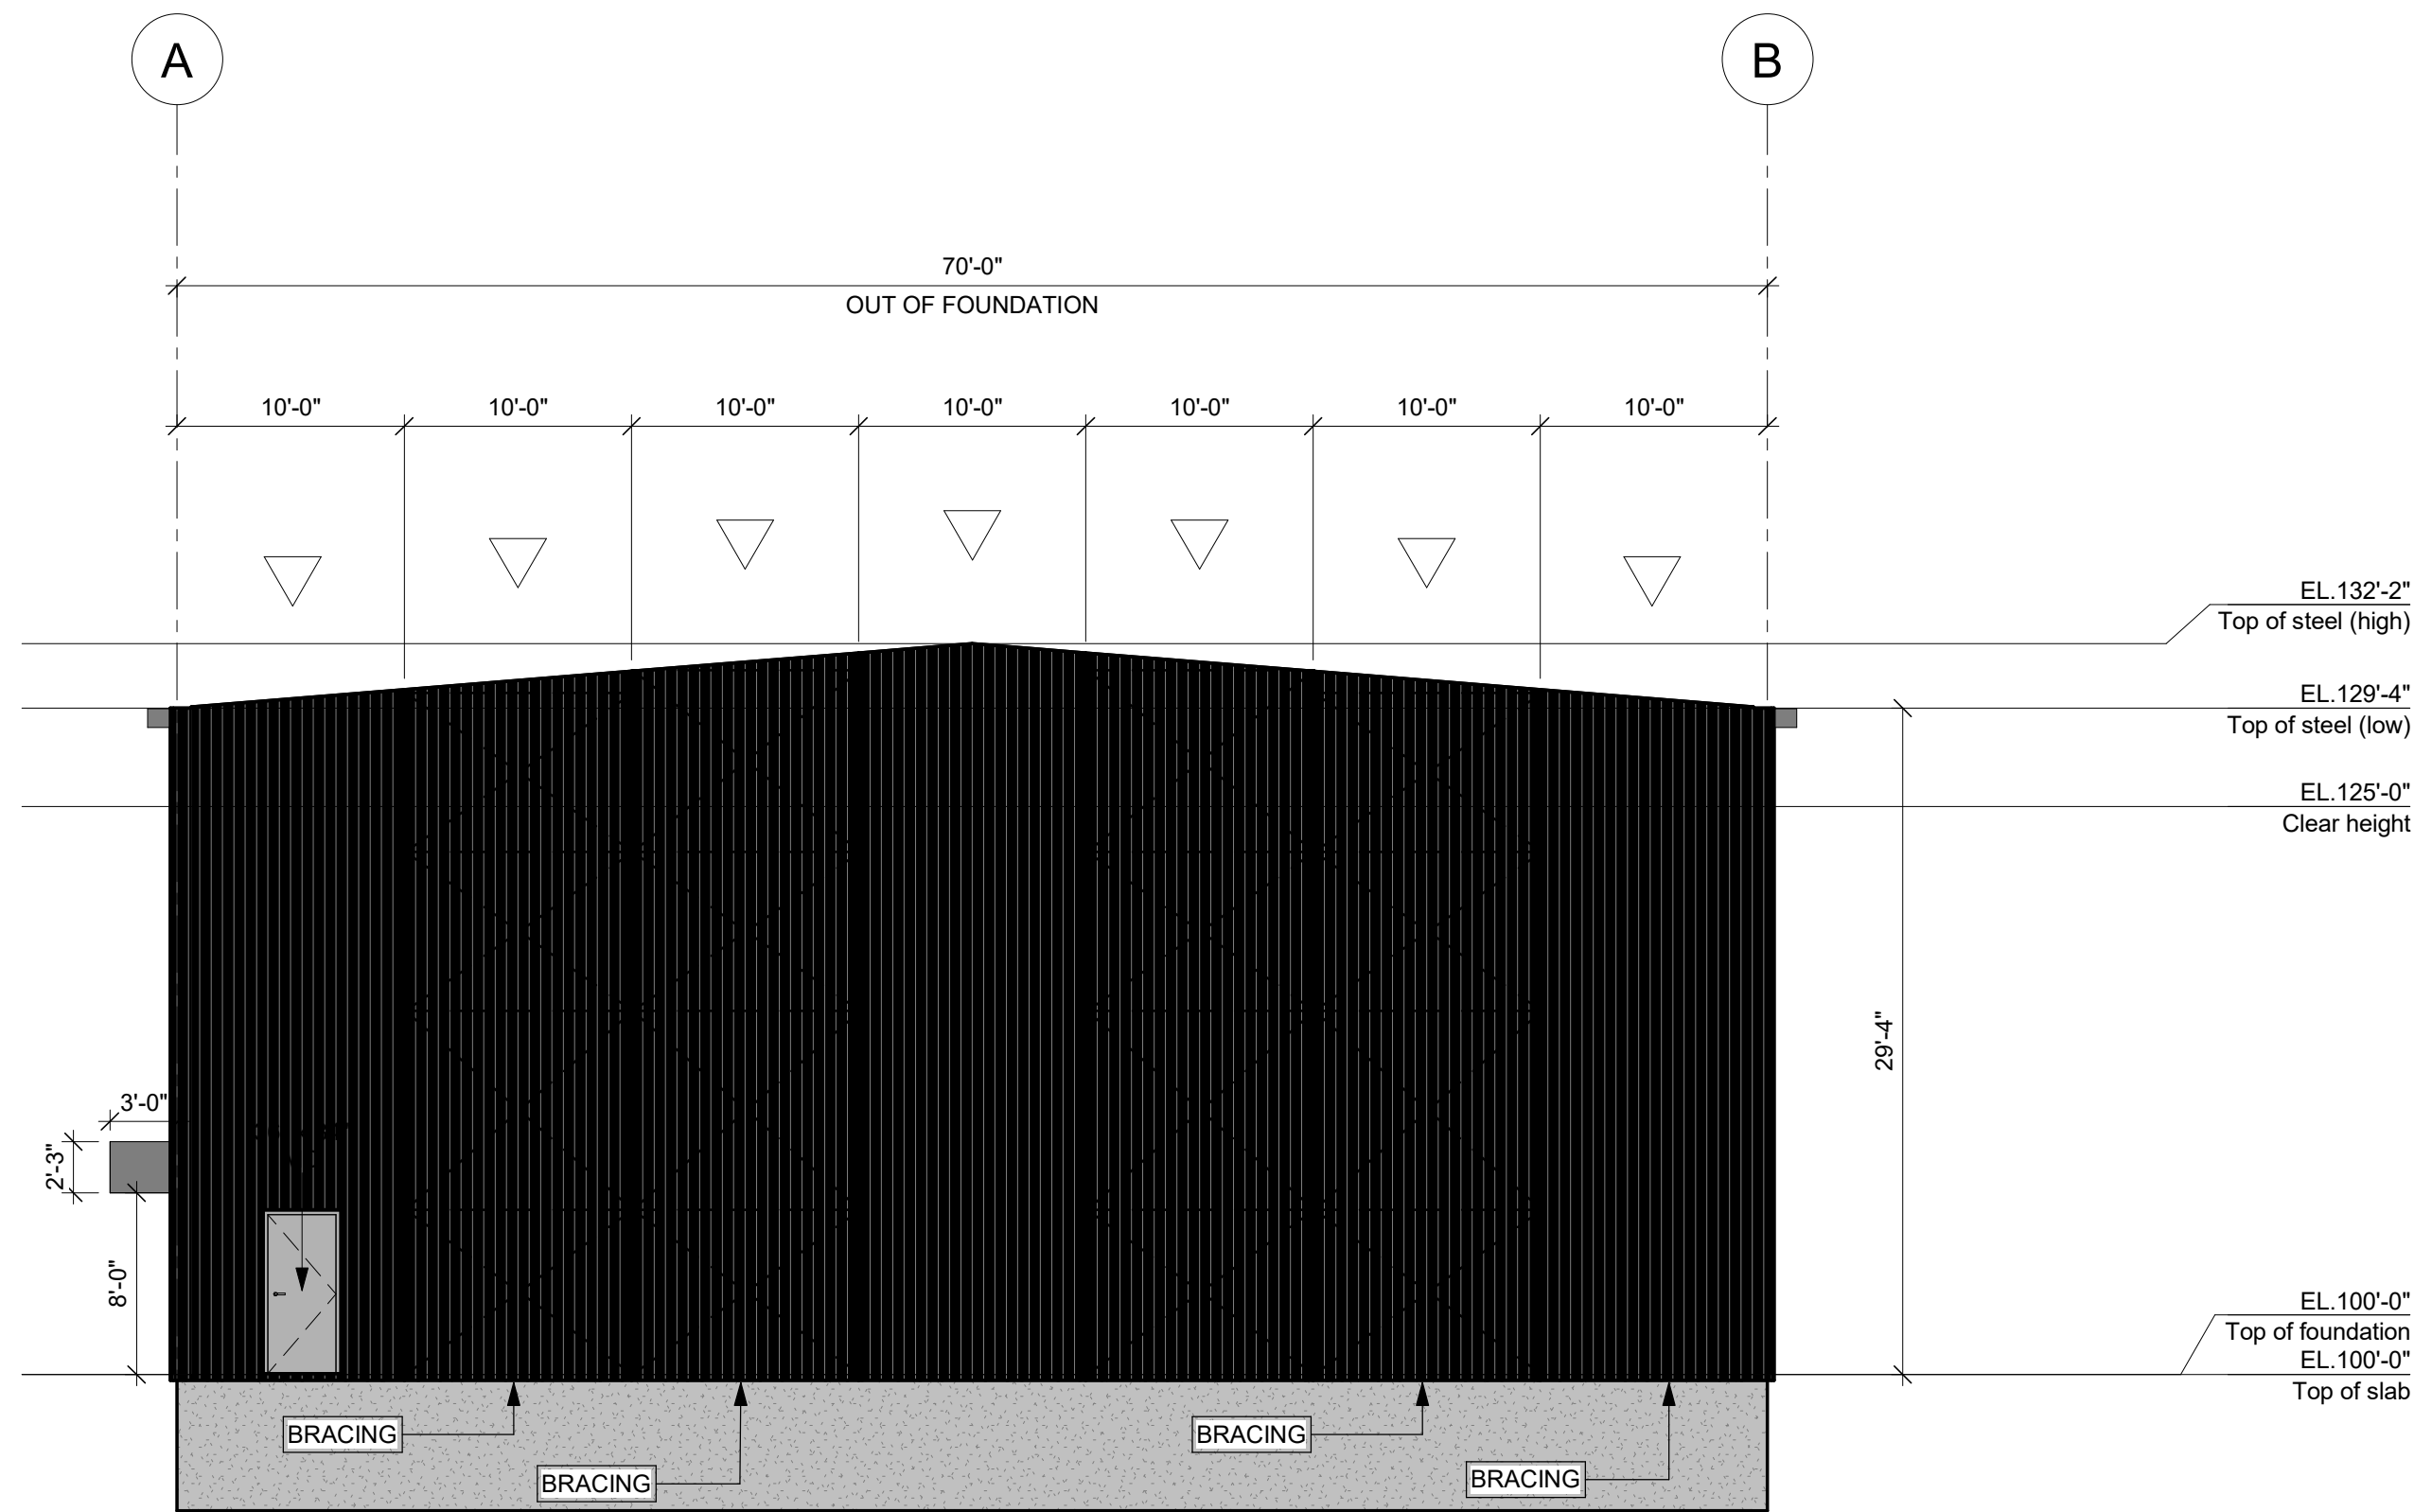


ELEVATION LINE 3 (WEST)
1/8" = 1'-0"

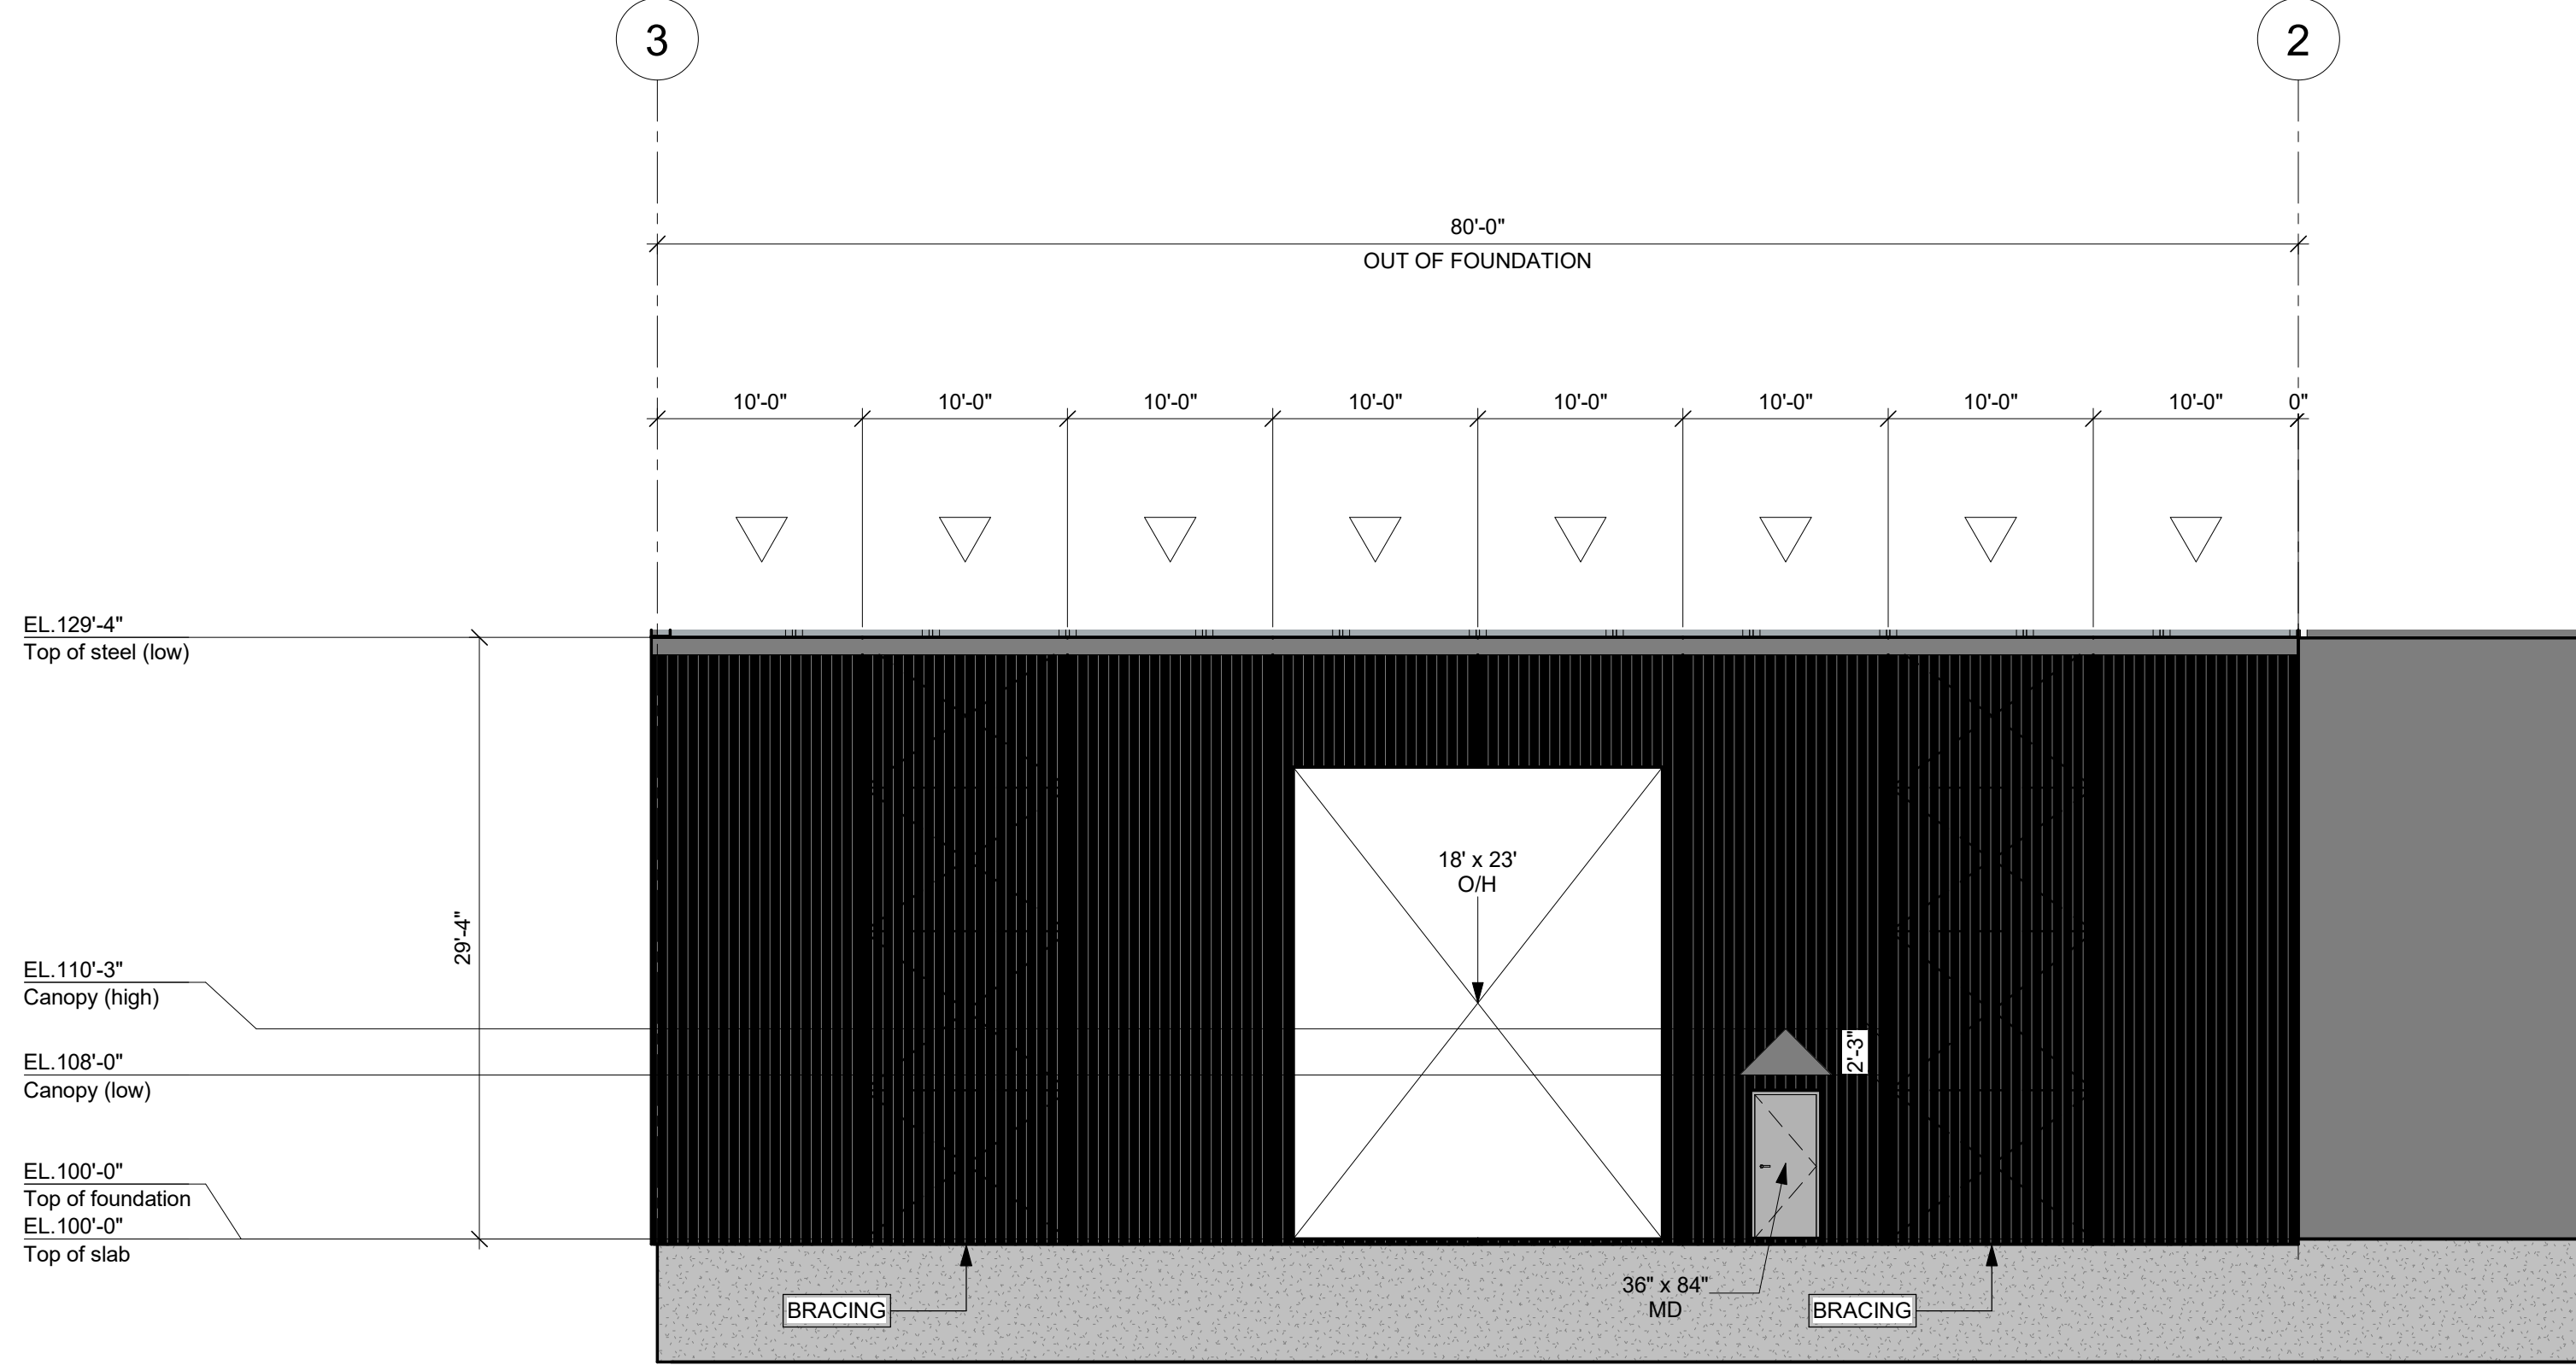

ELEVATION LINE B (SOUTH)
1/8" = 1'-0"

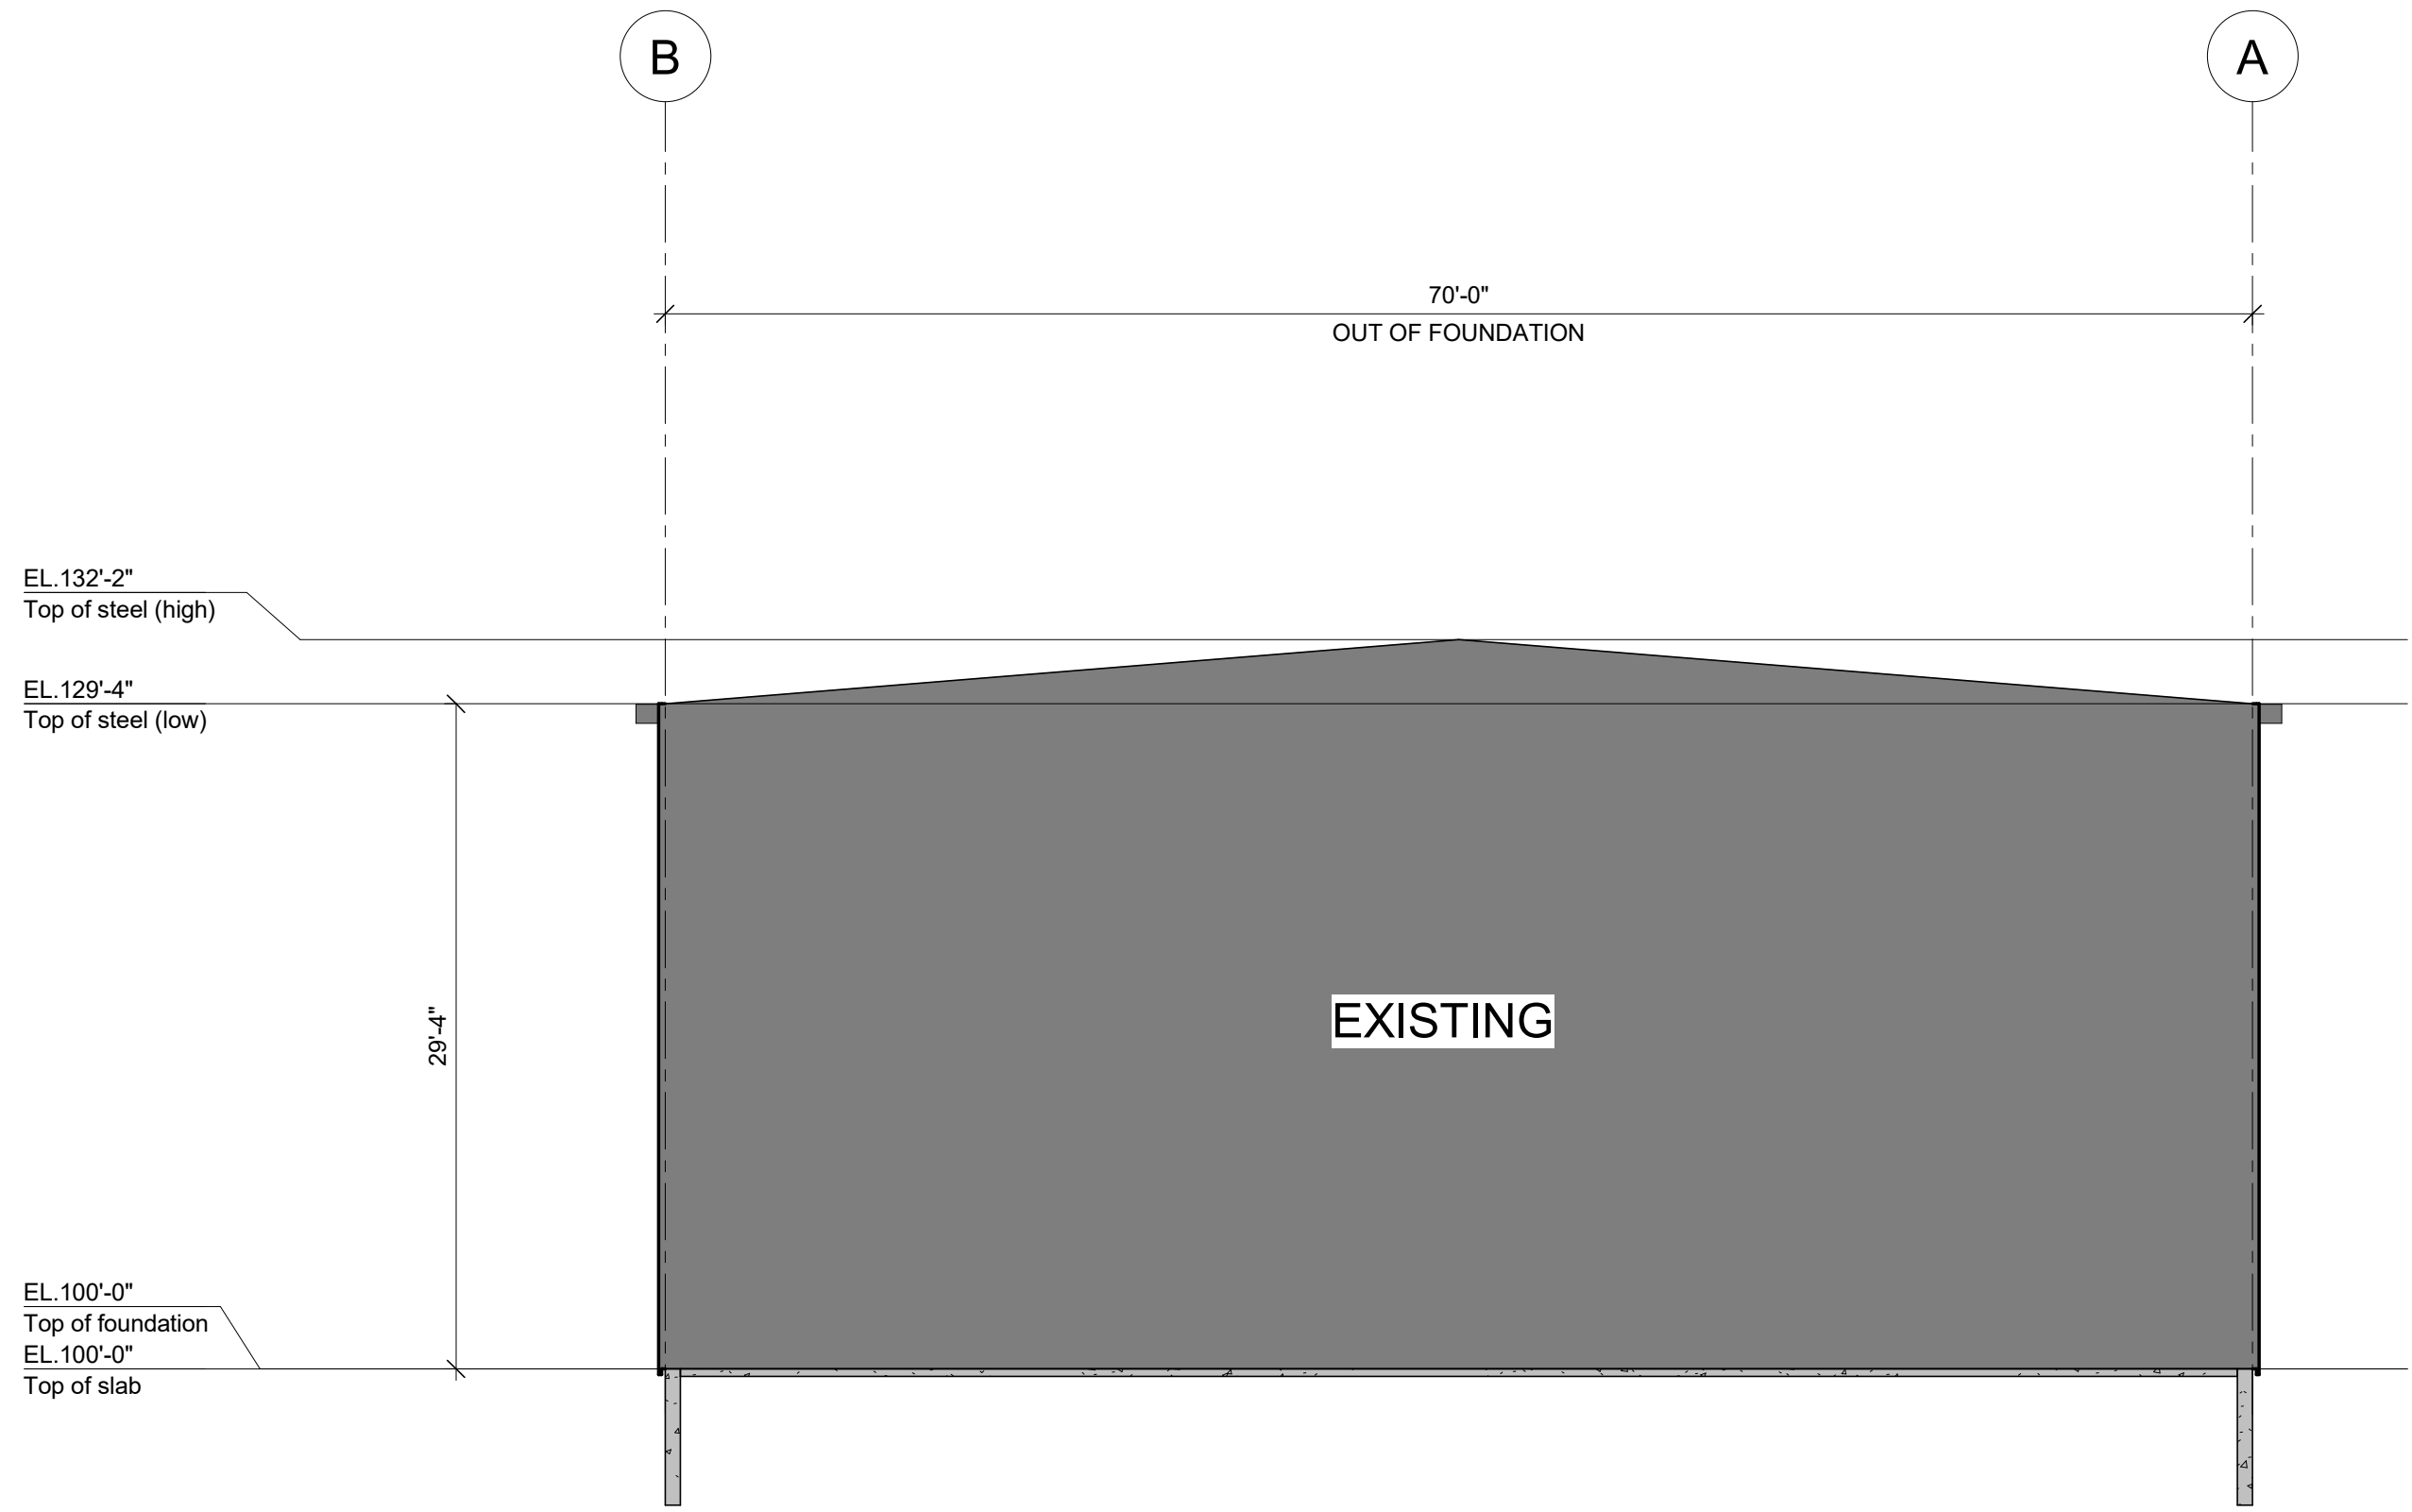

ELEVATION LINE 2 (EAST)(EXISTING)
1/8" = 1'-0"

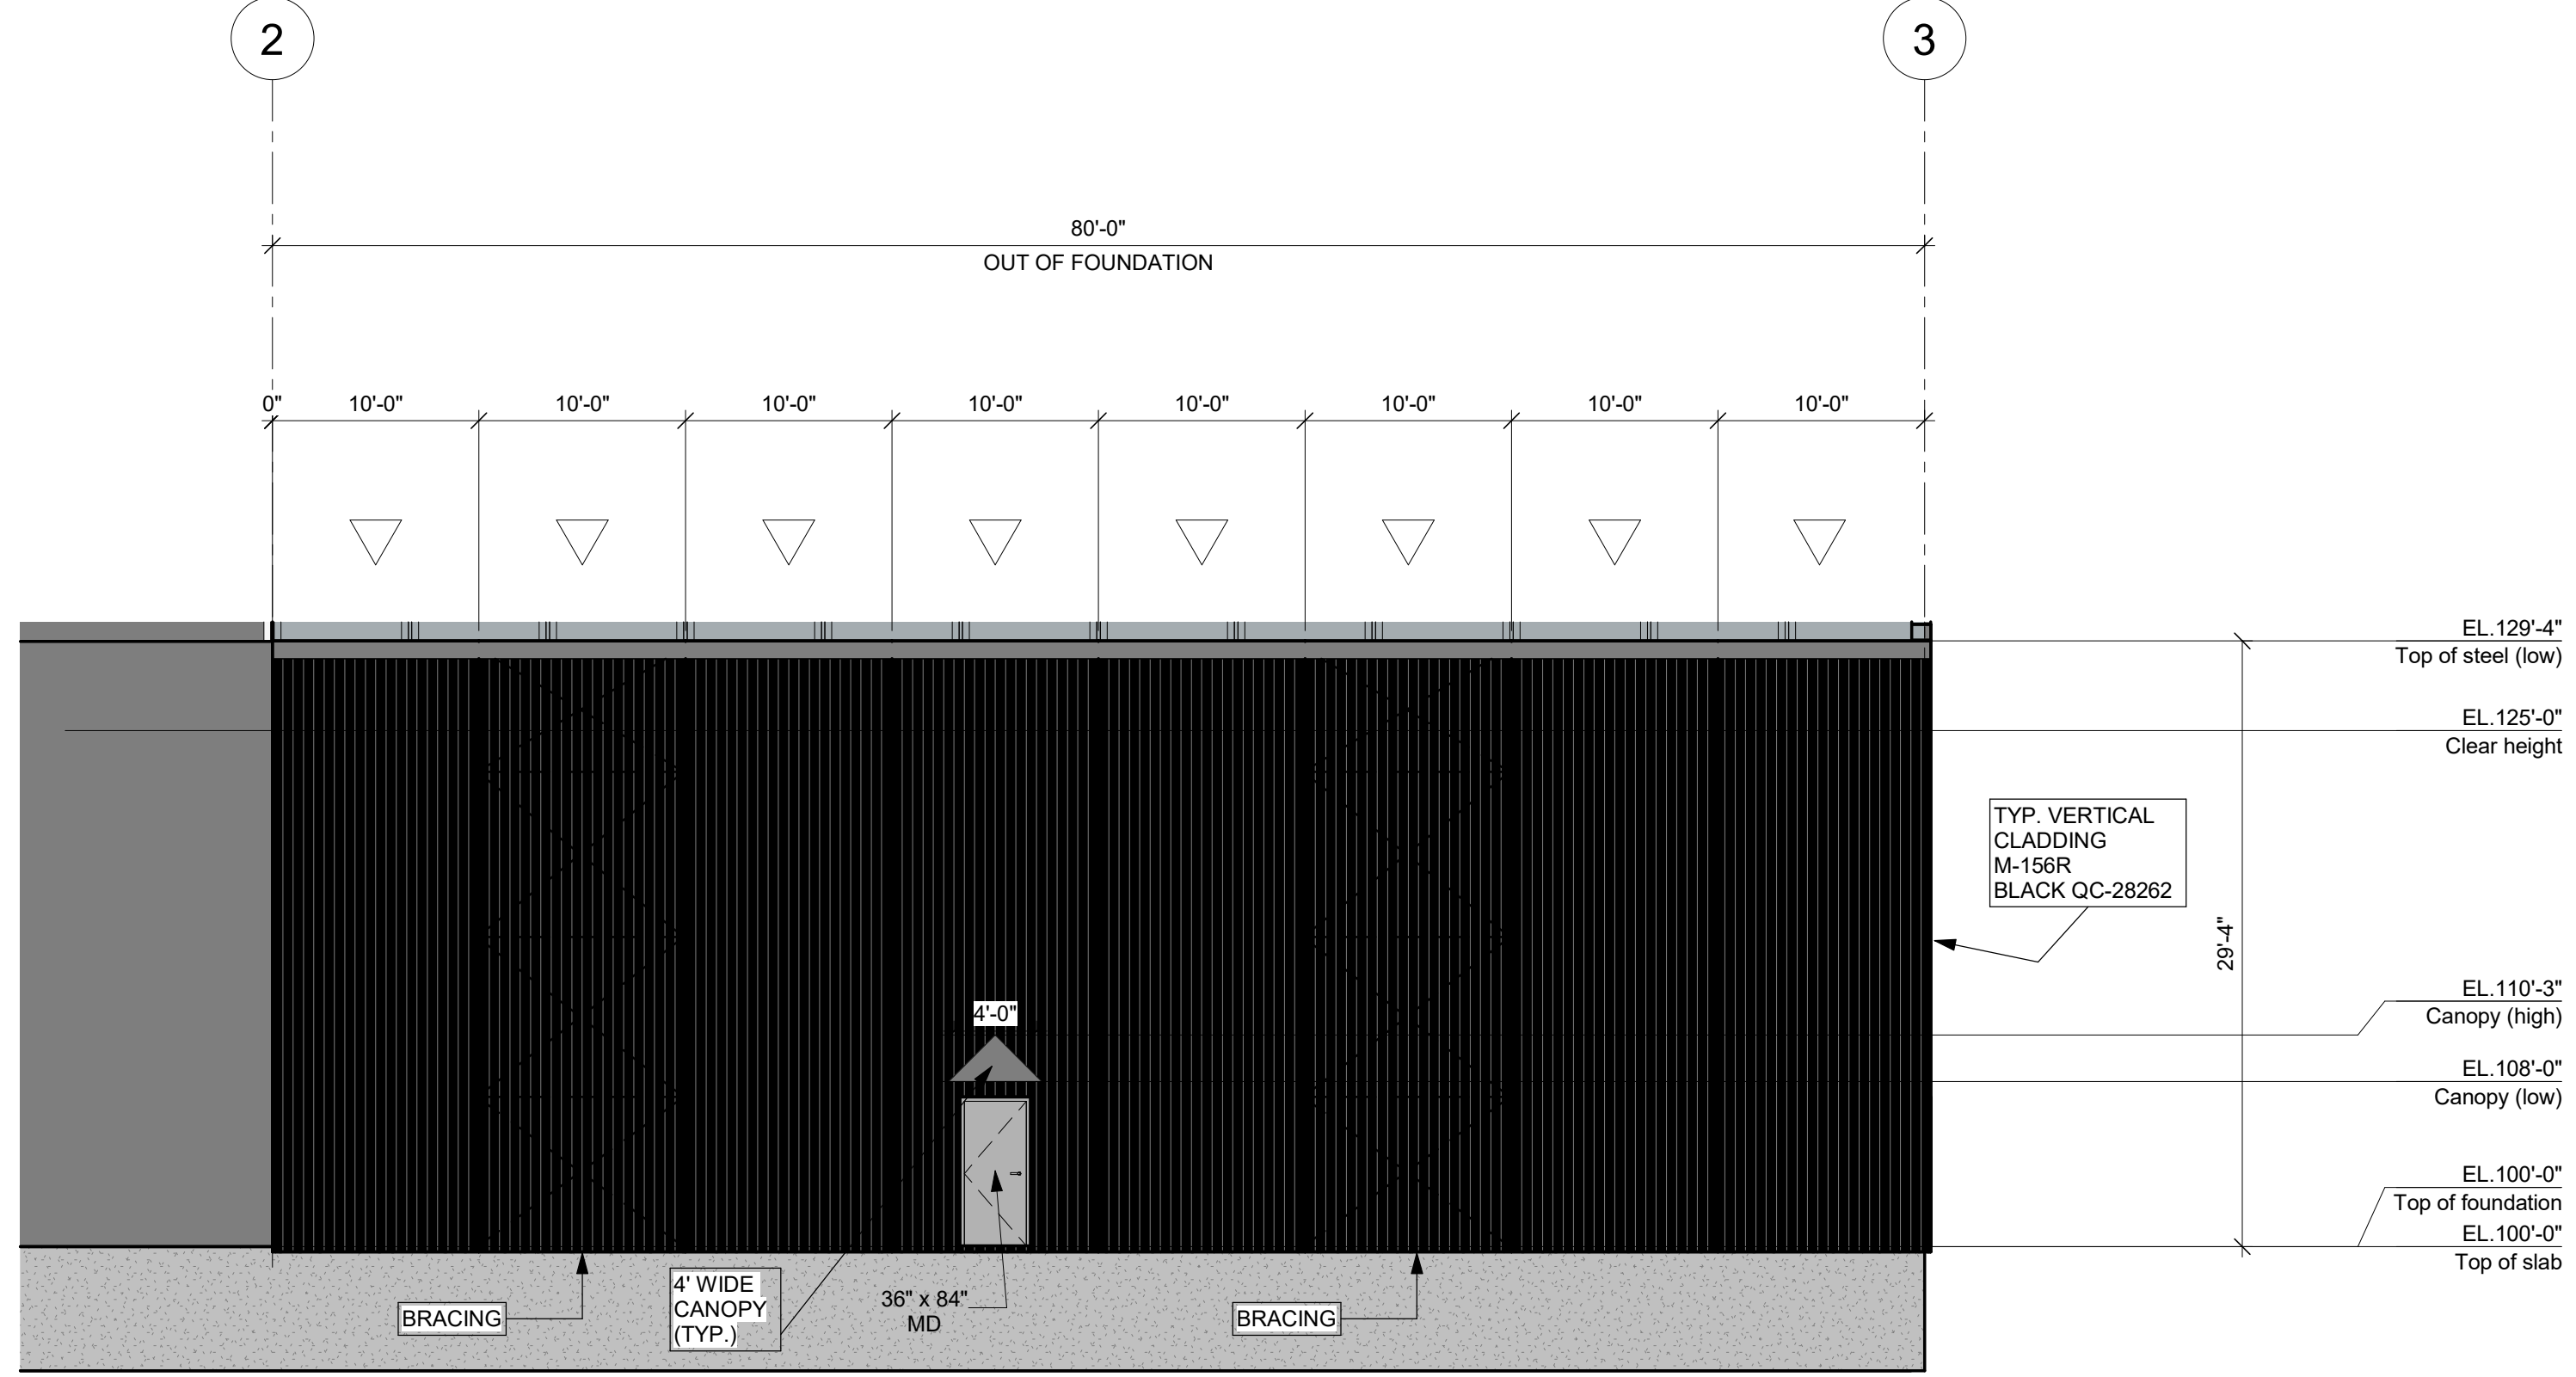

ELEVATION LINE A (NORTH)
1/8" = 1'-0"

PRELIMINARY

NOT TO BE USED FOR CONSTRUCTION

REVISION	DATE	DESCRIPTION	ISSUE	VER
----------	------	-------------	-------	-----

PROJECT MANAGER	-	-	-	-
-----------------	---	---	---	---

DRAWING	-	-	-	-
---------	---	---	---	---

INITIALE	DESIGNED	PROJECT ENGINEER	SCALE
			Comme indiqu�
CHECKED	CONSULTING ENGINEERS ARCHITECTS	DATE (yyyy/mm/aa)	
		2028/04/08	

CUSTOMER:

CANAM
11505, 1re Avenue, bureau 500, Saint-Georges Beauce
Quebec, Canada, G5Y 7G3
Phone : (418) 228-8031
Toll free : (877) 499-6049
www.canam.com

PROFESSIONAL SEAL

PROJECT

ESTEVAN, SASKATCHEWAN

DRAWING TITLE

PRELIMINARY SKETCH - ELEVATIONS

CONTRACT NUMBER	DRAWING NUMBER	DIVISION	REVISION
P2026-079	EsMx501		

