

30x40

CÉDULE DES FENÊTRES					
Identifiant	Qté.	Description	Dimensions ext. cadre largeur X hauteur	Couleur du cadre	Remarques
F1	19	Fenêtre en aluminium fixe avec bris thermique et verre scellé + Low-E argon clair	6'-0" x 4'-0"	Cadre d'Aluminium (Blanc ext. et int.)	
F2	4	Fenêtre en aluminium fixe avec bris thermique et verre scellé + Low-E argon clair	4'-0" x 4'-0"	Cadre d'Aluminium (Blanc ext. et int.)	


CÉDULE DES PORTES			
Identifiant	Qté.	Porte 16 ja. Dimensions	Remarques
P1	7	3'-0" x 7'-0" < multiples >	
P2	6	16'-0" x 16'-0" CADRE OUVERTURE PORTE MONTANTE	
P3	4	16'-0" x 16'-0" CADRE OUVERTURE PORTE MONTANTE	

Quincaillerie standard du fournisseur:


- Chamères : Stanley FBB179 4 5/8" x 4"
- Barre panique : Von Duprin 22 x 689 avec poignée extérieure 230L
- Cylindre permanent : Schlage 2000IC 626
- Ferme-porte : LCN 1261 669
- Coupe-froid de Mte et des montants : Unique 1650
- Coupe-froid du bas : Unique 1054
- Seuil : Voir la remarque dans la "Cédule de porte"

CÉDULE DES P.M. ET DES OUVERTURES				
Total	Type	Tag	Commentaires	
1	6'-0" x 7'-0"	OUV	OUVERTURE	


Total général: 1

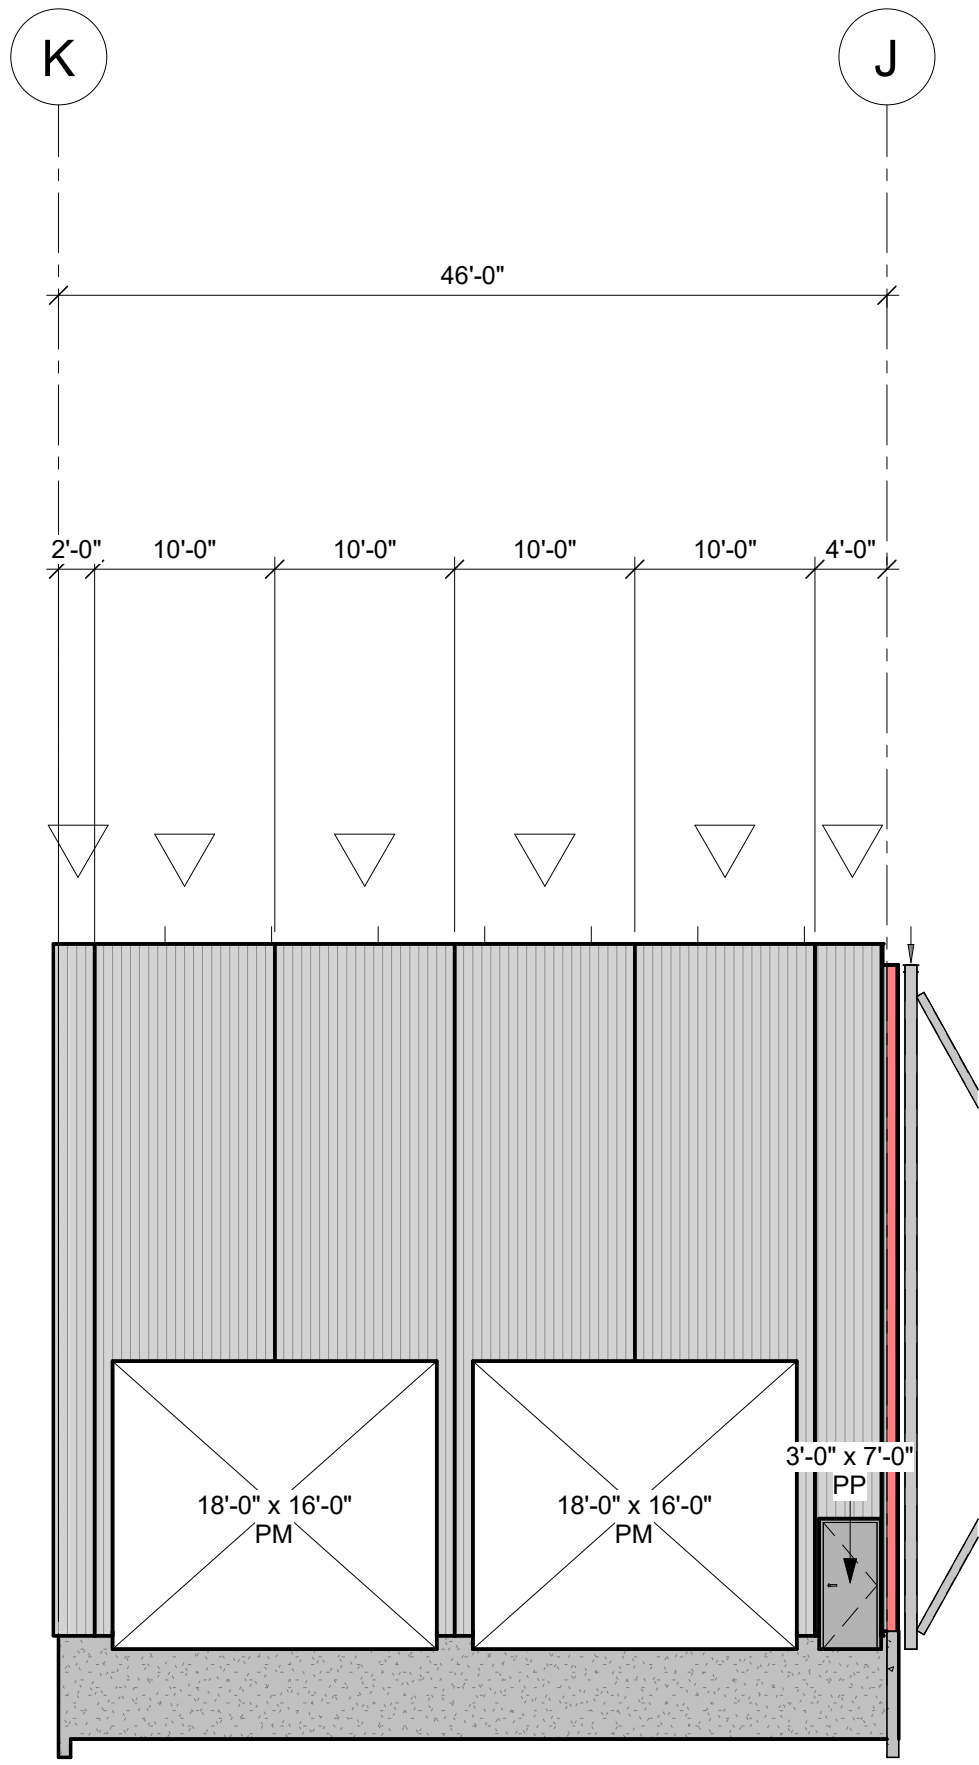


ÉLÉVATION AXE 3.6 (EST)
3/32" = 1'-0"

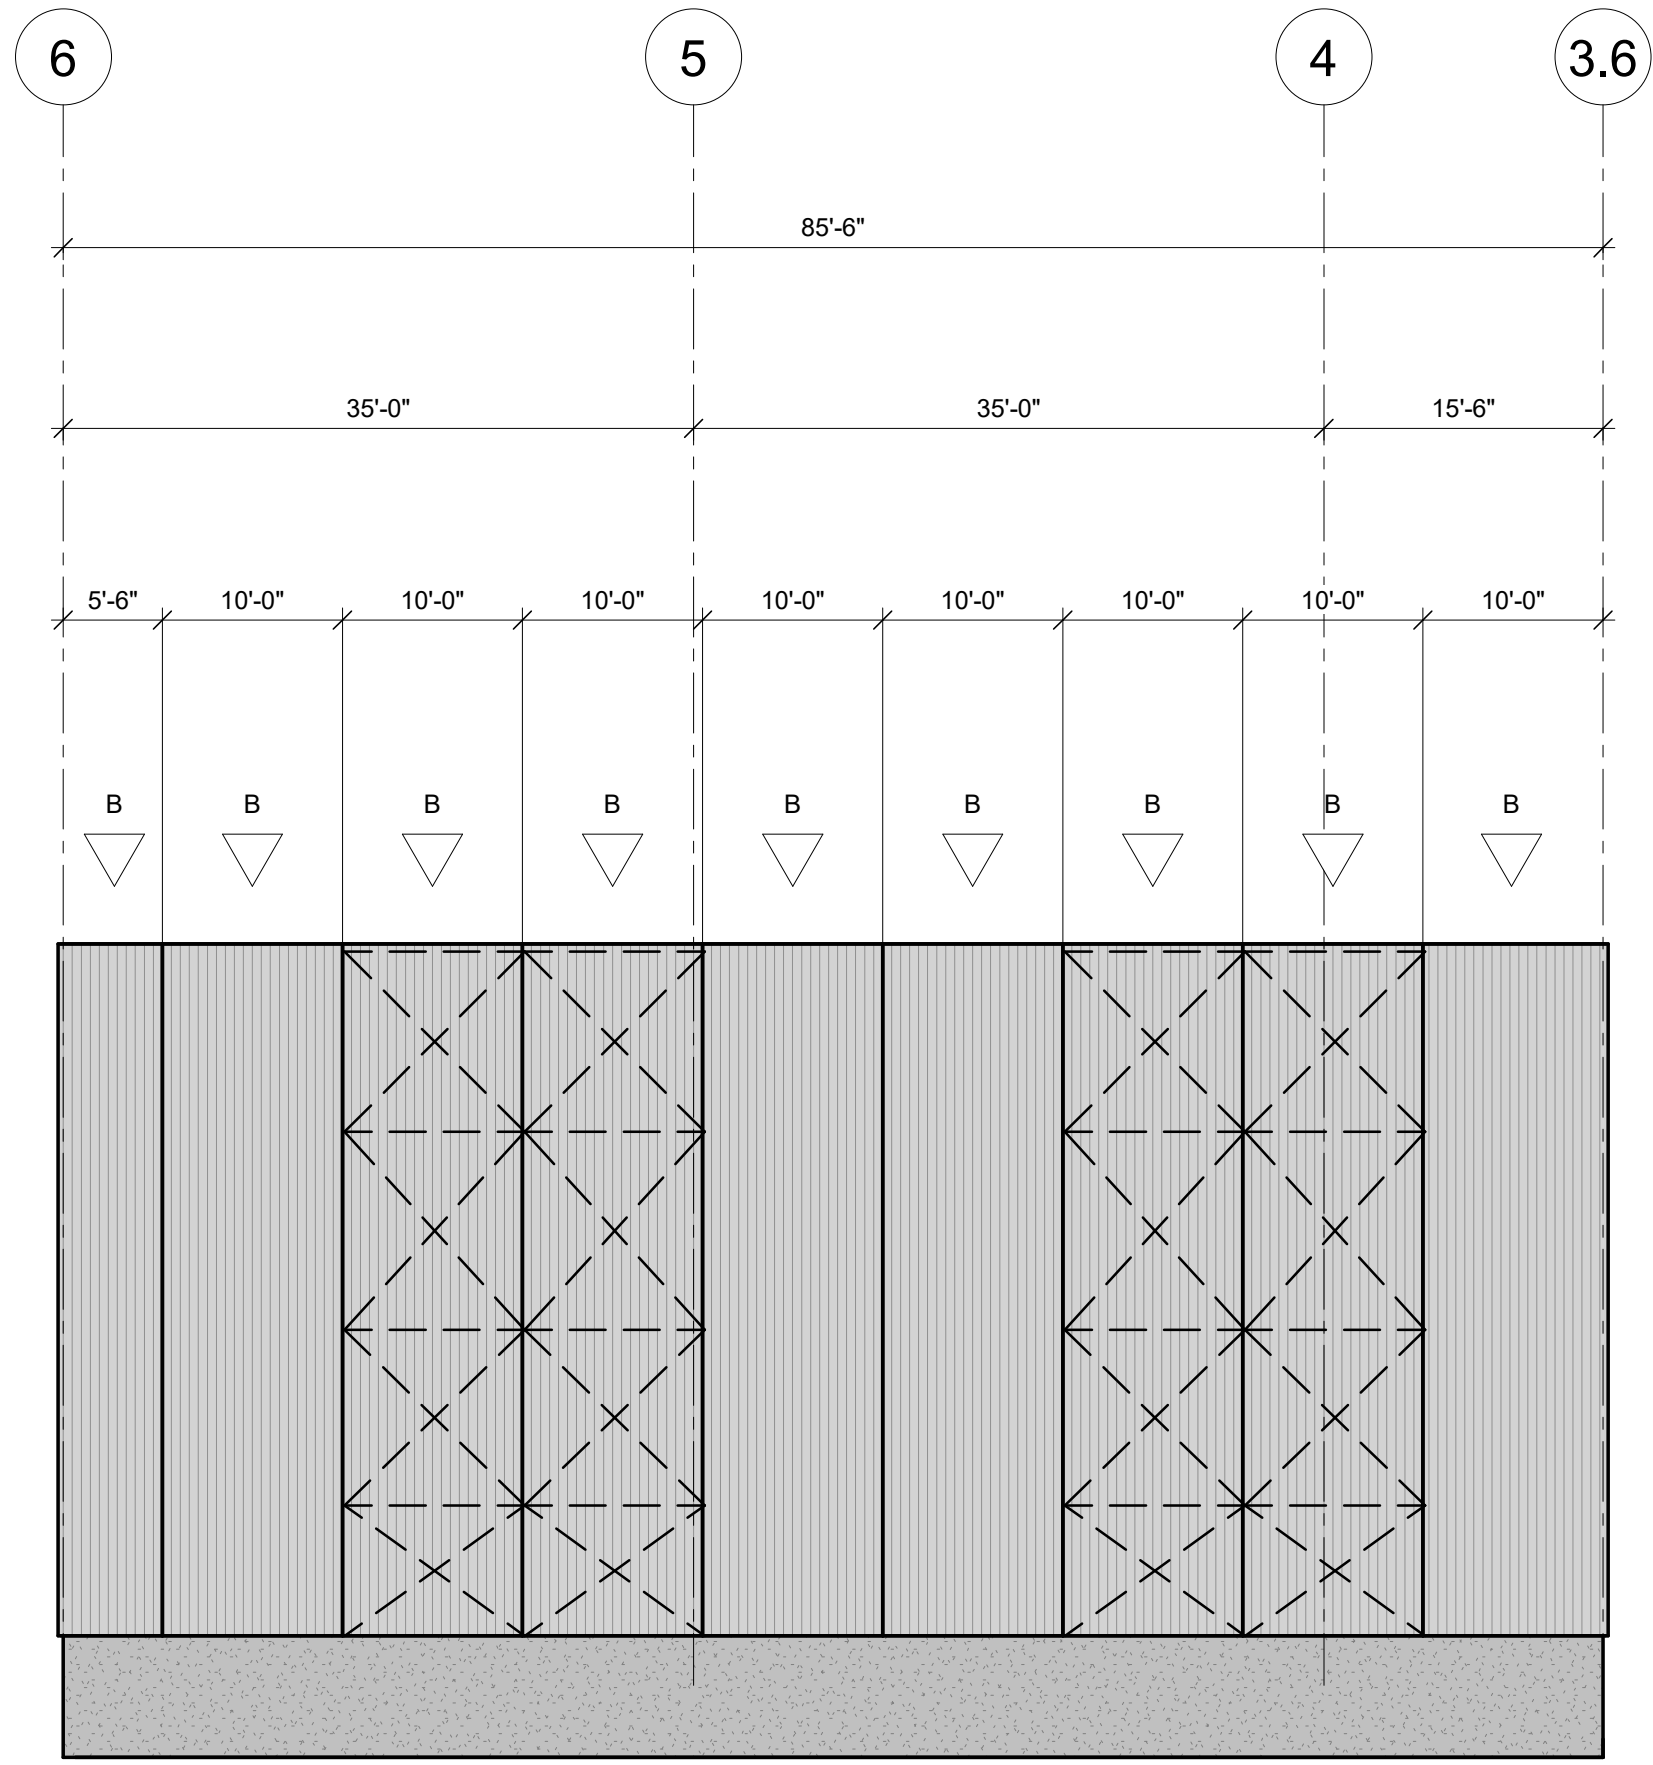

ÉLÉVATION AXE K (SUD)
3/32" = 1'-0"

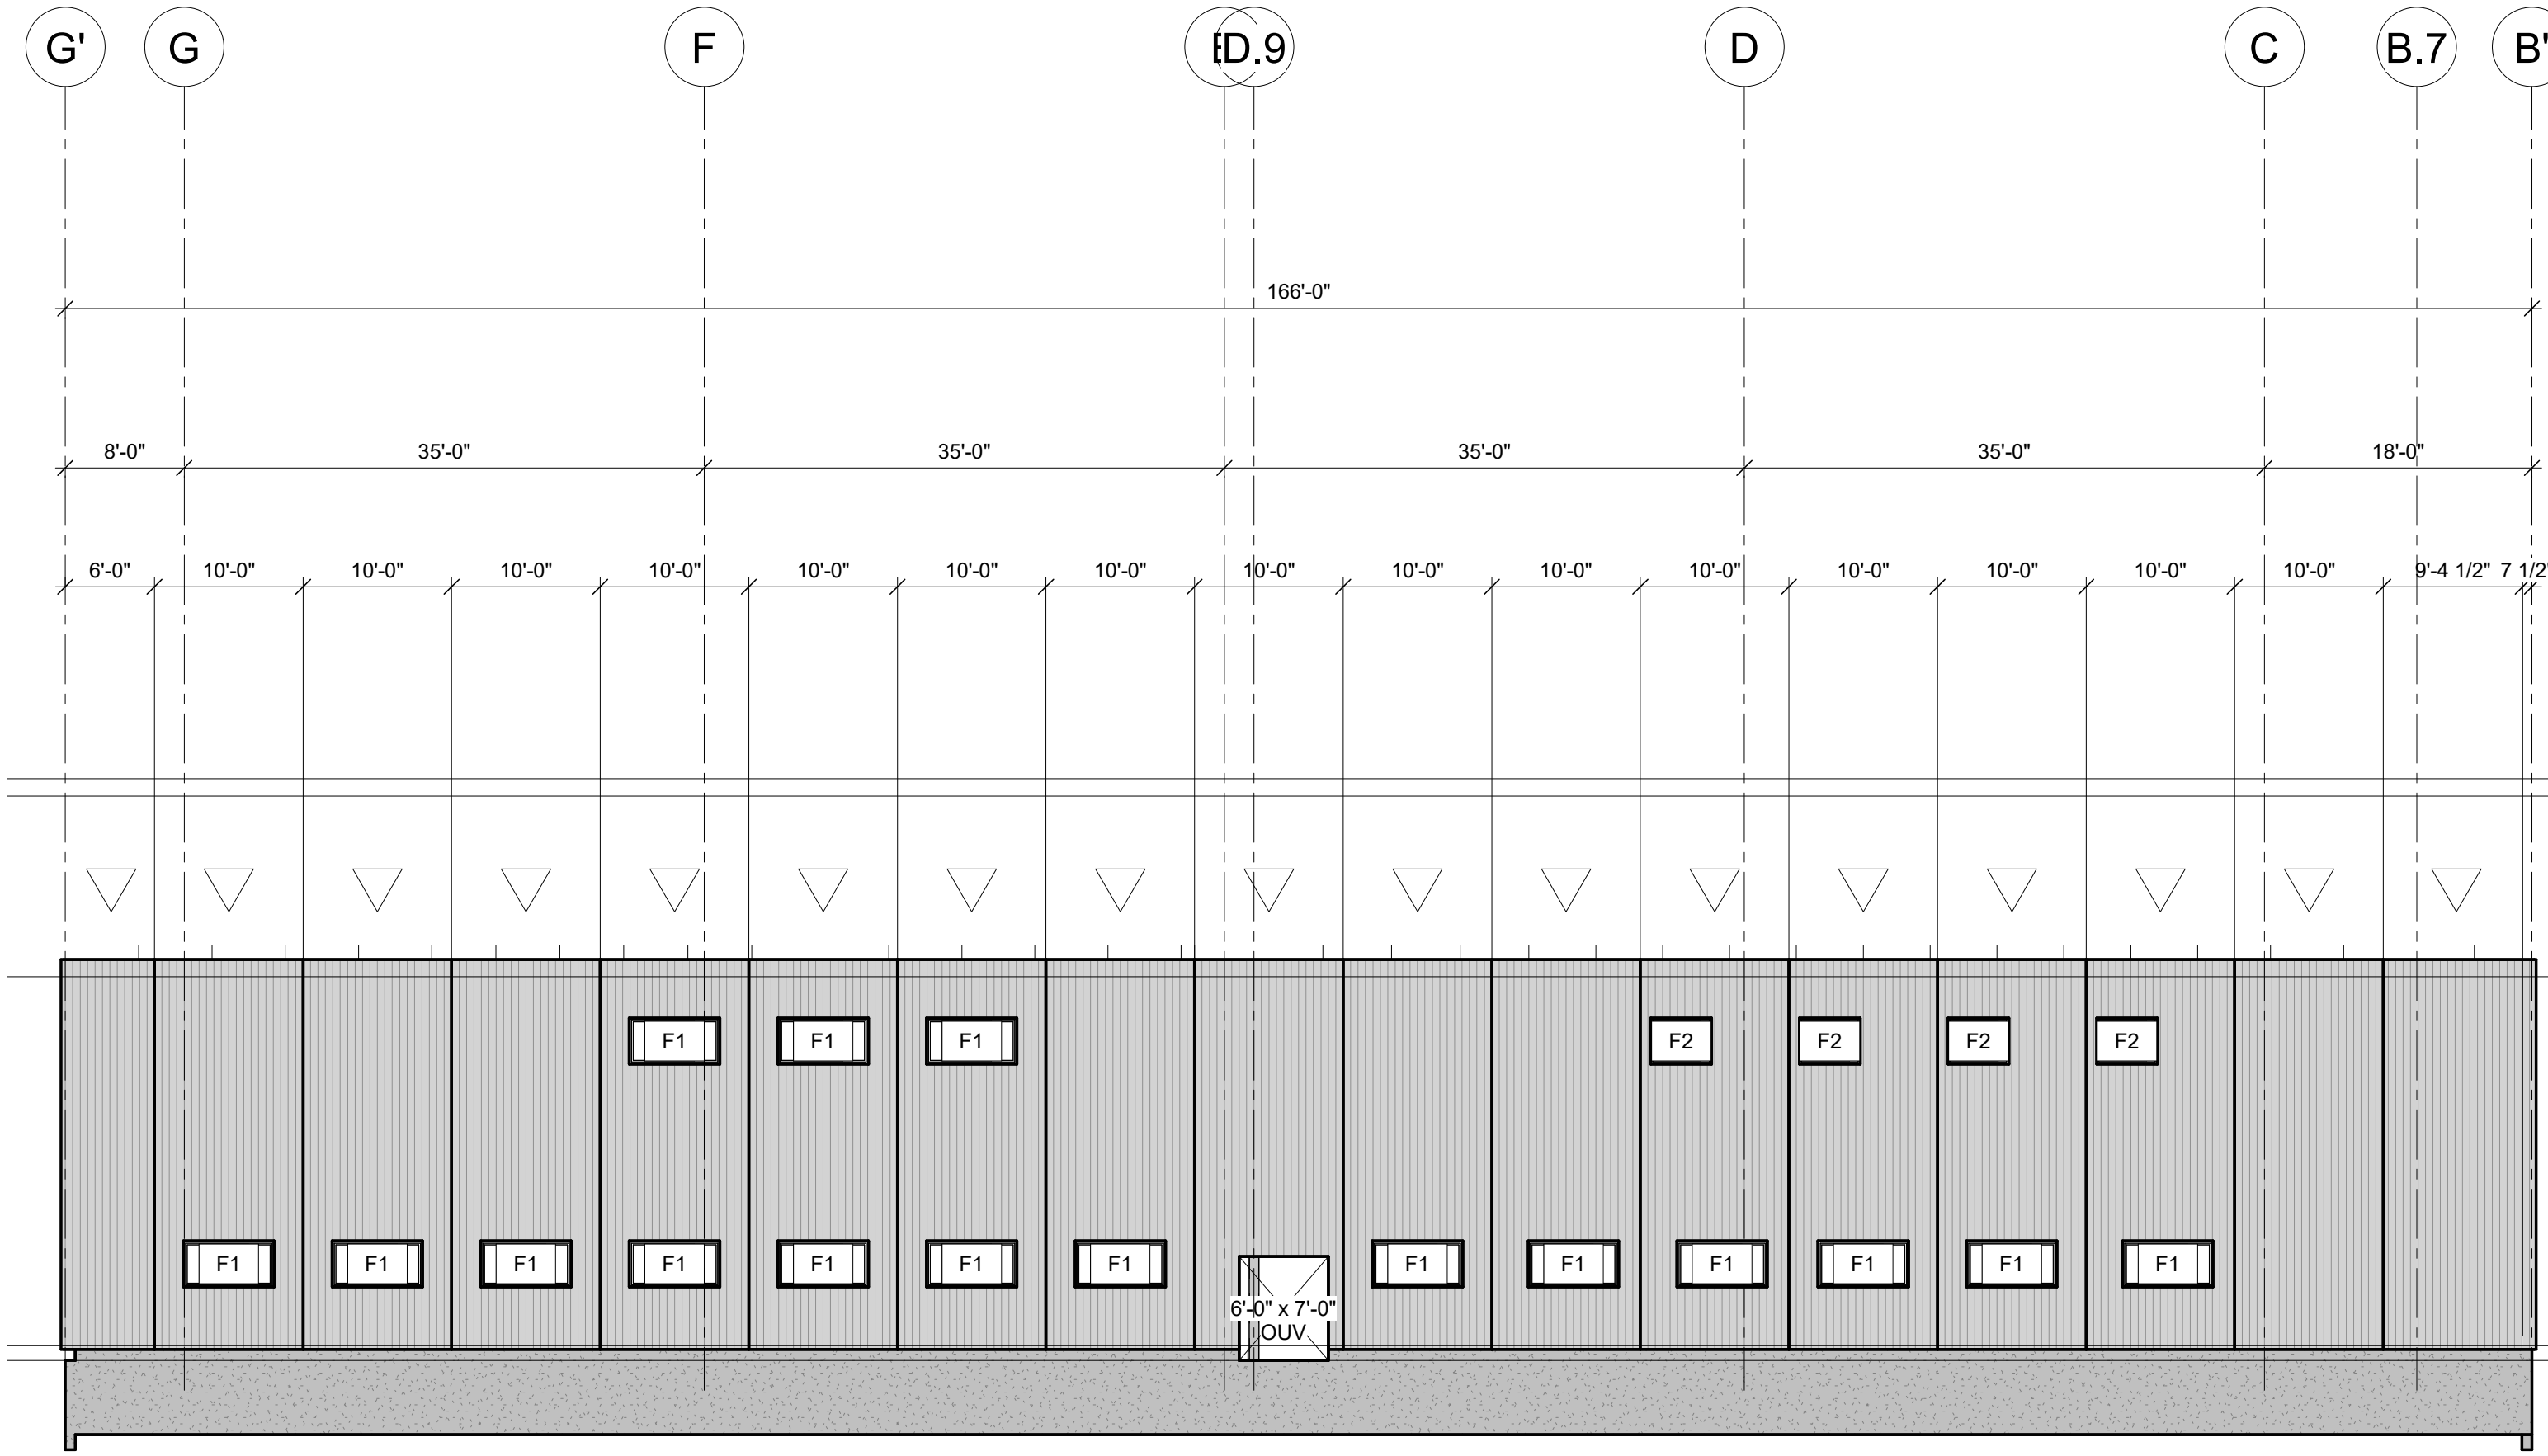

ÉLÉVATION AXE 1 (EST)
3/32" = 1'-0"

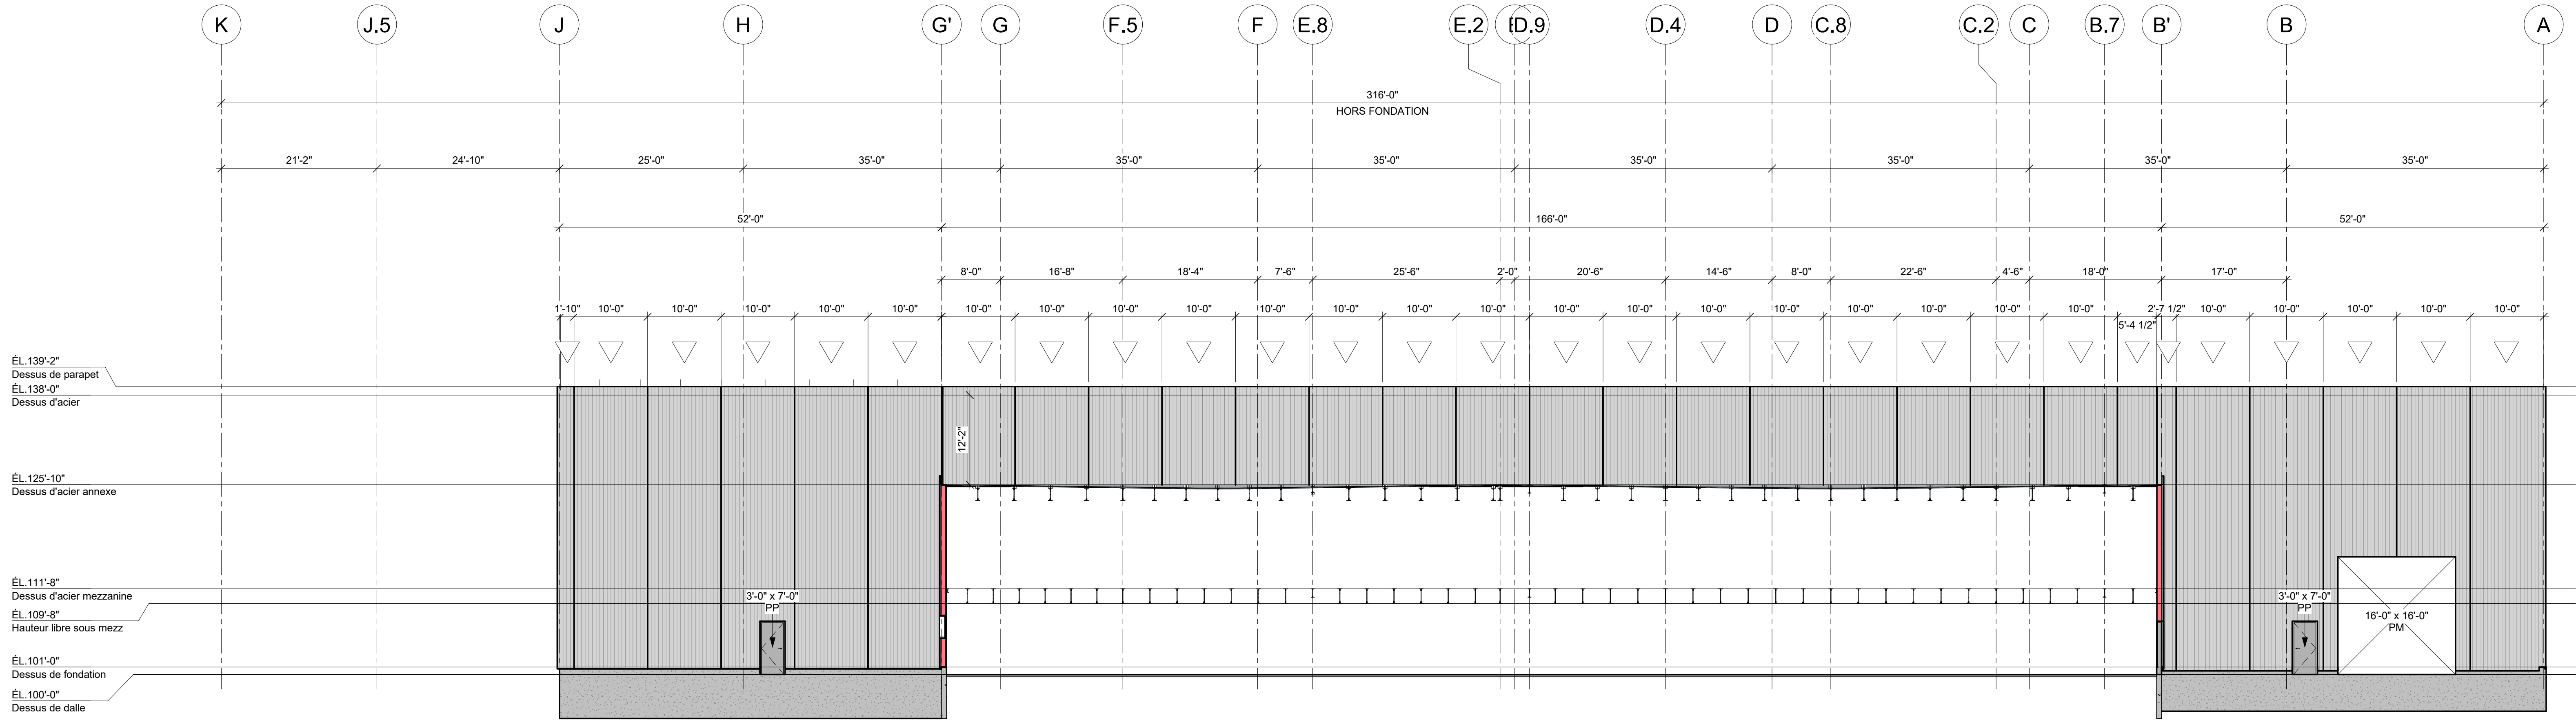

ÉLÉVATION AXE 2 (EST)
3/32" = 1'-0"

NOTE POUR LE CONTRACTEUR/ÉRECTEUR:
IL EST STRICTEMENT DÉFENDU DE MODIFIER, COPIER, REPRODUIRE OU DE DISTRIBUER CES DESSINS OU QUELQUES REPRÉSENTATIONS DE CES DESSINS, PAR TOUTES SOURCES DE MÉDIA INCLUANT ÉLECTRONIQUEMENT, SANS L'APPROBATION ÉCRITE DE GROUPE CANAM INC.

PRÉLIMINAIRE

NE DOIT PAS SERVIR À LA CONSTRUCTION

CANAM
11505, 1re Avenue, bureau 500, Saint-Georges Beaulac
Québec, Canada G5Y 7G5
Téléphone : (418) 228-8031
Sans frais : (877) 459-8049
www.canam.com

USINE PRINCIPALE SERVITECH
TROIS-RIVIÈRES, QC

CROQUIS PRÉLIMINAIRE - ÉLÉVATION
3 DE 3, COUPE DE MUR ET CÉDULES

Initiales	NUMÉRO CONTRAT P2026-090	NUMÉRO DESSIN EsMx502	DIVISION	REVISION