


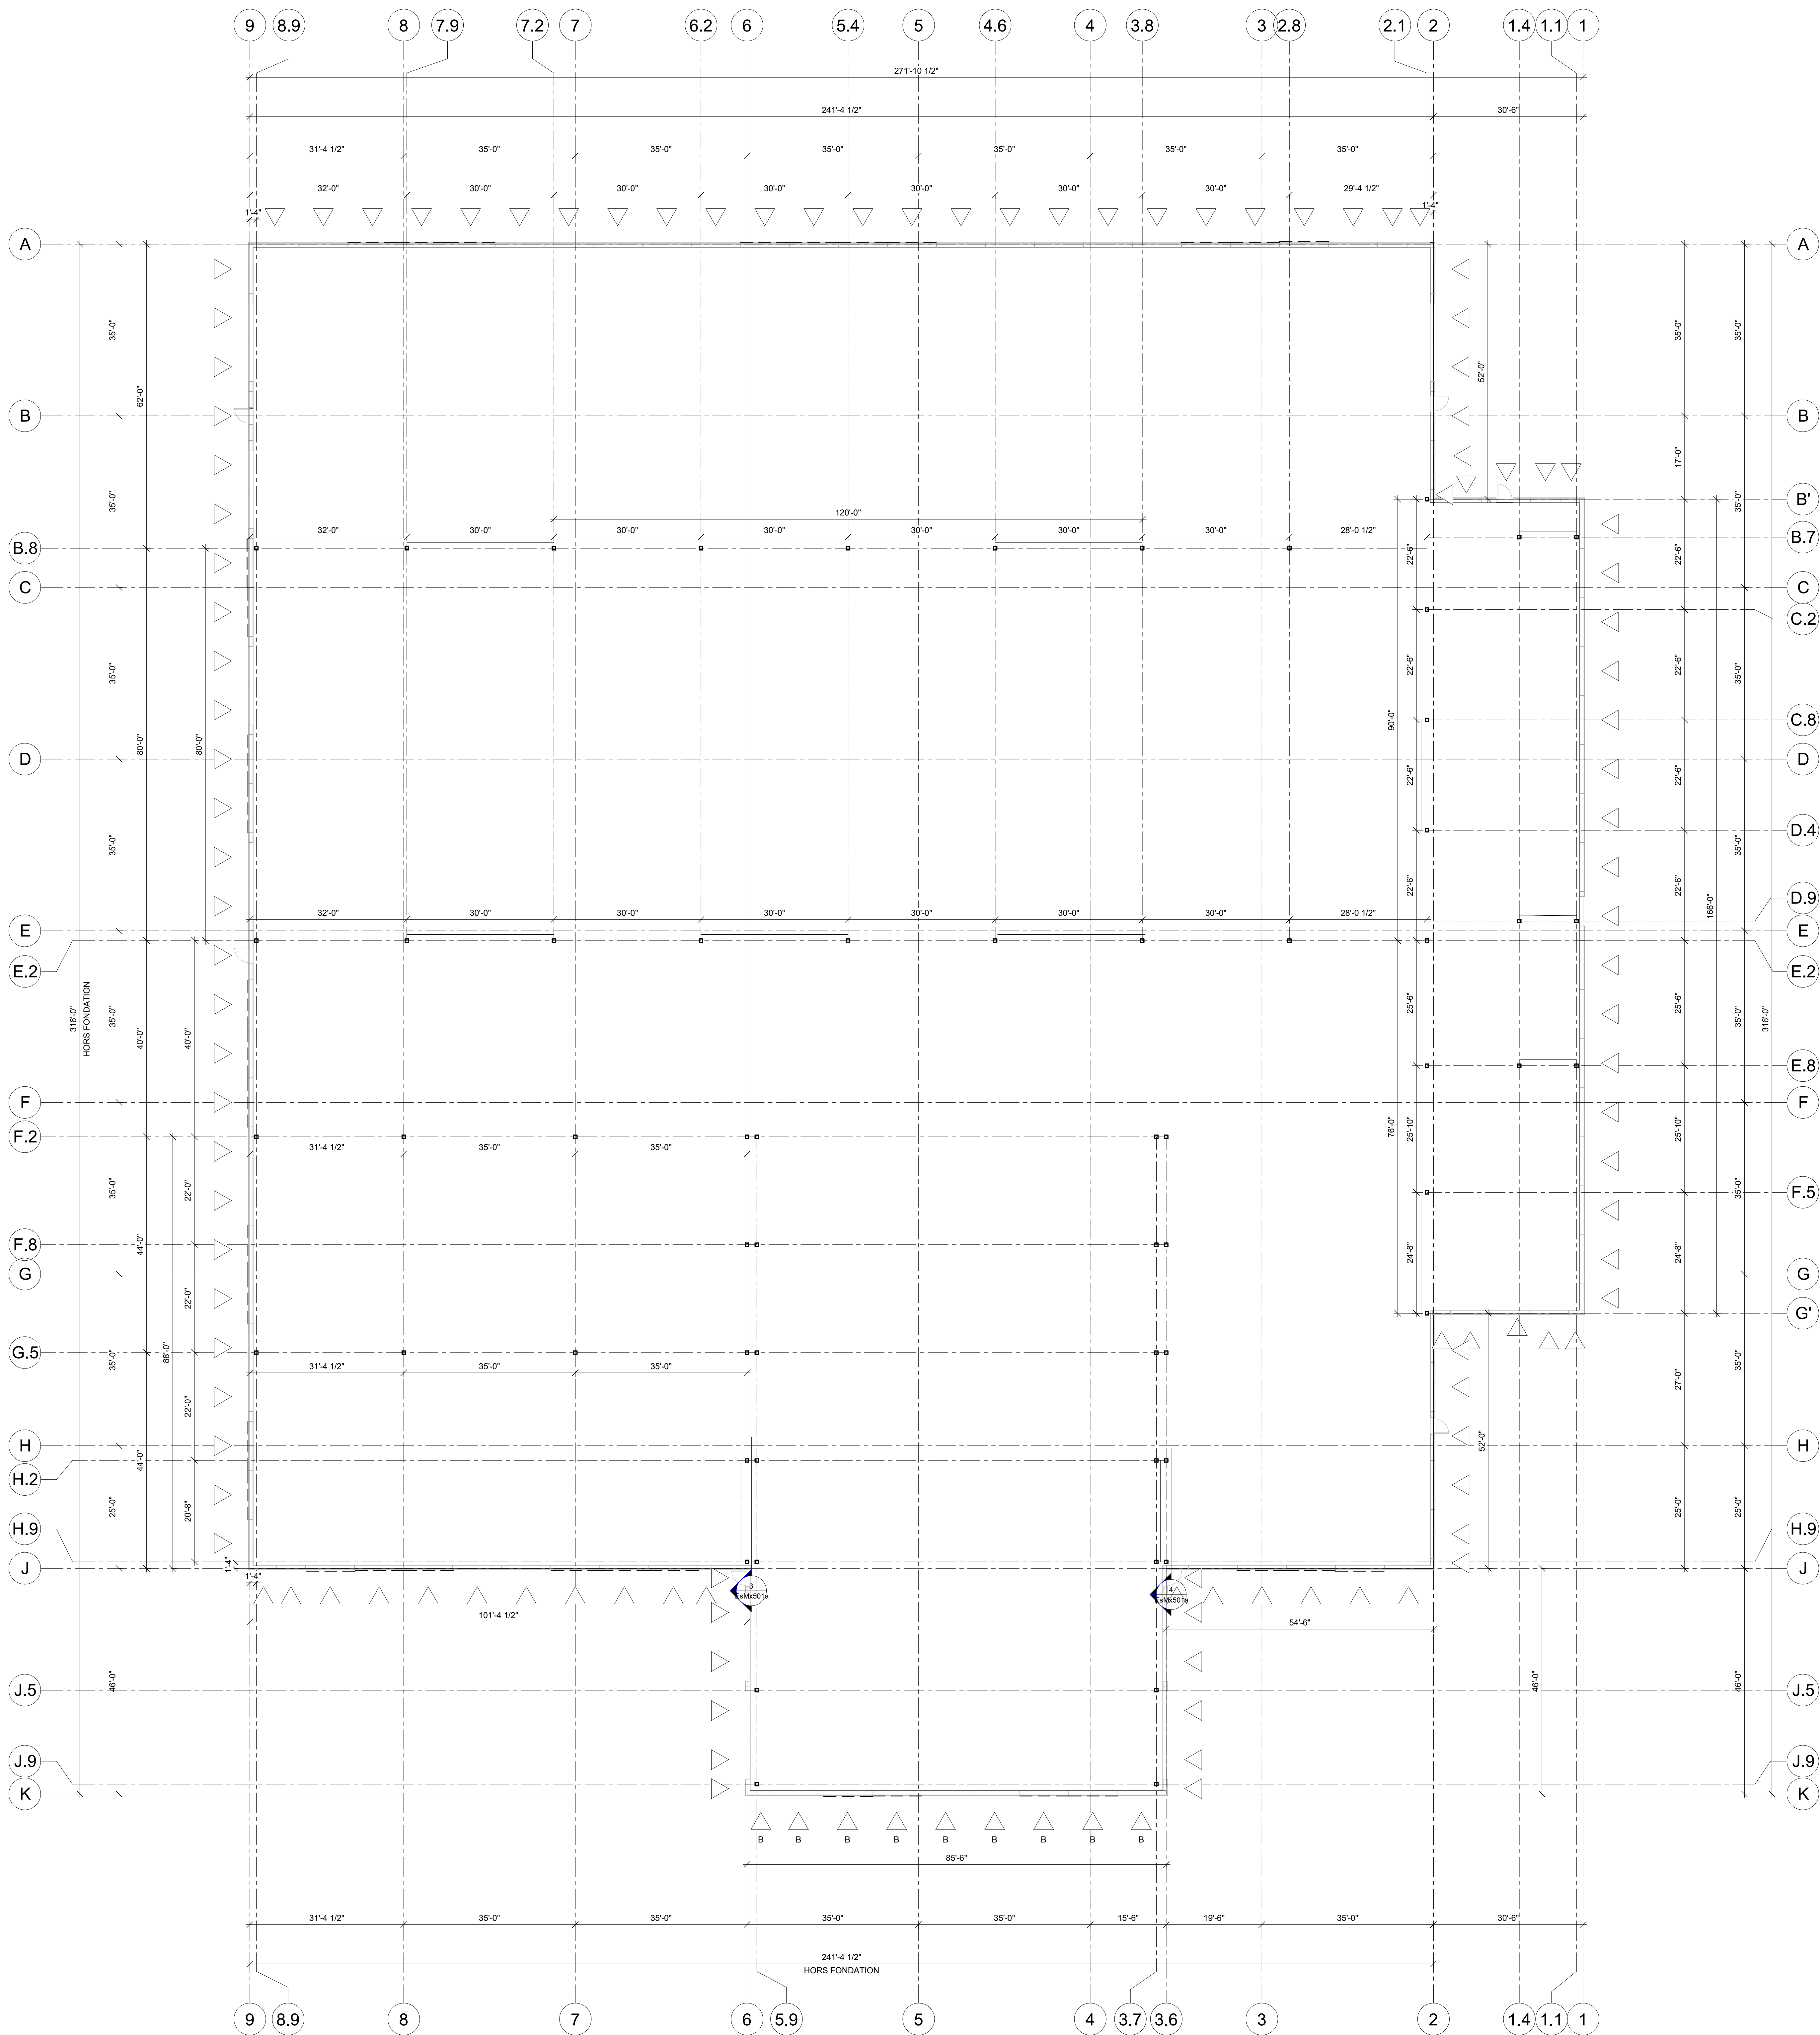

PLAN D'ANCRAGE
1:156

NOTE POUR LE CONTRACTEUR/ÉRECTEUR:
IL EST STRICTEMENT DÉFENDU DE MODIFIER, COPIER, REPRODUIRE OU DE DISTRIBUER CES DESSINS OU QUELQUES REPRÉSENTATIONS DE CES DESSINS, PAR TOUTES SOURCES DE MÉDIA INCLUANT ÉLECTRONIQUEMENT, SANS L'APPROBATION ÉCRITE DE GROUPE CANAM INC.

PRÉLIMINAIRE

NE DOIT PAS SERVIR À LA
CONSTRUCTION

REVISION	DATE	DESCRIPTION	DESS	VER
GERANT DE PROJET				

DESSIN	CONÇU PAR	INGÉNIEUR DU PROJET	ÉCHELLE:
DESSINÉ PAR	S.L.		1:156
VÉRIFIÉ PAR	INGÉNIEURS CONSEILS / ARCHITECTES	DATE (mm/aaaa)	07/05/2026

CLIENT: USINAGE SERVITECH



SCAUX PROFESSIONNEL

PROJET
USINE PRINCIPALE SERVITECH
TROIS-RIVIÈRES, QC

TITRE
CROQUIS PRÉLIMINAIRE - PLAN
D'ANCRAGE

NUMÉRO CONTRAT	NUMÉRO DESSIN	DIVISION	REVISION
P2026-090	EsMx101		