


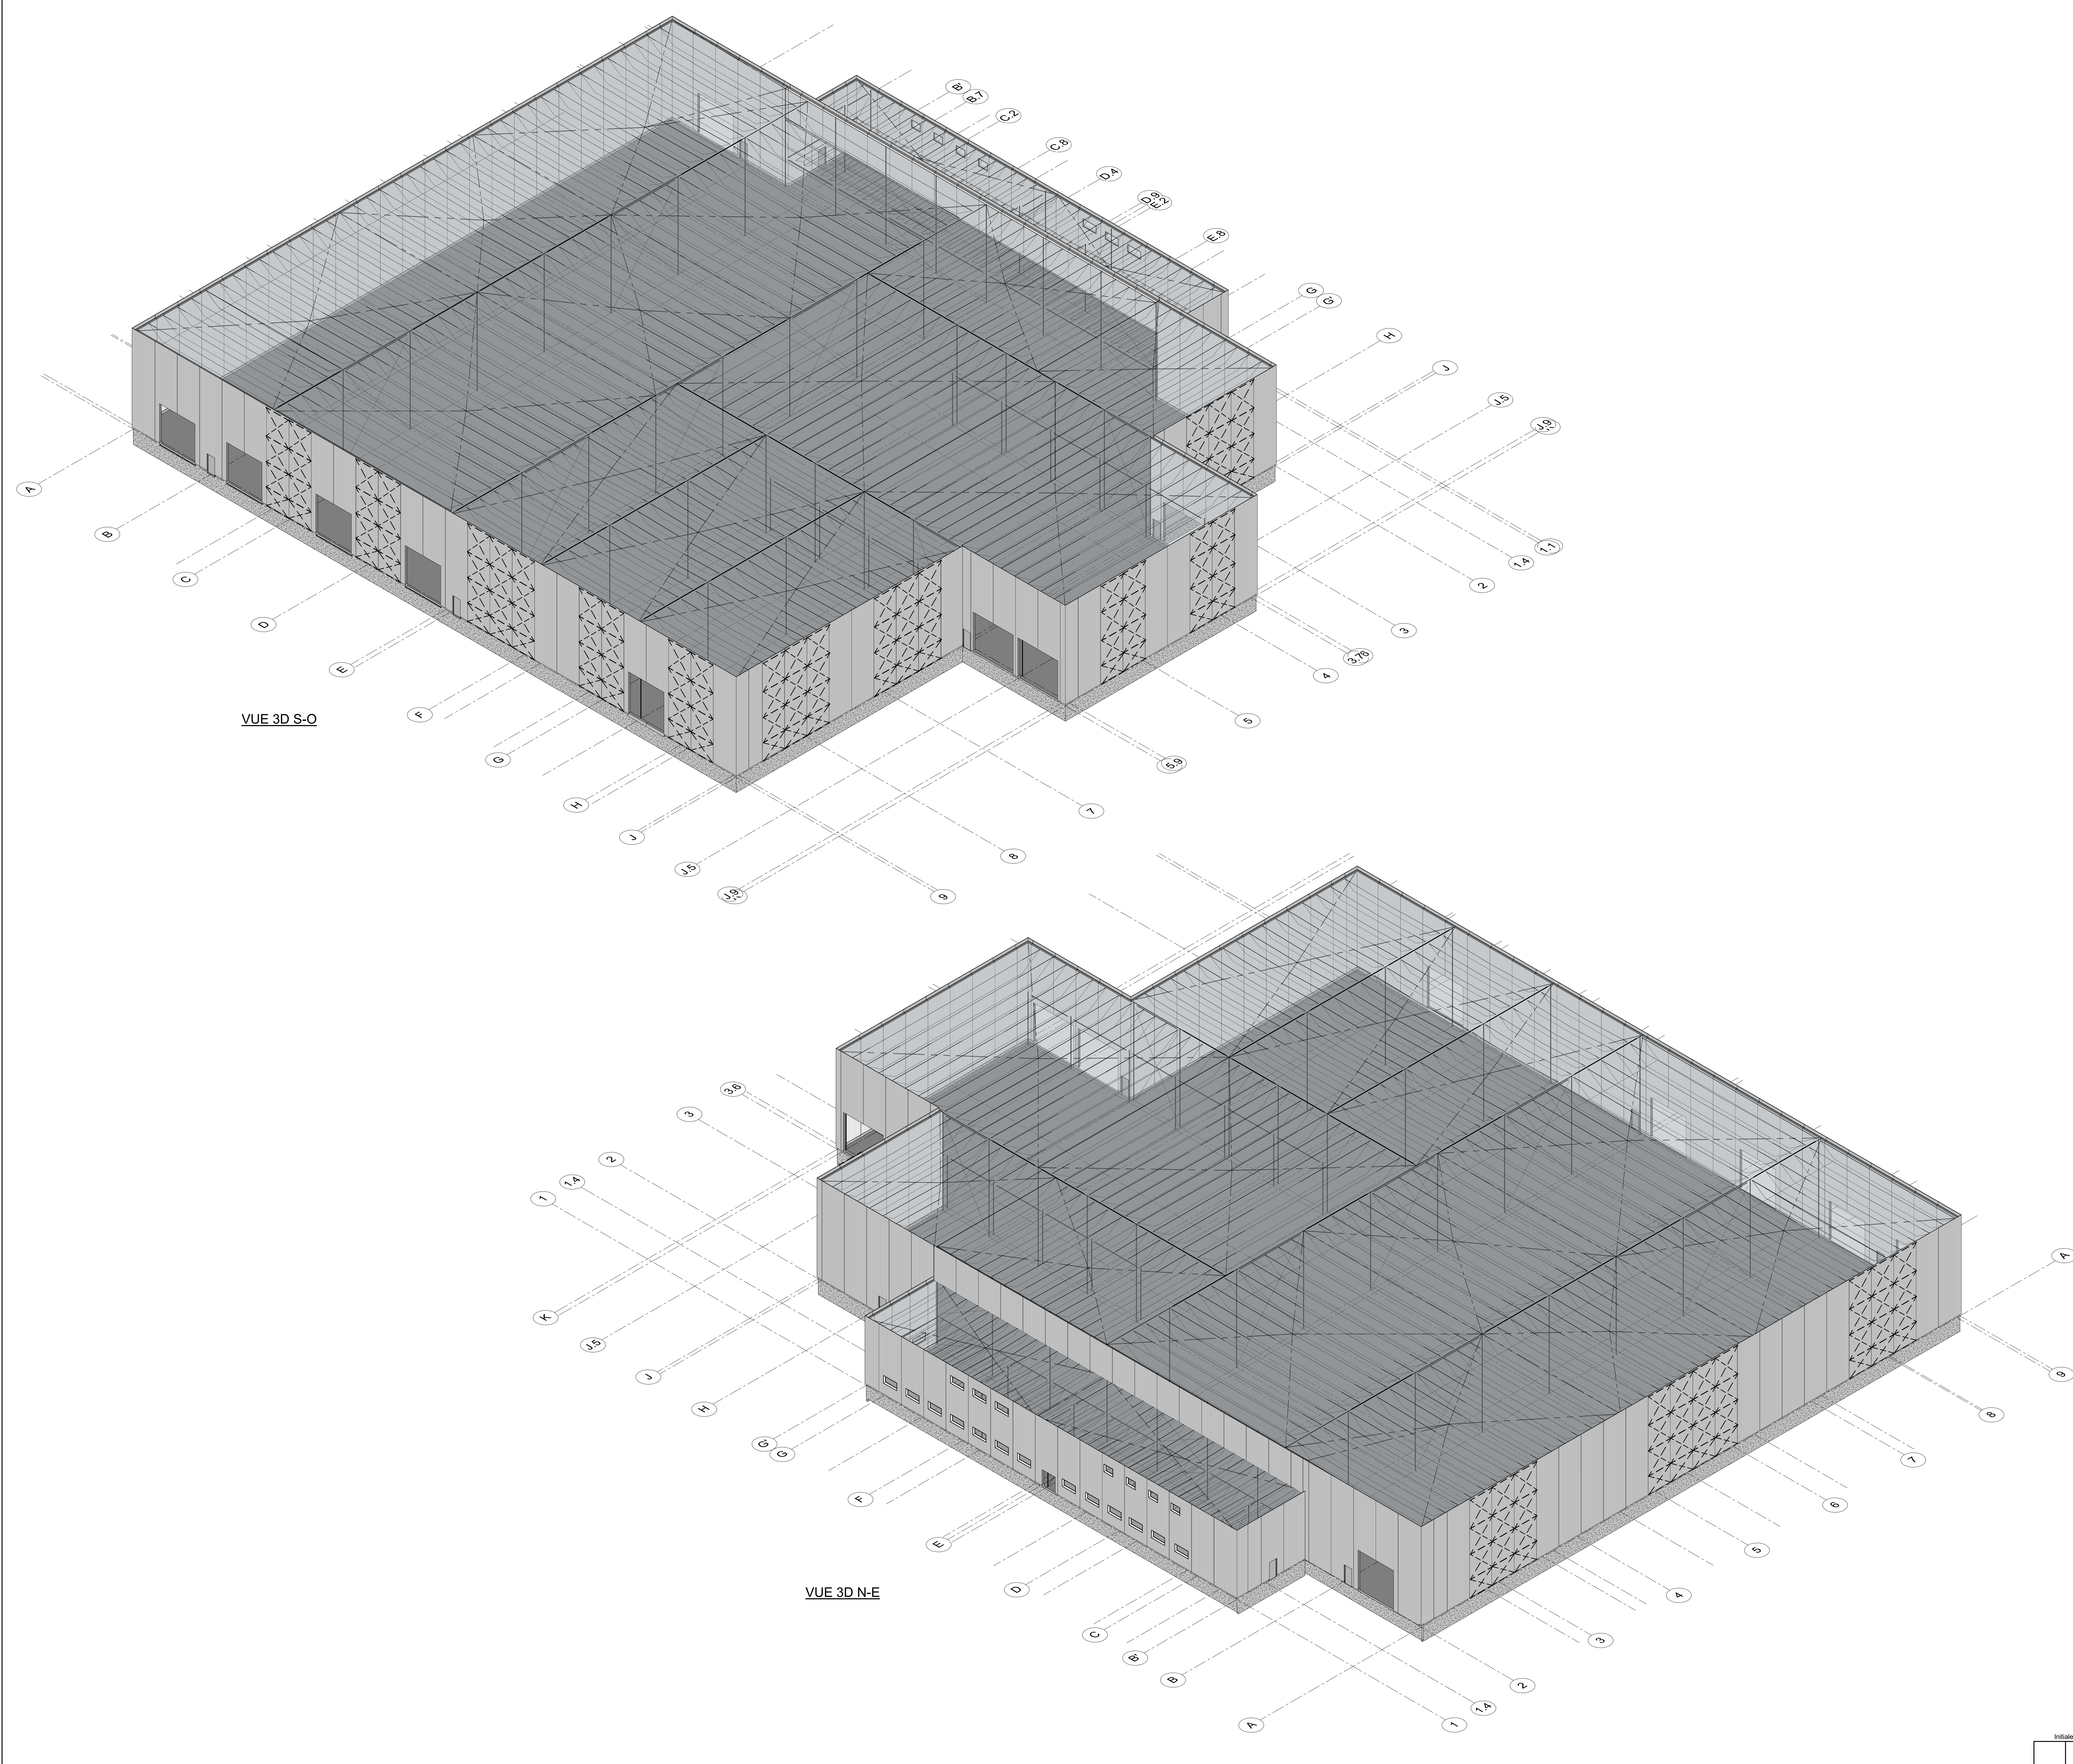

VUE 3D S-O

VUE 3D N-E

NOTE POUR LE CONTRACTEUR/ÉRECTEUR:
IL EST STRICTEMENT DÉFENDU DE MODIFIER, COPIER, REPRODUIRE OU DE DISTRIBUER CES DESSINS OU QUELQUES REPRÉSENTATIONS DE CES DESSINS, PAR TOUTES SOURCES DE MÉDIA INCLUANT ÉLECTRONIQUEMENT, SANS L'APPROBATION ÉCRITE DE GROUPE CANAM INC.

LISTE DES FEUILLES PRÉLIMINAIRES	
EsMx001	CROQUIS PRÉLIMINAIRE - VUES 3D
EsMx101	CROQUIS PRÉLIMINAIRE - PLAN D'ANCRAGE
EsMx201	CROQUIS PRÉLIMINAIRE - PLAN DE MEZZANINE
EsMx301	CROQUIS PRÉLIMINAIRE - PLAN DE PONTS ROULANTS
EsMx401	CROQUIS PRÉLIMINAIRE - PLAN DE TOIT
EsMx501	CROQUIS PRÉLIMINAIRE - ÉLEVATIONS 1 DE 3
EsMx501a	CROQUIS PRÉLIMINAIRE - ÉLEVATIONS 2 DE 3
EsMx502	CROQUIS PRÉLIMINAIRE - ÉLEVATION 3 DE 3, COUPE DE MUR ET CÉLULES
EsMx601	CROQUIS PRÉLIMINAIRE - DÉTAILS

Cliquer ici pour modèle 3D


PRÉLIMINAIRE

NE DOIT PAS SERVIR À LA CONSTRUCTION

REVISION	DATE	DESCRIPTION	DESS	VER
GERANT DE PROJET				
		-		
		-		
		-		

DESSIN			
DESSINÉ PAR	CONÇU PAR	INGÉNIEUR DU PROJET	ÉCHELLE:
S.L.			
VÉRIFIÉ PAR	INGÉNIEURS CONSEILS / ARCHITECTES		DATE (jj/mm/aaaa):
			07/05/2026

CLIENT: USINAGE SERVITECH

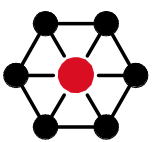**CANAM**

11505, 1re Avenue, bureau 500, Saint-Georges Beaulac
Québec, Canada, G5Y 7G5
Téléphone : (418) 228-8031
Sans frais : (877) 499-8049
www.canam.com

SCAUX PROFESSIONNEL


PROJET

USINE PRINCIPALE SERVITECH
TROIS-RIVIÈRES, QC

TITRE

CROQUIS PRÉLIMINAIRE - VUES 3D

NUMÉRO CONTRAT	NUMÉRO DESSIN	DIVISION	REVISION
P2026-090	EsMx001		

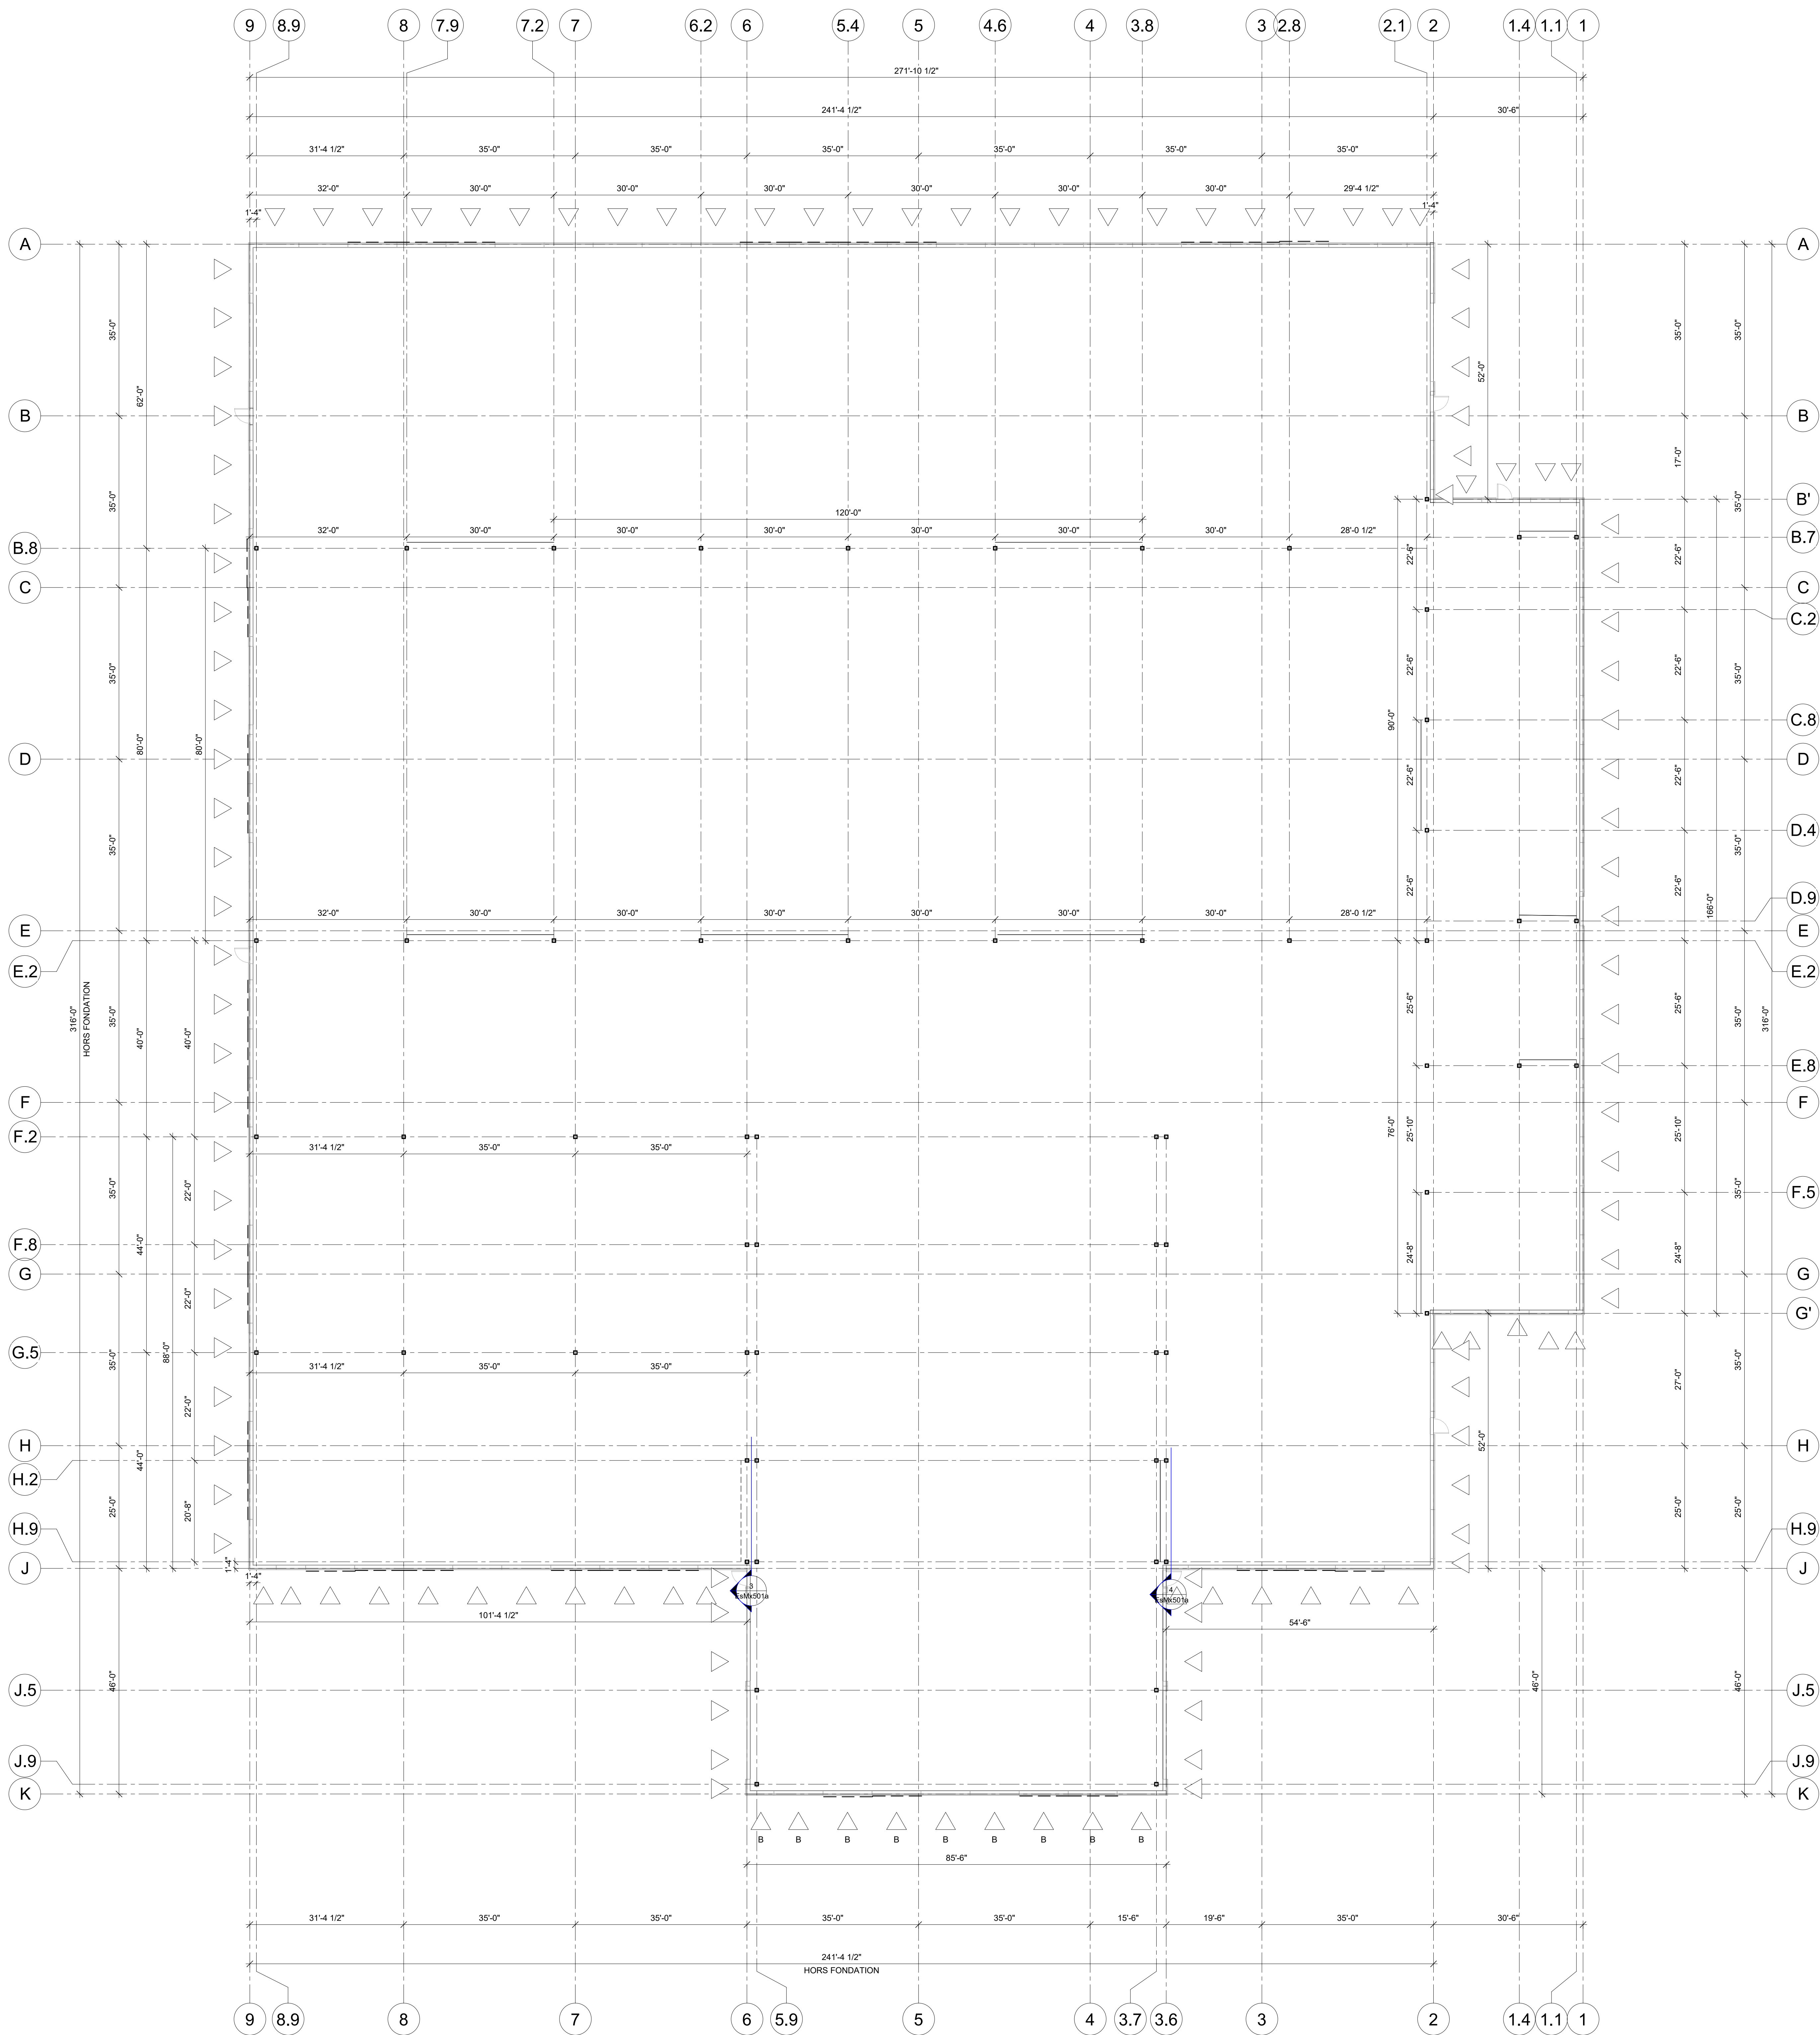

PLAN D'ANCRAGE
1:156

NOTE POUR LE CONTRACTEUR/ÉRECTEUR:
IL EST STRICTEMENT DÉFENDU DE MODIFIER, COPIER, REPRODUIRE OU DE DISTRIBUER CES DESSINS OU QUELQUES REPRÉSENTATIONS DE CES DESSINS, PAR TOUTES SOURCES DE MÉDIA INCLUANT ÉLECTRONIQUEMENT, SANS L'APPROBATION ÉCRITE DE GROUPE CANAM INC.

PRÉLIMINAIRE

NE DOIT PAS SERVIR À LA
CONSTRUCTION

REVISION	DATE	DESCRIPTION	DESS	VER
----------	------	-------------	------	-----

GERANT DE PROJET	.
.	.
.	.

DESSIN	
DESSINÉ PAR S.L.	CONÇU PAR INGÉNIEUR DU PROJET
VERIFIÉ PAR	INGÉNIEURS CONSEILS / ARCHITECTES
DATE (mm/aaaa) 07/05/2026	

CLIENT: USINAGE SERVITECH

CANAM
11505, 1re Avenue, bureau 500, Saint-Georges Beauce
Québec, Canada G5Y 7X5
Téléphone : (418) 228-8031
Sans frais : (877) 459-8049
www.canam.com

SCAUX PROFESSIONNEL


PROJET
**USINE PRINCIPALE SERVITECH
TROIS-RIVIÈRES, QC**

TITRE
**CROQUIS PRÉLIMINAIRE - PLAN
D'ANCRAGE**

NUMÉRO CONTRAT	NUMÉRO DESSIN	DIVISION	REVISION
P2026-090	EsMx101		

Initiales



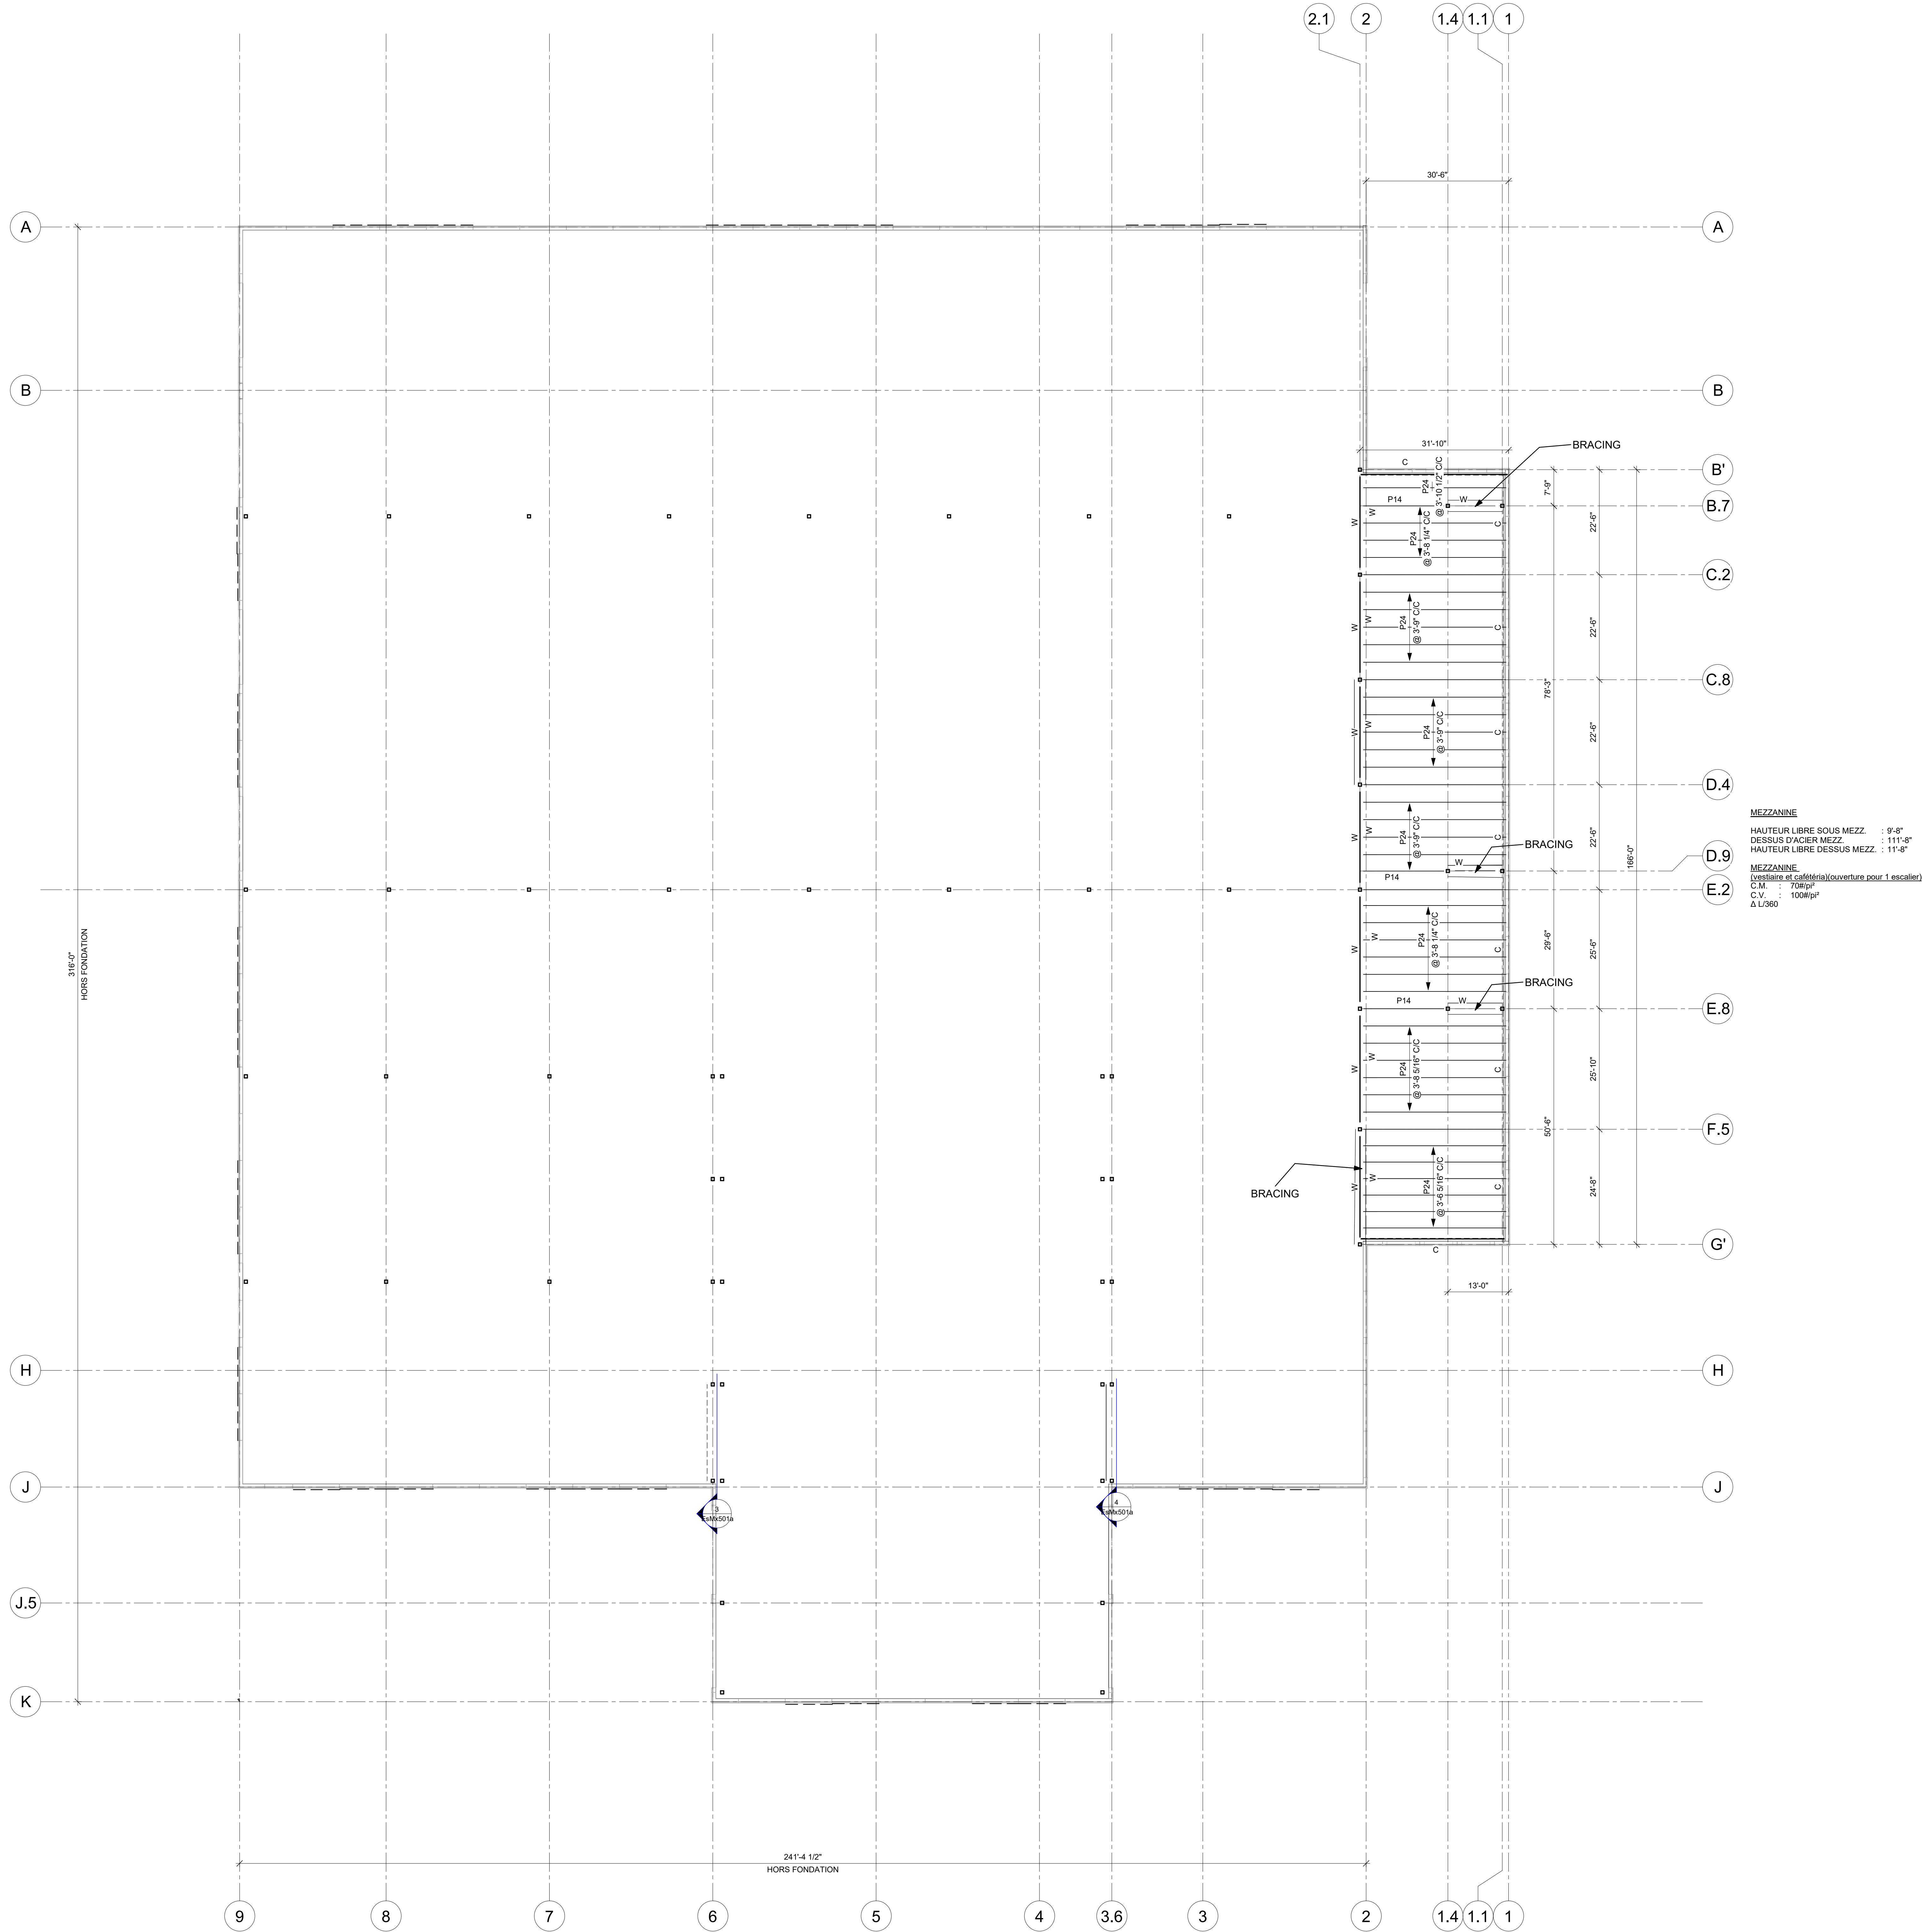

PLAN DE MEZZANINE
1:156

NOTE POUR LE CONTRACTEUR/ÉRECTEUR:
IL EST STRICTEMENT DÉFENDU DE MODIFIER, COPIER, REPRODUIRE OU DE DISTRIBUER CES DESSINS OU QUELQUES REPRÉSENTATIONS DE CES DESSINS, PAR TOUTES SOURCES DE MÉDIA INCLUANT ÉLECTRONIQUEMENT, SANS L'APPROBATION ÉCRITE DE GROUPE CANAM INC.


PRÉLIMINAIRE

NE DOIT PAS SERVIR À LA CONSTRUCTION

REVISION	DATE	DESCRIPTION	DESS	VER
GERANT DE PROJET			-	
			-	
			-	

DESSIN	CONÇU PAR	INGÉNIEUR DU PROJET	ÉCHELLE
DESSINÉ PAR	S.L.		1:156
VERIFIÉ PAR	INGÉNIEURS CONSEILS / ARCHITECTES	DATE (mm/aaaa)	
		07/05/2026	

CLIENT: USINAGE SERVITECH

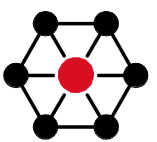**CANAM**

11505, 1re Avenue, bureau 500, Saint-Georges Beauce
Québec, Canada G5Y 7X5
Téléphone : (418) 228-8031
Sans frais : (877) 459-8049
www.canam.com

SCAUX PROFESSIONNEL


PROJET

USINE PRINCIPALE SERVITECH
TROIS-RIVIÈRES, QC

TITRE
CROQUIS PRÉLIMINAIRE - PLAN DE MEZZANINE


NUMÉRO CONTRAT	NUMÉRO DESSIN	DIVISION	REVISION
P2026-090	EsMx201		

Initiales

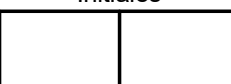

Signature



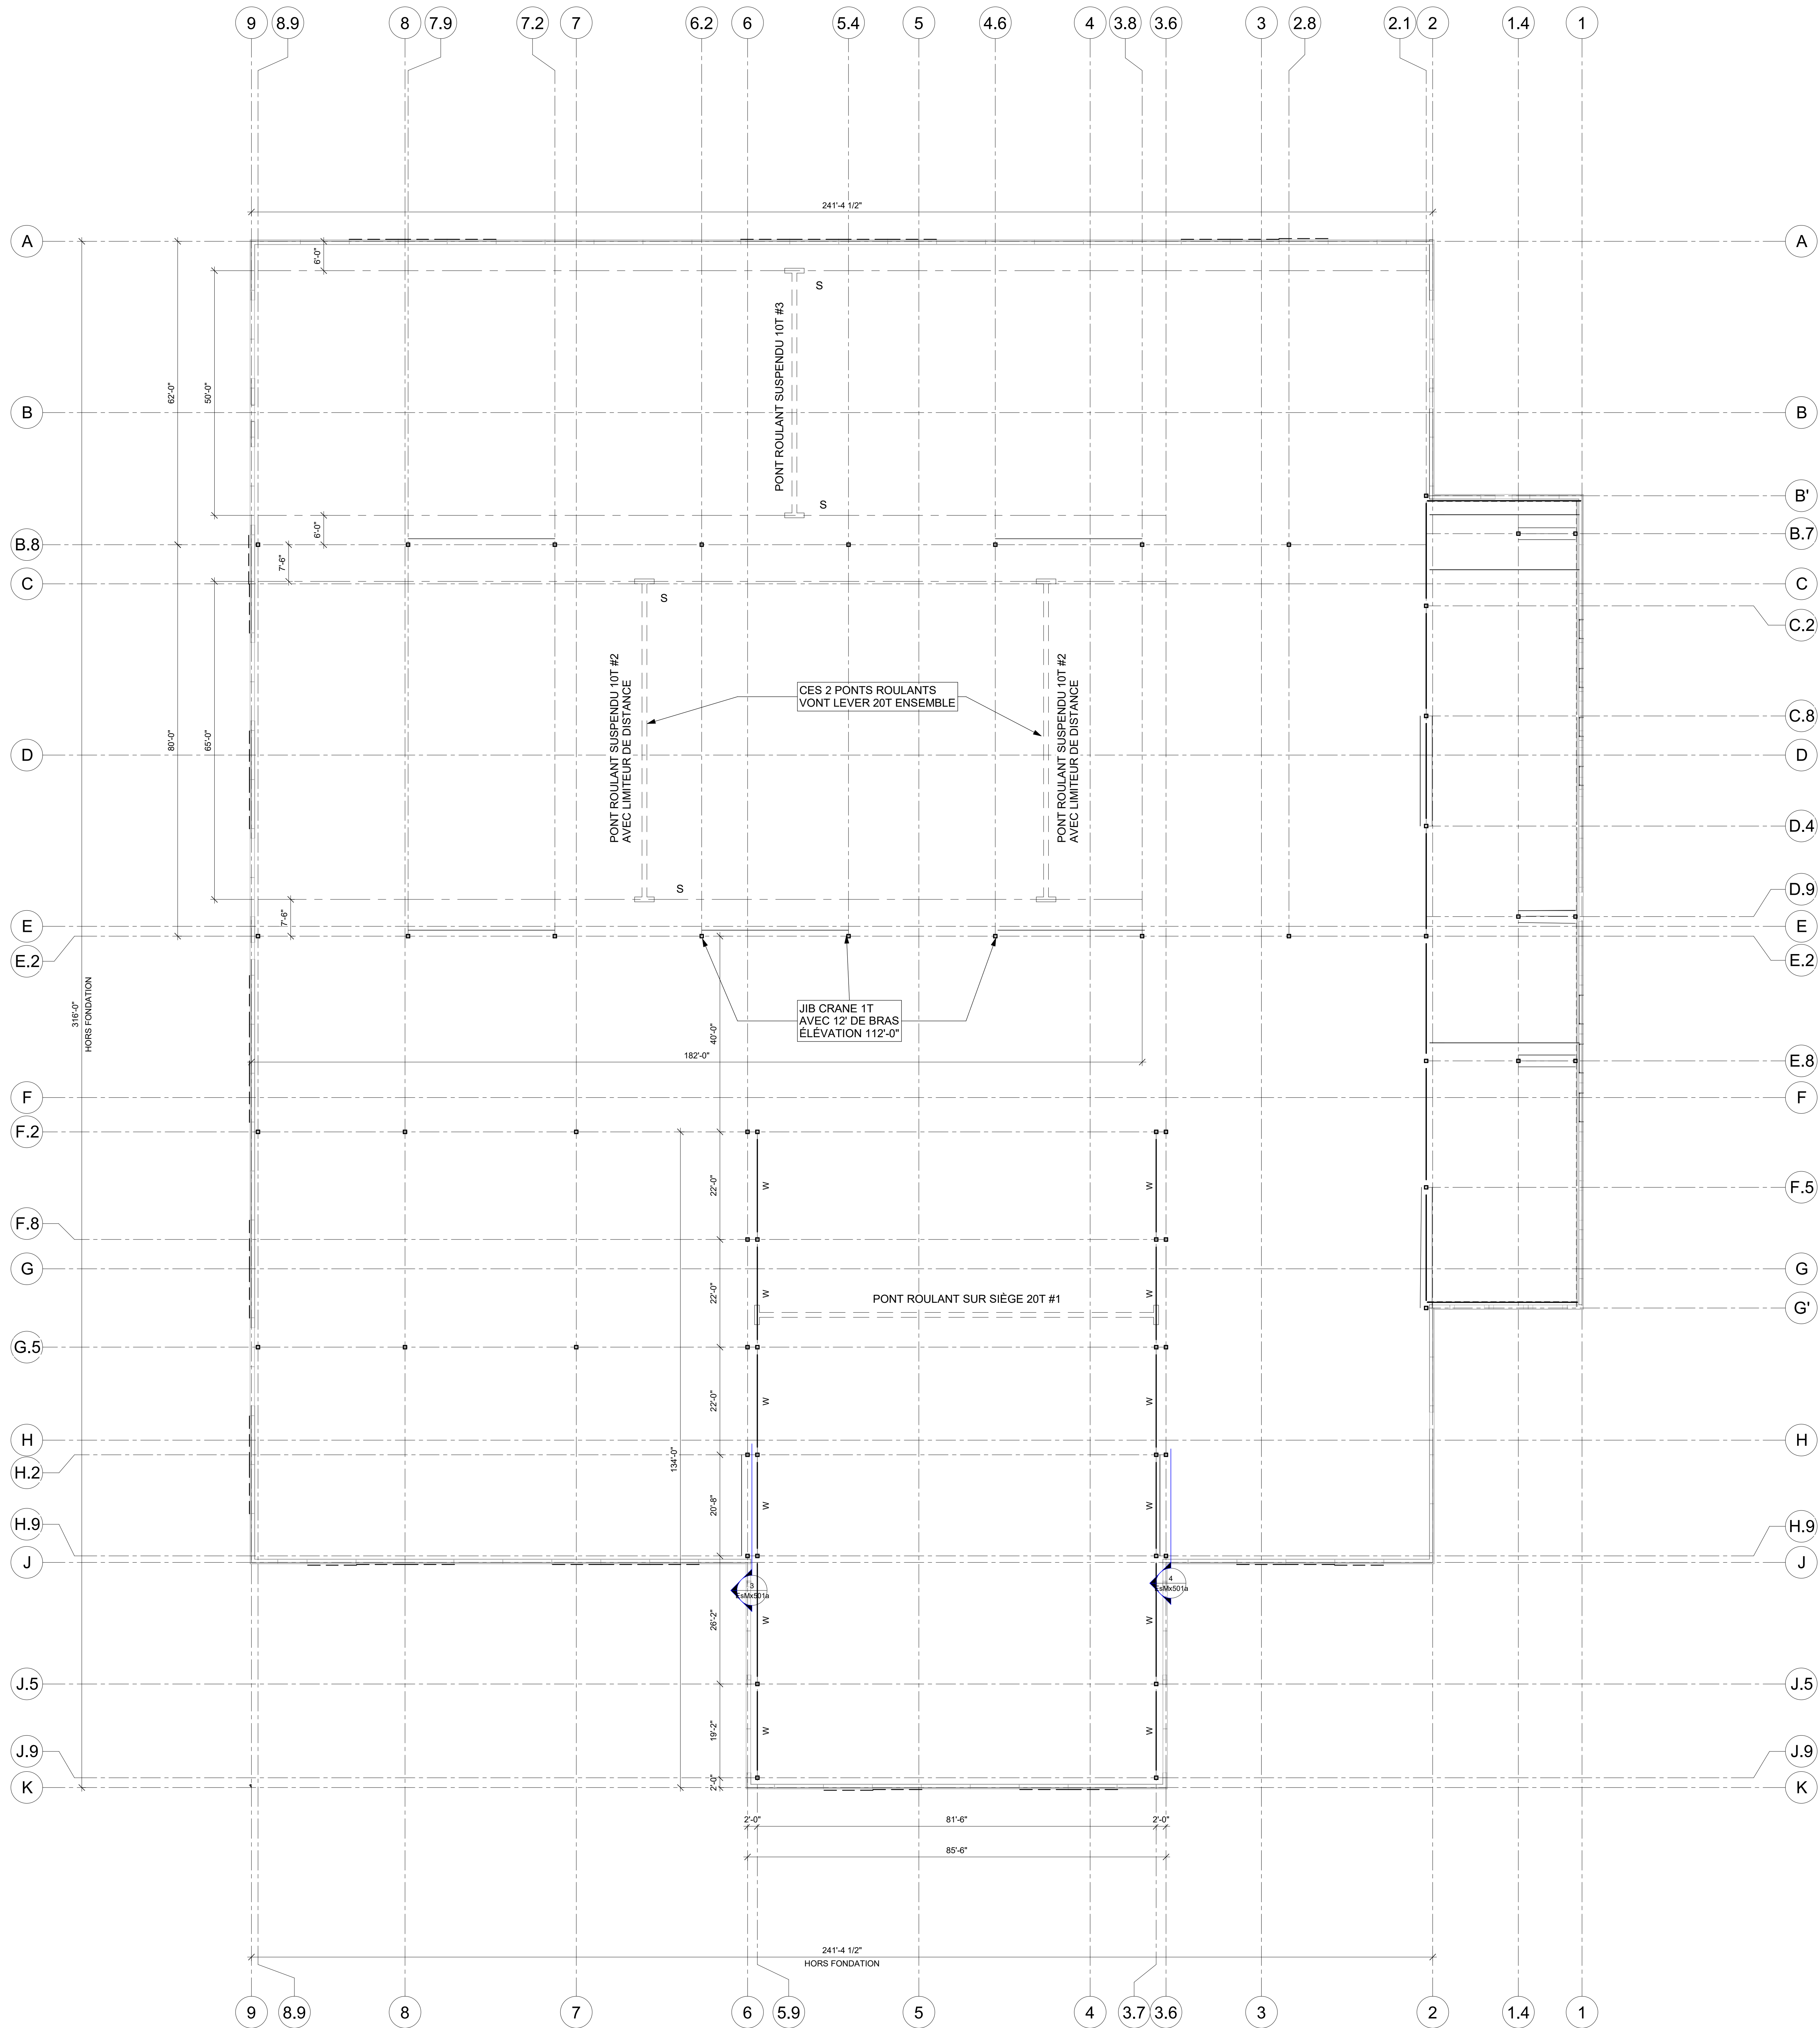

PLAN PONTS ROULANTS
1 : 100

NOTE POUR LE CONTRACTEUR/ÉRECTEUR:
IL EST STRICTEMENT DÉFENDU DE MODIFIER, COPIER, REPRODUIRE OU DE DISTRIBUER CES DESSINS OU QUELQUES REPRÉSENTATIONS DE CES DESSINS, PAR TOUTES SOURCES DE MÉDIA INCLUANT ÉLECTRONIQUEMENT, SANS L'APPROBATION ÉCRITE DE GROUPE CANAM INC.

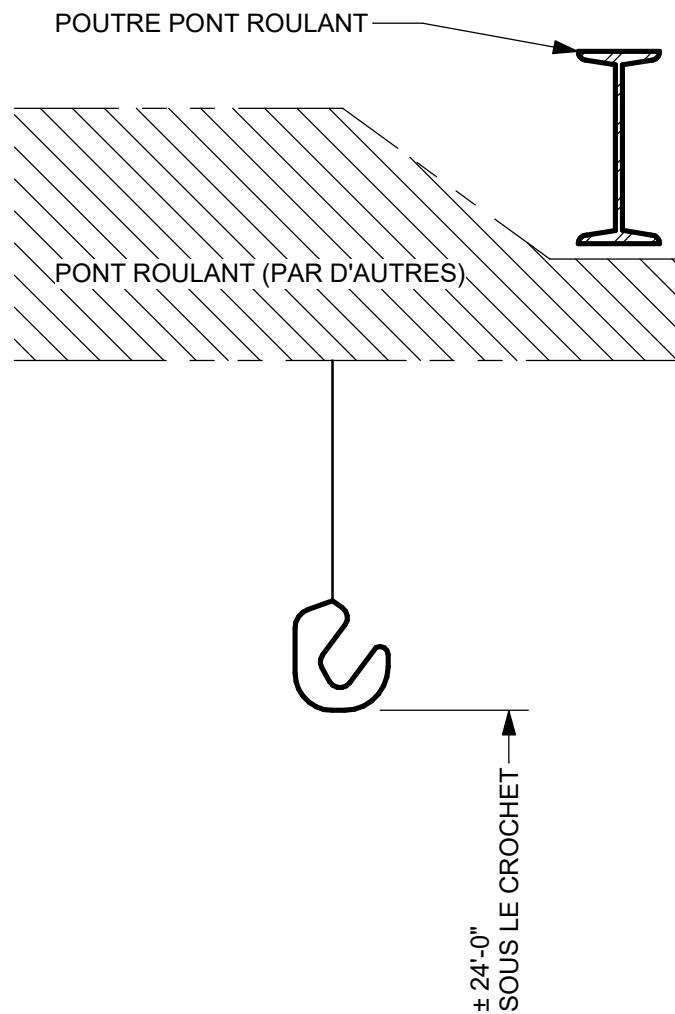


TABLEAU CHARGES PONT ROULANT				
CAPACITÉ	POIDS DU PONT	CHARIOT	CHARGE MAX. PAR ROUE (DYNAMIQUE)	ESPACEMENT DES ROUES
20T (#1)	36650 lb	3000 lb	40.8 kip	15'-0"
10T (#2)	18000 lb	1400 lb	20.3 kip	14'-2"
10T (#3)	11250 lb	1400 lb	18.2 kip	9'-2"

PRÉLIMINAIRE

NE DOIT PAS SERVIR À LA CONSTRUCTION

REVISION	DATE	DESCRIPTION	DESS	VER
----------	------	-------------	------	-----

DESSIN	CONÇU PAR	INGÉNIEUR DU PROJET	ÉCHELLE:
DESSINÉ PAR	S.L.		Comme indiqué
VERIFIÉ PAR	INGÉNIEURS CONSEILS / ARCHITECTES	DATE (mm/aaaa)	07/05/2026

CLIENT:	USINAGE SERVITECH
---------	-------------------



SCAUX PROFESSIONNEL

PROJET

USINE PRINCIPALE SERVITECH
TROIS-RIVIÈRES, QC


TITRE
CROQUIS PRÉLIMINAIRE - PLAN DE PONTS ROULANTS

NUMÉRO CONTRAT	NUMÉRO DESSIN	DIVISION	REVISION
P2026-090	EsMx301		



9 8.9 8 7.9 7.2 7 6.2 6 5.4 5 4.6 4 3.8 3.6 3 2.8 2.1 2 1.4 1.1 1

A B B.8 C D E E.2 F F.2 F.8 G G.5 H H.2 H.9 J J.5 J.9 K

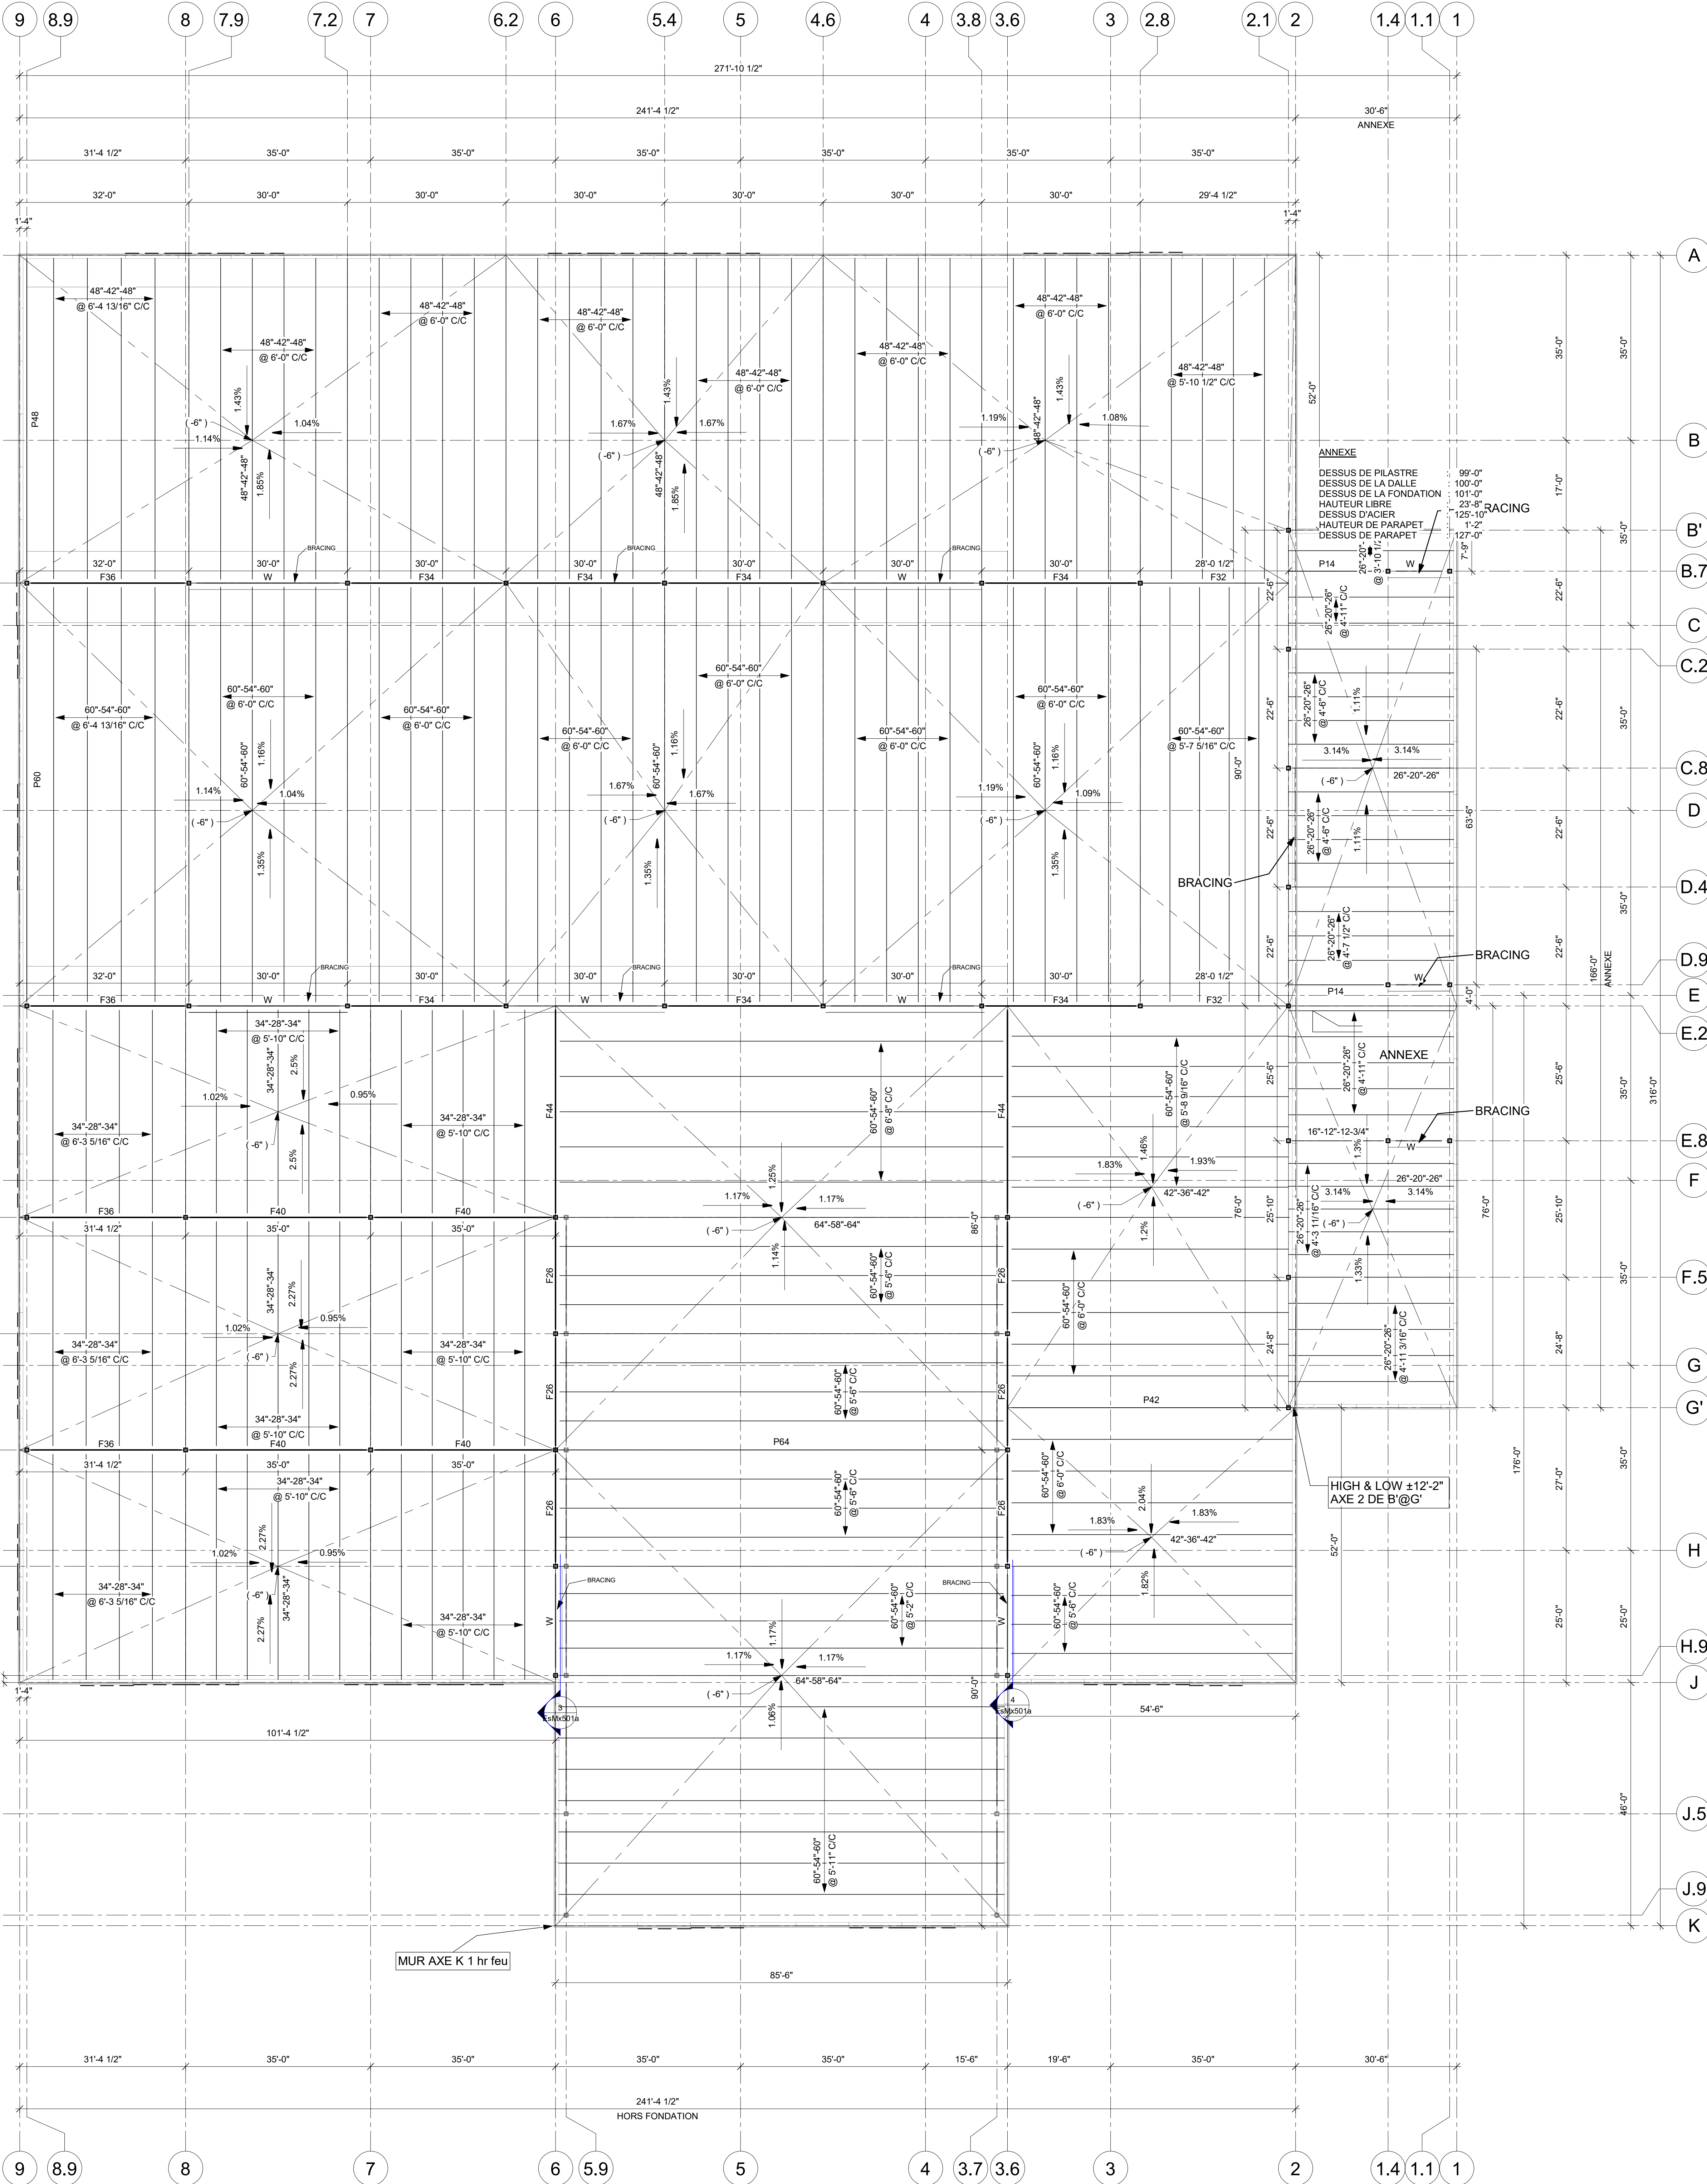

PLAN DE TOIT
1:156


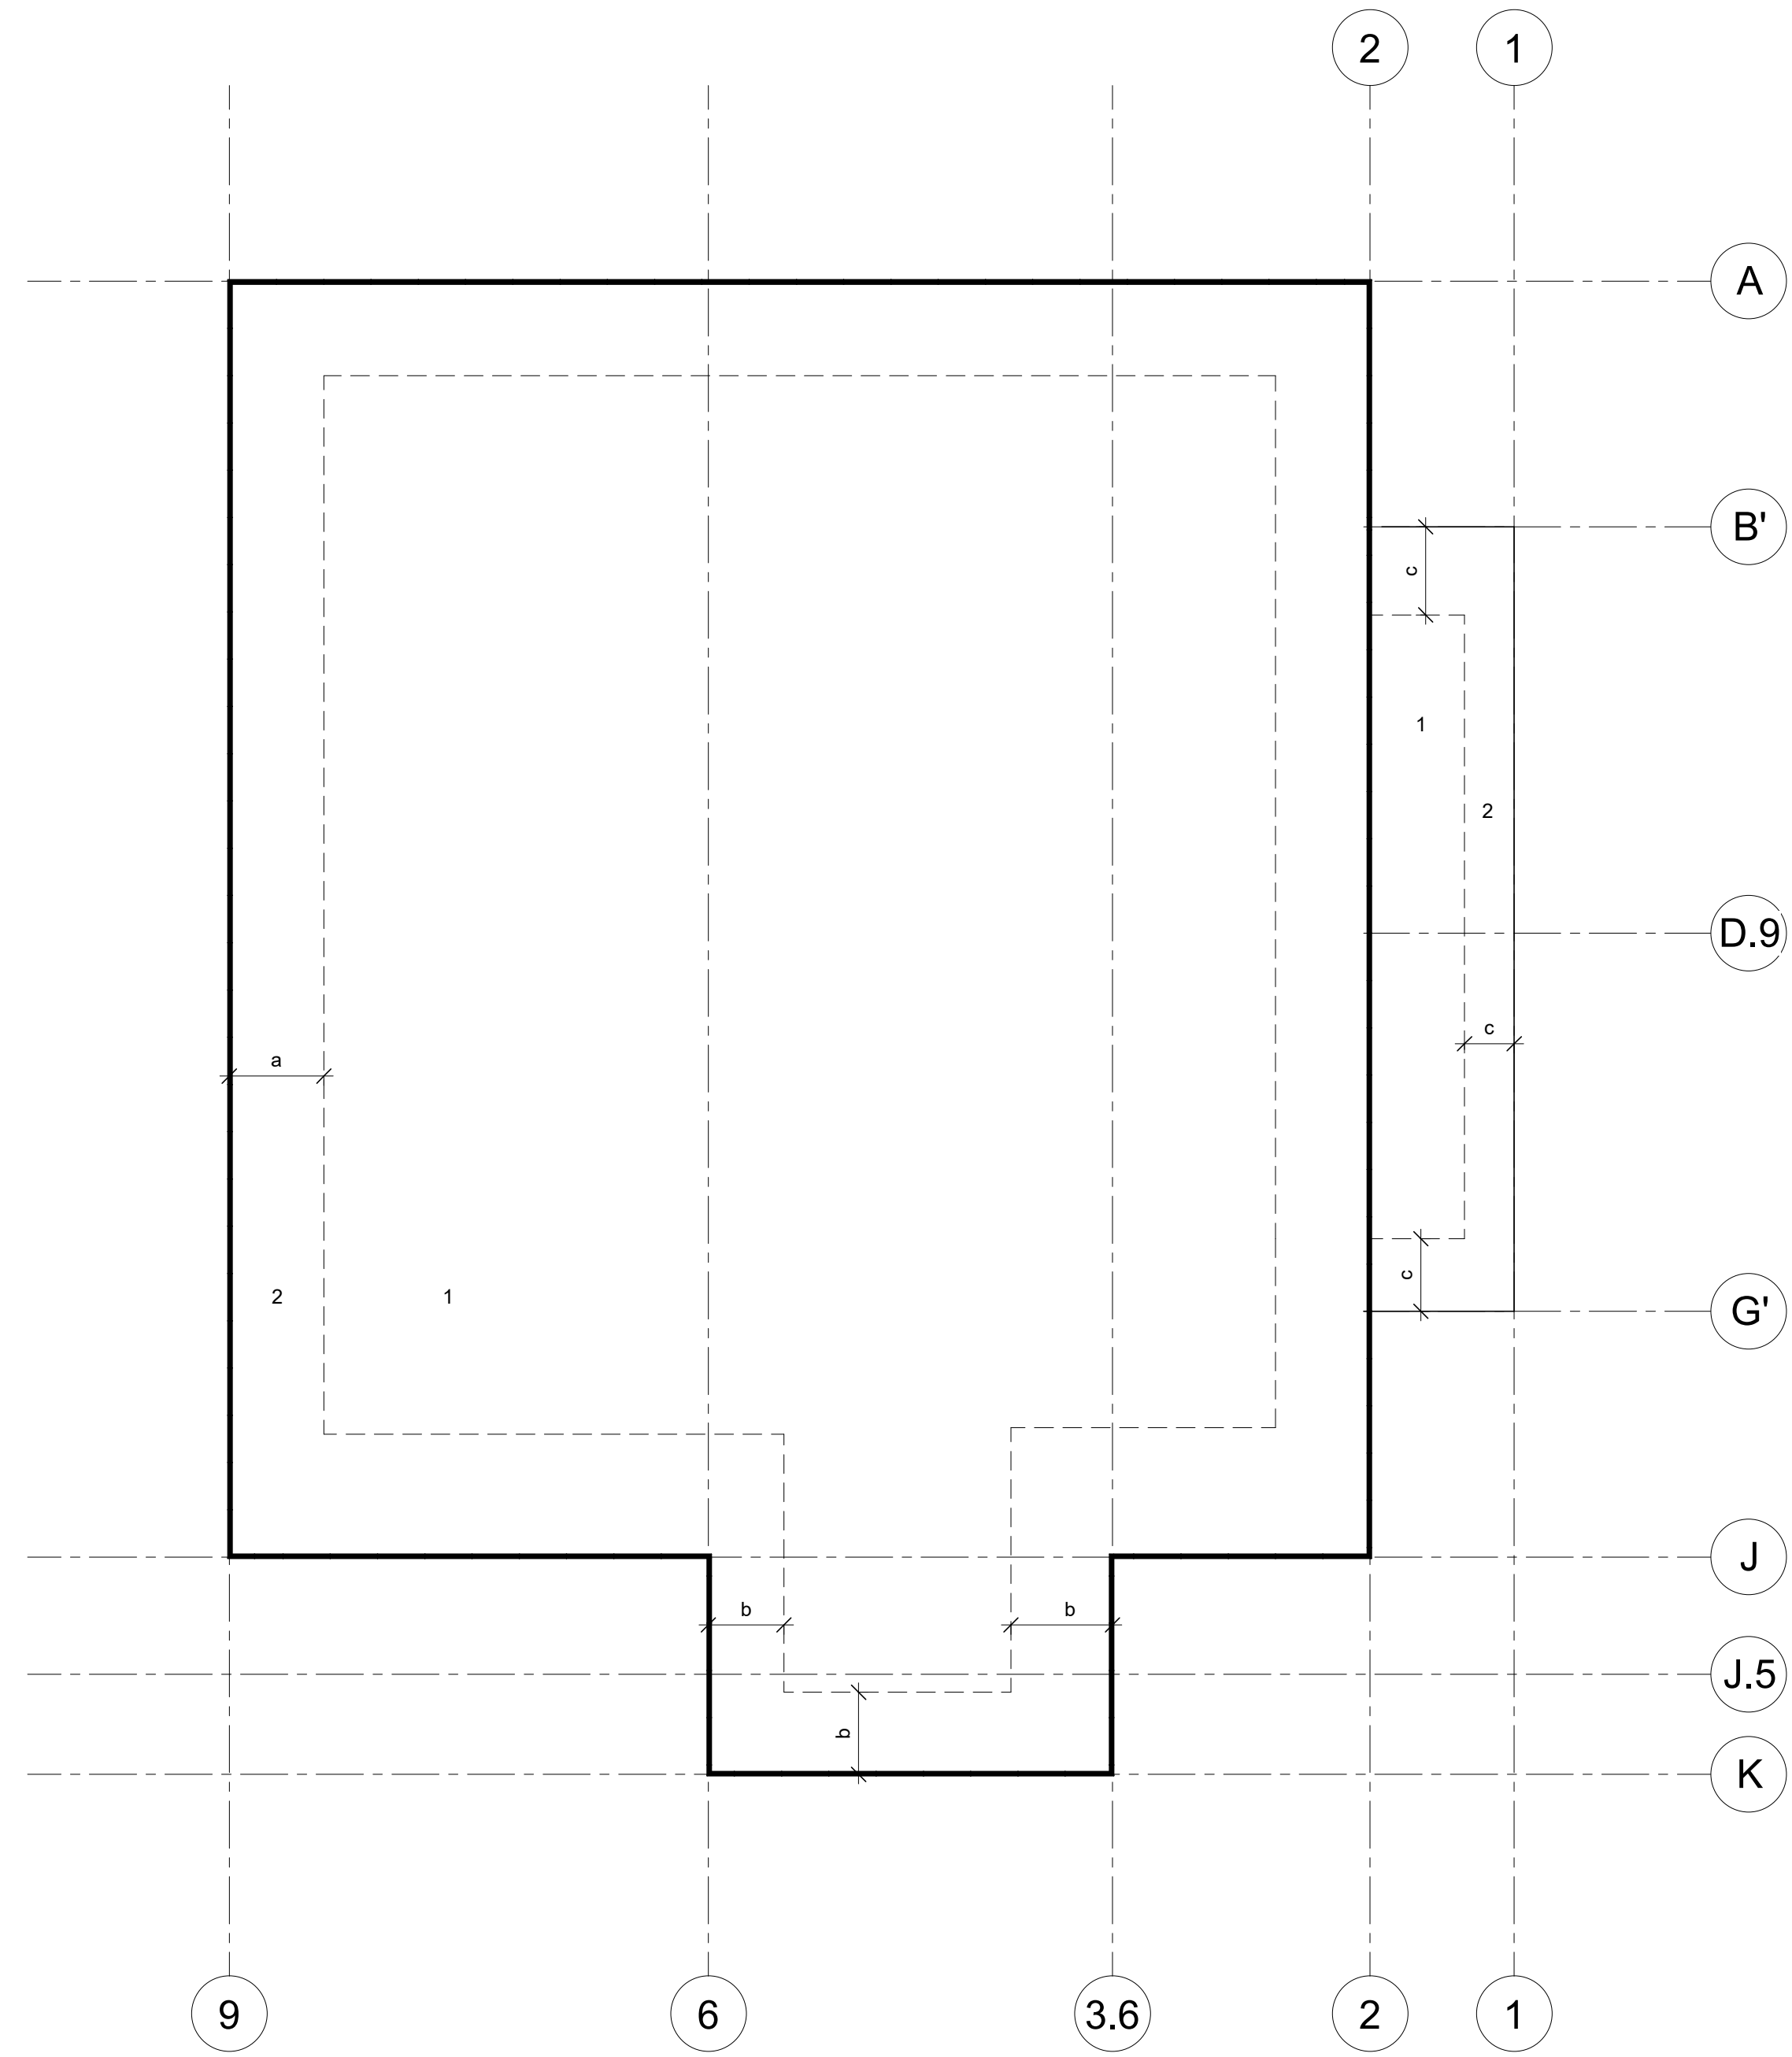


DIAGRAMME DE SOULEVEMENT BRUT (NON PONDERE)

PRESSION POSITIVE DU VENT
(NON PONDEREE) : +10.1W/pf
ZONE 1 : -18.7W/pf
ZONE 2 : -23.4W/pf
a: 15'-0"
b: 9'-0"
c: 4'-0"

ACCUMULATION DE NEIGE

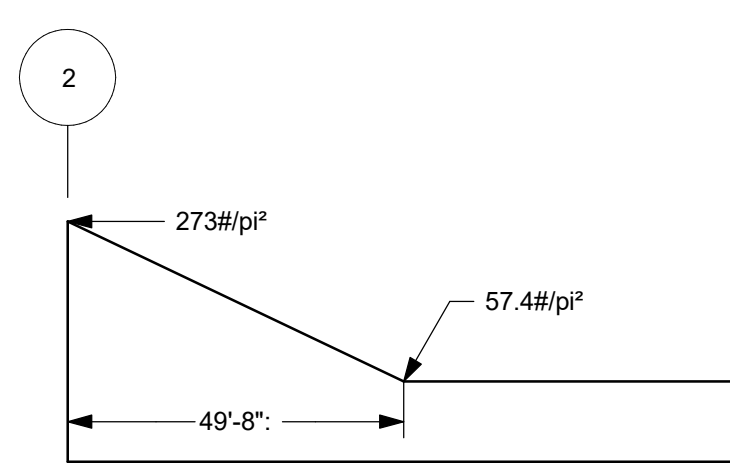

NOTE POUR LE CONTRACTEUR/ÉRECTEUR:

IL EST STRICTEMENT DEFENDU DE MODIFIER, COPIER, REPRODUIRE OU DE DISTRIBUER CES DESSINS OU QUELQUES REPRÉSENTATIONS DE CES DESSINS, PAR TOUTES SOURCES DE MÉDIA INCLUANT ÉLECTRONIQUEMENT, SANS L'APPROBATION ÉCRITE DE GROUPE CANAM INC.

TOIT

DESSUS DE PILASTRE : 99'-0"
DESSUS DE LA DALLE : 100'-0"
DESSUS DE LA FONDATION : 101'-0"
HAUTEUR LIBRE : 33'-0"
DESSUS STAGER : 138'-0"
HAUTEUR DE PARAPET : 1'-2"
DESSUS DE PARAPET : 139'-2"

Système (Sol de classe D assumé)

S_u : 1.0
 $S_u(0.2)$: 0.569
 $S_u(0.5)$: 0.516
 $S_u(1.0)$: 0.316
 $S_u(2.0)$: 0.194
 $S_u(5.0)$: 0.0434
 $S_u(10.0)$: 0.0137
PGA : 0.329
PCV : 0.361

CHARGES :

- Charge morte au toit (excluant charge collatérale) : lbs/pf
- Charge collatérale : lbs/pf (incluant éclairage étou mécanique et gicleurs plus petite que 4" de diamètre)
- Charge de neige au toit : 57.4 lbs/pf
- Charge vive au toit : 0 lbs/pf
- Charge de vent q 1/50 : 9.0 lbs/pf
- Charge de neige au sol : $S_s = 58.5$ lbs/pf
- Catégorie de risque : normal
- Coefficient de surcharge de neige : $C_s = 0.84$
- Coefficient de vent : $C_w = 1.0$

Code Applicable : Code National du Bâtiment du Canada
Code du bâtiment du Québec, dernières éditions adoptées
Code de Pratique Standard ICCA.

Type de sol assumé : classe D

NOTE :

1. Si toutefois la catégorie d'emplacement devient E ou F selon le rapport géotechnique, le concept structural préliminaire (localisation et géométrie des contreventements, etc.) devra être validé et coordonné par l'ingénieur de Canam.

PRÉLIMINAIRE

NE DOIT PAS SERVIR À LA CONSTRUCTION

REVISION	DATE	DESCRIPTION	DESS	VER
1				

DESSIN :

DESSINÉ PAR	CONÇU PAR	INGÉNIEUR DU PROJET	ÉCHELLE :
S.L.			Comme indiqué

VERIFIÉ PAR :

INGÉNIEURS CONSEILS / ARCHITECTES	DATE (général)
	07/05/2026

CLIENT : USINAGE SERVITECH

CANAM

11505, 1re Avenue, bureau 500, Saint-Georges Beauce
Québec, Canada G5Y 7X3
Téléphone : (418) 228-8031
Sans frais : (877) 469-8049
www.canam.com

SCAUX PROFESSIONNEL


PROJET :

USINE PRINCIPALE SERVITECH
TROIS-RIVIÈRES, QC

TITRE :


CROQUIS PRÉLIMINAIRE - PLAN DE TOIT

NUMÉRO CONTRAT : P2026-090
NUMÉRO DESSIN : EsMx401
DIVISION :
REVISION : 1

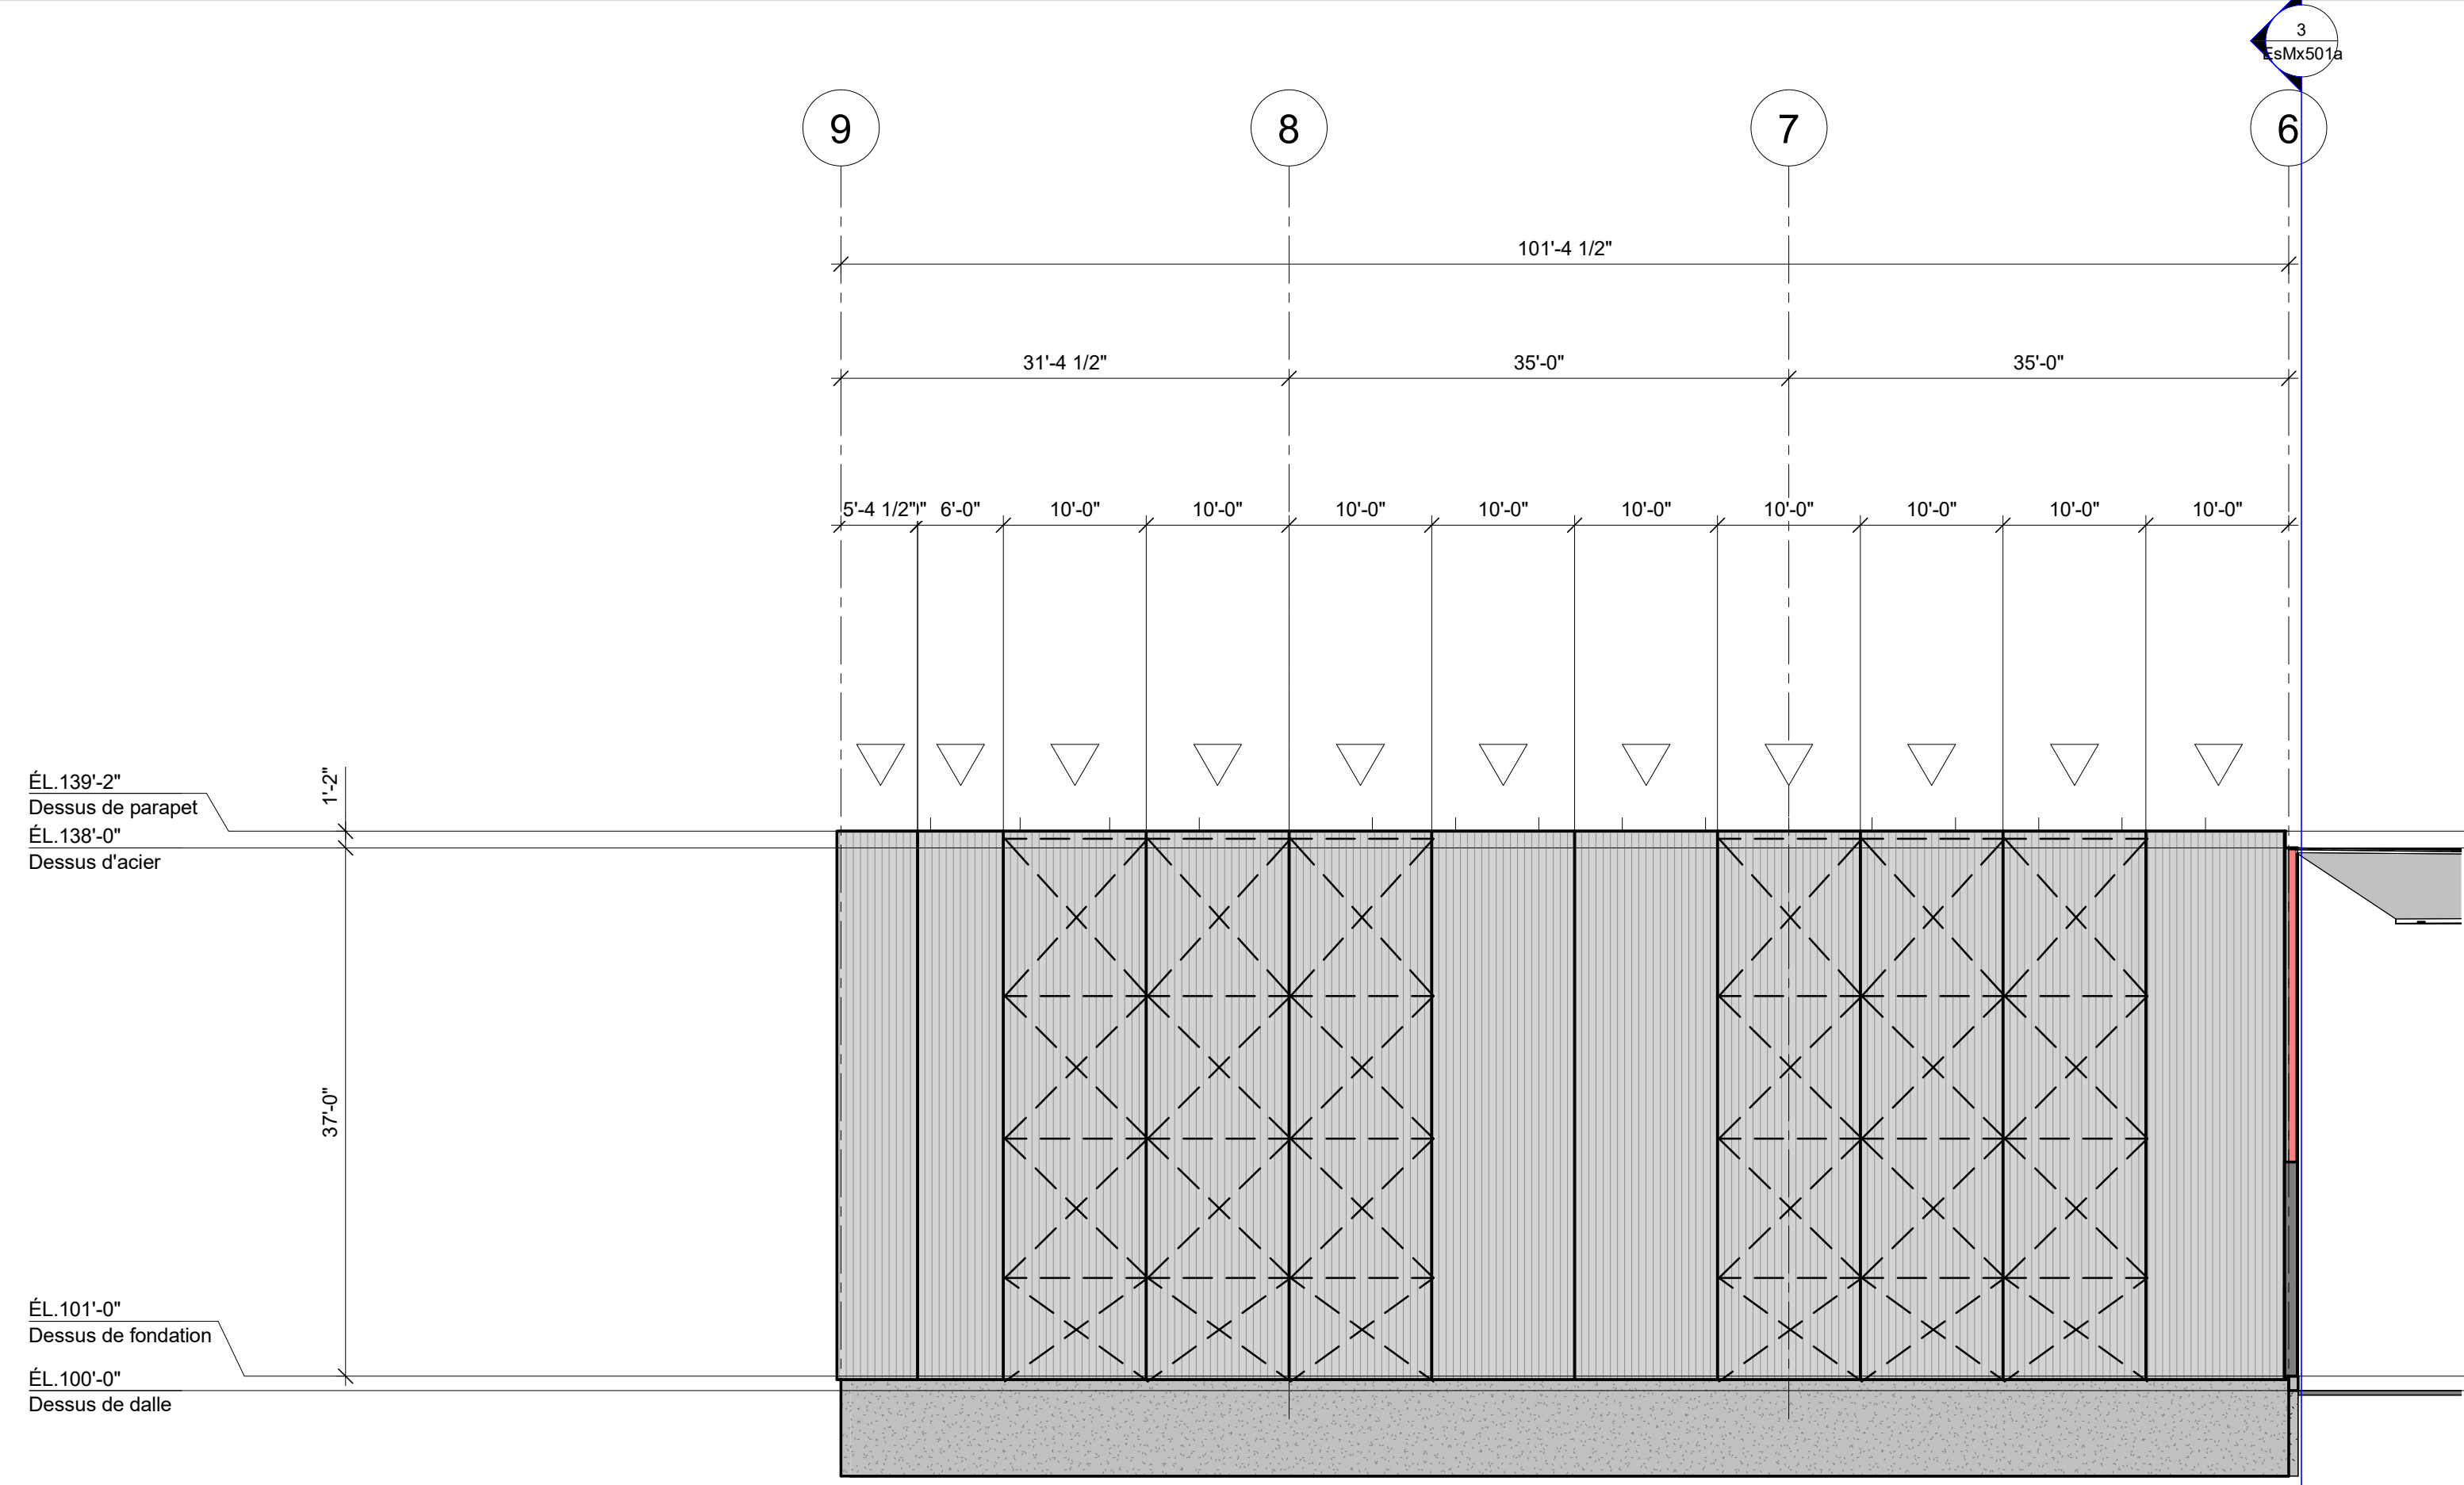


ÉLÉVATION AXE J DE 9@6 (SUD)

3/32" = 1'-0"

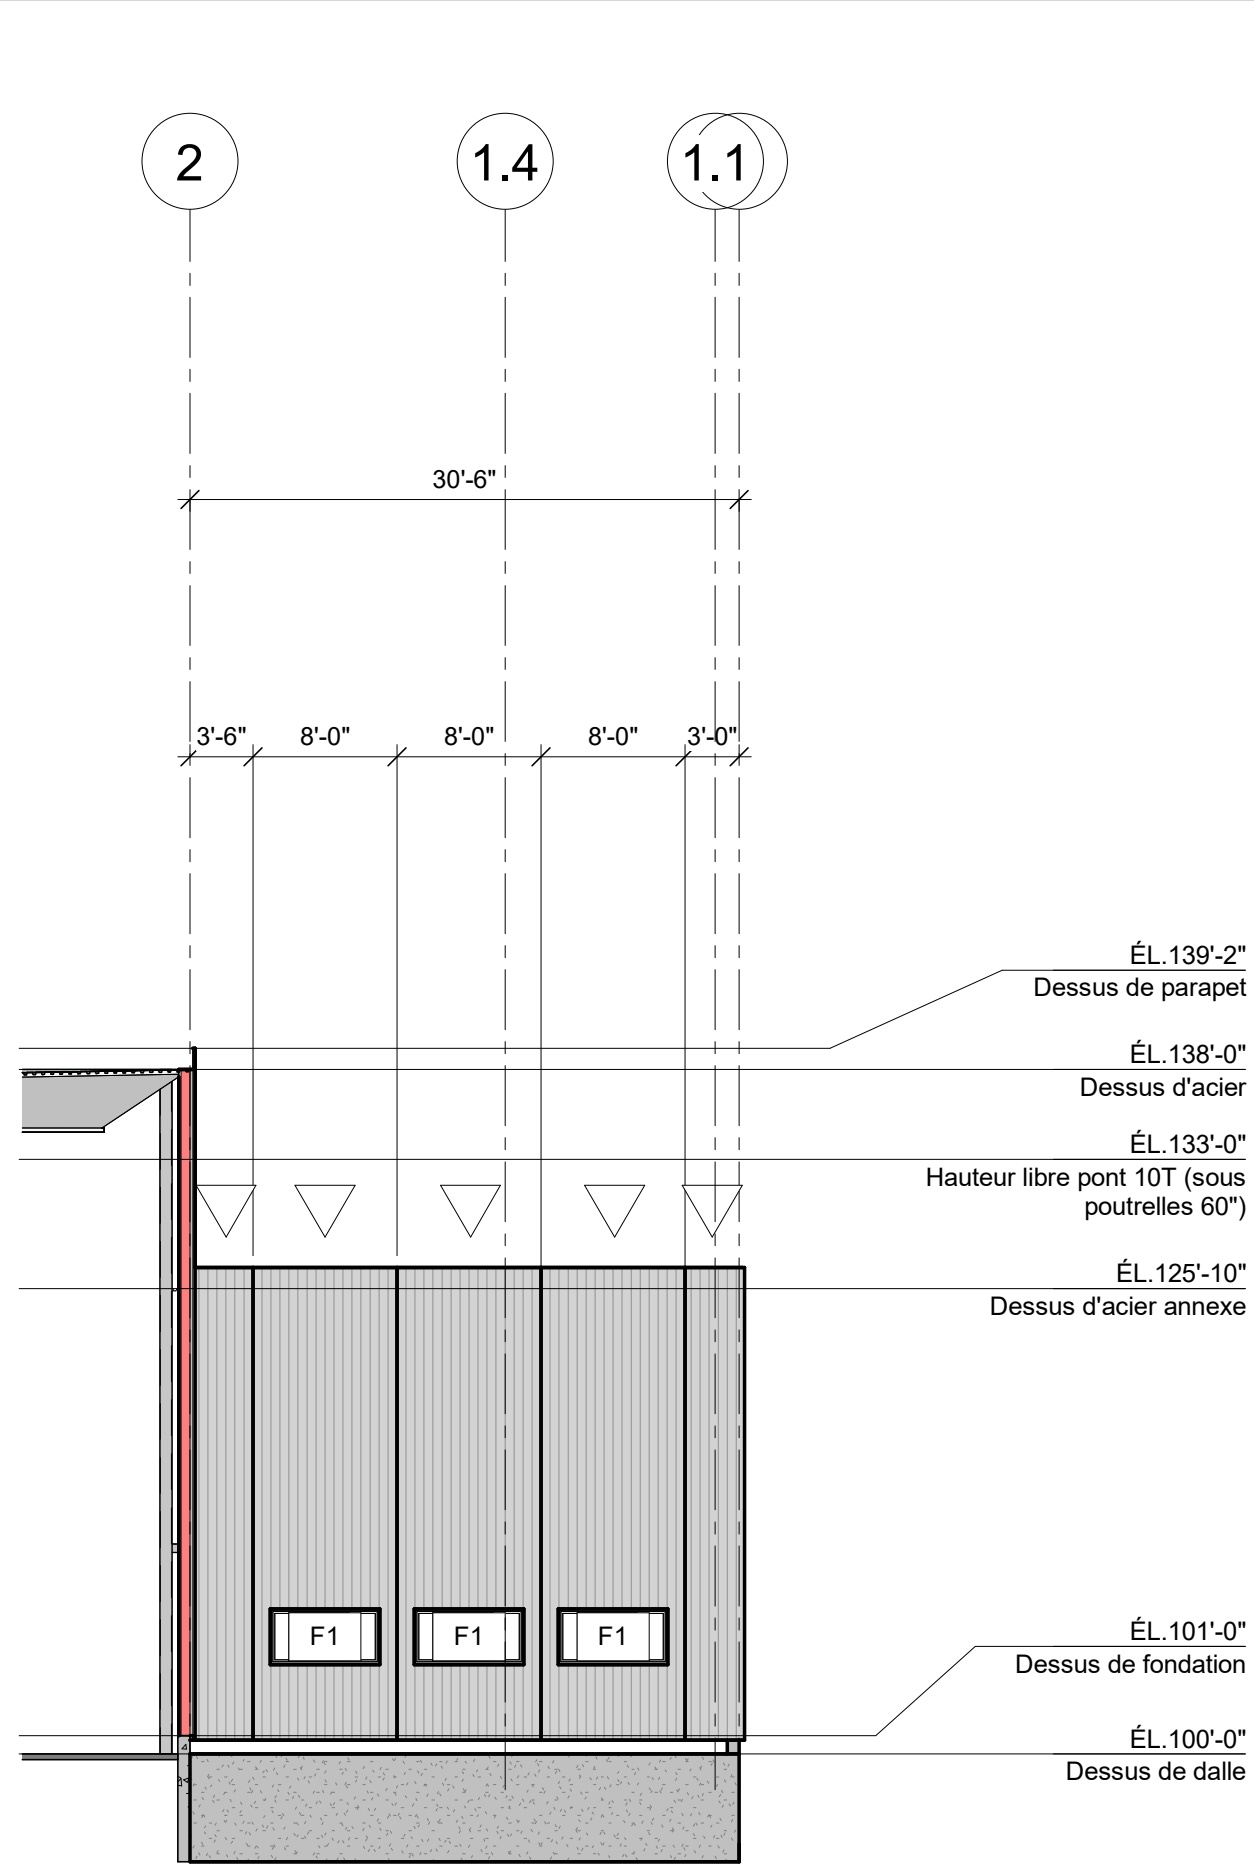


ÉLÉVATION AXE G' (SUD)

3/32" = 1'-0"

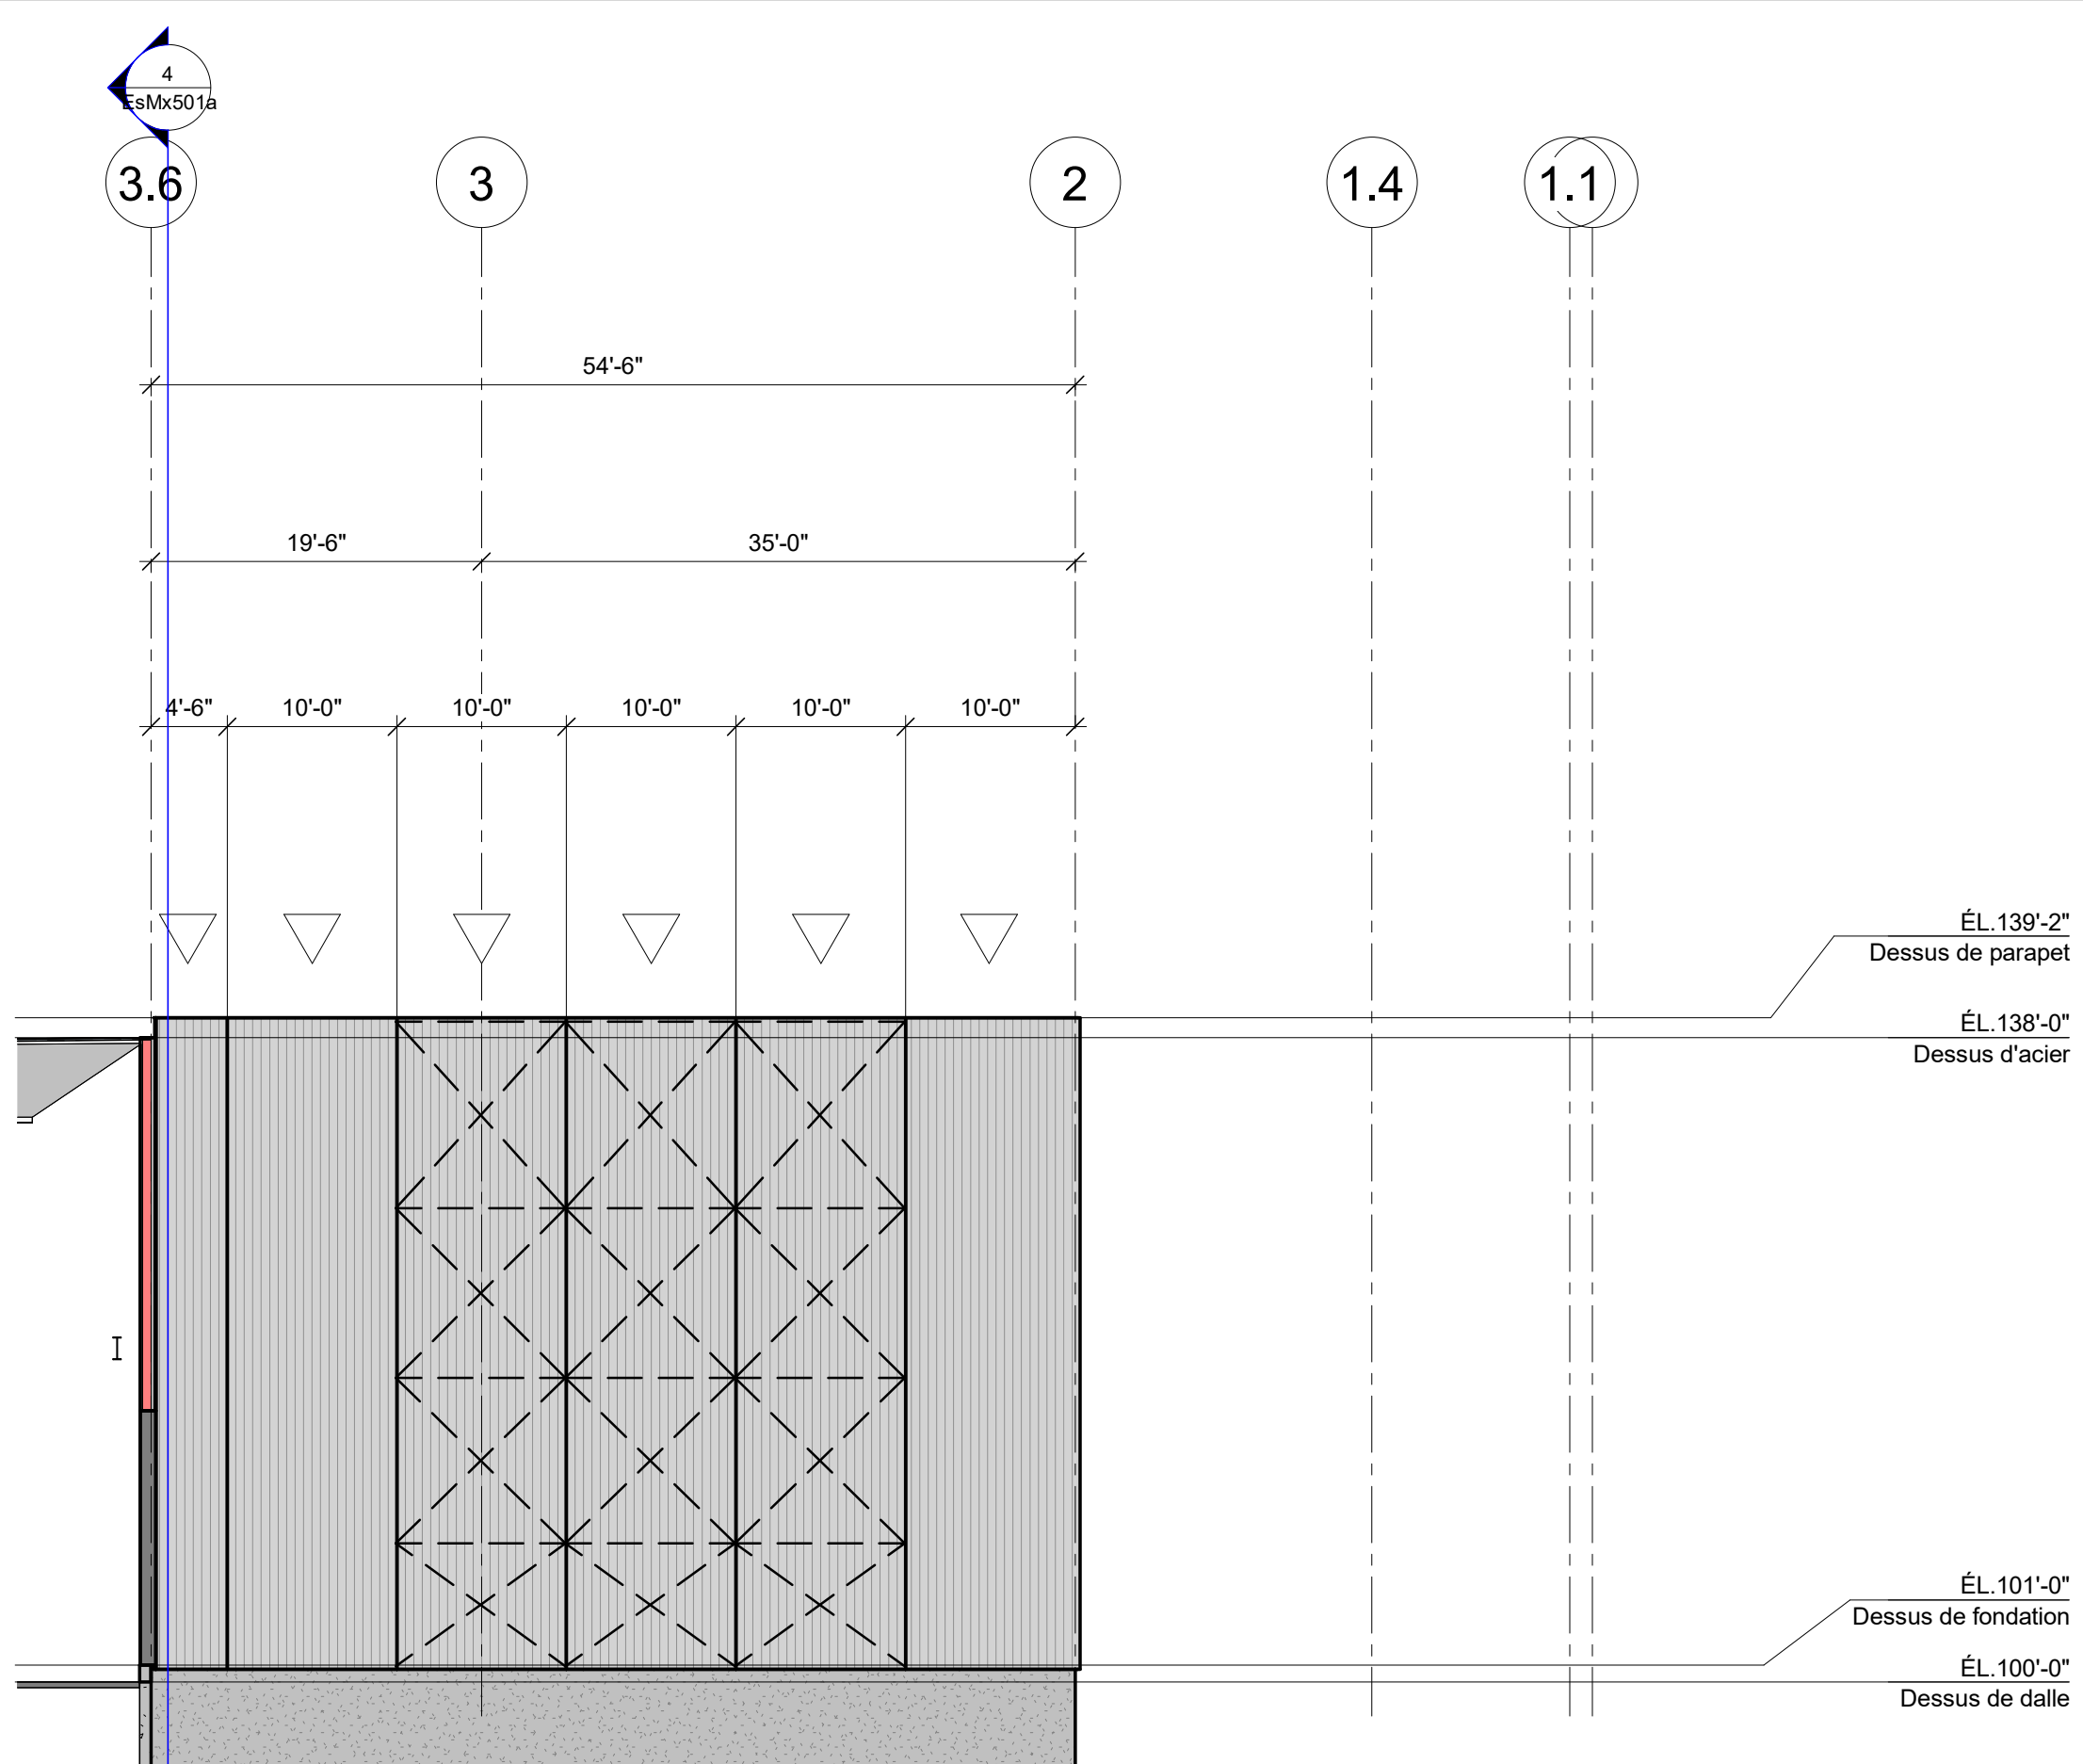


ÉLÉVATION AXE J DE 3.6@2 (SUD)

3/32" = 1'-0"

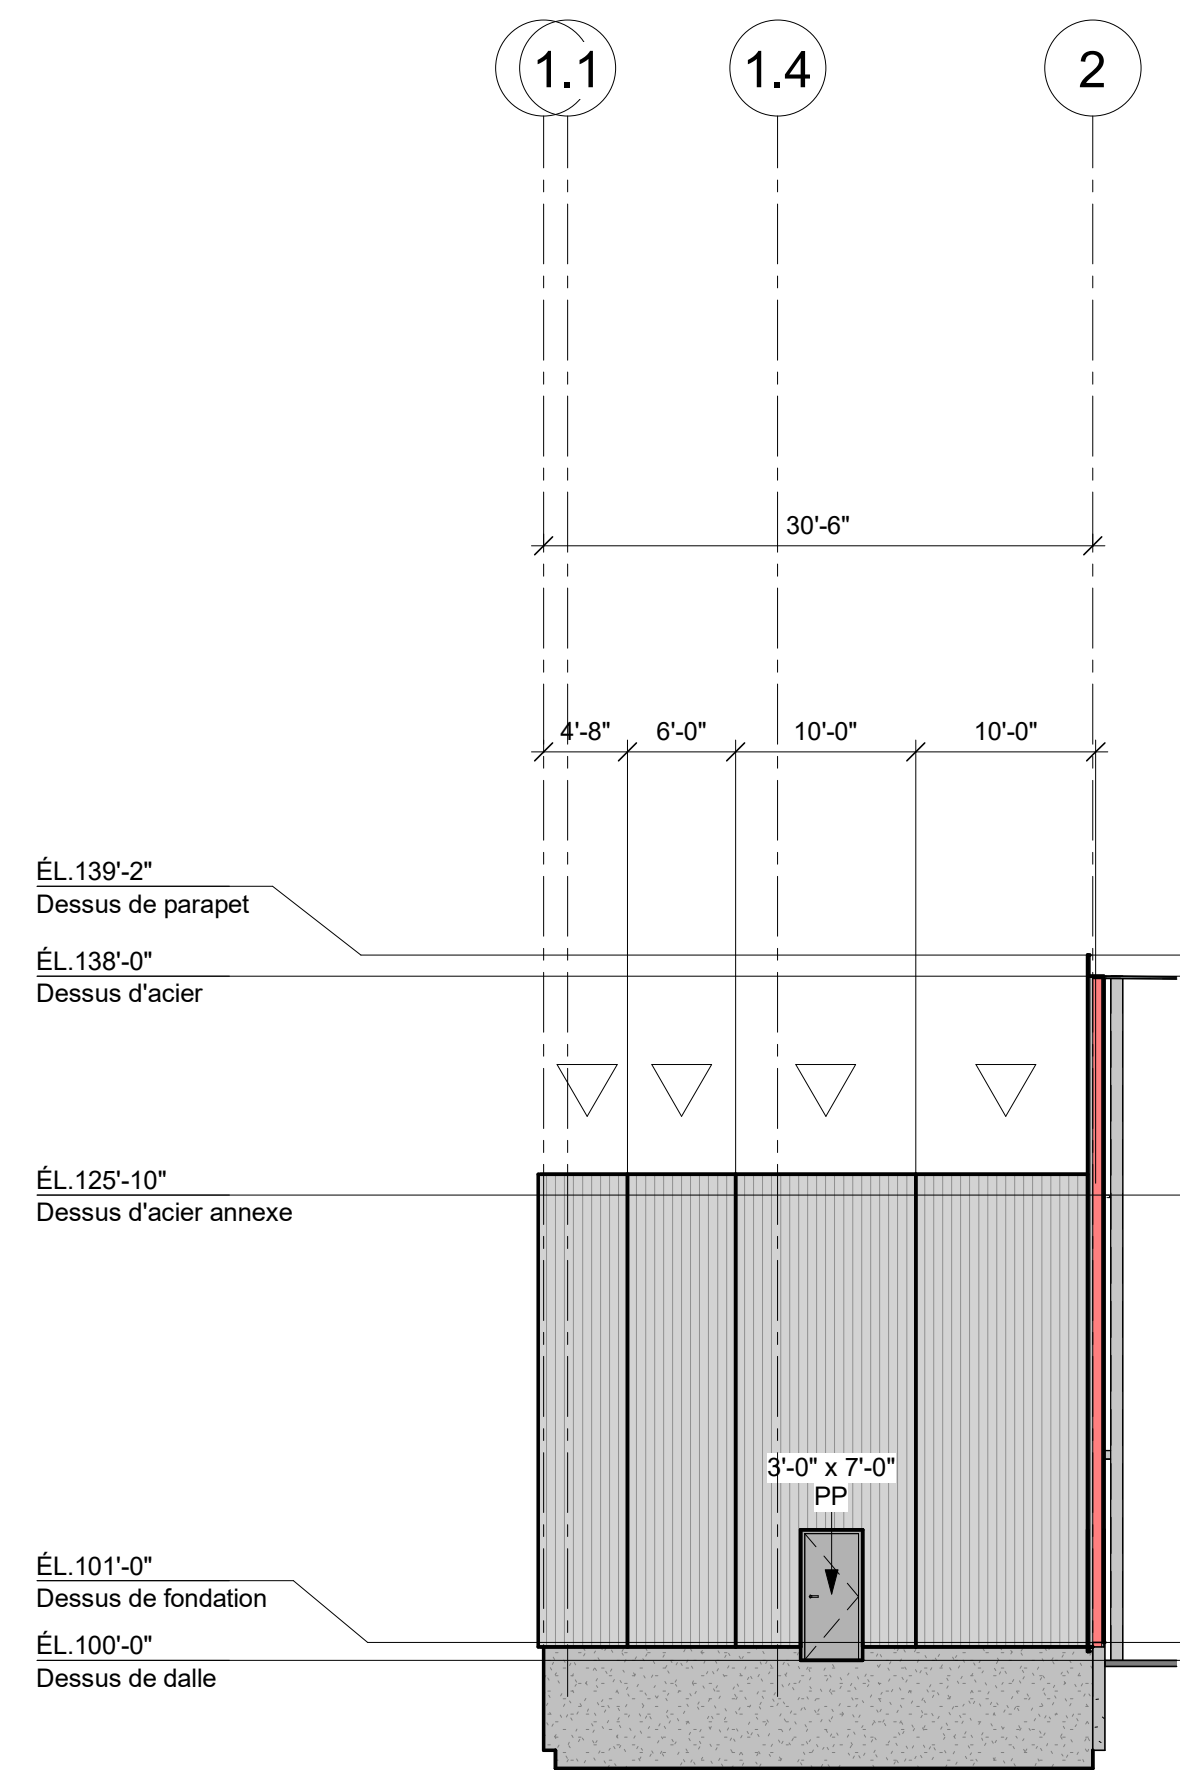


ÉLÉVATION AXE B' (NORD)

3/32" = 1'-0"

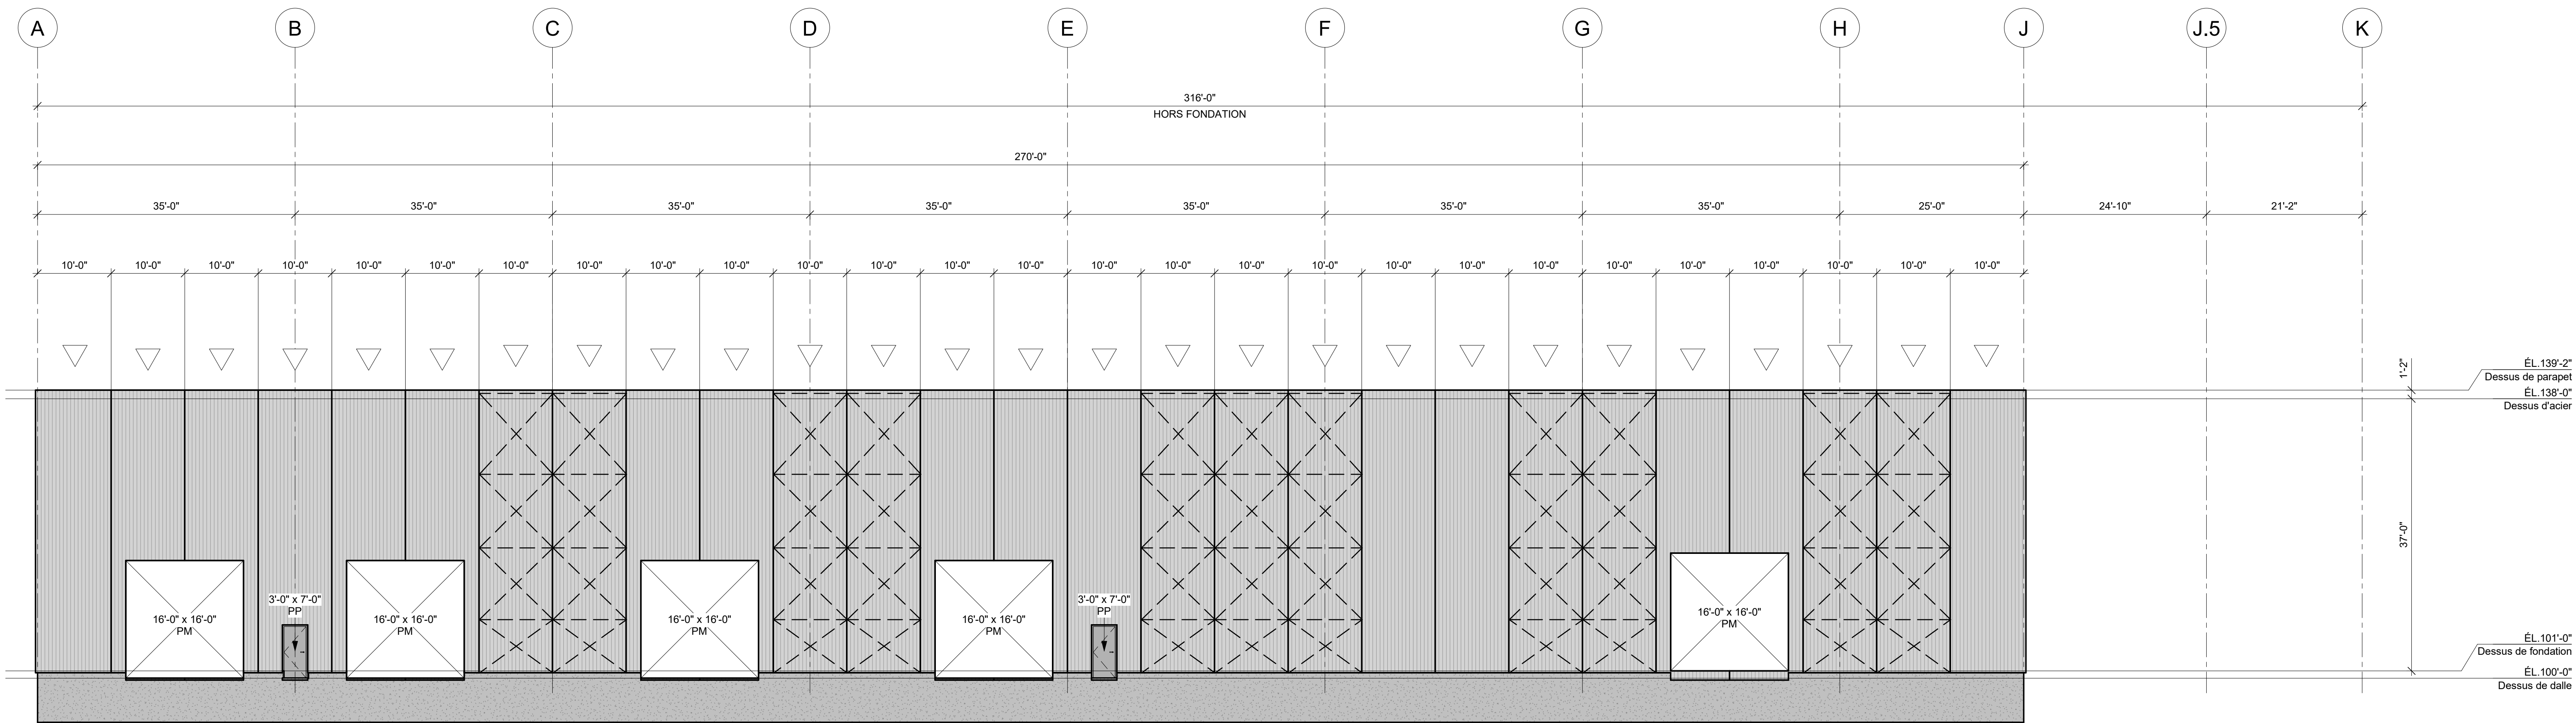


ÉLÉVATION AXE 9 (OUEST)

3/32" = 1'-0"

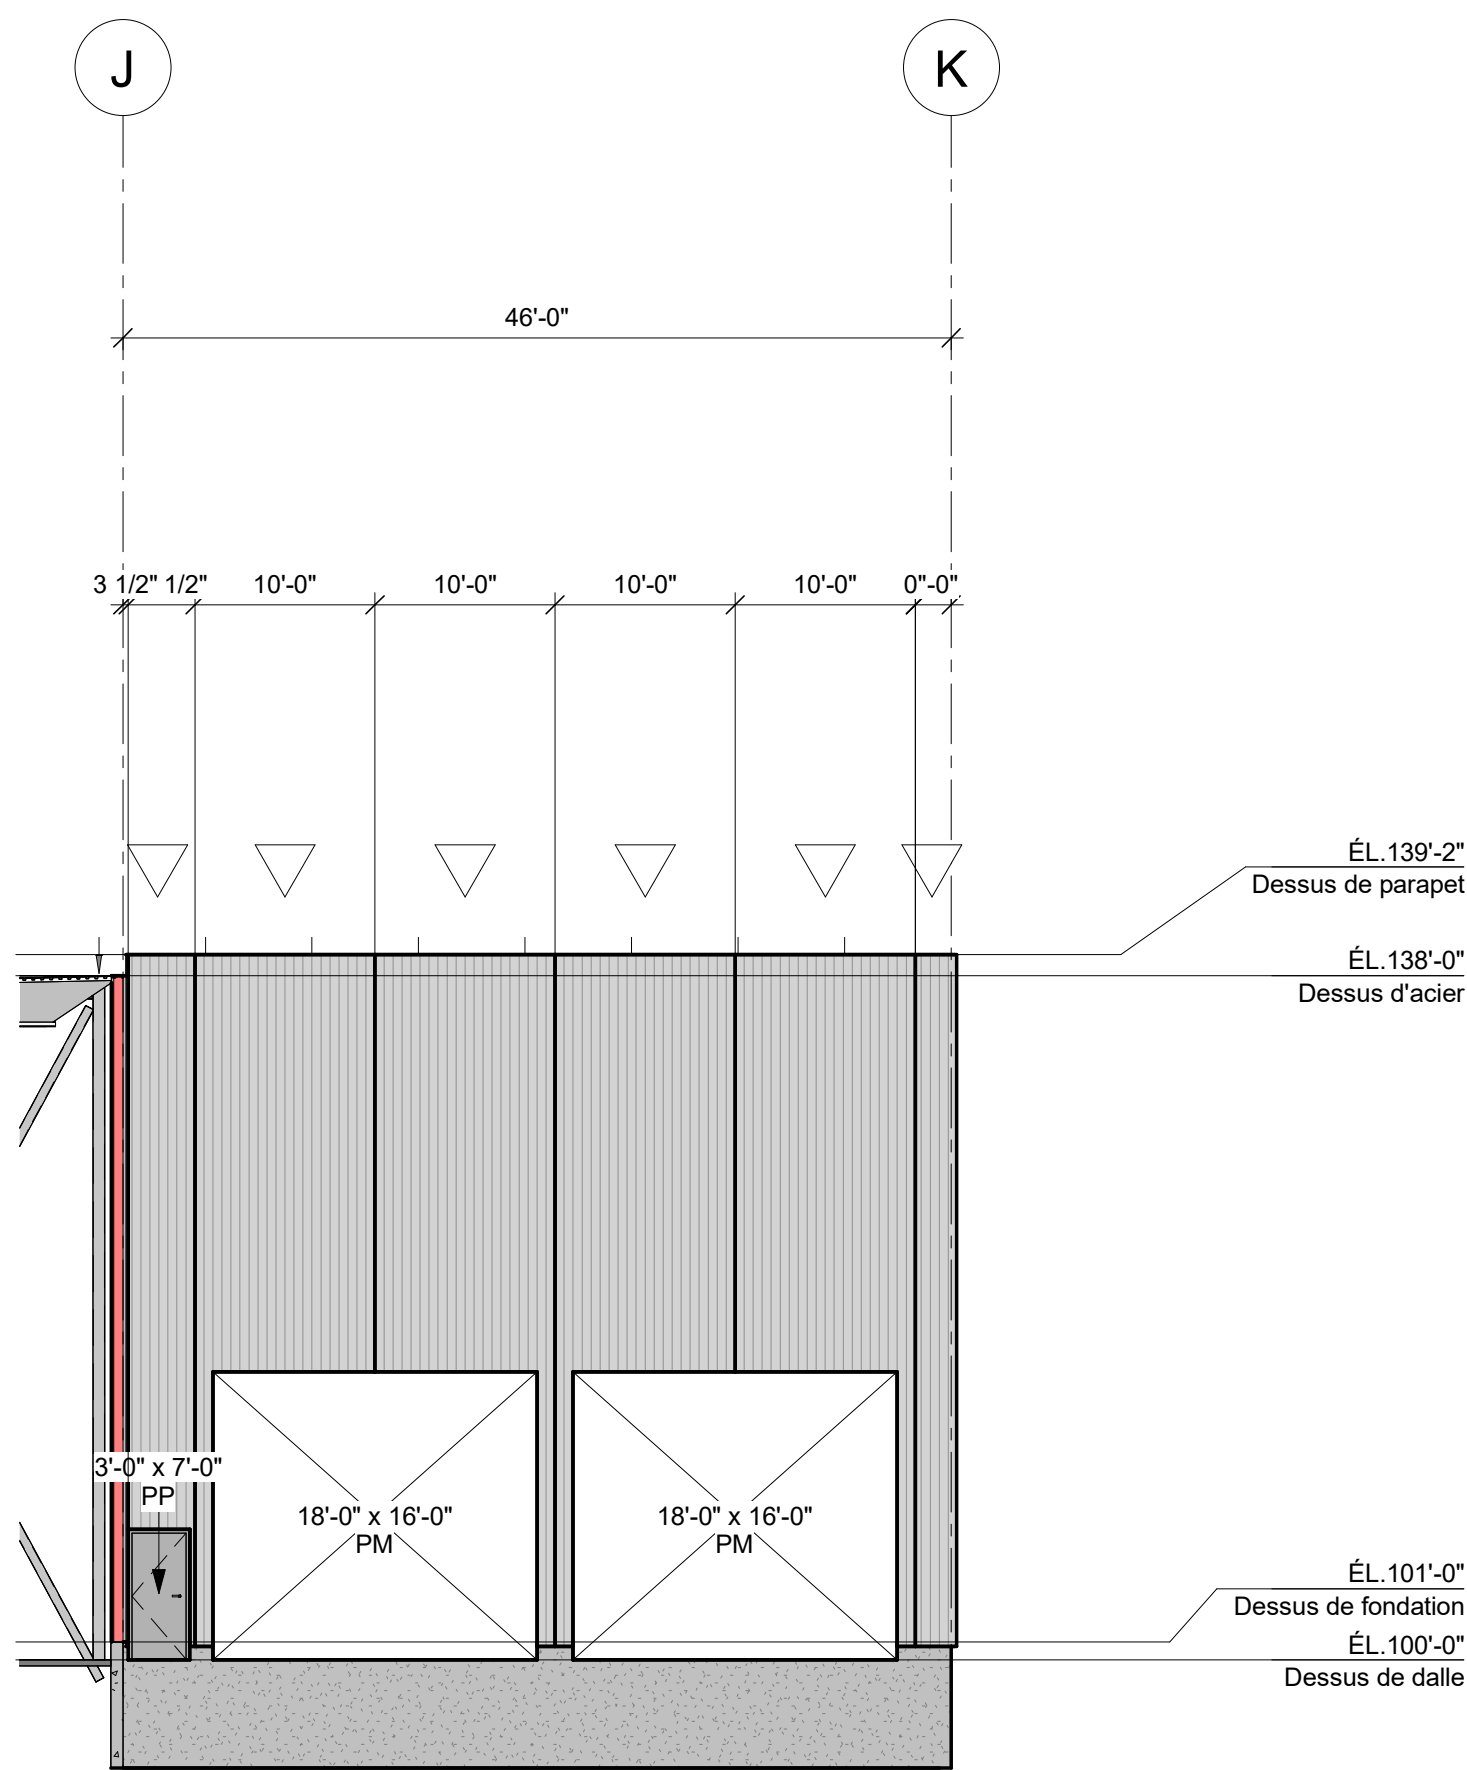

ÉLÉVATION AXE 6 (OUEST)

3/32" = 1'-0"

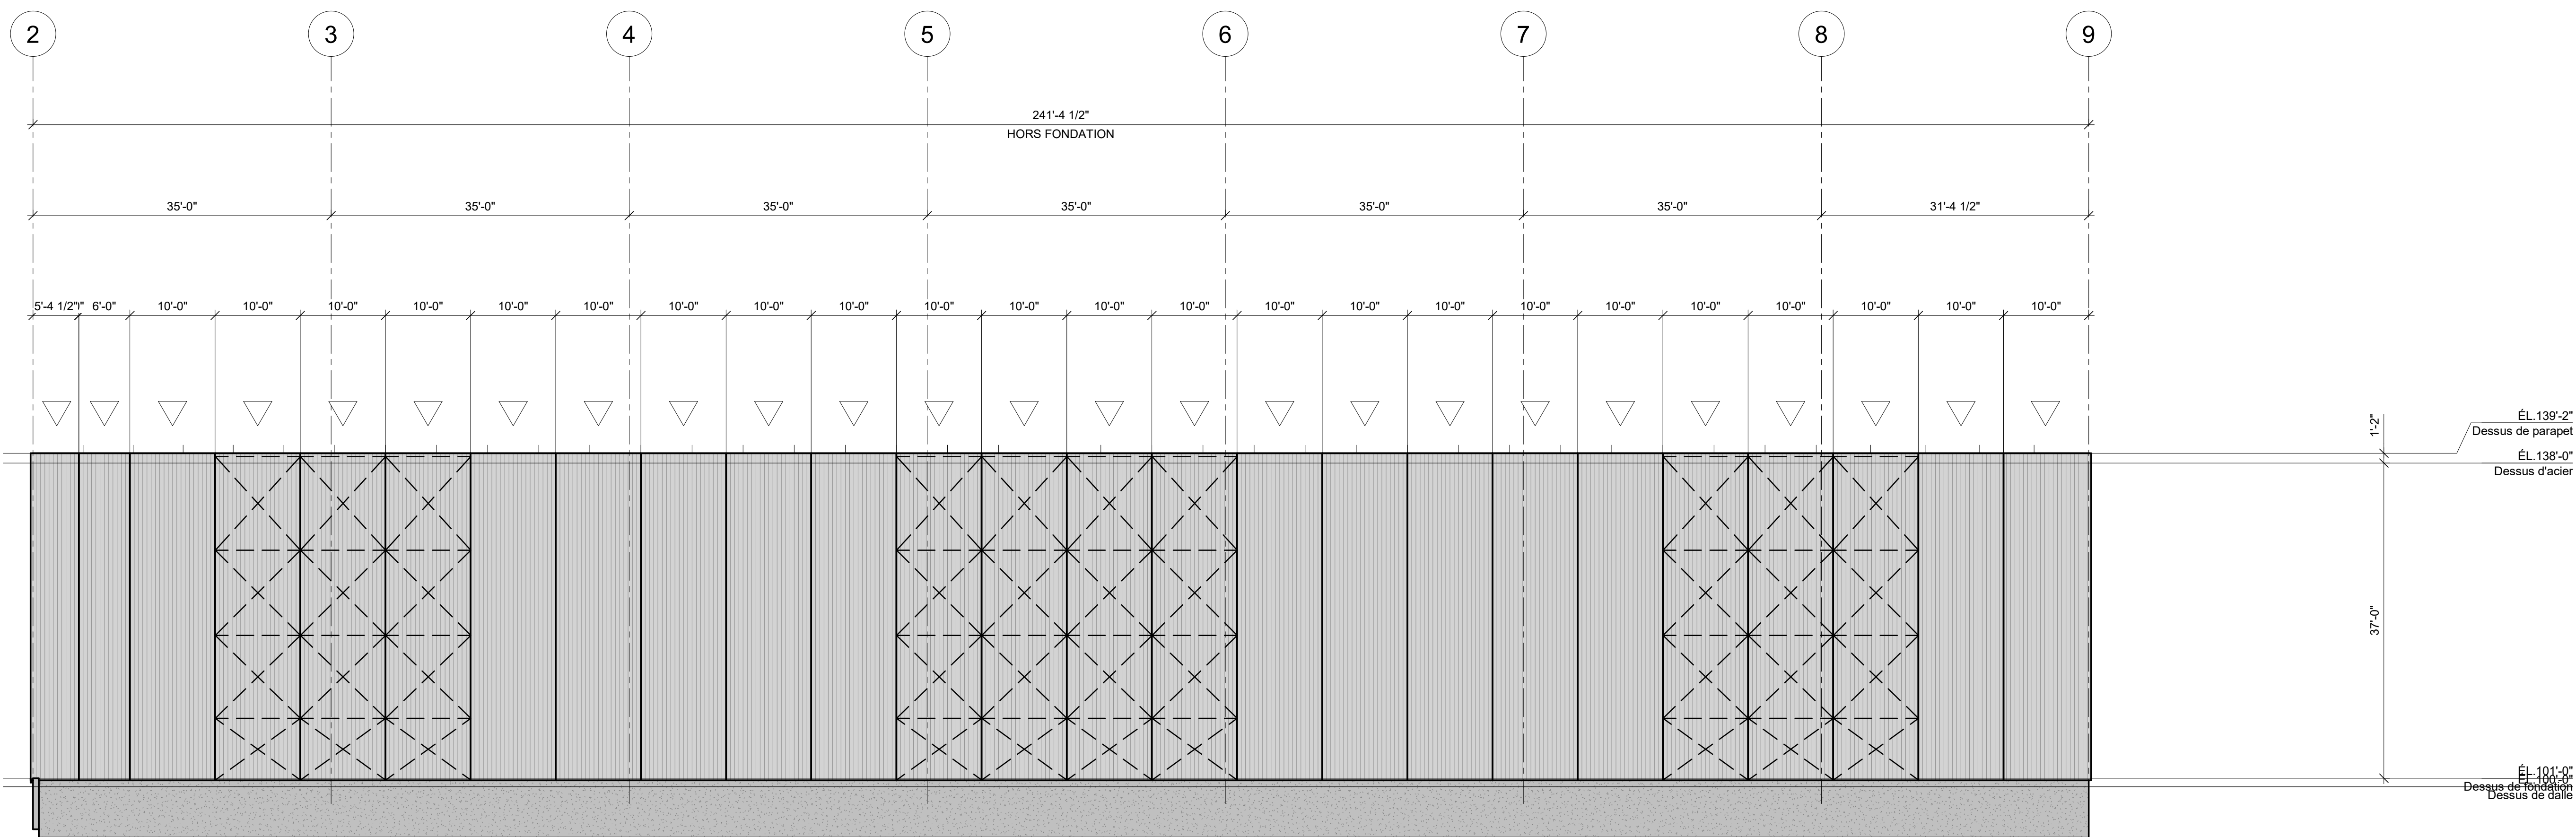

ÉLÉVATION AXE A (NORD)

3/32" = 1'-0"

NOTE POUR LE CONTRACTEUR/ÉRECTEUR:
IL EST STRICTEMENT DÉFENDU DE MODIFIER, COPIER, REPRODUIRE OU DE DISTRIBUER CES DESSINS OU QUELQUES REPRÉSENTATIONS DE CES DESSINS, PAR TOUTES SOURCES DE MÉDIA INCLUANT ÉLECTRONIQUEMENT, SANS L'APPROBATION ÉCRITE DE GROUPE CANAM INC.

PRÉLIMINAIRE

NE DOIT PAS SERVIR À LA CONSTRUCTION

REVISION	DATE	DESCRIPTION	DESS	VER
----------	------	-------------	------	-----

GERANT DE PROJET	-	-	-	-
------------------	---	---	---	---

DESSIN	CONÇU PAR	INGÉNIEUR DU PROJET	ÉCHELLE:
DESSINÉ PAR	S.L.		3/32" = 1'-0"
VÉRIFIÉ PAR	INGÉNIEURS CONSEILS / ARCHITECTES	DATE (mm/aa/aaaa)	07/05/2026

CLIENT:	USINAGE SERVITECH
---------	-------------------


CANAM
11505, 1re Avenue, bureau 500, Saint-Georges Beauce
Québec, Canada G5Y 7X3
Téléphone : (418) 228-8031
Sans frais : (877) 459-8049
www.canam.com

SCAUX PROFESSIONNEL


PROJET
**USINE PRINCIPALE SERVITECH
TROIS-RIVIÈRES, QC**

TITRE
**CROQUIS PRÉLIMINAIRE -
ÉLÉVATIONS 1 DE 3**


NUMÉRO CONTRAT	NUMÉRO DESSIN	DIVISION	REVISION
P2026-090	EsMx501		

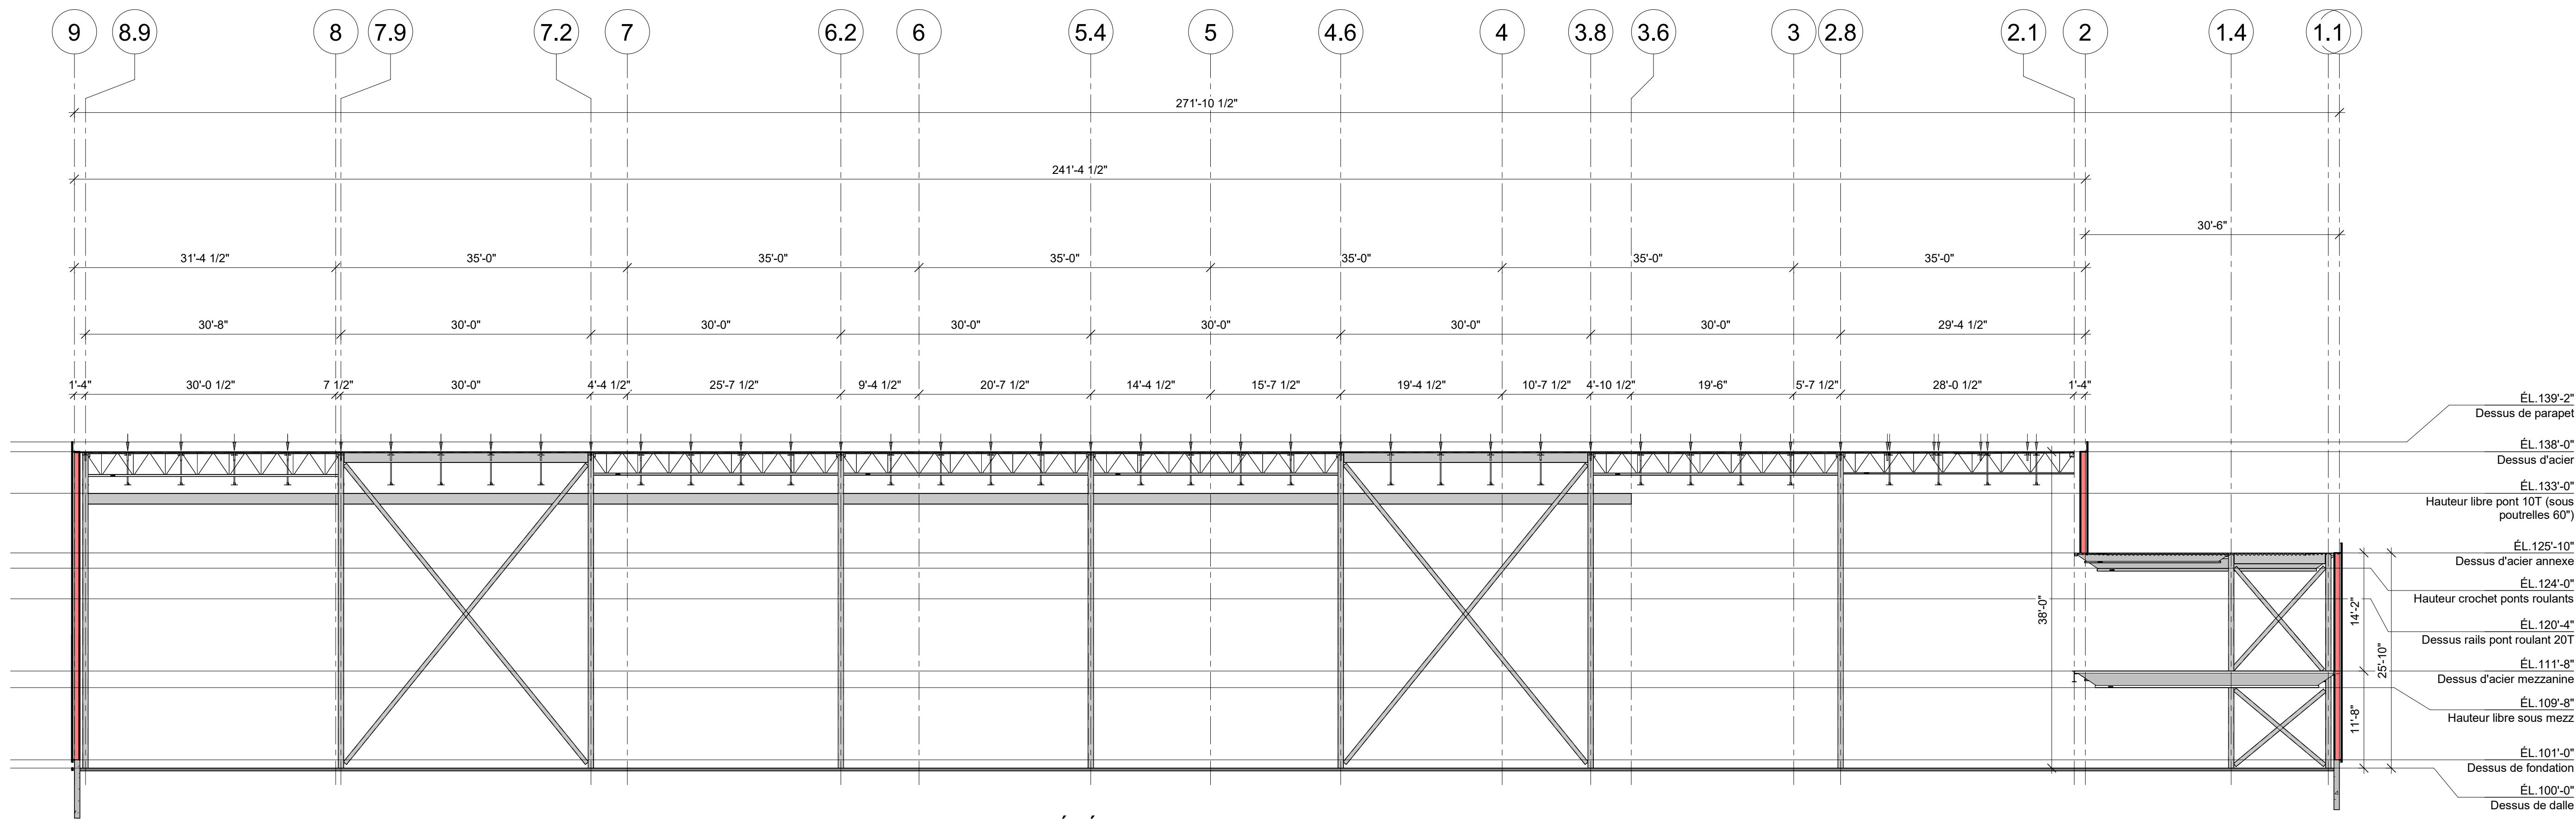


ÉLÉVATION AXE B.8 (STRUCTURE)(SUD)
3/32" = 1'-0"

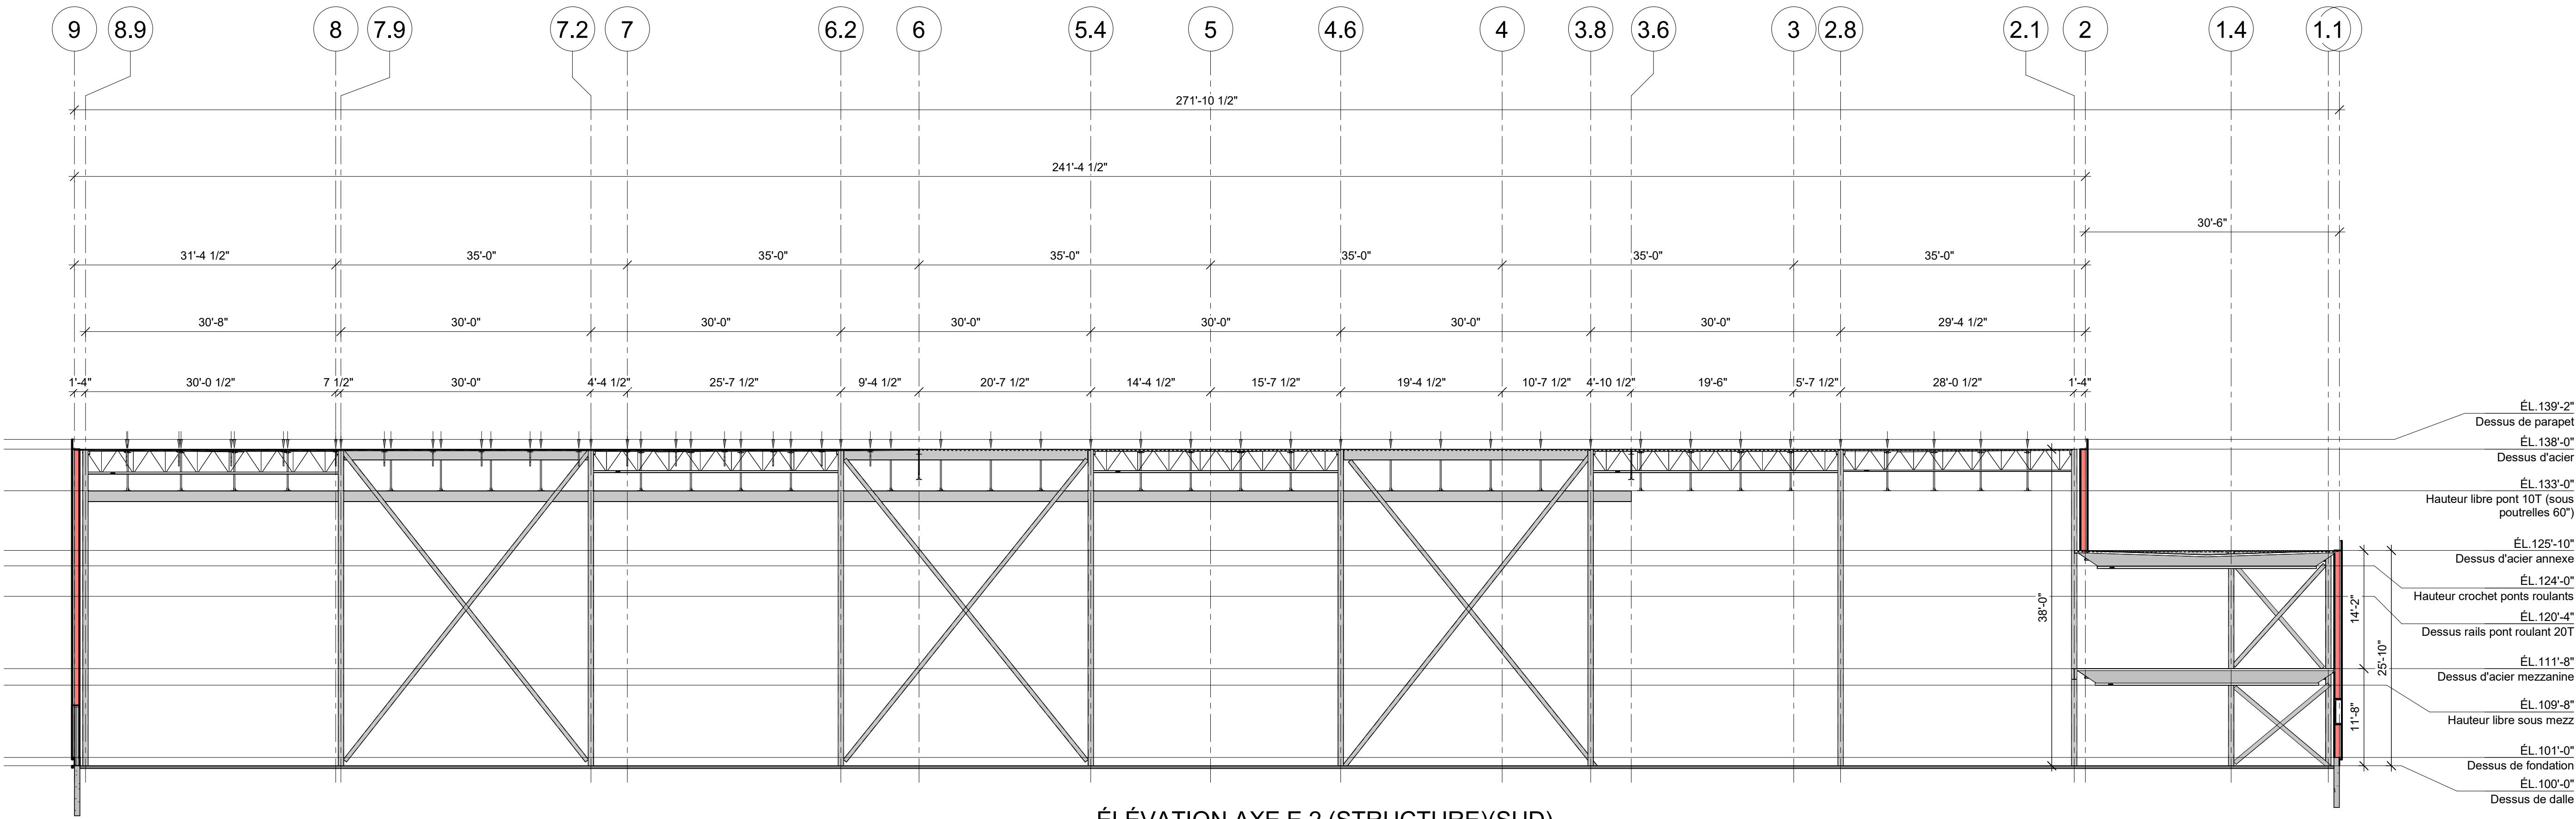

ÉLÉVATION AXE E.2 (STRUCTURE)(SUD)
3/32" = 1'-0"

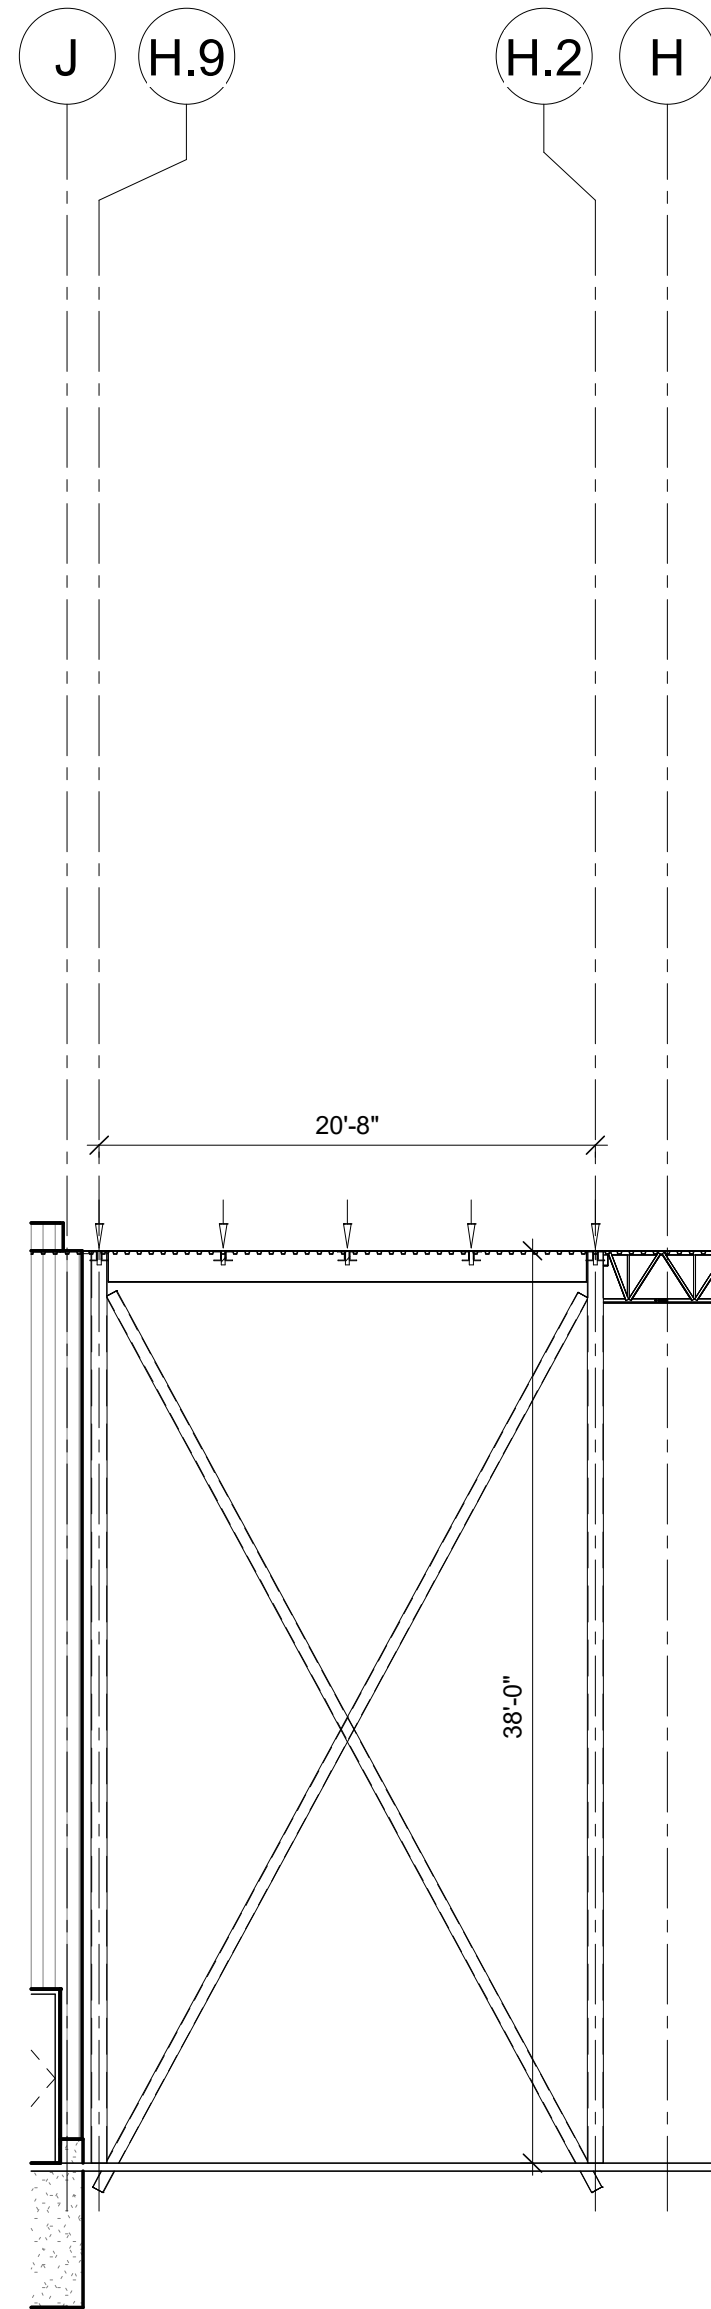

AXE 6 DE H.2@H.9
1/8" = 1'-0"

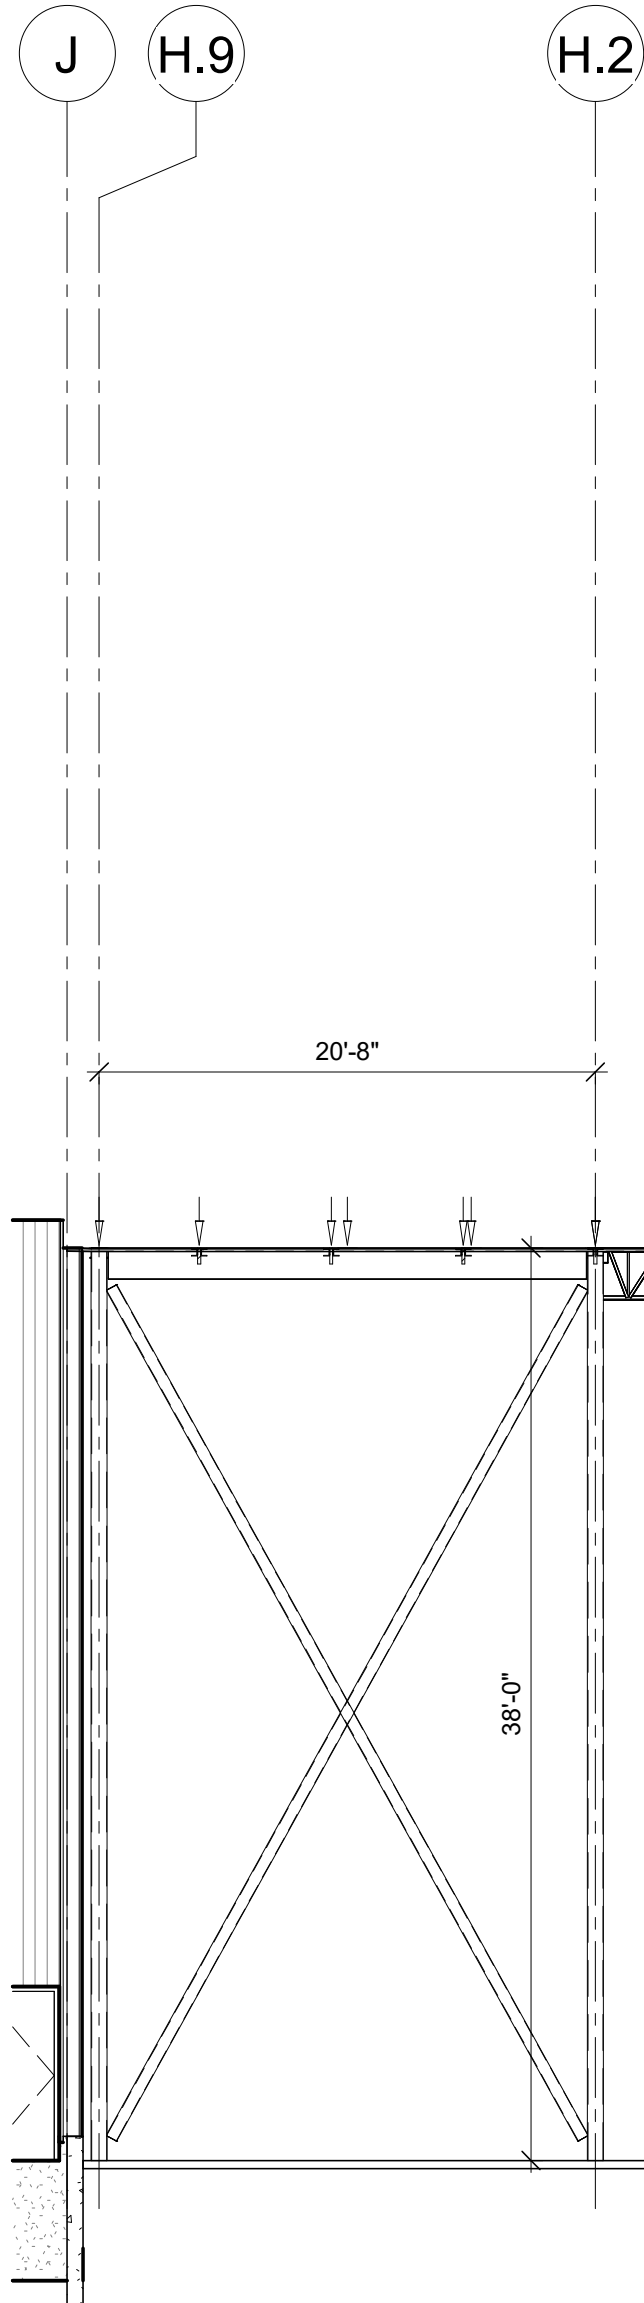

AXE 3.6 DE H.2@H.9
1/8" = 1'-0"

NOTE POUR LE CONTRACTEUR/ÉRECTEUR:
IL EST STRICTEMENT DÉFENDU DE MODIFIER, COPIER, REPRODUIRE OU DE DISTRIBUER CES DESSINS OU QUELQUES REPRÉSENTATIONS DE CES DESSINS, PAR TOUTES SOURCES DE MÉDIA INCLUANT ÉLECTRONIQUEMENT, SANS L'APPROBATION ÉCRITE DE GROUPE CANAM INC.

PRÉLIMINAIRE

NE DOIT PAS SERVIR À LA CONSTRUCTION

REVISION	DATE	DESCRIPTION	DESS	VER
----------	------	-------------	------	-----

DEVANT DE PROJET	-	-	-	-
------------------	---	---	---	---

DESSIN	CONÇU PAR	INGÉNIEUR OU PROJET	ÉCHELLE
DESSINÉ PAR	S.L.		Comme indiqué
VÉRIFIÉ PAR	INGÉNIEURS CONSEILS / ARCHITECTES	DATE (mm/aaaa)	07/05/2026

CLIENT:	USINAGE SERVITECH
---------	-------------------

**CANAM**

11505, 1re Avenue, bureau 500, Saint-Georges Beauce
Québec, Canada G5Y 7X3
Téléphone : (418) 228-8031
Sans frais : (877) 459-8049
www.canam.com

SCAUX PROFESSIONNEL

PROJET

USINE PRINCIPALE SERVITECH TROIS-RIVIÈRES, QC
--

TITRE
CROQUIS PRÉLIMINAIRE - ÉLÉVATIONS 2 DE 3

NUMÉRO CONTRAT	NUMÉRO DESSIN	DIVISION	REVISION
P2026-090	EsMx501a		

Initiales



Initiales



