CÉDULE DES FENÊTRES

Identifiant	Qté.	Description	Dimensions ext. cadre largeur X hauteur	Couleur du cadre	Remarques
F1	19	Fenêtre en aluminium fixe avec bris thermique et verre scellé + Low-E argon clair	6'-0" x 4'-0"	Cadre d'Aluminium (Blanc ext. et int.)	
F2	4	Fenêtre en aluminium fixe avec bris thermique et verre scellé + Low-E argon clair	4'-0" x 4'-0"	Cadre d'Aluminium (Blanc ext. et int.)	

CÉDULE DES PORTES


Identifiant	Qté.	Porte 18 ja. Dimensions	Remarques
P1	7	3'-0" x 7'-0"	<multiples>
P2	6	16'-0" x 16'-0"	CADRE OUVERTURE PORTE MONTANTE
P3	4	18'-0" x 16'-0"	CADRE OUVERTURE PORTE MONTANTE

Quincaillerie standard du fournisseur:
- Charnières : Stanley FBB179 4.5" x 4"
- Barre panique : Von Duprin 22 x 689 avec poignée extérieure 230L
- Cylindre permanent : Schlage 20001C 626
- Ferme-porte : LCN 1261 689
- Coupe-froid de tête et des montants : Unique 1650
- Coupe-froid du bas : Unique DS4
- Seuil : Voir la remarque dans la "Cédule de porte"


CÉDULE DES P.M. ET DES OUVERTURES

Total	Type	Tag	Commentaires
1	6'-0" x 7'-0"	OUV	OUVERTURE

Total général: 1

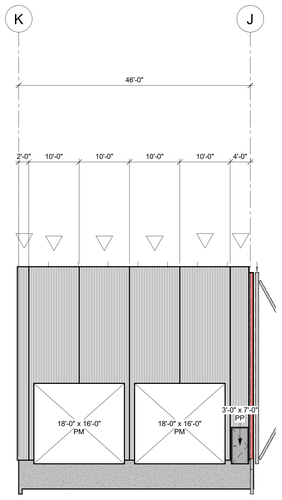


ÉLÉVATION AXE 3.6 (EST)
3/32" = 1'-0"

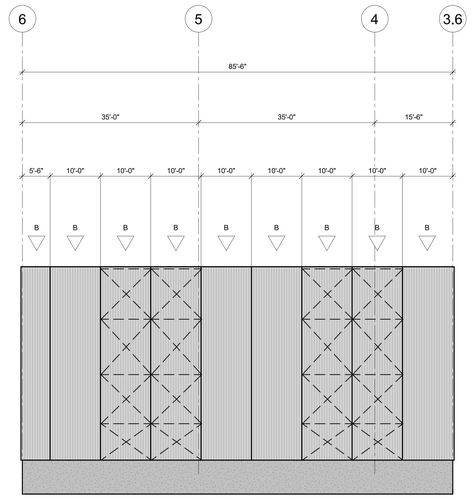


MUR 1 HEURE AU FEU

ÉLÉVATION AXE K (SUD)
3/32" = 1'-0"

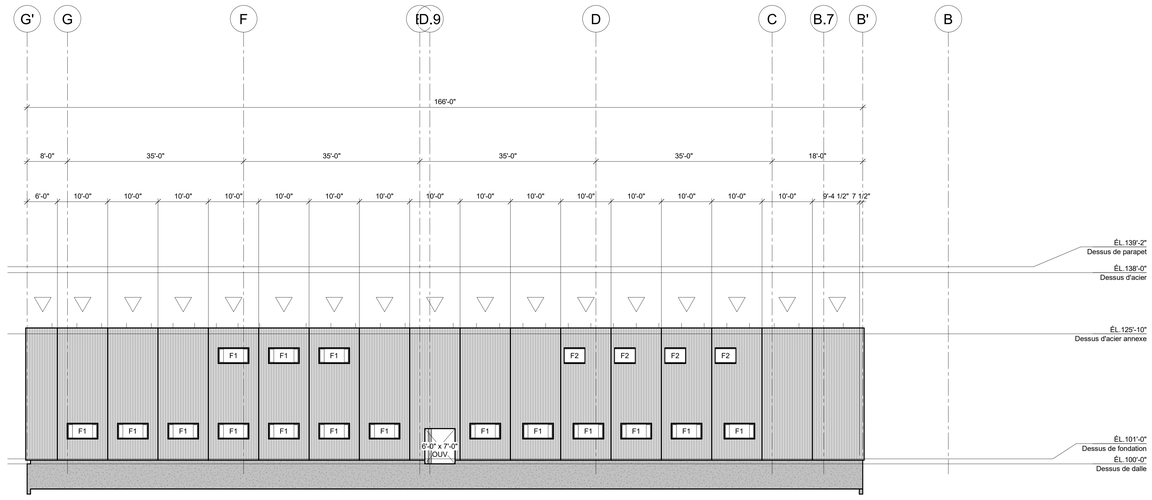

ÉLÉVATION AXE 1 (EST)
3/32" = 1'-0"

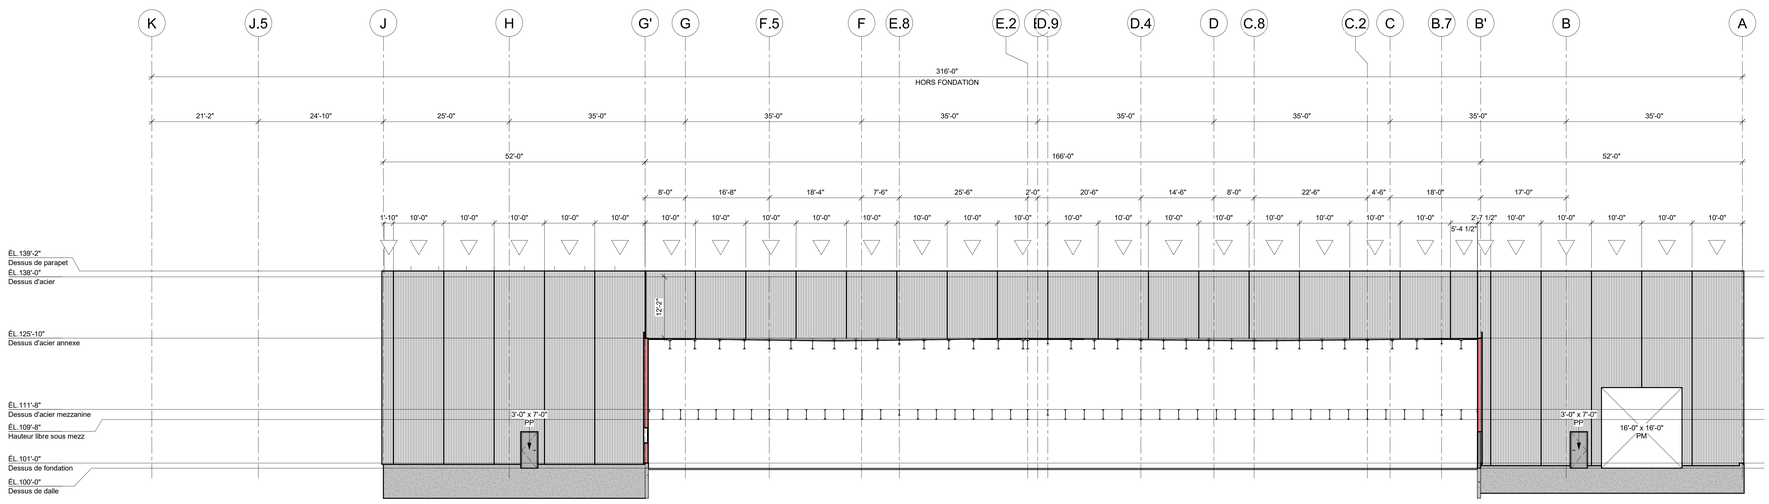

ÉLÉVATION AXE 2 (EST)
3/32" = 1'-0"

NOTE POUR LE CONTRACTEUR/ÉRECTEUR:

Il EST STRICTEMENT DÉFENDU DE MODIFIER, COPIER, REPRODUIRE OU DE DISTRIBUER CES DESSINS OU QUELQUES REPRÉSENTATIONS DE CES DESSINS, PAR TOUTES SOURCES DE MÉDIA INCLUANT ÉLECTRONIQUEMENT, SANS L'APPROBATION ÉCRITE DE GROUPE CANAM INC.

PRÉLIMINAIRE

NE DOIT PAS SERVIR À LA CONSTRUCTION

RÉVISION	DATE	DESCRIPTION	DESS.	VÉR.

GÉRANT DE PROJET

DESSIN:

DESSINÉ PAR	CONÇU PAR	INGÉNIEUR DU PROJET	ÉCHELLE:
S.L.			Comme indiqué
VÉRIFIÉ PAR	INGÉNIEURS CONSEILS / ARCHITECTES		DATE (j/mm/aaaa): 07/05/2026

CLIENT: USINAGE SERVITECH

CANAM
11505, 1re Avenue, bureau 500, Saint-Georges Beauce
Québec, Canada, G5Y 7X3
Téléphone : (418) 228-8031
Sans frais : (877) 469-6049
www.canam.com

SCEAU PROFESSIONNEL

PROJET

USINE PRINCIPALE SERVITECH
TROIS-RIVIÈRES, QC

TITRE

CROQUIS PRÉLIMINAIRE - ÉLÉVATION
3 DE 3, COUPE DE MUR ET CÉDULES

Initiales

NUMÉRO CONTRAT	NUMÉRO DESSIN	DIVISION	RÉVISION
P2026-090	EsMx502		