




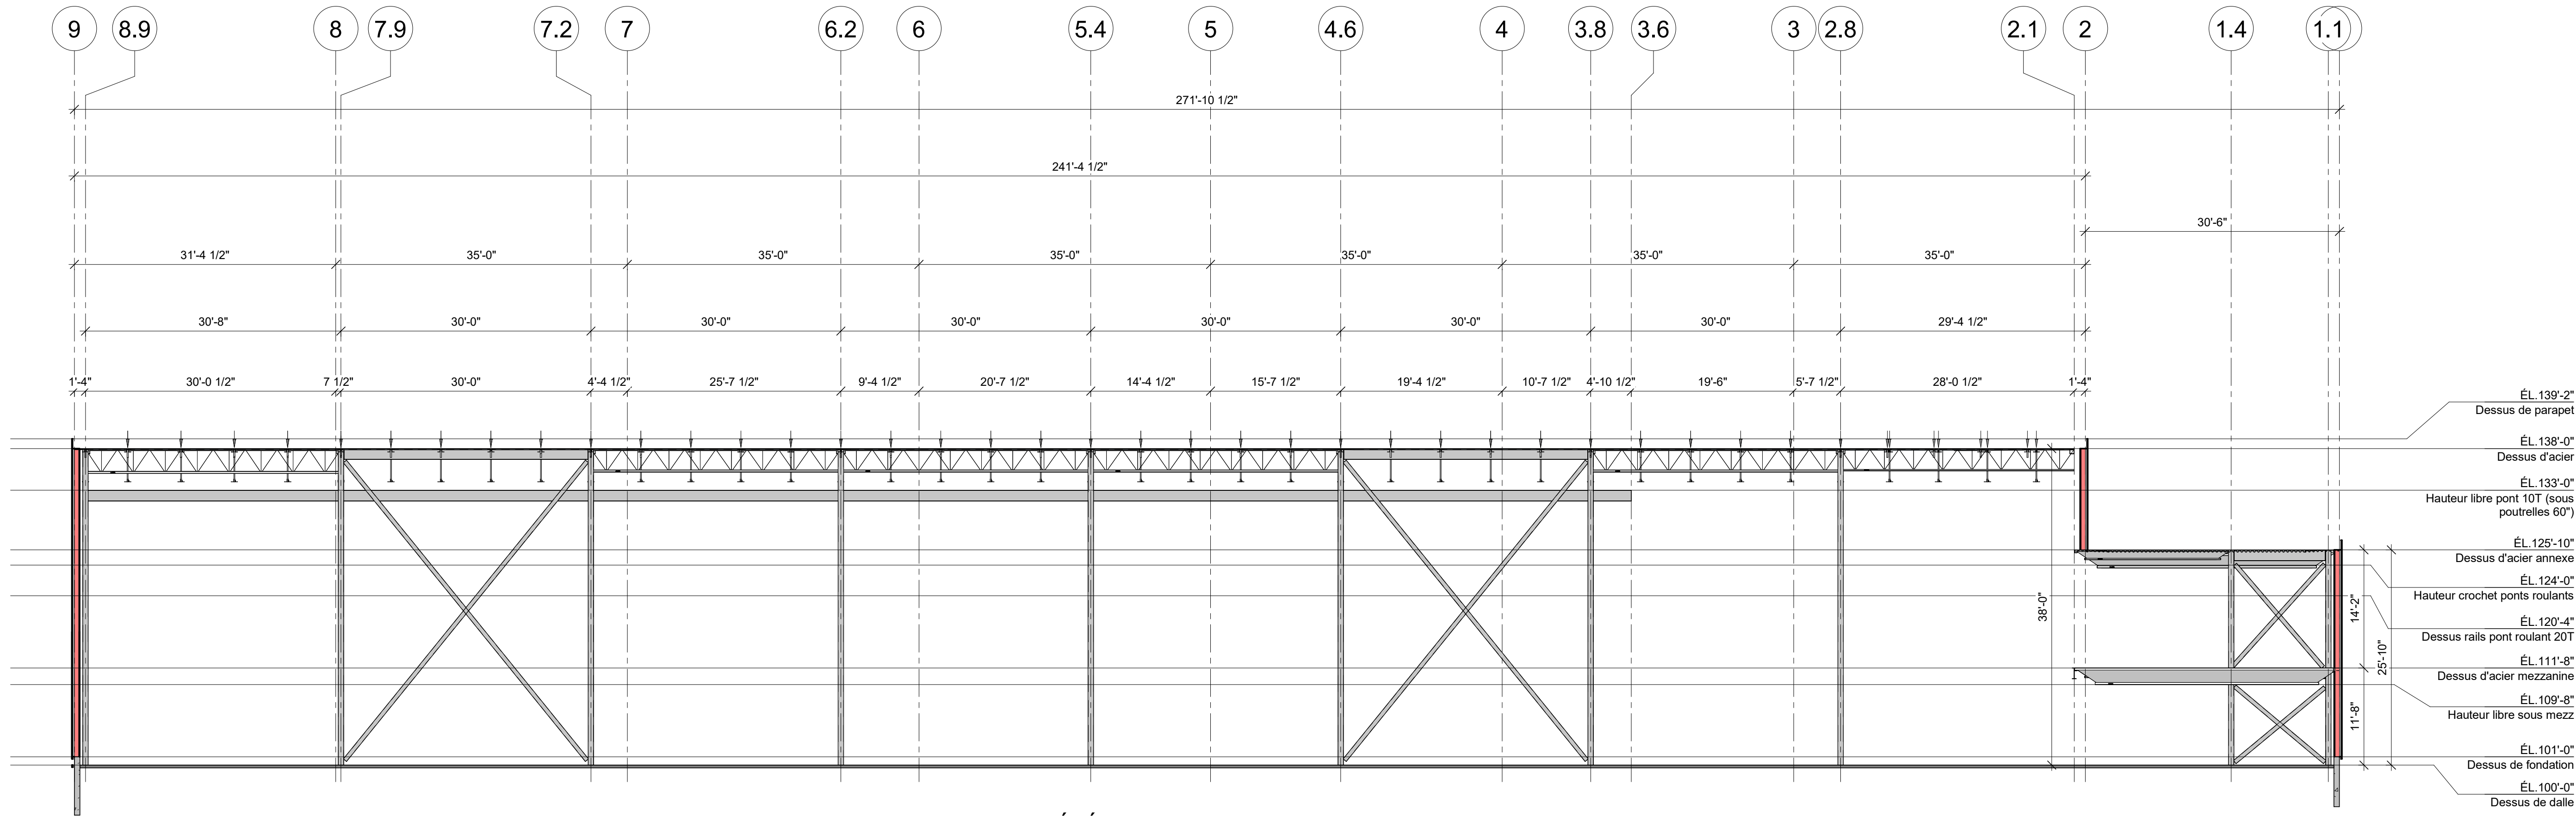


ÉLÉVATION AXE B.8 (STRUCTURE)(SUD)
3/32" = 1'-0"

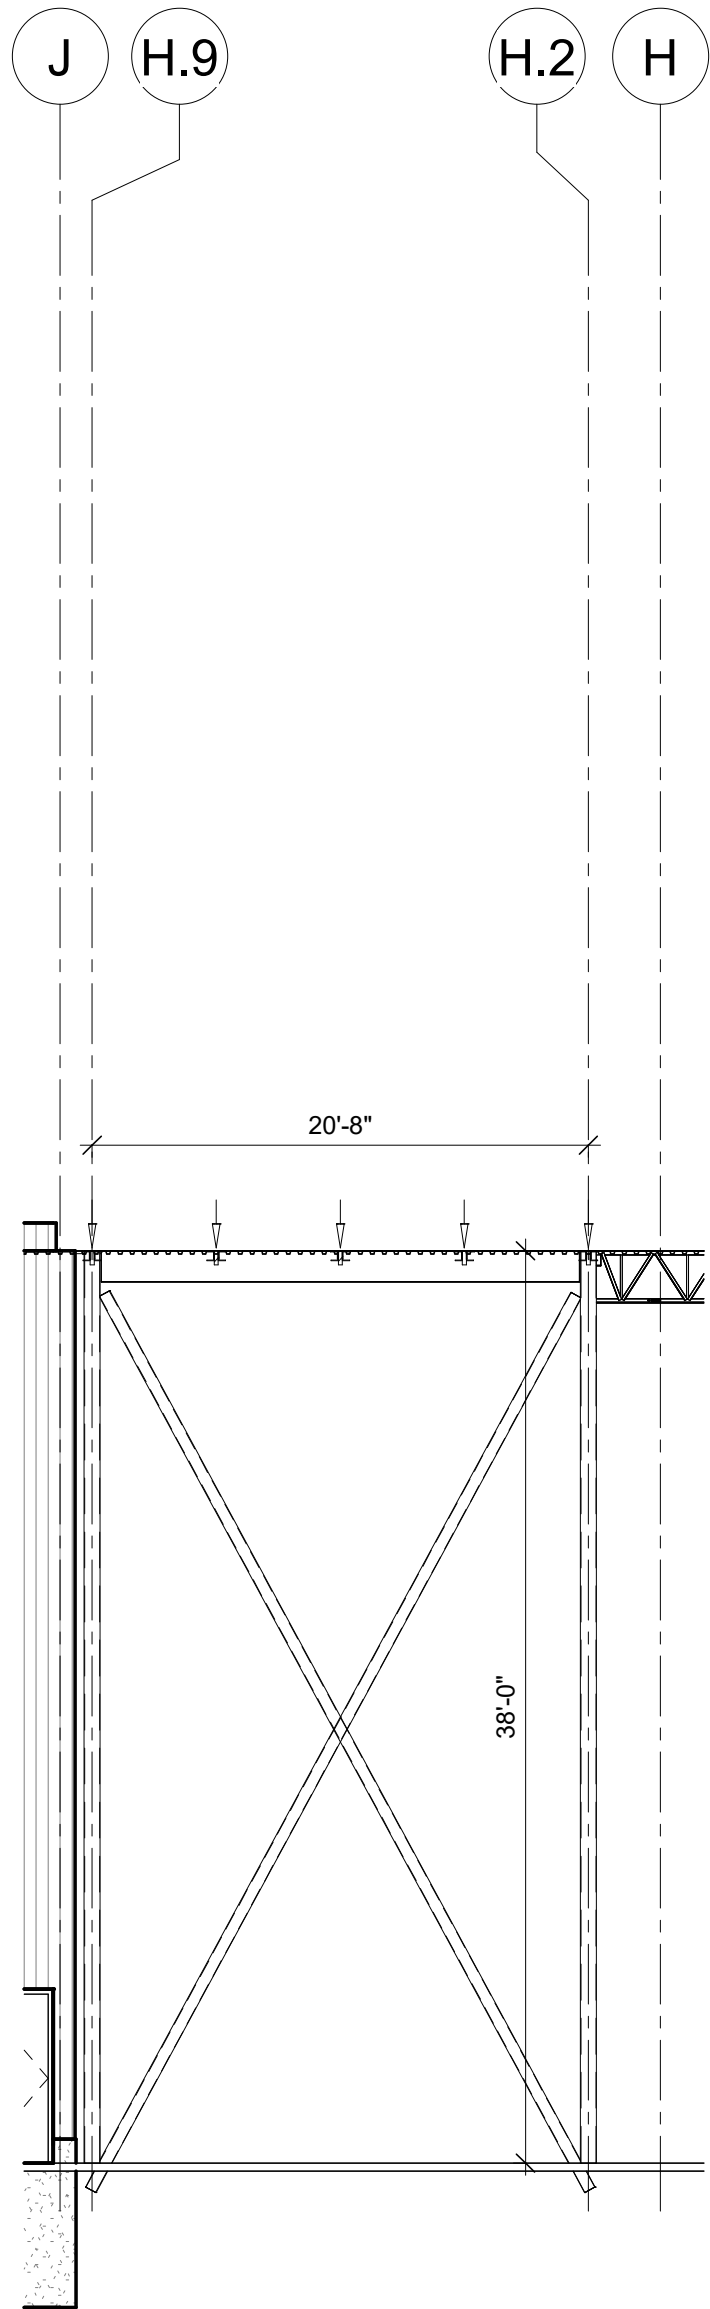

AXE 6 DE H.2@H.9
1/8" = 1'-0"

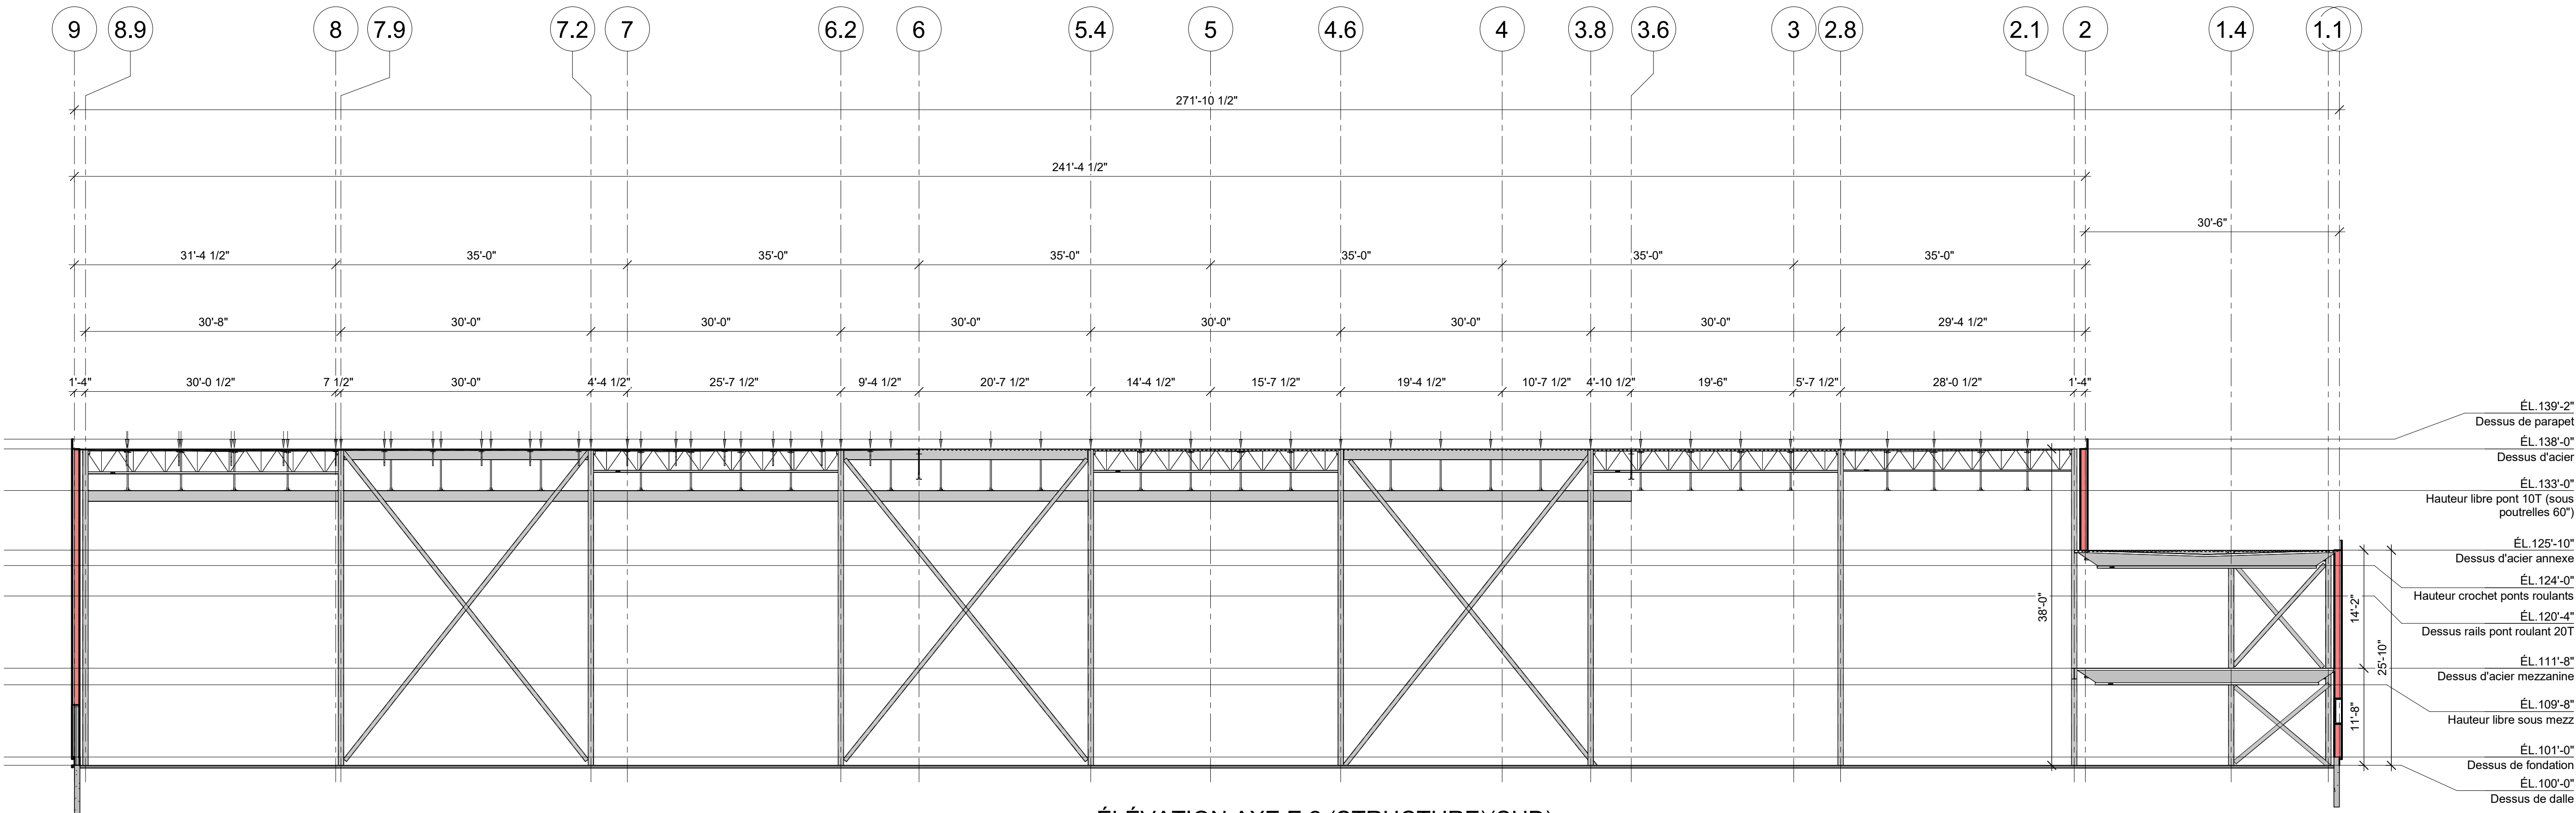

ÉLÉVATION AXE E.2 (STRUCTURE)(SUD)
3/32" = 1'-0"

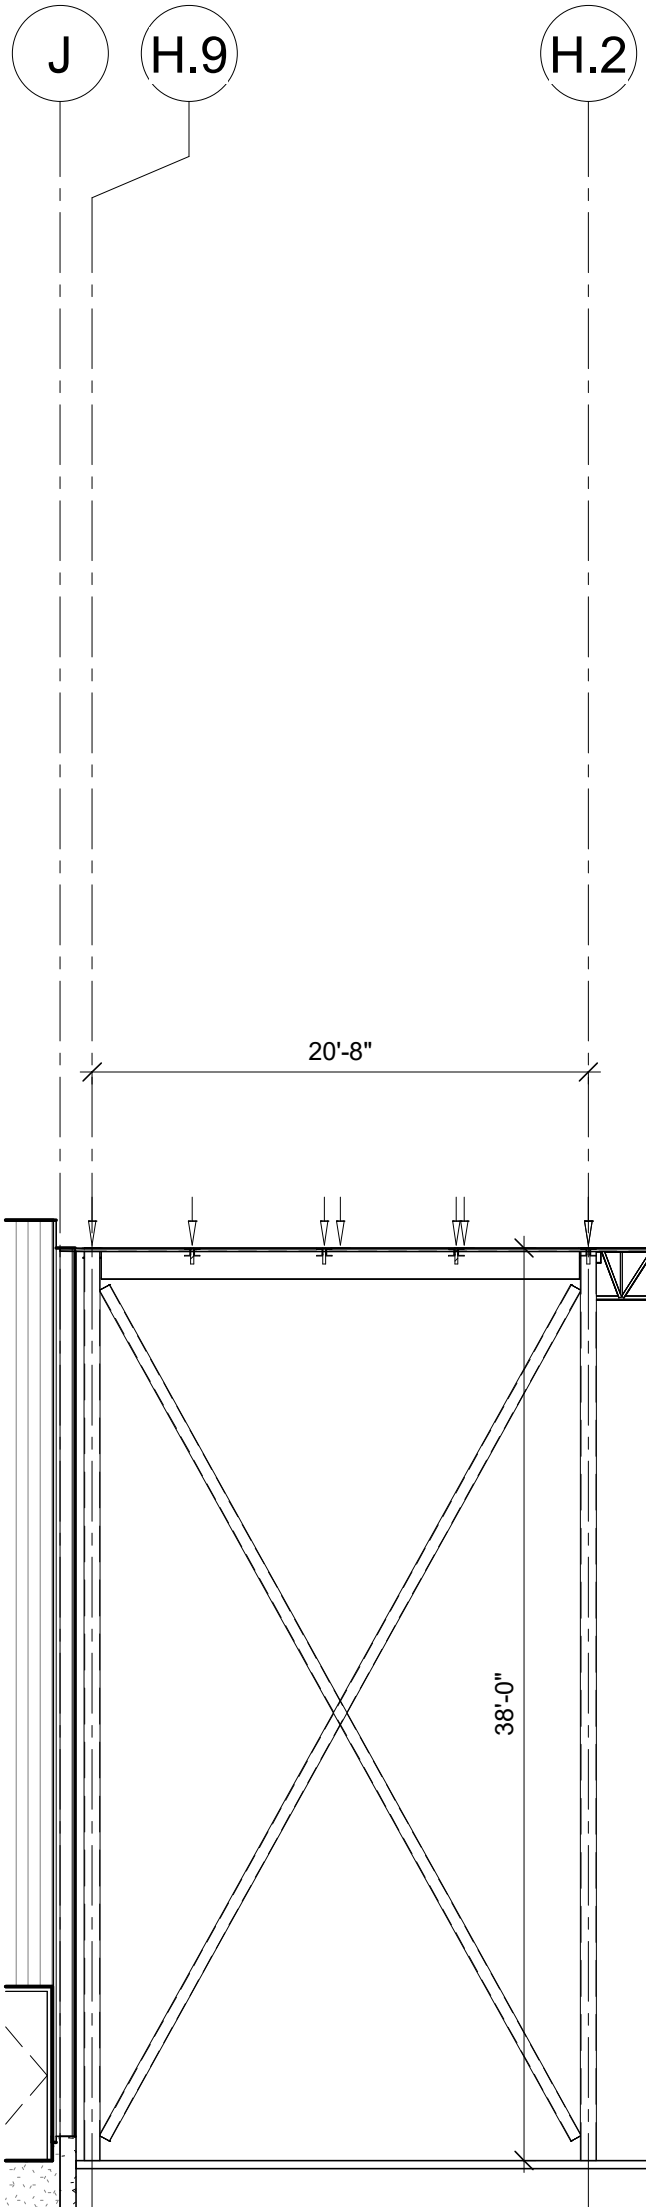

AXE 3.6 DE H.2@H.9
1/8" = 1'-0"

NOTE POUR LE CONTRACTEUR/ÉRECTEUR:
IL EST STRICTEMENT DÉFENDU DE MODIFIER, COPIER, REPRODUIRE OU DE DISTRIBUER CES DESSINS OU QUELQUES REPRÉSENTATIONS DE CES DESSINS, PAR TOUTES SOURCES DE MÉDIA INCLUANT ÉLECTRONIQUEMENT, SANS L'APPROBATION ÉCRITE DE GROUPE CANAM INC.

PRÉLIMINAIRE

NE DOIT PAS SERVIR À LA CONSTRUCTION

REVISION	DATE	DESCRIPTION	DESS	VER
----------	------	-------------	------	-----

DEVANT DE PROJET	-	-	-	-
------------------	---	---	---	---

DESSIN	CONÇU PAR	INGÉNIEUR OU PROJET	ÉCHELLE
DESSINÉ PAR	S.L.		Comme indiqué
VÉRIFIÉ PAR	INGÉNIEURS CONSEILS / ARCHITECTES	DATE (mm/aaaa)	07/05/2026

CLIENT:	USINAGE SERVITECH
---------	-------------------

 **CANAM**
11505, 1re Avenue, bureau 500, Saint-Georges Beauce
Québec, Canada G5Y 7X3
Téléphone : (418) 228-8031
Sans frais : (877) 459-8049
www.canam.com

SCAUX PROFESSIONNEL

PROJET

USINE PRINCIPALE SERVITECH TROIS-RIVIÈRES, QC
--

TITRE

CROQUIS PRÉLIMINAIRE - ÉLÉVATIONS 2 DE 3

NUMÉRO CONTRAT	NUMÉRO DESSIN	DIVISION	REVISION
P2026-090	EsMx501a		

Initiales



Initiales

