


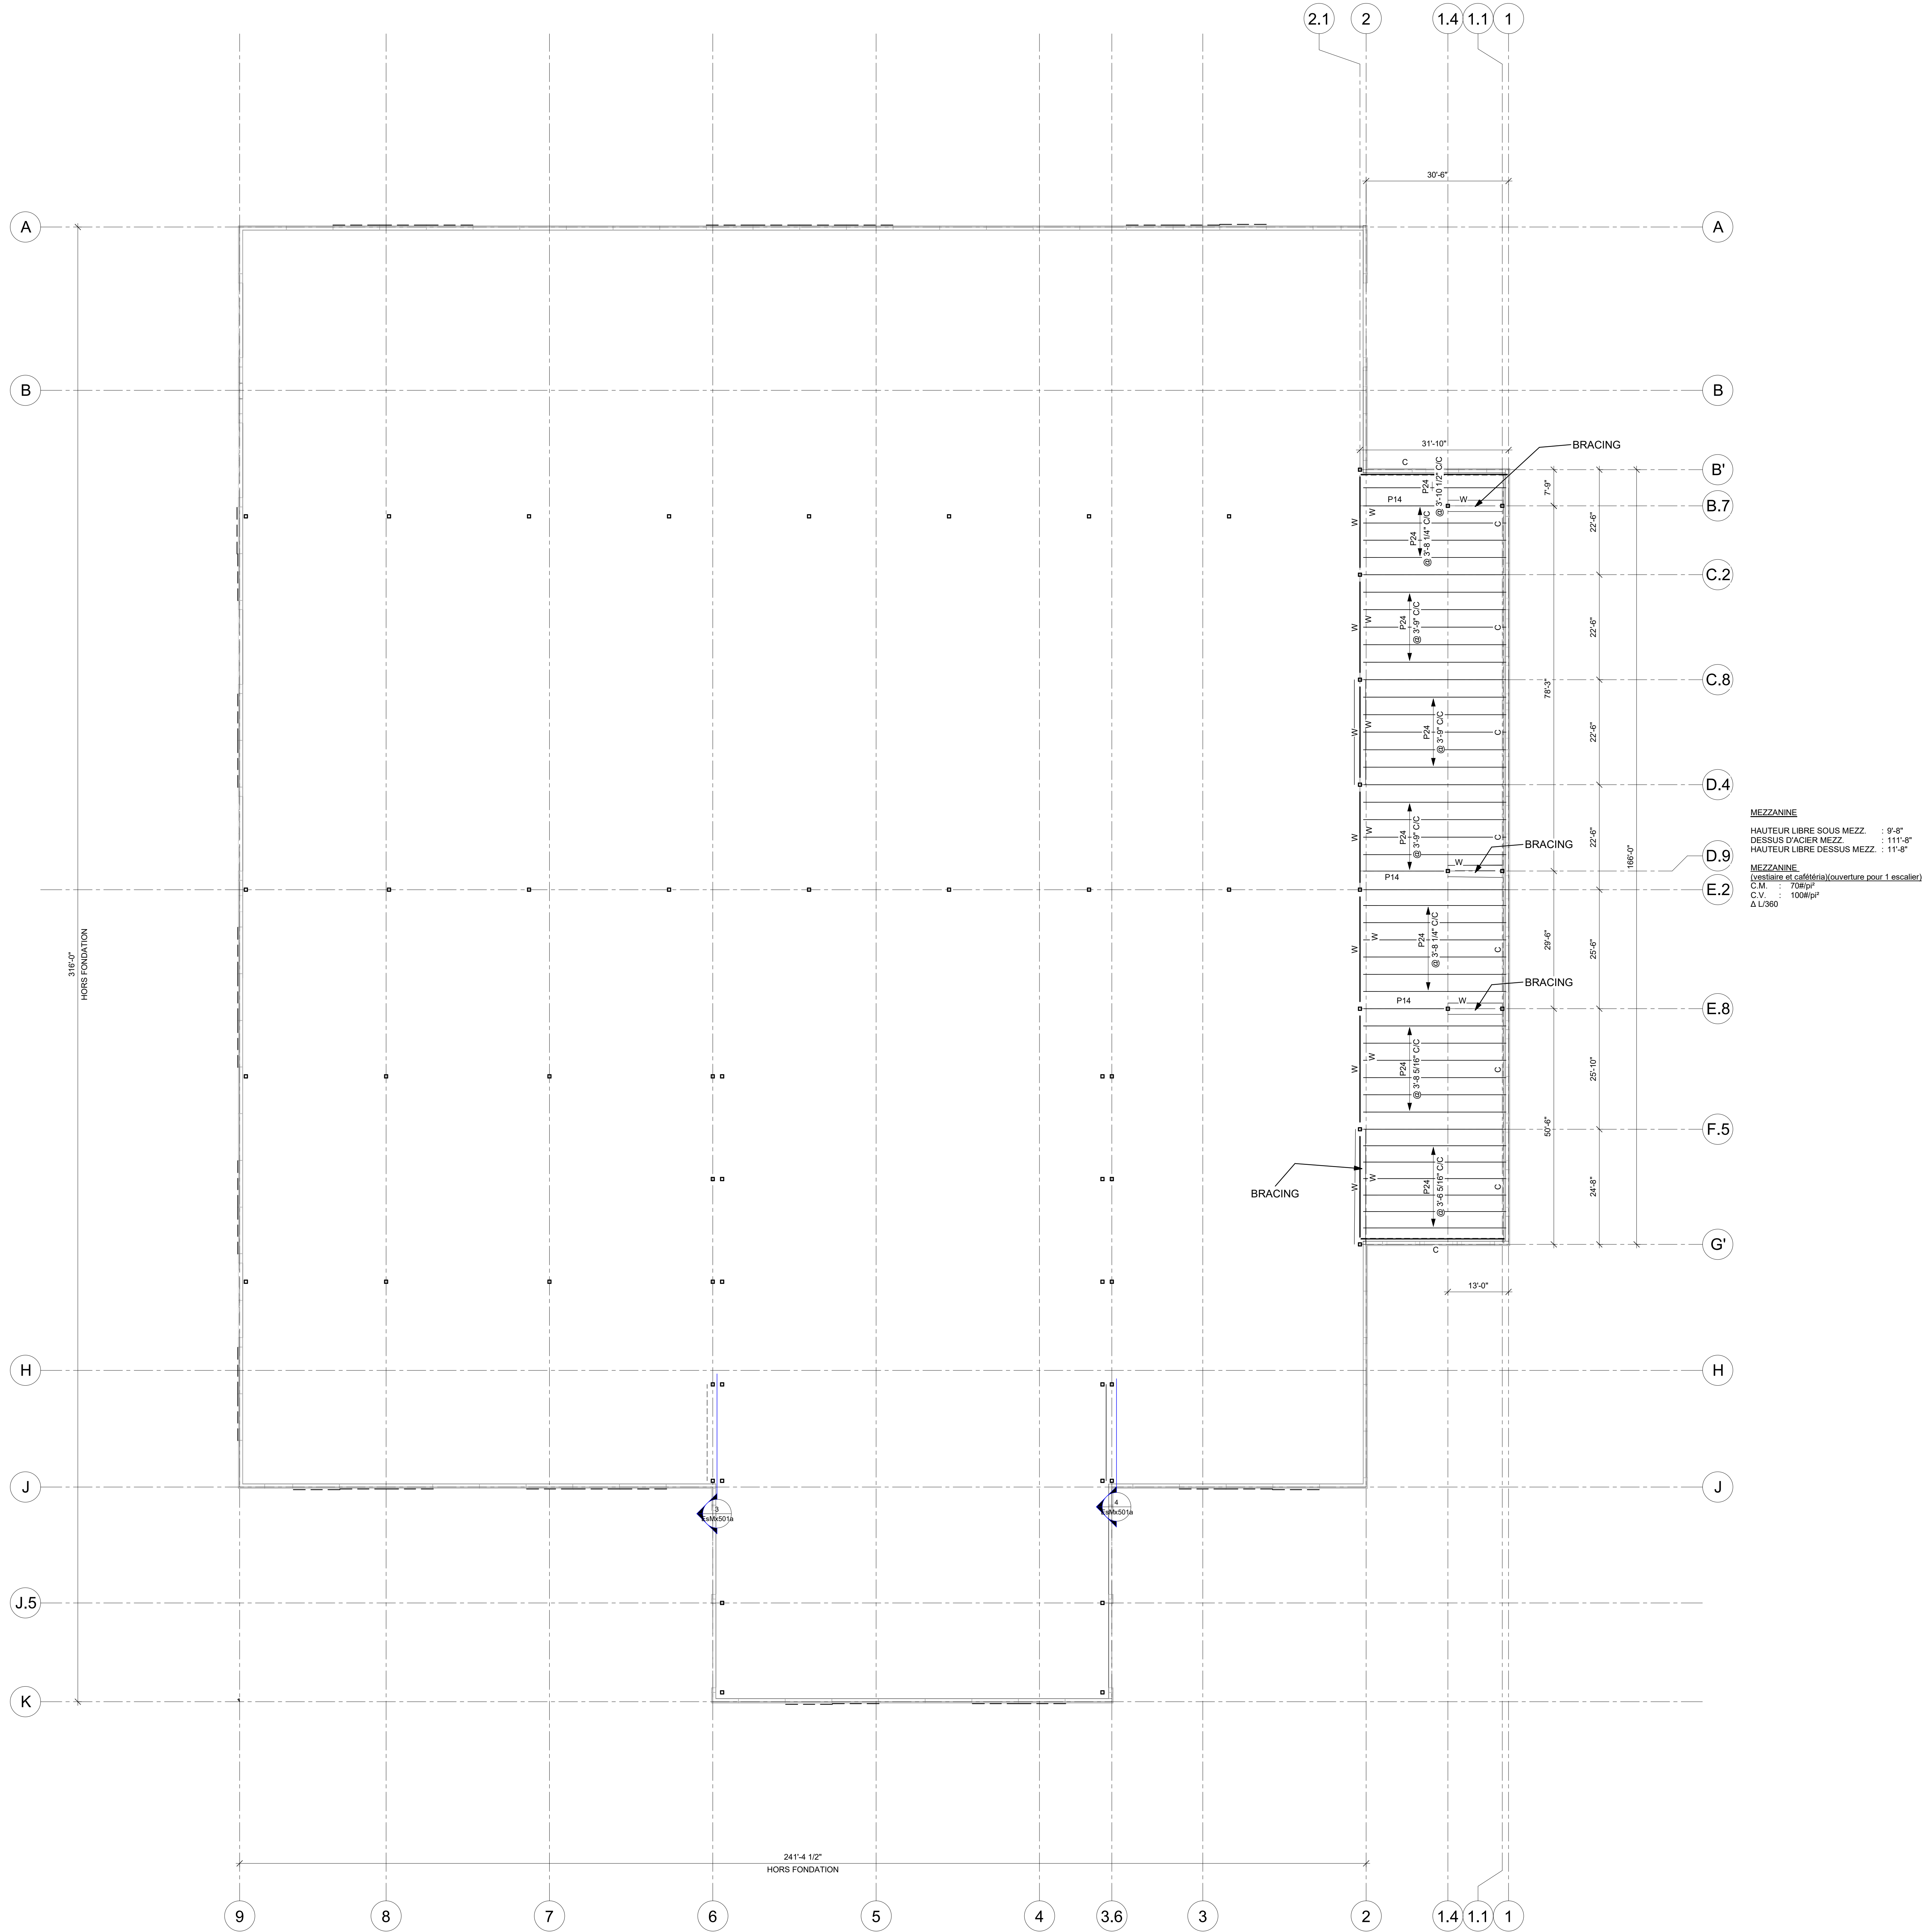

PLAN DE MEZZANINE
1:156

NOTE POUR LE CONTRACTEUR/ÉRECTEUR:
IL EST STRICTEMENT DÉFENDU DE MODIFIER, COPIER, REPRODUIRE OU DE DISTRIBUER CES DESSINS OU QUELQUES REPRÉSENTATIONS DE CES DESSINS, PAR TOUTES SOURCES DE MÉDIA INCLUANT ÉLECTRONIQUEMENT, SANS L'APPROBATION ÉCRITE DE GROUPE CANAM INC.

PRÉLIMINAIRE

NE DOIT PAS SERVIR À LA
CONSTRUCTION

REVISION	DATE	DESCRIPTION	DESS	VER
----------	------	-------------	------	-----

GERANT DE PROJET	-
-	-
-	-
-	-

DESSIN

DESSINÉ PAR	CONÇU PAR	INGÉNIEUR DU PROJET	ÉCHELLE:
-------------	-----------	---------------------	----------

VERIFIÉ PAR	INGÉNIEURS CONSEILS / ARCHITECTES	DATE (mm/aaaa)
-------------	-----------------------------------	----------------

CLIENT: USINAGE SERVITECH

CANAM

11505, 1^{re} Avenue, bureau 500, Saint-Georges Beauce
Québec, Canada G5Y 7X5
Téléphone : (418) 228-8031
Sans frais : (877) 459-8049
www.canam.com

SCAUX PROFESSIONNEL

PROJET

USINE PRINCIPALE SERVITECH
TROIS-RIVIÈRES, QC

TITRE

CROQUIS PRÉLIMINAIRE - PLAN DE MEZZANINE

NUMÉRO CONTRAT

P2026-090

NUMÉRO DESSIN

EsMx201

DIVISION

REVISION

Initiales

Signature