




NORD POUR
L'ÉRECTION

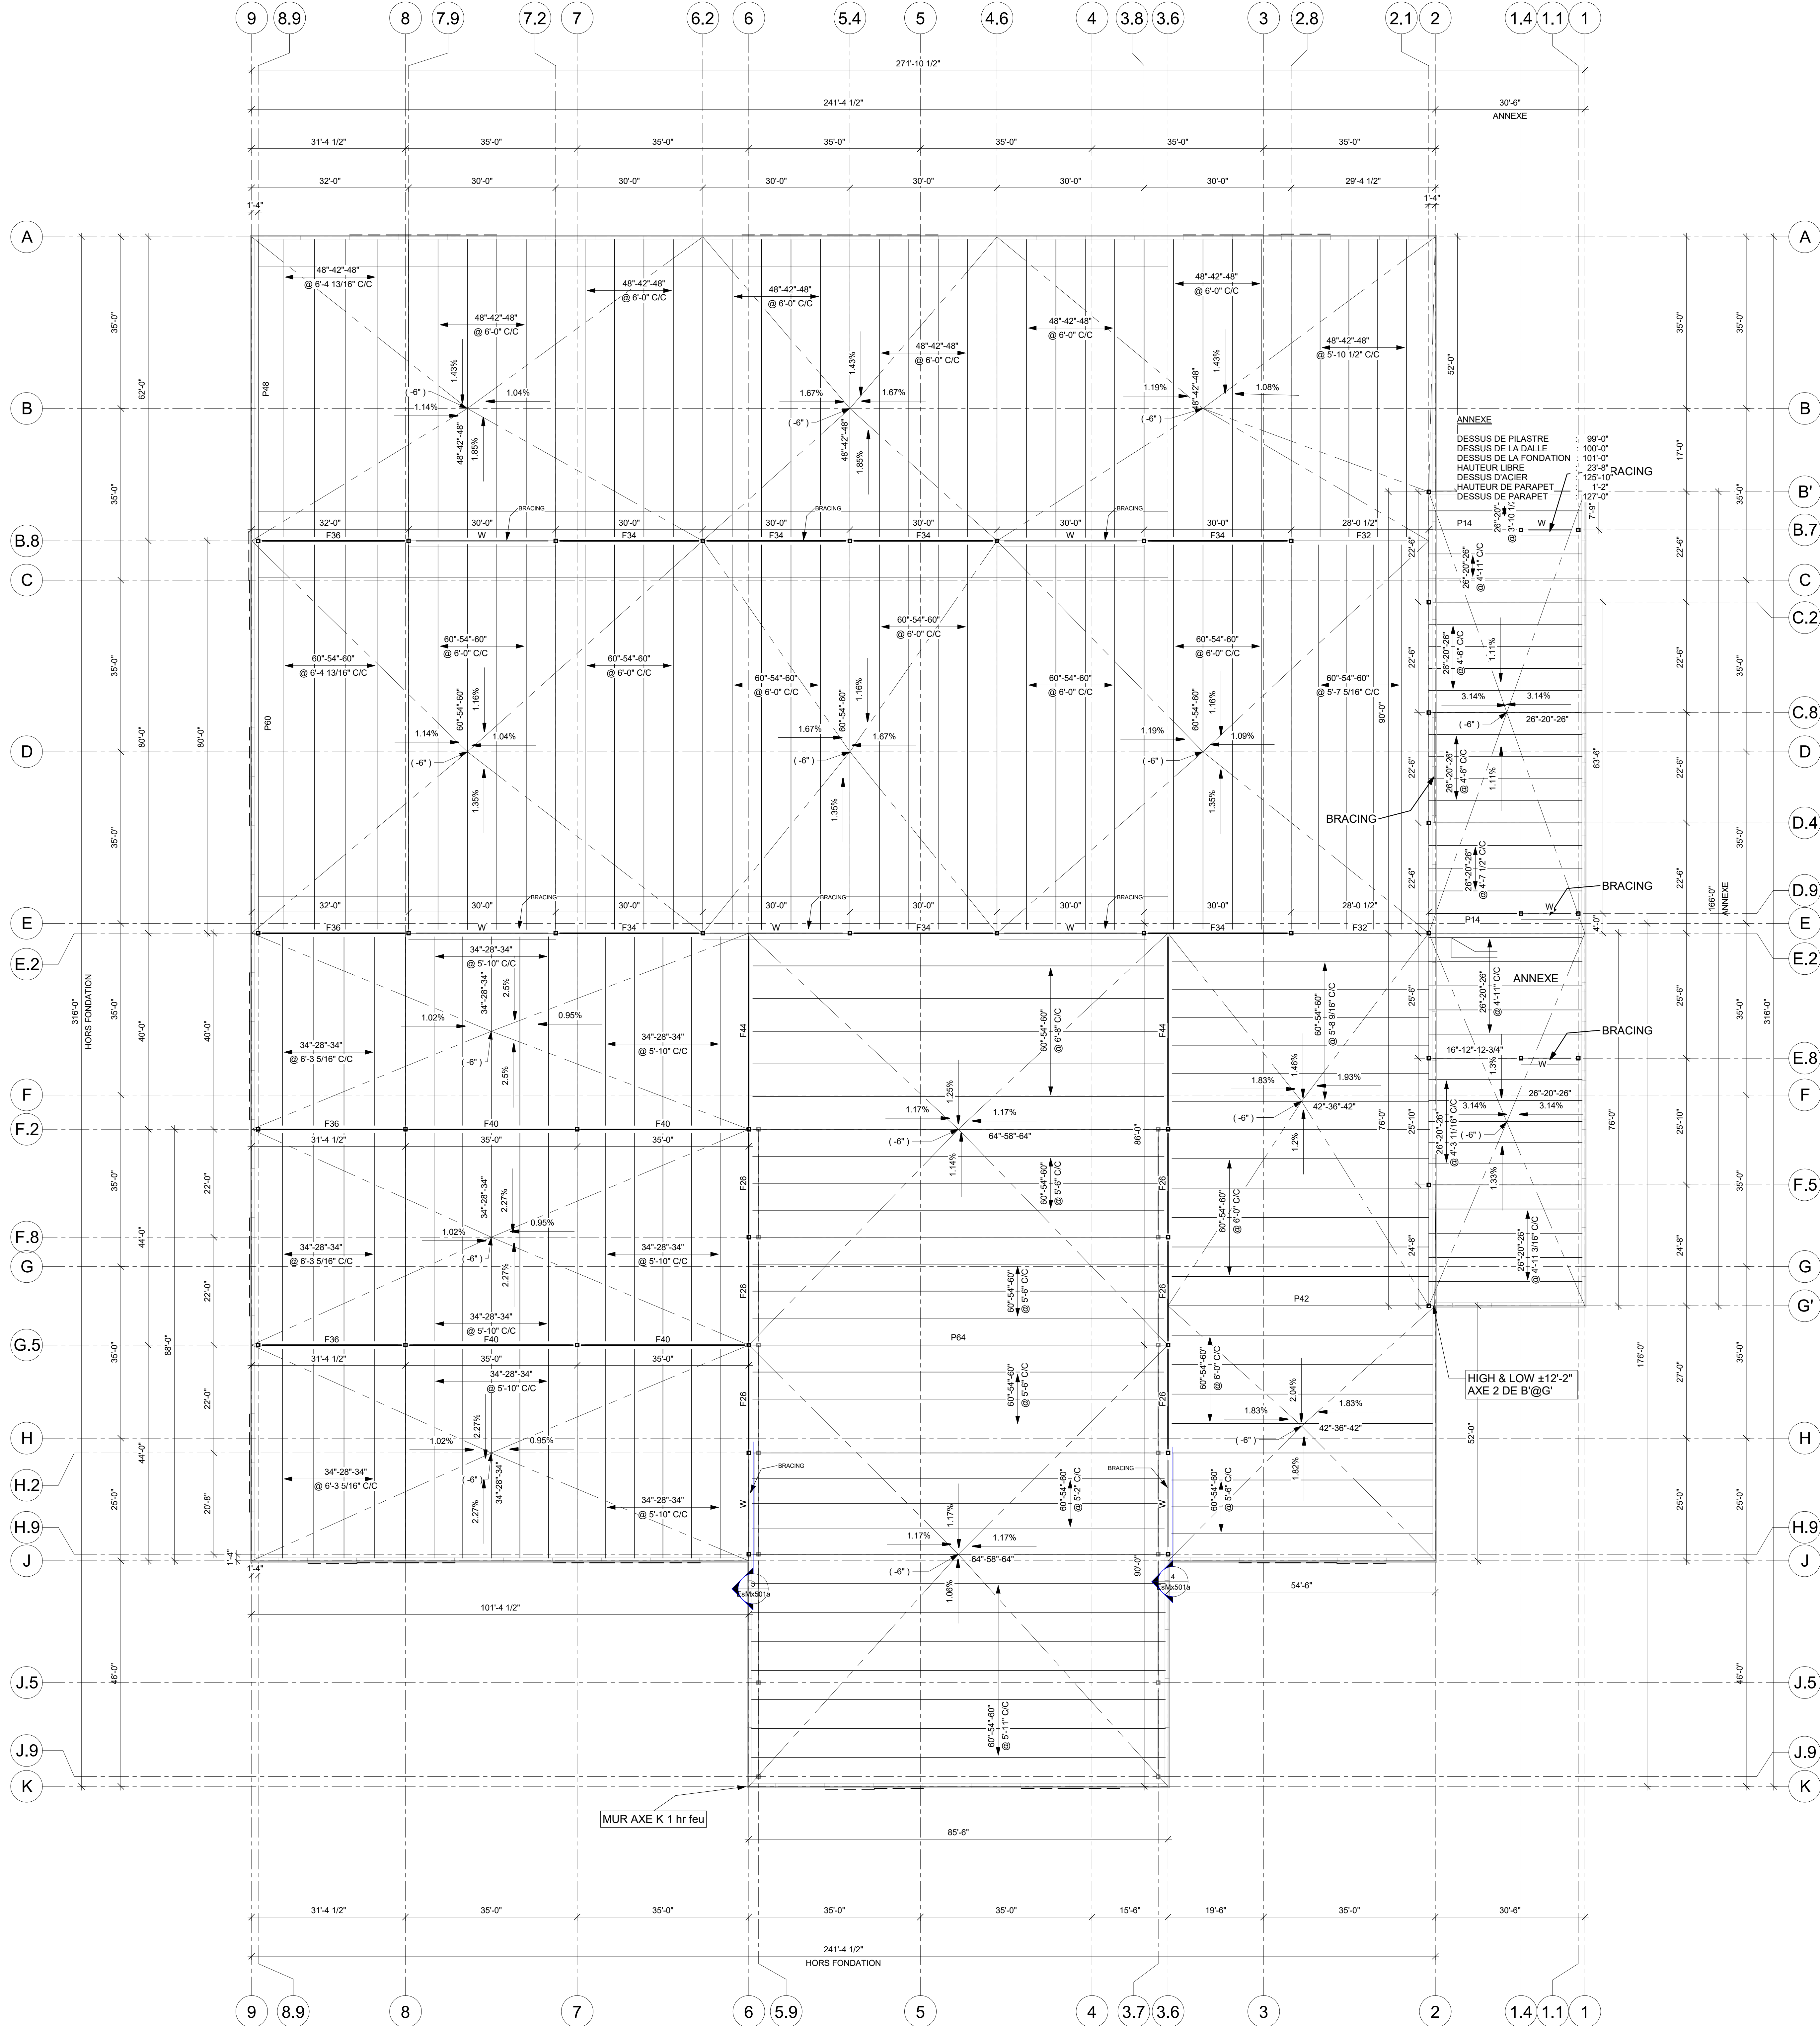

PLAN DE TOIT

1:156


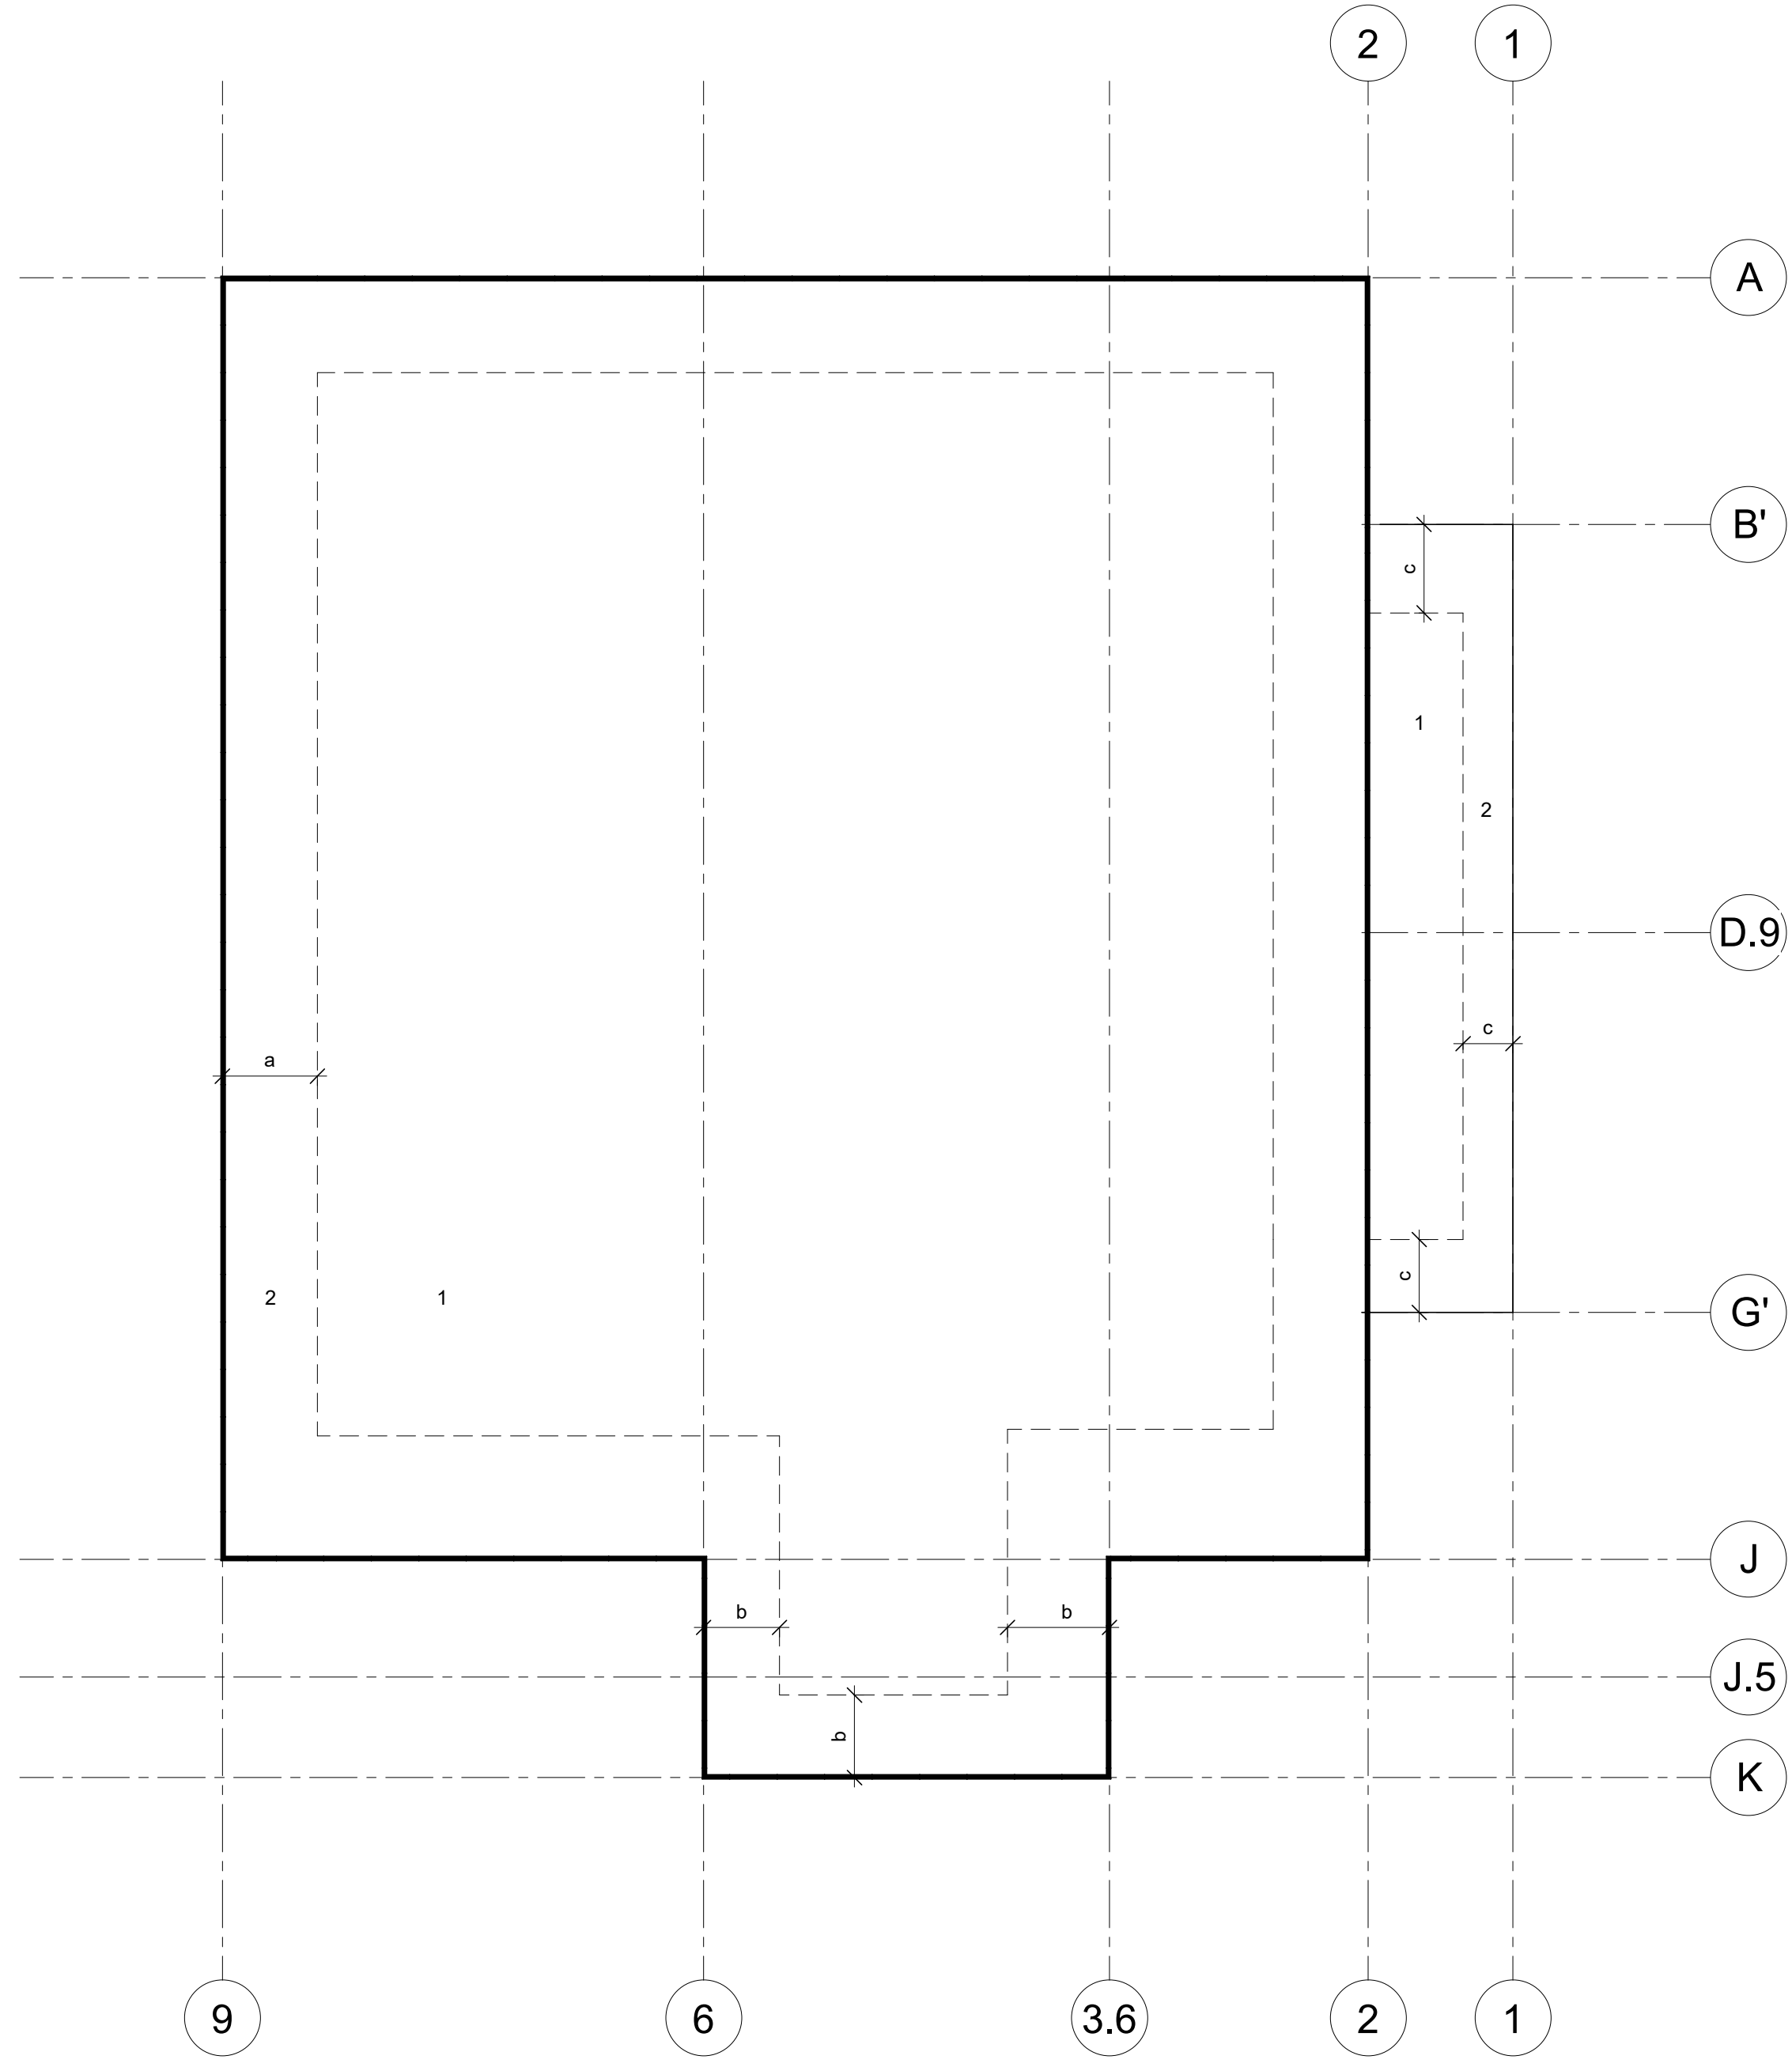


DIAGRAMME DE SOULÈVEMENT BRUT (NON PONDERÉ)

PRESSION POSITIVE DU VENT
(NON PONDERÉE) : +10.1Wp
ZONE 1 : -18.7Wp
ZONE 2 : -23.4Wp
a : 15'-0"
b : 9'-0"
c : 4'-0"

ACCUMULATION DE NEIGE

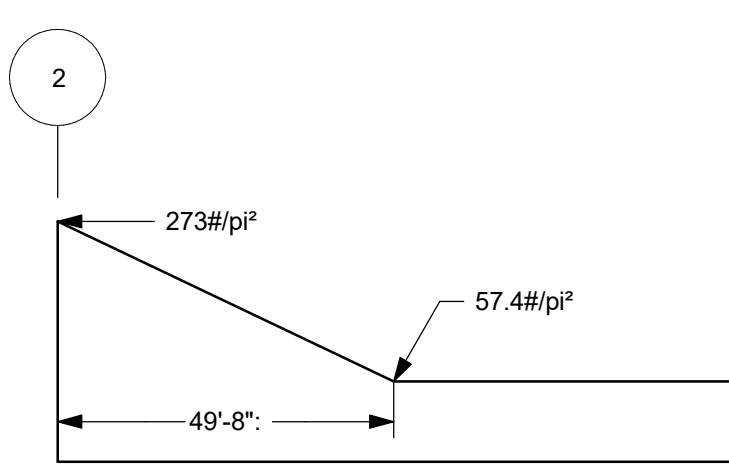

NOTE POUR LE CONTRACTEUR/ÉRECTEUR :

IL EST STRICTEMENT DEFENDU DE MODIFIER, COPIER, REPRODUIRE OU DE DISTRIBUER CES DESSINS OU QUELQUES REPRÉSENTATIONS DE CES DESSINS, PAR TOUTES SOURCES DE MÉDIA INCLUANT ÉLECTRONIQUEMENT, SANS L'APPROBATION ÉCRITE DE GROUPE CANAM INC.

TOIT

DESSUS DE PILASTRE : 99'-0"
DESSUS DE LA DALLE : 100'-0"
DESSUS DE LA FONDATION : 101'-0"
HAUTEUR LIBRE : 33'-0"
DESSUS STAGER : 138'-0"
HAUTEUR DE PARAPET : 1'-2"
DESSUS DE PARAPET : 139'-2"

Système (Sol de classe D assumé)

S_s : 1.0
 $S_s(0.2)$: 0.569
 $S_s(0.5)$: 0.516
 $S_s(1.0)$: 0.316
 $S_s(2.0)$: 0.194
 $S_s(5.0)$: 0.0434
 $S_s(10.0)$: 0.0137
PGA : 0.329
PCV : 0.361

CHARGES :

- Charge morte au toit (excluant charge collatérale) : lbs/p²
- Charge collatérale : lbs/p² (incluant éclairage étou mécanique et gicleurs plus petite que 4" de diamètre)
- Charge de neige au toit : 57.4 lbs/p²
- Charge vive au toit : 0 lbs/p²
- Charge de vent q 1/50 : 9.0 lbs/p²
- Charge de neige au sol : $S_s = 58.5$ lbs/p²
- Catégorie de risque : normal
- Coefficient de surcharge de neige : $C_s = 0.84$
- Coefficient de vent : $C_w = 1.0$

• Code Applicable : Code National du Bâtiment du Canada
Code du bâtiment du Québec, dernières éditions adoptées
Code de Pratique Standard ICCA.

• Type de sol assumé : classe D

• NOTE :
1. Si toutefois la catégorie d'emplacement devient E ou F selon le rapport géotechnique, le concept structural préliminaire (localisation et géométrie des contreventements, etc.) devra être validé et coordonné par l'ingénieur de Canam.

PRÉLIMINAIRE

NE DOIT PAS SERVIR À LA CONSTRUCTION

REVISION	DATE	DESCRIPTION	DESS	VER
1		DESSIN DE PROJET	-	-
2			-	-
3			-	-
4			-	-
5			-	-

DESSIN :

DESSINÉ PAR : S.L.	CONÇU PAR :	INGÉNIEUR DU PROJET :	ÉCHELLE : Comme indiqué
VERIFIÉ PAR :	INGÉNIEURS CONSEILS / ARCHITECTES :	DATE (général) :	07/05/2026

CLIENT : USINAGE SERVITECH

CANAM

11505, 1re Avenue, bureau 500, Saint-Georges Beauce
Québec, Canada G5Y 7X3
Téléphone : (418) 228-8031
Sans frais : (877) 469-8049
www.canam.com

SCAUX PROFESSIONNEL :

PROJET :

USINE PRINCIPALE SERVITECH
TROIS-RIVIÈRES, QC

TITRE :

CROQUIS PRÉLIMINAIRE - PLAN DE TOIT

NUMÉRO CONTRAT	NUMÉRO DESSIN	DIVISION	REVISION
P2026-090	EsMx401		

Initiales :