
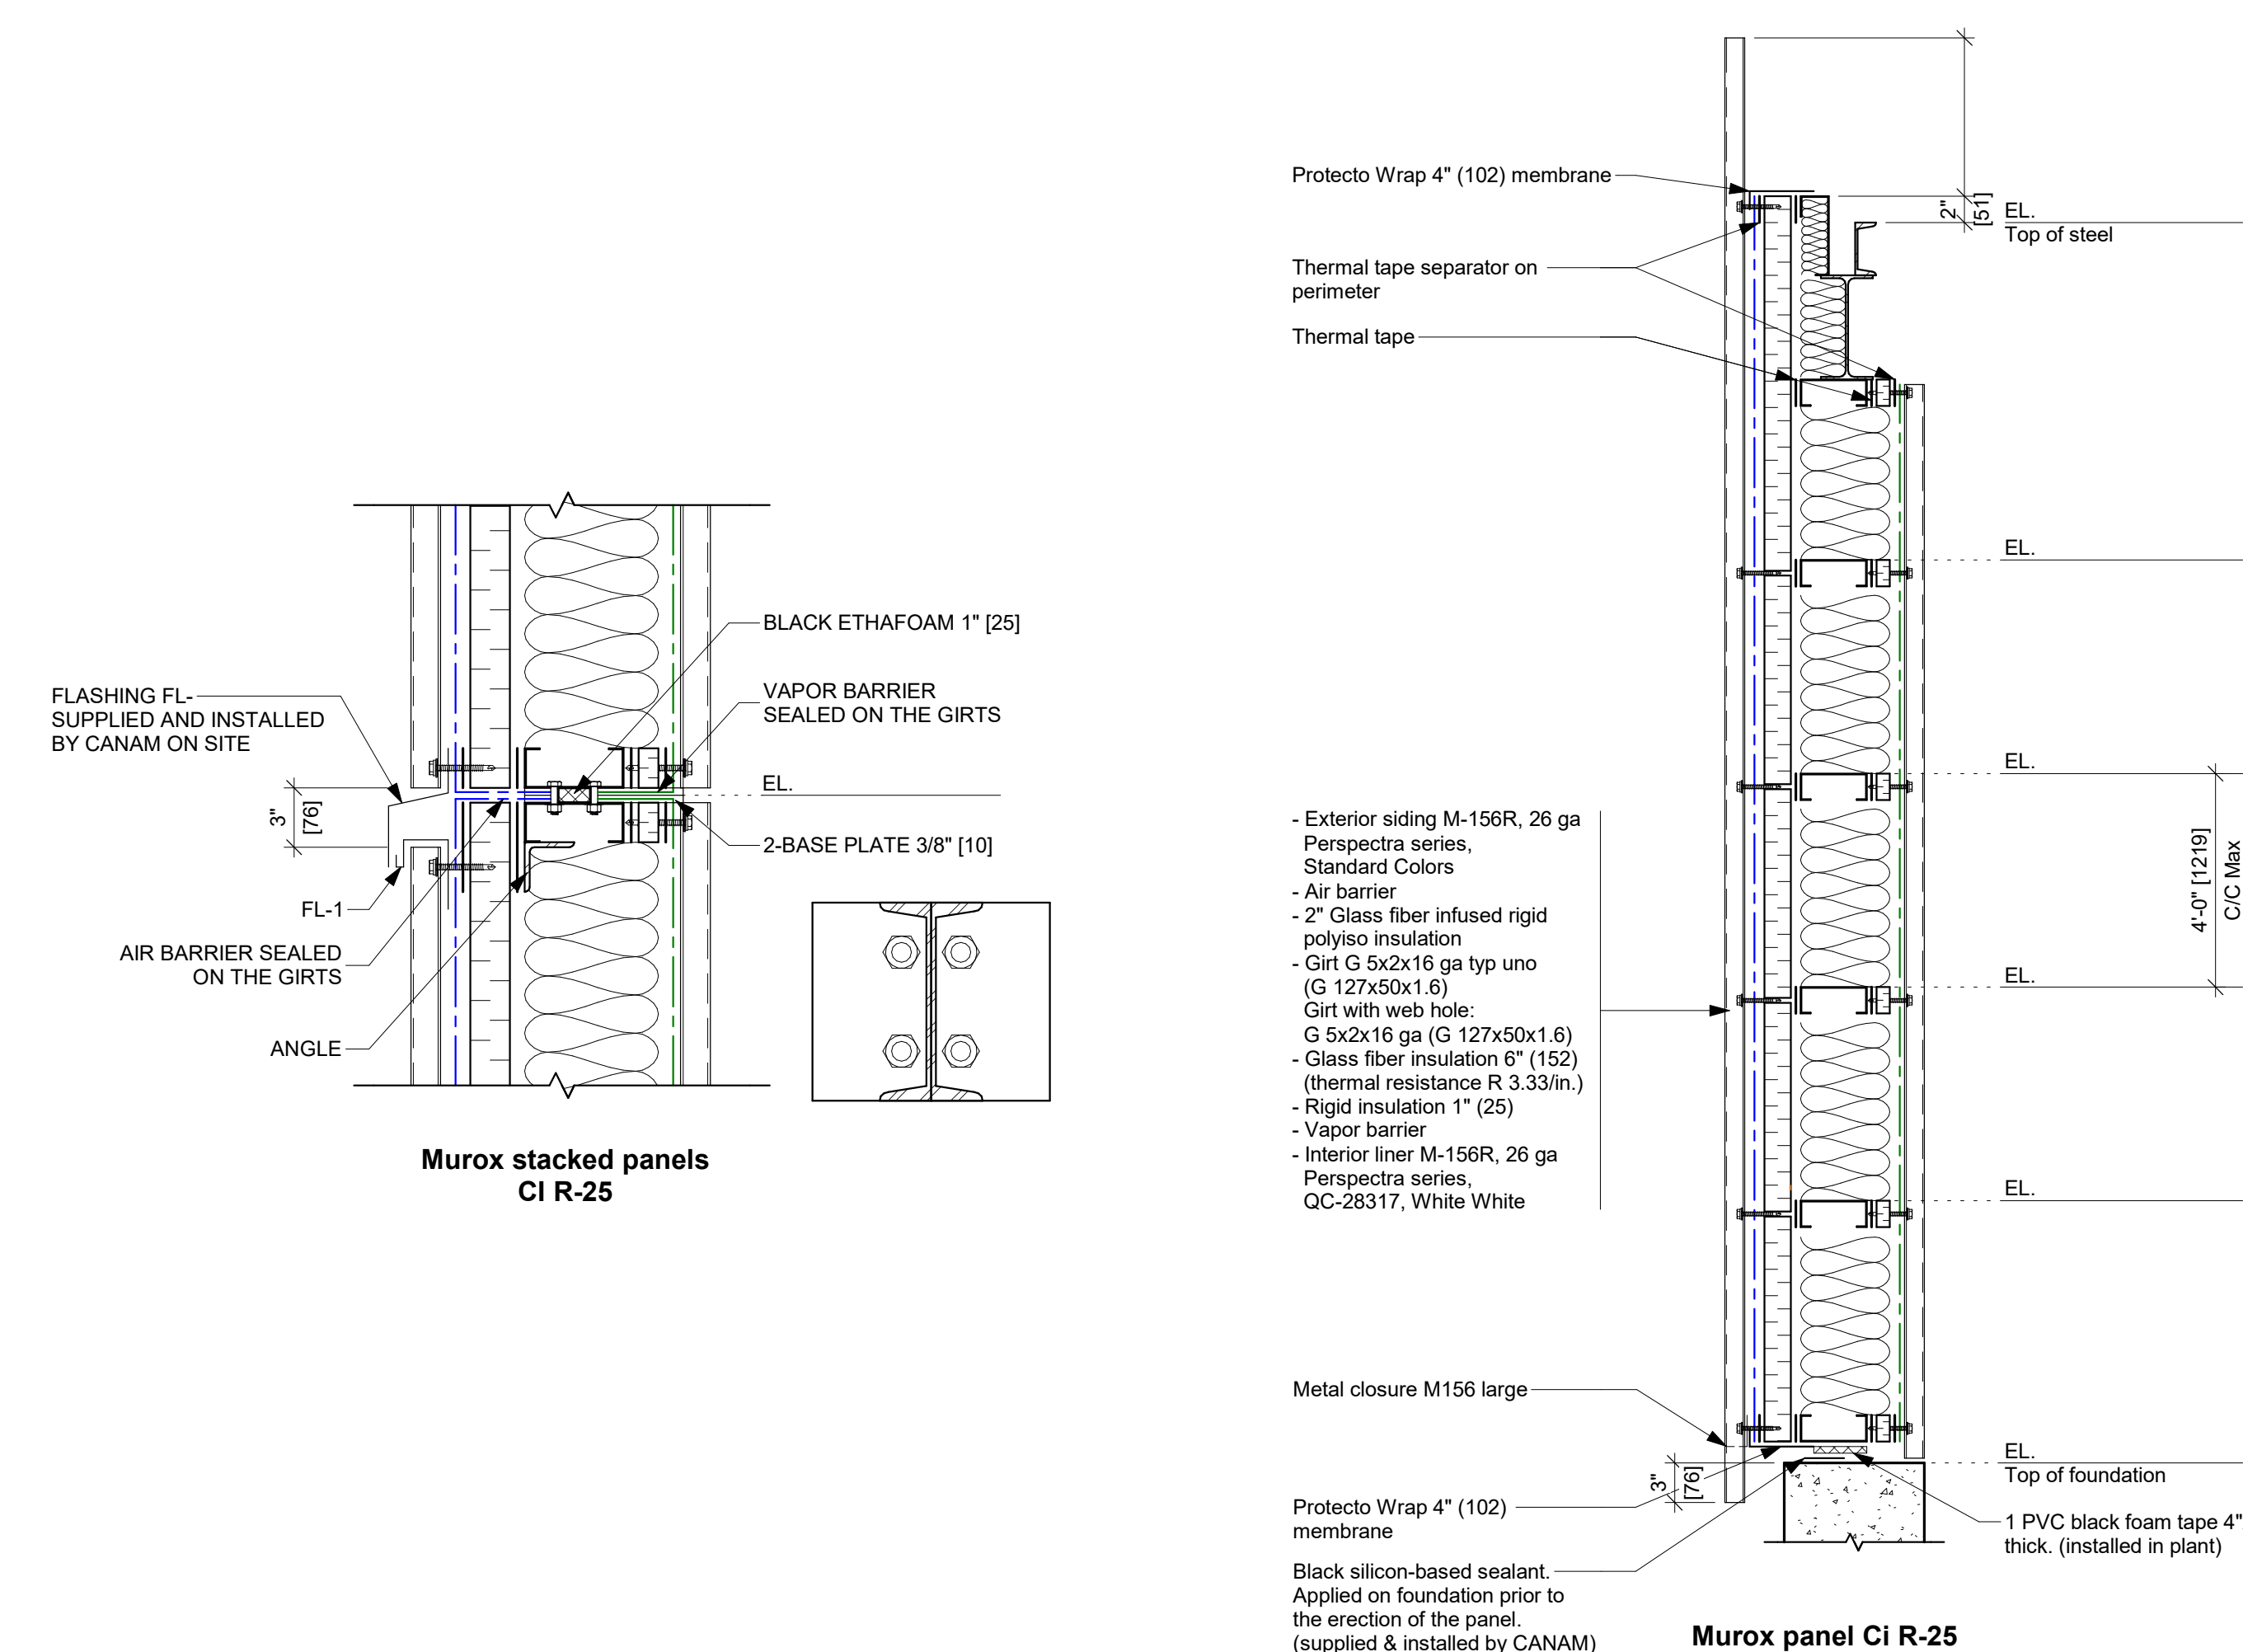
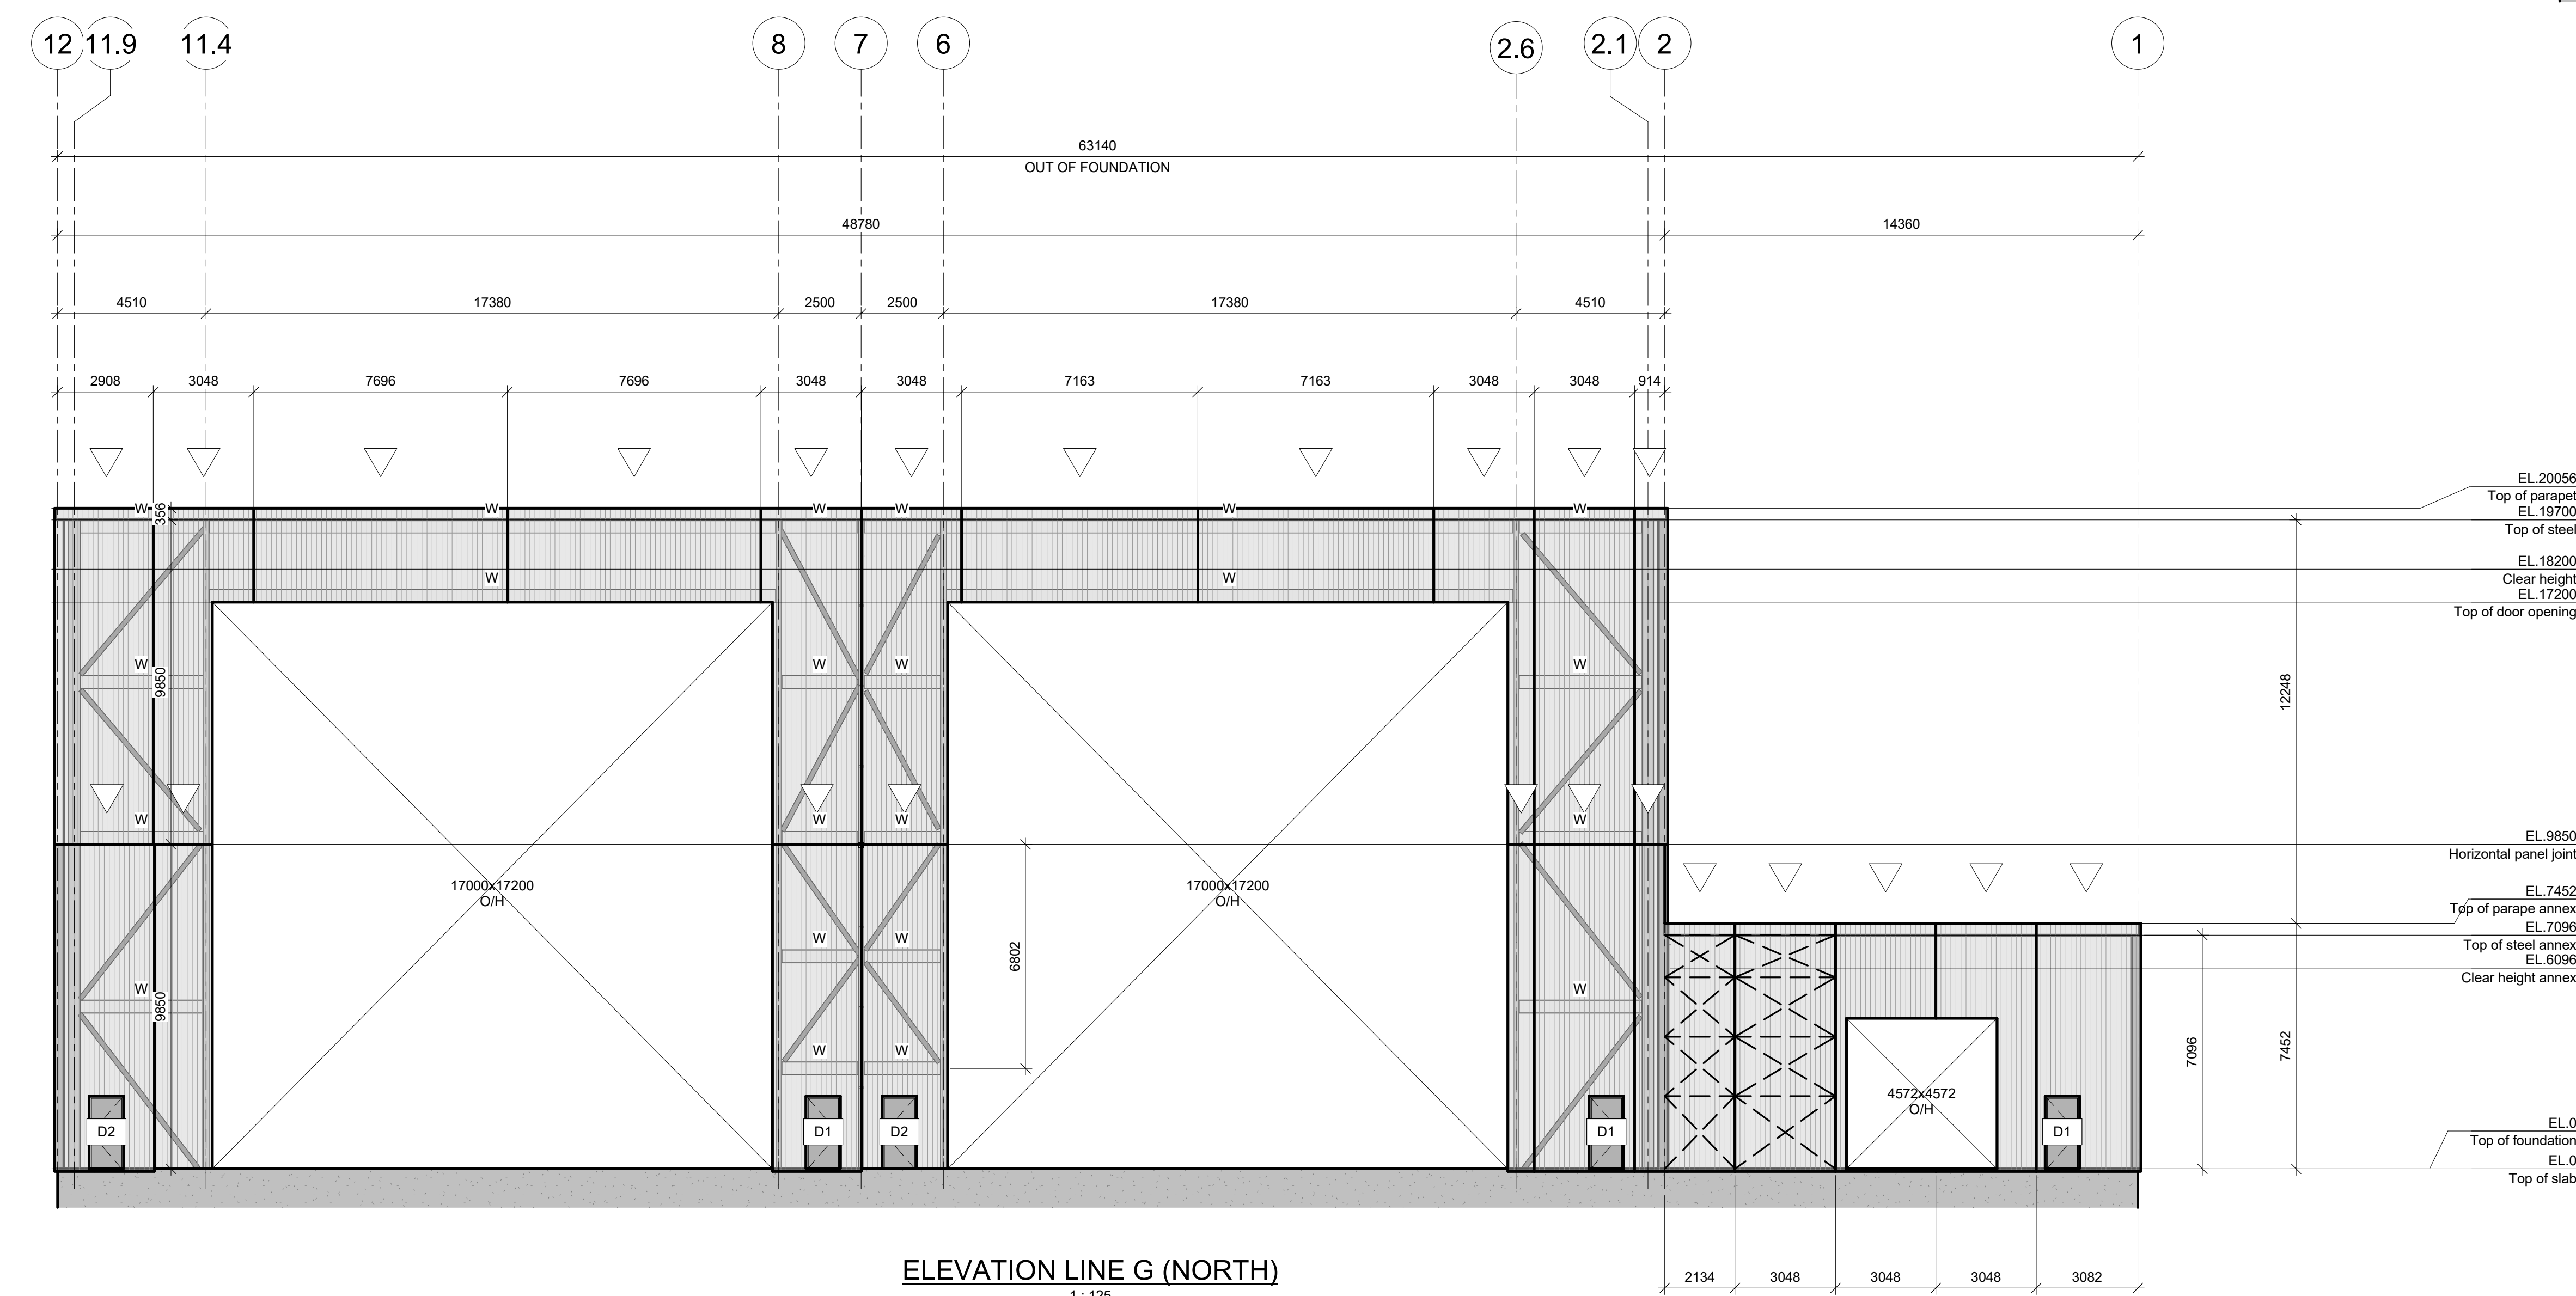
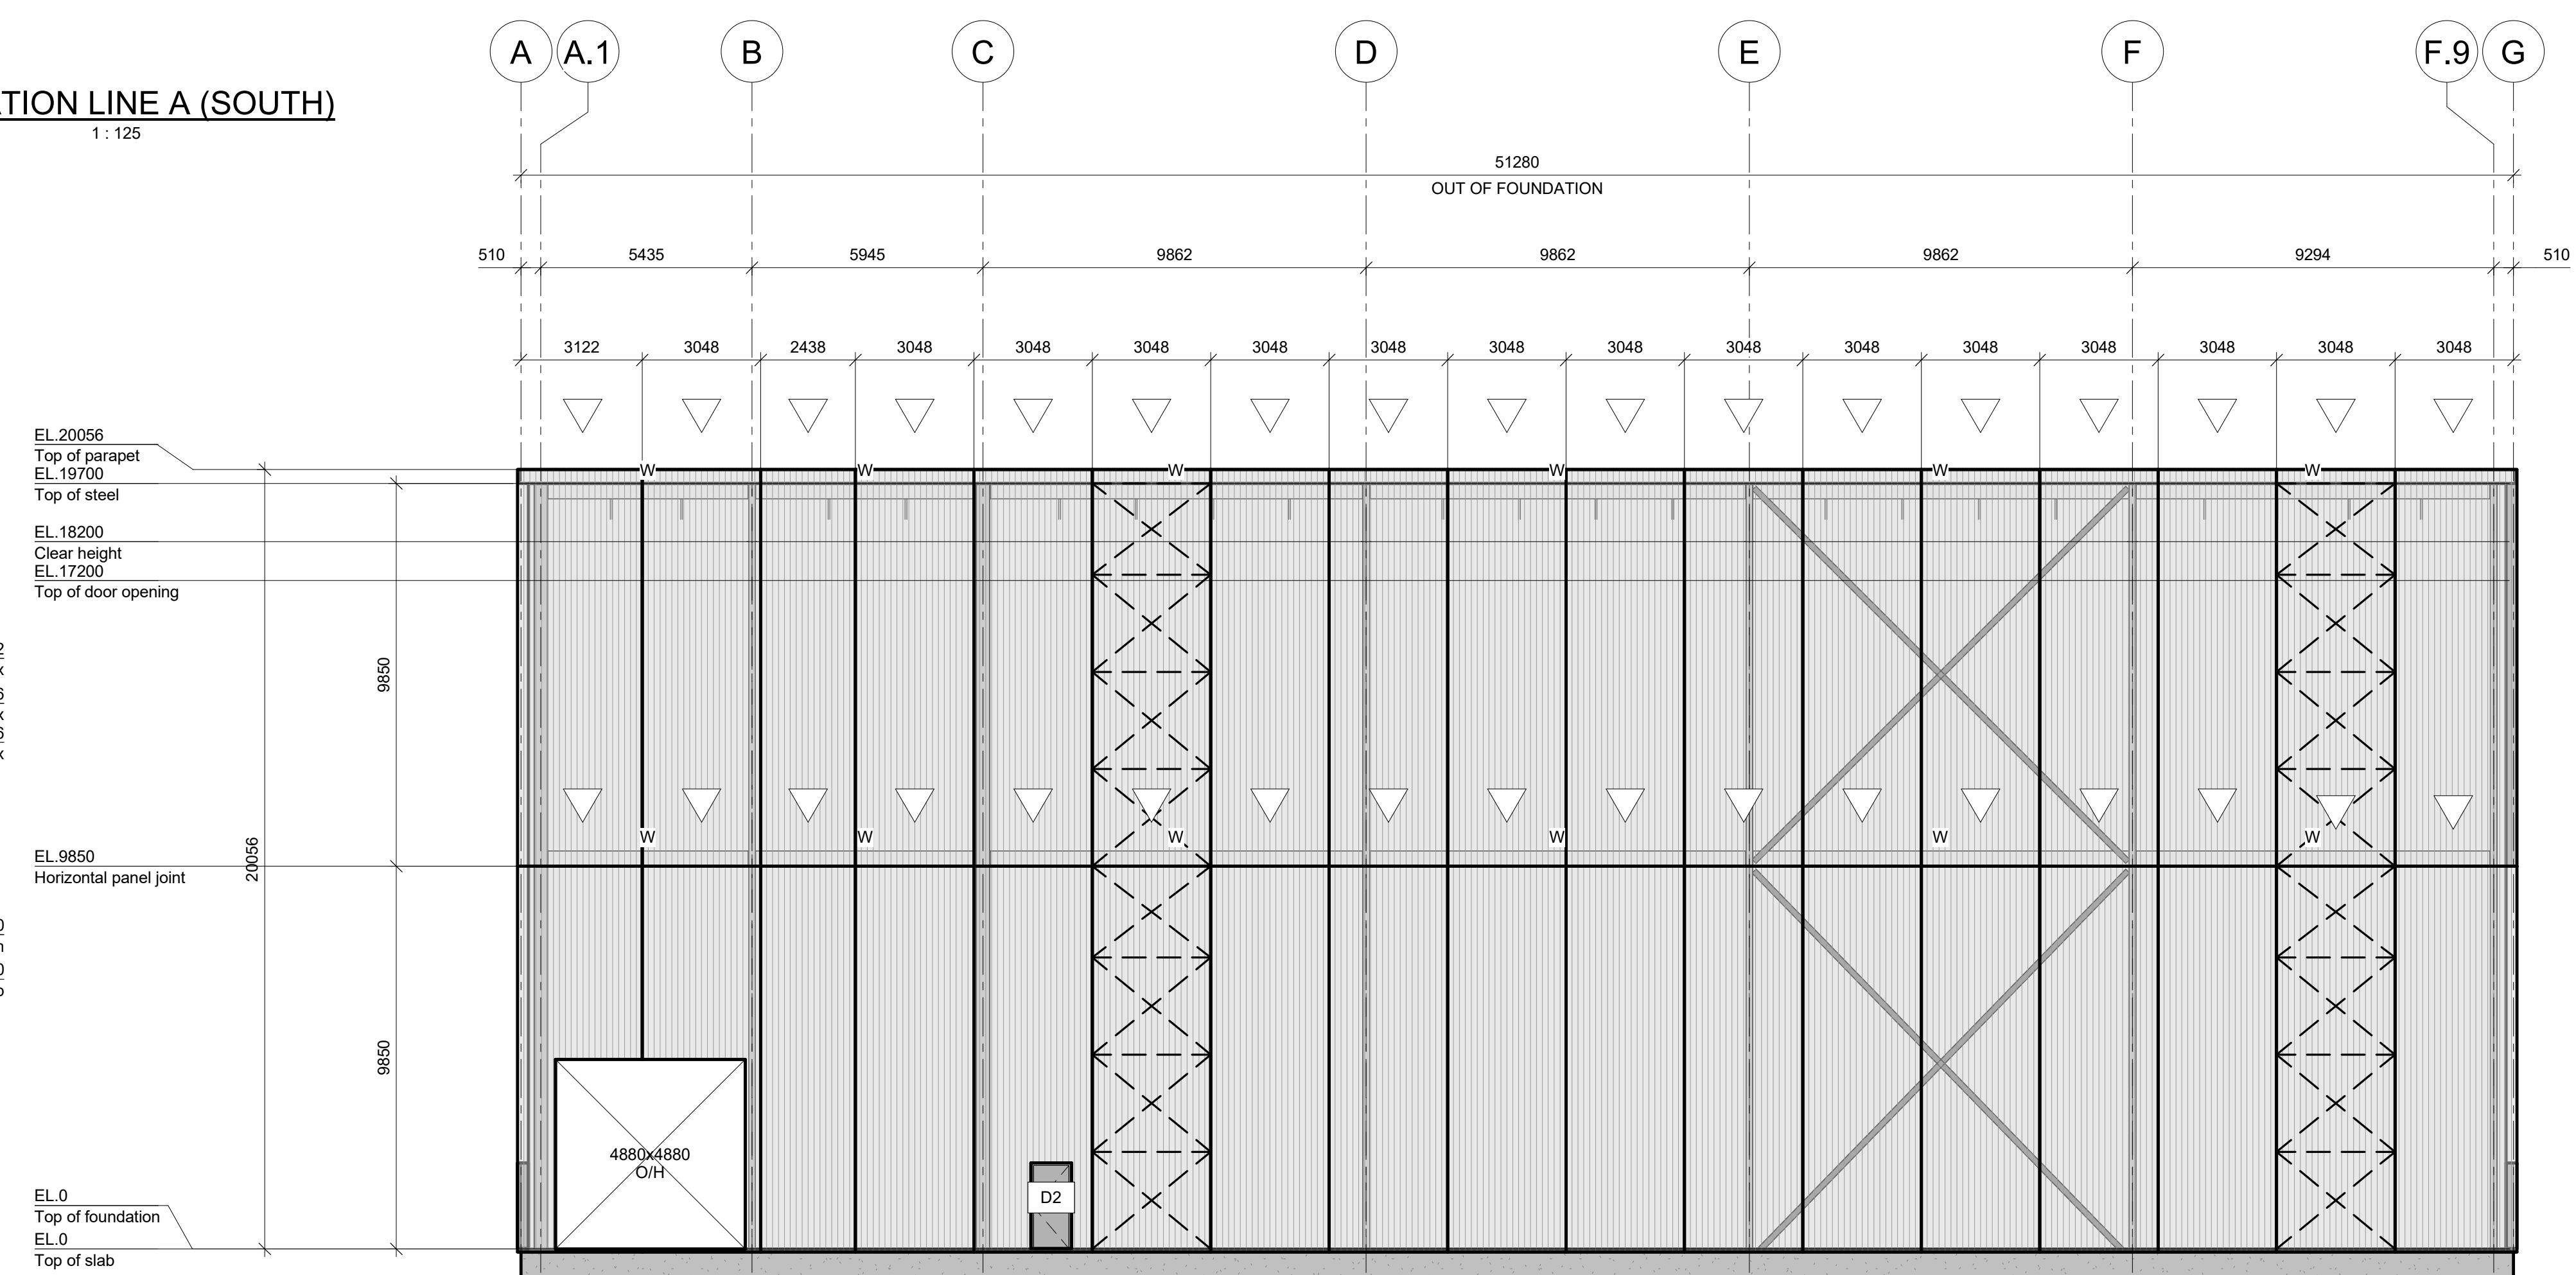
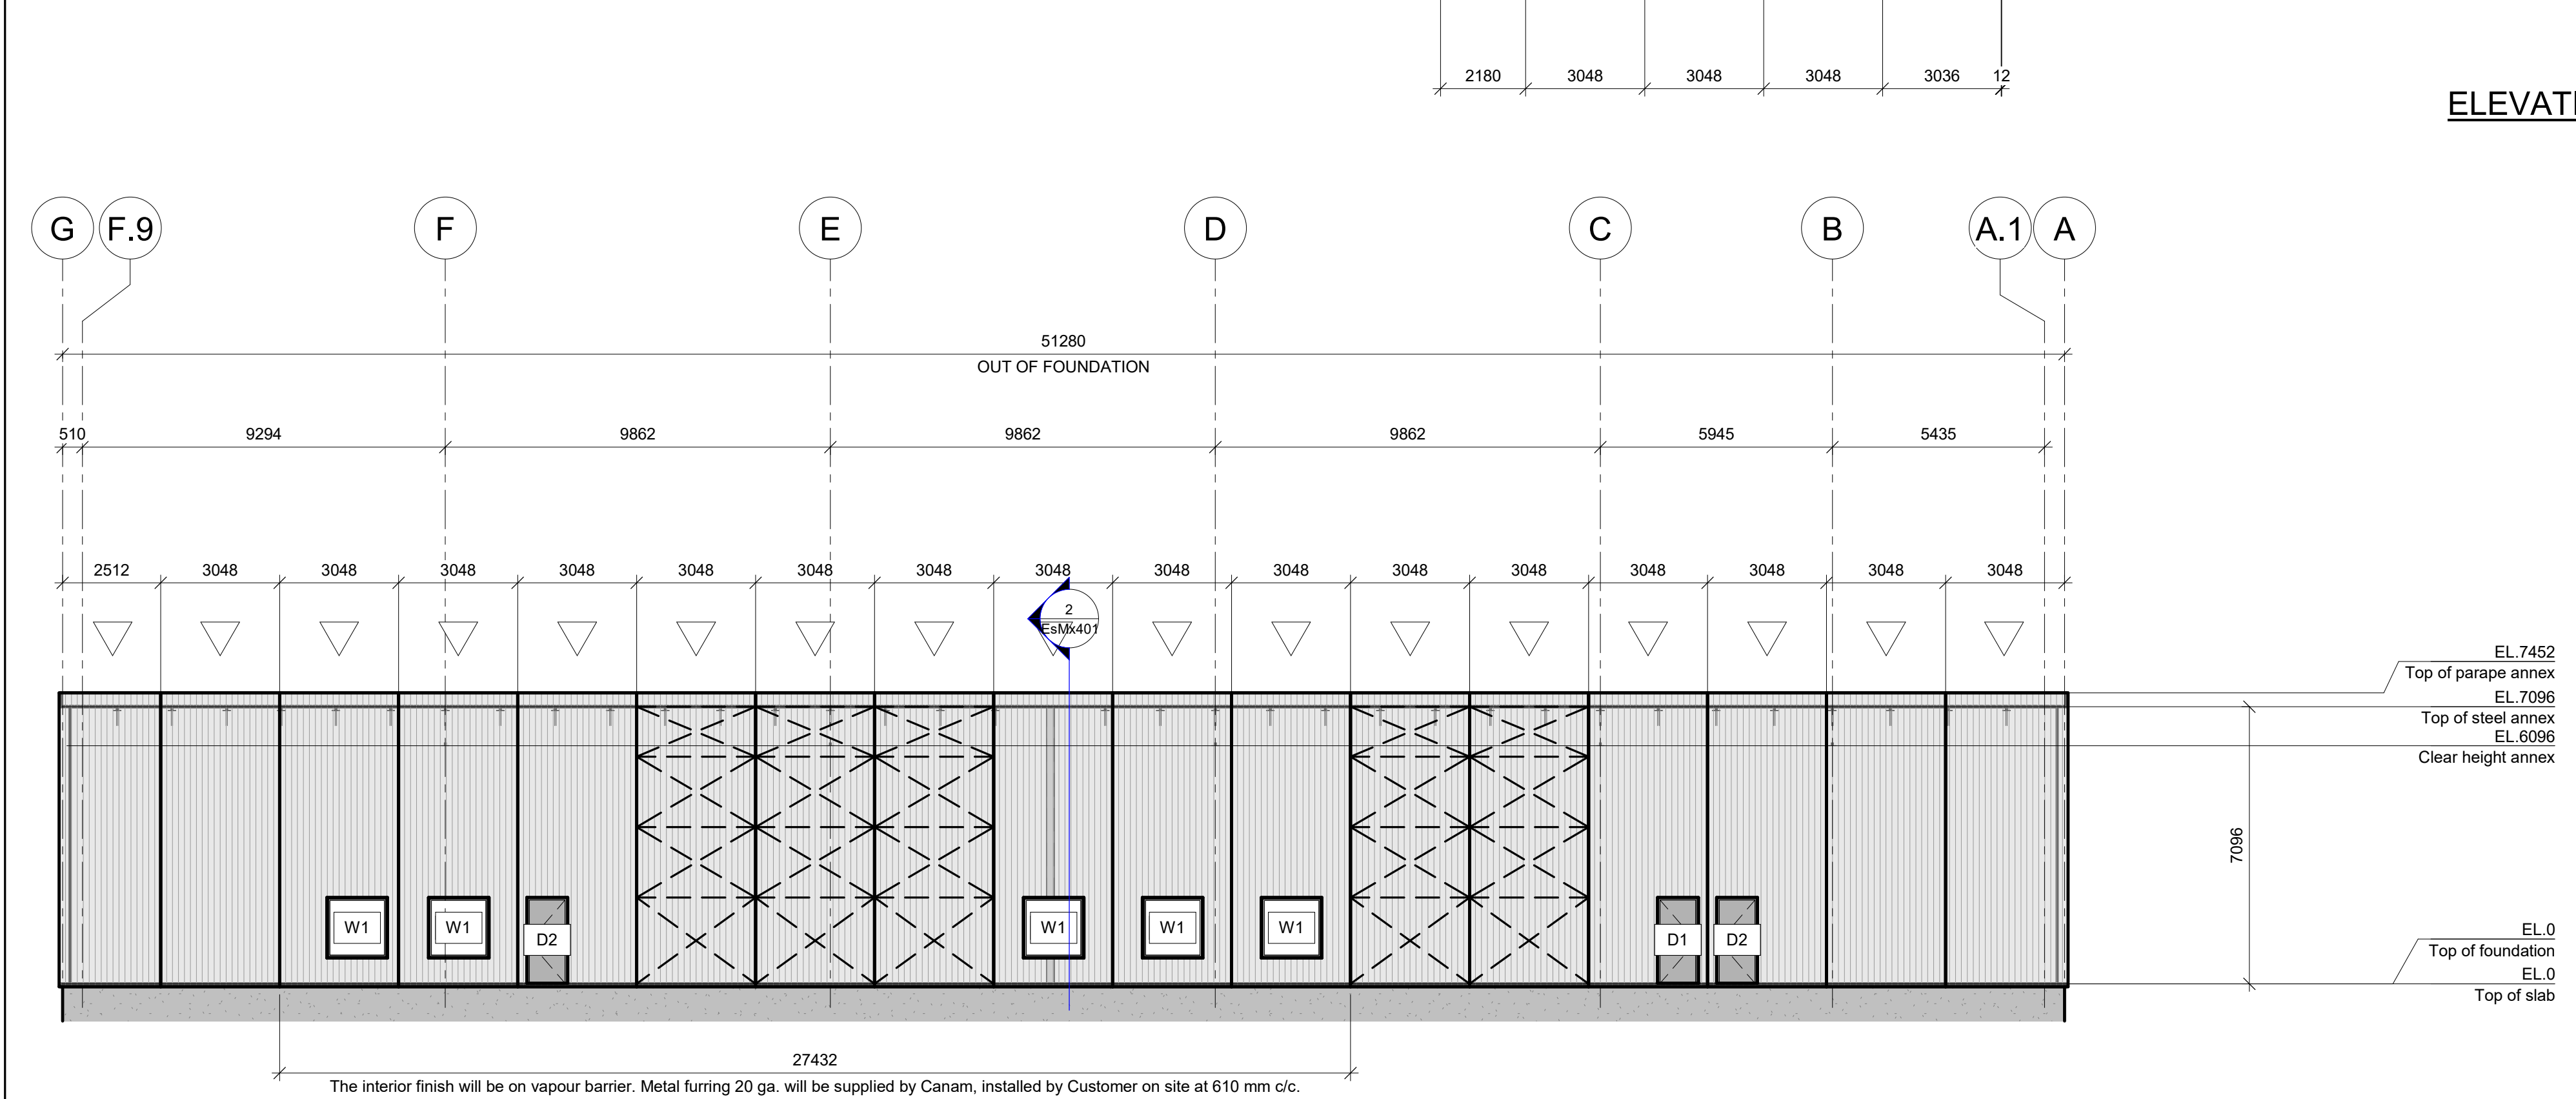


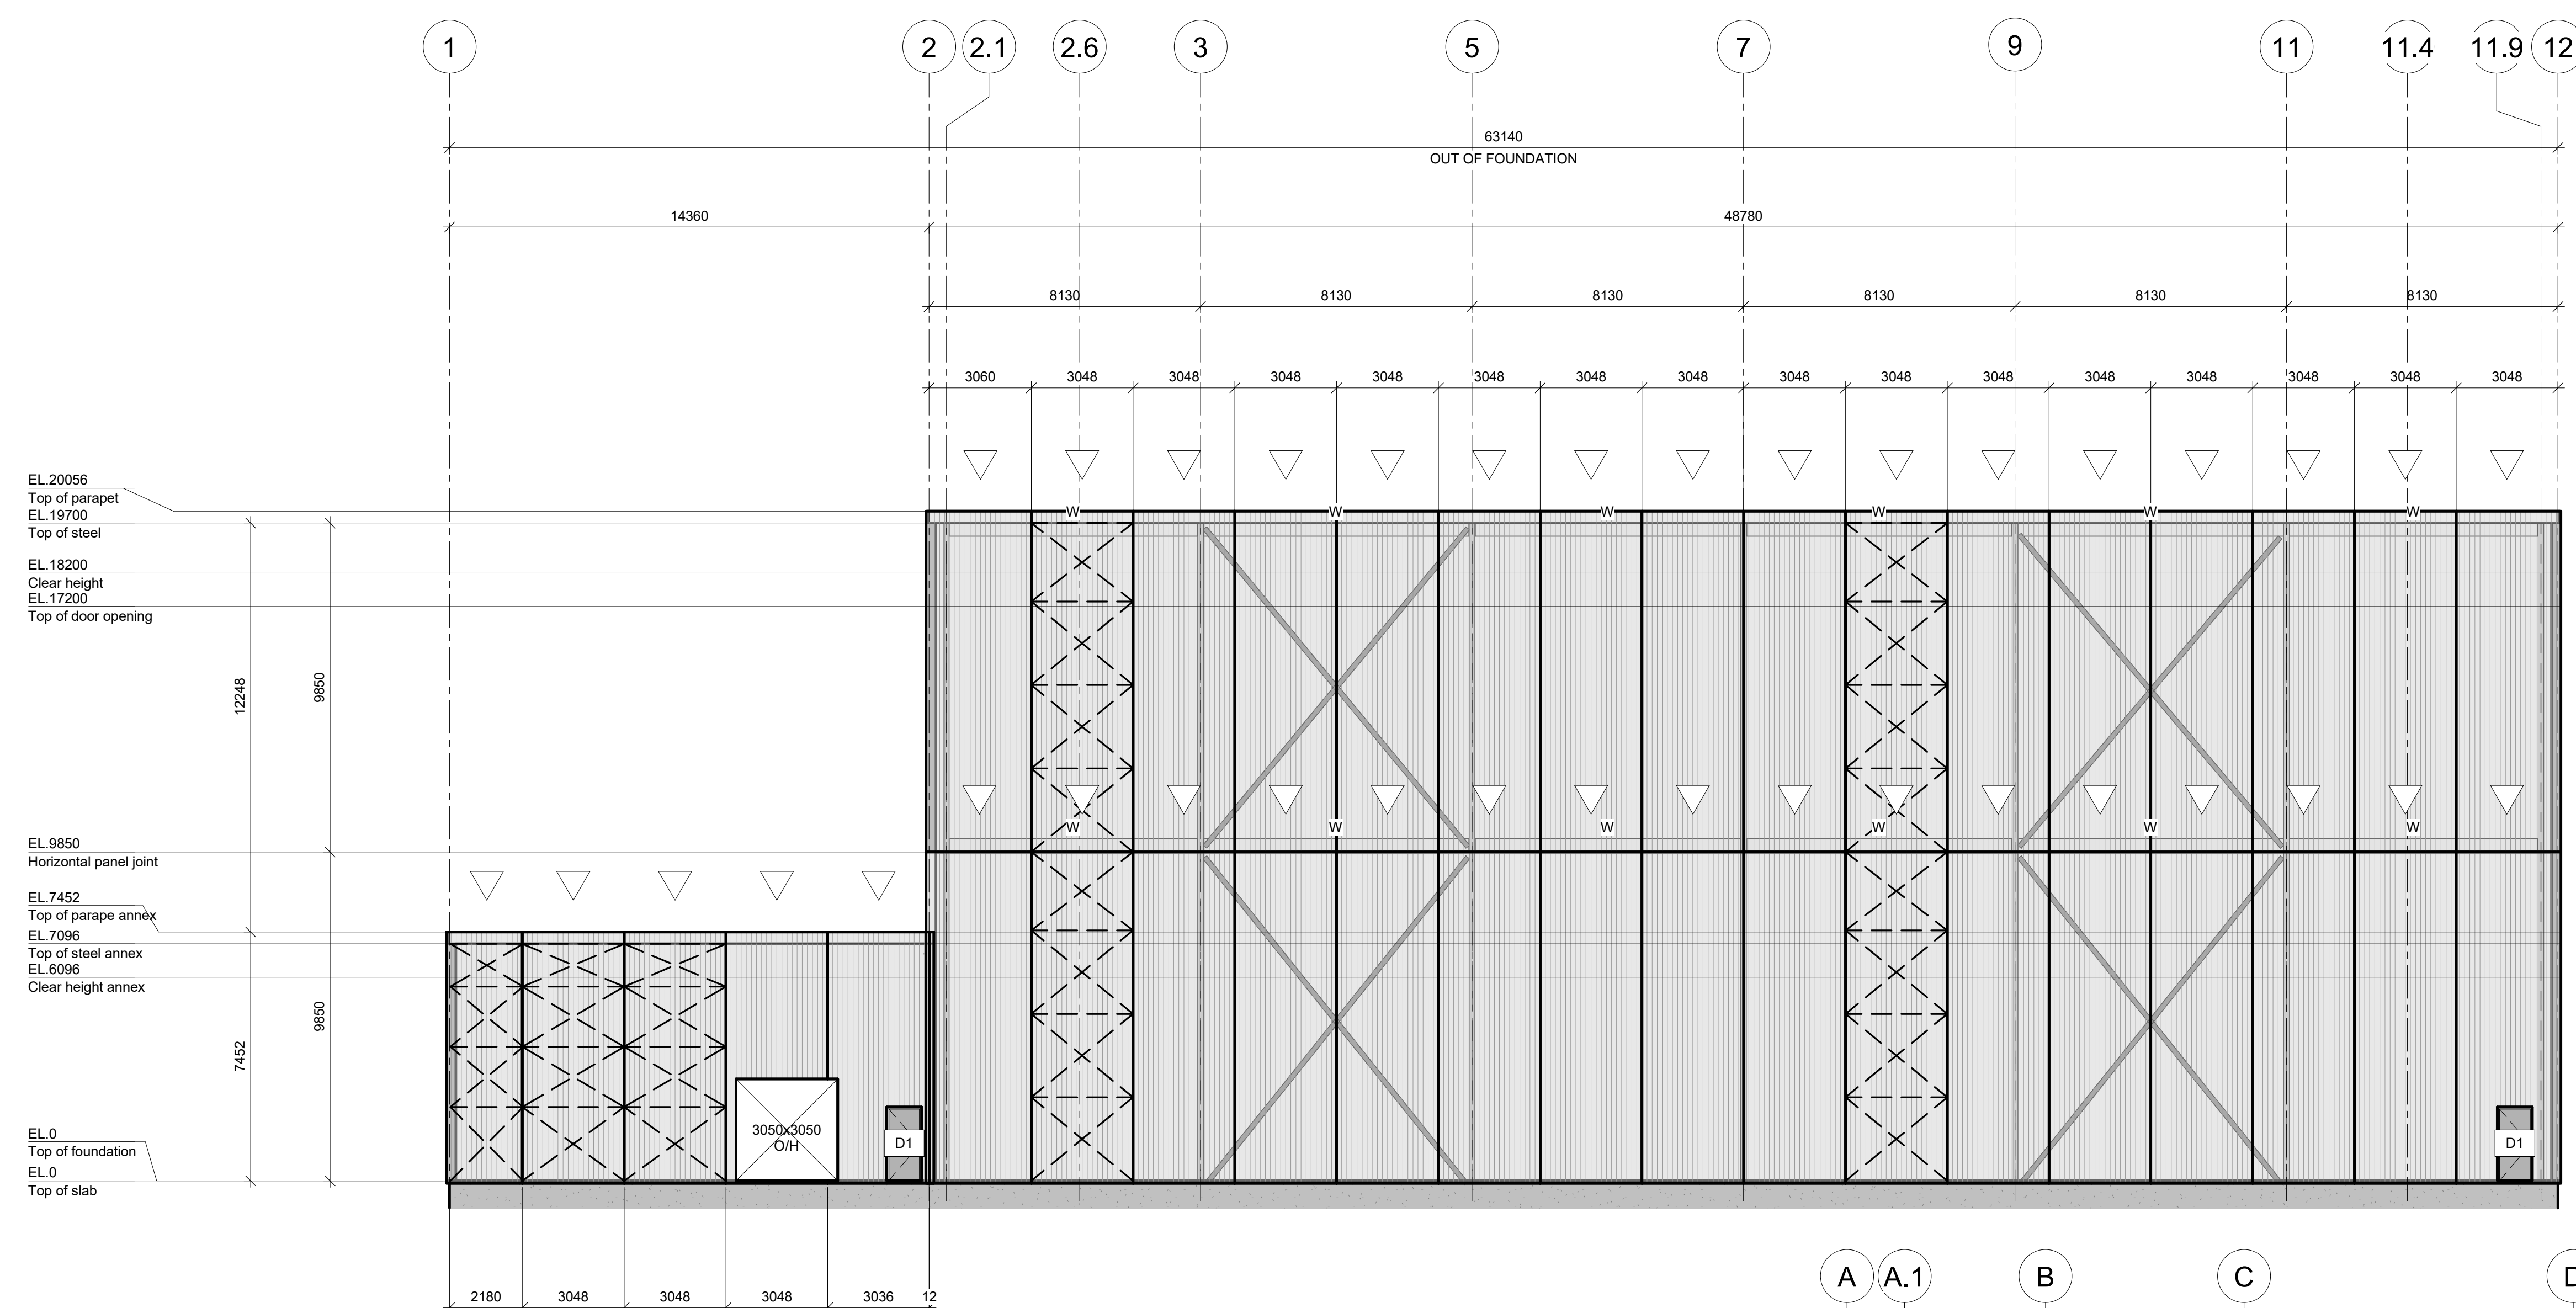

CONTRACTOR/ERECTOR NOTE:

IT IS PROHIBITED TO MODIFY, COPY, REPRODUCE OR OTHERWISE
DISTRIBUTE THIS DRAWING OR ANY REPRESENTATION OF THIS
DRAWING, OR ANY MEDIA, INCLUDING ELECTRONIC, WITHOUT THE
PRIOR WRITTEN APPROVAL OF CANAM GROUP INC.

PRELIMINARY

NOT TO BE USED FOR CONSTRUCTION

REVISION	DATE	DESCRIPTION	DESS	VER
PROJECT MANAGER				
		-		
		-		
		-		
		-		
		-		

DRAFTING			
DRAWN Donald Piché	DESIGNED	PROJECT ENGINEER	SCALE: Comme indiqué
CHECKED	CONSULTING ENGINEERS / ARCHITECTS		DATE (yyyy/mm/dd) : 2026-04-22

CUSTOMER: Pearlson & Pearlson Incorporated



11505, 1re Avenue, bureau 500, Saint-Georges Beauce
Quebec, Canada, G5Y 7X3
Phone : (418) 228-8031
Toll free : (877) 499-6049
www.canam.com

PROFESSIONAL SEAL

PROJECT

**Davie Shipyard - Paint and Blast facility
Lévis, QC**

DRAWING TITLE

PRELIMINARY SKETCH - ELEVATIONS

CONTRACT NUMBER P2026-091	DRAWING NUMBER EsMx501	DIVISION	REVISION 
------------------------------	----------------------------------	----------	---