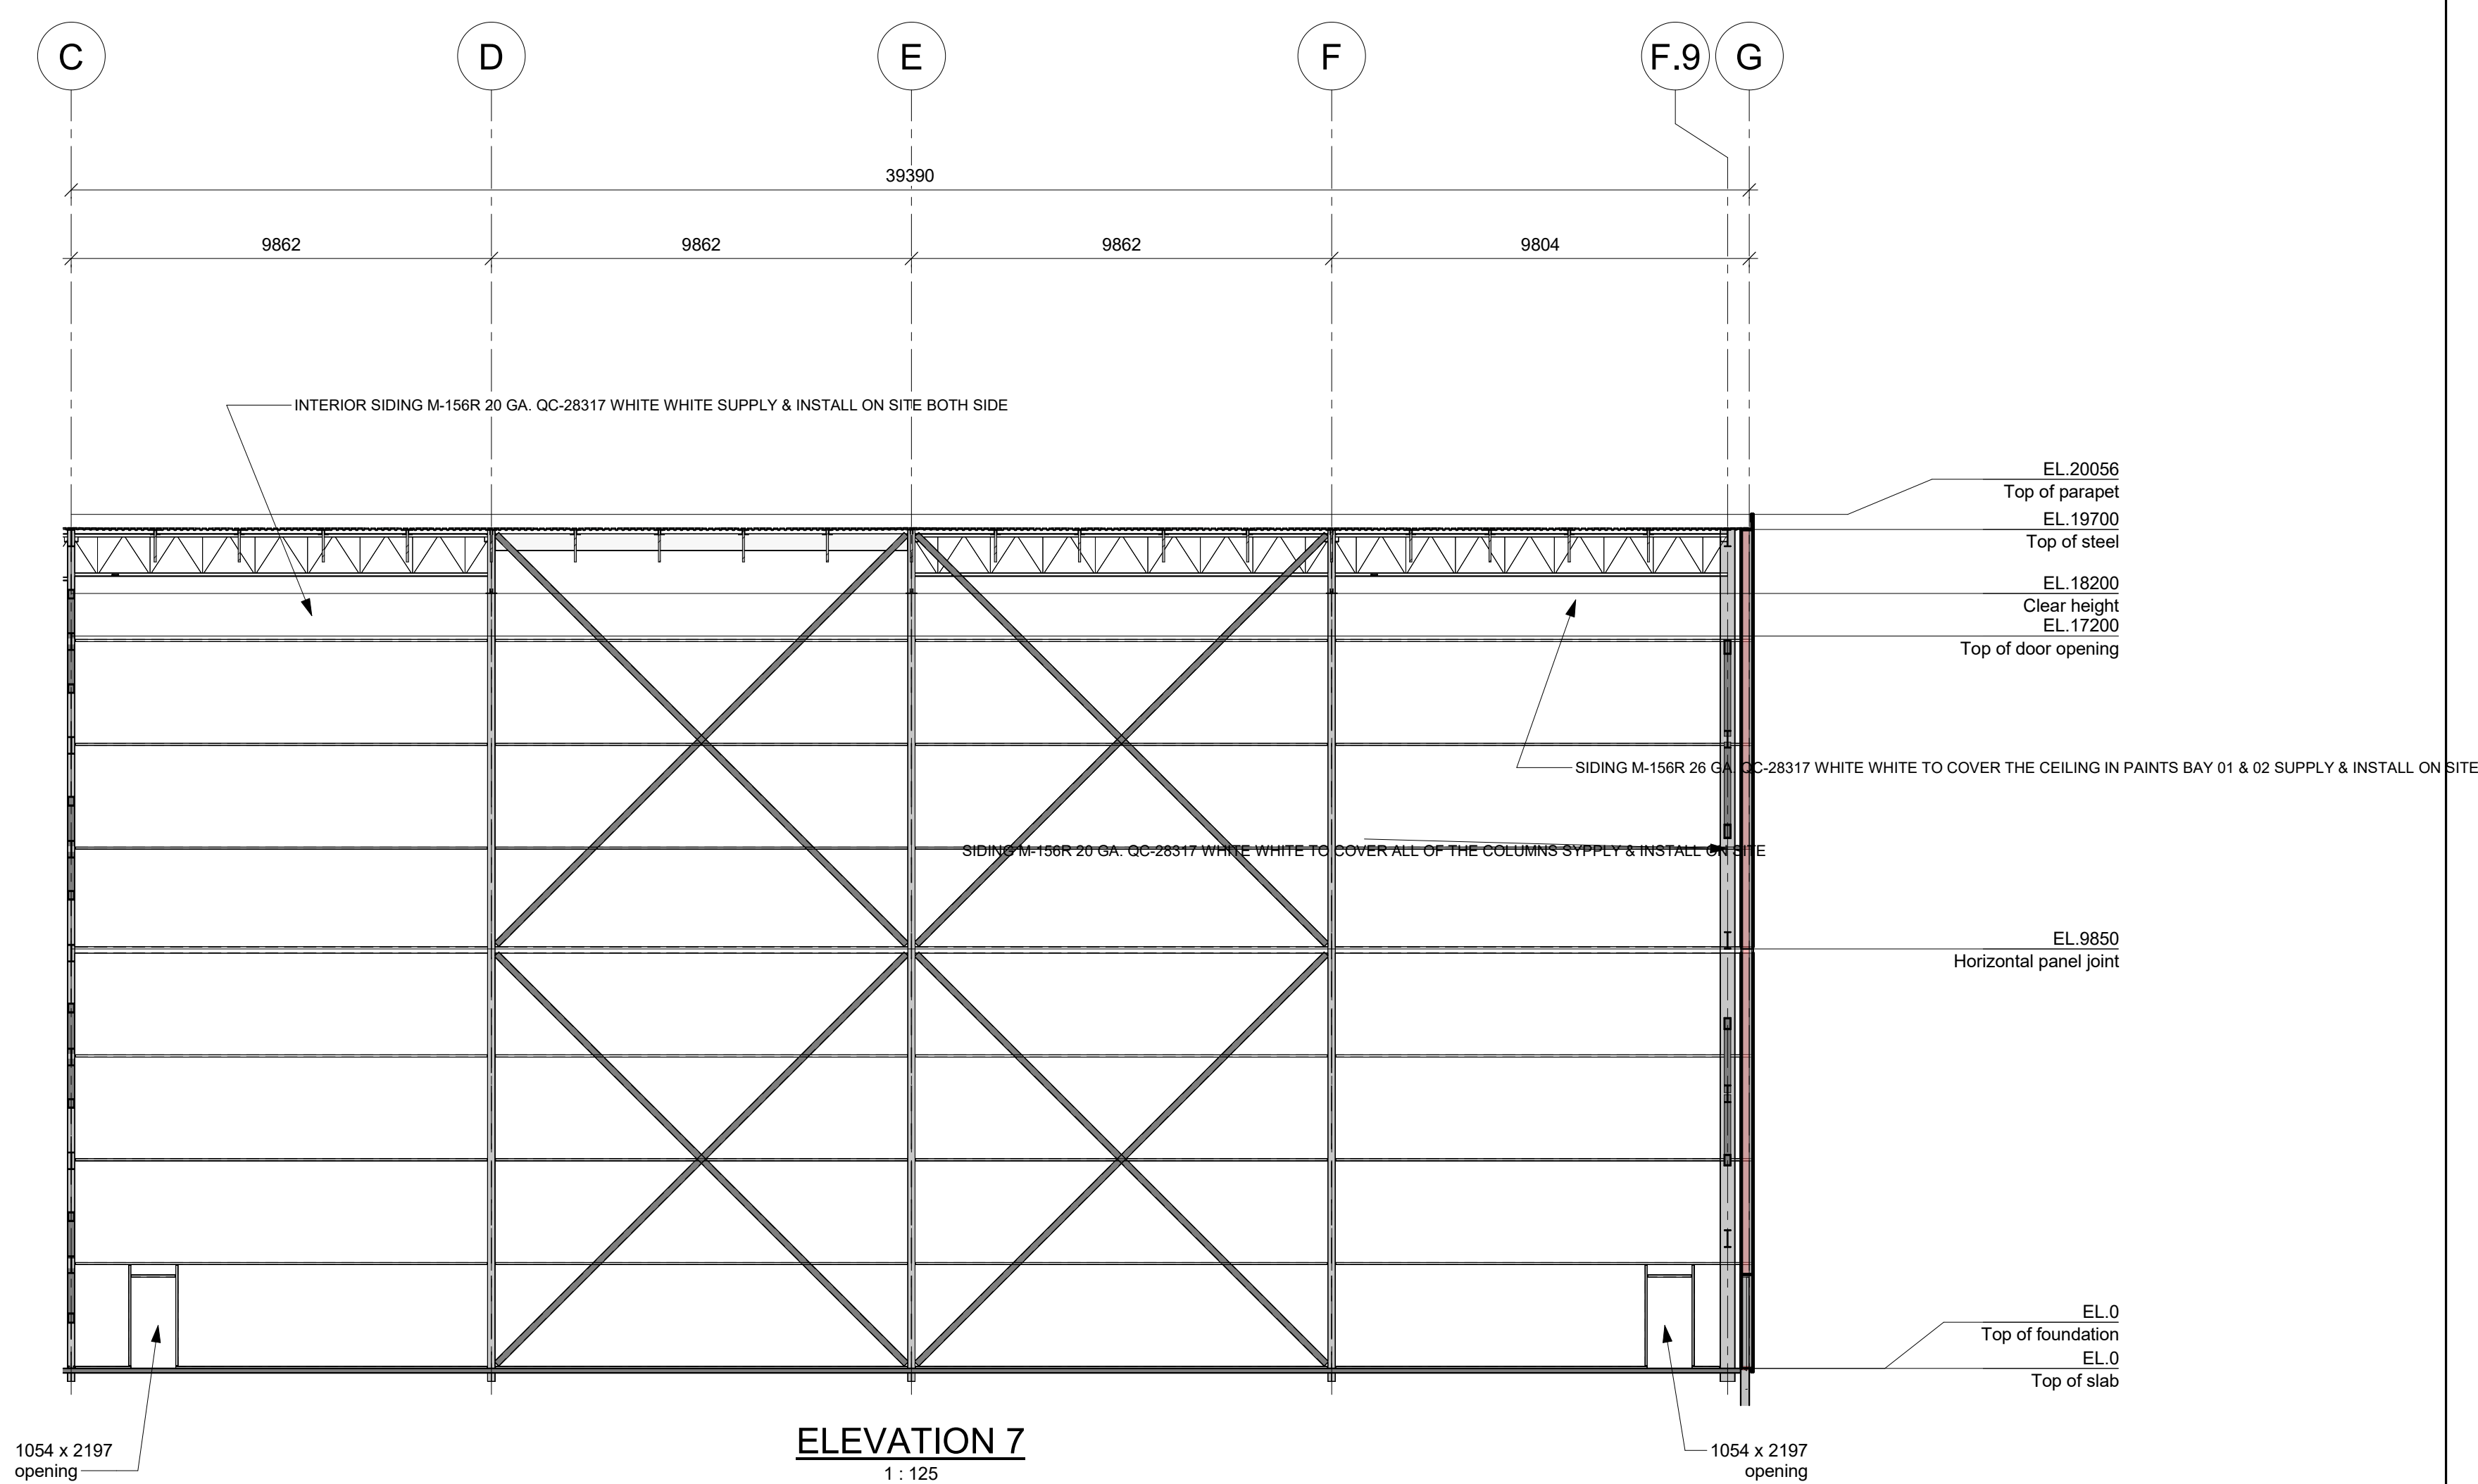


O/H & OPENING SCHEDULE			
Total	Type	Tag	Remarks
1	4572x4572	O/H	
1	4880x4880	O/H	
2	17000x17200	O/H	
Total général: 4			

Supplier's standard hardware:

- Hinges: Stanley FBB179 4.5" x 4"
- Exit device: Von Duprin 22 x 689 with outside trim 230L
- Permanent cylinder: Schlage 20001C 626
- Door closure: LCN 1261 689
- Head and jamb seal: Unique 1650
- Bottom seal: Unique DS4
- Threshold: See the remarks in "Door schedule"

CONTRACTOR/ERECTOR NOTE:

IT IS PROHIBITED TO MODIFY, COPY, REPRODUCE OR OTHERWISE
DISTRIBUTE THIS DRAWING OR ANY REPRESENTATION OF THIS
DRAWING, OR ANY MEDIA, INCLUDING ELECTRONIC, WITHOUT THE
PRIOR WRITTEN APPROVAL OF CANAM GROUP INC.

NOT TO BE USED FOR CONSTRUCTION

REVISION	DATE	DESCRIPTION	DESS.	VER.
----------	------	-------------	-------	------

PROJECT MANAGER	-
	-
	-
	-
	-
	-

DRAFTING:

DRAWN Donald Piché	DESIGNED	PROJECT ENGINEER	SCALE: Comme indiqué
---------------------------	----------	------------------	-----------------------------

CHECKED	CONSULTING ENGINEERS / ARCHITECTS	DATE (yyyy/mm/dd): 2026-04-22
---------	-----------------------------------	----------------------------------

CUSTOMER: Pearlson & Pearlson Incorporated



PROFESSIONAL SEAL

PROSPECT

Davie Shipyard - Paint and Blast facility
Lévis, QC

DRAWING TITLE

PRELIMINARY SKETCH - ELEVATION WALL SECTION AND SCHEDULES

CONTRACT NUMBER	DRAWING NUMBER	DIVISION	REVISION
-----------------	----------------	----------	----------

