



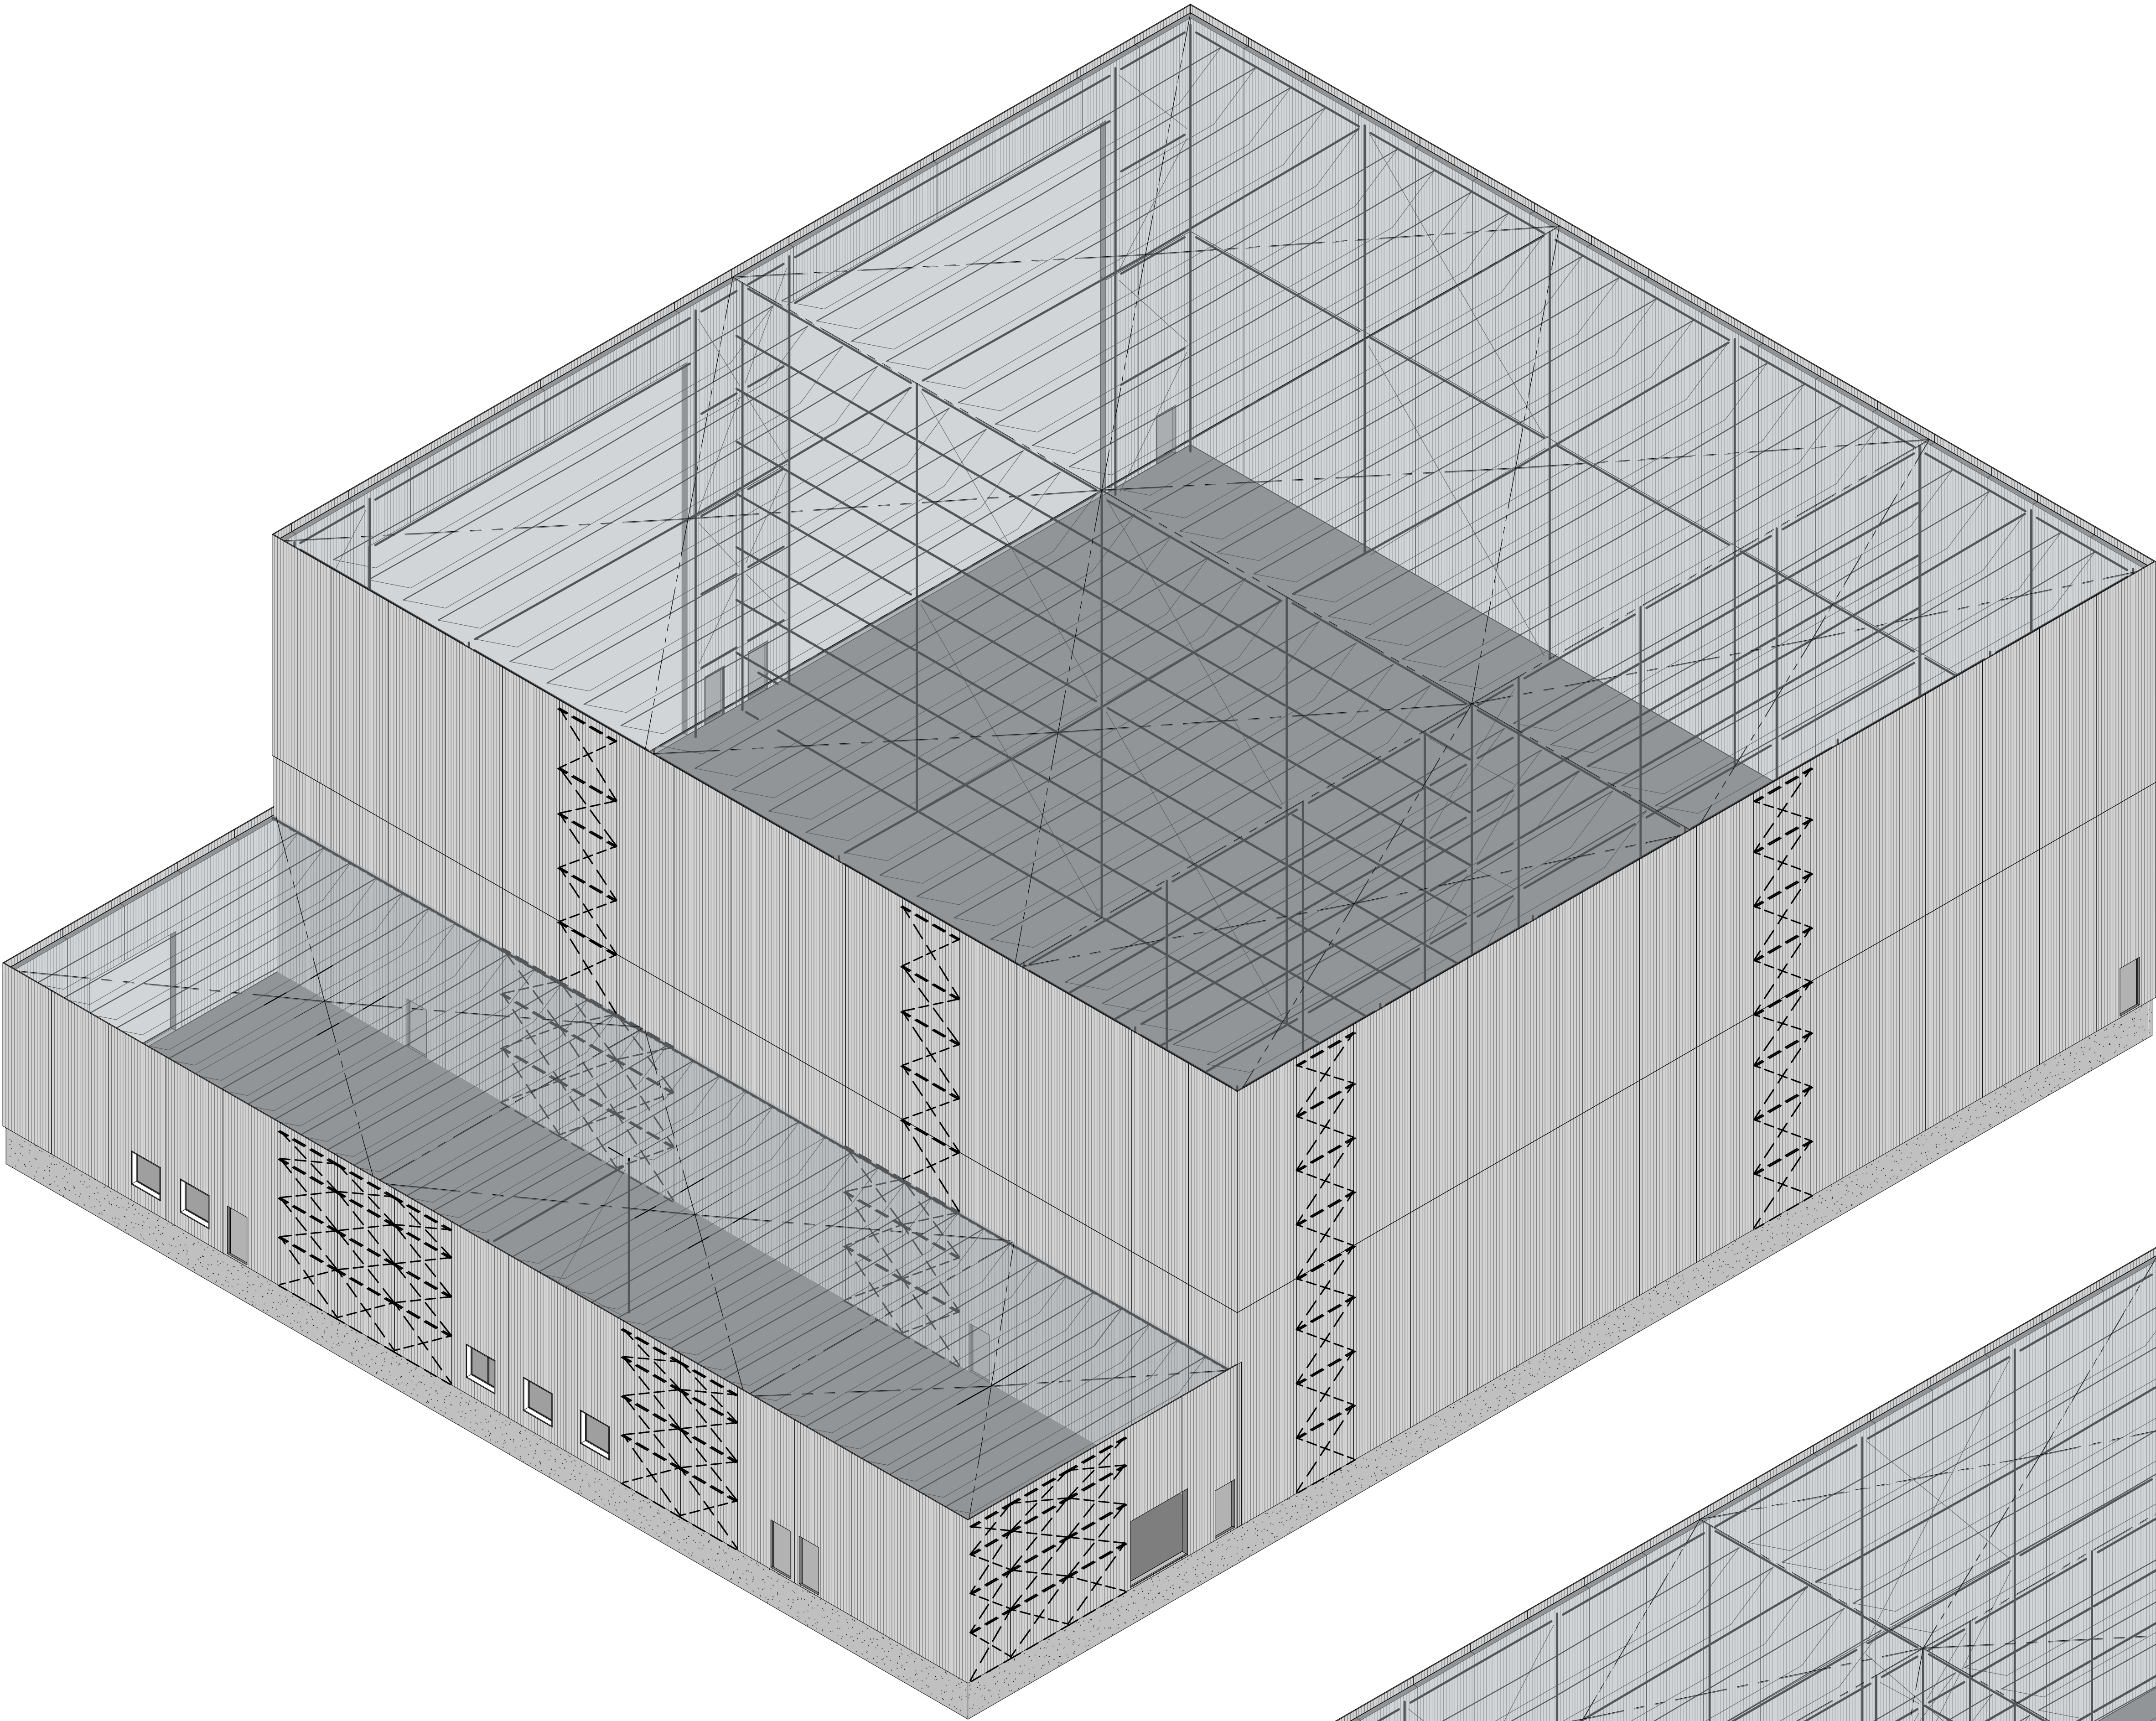

3D VIEW S-W

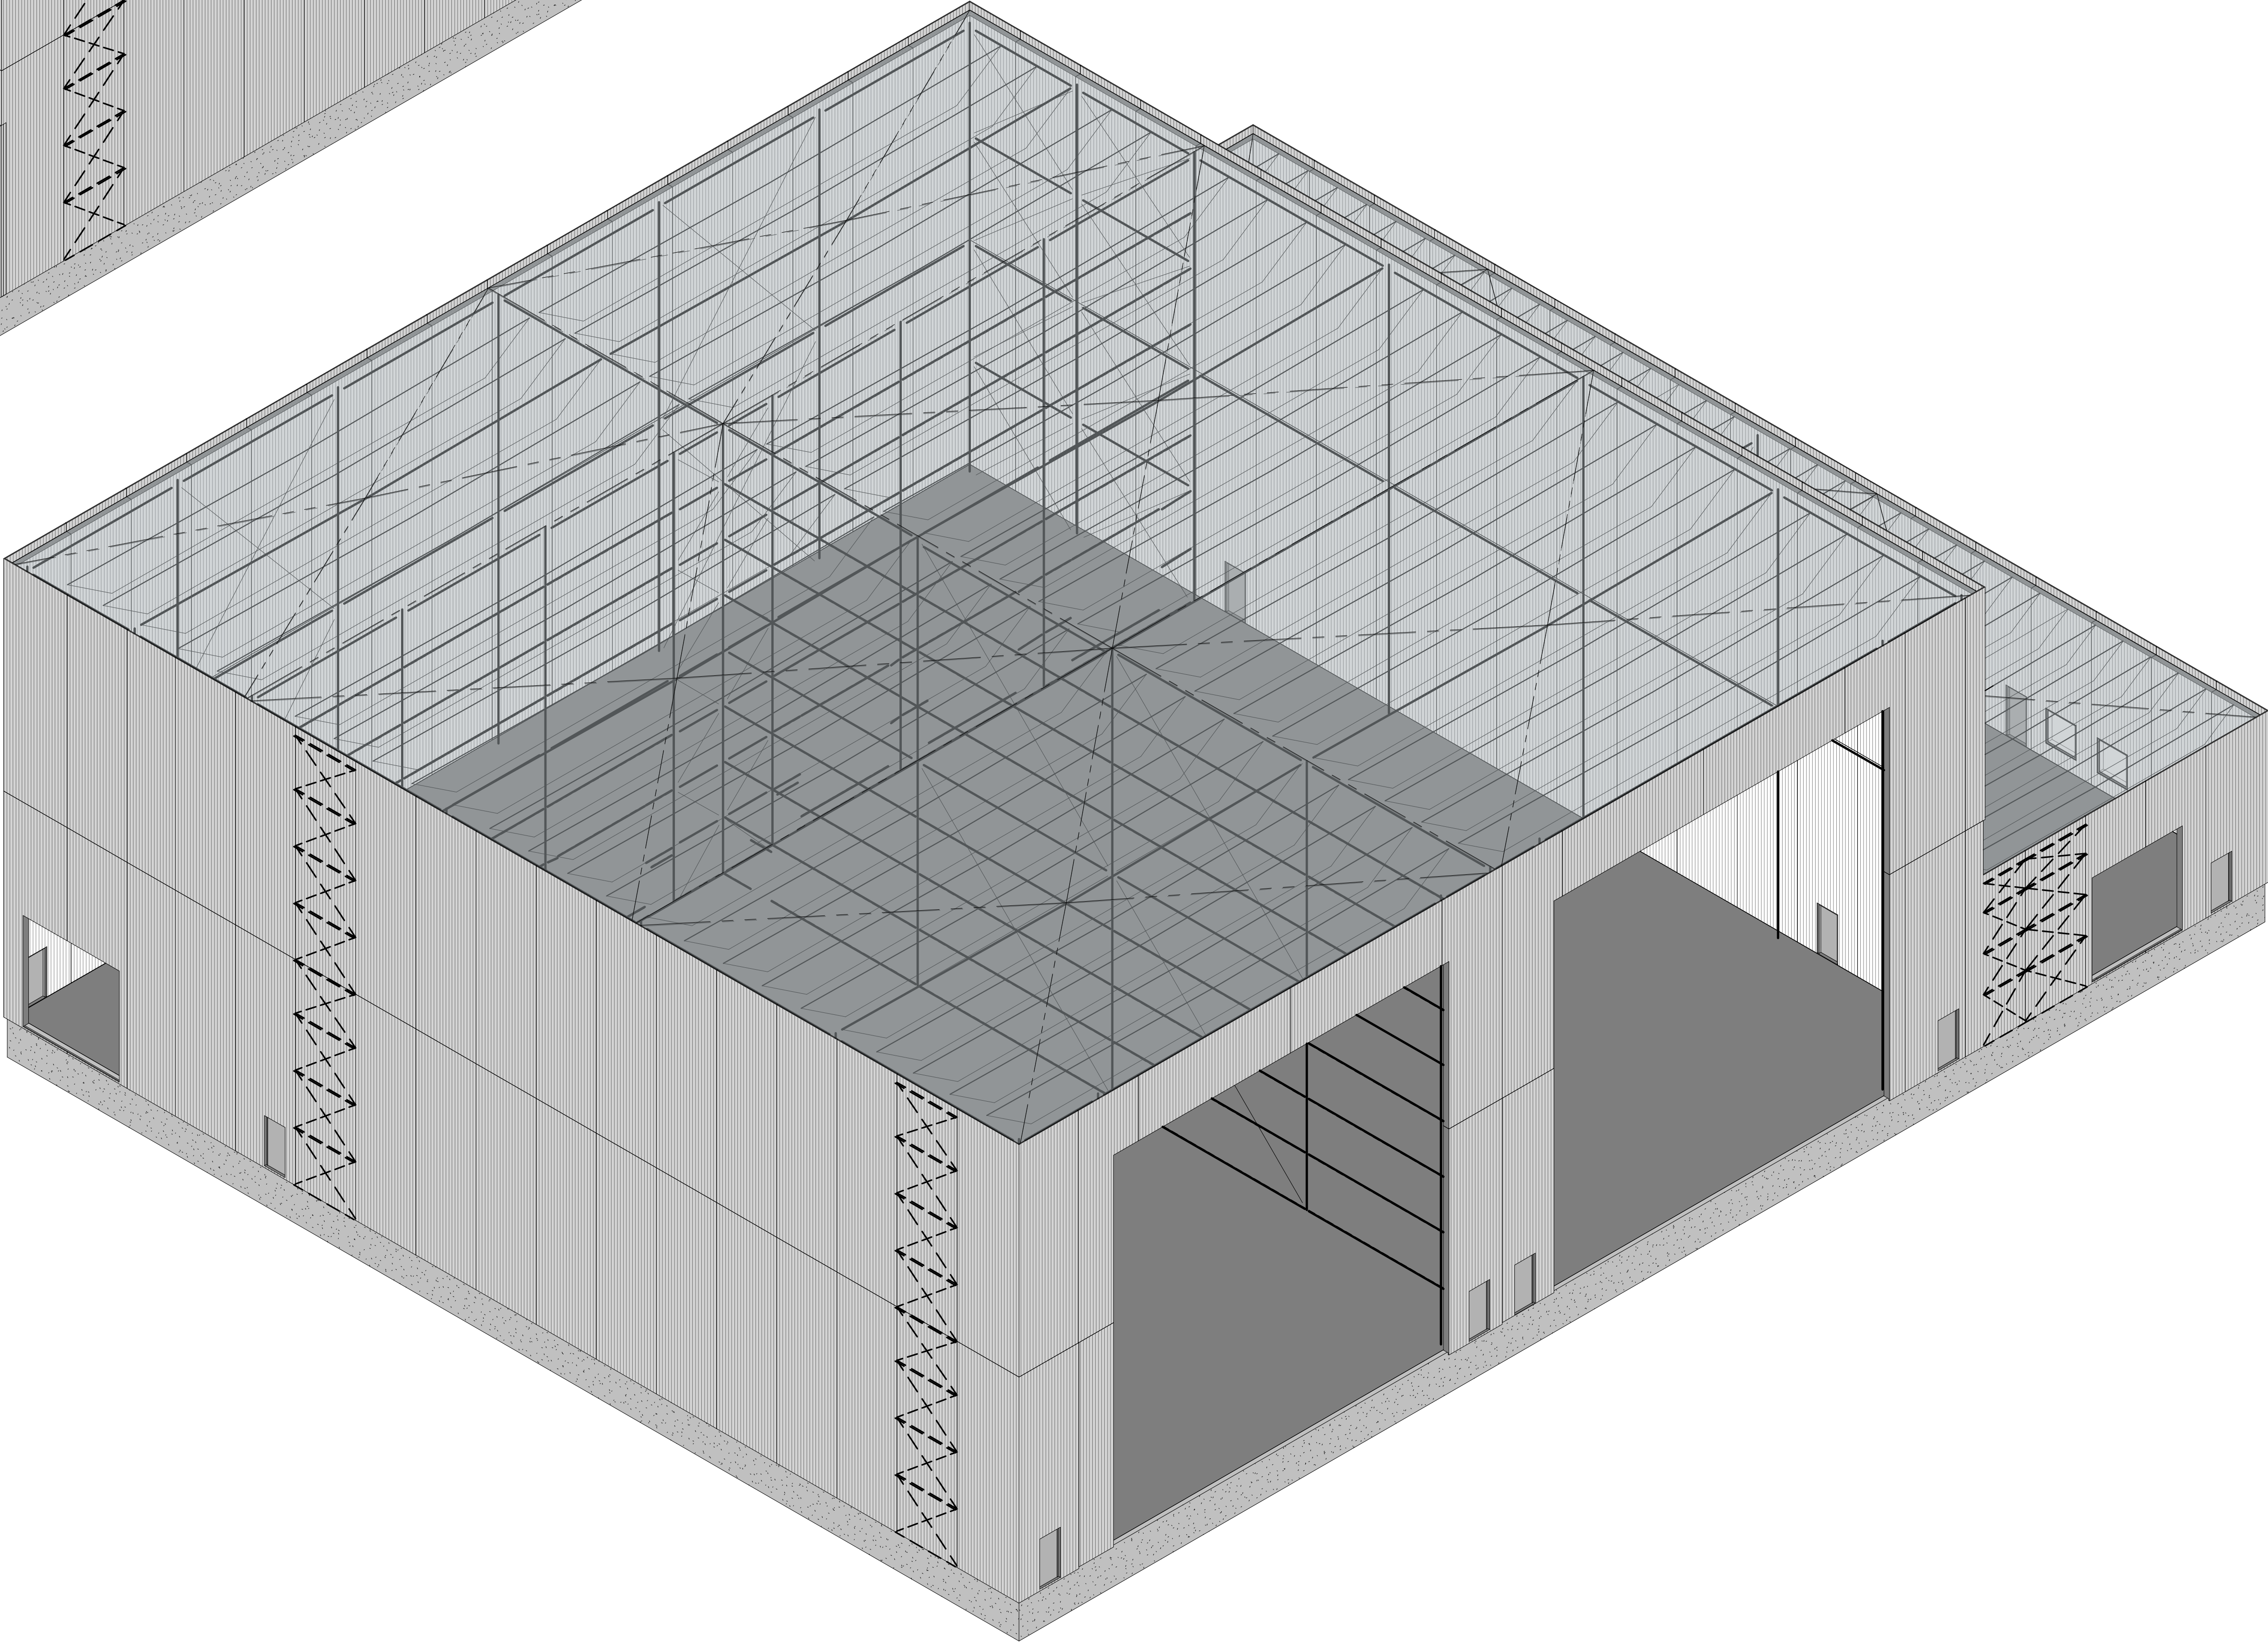

3D VIEW N-E

CONTRACTOR/RECTOR NOTE:
IT IS PROHIBITED TO MODIFY, COPY, REPRODUCE OR OTHERWISE
DISTRIBUTE THIS DRAWING OR ANY REPRESENTATION OF THIS
DRAWING, OR ANY MEDIA, INCLUDING ELECTRONIC, WITHOUT THE
PRIOR WRITTEN APPROVAL OF CANAM GROUP INC.

PRELIMINARY SHEET LIST	
EsMx001	PRELIMINARY SKETCH - 3D VIEWS
EsMx001	PRELIMINARY SKETCH - ROOF PLAN
EsMx001	PRELIMINARY SKETCH - ELEVATIONS
EsMx001	PRELIMINARY SKETCH - ELEVATION, WALL SECTION AND SCHEDULES


[Click here for 3D model](#)

PRELIMINARY

NOT TO BE USED FOR CONSTRUCTION

REVISION	DATE	DESCRIPTION	ISS	VER
PROJECT MANAGER				
		-		
		-		
		-		
DRAFTING				
DRAWN	DESIGNED	PROJECT ENGINEER	SCALE:	
Donald Piché				
CHECKED	CONSULTING ENGINEERS - ARCHITECTS		DATE (yyyy-mm-dd)	
			2026-04-22	

CUSTOMER: Pearson & Pearson Incorporated

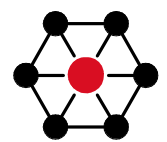 **CANAM**
11505, 1re Avenue, bureau 500, Saint-Georges Beauce
Québec, Canada, G5Y 7G5
Phone : (418) 228-8031
Toll free : (877) 499-6049
www.canam.com

PROFESSIONAL SEAL


PROJECT

Davie Shipyard - Paint and Blast facility
Lévis, QC


DRAWING TITLE

PRELIMINARY SKETCH - 3D VIEWS

CONTRACT NUMBER	DRAWING NUMBER	DIVISION	REVISION
P2026-091	EsMx001		

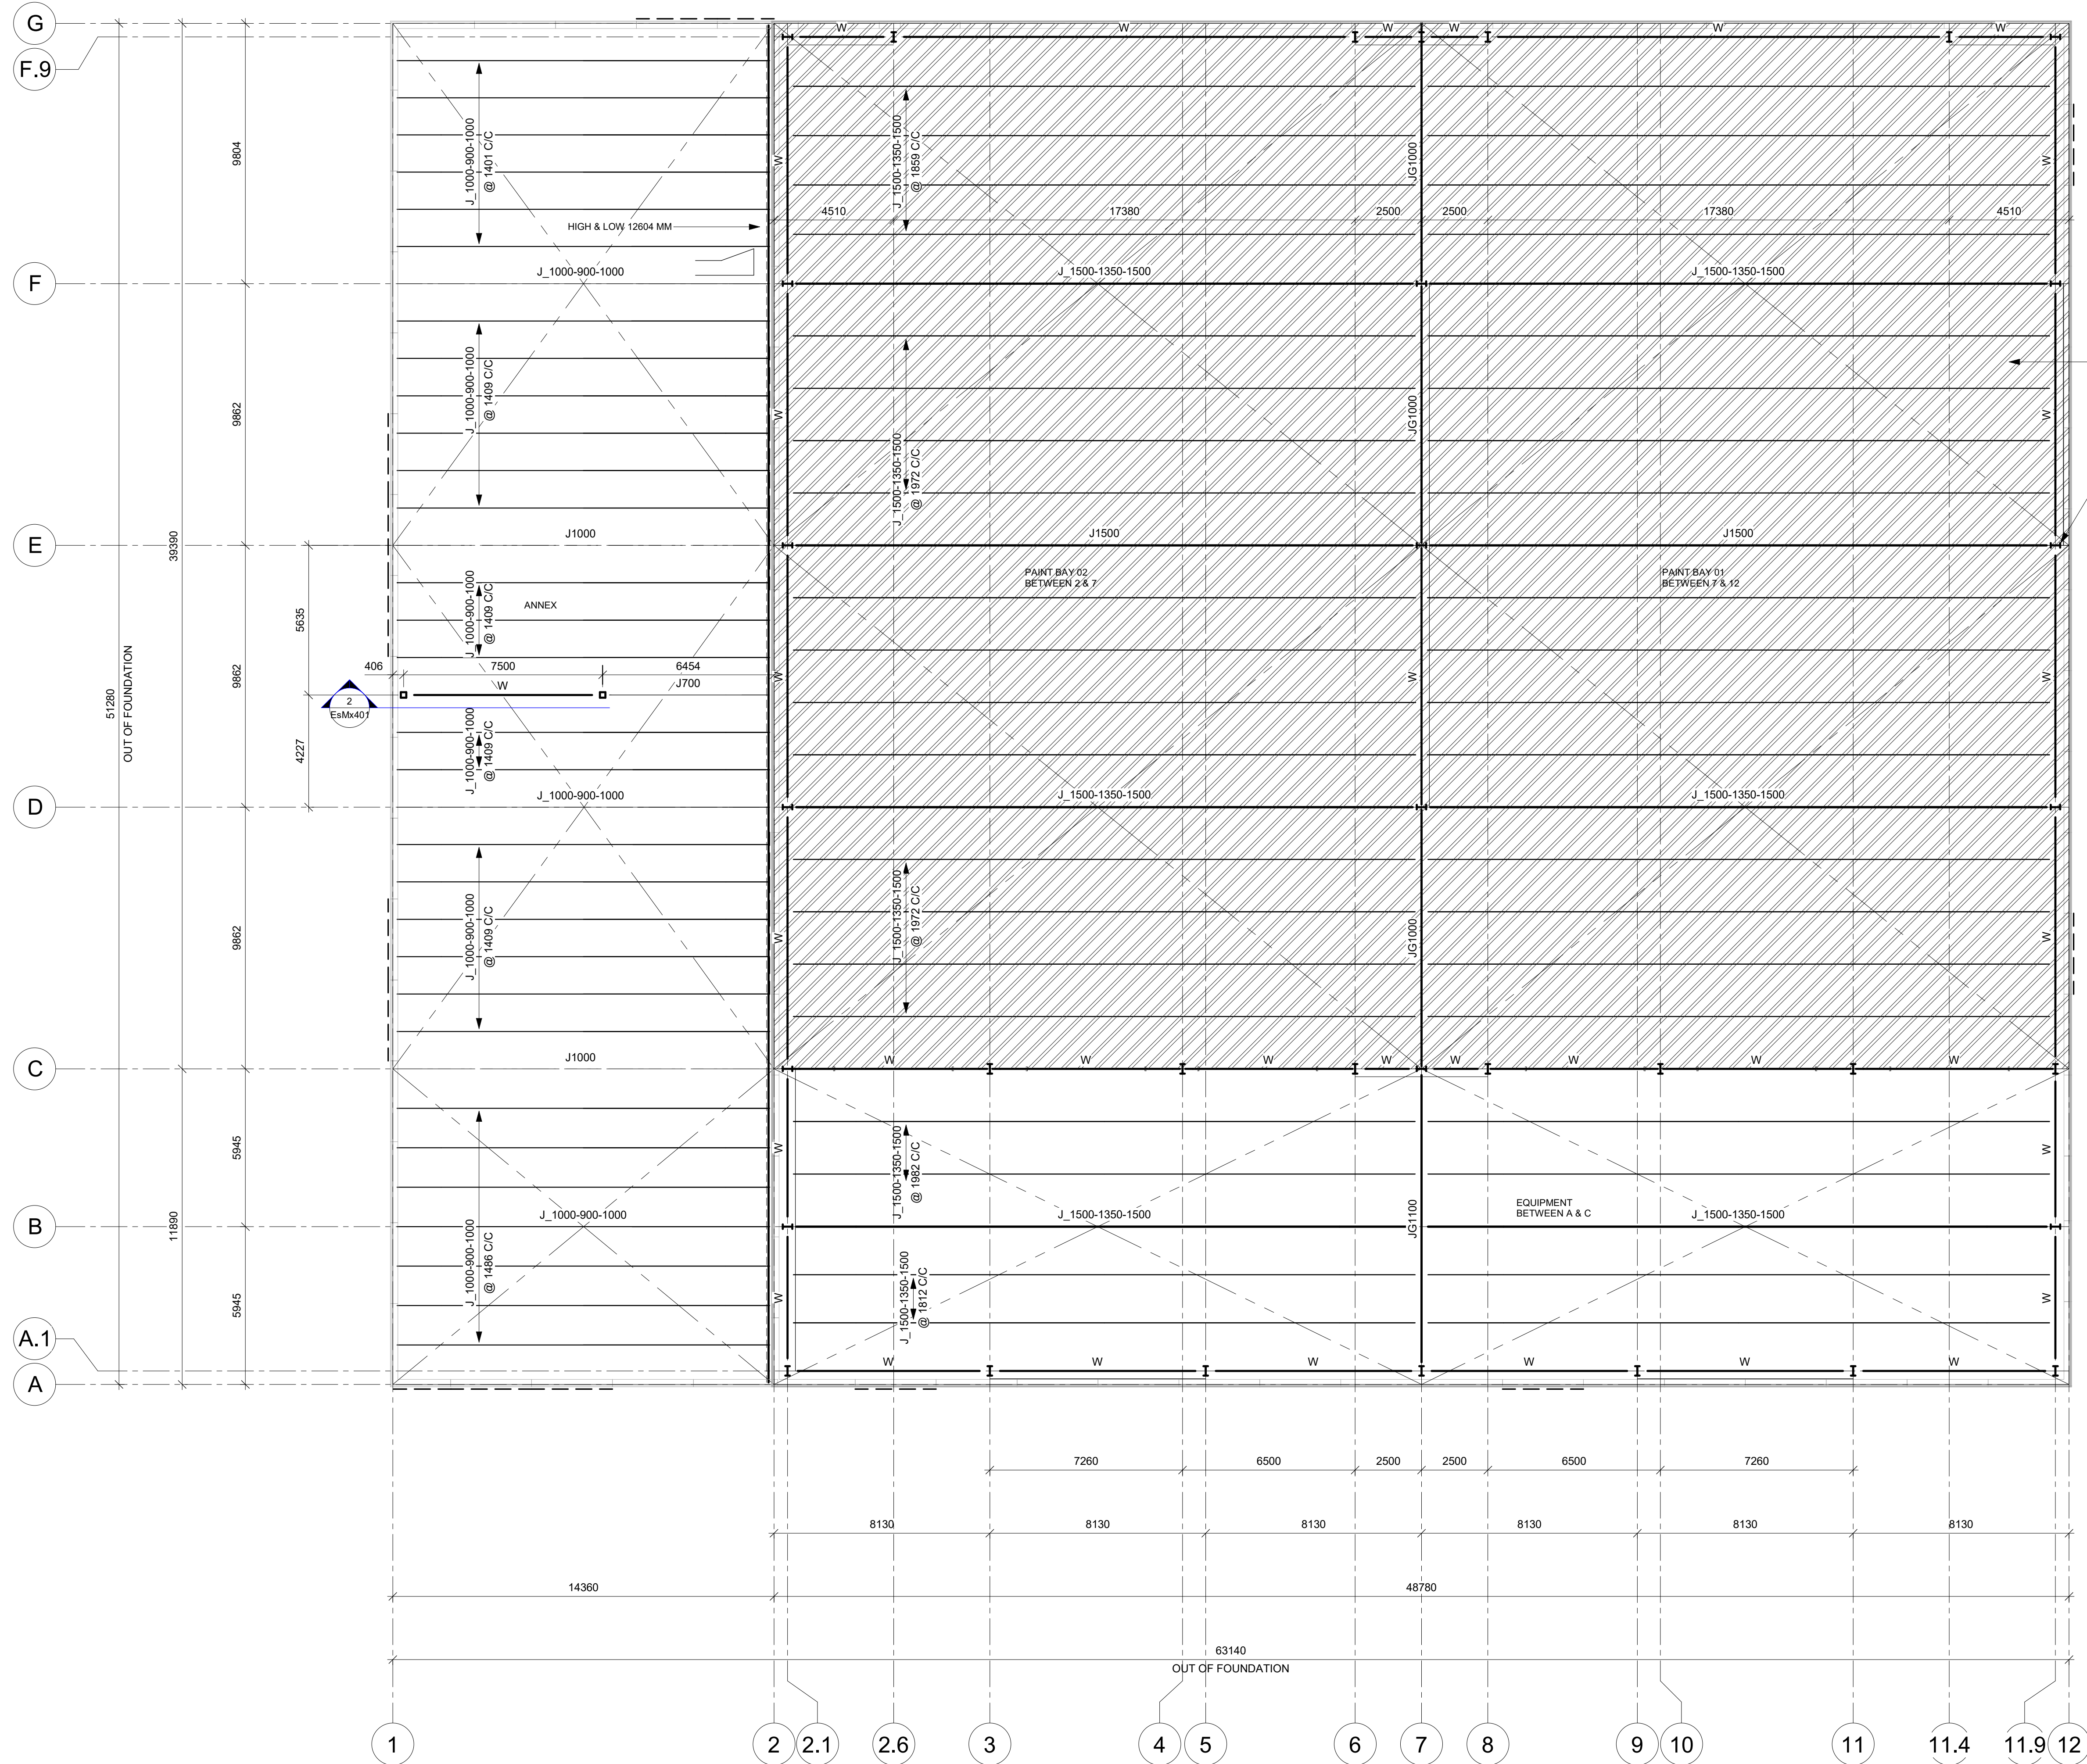

ROOF PLAN
1:125

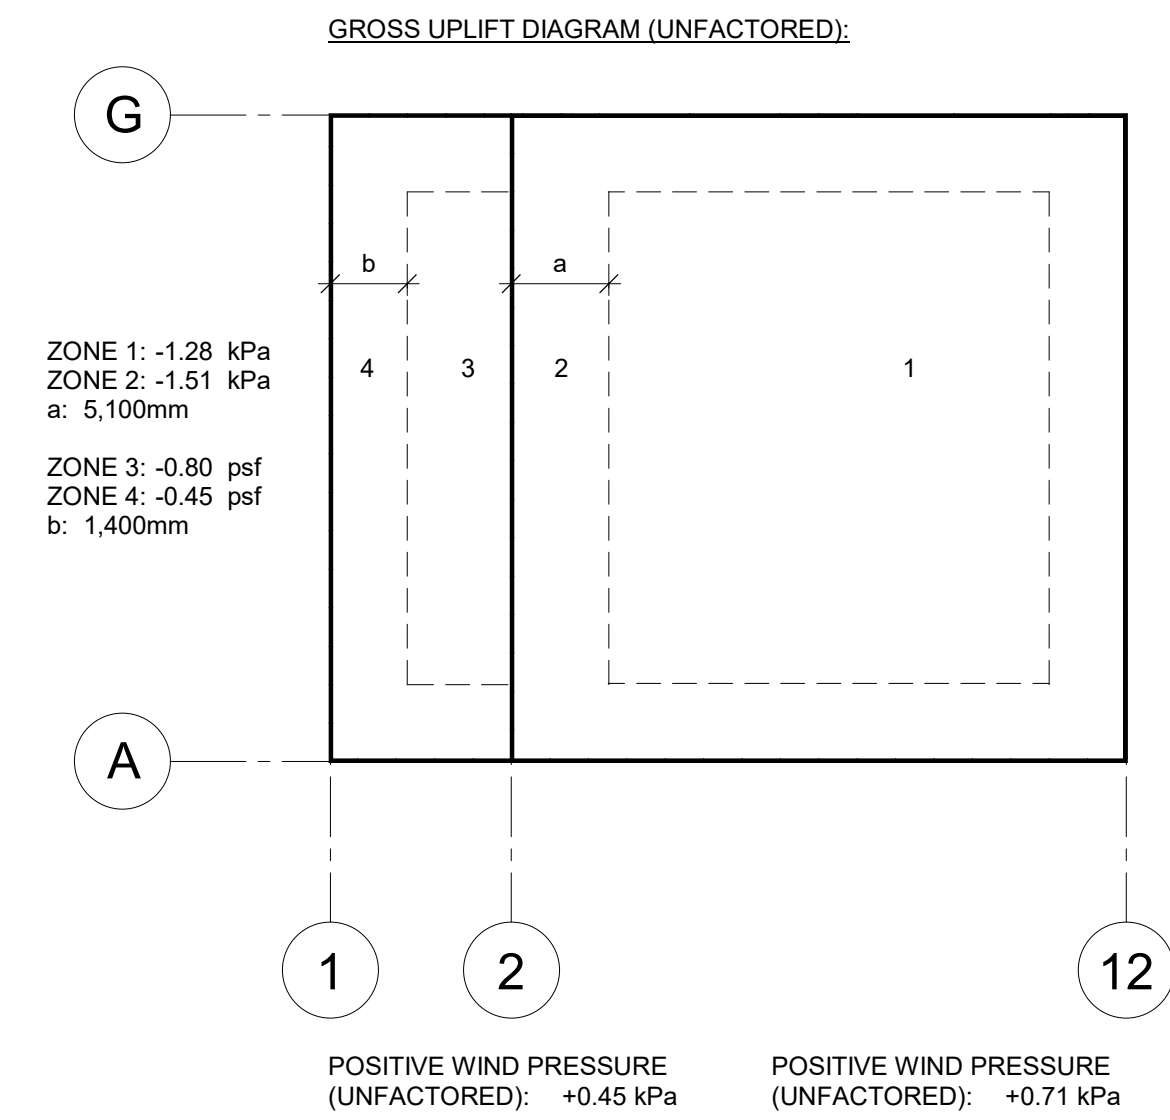

CONTRACTOR/RECTOR NOTE:
IT IS PROHIBITED TO MODIFY, COPY, REPRODUCE OR OTHERWISE
DISTRIBUTE THIS DRAWING OR ANY REPRESENTATION OF THIS
DRAWING, OR ANY MEDIA, INCLUDING ELECTRONIC, WITHOUT THE
PRIOR WRITTEN APPROVAL OF CANAM GROUP INC.


ROOF
TOP OF PLASTER RWL : -610
TOP OF PLASTER : -305
TOP OF SLAB : 0
TOP OF FOUNDATION : 0
CLEAR HEIGHT : 18200
TOP OF STEEL : 19700
PARAPET HEIGHT : 395
TOP OF PARAPET : 20056
LOADS
D.L. : 0.9k Pa
Coll. : 0.25 kPa
S₄ : 3.3 kPa
S_r : 0.6 kPa
C₀ x C_w : 0.8
Roof L.L. : 0.0 kPa
I_h : 1.0
Roof snow load : 3.24 kPa
I_w : 1.0
Wind q = 150 : 0.41 kPa
Seismic (Site class: D (Assumed))
I_s : 1.0
S_h(0.2) : 0.747
S_h(0.5) : 0.591
S_h(1.0) : 0.366
S_h(2.0) : 0.171
S_h(5.0) : 0.048
S_h(10.0) : 0.151
PGA : 0.433
PGV : 0.420

ANNEX
TOP OF PLASTER RWL : -610
TOP OF PLASTER : -305
TOP OF SLAB : 0
TOP OF FOUNDATION : 0
CLEAR HEIGHT : 6096
TOP OF STEEL : 7096
PARAPET HEIGHT : 395
TOP OF PARAPET : 7452






• Code Applicable : National building Code of Canada
Quebec Building Code, latest adopted editions
Code of Standard Practice CBC
• Assumed soil site class: D
• NOTE:
1. If, however, the seismic site class is determined to be E or F according to the
geotechnical report, the preliminary structural concept (location and geometry
of bracings, etc.) must be validated and coordinated by a Canam's engineer.

PRELIMINARY

NOT TO BE USED FOR CONSTRUCTION

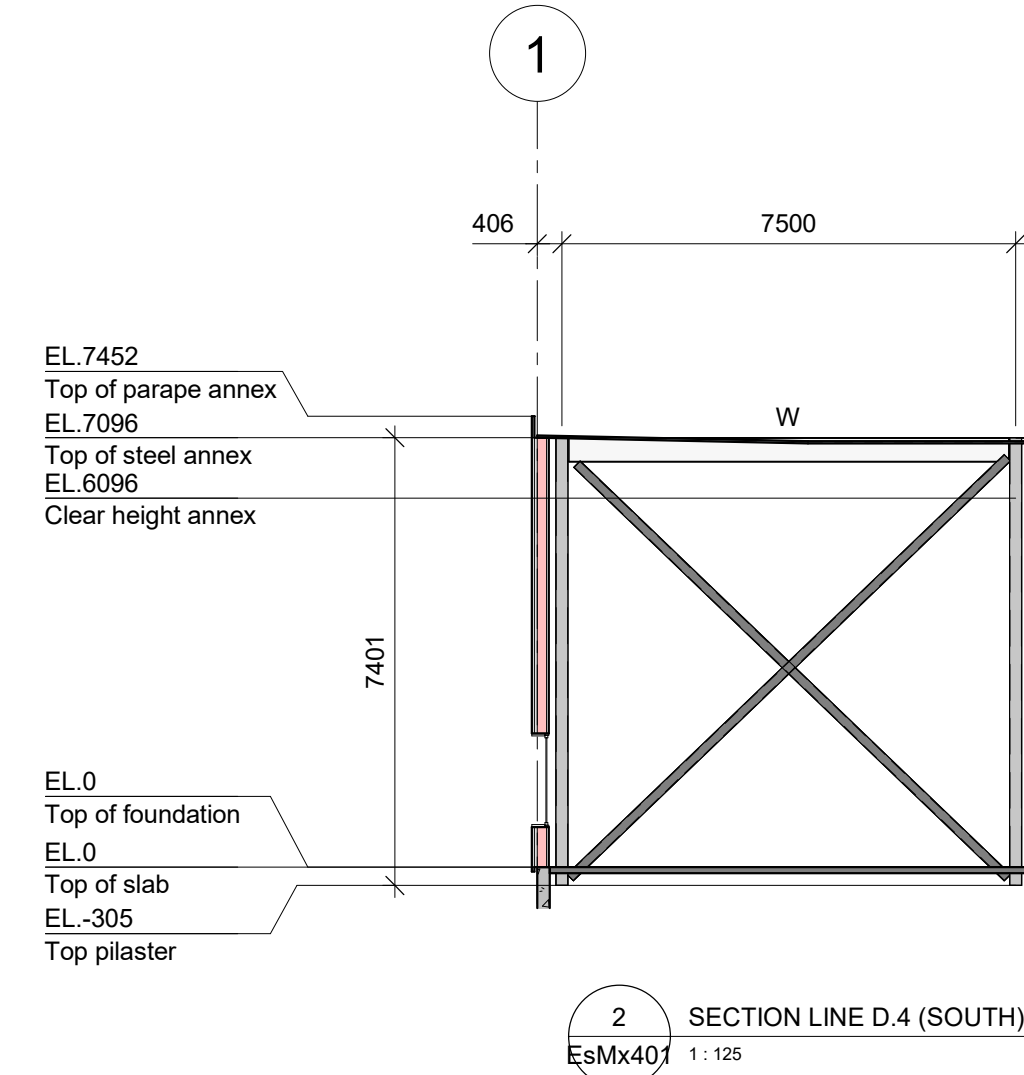

REVISION	DATE	DESCRIPTION	DESIGN	VER
		-		
		-		
		-		
		-		
PROJECT MANAGER				

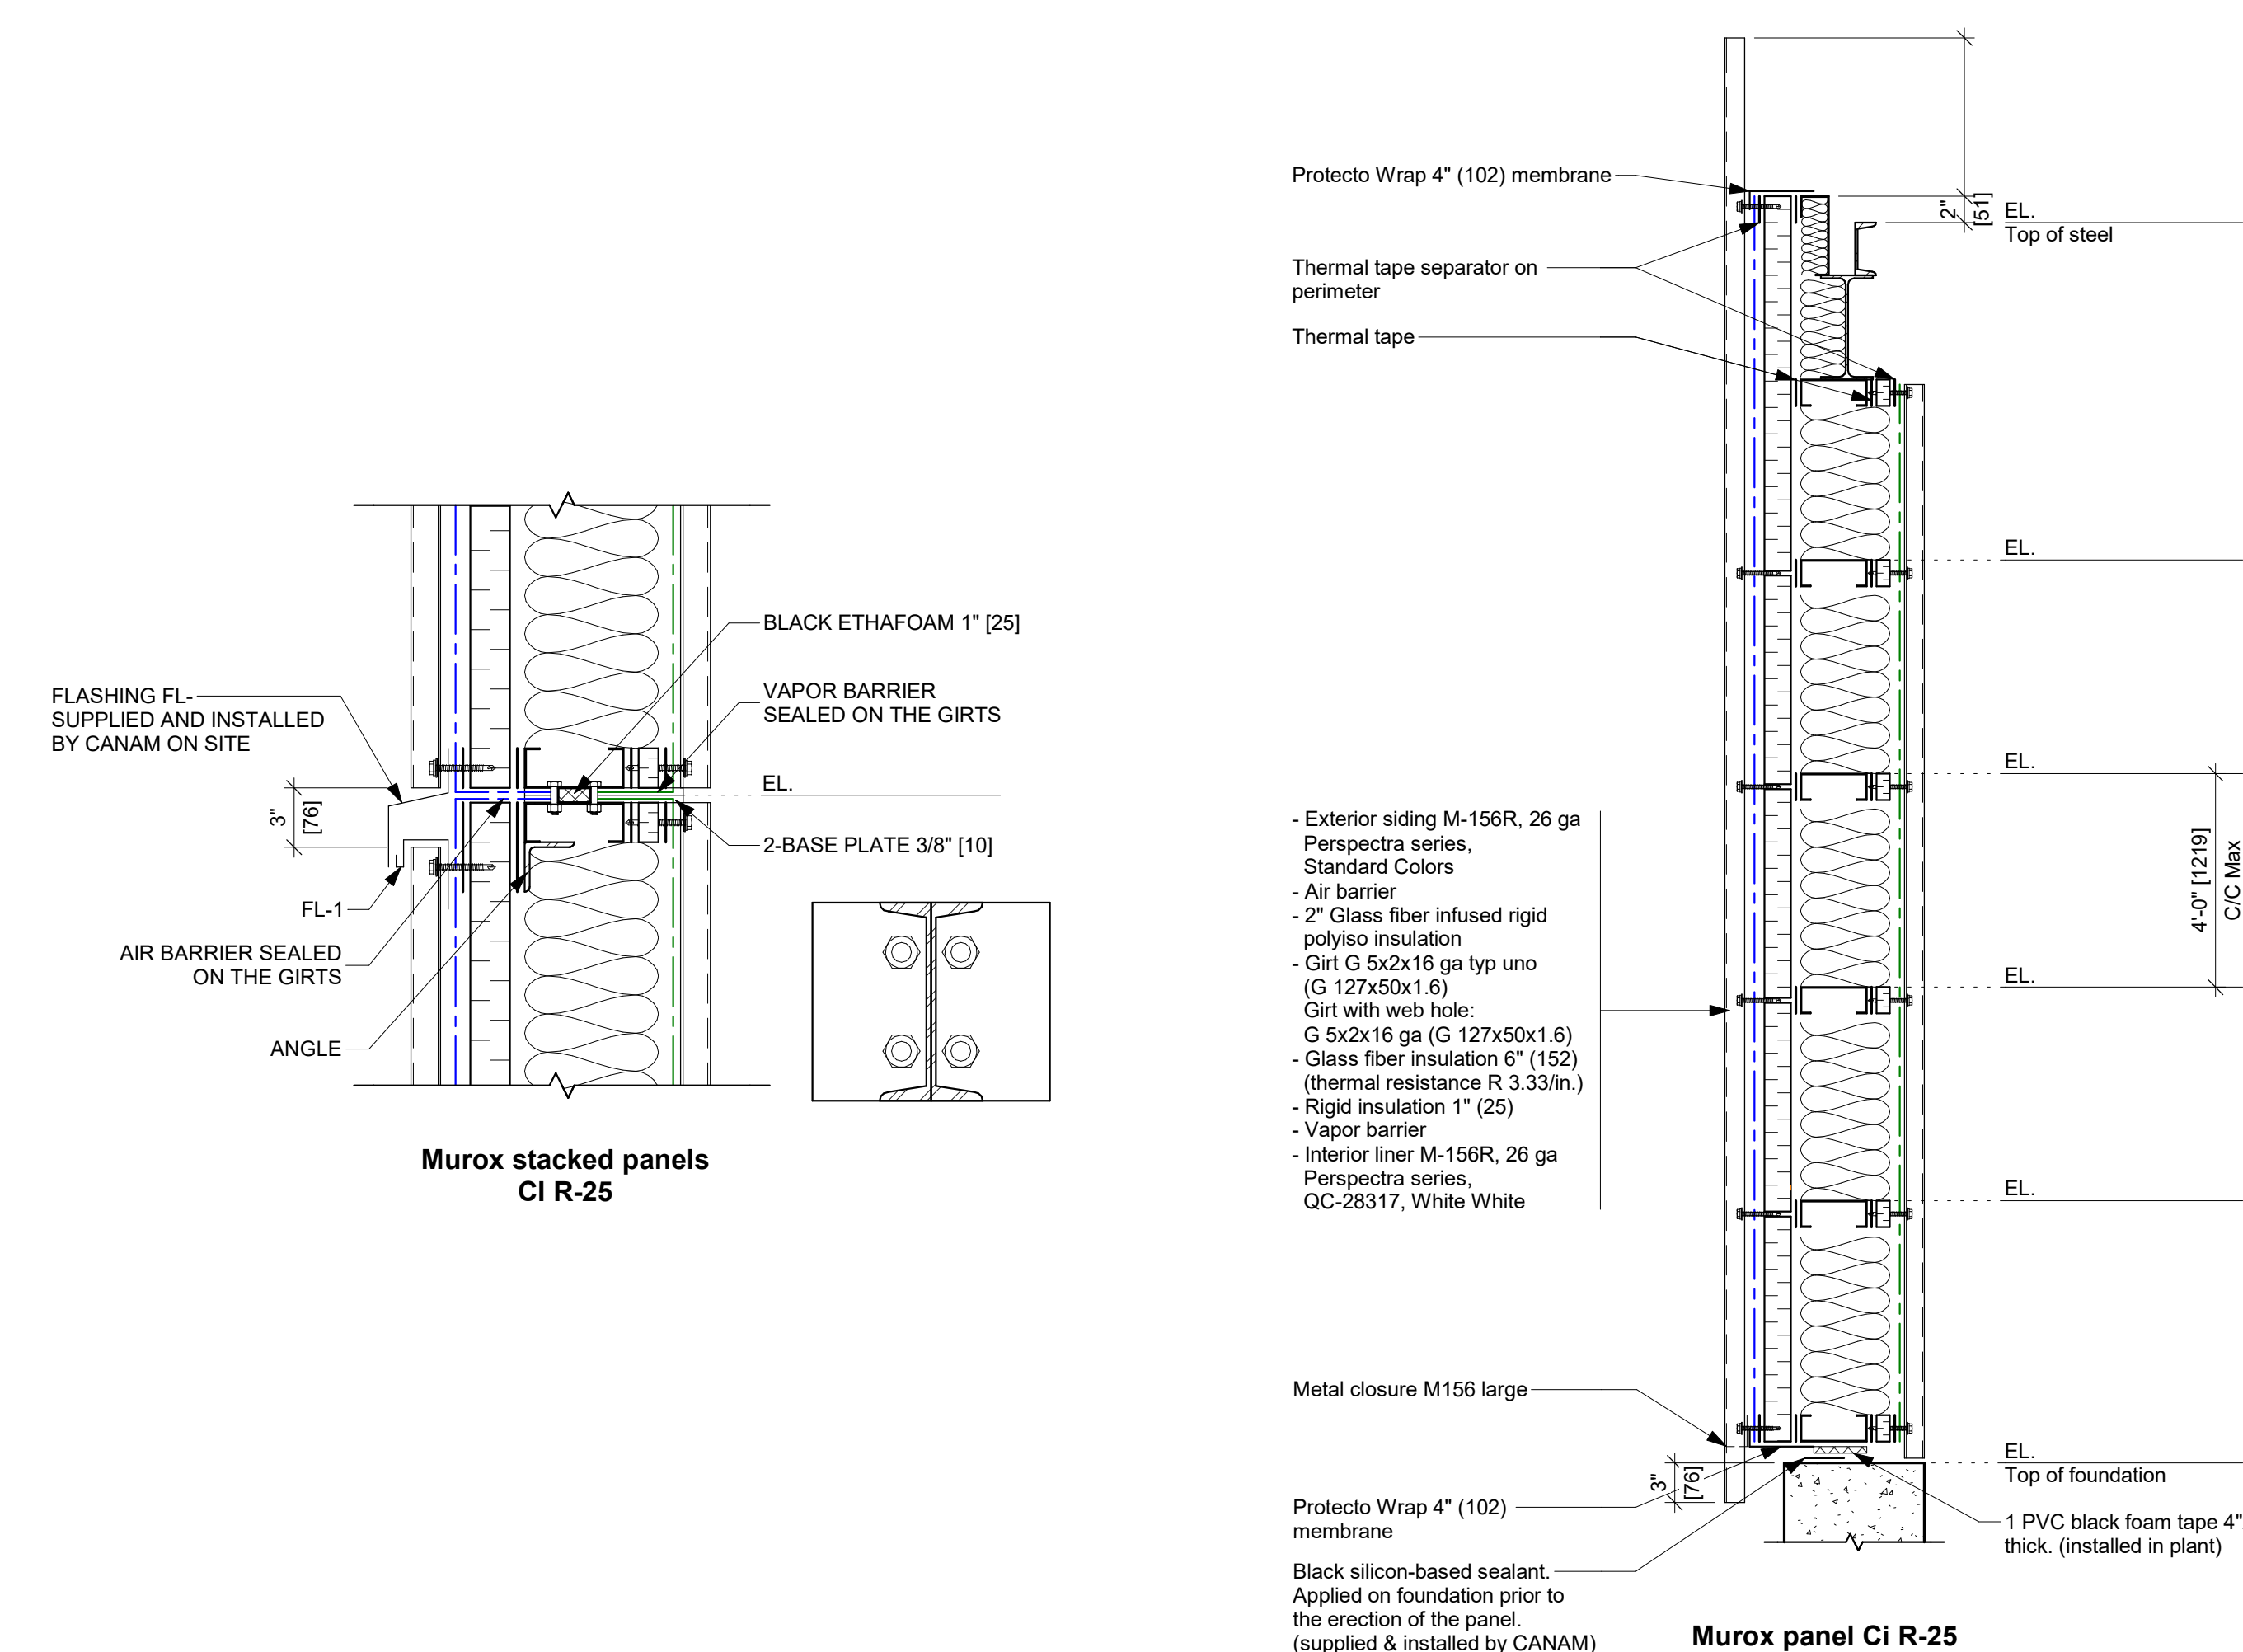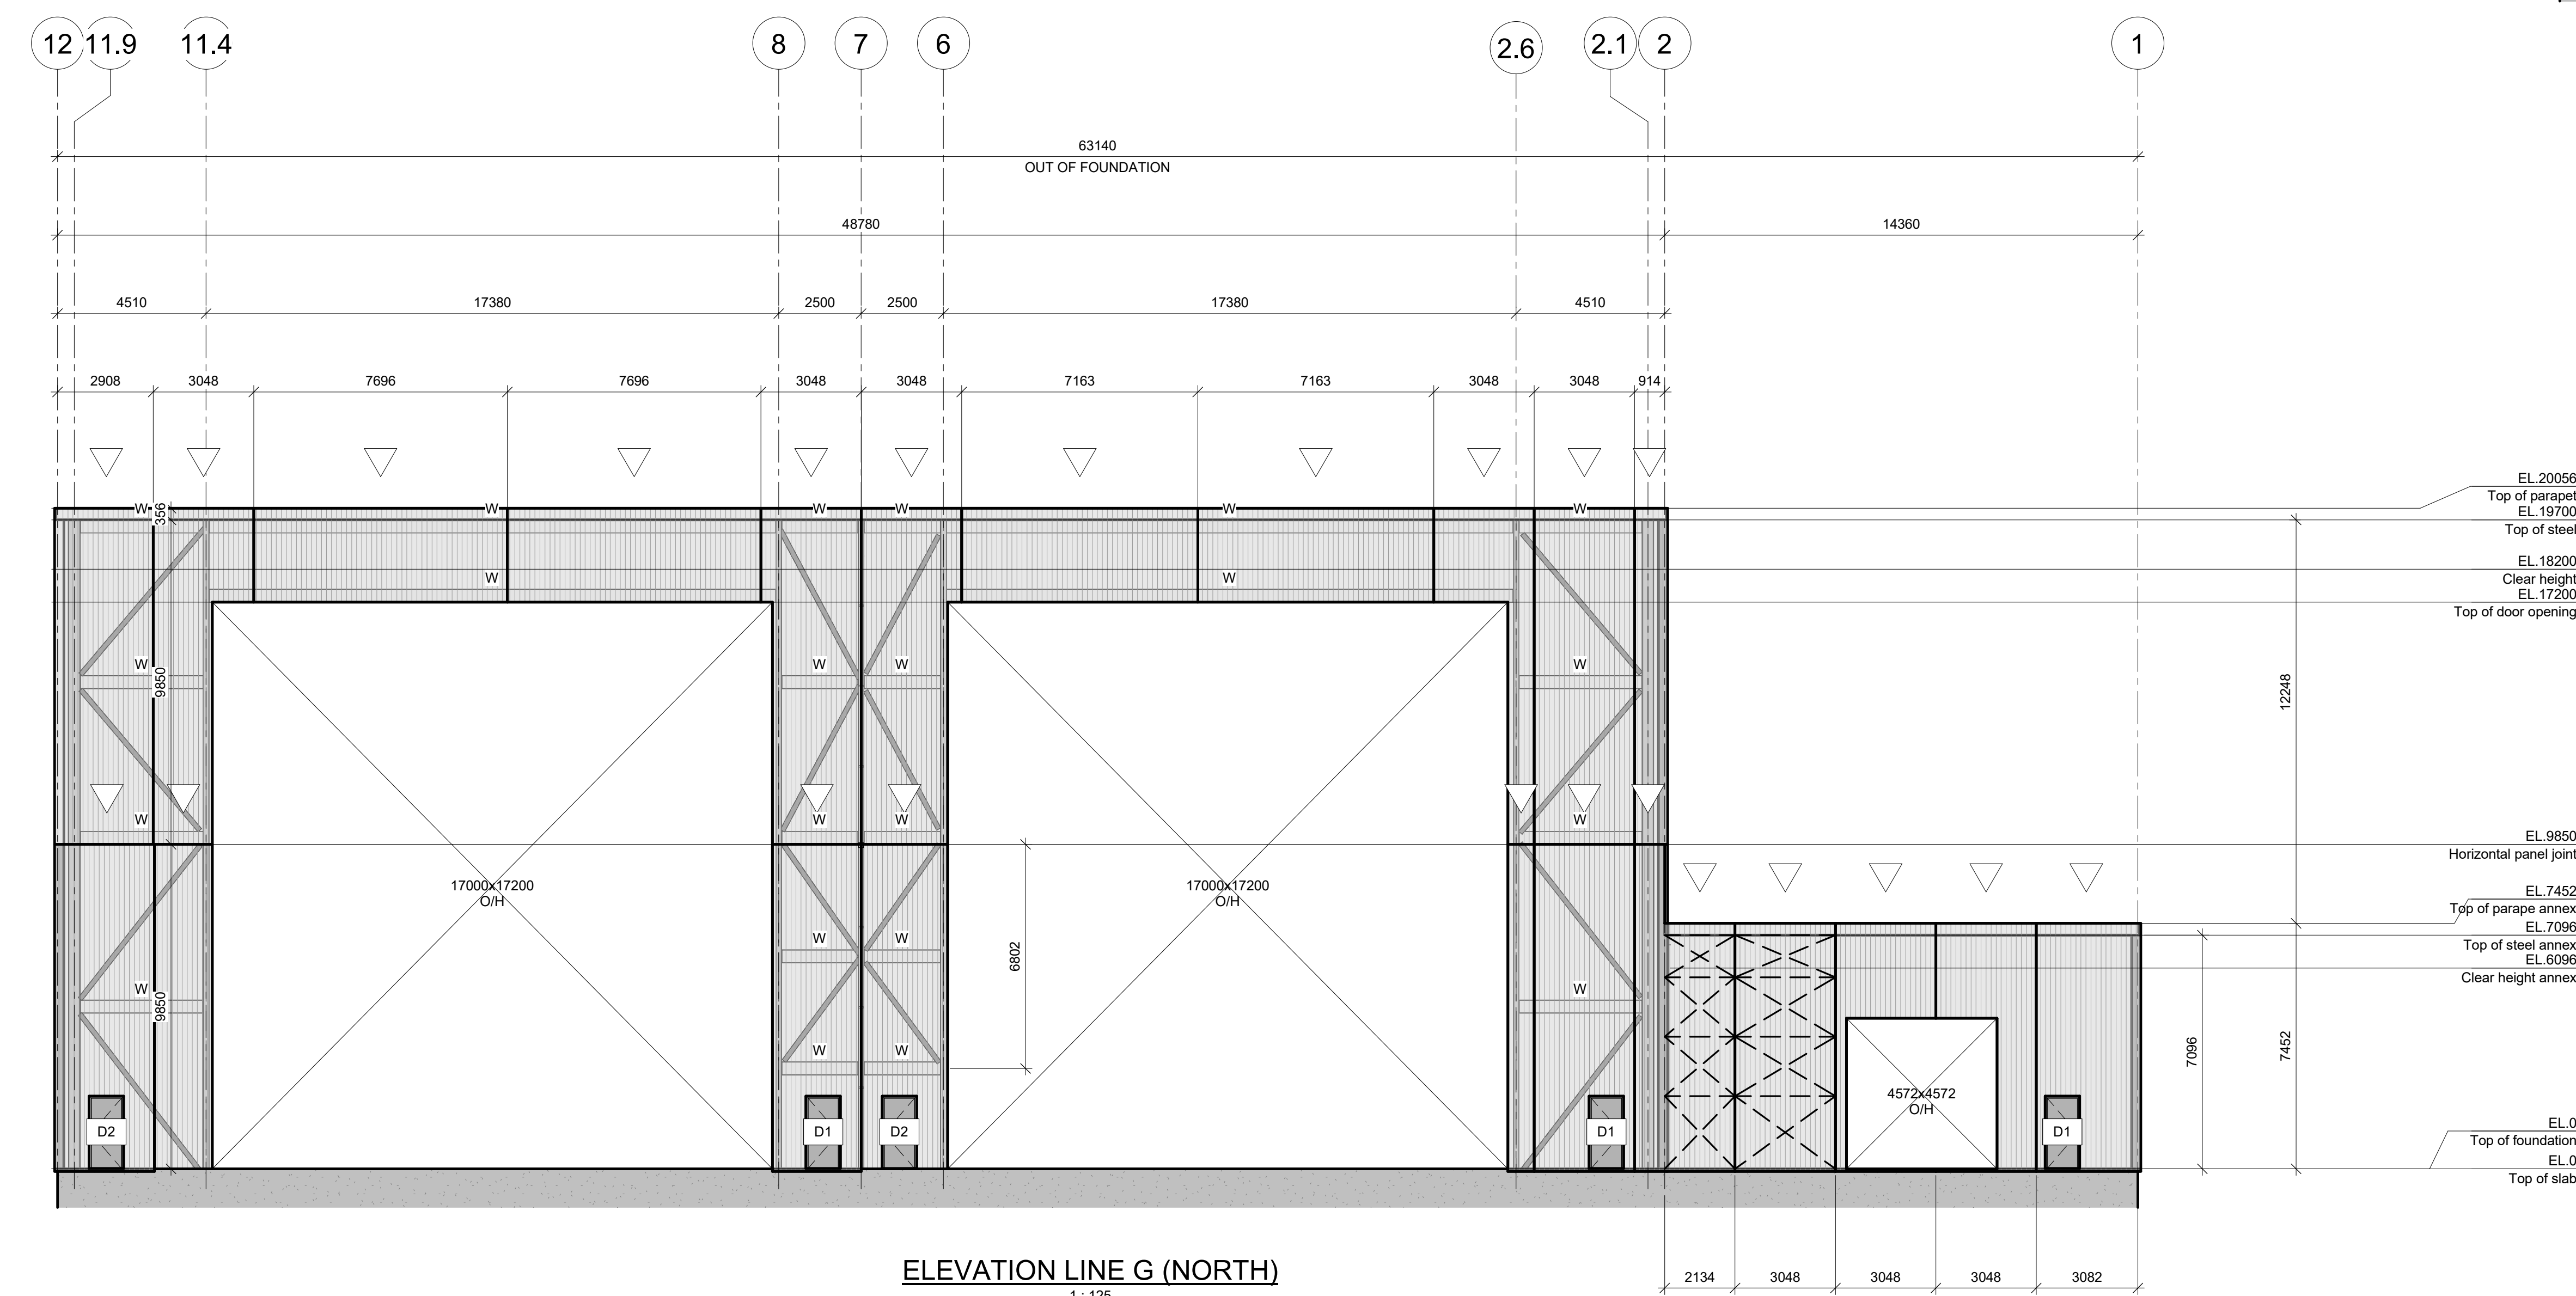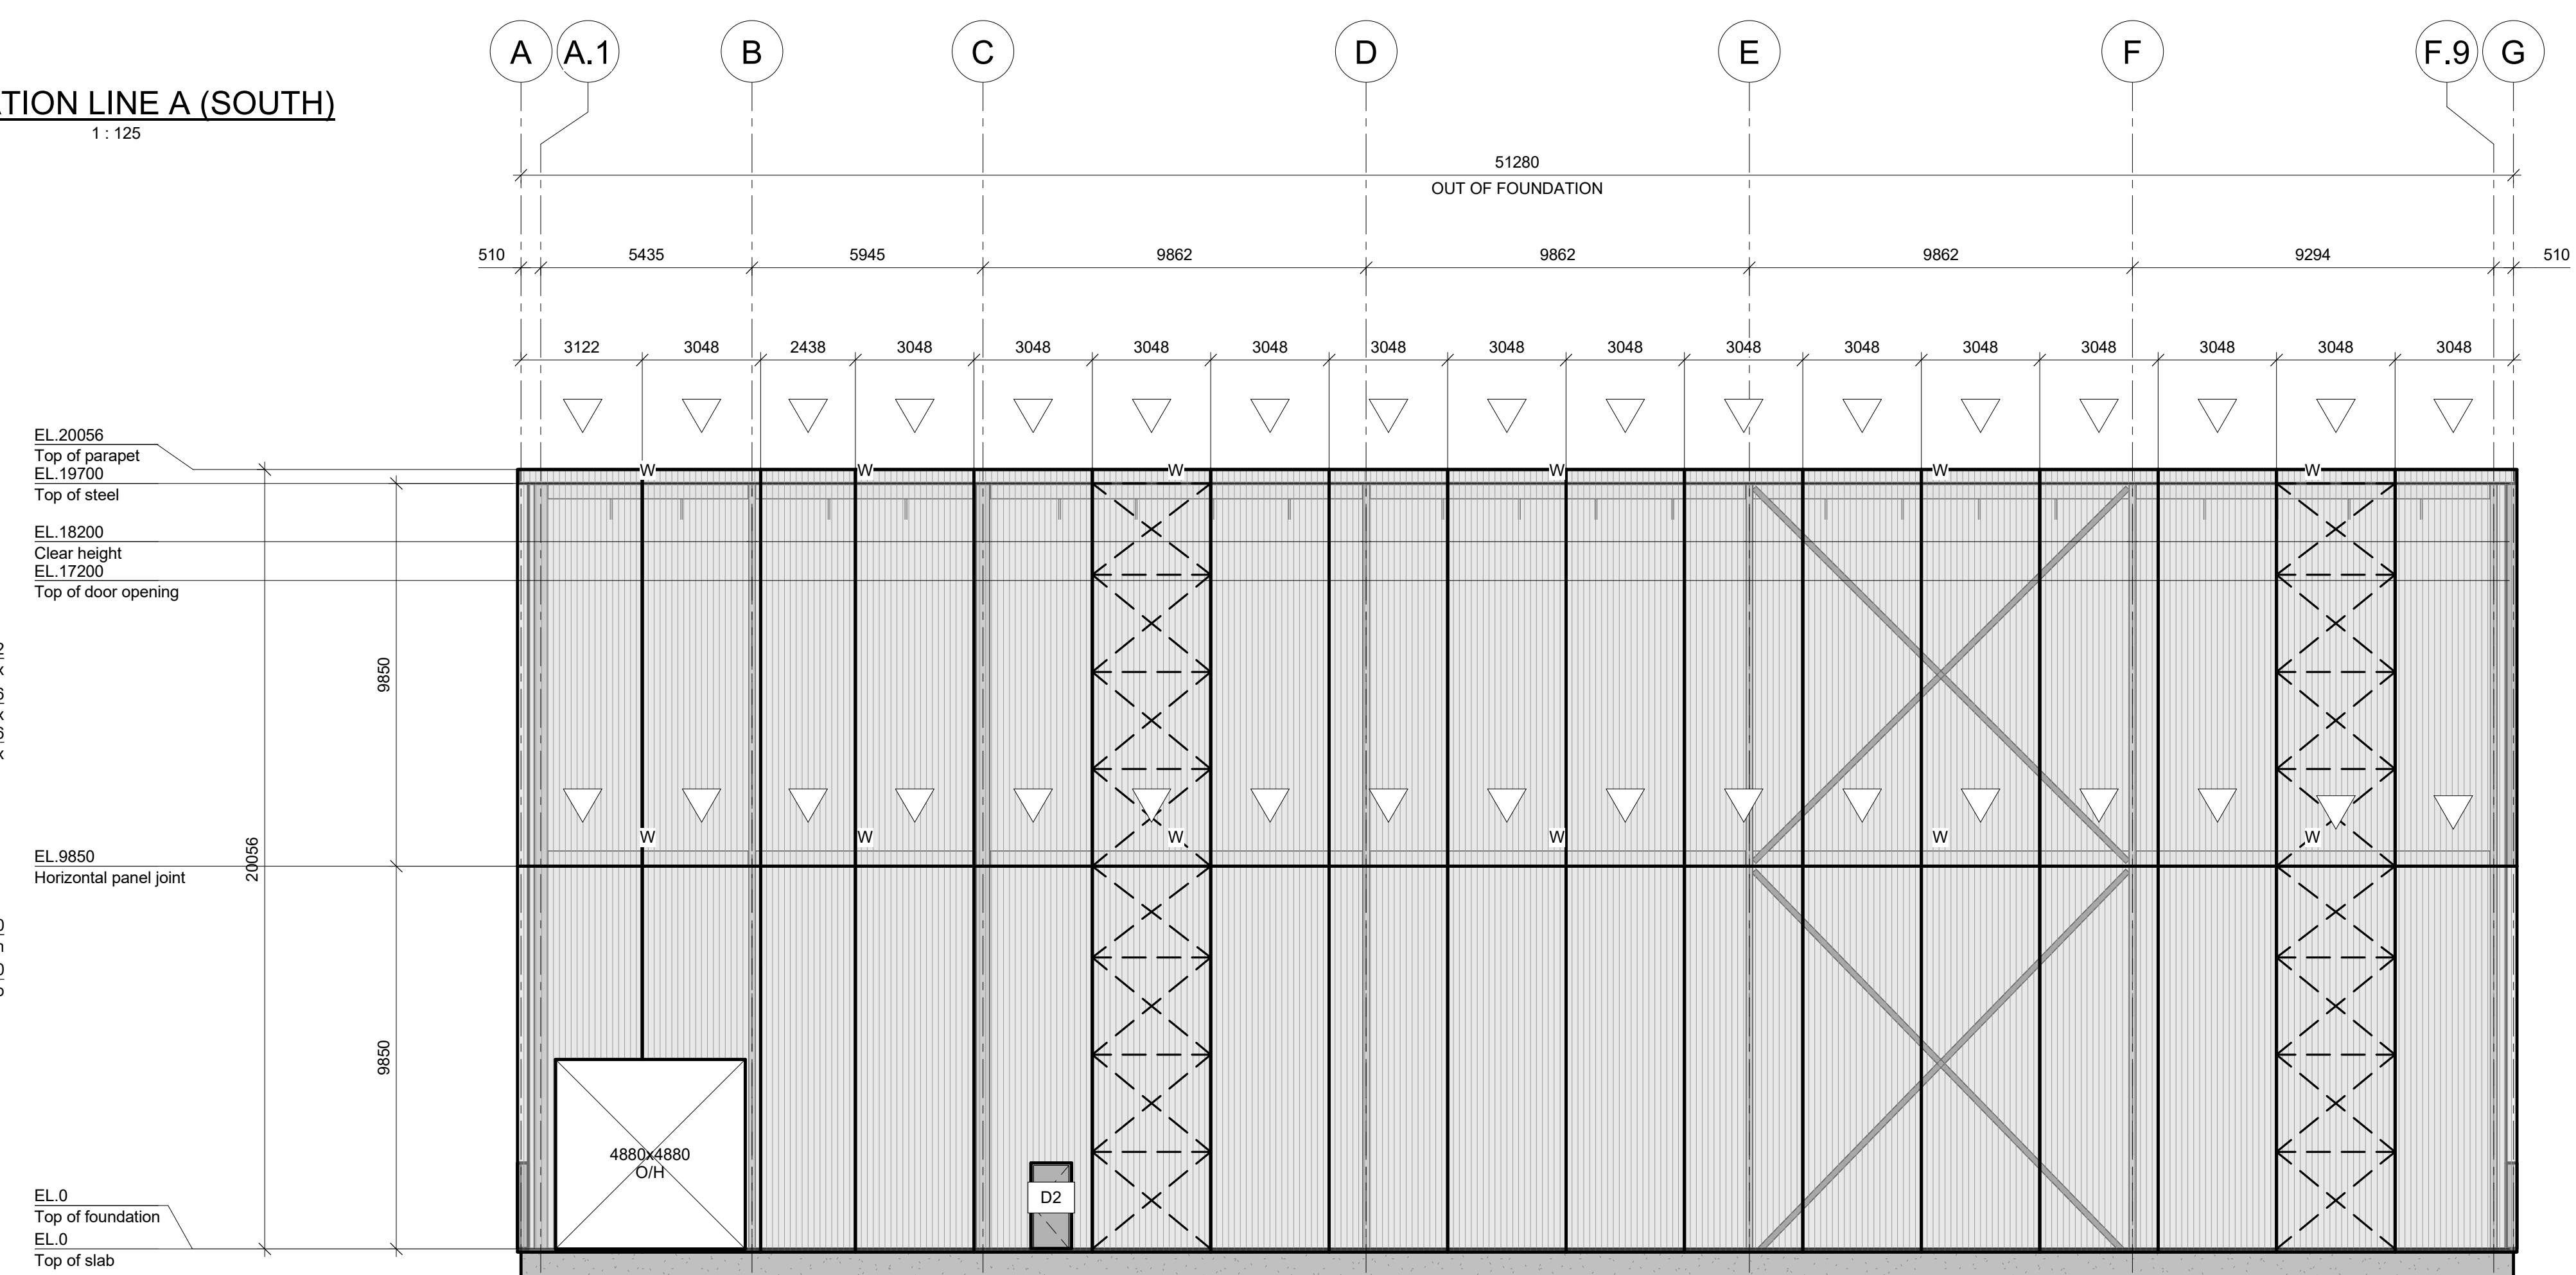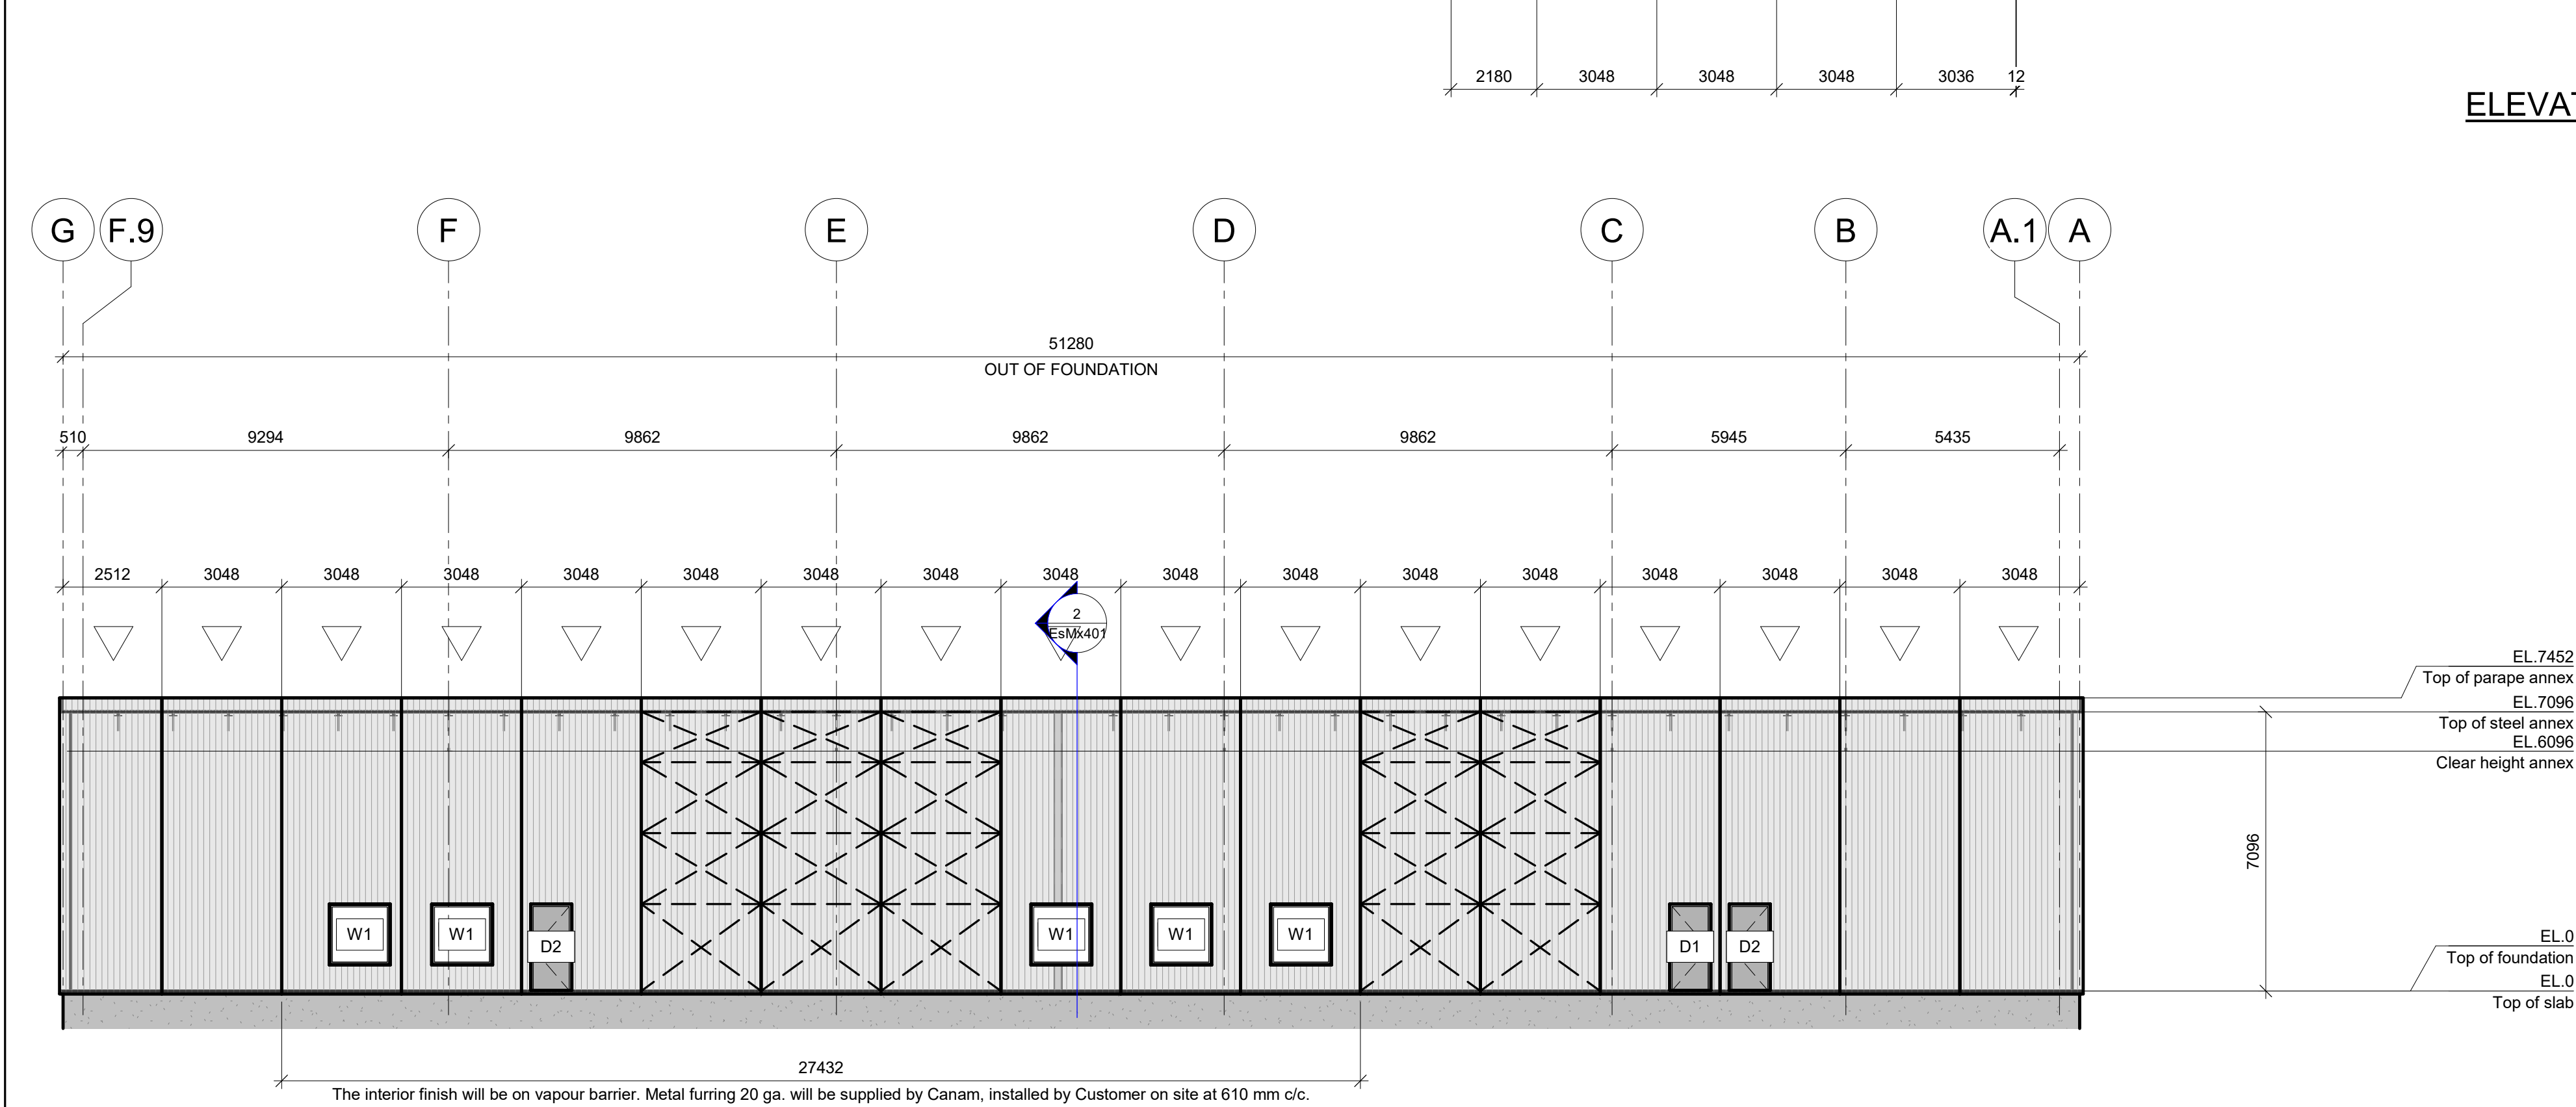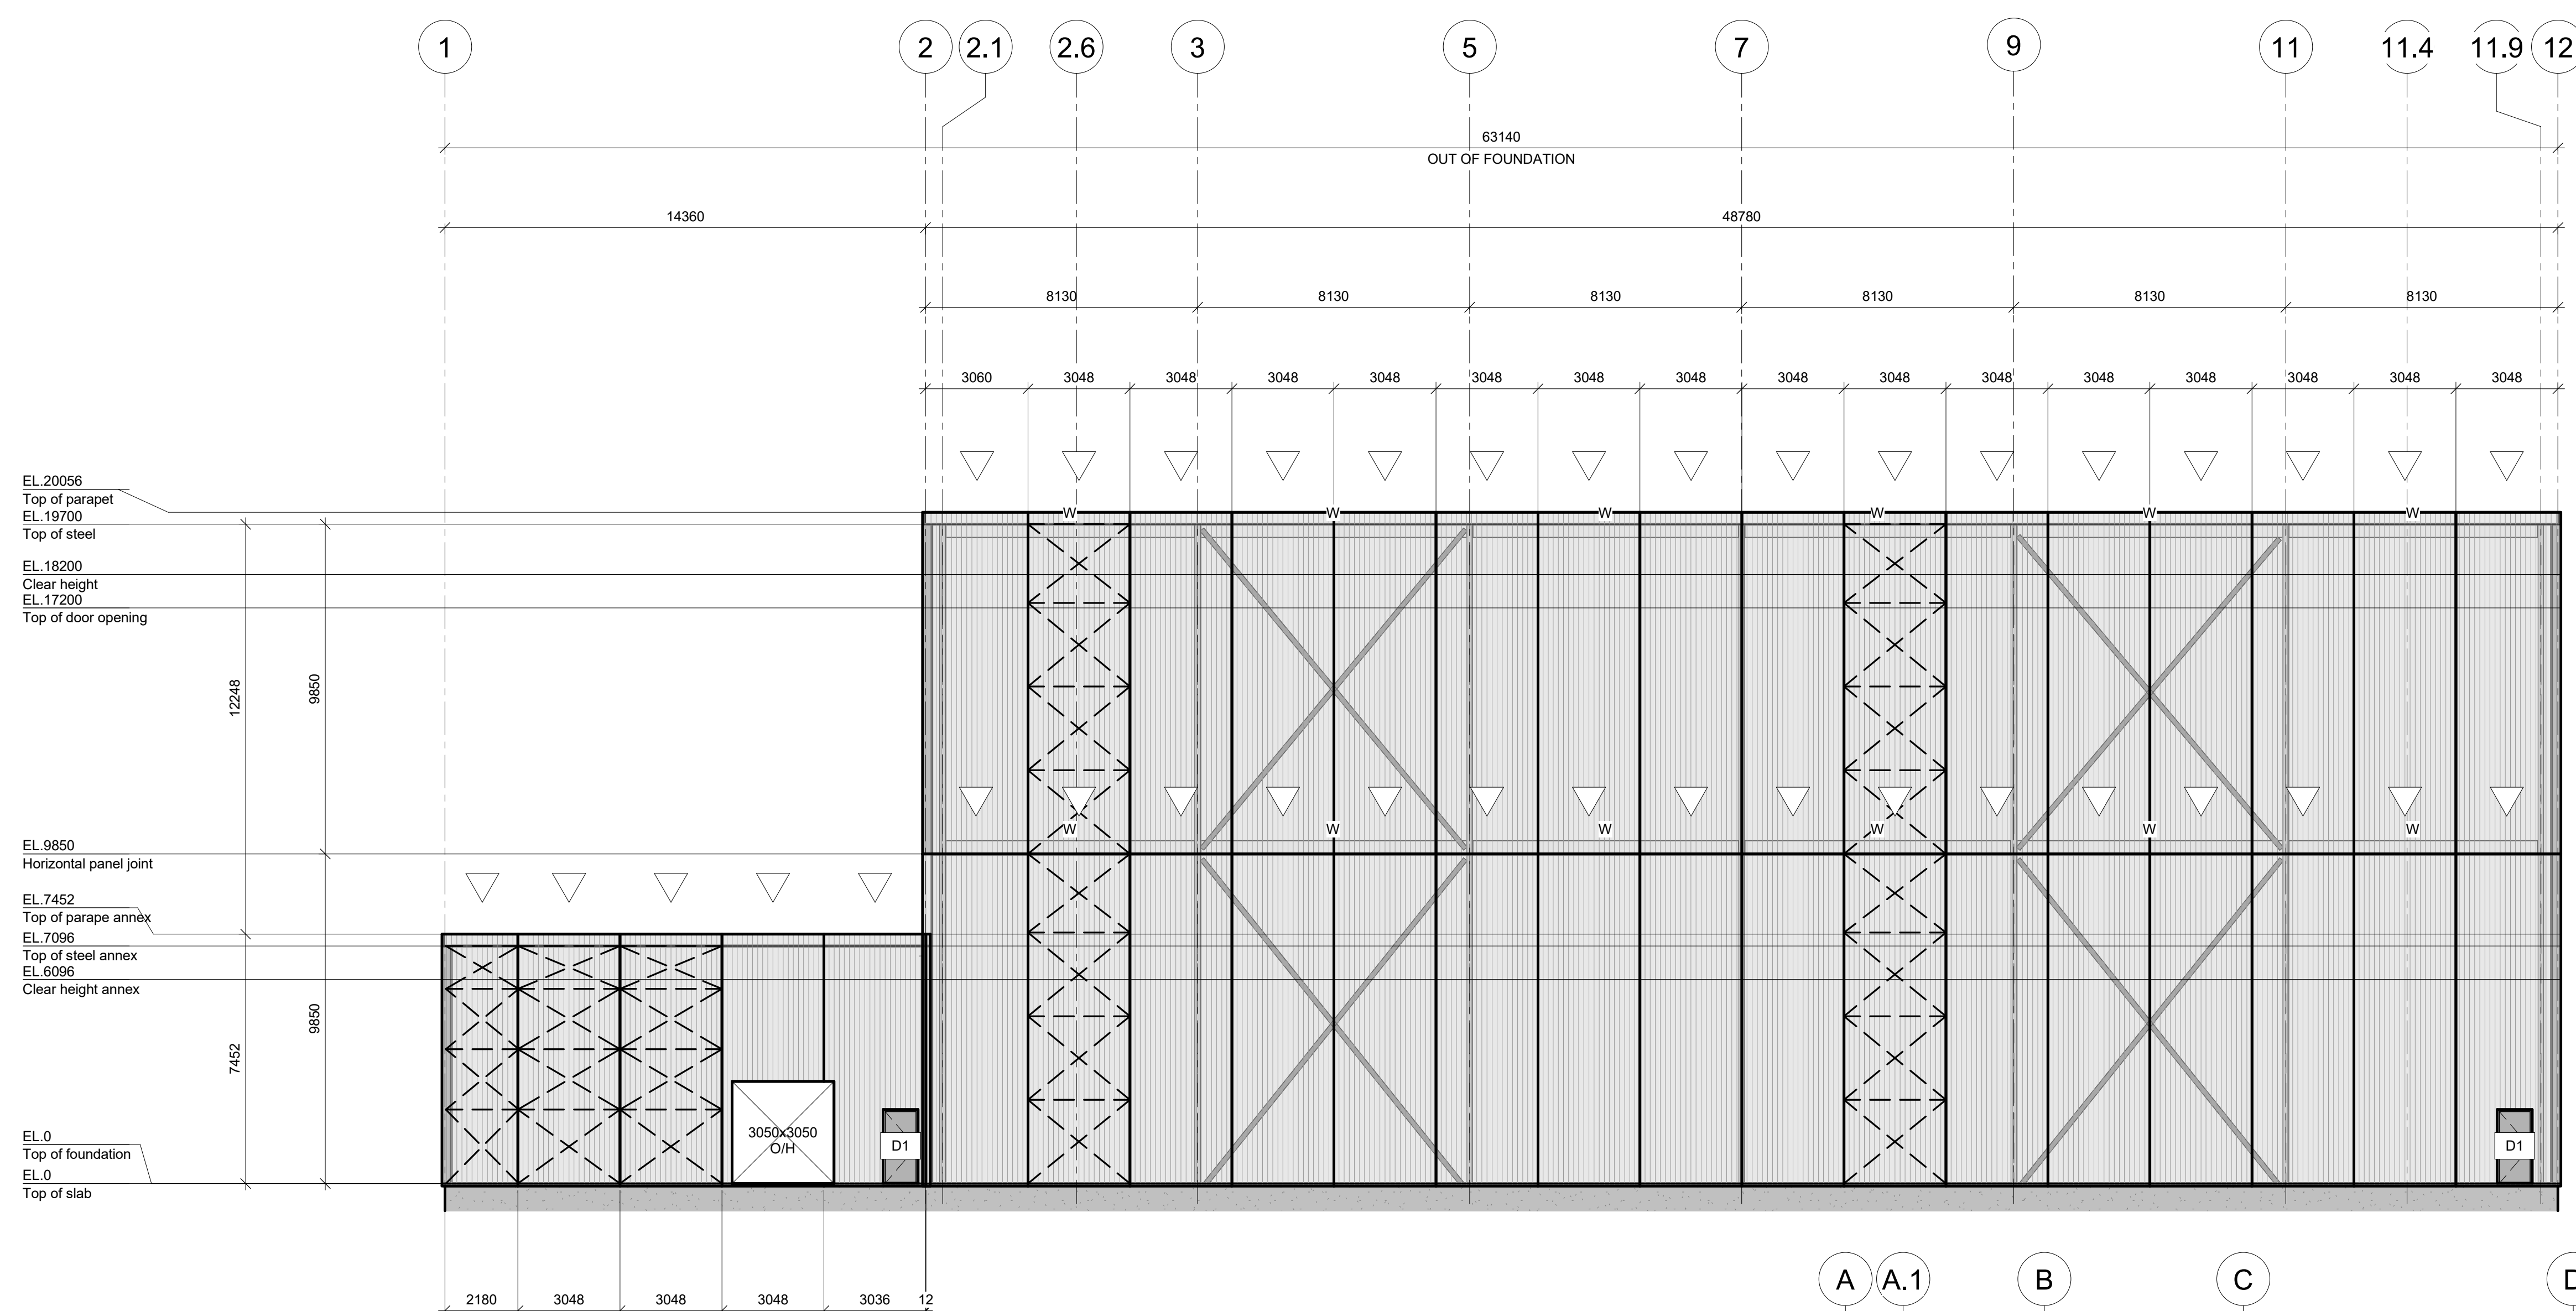

CONTRACTOR/ERECTOR NOTE:

IT IS PROHIBITED TO MODIFY, COPY, REPRODUCE OR OTHERWISE
DISTRIBUTE THIS DRAWING OR ANY REPRESENTATION OF THIS
DRAWING, OR ANY MEDIA, INCLUDING ELECTRONIC, WITHOUT THE
PRIOR WRITTEN APPROVAL OF CANAM GROUP INC.

PRELIMINARY

NOT TO BE USED FOR CONSTRUCTION

REVISION	DATE	DESCRIPTION	DESS	VER
PROJECT MANAGER				
		-		
		-		
		-		
		-		
		-		

DRAFTING			
DRAWN Donald Piché	DESIGNED	PROJECT ENGINEER	SCALE: Comme indiqué
CHECKED	CONSULTING ENGINEERS / ARCHITECTS		DATE (yyyy/mm/dd) : 2026-04-22

CUSTOMER: Pearlson & Pearlson Incorporated



11505, 1re Avenue, bureau 500, Saint-Georges Beauce
Quebec, Canada, G5Y 7X3
Phone : (418) 228-8031
Toll free : (877) 499-6049
www.canam.com

PROFESSIONAL SEAL





PROJECT

**Davie Shipyard - Paint and Blast facility
Lévis, QC**

DRAWING TITLE

PRELIMINARY SKETCH - ELEVATIONS

CONTRACT NUMBER P2026-091	DRAWING NUMBER EsMx501	DIVISION	REVISION 
------------------------------	---------------------------	----------	---

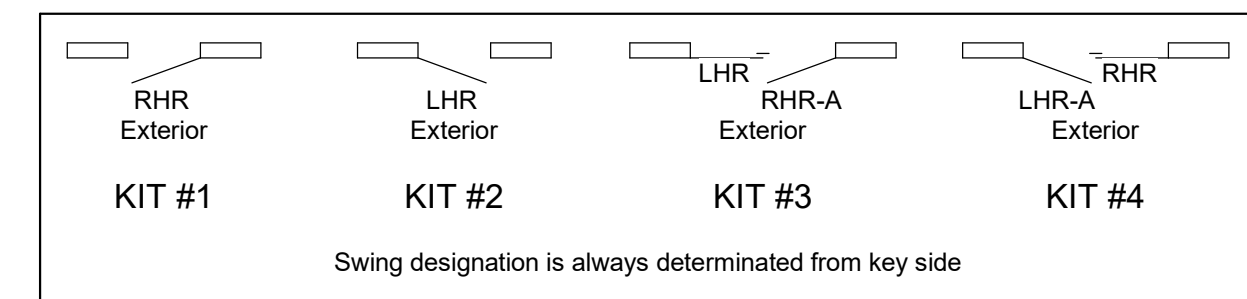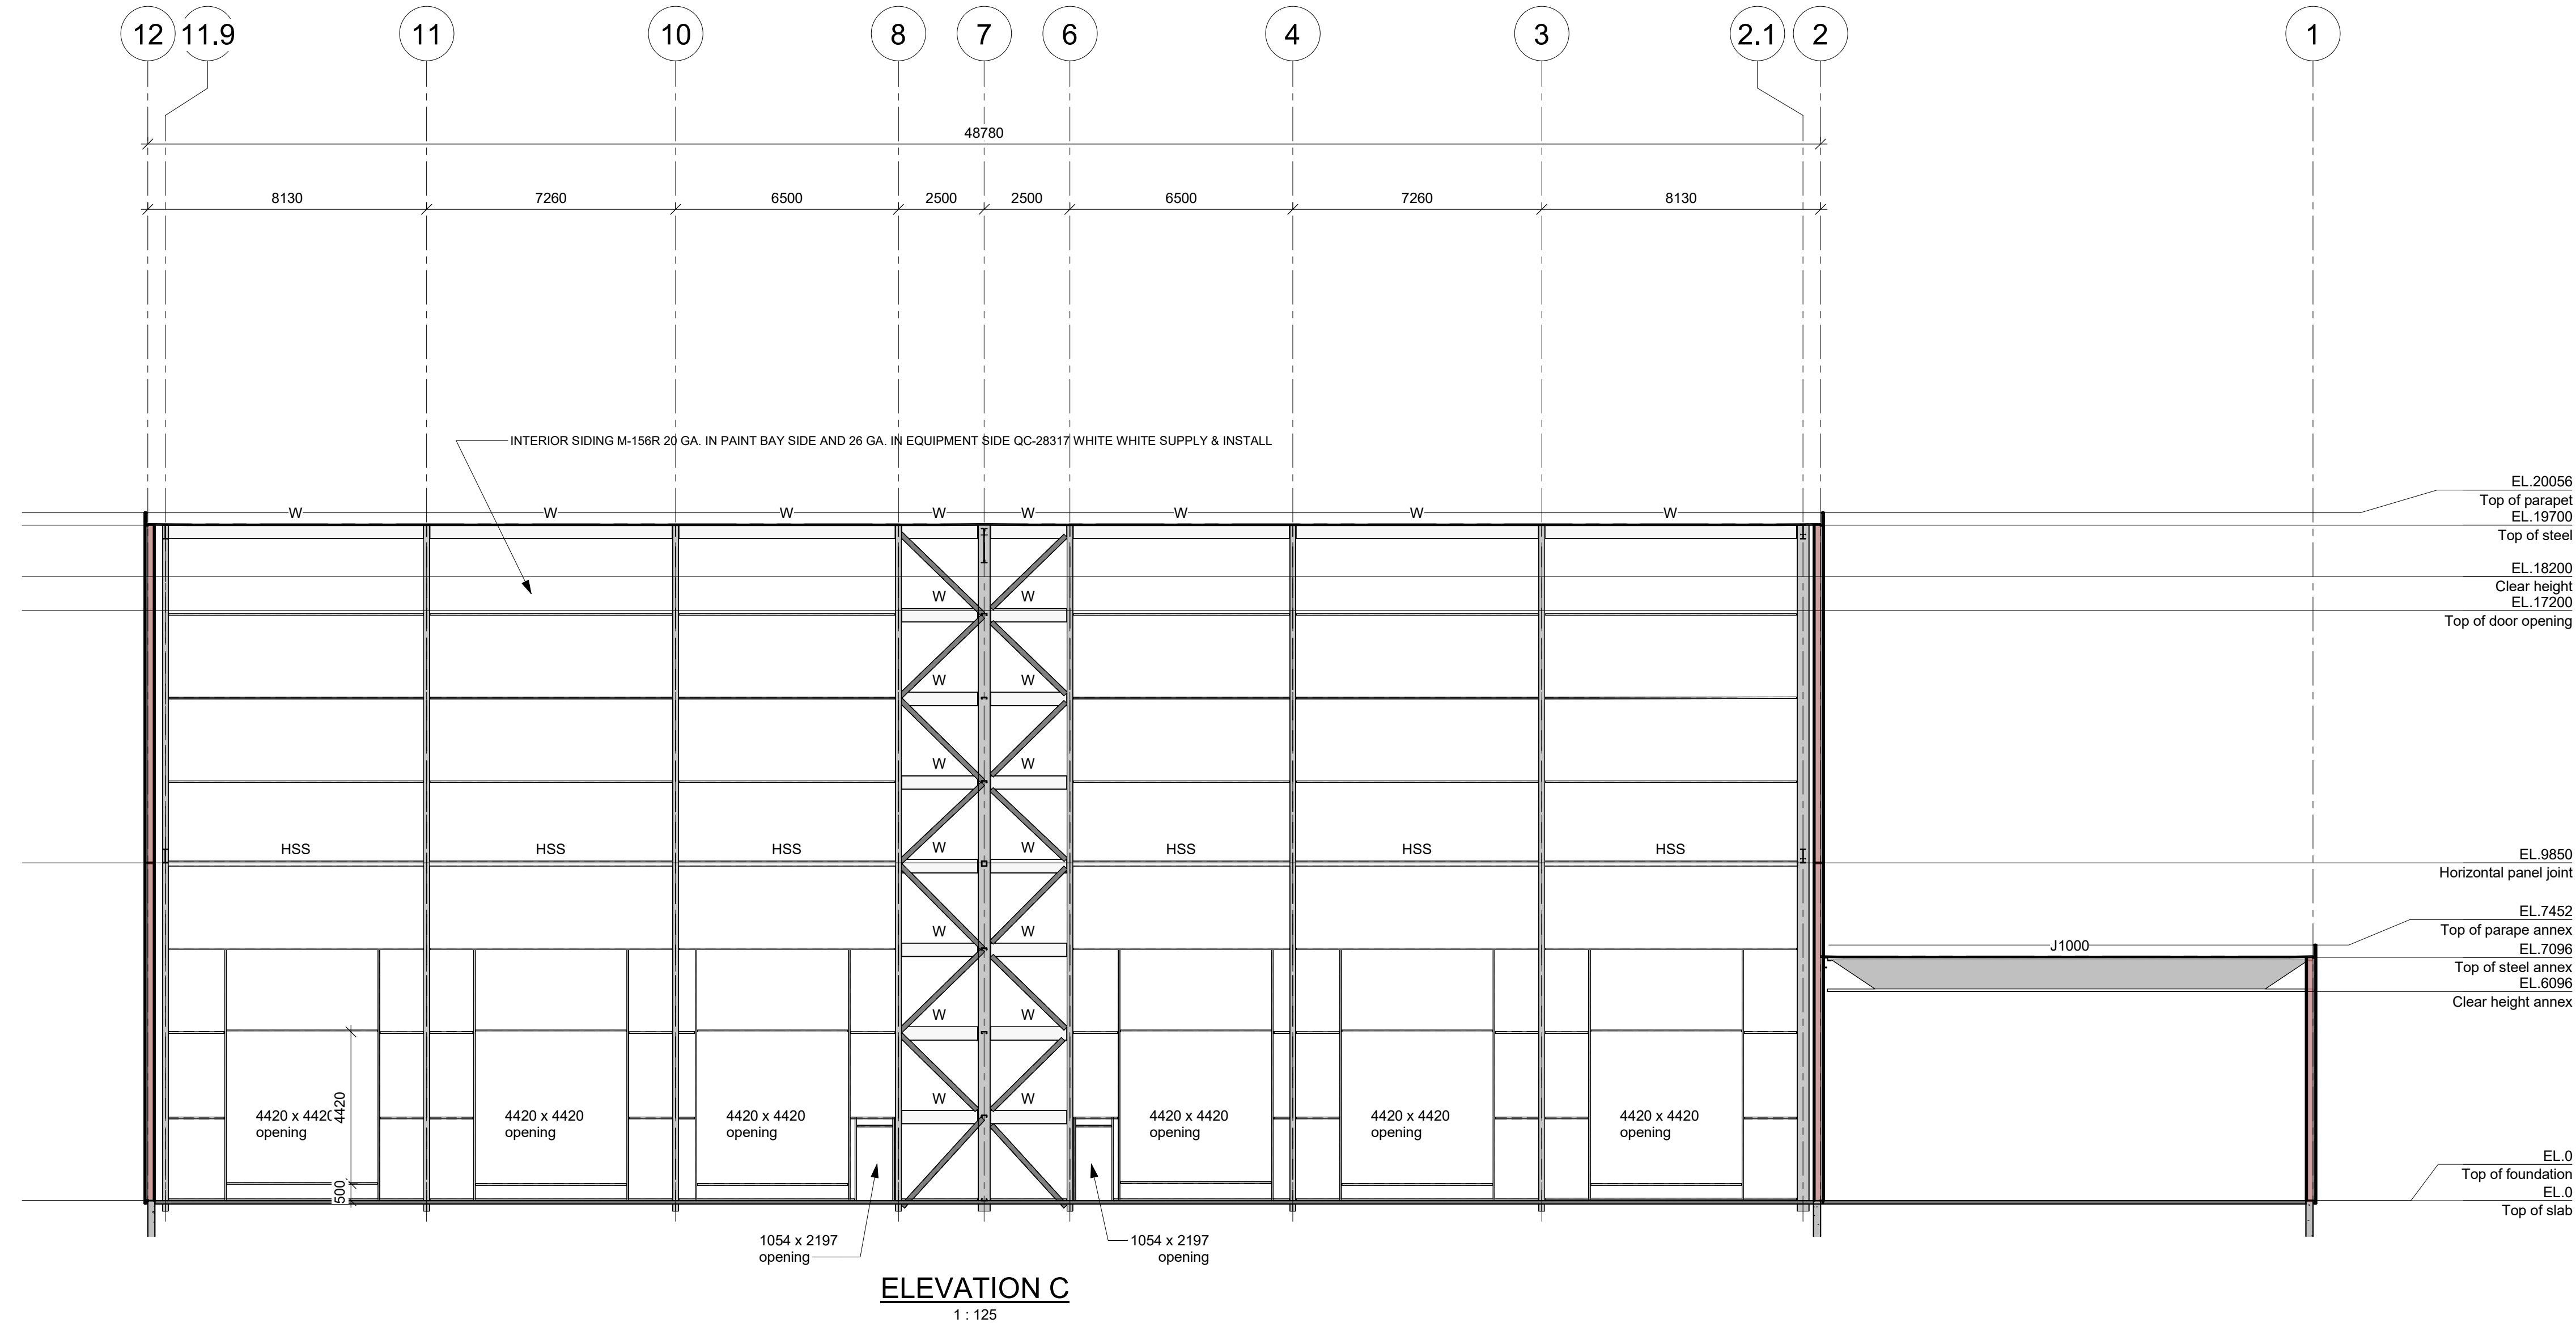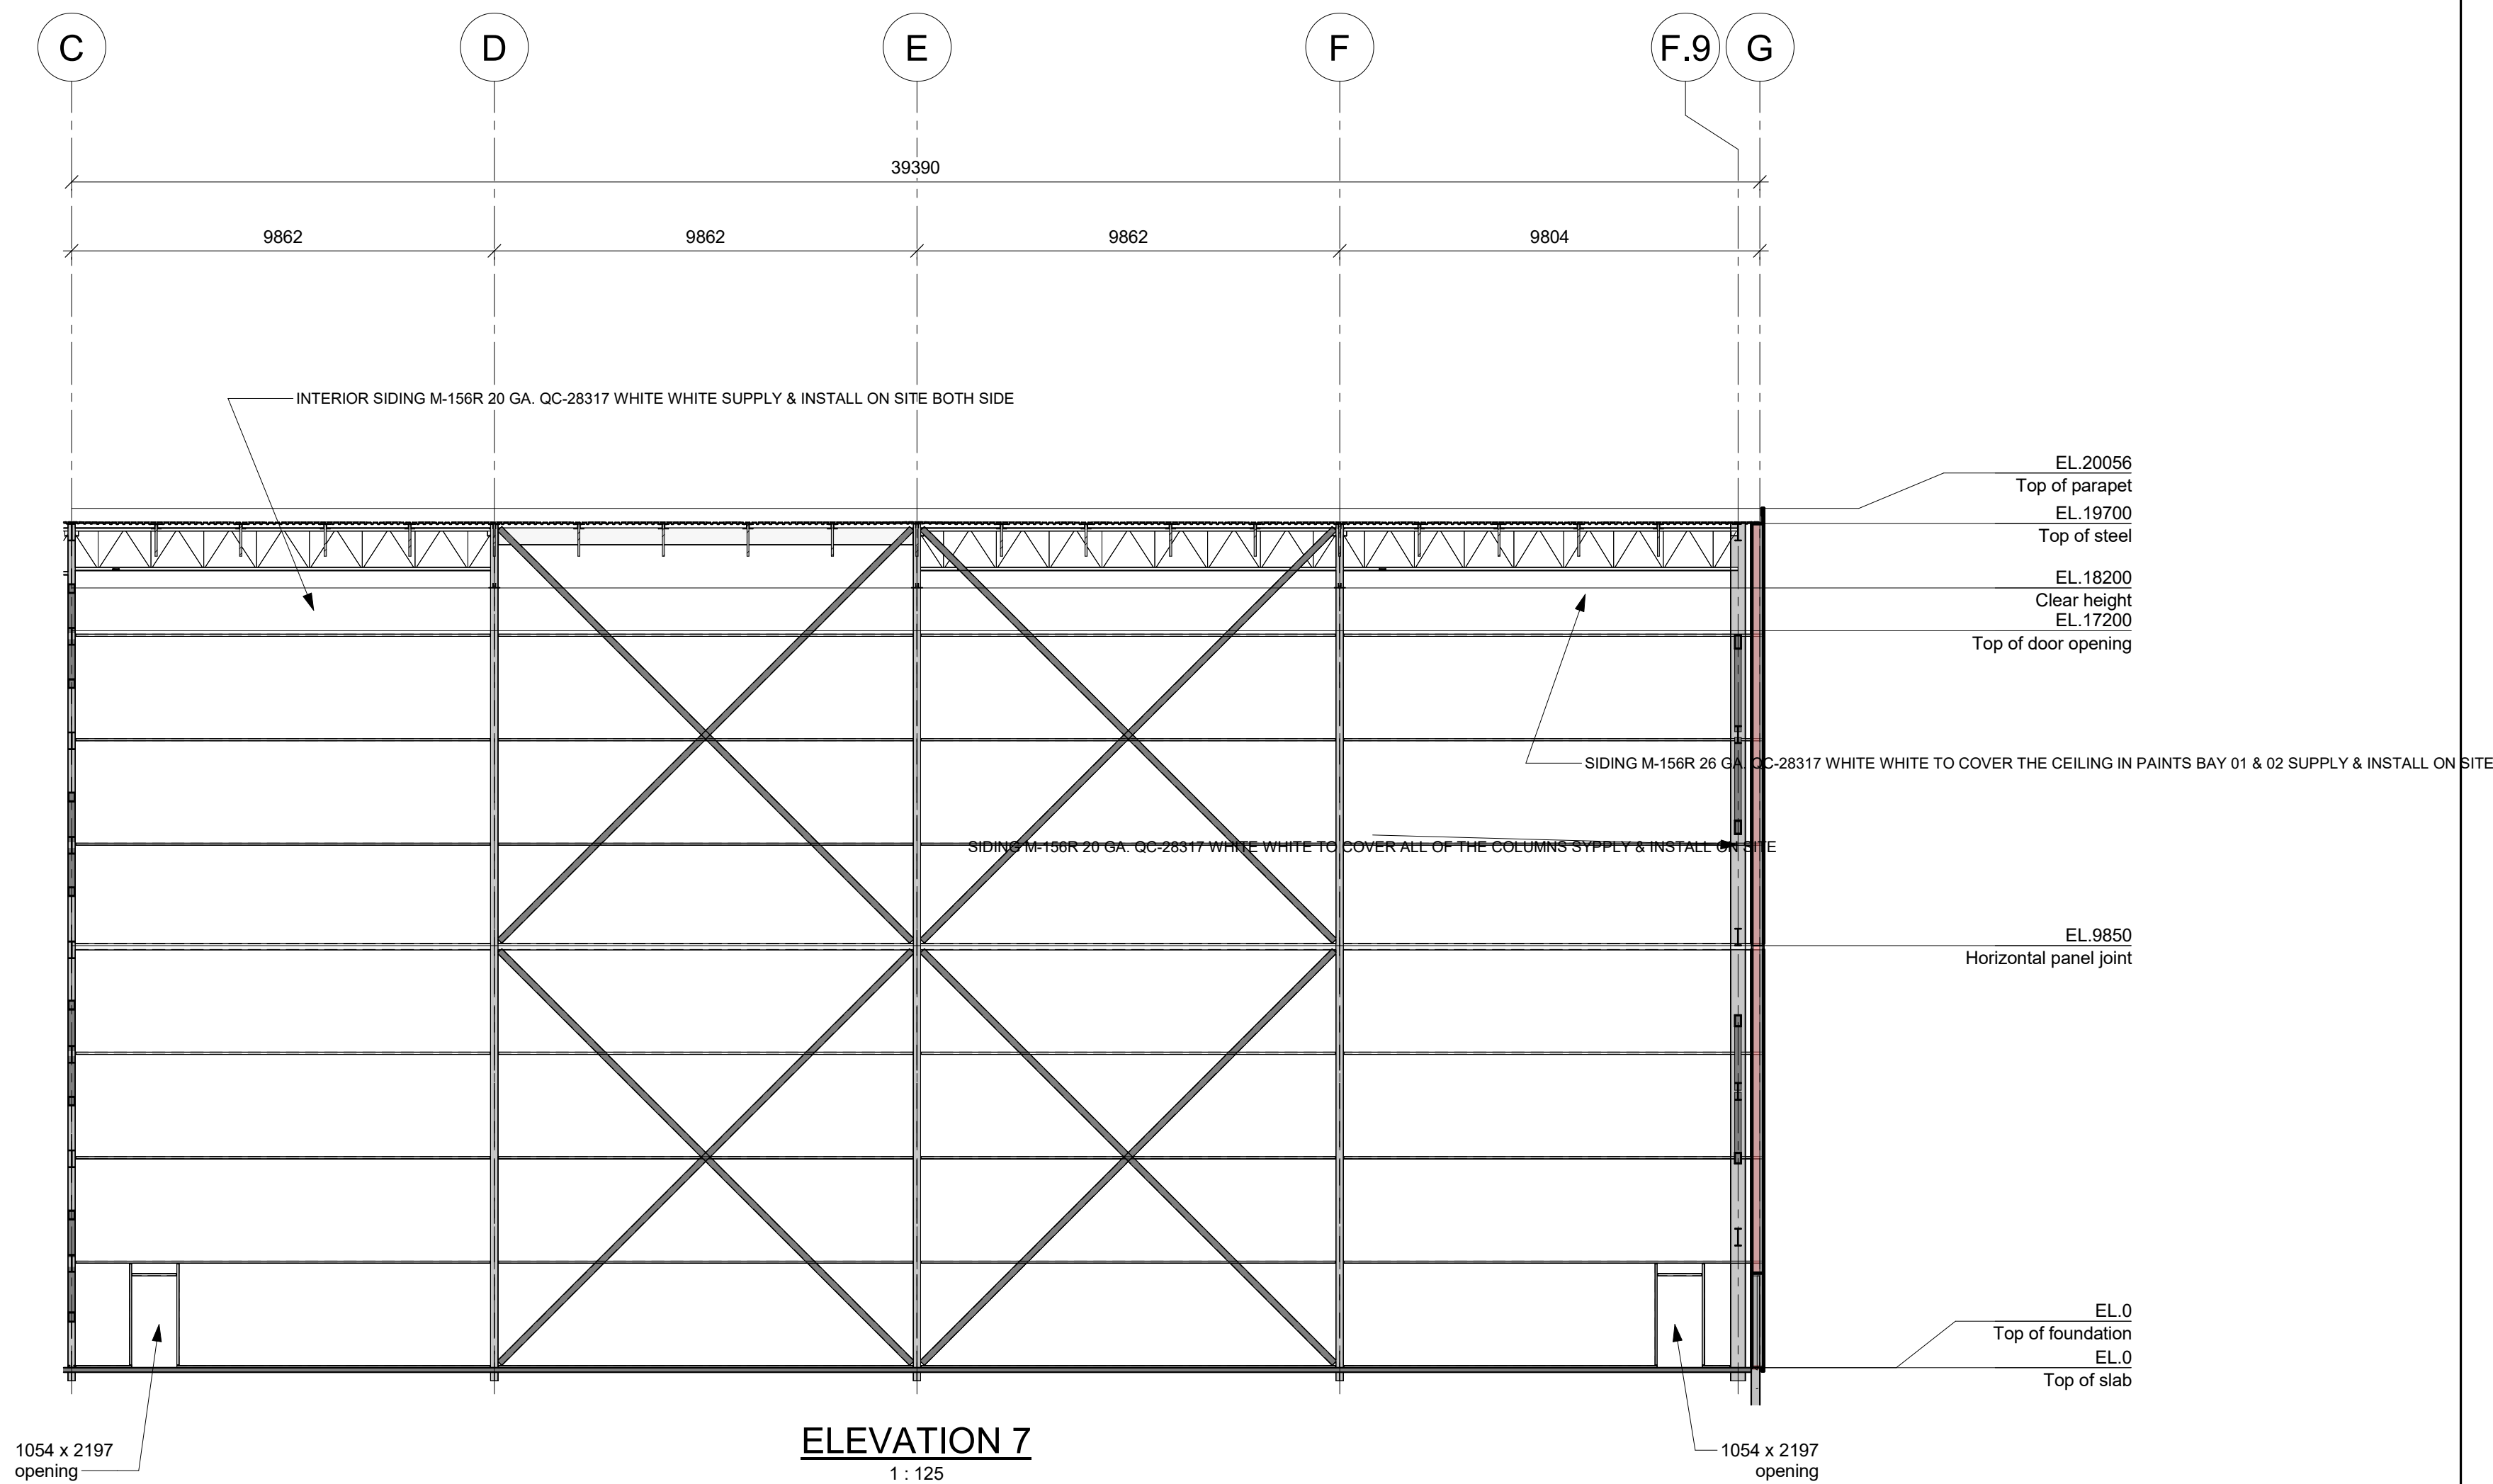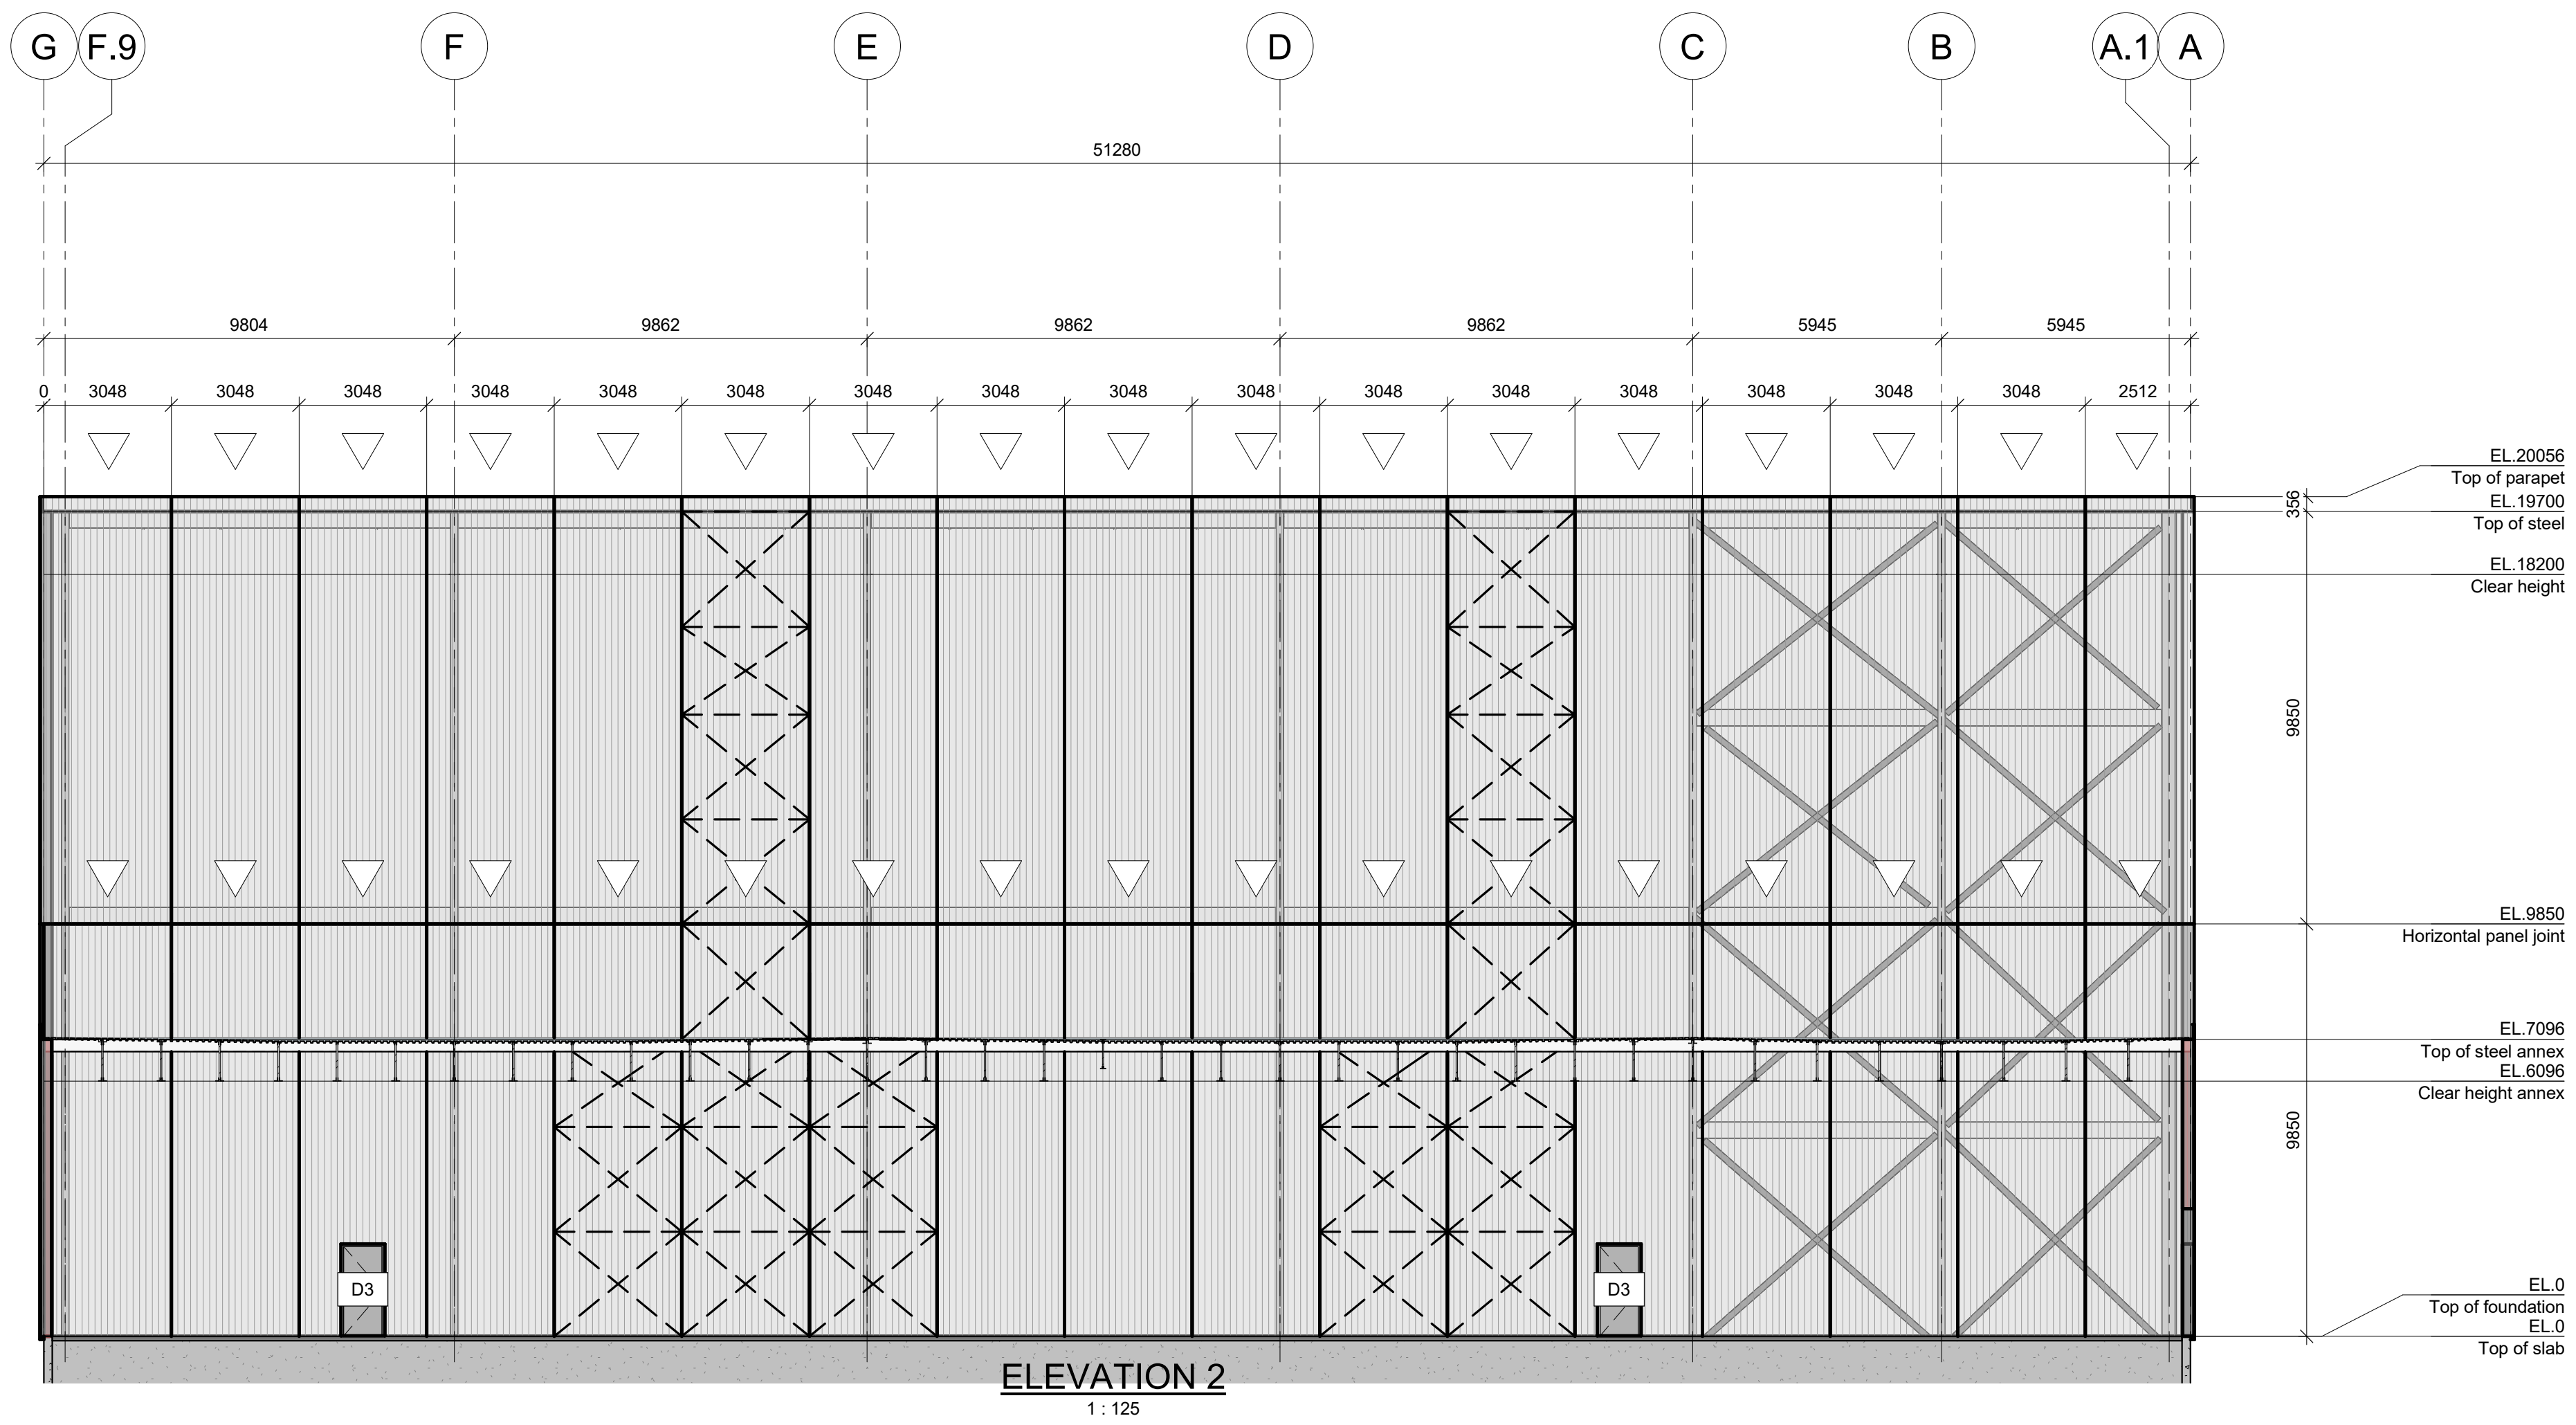

Supplier's standard hardware:
- Hinges : Stanley FBB179 4.5" x 4"
- Exit device : Von Duprin 22" x 689 with outside trim 230L
- Permanent cylinder : Schlage 2000IC 626
- Door closure : LCN 1261 689
- Head and jamb seal : Unique 1650
- Bottom seal : Unique DS4
- Threshold : See the remarks in "Door schedule"

Estimation Murox - Tableau de quantité - Fenêtre					
Identifiant	Qté.	Installation	Description	Dimensions ext. cadre largeur X hauteur	Couleur du cadre
W1	5		Fenêtre en aluminium fixe avec bris thermique et verre scellé + Low-E argon clair	5' x 5'	Aluminium Frame (no color)

DOOR SCHEDULE													
Door 16 ga				Glass				Hardware					
Identity	Type	Qty.	Installation	Insulation (R12)	Dimensions	Swing side	Width	Height	Steel frame 16 ga with thermal break	(3) Hinges non-rising removable pin	Door lock & latch set	Panic bar without outside trim 22EO	Panic bar with outside trim 230L
D1	6				< multiples >								
D2	5				36" x 84"								
D3	2				36" x 84"								
D9	1				3050x3050								
Remarks													

OH & OPENING SCHEDULE			
Total	Type	Tag	Remarks
1	4572x4572	OH	
1	4800x4800	OH	
2	17000x17200	OH	
Total général: 4			

PRELIMINARY

NOT TO BE USED FOR CONSTRUCTION

REVISION	DATE	DESCRIPTION	DES	VER
PROJECT MANAGER				
-				
-				
-				

DRAFTING			
DRAWN	DESIGNED	PROJECT ENGINEER	SCALE
Donald Piché			Comme indiqué
CHECKED	CONSULTING ENGINEERS / ARCHITECTS		DATE (yyyy/mm/dd)
			2026-04-22

CUSTOMER: Pearson & Pearson Incorporated



PROFESSIONAL SEAL

PROJECT

Davie Shipyard - Paint and Blast facility
Lévis, QC

DRAWING TITLE

PRELIMINARY SKETCH - ELEVATION,
WALL SECTION AND SCHEDULES

CONTRACT NUMBER	DRAWING NUMBER	DIVISION	REVISION
P2026-091	EsMx502		