

black

ERECTION NORTH

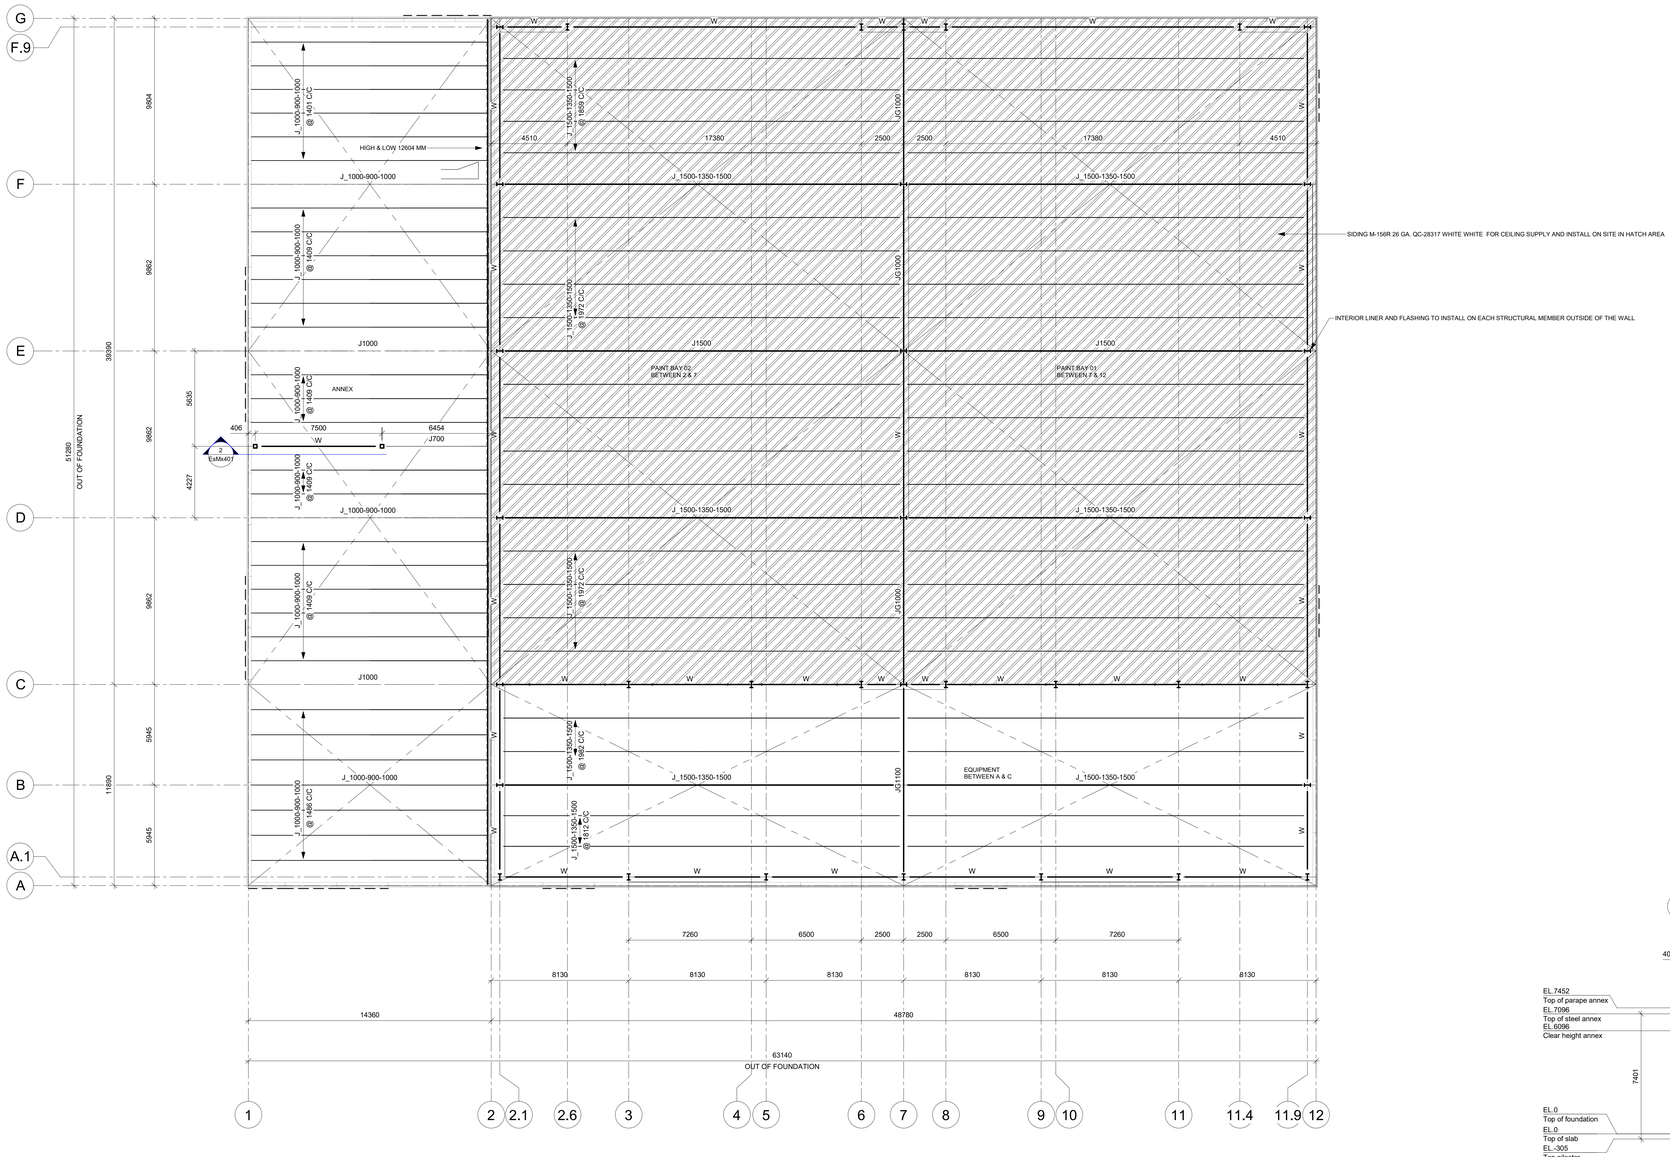

ROOF PLAN
1 : 125

GROSS UPLIFT DIAGRAM (UNFACTORED):

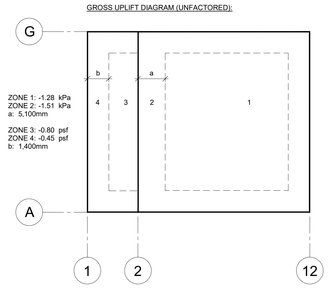


ZONE 1: -1.28 kPa
ZONE 2: -1.51 kPa
a: 5,100mm

ZONE 3: -0.80 psf
ZONE 4: -0.45 psf
b: 1,400mm

POSITIVE WIND PRESSURE (UNFACTORED): +0.45 kPa

POSITIVE WIND PRESSURE (UNFACTORED): +0.71 kPa

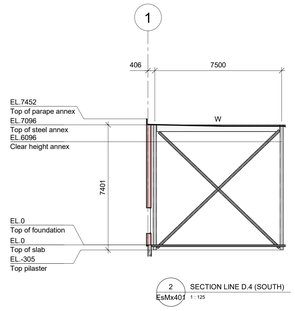

2 SECTION LINE D.4 (SOUTH)
EsMx401 1 : 125

CONTRACTOR/ERECTOR NOTE:

IT IS PROHIBITED TO MODIFY, COPY, REPRODUCE OR OTHERWISE DISTRIBUTE THIS DRAWING OR ANY REPRESENTATION OF THIS DRAWING, OR ANY MEDIA, INCLUDING ELECTRONIC, WITHOUT THE PRIOR WRITTEN APPROVAL OF CANAM GROUP INC.

ROOF

TOP OF PILASTER RWL	: -610
TOP OF PILASTER	: -305
TOP OF SLAB	: 0
TOP OF FOUNDATION	: 0
CLEAR HEIGHT	: 18200
TOP OF STEEL	: 19700
PARAPET HEIGHT	: 356
TOP OF PARAPET	: 20056

LOADS

D.L.	: 0.9k Pa
Coll.	: 0.23 kPa
Ss	: 3.3 kPa
Sr	: 0.6 kPa
Cb x Cw	: 0.8
Roof L.L.	: 0.0 kPa
Is	: 1.0
Roof snow load	: 3.24 kPa
Iw	: 1.0
Wind q= 1/50	: 0.41 kPa

Seismic (Site class: D (Assumed))

I_E	: 1.0
S_a (0.2)	: 0.747
S_a (0.5)	: 0.591
S_a (1.0)	: 0.356
S_a (2.0)	: 0.171
S_a (5.0)	: 0.048
S_a (10.0)	: 0.151
PGA	: 0.433
PGV	: 0.420

ANNEX

TOP OF PILASTER RWL	: -610
TOP OF PILASTER	: -305
TOP OF SLAB	: 0
TOP OF FOUNDATION	: 0
CLEAR HEIGHT	: 6096
TOP OF STEEL	: 7096
PARAPET HEIGHT	: 356
TOP OF PARAPET	: 7452

- Code Applicable : National building Code of Canada
 Quebec Building Code, latest adopted editions
 Code of Standard Practice CISC.
- Assumed soil site class: D
- NOTE :
 1. If, however, the seismic site class is determined to be E or F according to the geotechnical report, the preliminary structural concept (location and geometry of bracings, etc.) must be validated and coordinated by a Canam's engineer.

PRELIMINARY

NOT TO BE USED FOR CONSTRUCTION

REVISION	DATE	DESCRIPTION	DESS.	VER.

PROJECT MANAGER

DRAFTING:

DRAWN	DESIGNED	PROJECT ENGINEER	SCALE:
Donald Piché			Comme indiqué
CHECKED	CONSULTING ENGINEERS / ARCHITECTS		DATE (yyyy/mm/dd) : 2026-04-22

CUSTOMER: Pearlson & Pearlson Incorporated

CANAM
11505, 1re Avenue, bureau 500, Saint-Georges Beauce
Quebec, Canada, G5Y 7X3
Phone : (418) 228-8031
Toll free : (877) 499-6049
www.canam.com

PROFESSIONAL SEAL

PROJECT

Davie Shipyard - Paint and Blast facility
Lévis, QC

DRAWING TITLE

PRELIMINARY SKETCH - ROOF PLAN

CONTRACT NUMBER	DRAWING NUMBER	DIVISION	REVISION
P2026-091	EsMx401		

Initials