




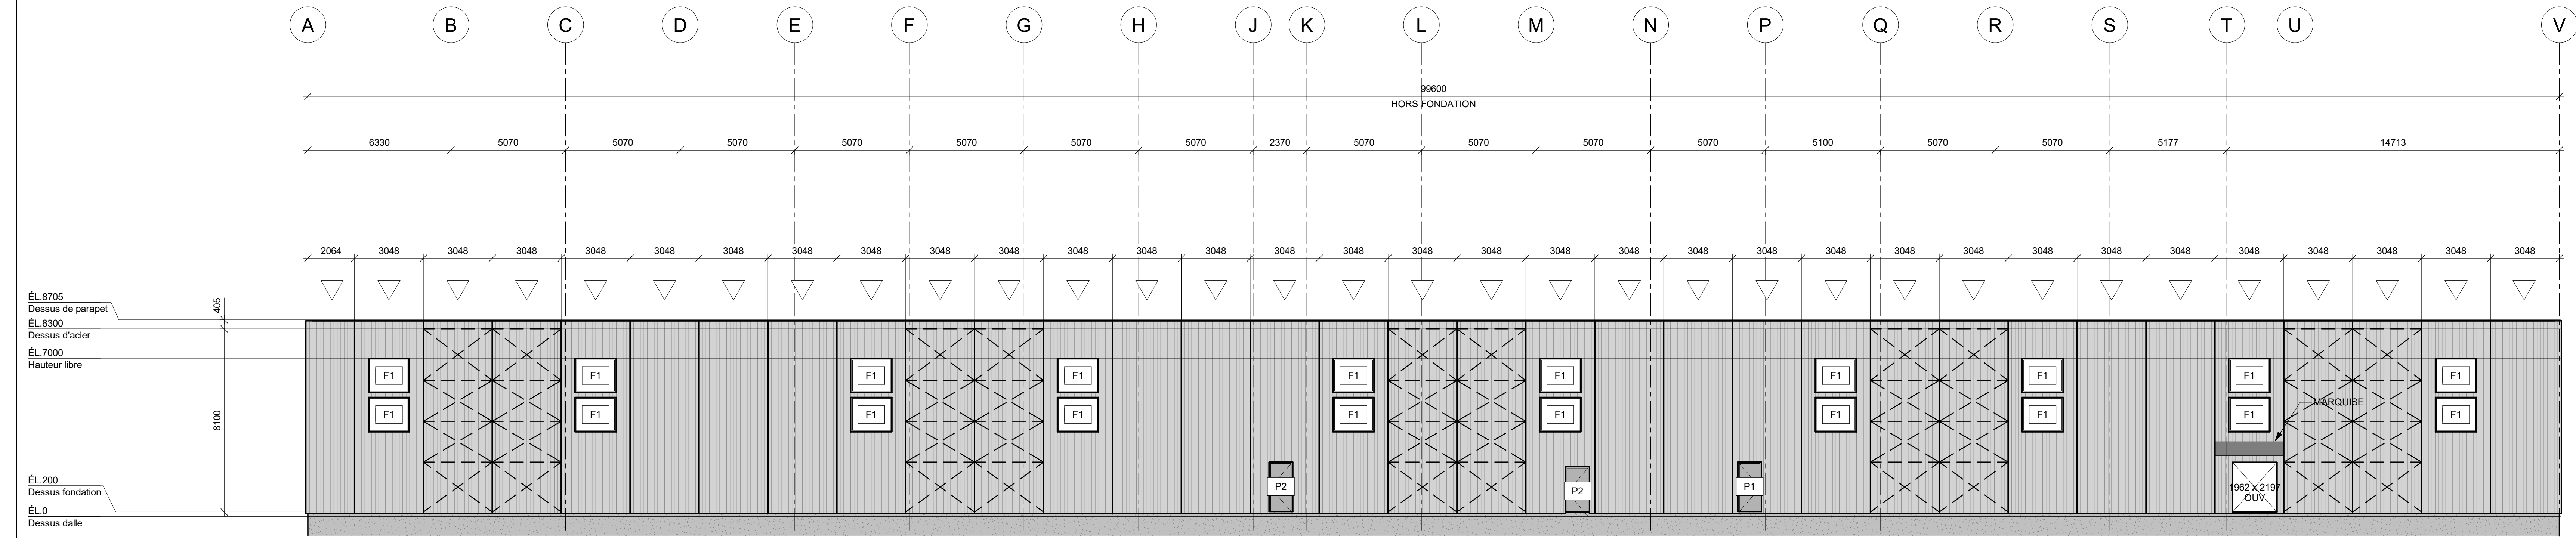


ÉLÉVATION AXE 6 (SUD)
1 : 125

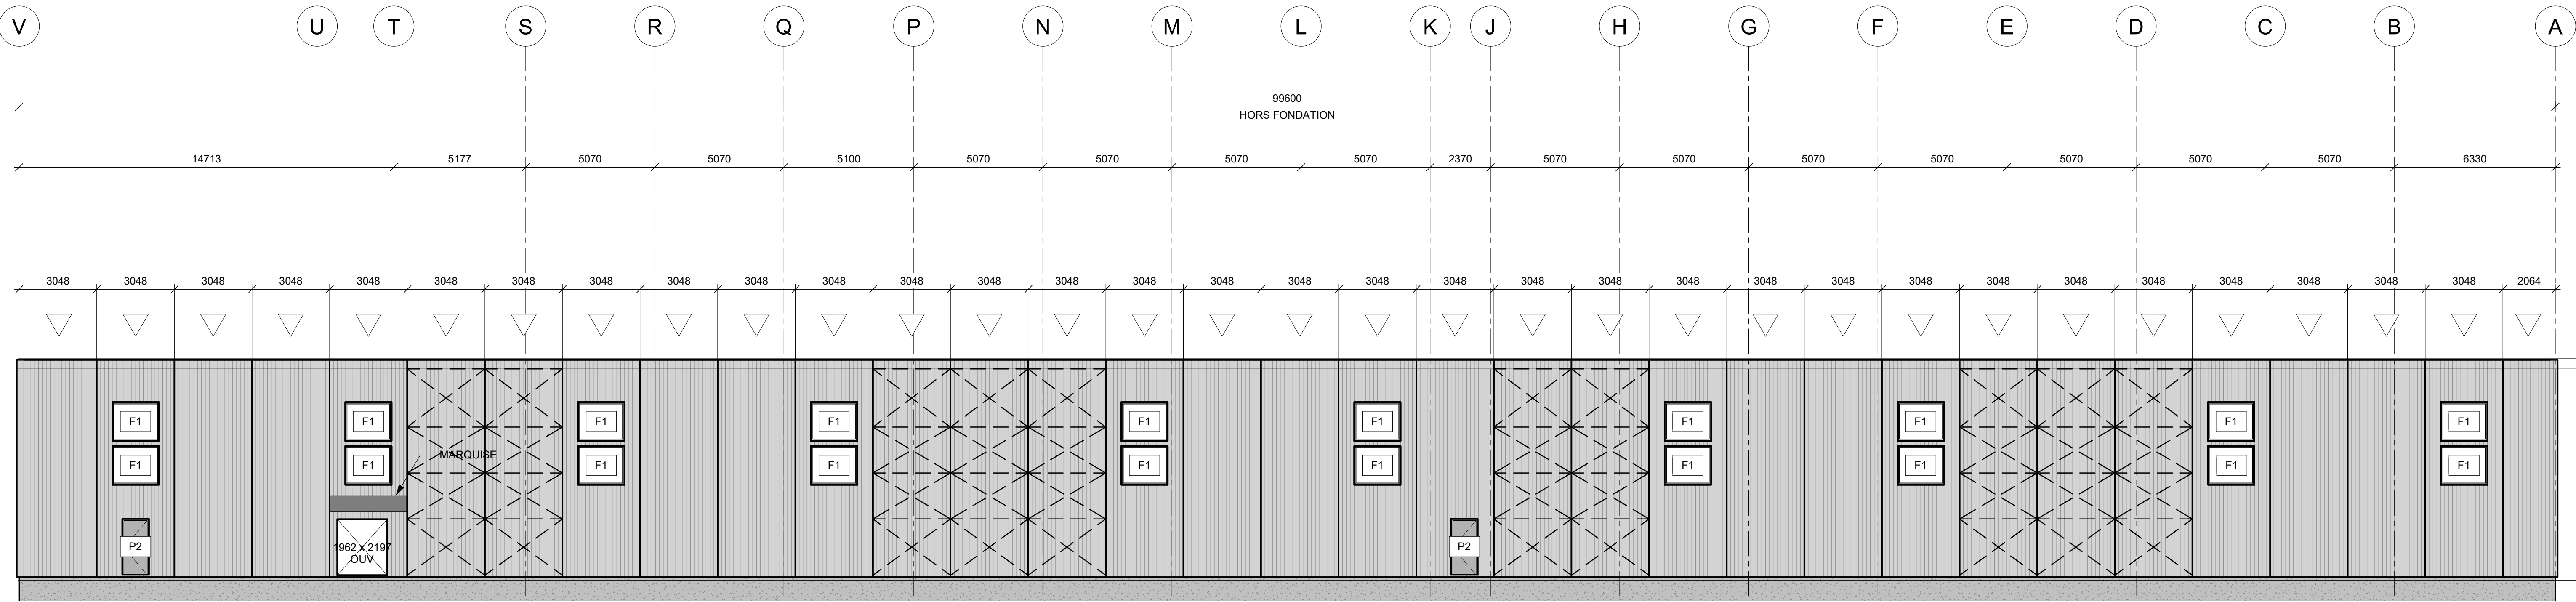

ÉLÉVATION AXE 1 (NORD)
1 : 125

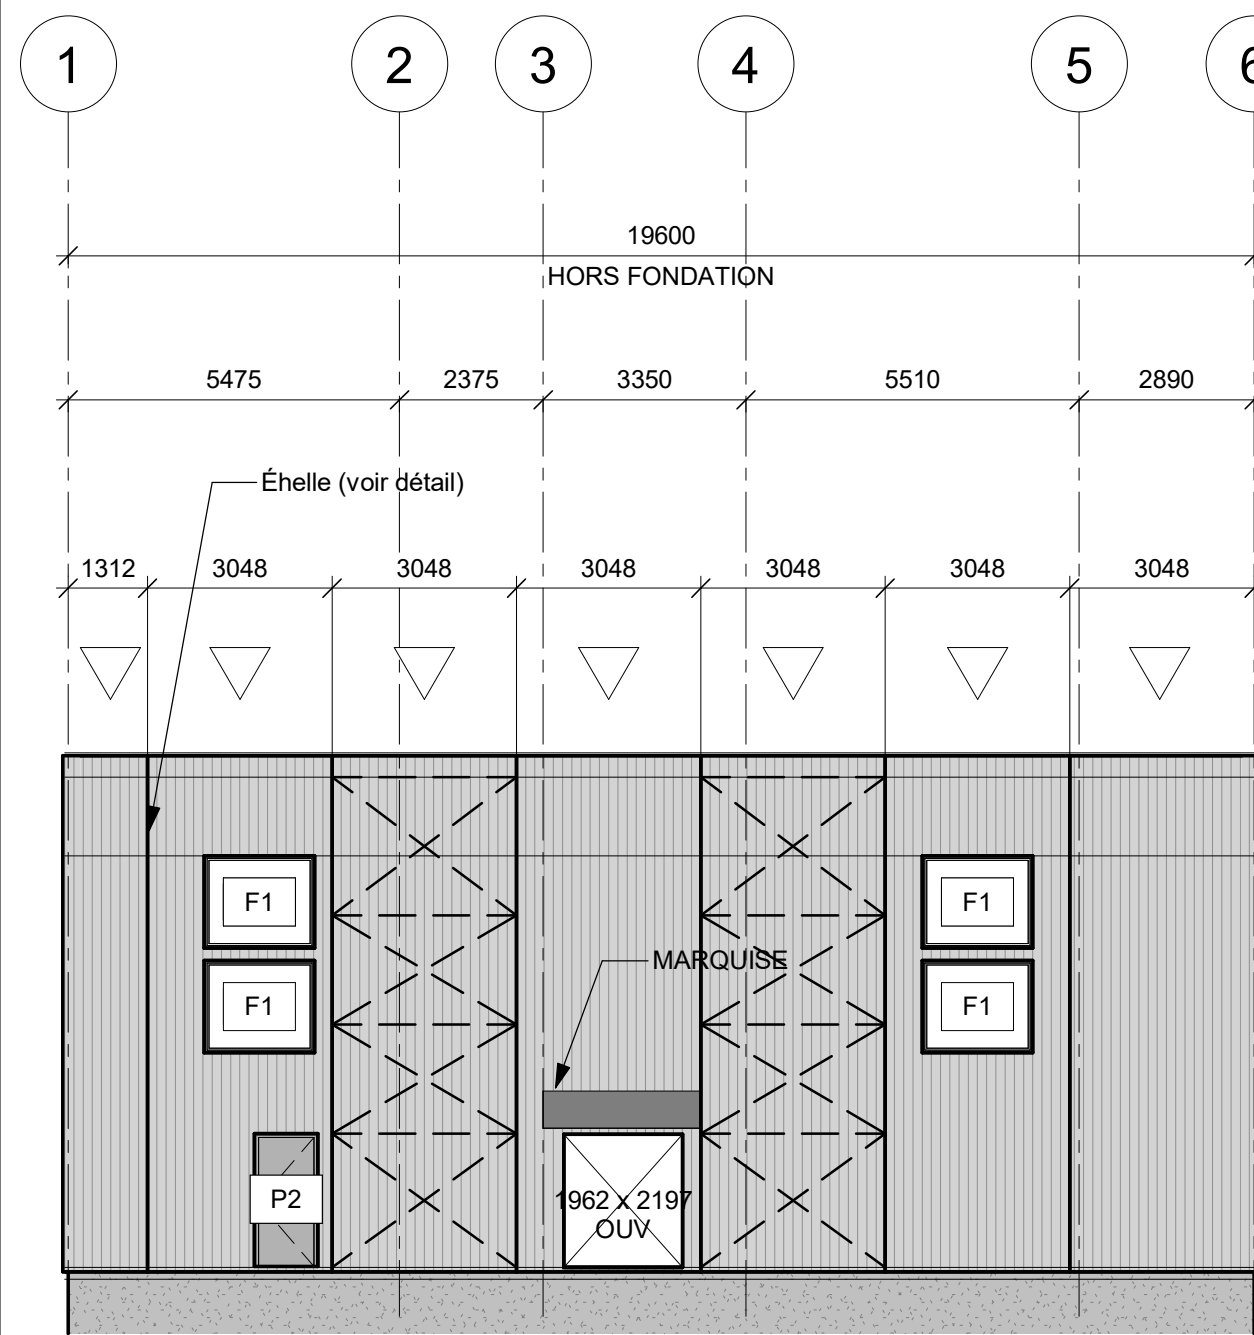


ÉLÉVATION AXE A (OUEST)
1 : 125

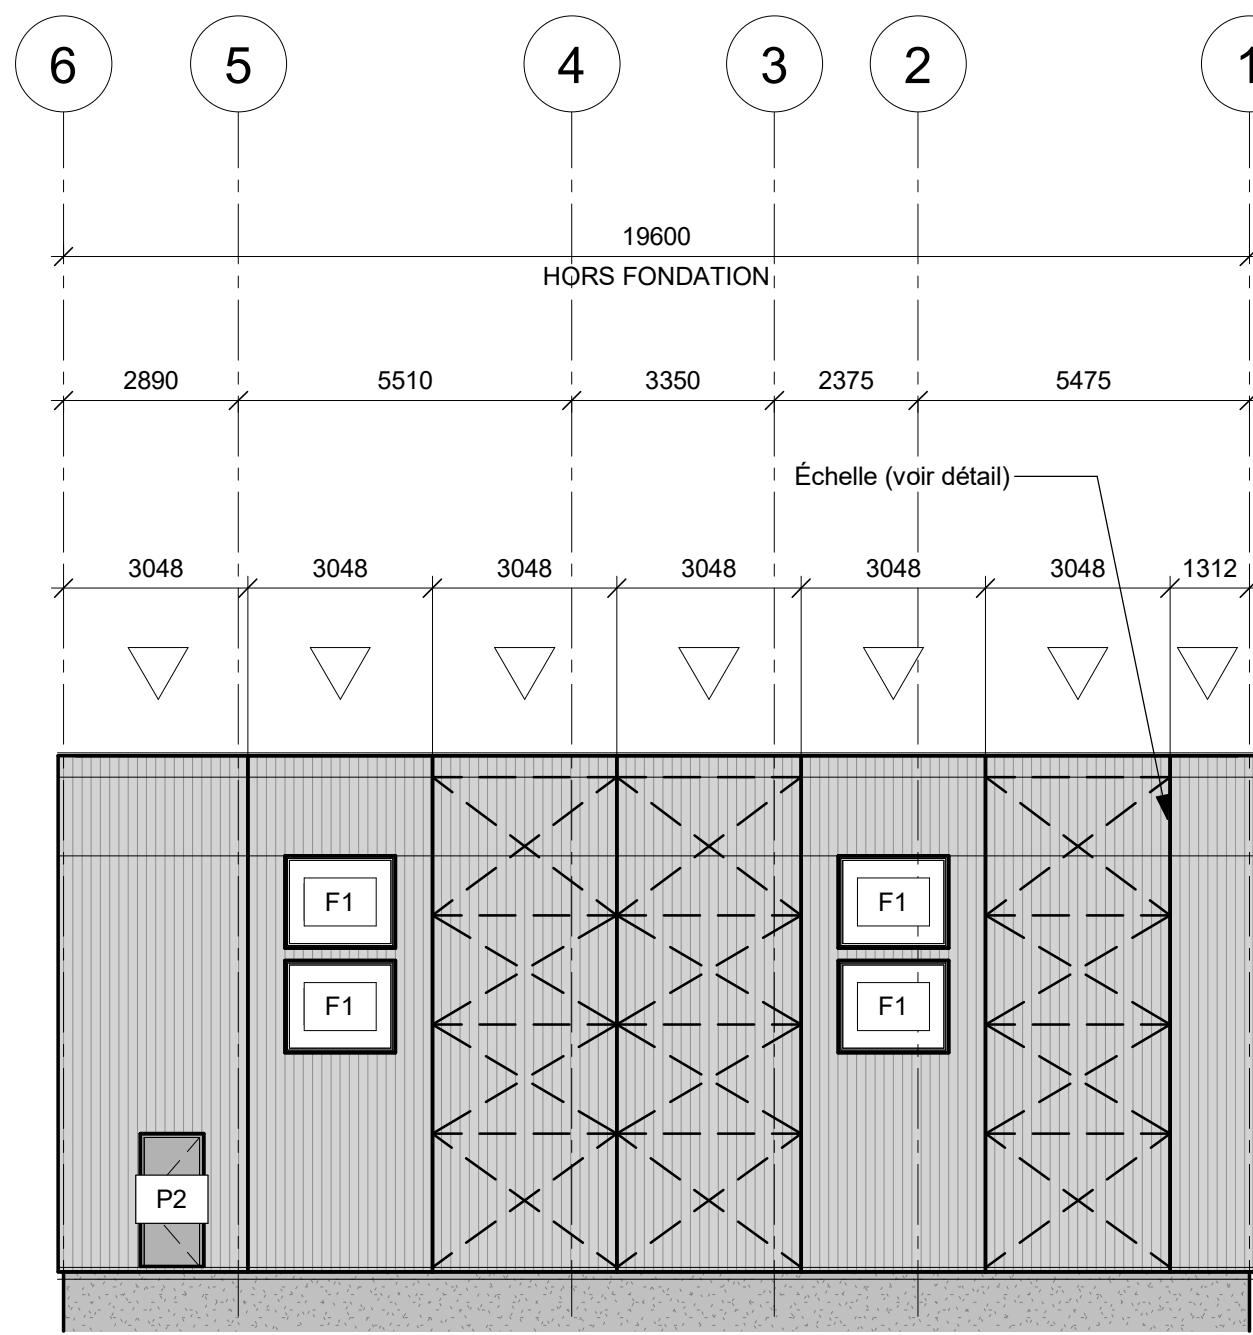

ÉLÉVATION AXE V (EST)
1 : 125

CÉDULE DES FENÊTRES					
Identifiant	Qté	Installation	Description	Dimensions (ext. cadre) largeur X hauteur	Couleur du cadre Aluminum Frame (no color)
F1	48		Fenêtre en aluminium fixe avec bris thermique et verre scellé + Low-E argon clair	1800 x 1500	

CÉDULE DES P.M.L ET DES OUVERTURES			
Total	Type	Tag	Commentaires
3	1962 x 2197	OUV.	
Total général: 3			

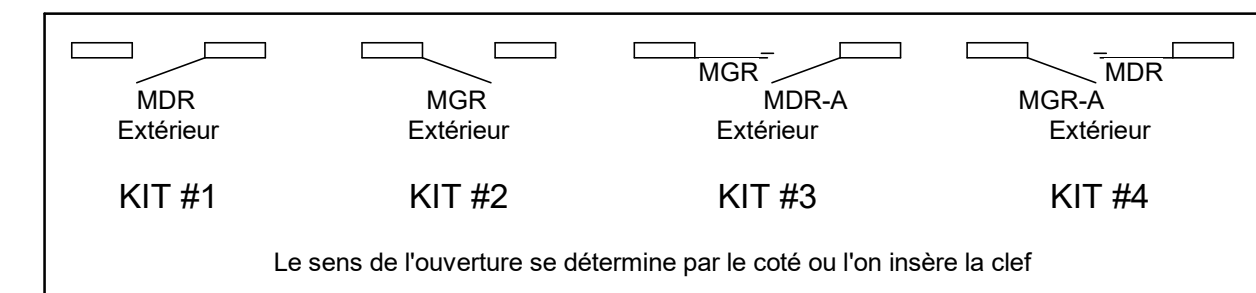


Quincaillerie standard du fournisseur:
- Chambrées: Stanley FB8179 4.5" x 4"
- Barre panique: Von Duprin 22 x 689 avec poignée extérieure 230L
- Cylindre permanent: Schlage 20001C 626
- Fourniture: LCN 1201 685
- Coupe-froid de tête et des montants: Unique 1650
- Coupe-froid du bas: Unique D54
- Seul: Voir la remarque dans la "Cédoule de porte"

CÉDULE DES PORTES											
Porte 18 ja.			Vitrage			Quincaillerie					
Identifiant	Qté	Installation	Isolation (R12)	Dimensions	Sens ouv.	Largeur	Hauteur	Cadre d'acier 18 ja. avec bris thermique	(3) Pertuis @ 1/2" fixe	Poignée seulement	Remarques
P1	1			36" x 84"				Barre panique sans poignée ext. 2350			
P2	6			36" x 84"				Barre panique avec poignée ext. 2350			

- Revêtement extérieur M-156R,
26 ja. série Perspectives,
Couleurs Standards
- Coupe-air
- Isolant rigide continu de fibre
de roche "Z" (50.8 mm)
Rockwool Comfortboard 110
(R-8)
- U 8.2x16 ja (U 203x50x1.6)
(à la base & tête du panneau,
à EL 1071"0" et
autour des ouvertures)
- Z 26x216 ja typ sec
(Z 203x50x1.6)
- Isolation fibre de roche Roxul
Safe 55, densité 4.5 kg/m³,
2 épaisseurs de 4"
- Coupe vapeur
- Revêtement intérieur M-156R,
24 ja. série Perspectives,
QC-28317, Blanc Pur

Membrane autocollante
Protecto Wrap 4" (102)
Scellant noir à base de silicone.
Appliqué sur la fondation avant
le montage, (fourni et installé
par CANAM)


Panneau Murox avec résistance
au feu deux heures CI R-29

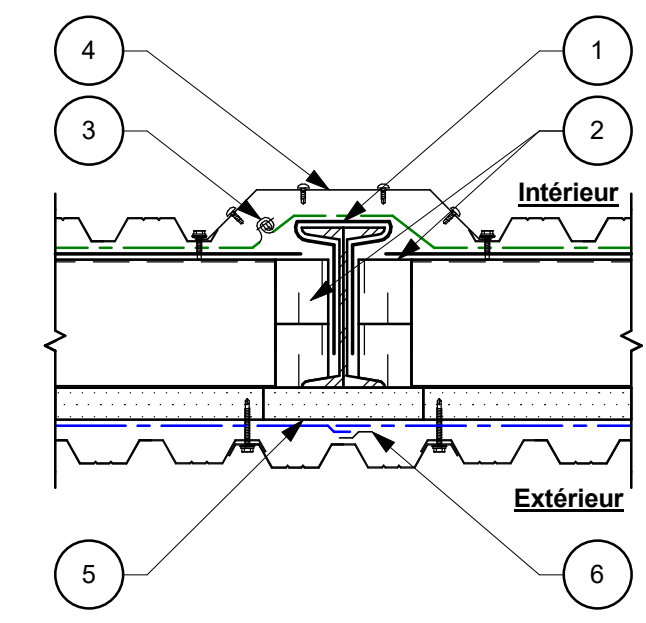

VOIR COUPE DE MUR
SOLIN FL-7777
C/A SCÉLANT CLAIR **
① VIS TEK 3
#14 - 14 x 5" @ 6" C/C
QC-8777 **
CLOSIR MÉTALLIQUE
(PETIT), QC-28777 ** +
CLOSIR DE CAOUTCHOUC
(PETIT), 38-655 **
MARQUISE F4 QC-28777
(PLAQUE PLIÉE 16 JA.) **


EL
DESSOUS SOFFITE
CLOSIR MÉTALLIQUE
(PETIT), QC-28777 **

Canopy - Folded plate (R-29)
1 : 12

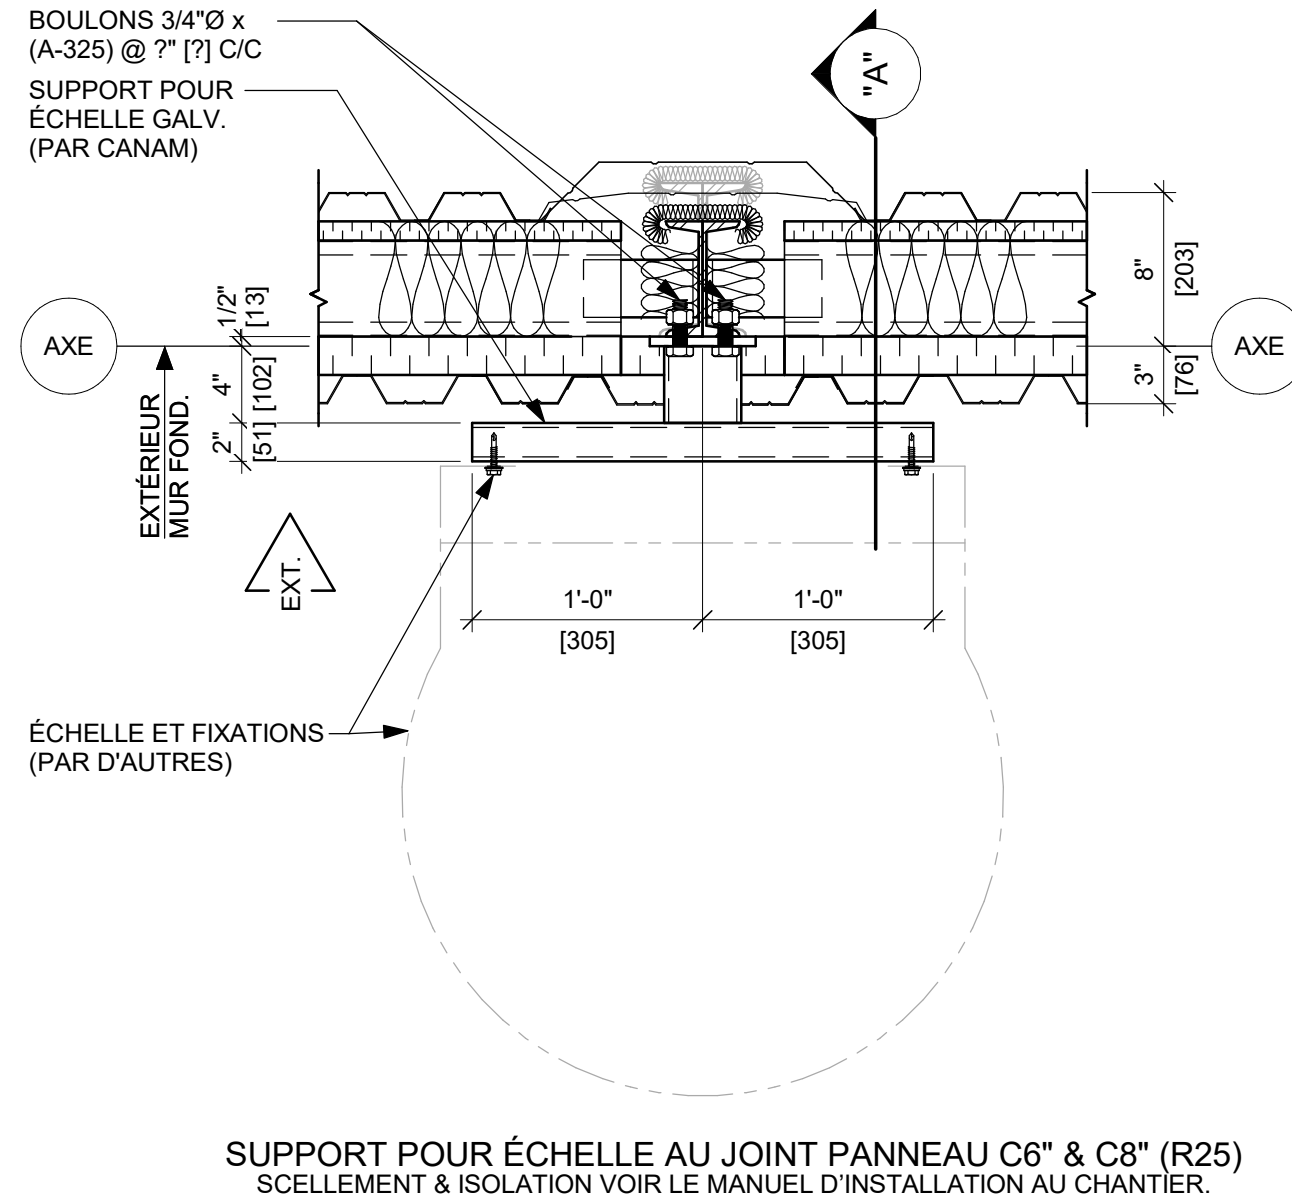


SUPPORT POUR ÉCHELLE AU JOINT PANNEAU C6" & C8" (R25)
SCÉLLEMENT & ISOLATION VOIR LE MANUEL D'INSTALLATION AU CHANTIER

Notes:
* Fourni et installé par CANAM
en chantier
** Fourni par CANAM et
installé par l'entrepreneur général
*** Fourni et installé par
l'entrepreneur général

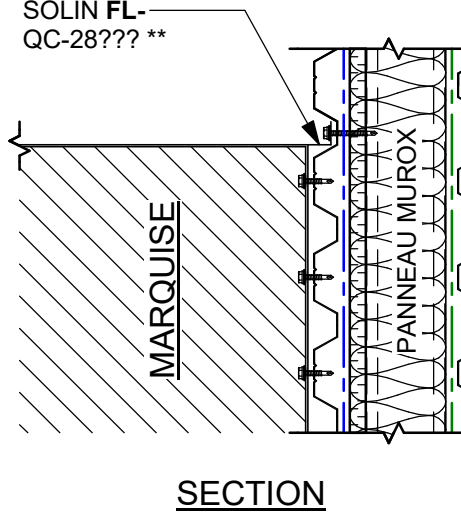

SECTION

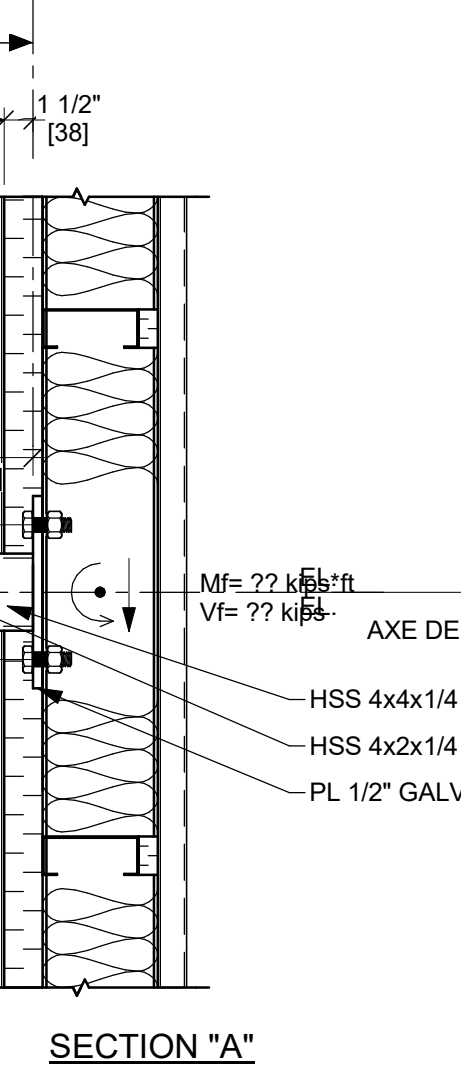

SECTION "A"

PRÉLIMINAIRE
NE DOIT PAS SERVIR À LA
CONSTRUCTION

REVISION	DATE	DESCRIPTION	DESS	VER
DEVANT DE PROJET				
			-	
			-	
			-	
			-	
DESIGN				
DESIGNÉ PAR	CONÇU PAR	INGÉNIEUR DU PROJET	ÉCHELLE:	
Donald Piché			Comme indiqué	
VERIFIÉ PAR	INGÉNIEURS CONSEILS / ARCHITECTES			DATE (mm/aa/aaaa)
				2026-04-23

CLIENT: Construction de Défense Canada

CANAM
11505, 1re Avenue, bureau 500, Saint-Georges Beaulieu
Québec, Canada G5V 7G3
Téléphone : (418) 228-8031
Sans frais : (877) 459-8049
www.canam.com

PROJET
6 Nouveaux Bâtiments Préfabriqués
St-Jean-sur-le-Richelieu, QC

TITRE CROQUIS PRÉLIMINAIRE - ÉLÉVATIONS			
NUMÉRO CONTRAT P2026-093	NUMÉRO DESIGN EsMx501	DIVISION	REVISION