


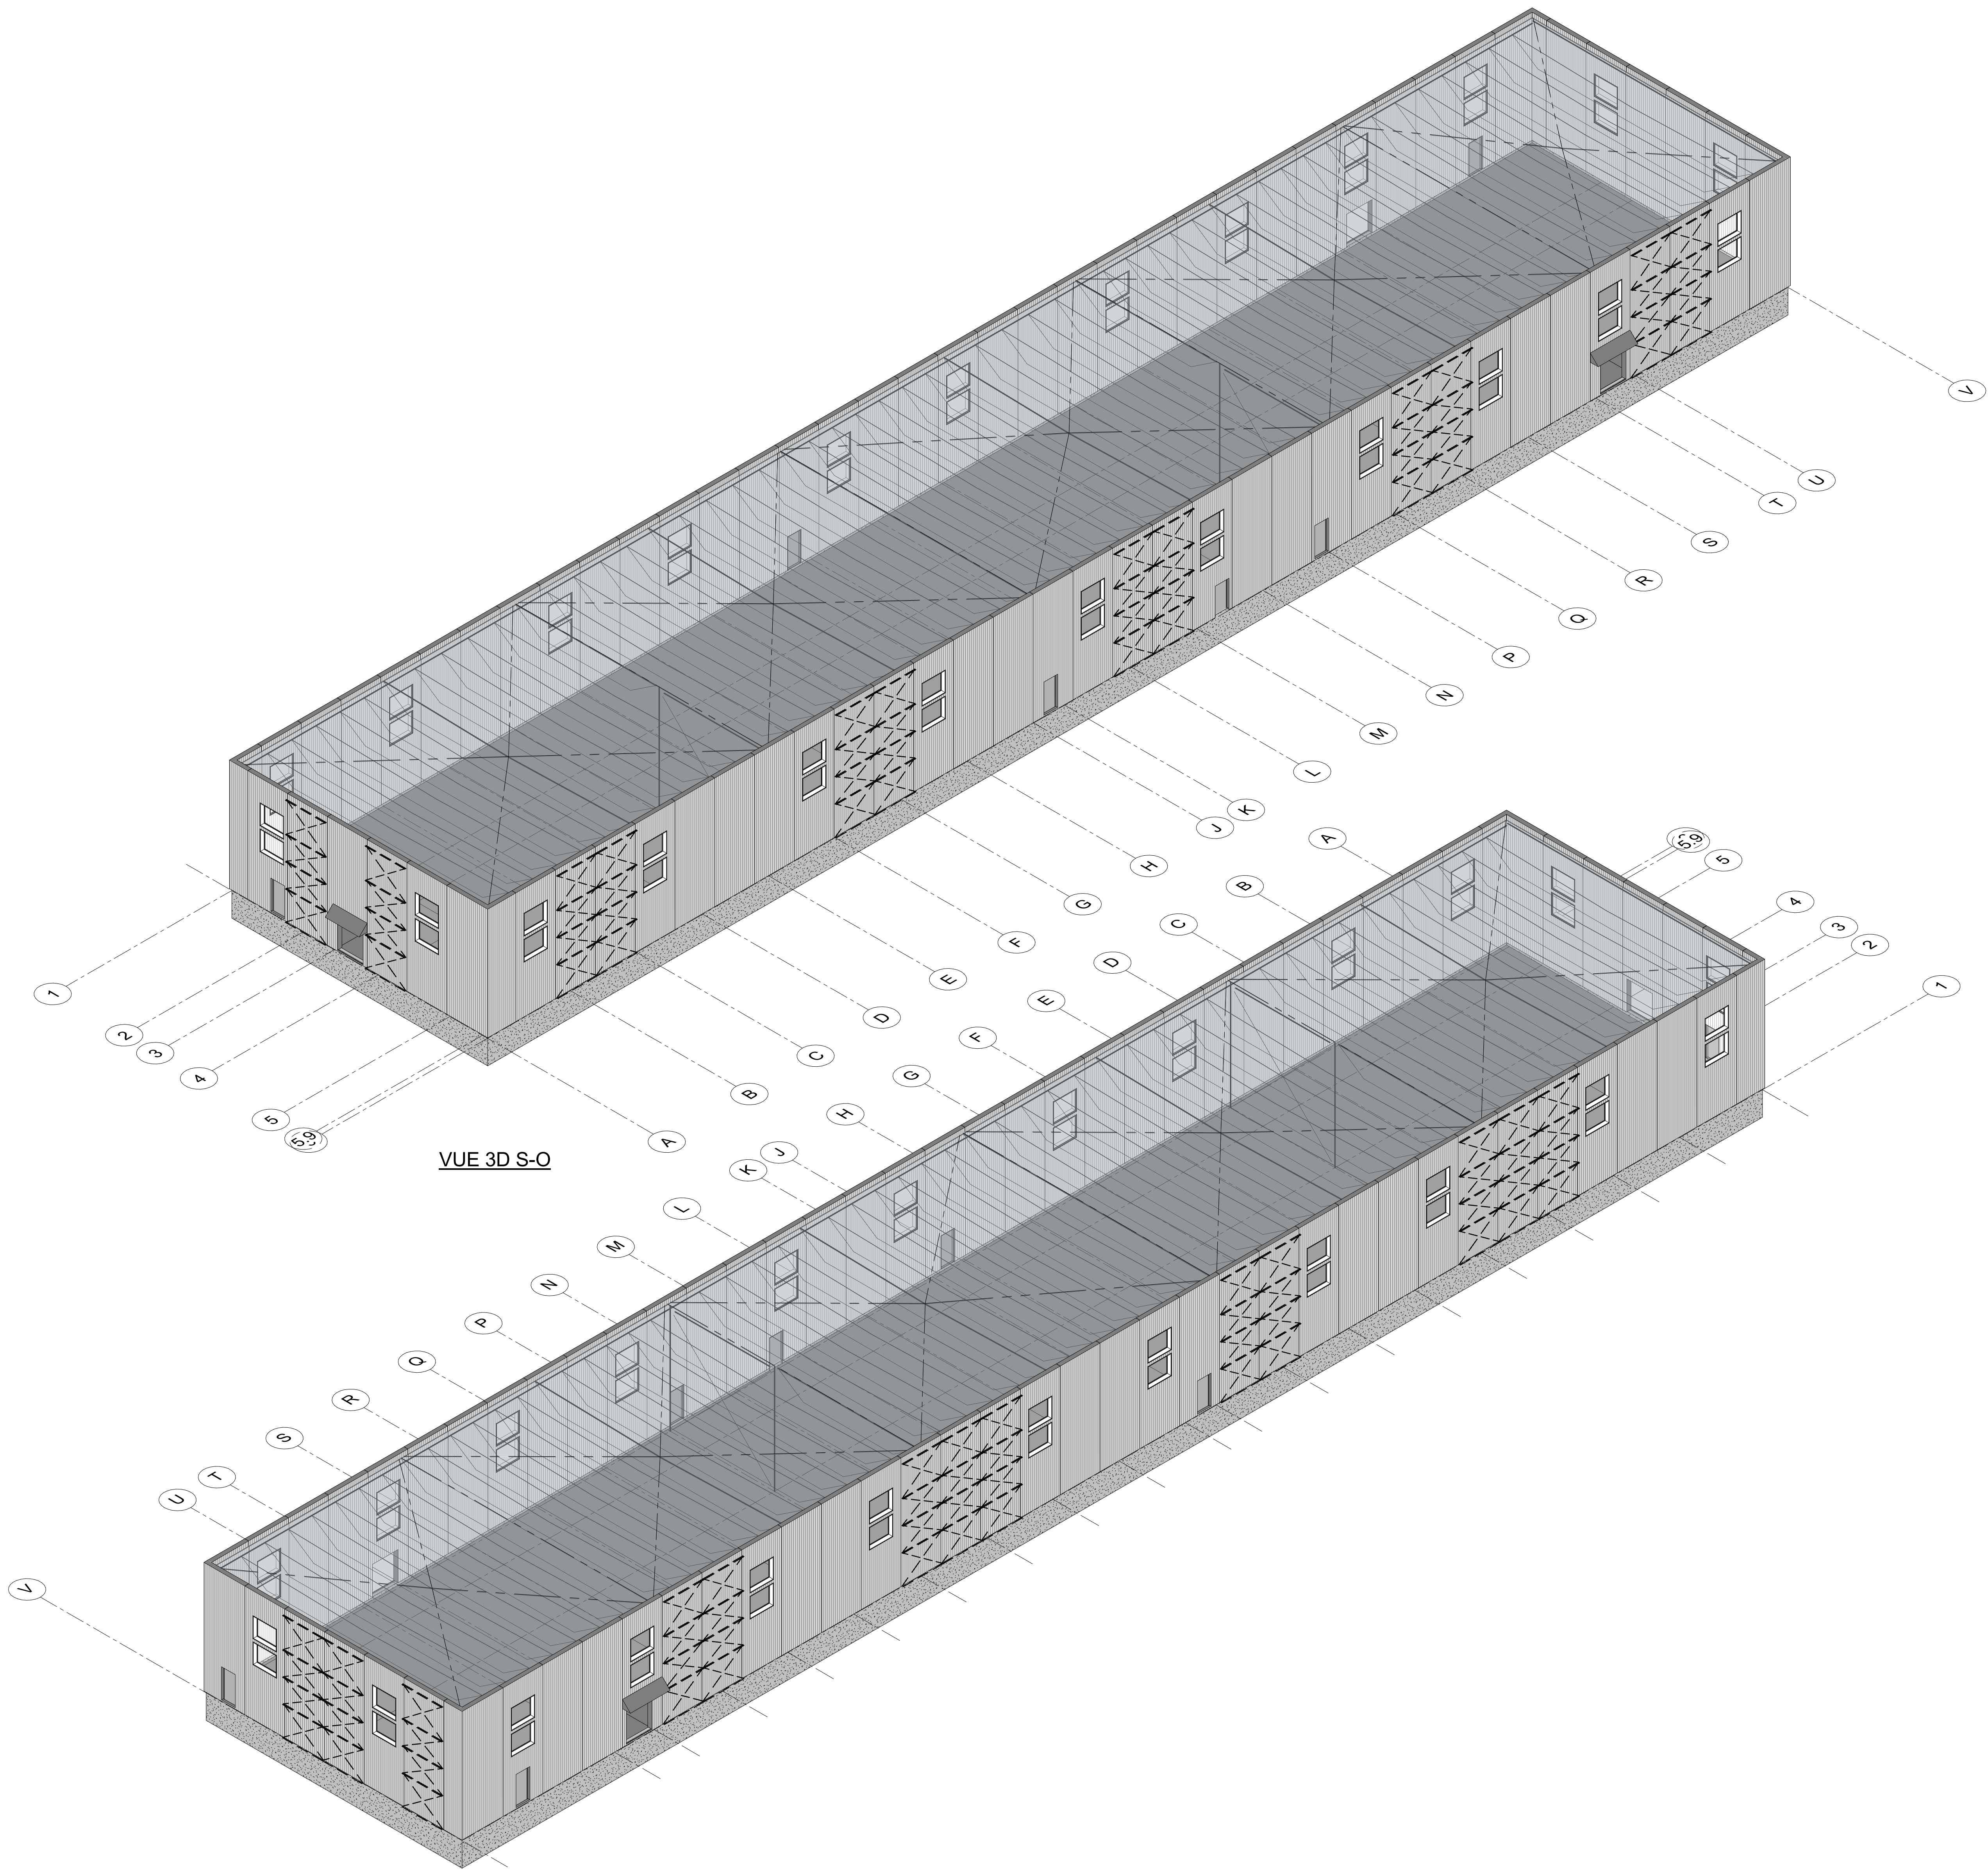

VUE 3D S-O

VUE 3D N-E

NOTE POUR LE CONTRACTEUR/ÉRECTEUR:
IL EST STRICTEMENT DÉFENDU DE MODIFIER, COPIER, REPRODUIRE OU DE DISTRIBUER CES DESSINS OU QUELQUES REPRÉSENTATIONS DE CES DESSINS, PAR TOUTES SOURCES DE MÉDIA INCLUANT ÉLECTRONIQUEMENT, SANS L'APPROBATION ÉCRITE DE GROUPE CANAM INC.


LISTE DES FEUILLES PRÉLIMINAIRES	
EsMx001	CROQUIS PRÉLIMINAIRE - VUES 3D
EsMx101	CROQUIS PRÉLIMINAIRE - PLAN D'ANCRAGE
EsMx201	CROQUIS PRÉLIMINAIRE - PLAN DE MEZZANINE
EsMx301	CROQUIS PRÉLIMINAIRE - PLAN DE PONT ROULANT
EsMx401	CROQUIS PRÉLIMINAIRE - PLAN DE TOIT
EsMx501	CROQUIS PRÉLIMINAIRE - ÉLEVATIONS
EsMx502	CROQUIS PRÉLIMINAIRE - ÉLEVATION, COUPE DE MUR ET CÉDULES
EsMx601	CROQUIS PRÉLIMINAIRE - DÉTAILS

[Cliquez ici pour modèle 3D](#)

PRÉLIMINAIRE

NE DOIT PAS SERVIR À LA CONSTRUCTION

REVISION	DATE	DESCRIPTION	DESS	VER
DEVANT DE PROJET				
		-		
		-		
		-		
		-		
		-		
DESSIN				
DESSINÉ PAR	CONÇU PAR	INGÉNIEUR DU PROJET	ÉCHELLE:	
Donald Piché				
VERIFIÉ PAR	INGÉNIEURS CONSEILS / ARCHITECTES		DATE (jj/mm/aaaa)	
			2026-04-23	
CLIENT: Construction de Défense Canada				

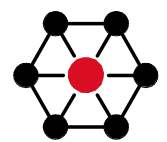**CANAM**

11505, 1re Avenue, bureau 500, Saint-Georges Beaulac
Québec, Canada, G5Y 7X5
Téléphone : (418) 228-8031
Sans frais : (877) 459-8049
www.canam.com

SCÉAU PROFESSIONNEL

PROJET

6 Nouveaux Bâtiments Préfabriqués
St-Jean-sur-le-Richelieu, QC

TITRE

CROQUIS PRÉLIMINAIRE - VUES 3D

NUMÉRO CONTRAT	NUMÉRO DESSIN	DIVISION	REVISION
P2026-093	EsMx001		



ACCUMULATION DE NEIGE (AUTOUR DES UNITES RTU-1)


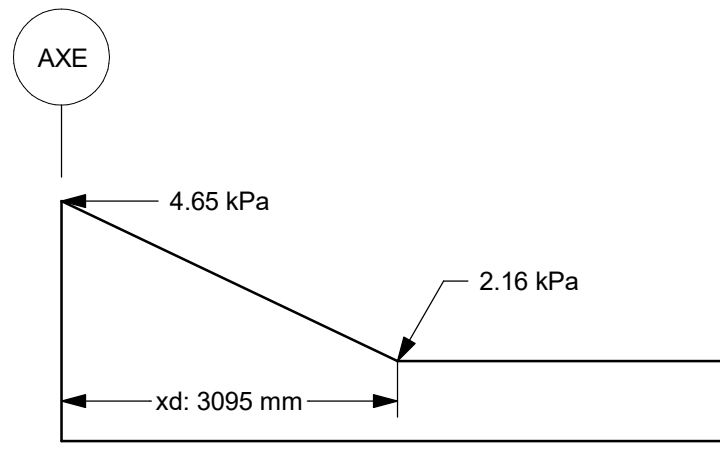


DIAGRAMME DE SOULEVEMENT BRUT (NON PONDERÉ)

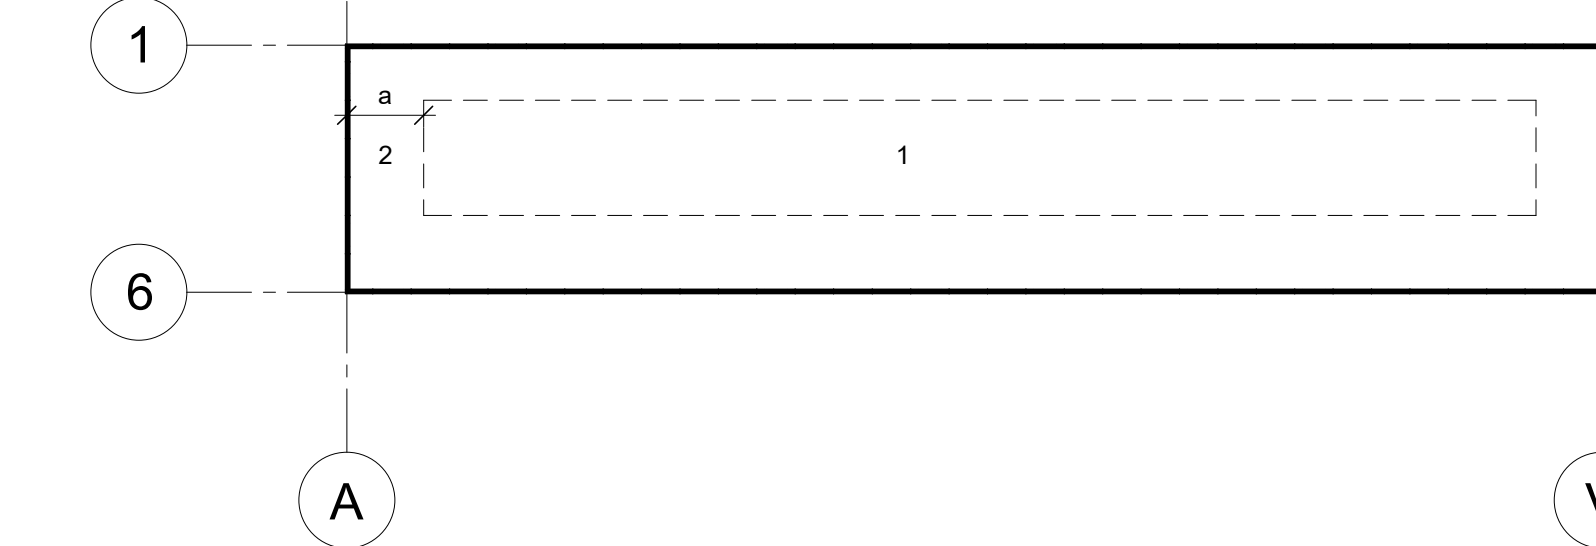

PRESSION POSITIVE DU VENT
(NON PONDEREE) +0.34 kPa

NOTE POUR LE CONTRACTEUR/ÉRECTEUR:

IL EST STRICTEMENT DEFENDU DE MODIFIER, COPIER, REPRODUIRE OU DE DISTRIBUER CES DESSINS OU QUELQUES REPRESENTATIONS DE CES DESSINS, PAR TOUTES SOURCES DE MEDIA INCLUANT ELECTRONIQUEMENT, SANS L'APPROBATION ECRITE DE GROUPE CANAM INC.

TOIT

DESSUS DE PILASTRE DOP : -600
DESSUS DE PILASTRE : -300
DESSUS DE LA DALLE : 0
DESSUS DE LA FONDATION : 200
HAUTEUR LIBRE : 7 000
DESSUS D'ACIER : 8 300
HAUTEUR DE PARAPET : 350
DESSUS DE PARAPET : 8 656

CHARGES

C.M. : 0.85 kPa
Coll. : 0.25 kPa
Sd : 2.2 kPa
Sr : 0.4 kPa
C.D. x Cw : 0.8 kPa
C.V. au toit : 0 kPa
Ch. de neige au toit : 1.0
Lr : 1.0
Vent qe 1/50 : 0.41 kPa


Seisme (Sol de classe D assumé)

I_s : 1.0
S_w(0.2) : 0.737
S_w(0.5) : 0.558
S_w(1.0) : 0.335
S_w(2.0) : 0.160
S_w(5.0) : 0.0447
S_w(10.0) : 0.014
PGA : 0.442
PGV : 0.397

• Code Applicable : Code National du Bâtiment du Canada
Code du bâtiment du Québec, dernières éditions adoptées
Code de Pratique Standard ICCA.

• Type de sol assumé : classe D

• NOTE :
1. Si toutefois la catégorie d'emplacement devient E ou F selon le rapport géotechnique, le concept structurel préliminaire (localisation et géométrie des contreventements, etc.) devra être validé et coordonné par l'ingénieur de Canam.

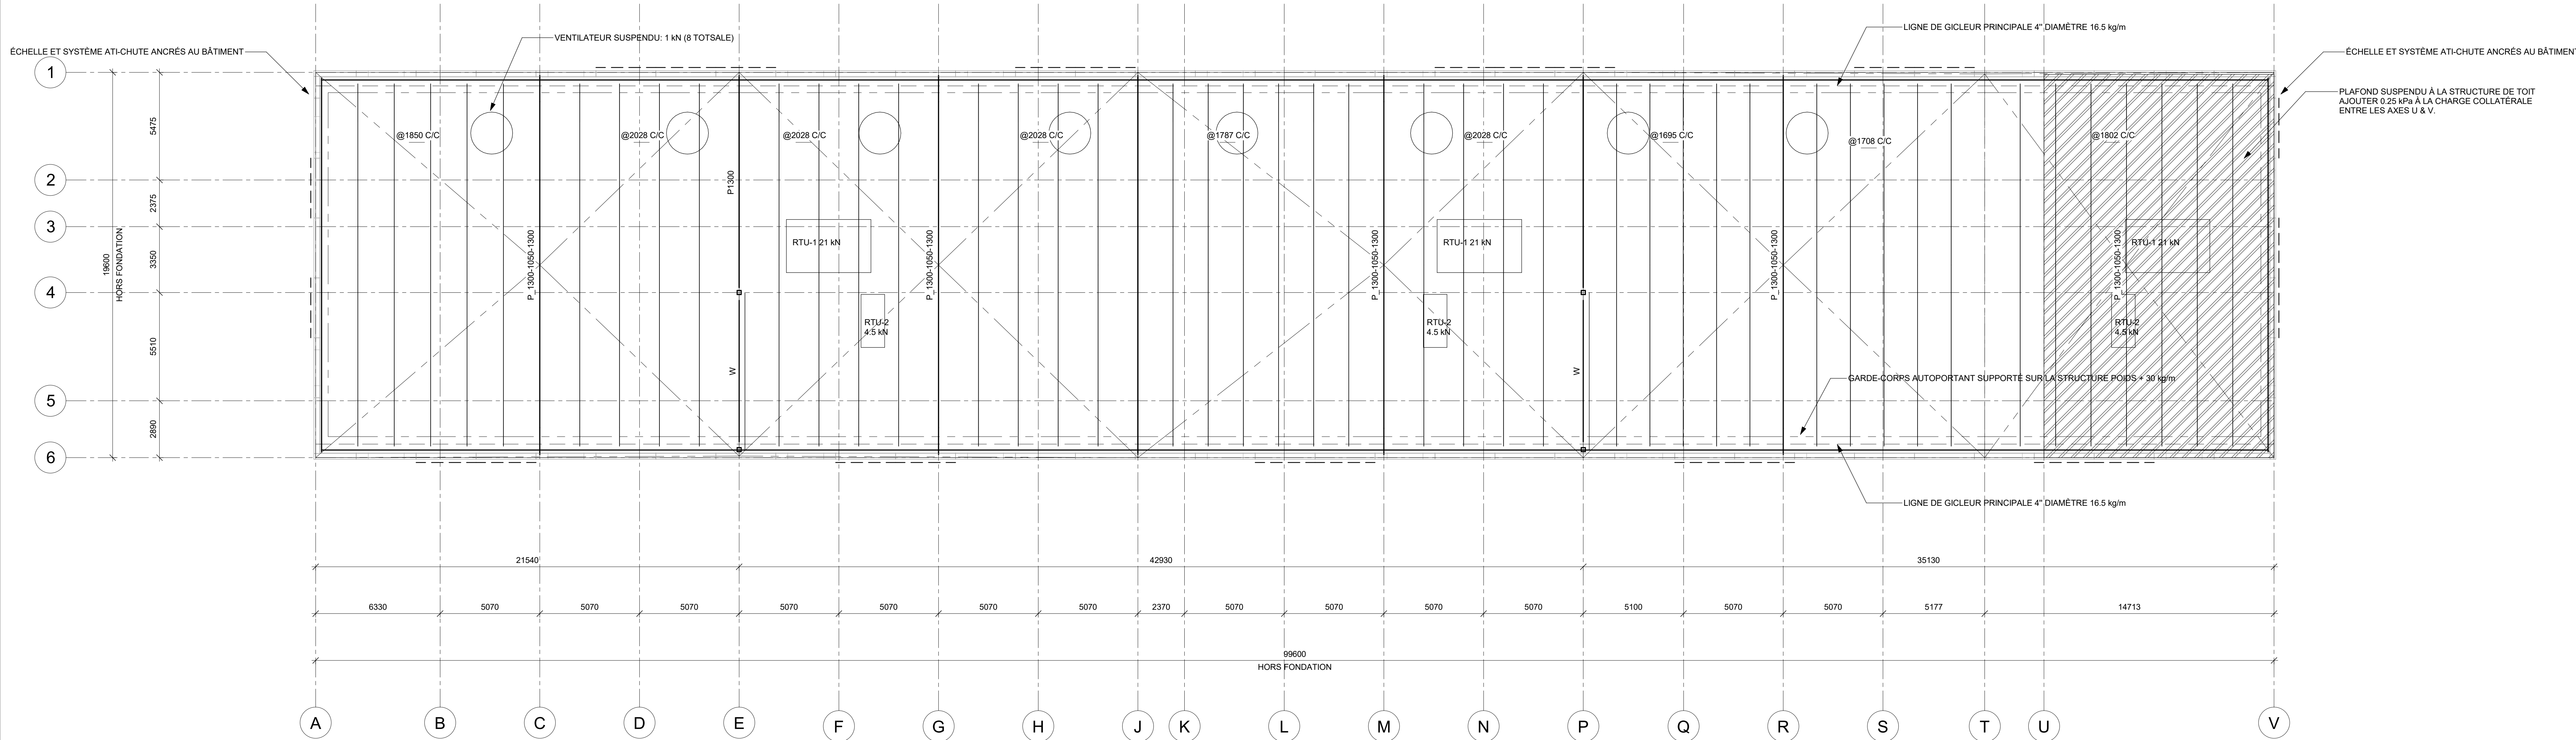

PLAN DE TOIT
1-125

PRÉLIMINAIRE

NE DOIT PAS SERVIR À LA
CONSTRUCTION

REVISION	DATE	DESCRIPTION	DESS	VER
----------	------	-------------	------	-----

GERANT DE PROJET	-
-	-
-	-
-	-

DESSIN	CONÇU PAR	INGÉNIEUR DU PROJET	ÉCHELLE
DESSINÉ PAR	Donald Piché		Comme indiqué
VÉRIFIÉ PAR	INGÉNIEURS CONSEILS / ARCHITECTES	DATE (mm/aaaa)	2026-04-23

CLIENT: Construction de Défense Canada



SCAUX PROFESSIONNEL

PROJET

6 Nouveaux Bâtiments Préfabriqués
St-Jean-sur-le-Richelieu, QC

TITRE

CROQUIS PRÉLIMINAIRE - PLAN DE
TOIT

NUMERO CONTRAT	NUMERO DESSIN	DIVISION	REVISION
----------------	---------------	----------	----------

EsMx401



