



ACCUMULATION DE NEIGE (AUTOUR DES UNITES RTU-1)


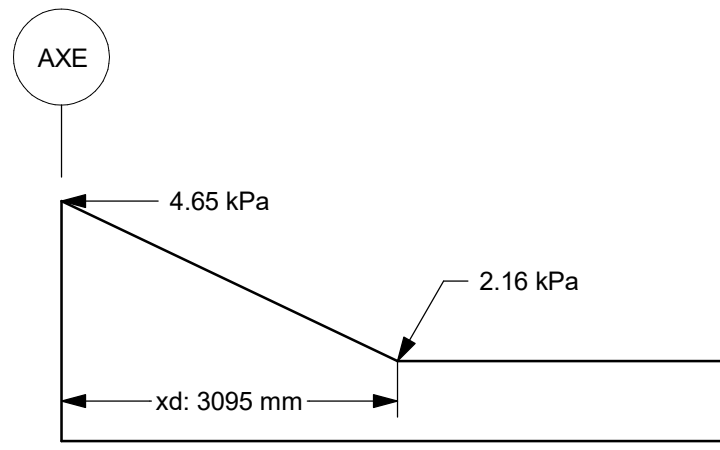


DIAGRAMME DE SOULEVEMENT BRUT (NON PONDERÉ)

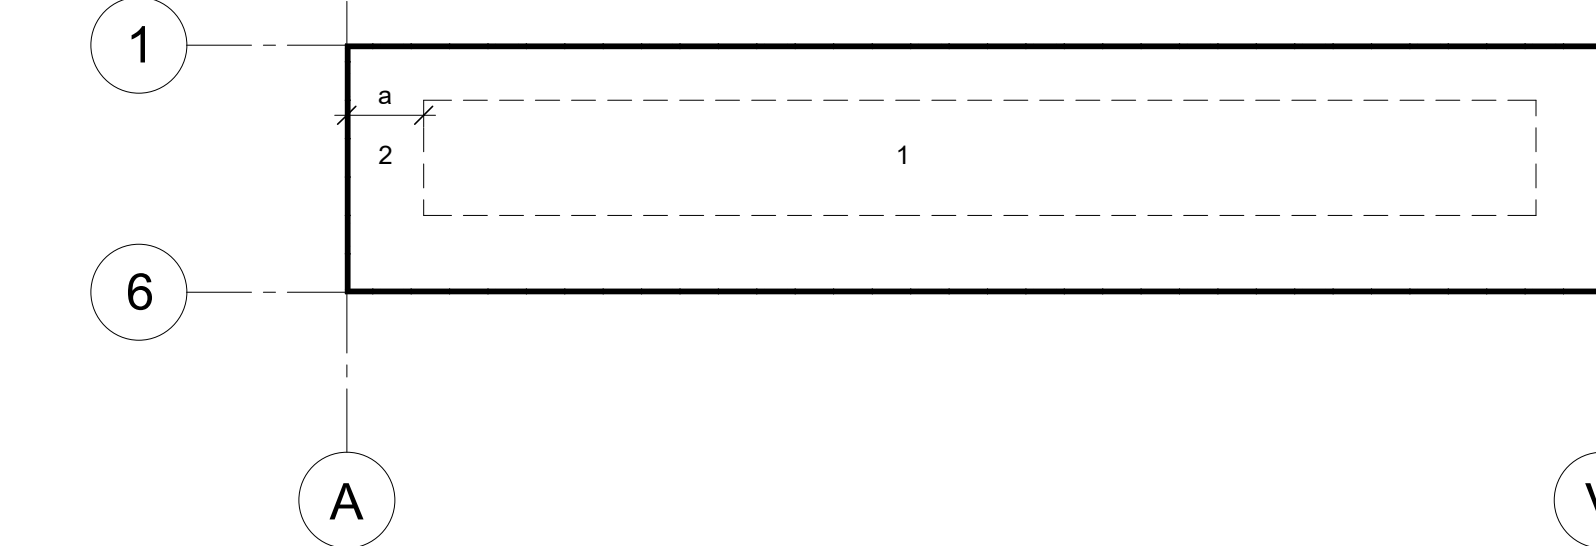

NOTE POUR LE CONTRACTEUR/ÉRECTEUR:

IL EST STRICTEMENT DEFENDU DE MODIFIER, COPIER, REPRODUIRE OU DE DISTRIBUER CES DESSINS OU QUELQUES REPRESENTATIONS DE CES DESSINS, PAR TOUTES SOURCES DE MEDIA INCLUANT ELECTRONIQUEMENT, SANS L'APPROBATION ECRITE DE GROUPE CANAM INC.

TOIT

DESSUS DE PILASTRE DOP : -600  
DESSUS DE PILASTRE : -300  
DESSUS DE LA DALLE : 0  
DESSUS DE LA FONDATION : 200  
HAUTEUR LIBRE : 7 000  
DESSUS D'ACIER : 8 300  
HAUTEUR DE PARAPET : 350  
DESSUS DE PARAPET : 8 656

CHARGES

C.M. : 0.85 kPa  
Coll. : 0.25 kPa  
Sa : 2.2 kPa  
Sr : 0.4 kPa  
C.D. x Cw : 0.8 kPa  
C.V. au toit : 0 kPa  
Charge de neige au toit : 1.0  
Lr : 1.0  
Vent qe 1/50 : 0.41 kPa


Seisme (Sol de classe D assumé)

I<sub>s</sub> : 1.0  
S<sub>w</sub>(0.2) : 0.737  
S<sub>w</sub>(0.5) : 0.558  
S<sub>w</sub>(1.0) : 0.335  
S<sub>w</sub>(2.0) : 0.160  
S<sub>w</sub>(5.0) : 0.0447  
S<sub>w</sub>(10.0) : 0.014  
PGA : 0.442  
PGV : 0.397

• Code Applicable : Code National du Bâtiment du Canada  
Code du bâtiment du Québec, dernières éditions adoptées  
Code de Pratique Standard ICCA.

• Type de sol assumé : classe D

• NOTE :  
1. Si toutefois la catégorie d'emplacement devient E ou F selon le rapport géotechnique, le concept structural préliminaire (localisation et géométrie des contreventements, etc.) devra être validé et coordonné par l'ingénieur de Canam.

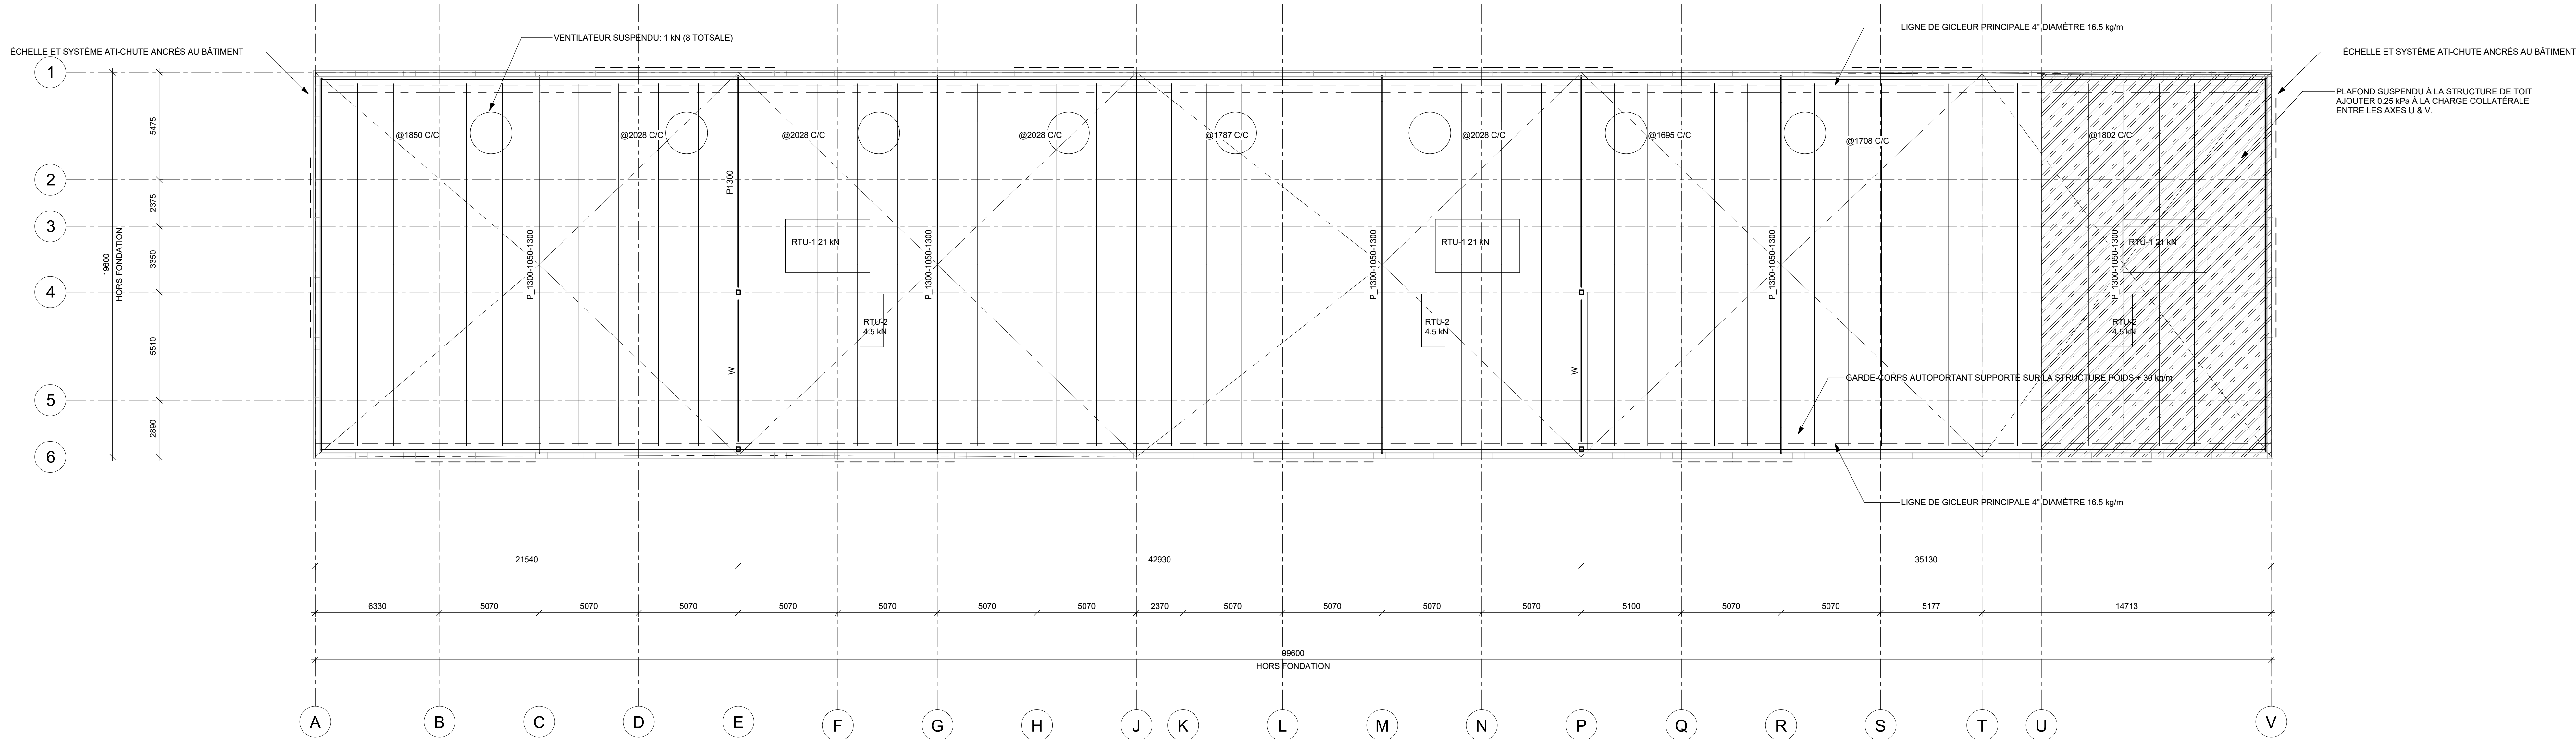

PLAN DE TOIT  
1-125

PRÉLIMINAIRE

NE DOIT PAS SERVIR À LA  
CONSTRUCTION

REVISION DATE DESCRIPTION DESSIN VER

GERANT DE PROJET

DESIGN

CONÇU PAR INGÉNIEUR DU PROJET ÉCHELLE: Comme indiqué

VERIFIÉ PAR INGÉNIEURS CONSEILS / ARCHITECTES DATE (mm/ann): 2026-04-23

CLIENT: Construction de Défense Canada



11505, 1<sup>re</sup> Avenue, bureau 500, Saint-Georges Beauce  
Québec, Canada G5Y 7X5  
Téléphone : (418) 228-8031  
Sans frais : (877) 459-8049  
www.canam.com

SCAUX PROFESSIONNEL

PROJET

6 Nouveaux Bâtiments Préfabriqués  
St-Jean-sur-le-Richelieu, QC

TITRE  
CROQUIS PRÉLIMINAIRE - PLAN DE  
TOIT

NUMERO CONTRAT P2026-093

NUMERO DESSIN EsMx401

DIVISION

REVISION

Initiales