
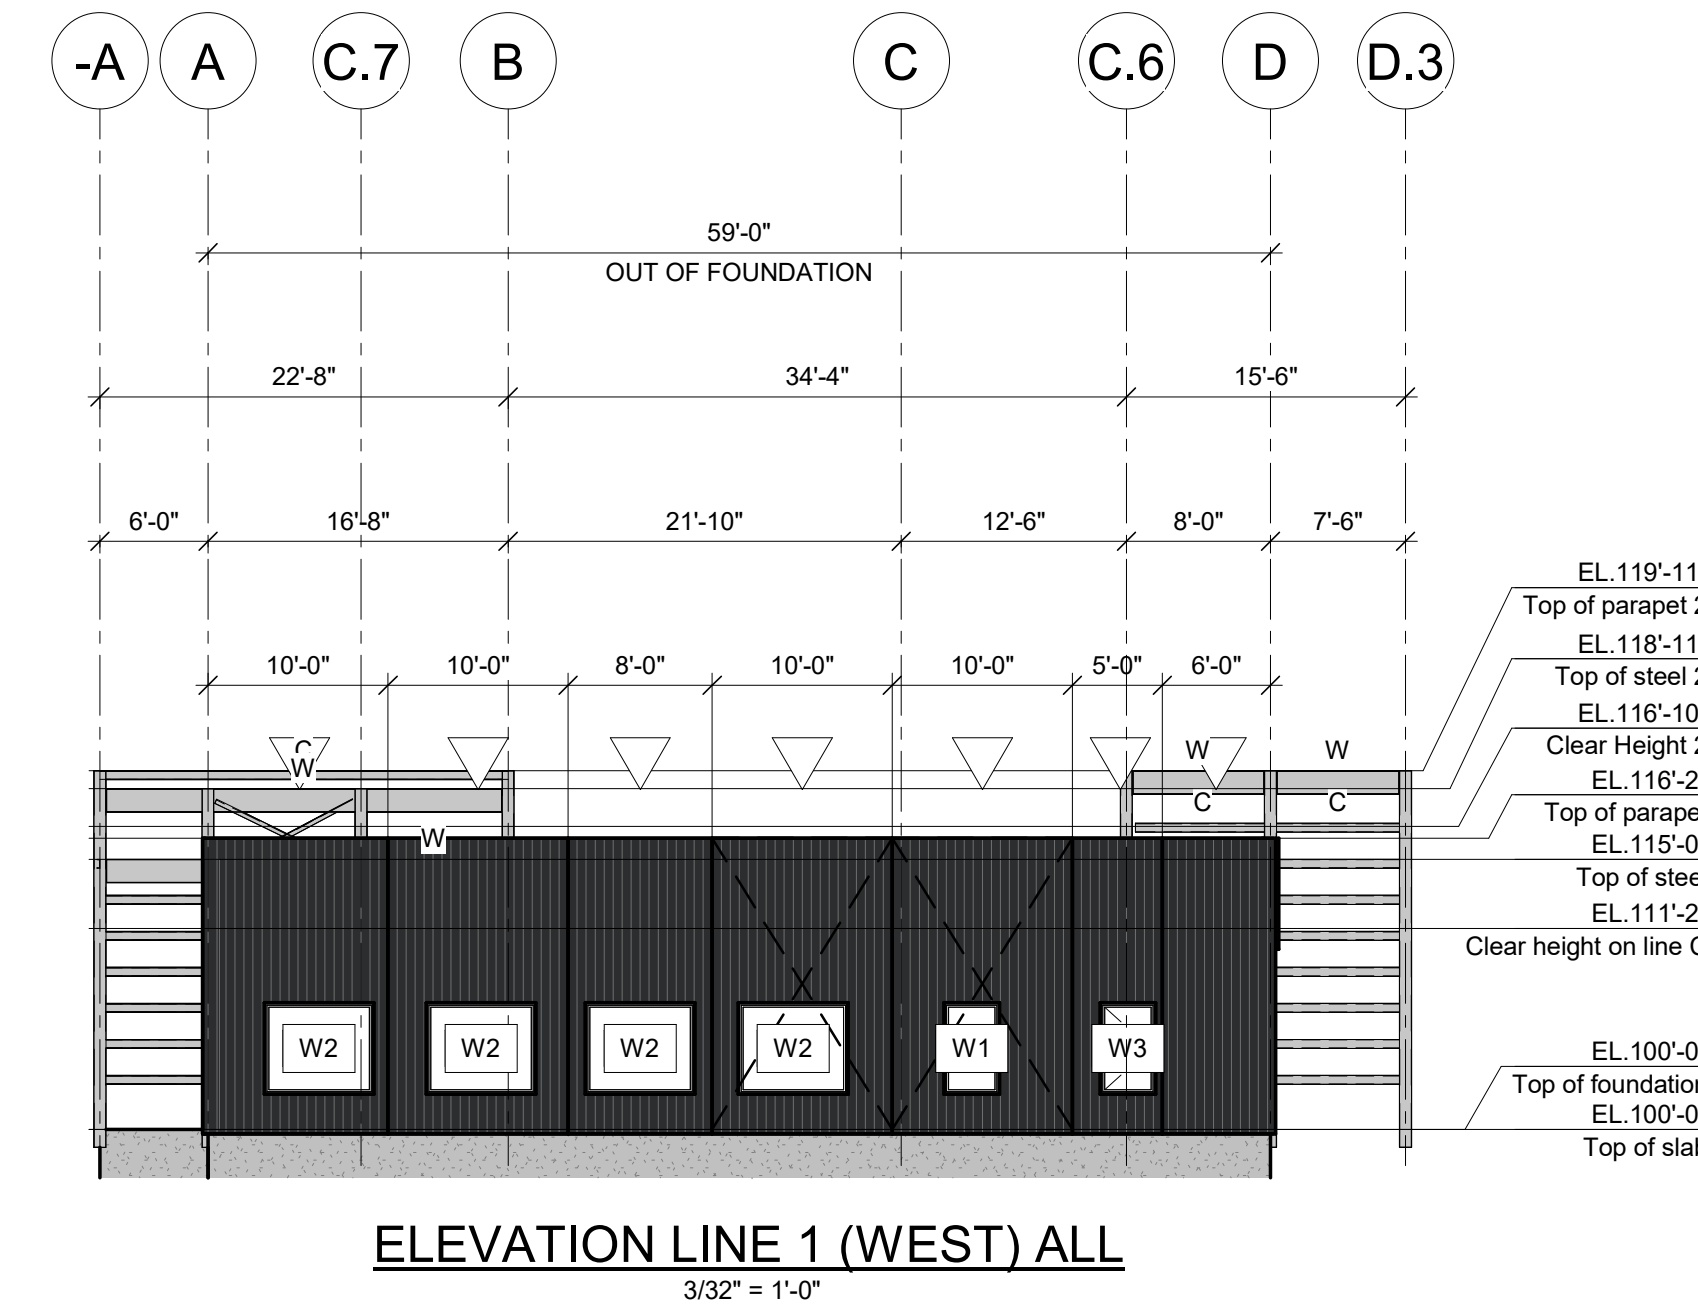
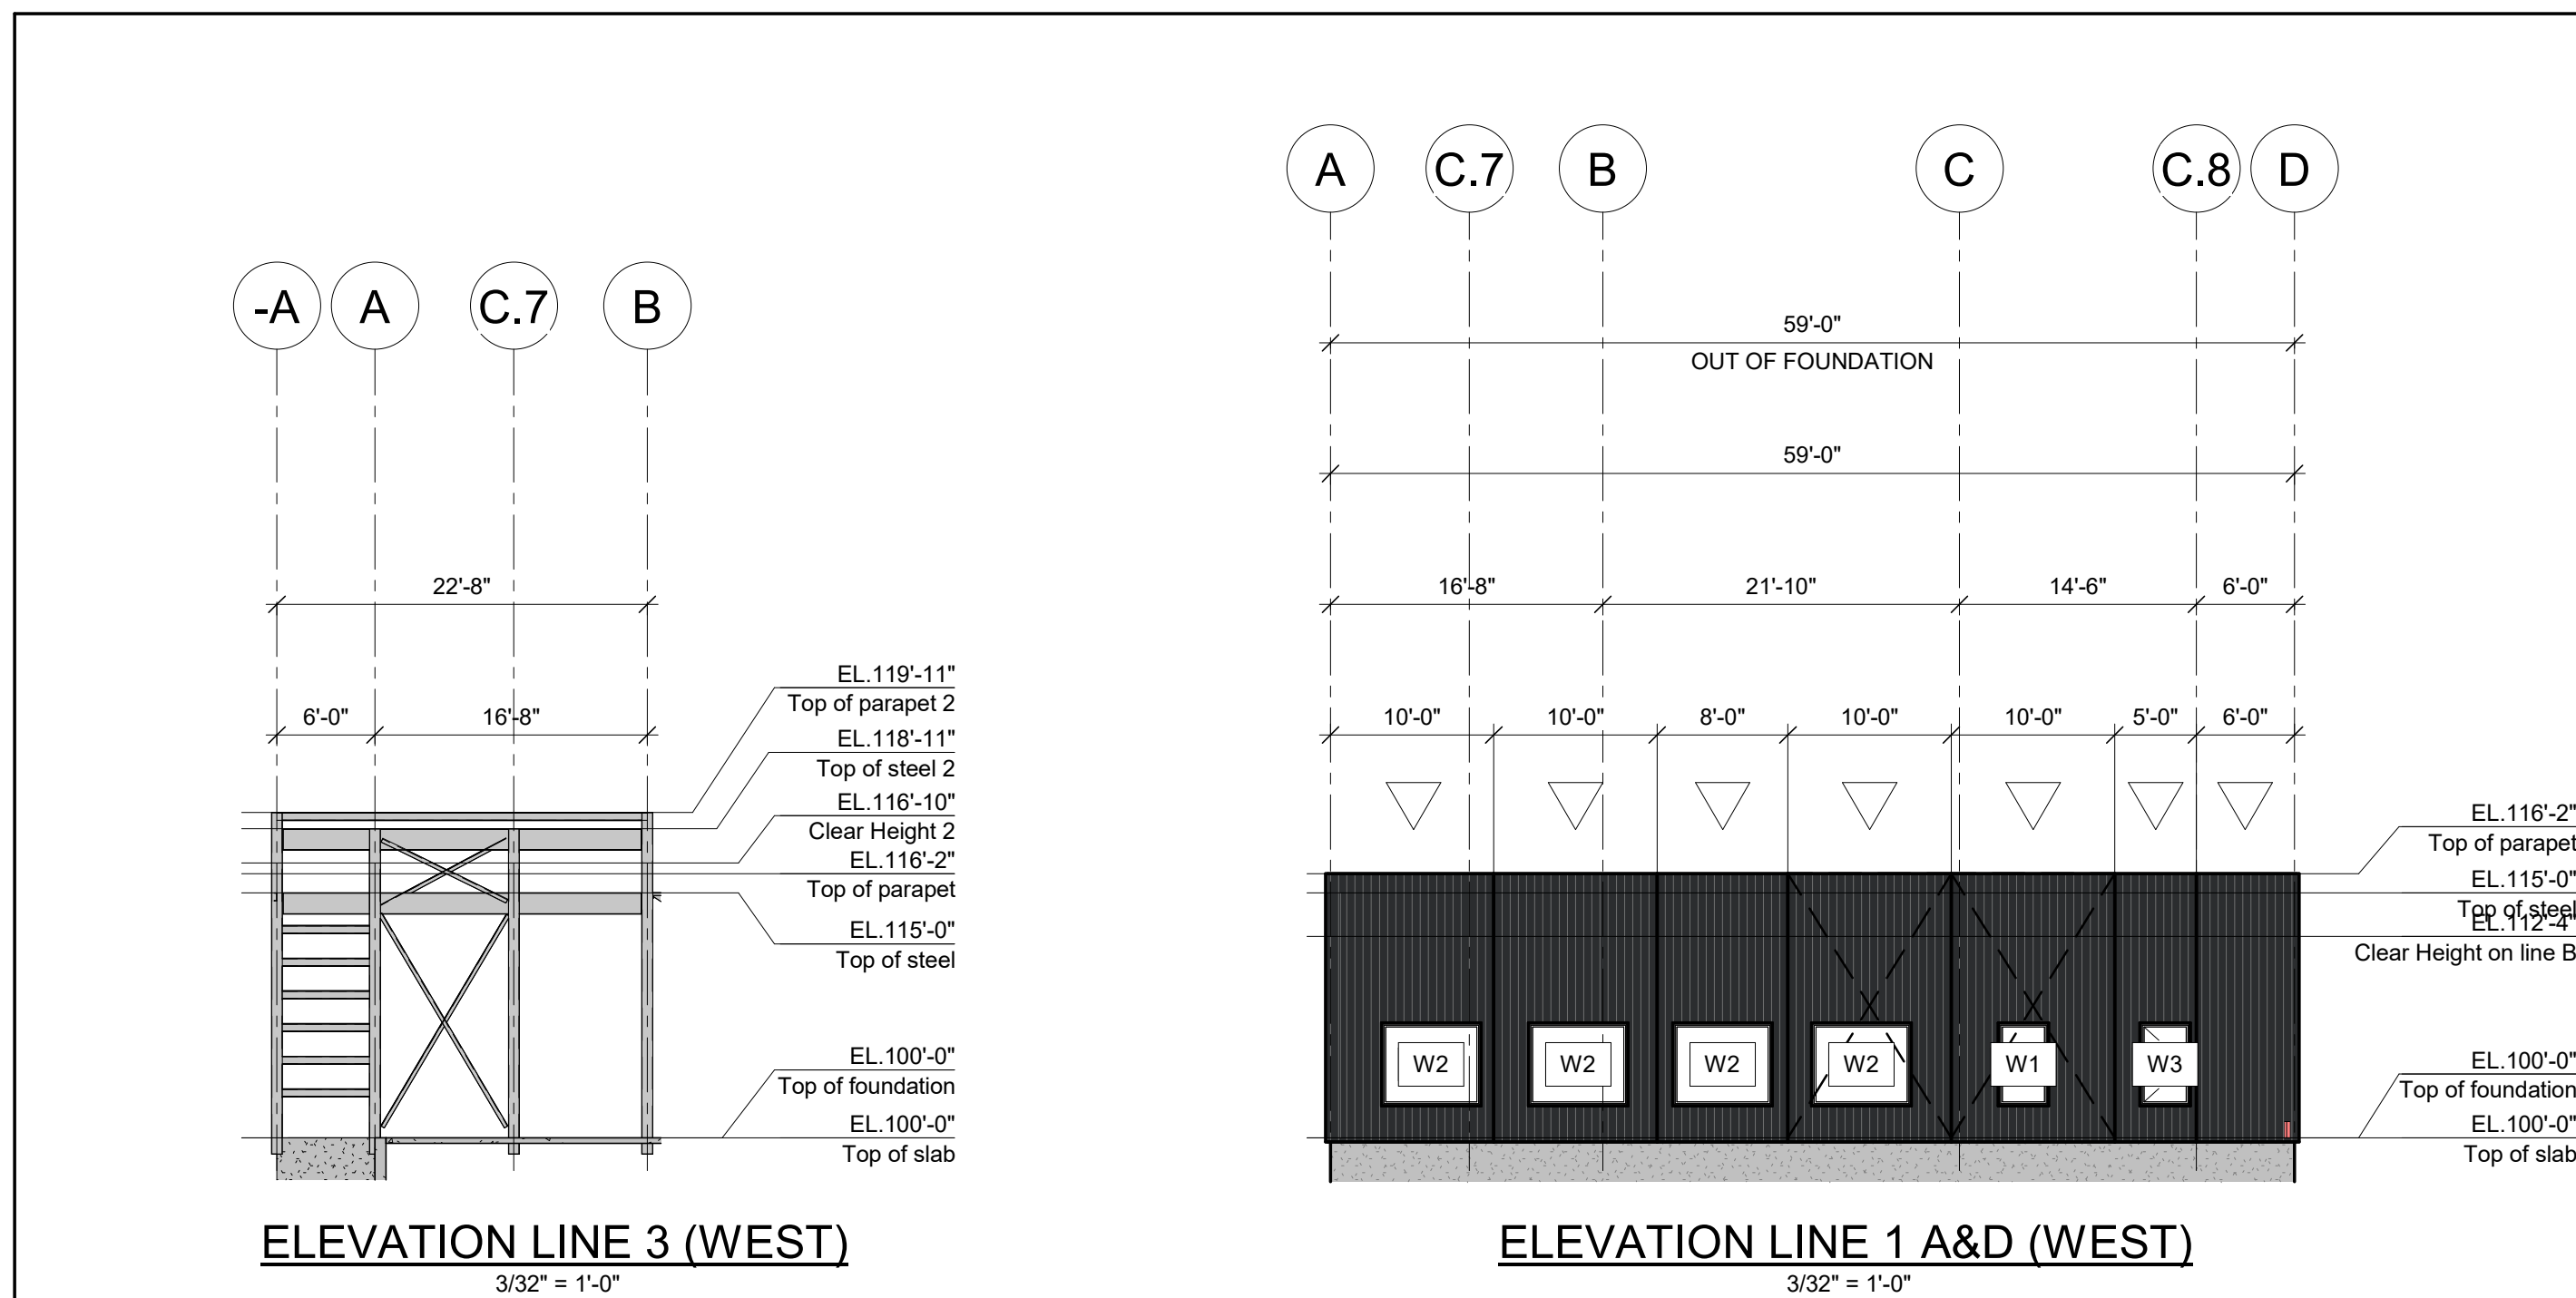
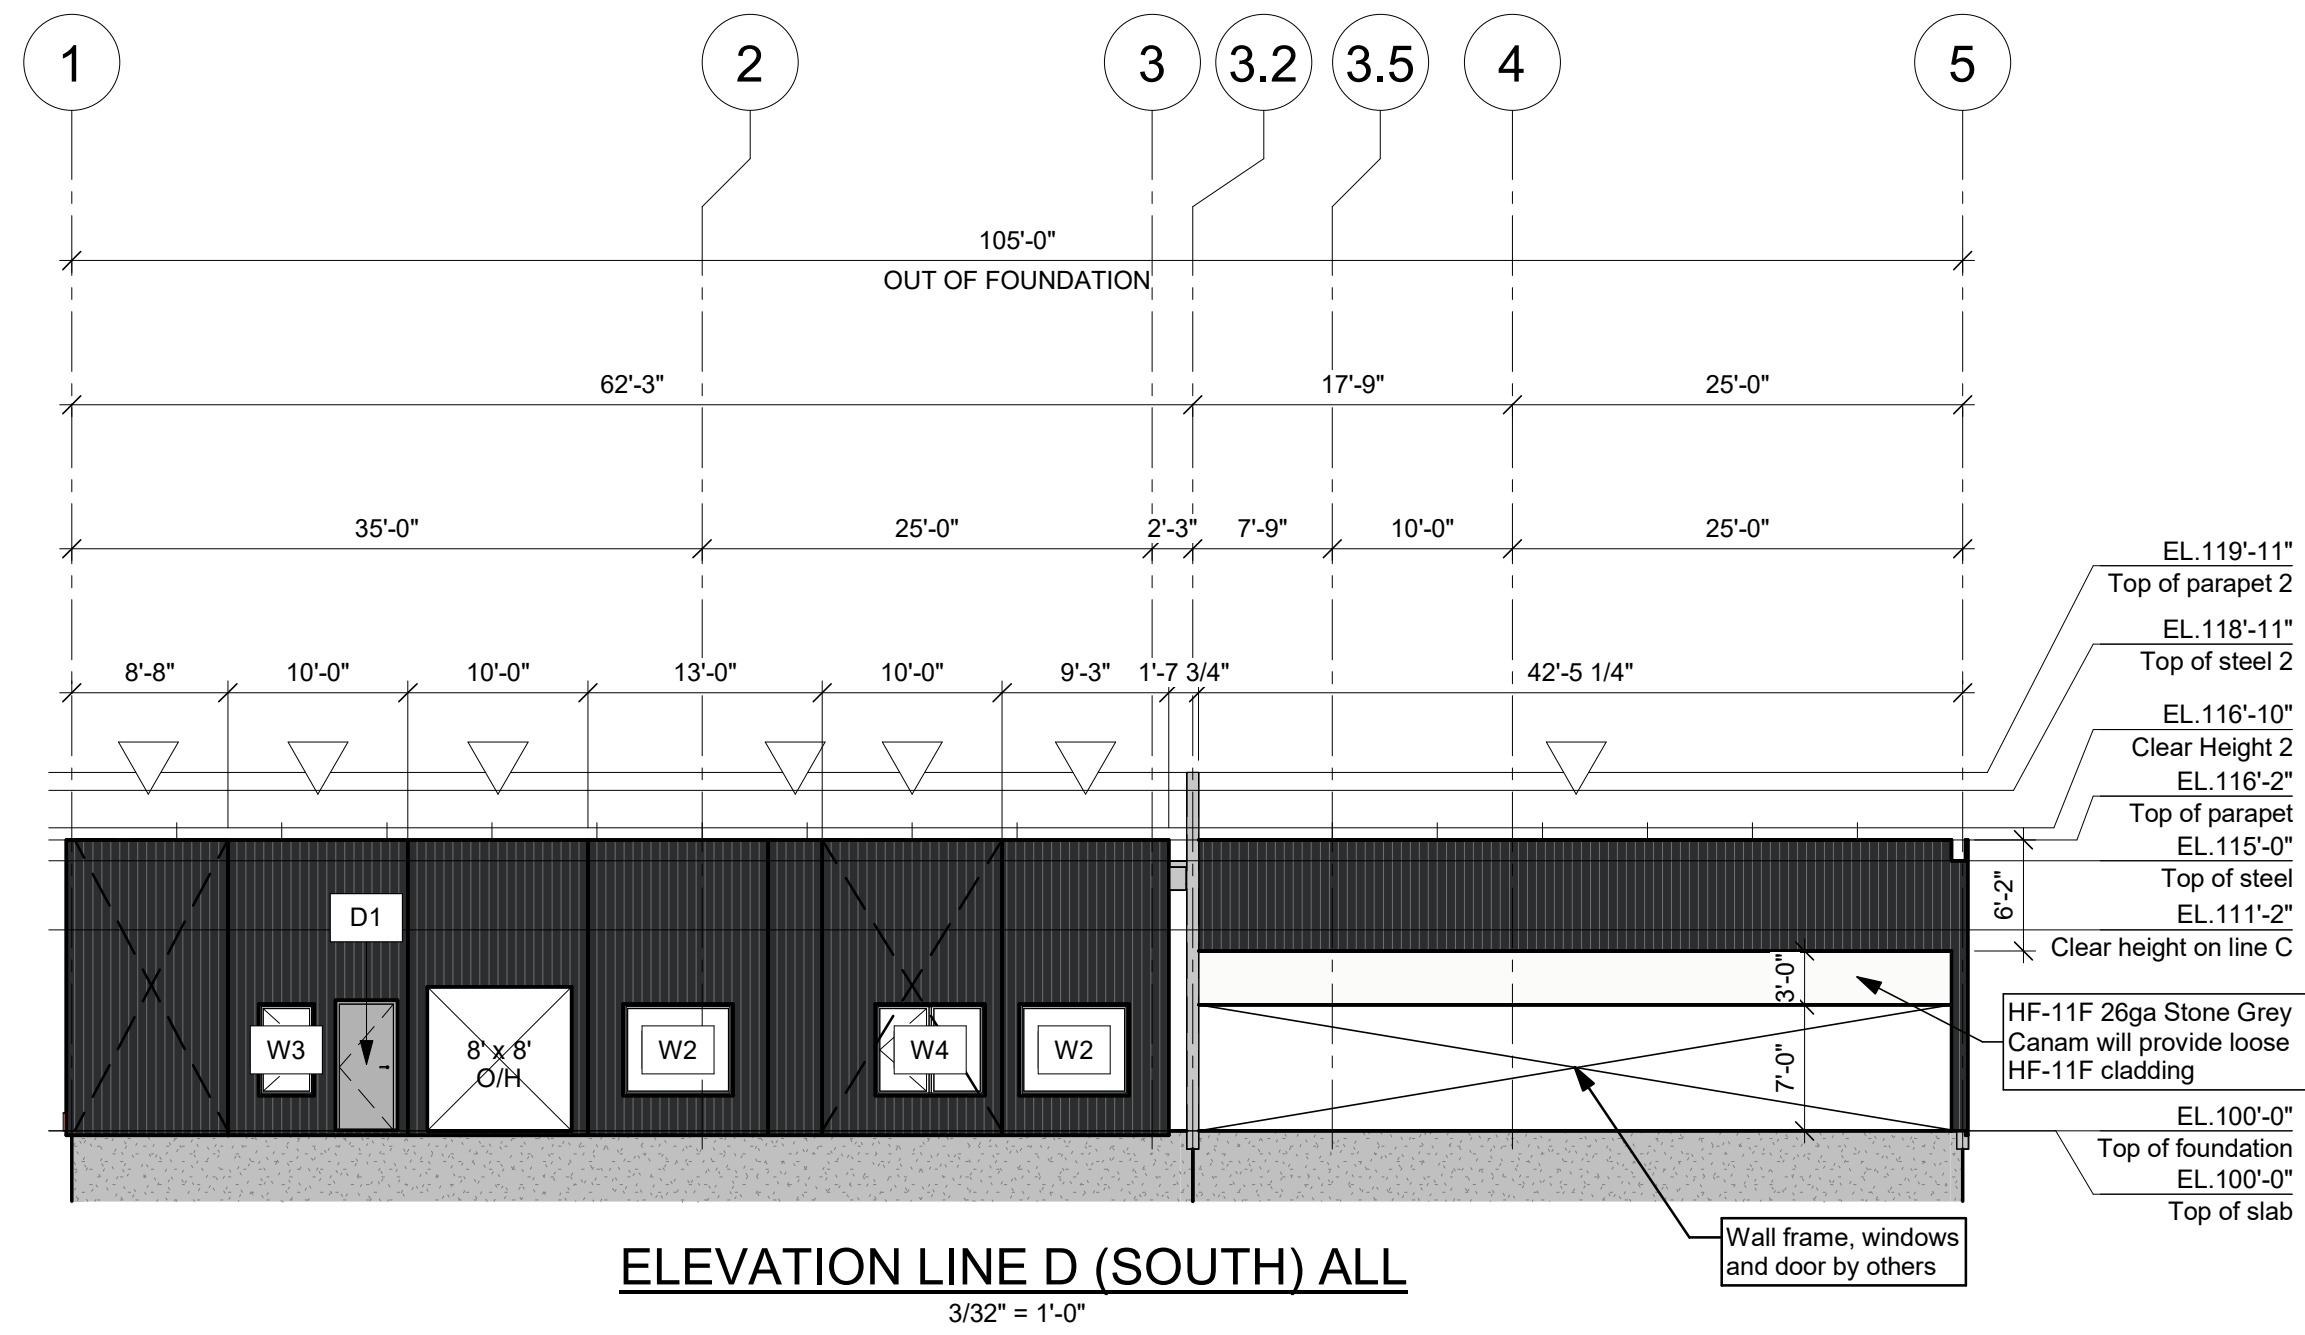
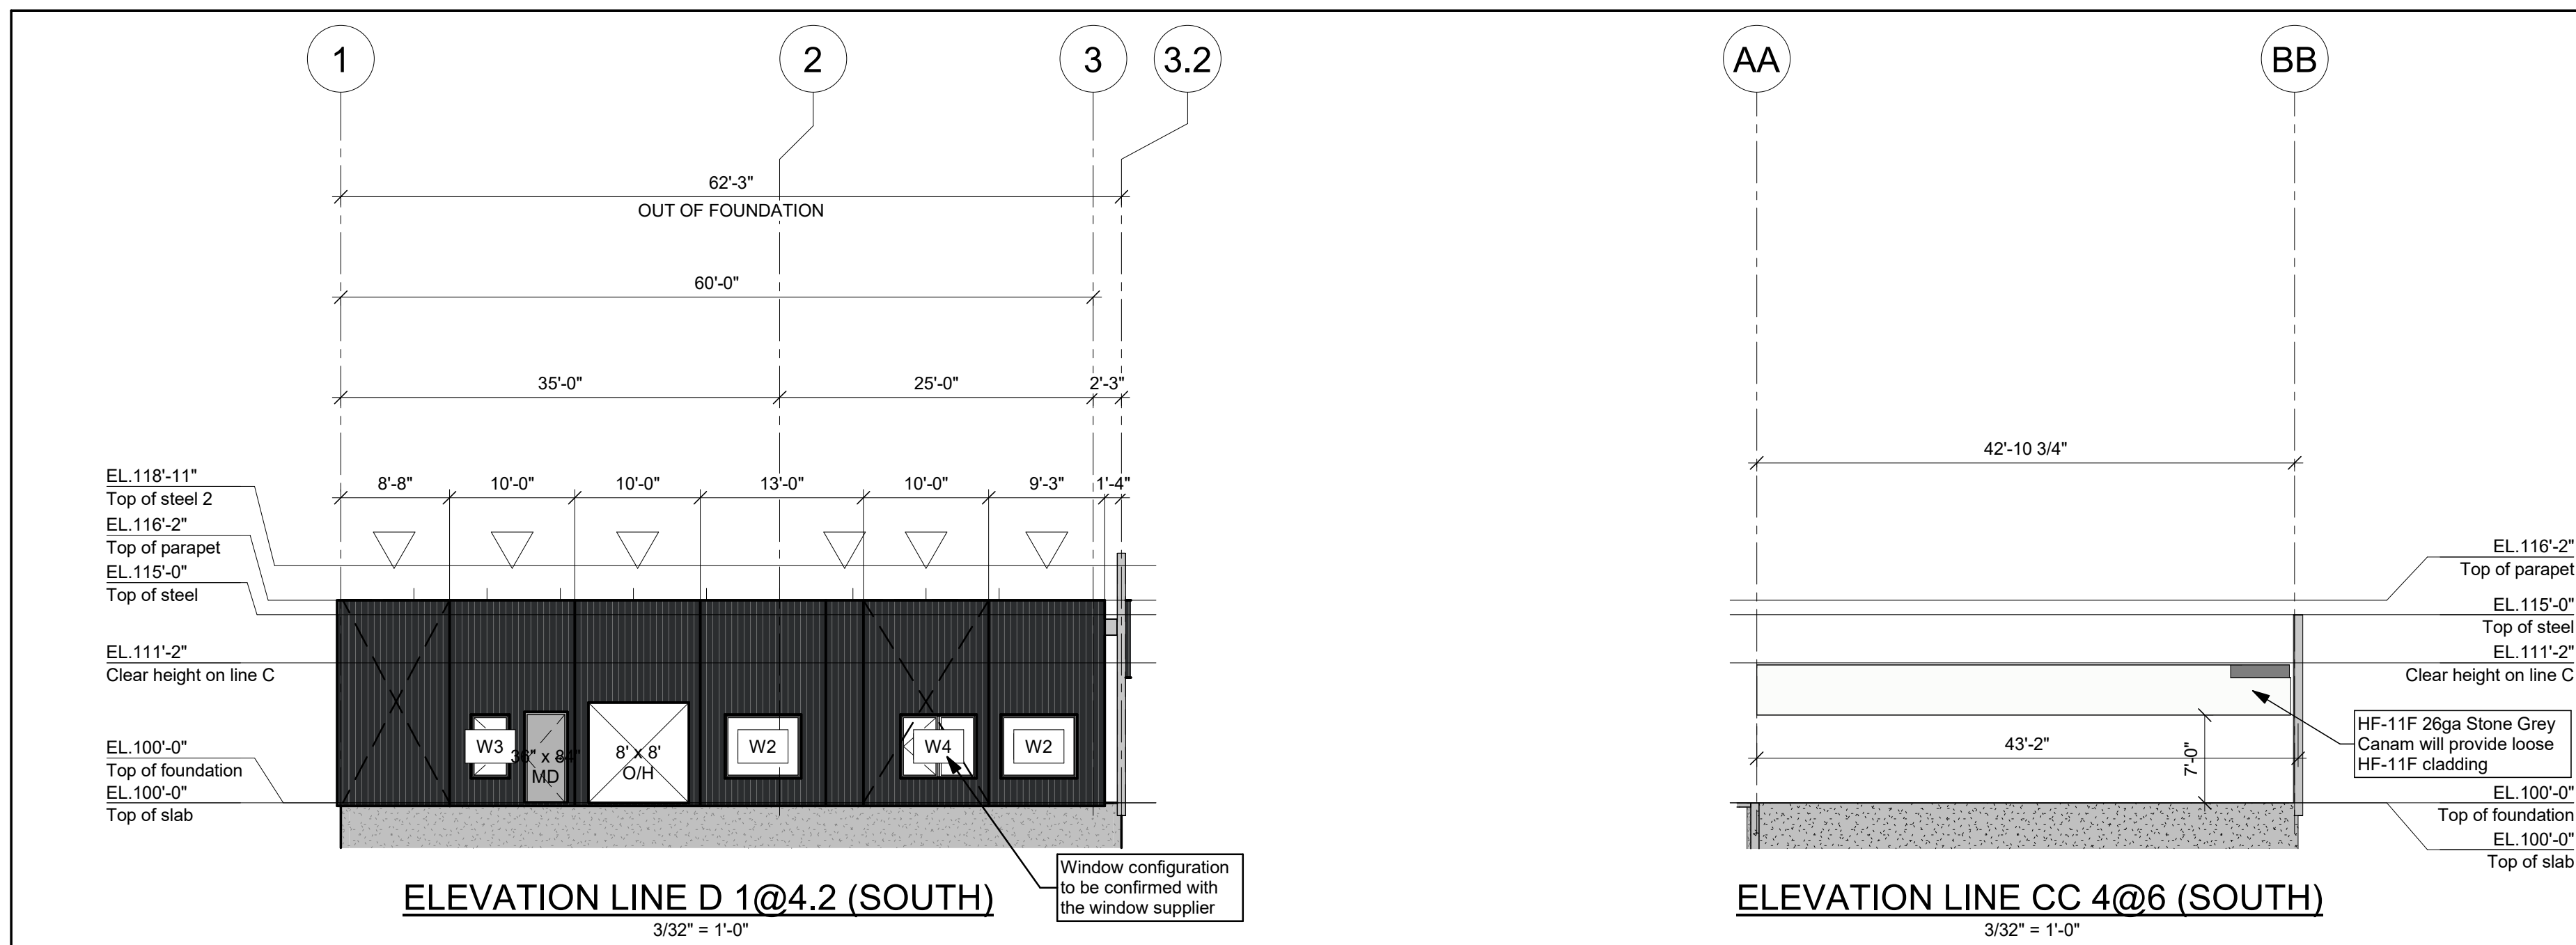
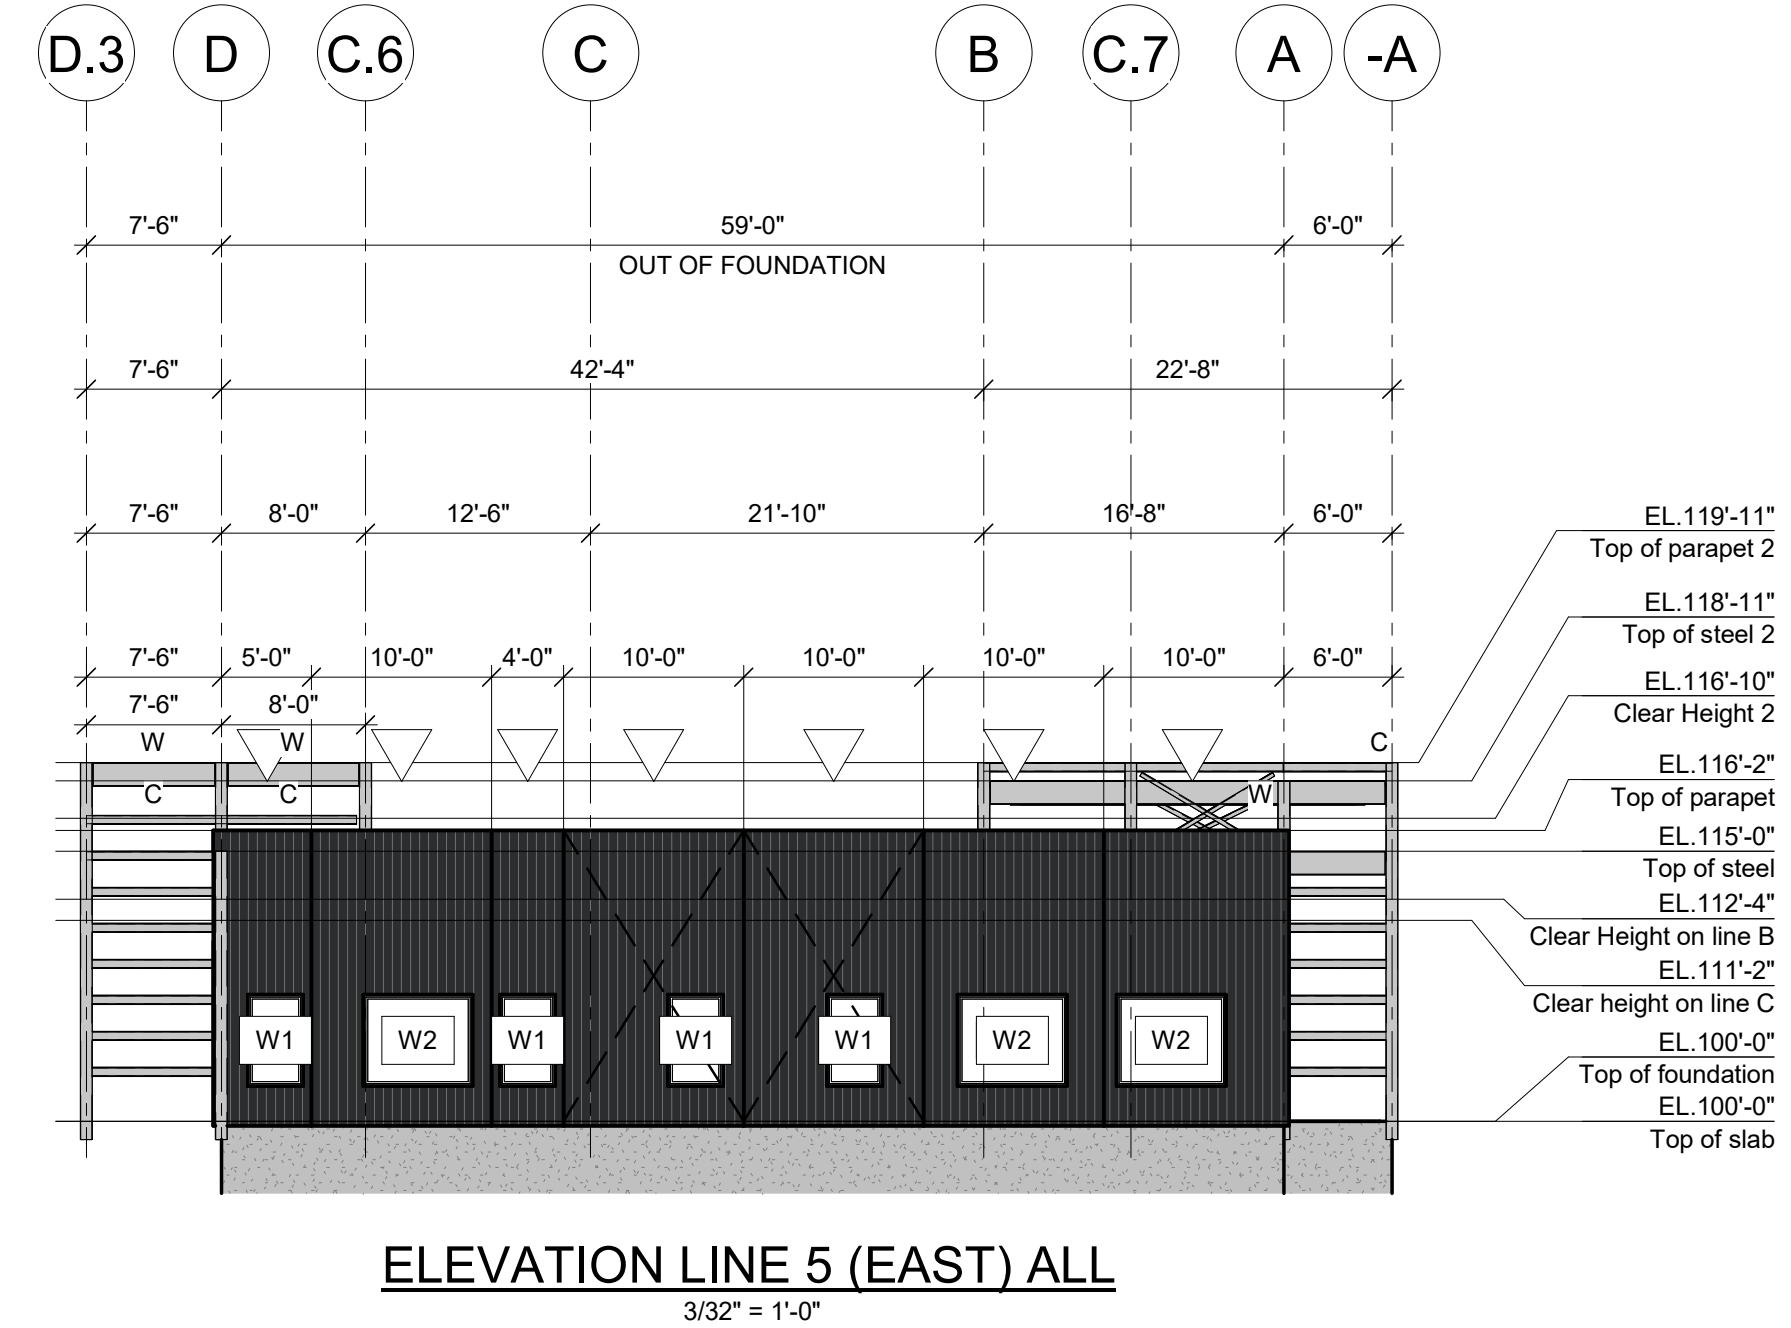
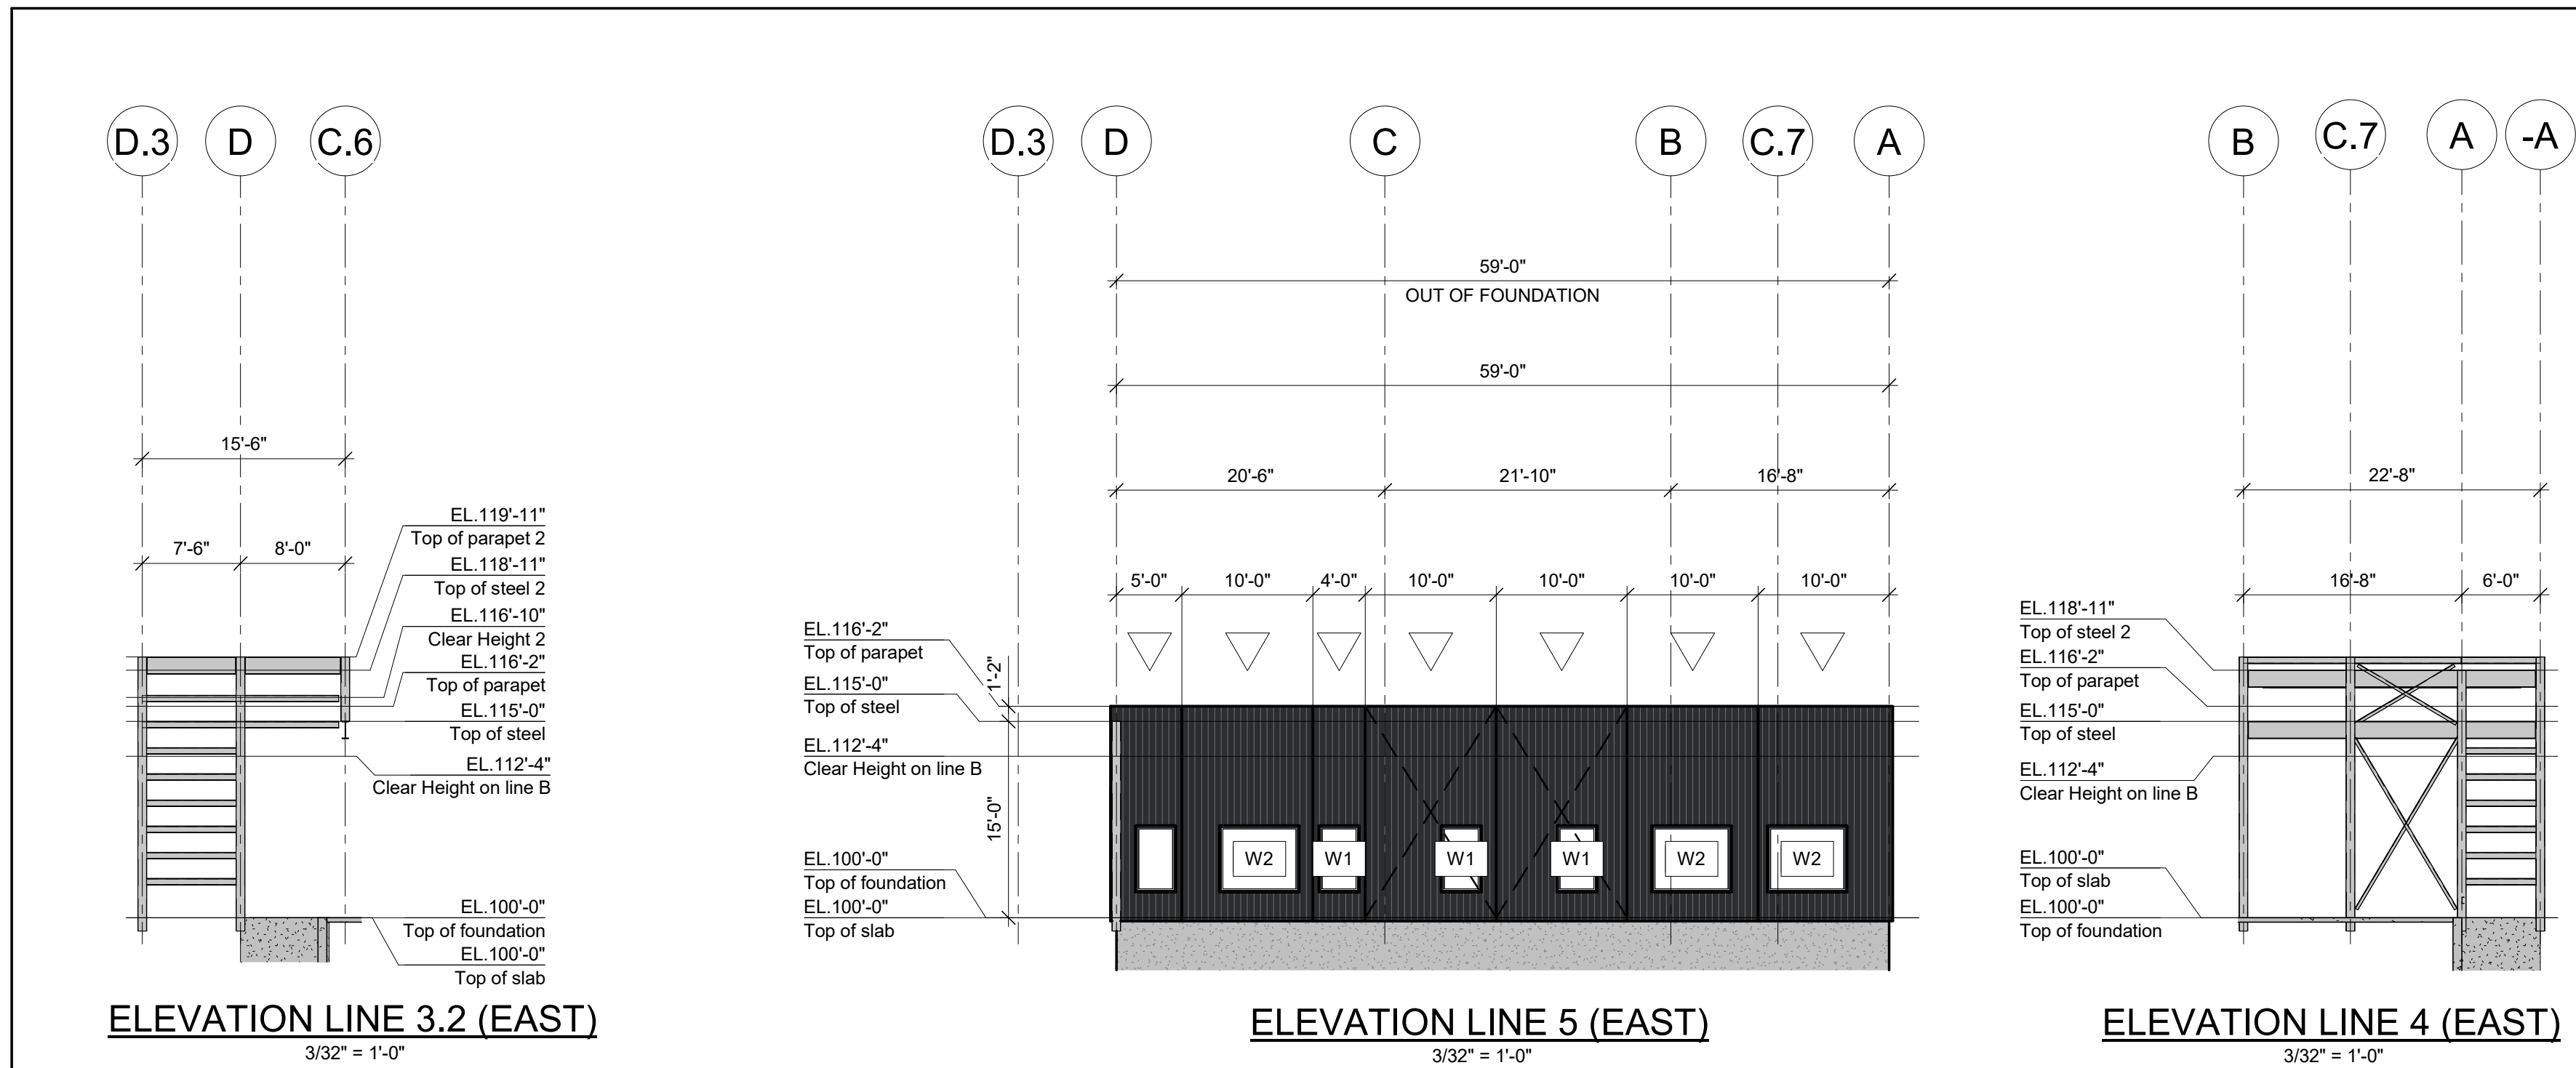
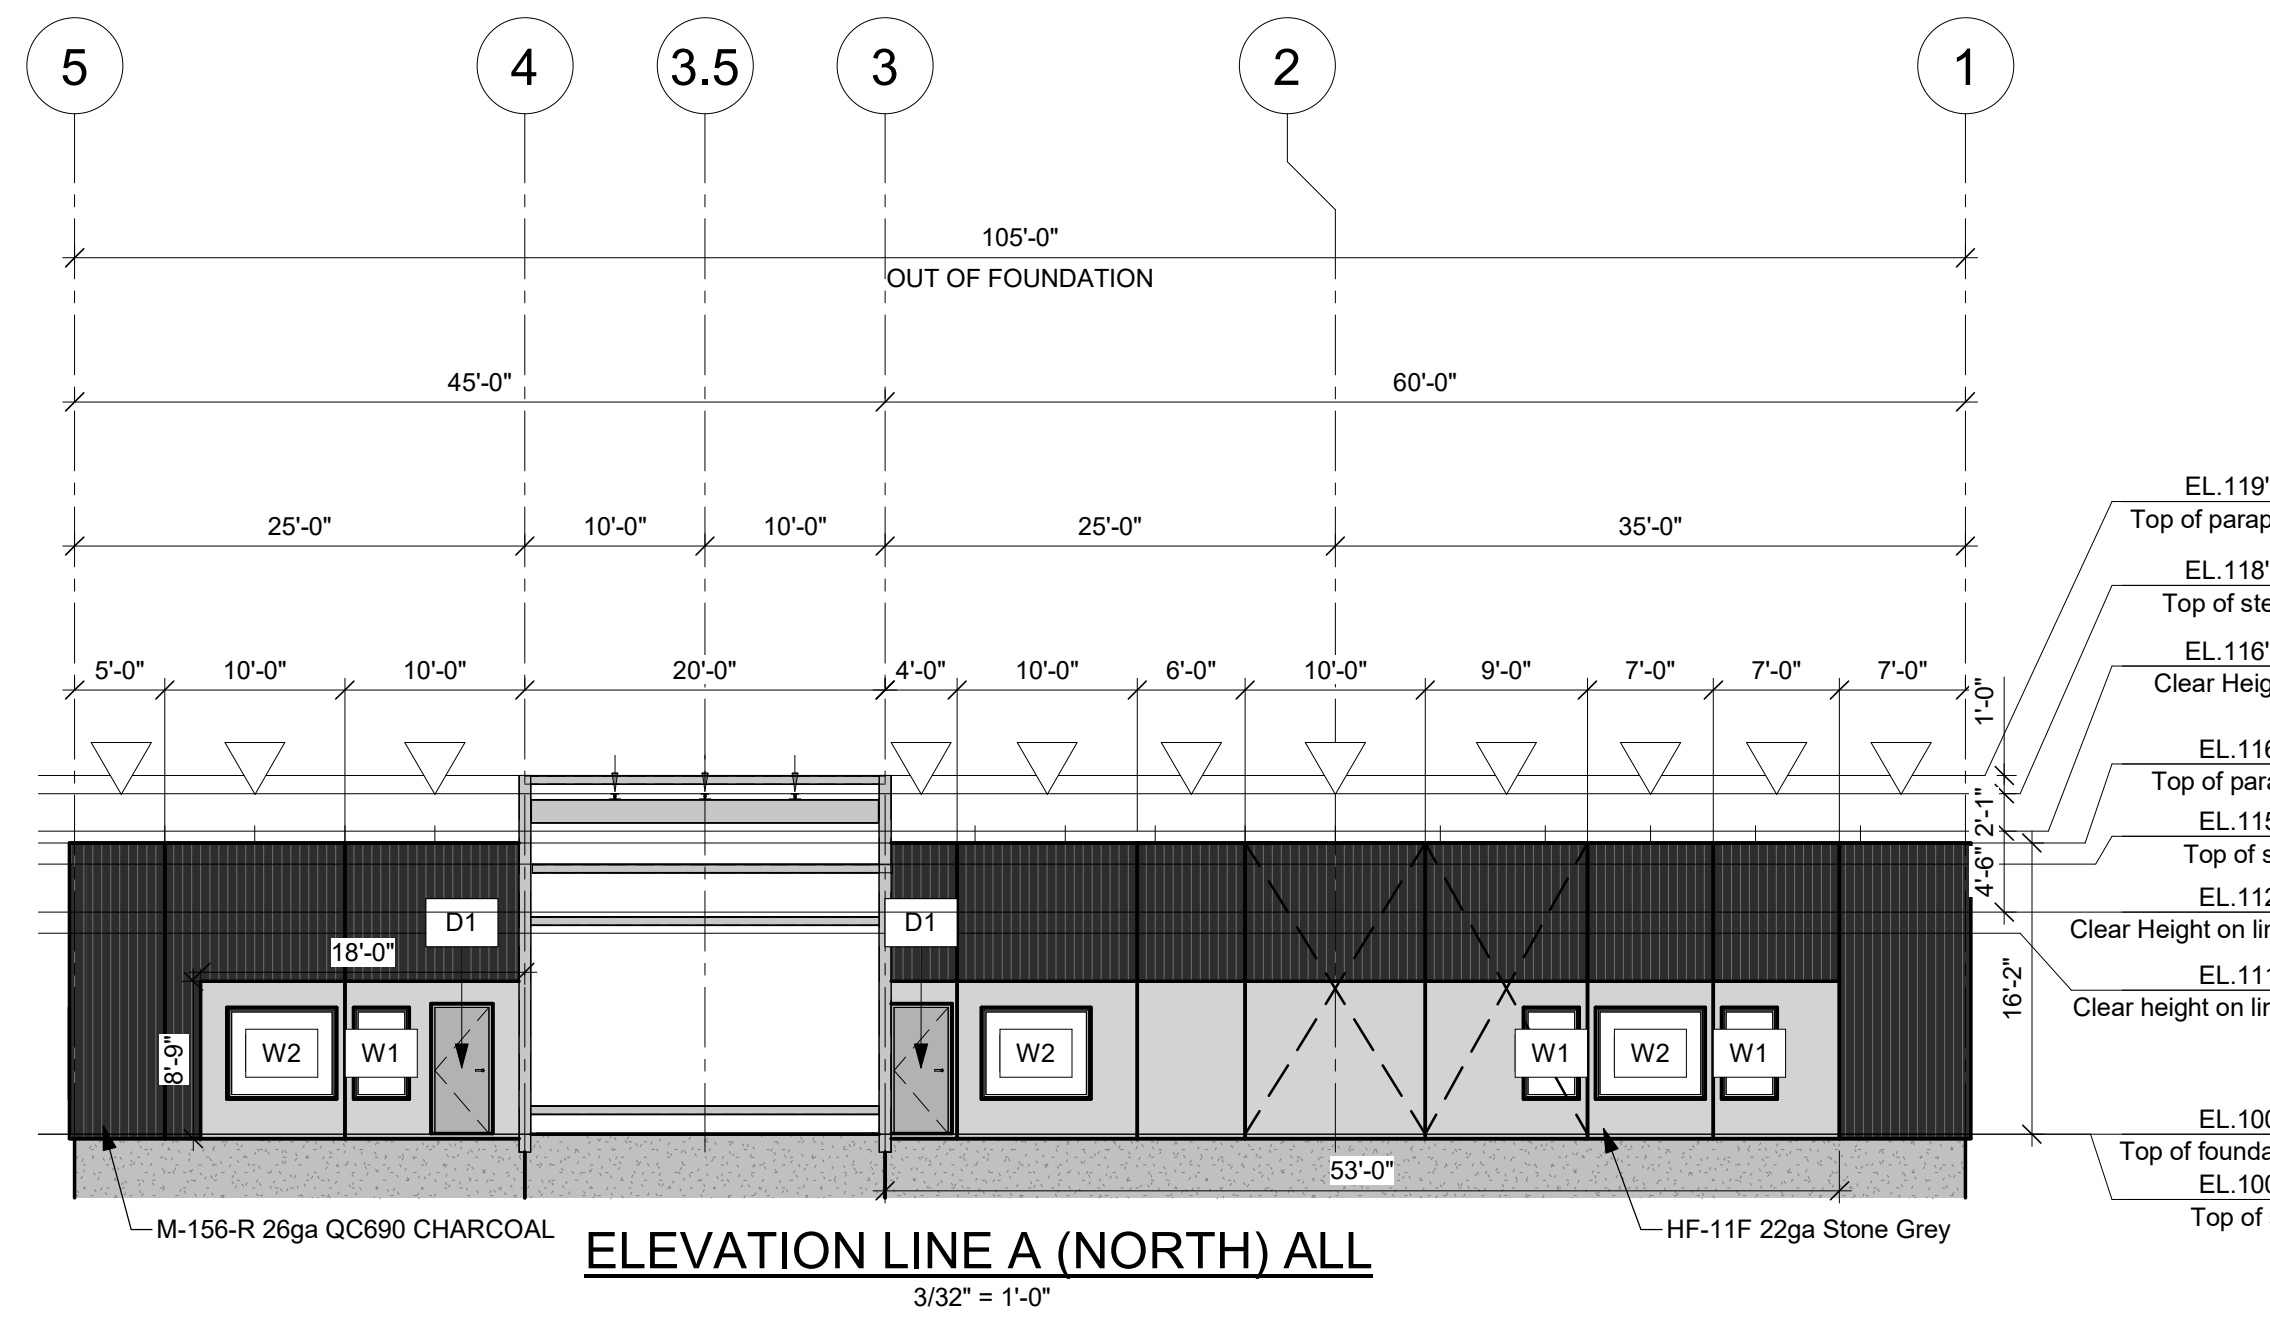


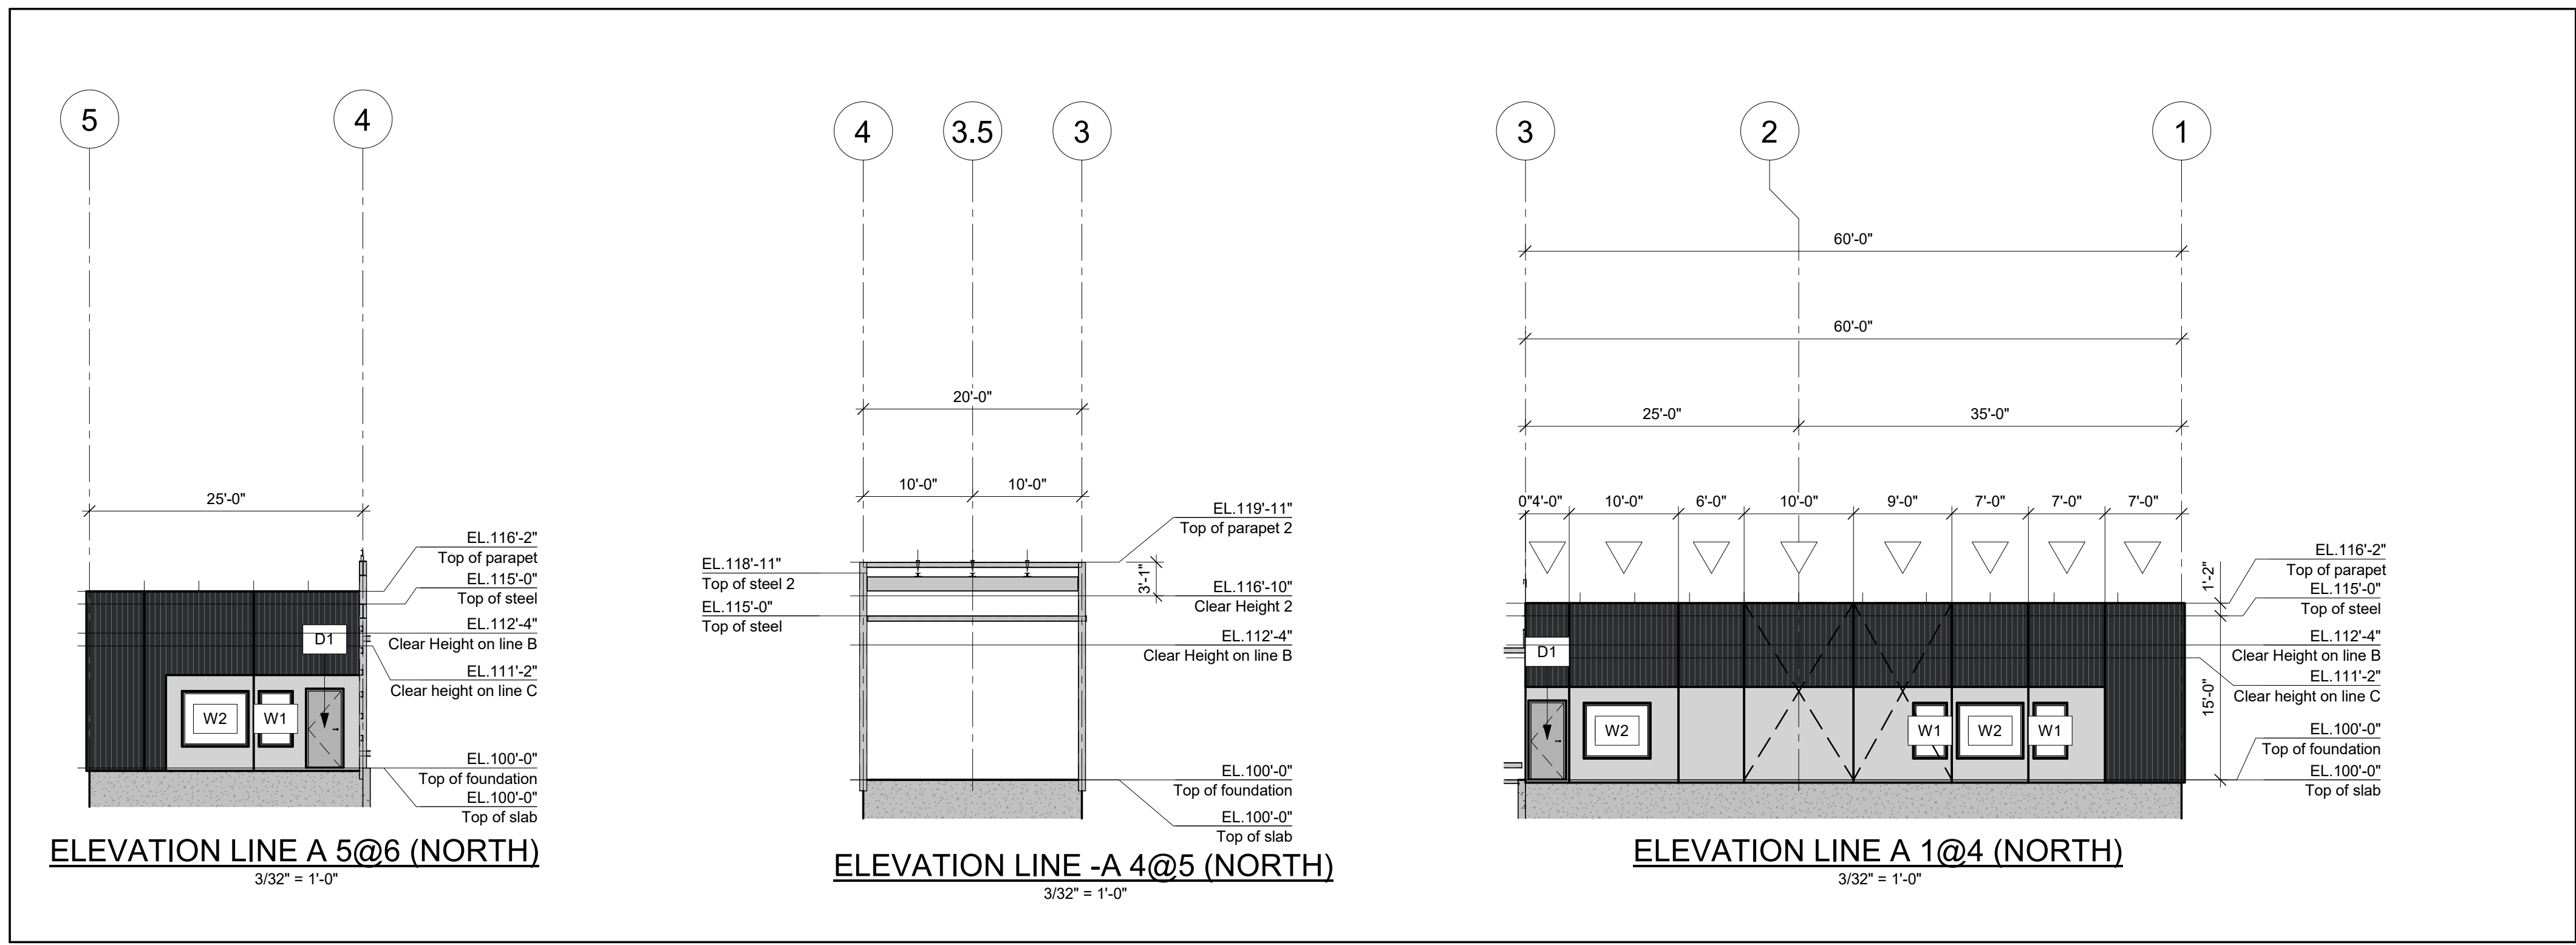

CONTRACTOR/RECTOR NOTE:
IT IS PROHIBITED TO MODIFY, COPY, REPRODUCE OR OTHERWISE
DISTRIBUTE THIS DRAWING OR ANY REPRESENTATION OF THIS
DRAWING, OR ANY MEDIA, INCLUDING ELECTRONIC, WITHOUT THE
PRIOR WRITTEN APPROVAL OF CANAM GROUP INC.

PRELIMINARY

NOT TO BE USED FOR CONSTRUCTION

REVISION	DATE	DESCRIPTION	USER	VER
PROJECT MANAGER	-	-	-	-
-	-	-	-	-
-	-	-	-	-
-	-	-	-	-

DRAWING			
DRAWN	DESIGNED	PROJECT ENGINEER	SCALE
INITIALE		PROJECT ENG.	3/32" = 1'-0"
CHECKED	CONSULTING ENGINEERS ARCHITECTS	ENGINEER	DATE (YYYYMMDD)
		ARCHITECT	YYYYMMDD

CUSTOMER:

CANAM
11505, 1re Avenue, bureau 500, Saint-Georges Beauséjour
Québec, Canada, G2V 7G3
Phone : (418) 228-8031
Toll free : (877) 499-6049
www.canam.com

PROFESSIONAL SEAL

PROJECT

Scarborough, ME

DRAWING TITLE
PRELIMINARY SKETCH - ELEVATIONS

CONTRACT NUMBER	DRAWING NUMBER	DIVISION	REVISION
PJ NO.	EsMx501		