
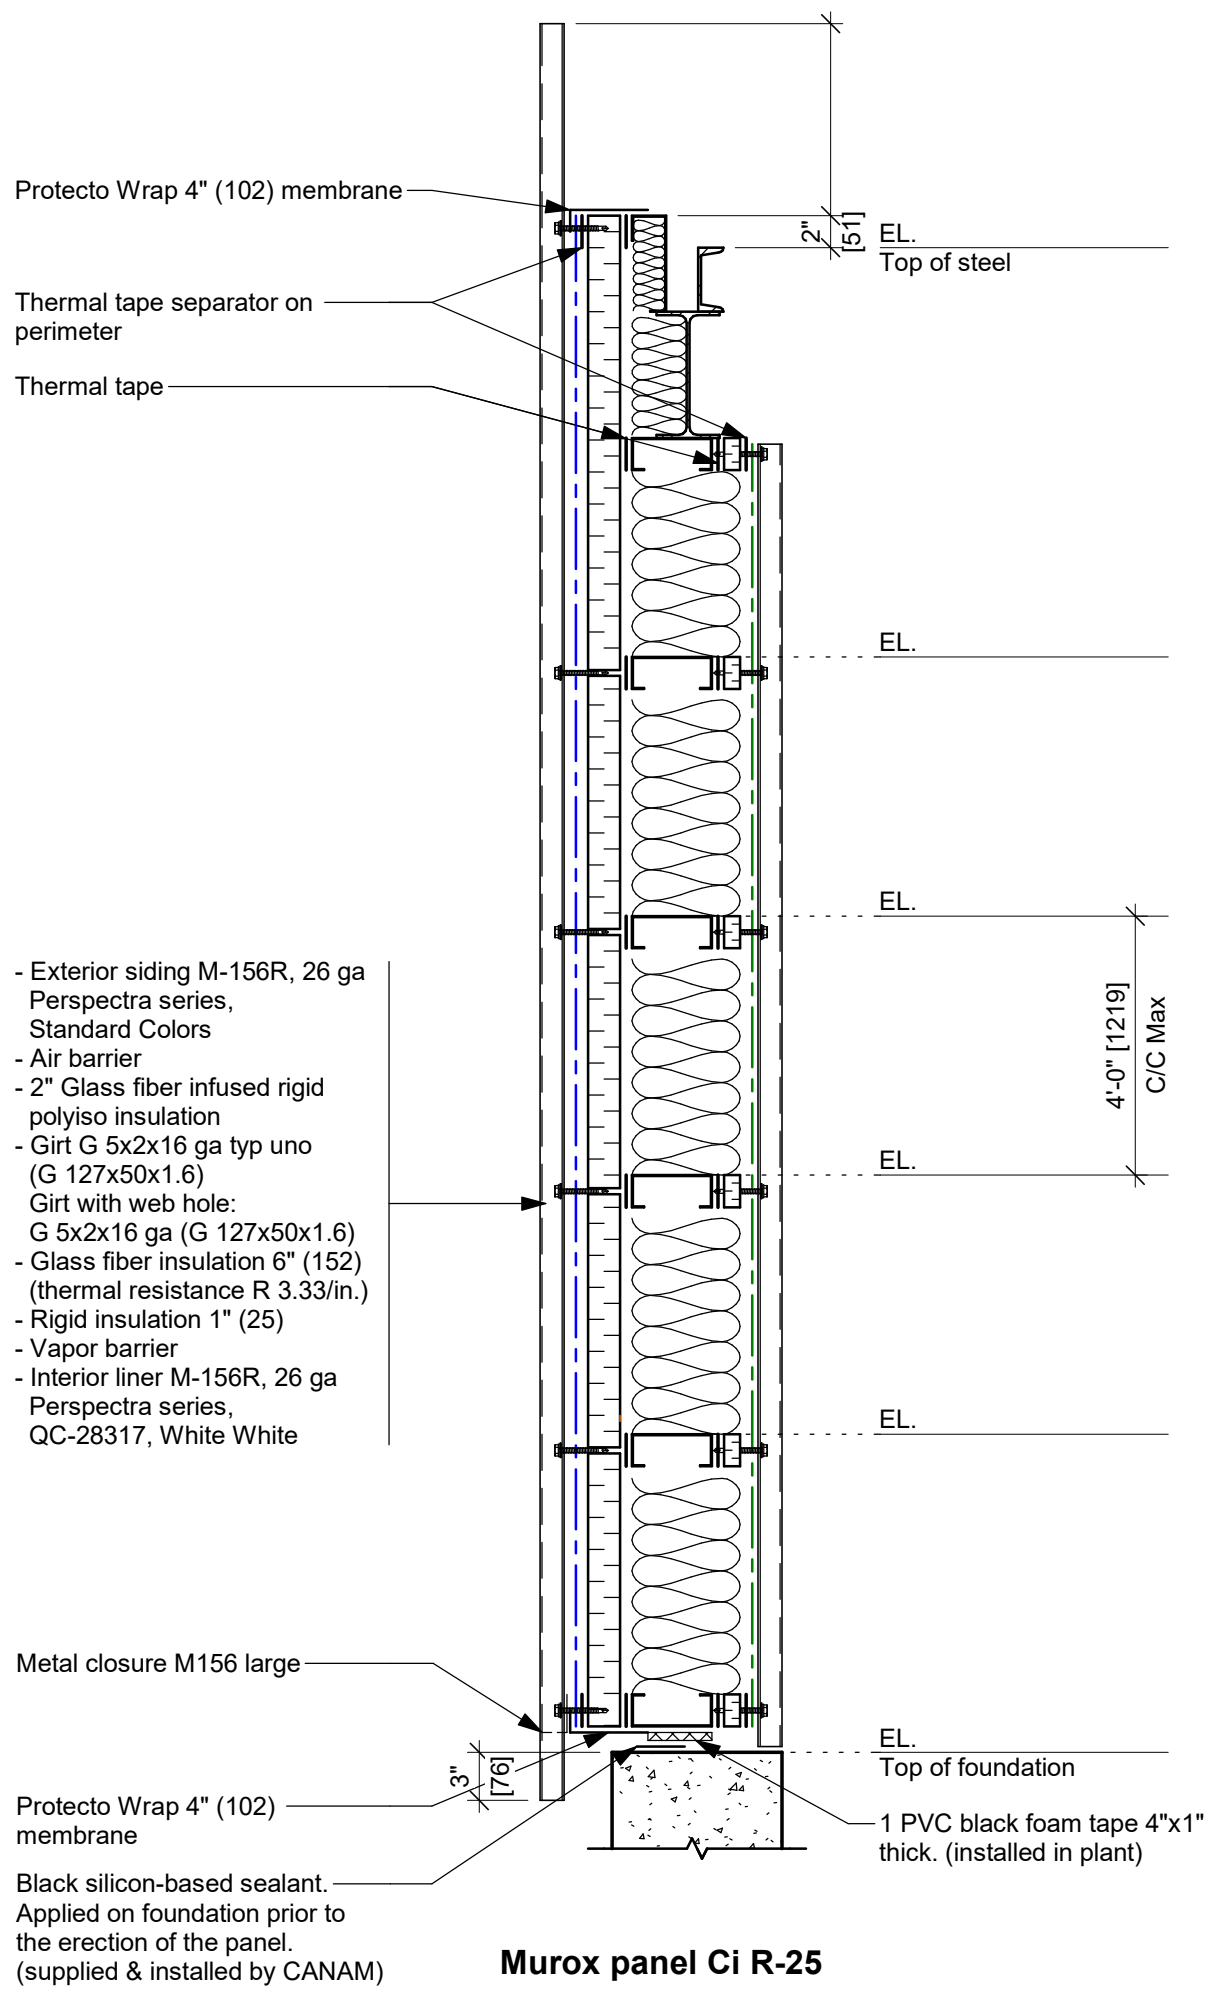
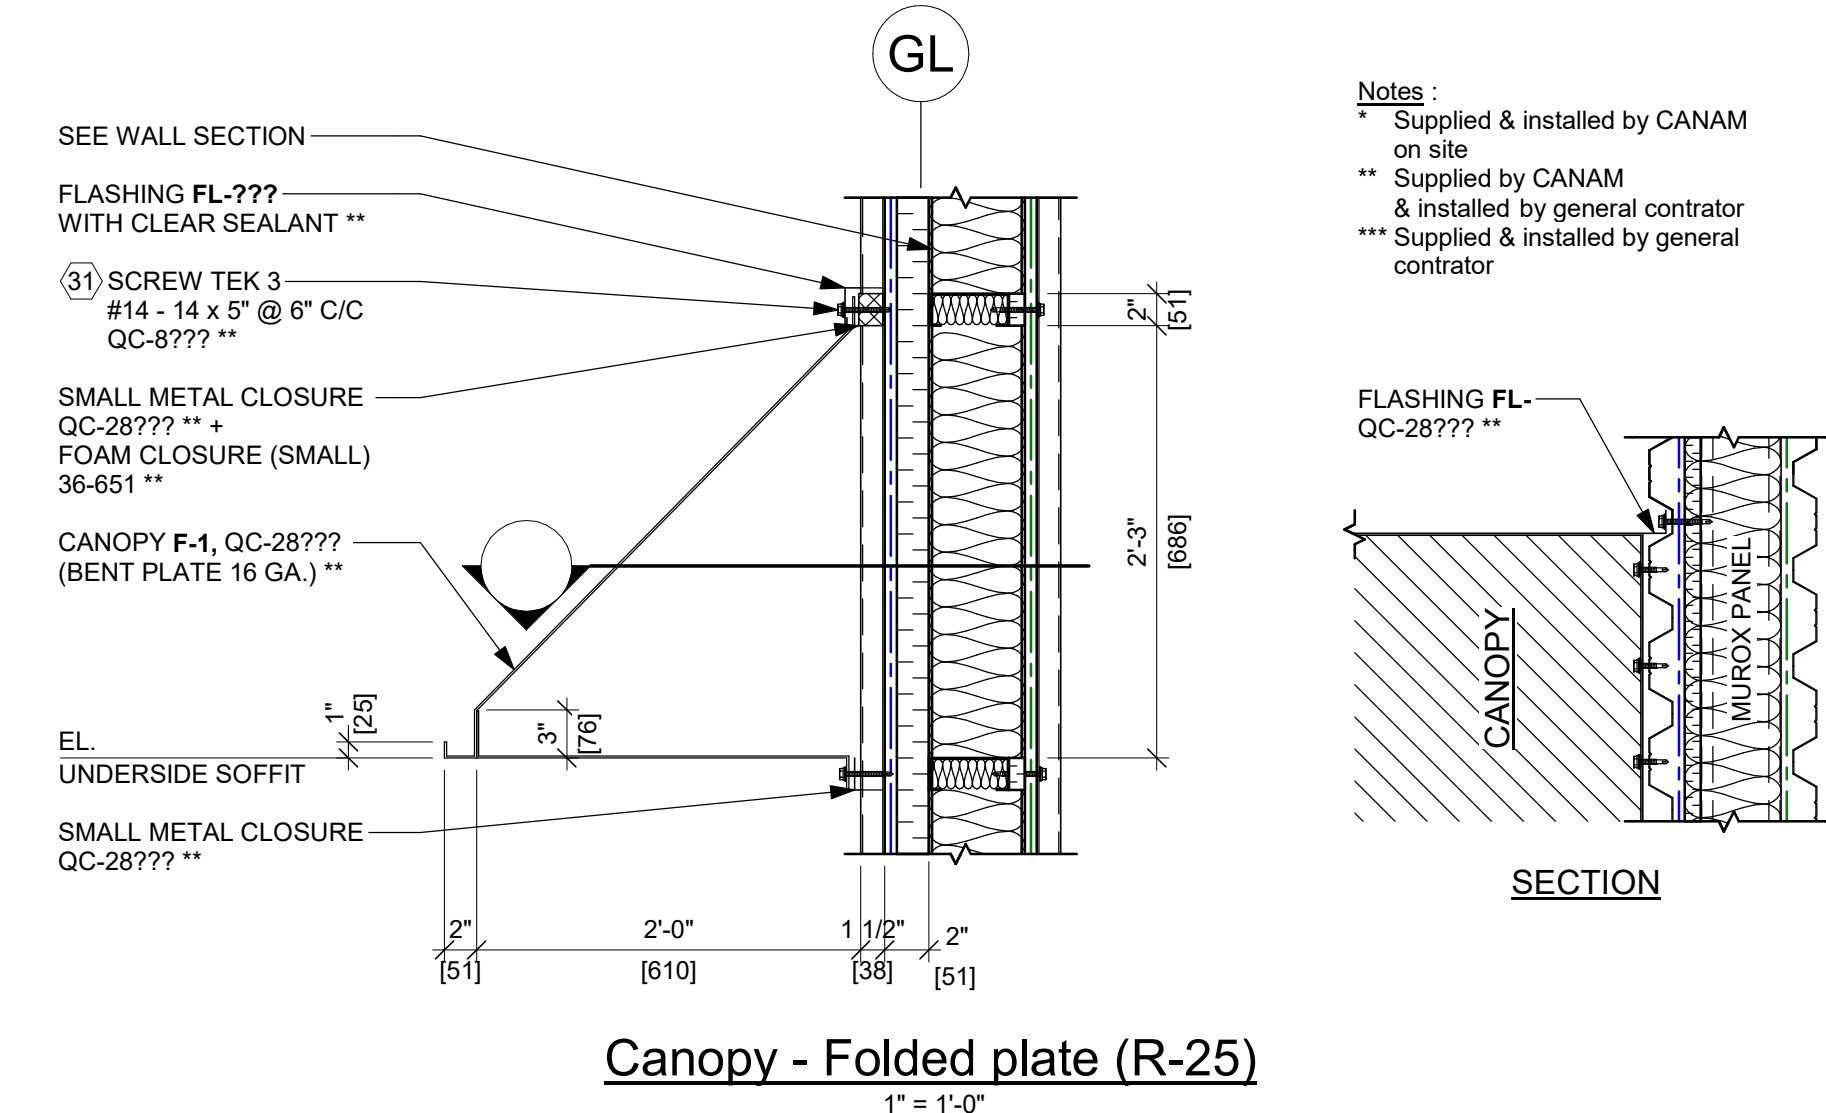


WINDOW SCHEDULE					
Identity	Qty.	Installation	Description	Size (Ext. of frame) (width & height)	Frame color
W1	8		Fixed aluminum window with thermal break and sealed glass + Low-E argon clear	3' x 5'	Aluminum Frame (no color)
W2	12		Fixed aluminum window with thermal break and sealed glass + Low-E argon clear	6' x 5'	Aluminum Frame (no color)
W3	2		Casement single aluminum window with thermal break and sealed glass + Low-E argon clear	3' x 5'	Aluminum Frame (no color)
W4	1		Casement right aluminum window with thermal break and sealed glass + Low-E argon clear (2 wide x 1 high)	6' x 5' (casement on right / battant à droite)	Aluminum Frame (no color)



OPENING SCHEDULE			
Total	Type	Tag	Remarks

DOOR SCHEDULE															
Door 19 ga.				Glass		Hardware									
Identity	Qty.	Installation	Insulation (R12)	Dimensions	Swing side	Width	Height	Steel frame 16 ga with thermal break	(3) Hinges non-rising removable pin	Door lock & latch set	Panic bar without outside trim 22EO	Panic bar with outside trim 23OL	Surface bolt Inactive door	Threshold	Remarks
D1	3	Installation		36" x 84"											


OH & OPENING SCHEDULE			
Total	Type	Tag	Remarks
1	6' x 8'	OH	
Total général: 1			

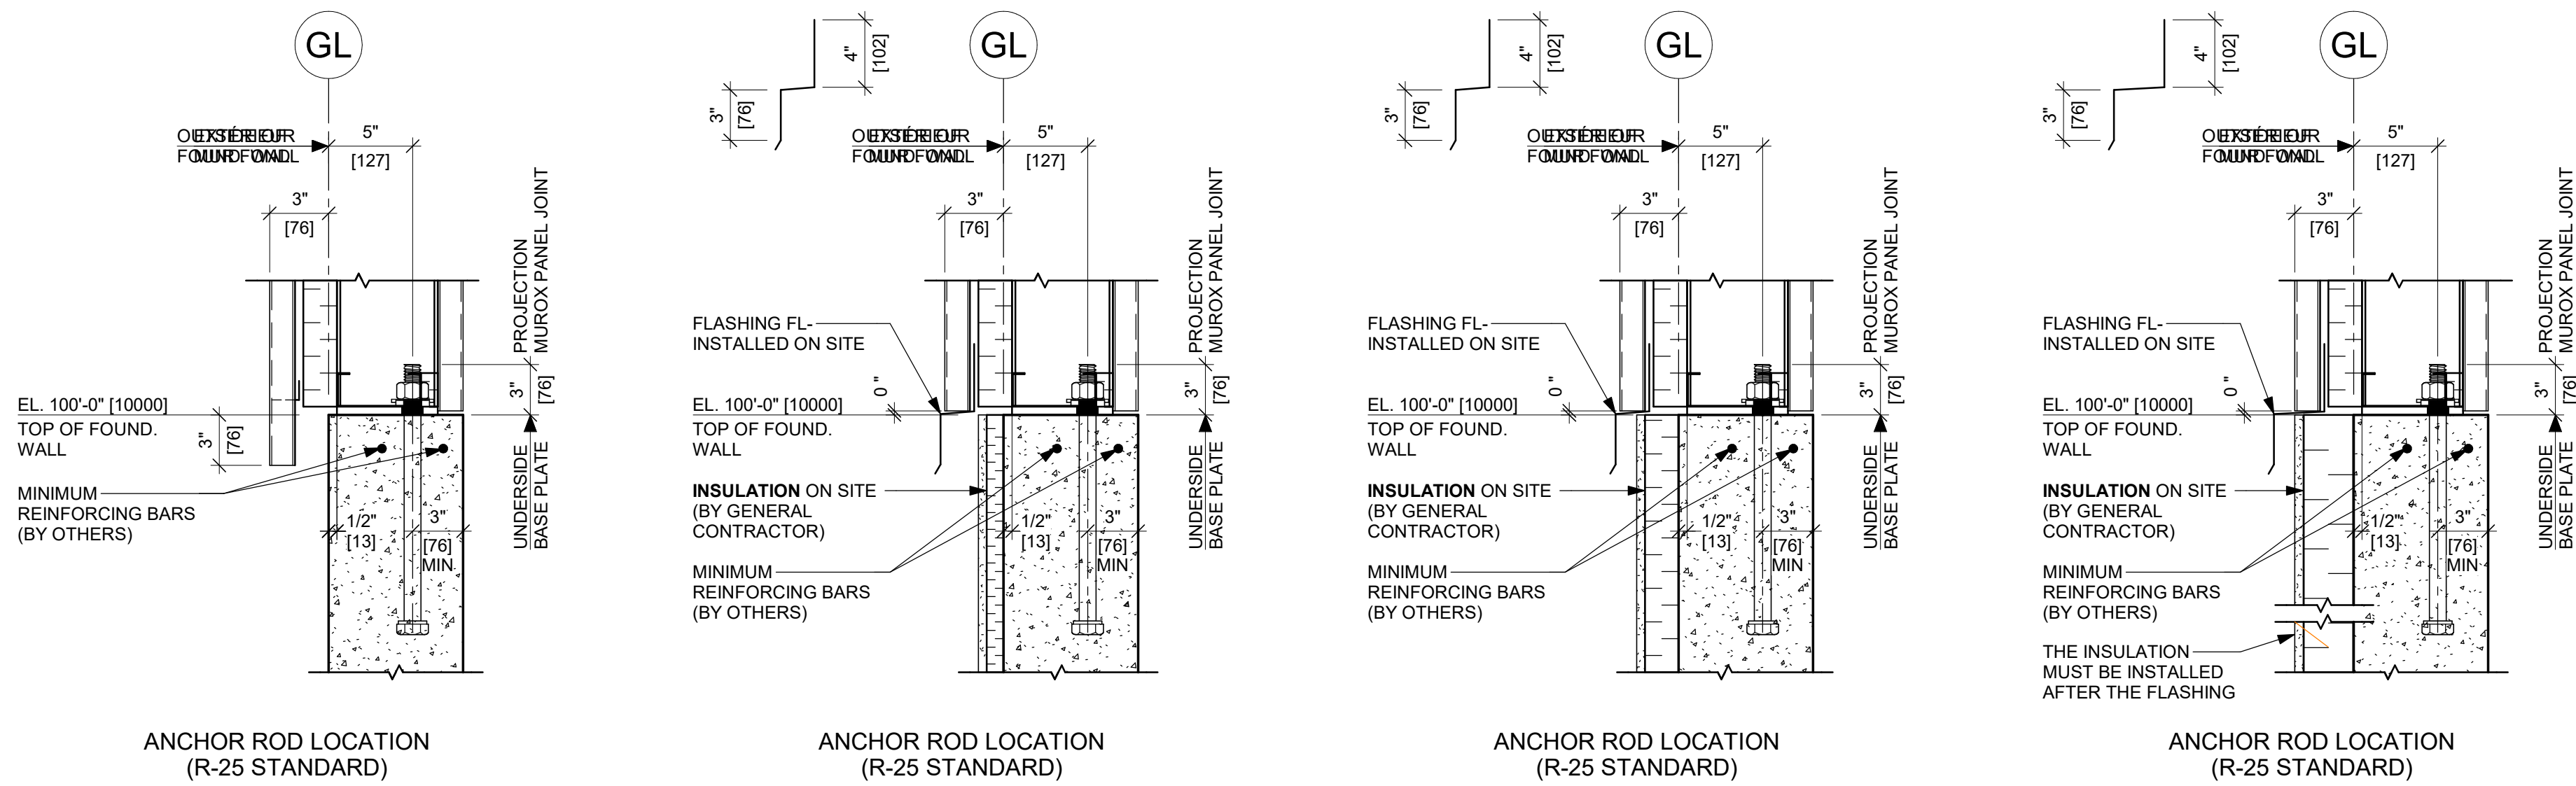


Panel at the mezz R-25 & R-27 (C6) (siding, liner, joist para.)

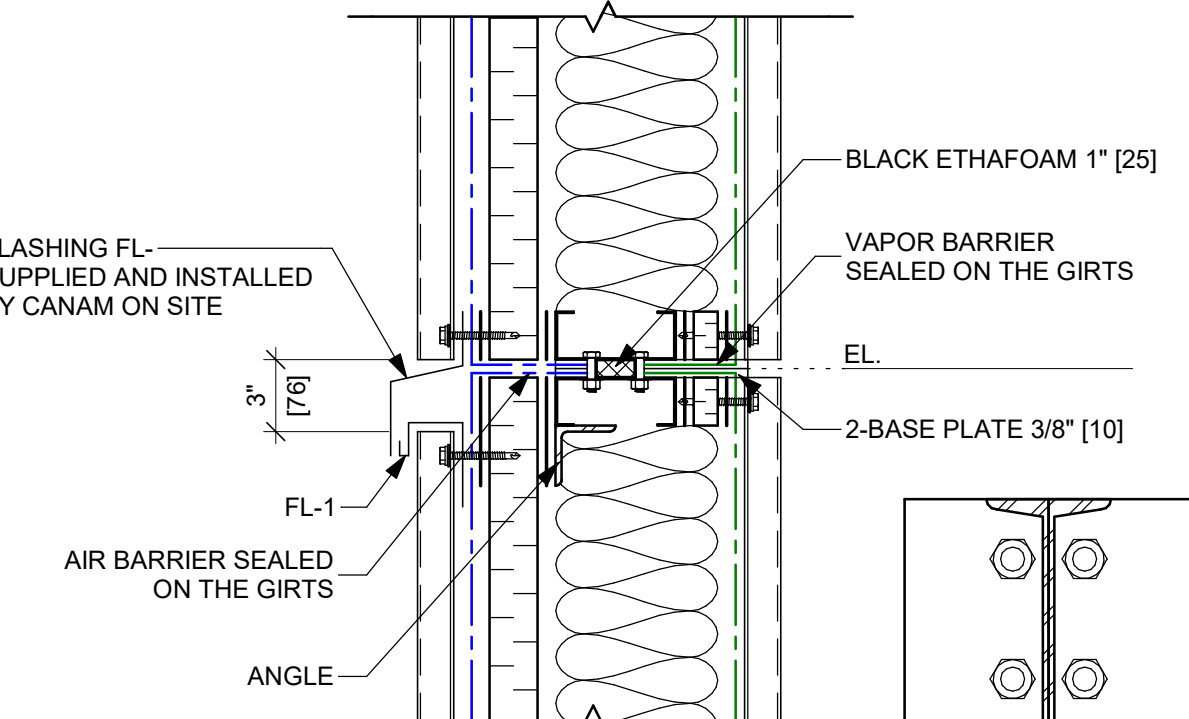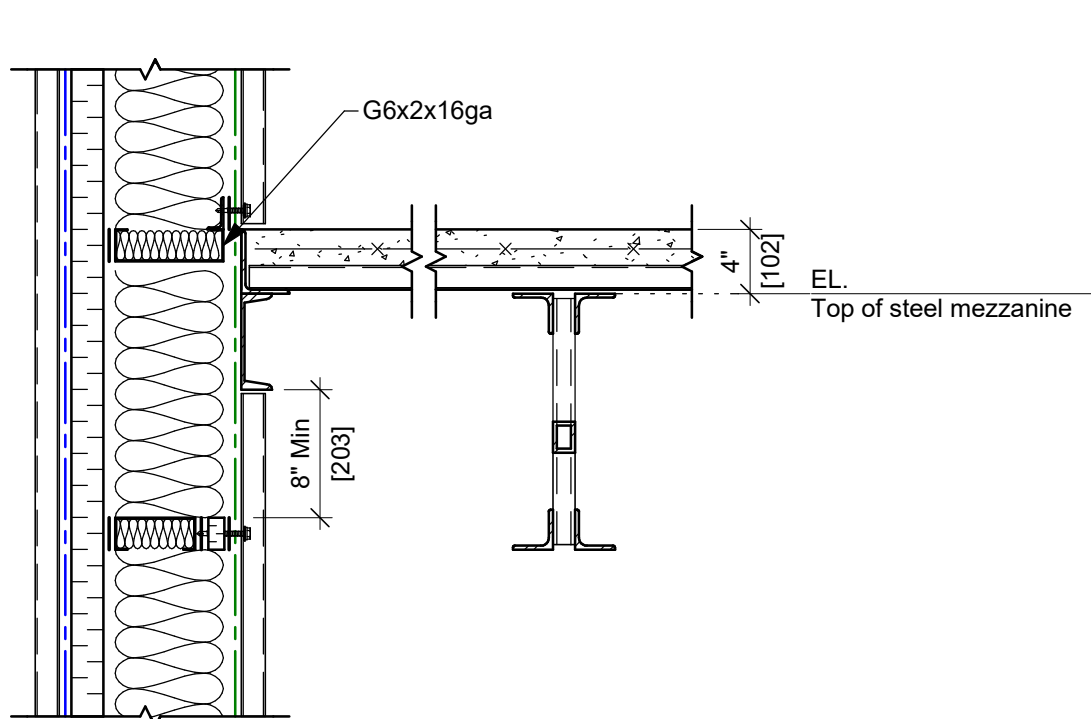


Murox stacked panels CI R-25 & CI R-27

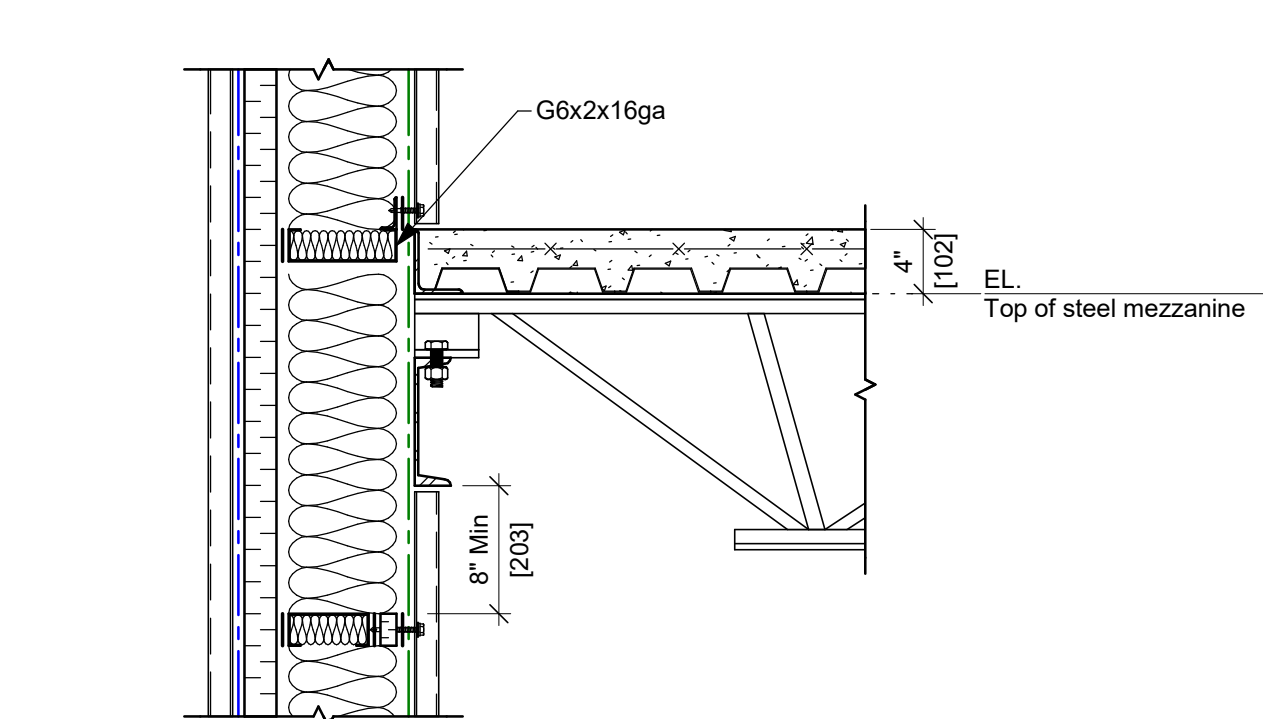

Panel at the mezz R-25 & R-27 (C6) (siding, liner, joist perp.)

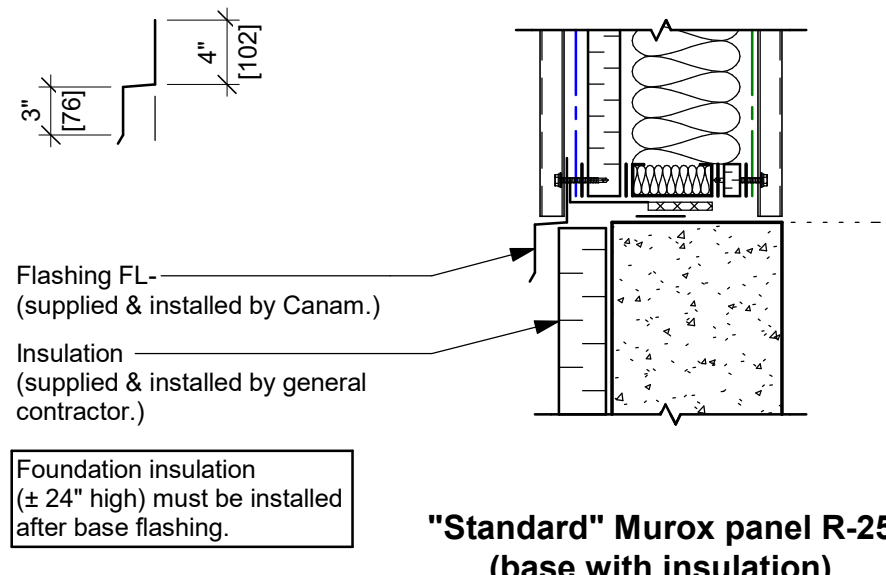

"Standard" Murox panel R-25 (base with insulation)

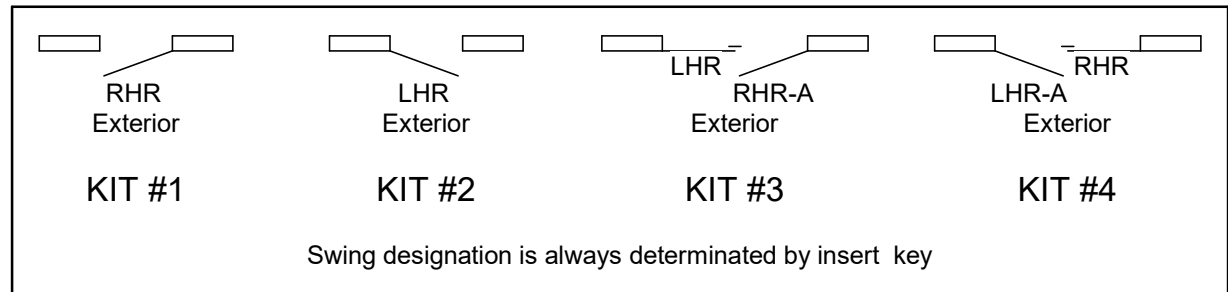

Supplier's standard hardware:
 - Hinges: Stanley FB3175 4.5" x 4"
 - Exit device: Von Duprin 22 x 689 with outside trim 23OL
 - Permanent cylinder: Schlage 2001C 626
 - Door closure: LCN 1261 680
 - Head and jamb seal: Unique 1650
 - Bottom seal: Unique DS4
 - Threshold: See the remarks in "Door schedule"

CONTRACTOR/RECTOR NOTE:

IT IS PROHIBITED TO MODIFY, COPY, REPRODUCE OR OTHERWISE DISTRIBUTE THIS DRAWING OR ANY REPRESENTATION OF THIS DRAWING OR ANY MEDIA, INCLUDING ELECTRONIC, WITHOUT THE PRIOR WRITTEN APPROVAL OF CANAM GROUP INC.

PRELIMINARY

NOT TO BE USED FOR CONSTRUCTION

REVISION	DATE	DESCRIPTION	USER	VER
PROJECT MANAGER				
-				
-				
-				
-				
DRAFTING				
-				
DRAWN	DESIGNED	PROJECT ENGINEER	SCALE:	
INITIALE		PROJECT ENG.	Comme indiqué	
CHECKED	CONSULTING ENGINEERS ARCHITECTS	ENGINEER	DATE (yyyy/mm/dd)	
		ARCHITECT	YYYY/MM/DD	
CUSTOMER:				
 11505, 1re Avenue, bureau 500, Saint-Georges Beauce Québec, Canada, G5Y 7G3 Phone : (418) 228-8031 Toll free : (877) 499-6049 www.canam.com				
PROFESSIONAL SEAL				
PROJECT				
Scarborough, ME				
DRAWING TITLE				
PRELIMINARY SKETCH - ELEVATION, WALL SECTION AND SCHEDULES				
CONTRACT NUMBER	DRAWING NUMBER	DIVISION	REVISION	
PJ NO.	EsMx502			

Initials



Initials

