

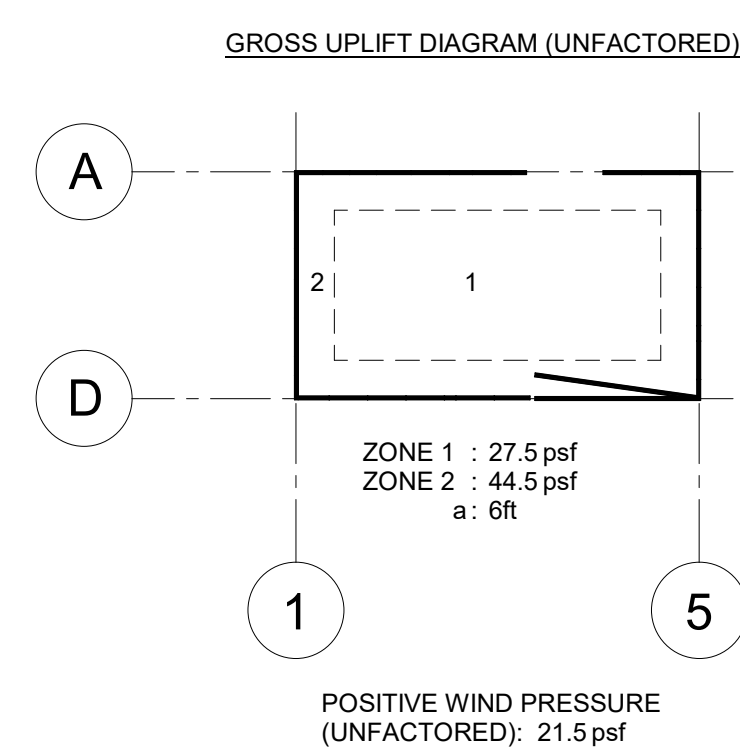


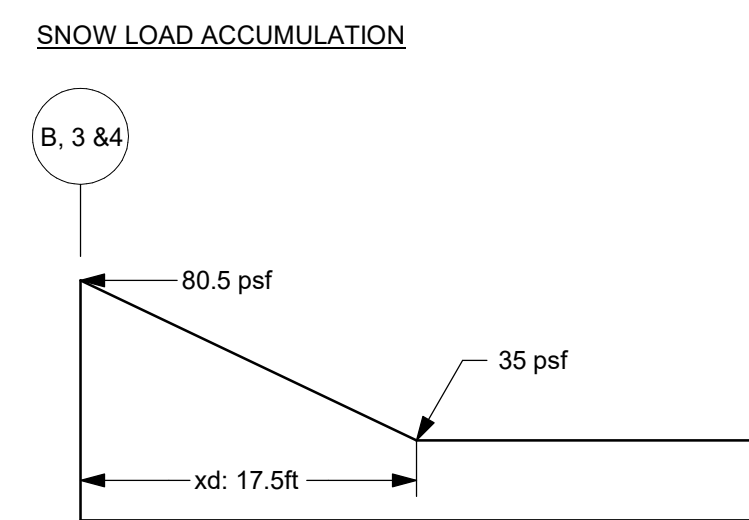


TOP OF PILASTER RWL	: 98'-0"
TOP OF PILASTER	: 99'-0"
TOP OF SLAB	: 100'-0"
TOP OF FOUNDATION	: 100'-0"
CLEAR HEIGHT LOW	: 110'-2"
CLEAR HEIGHT HIGH	: 116'-10"
TOP OF STEEL	: 114'-0"
TOP OF STEEL 2	: 118'-11"
PARAPET HEIGHT	: 1'-2"
TOP OF PARAPET	: 115'-2"
PARAPET HEIGHT 2	: 1'-0"
TOP OF PARAPET 2	: 119'-11"

- Roof dead load excluding collateral load : 18 psf
- Collateral load : 20 psf (includes lighting and/or mechanical and sprinklers 4 inches in diameter and less)
- Roof snow load : 35 psf
- Ground snow load : 50 psf
- Wind load $q = 150 - 112$ mph
- Roof live load : 0 psf
- Ground snow load : $S_s = 0.283$ psf
- $S_i = 0.072$ psf
- Risk Category : II
- Snow load factors : $C_s = 1.0$
- $C_w = 0.8$

- Assumed soil site class: D
- NOTE :
 1. If, however, the seismic site class is determined to be E or F according to the geotechnical report, the preliminary structural concept (location and geometry of bracings, etc.) must be validated and coordinated by a Canam's engineer.

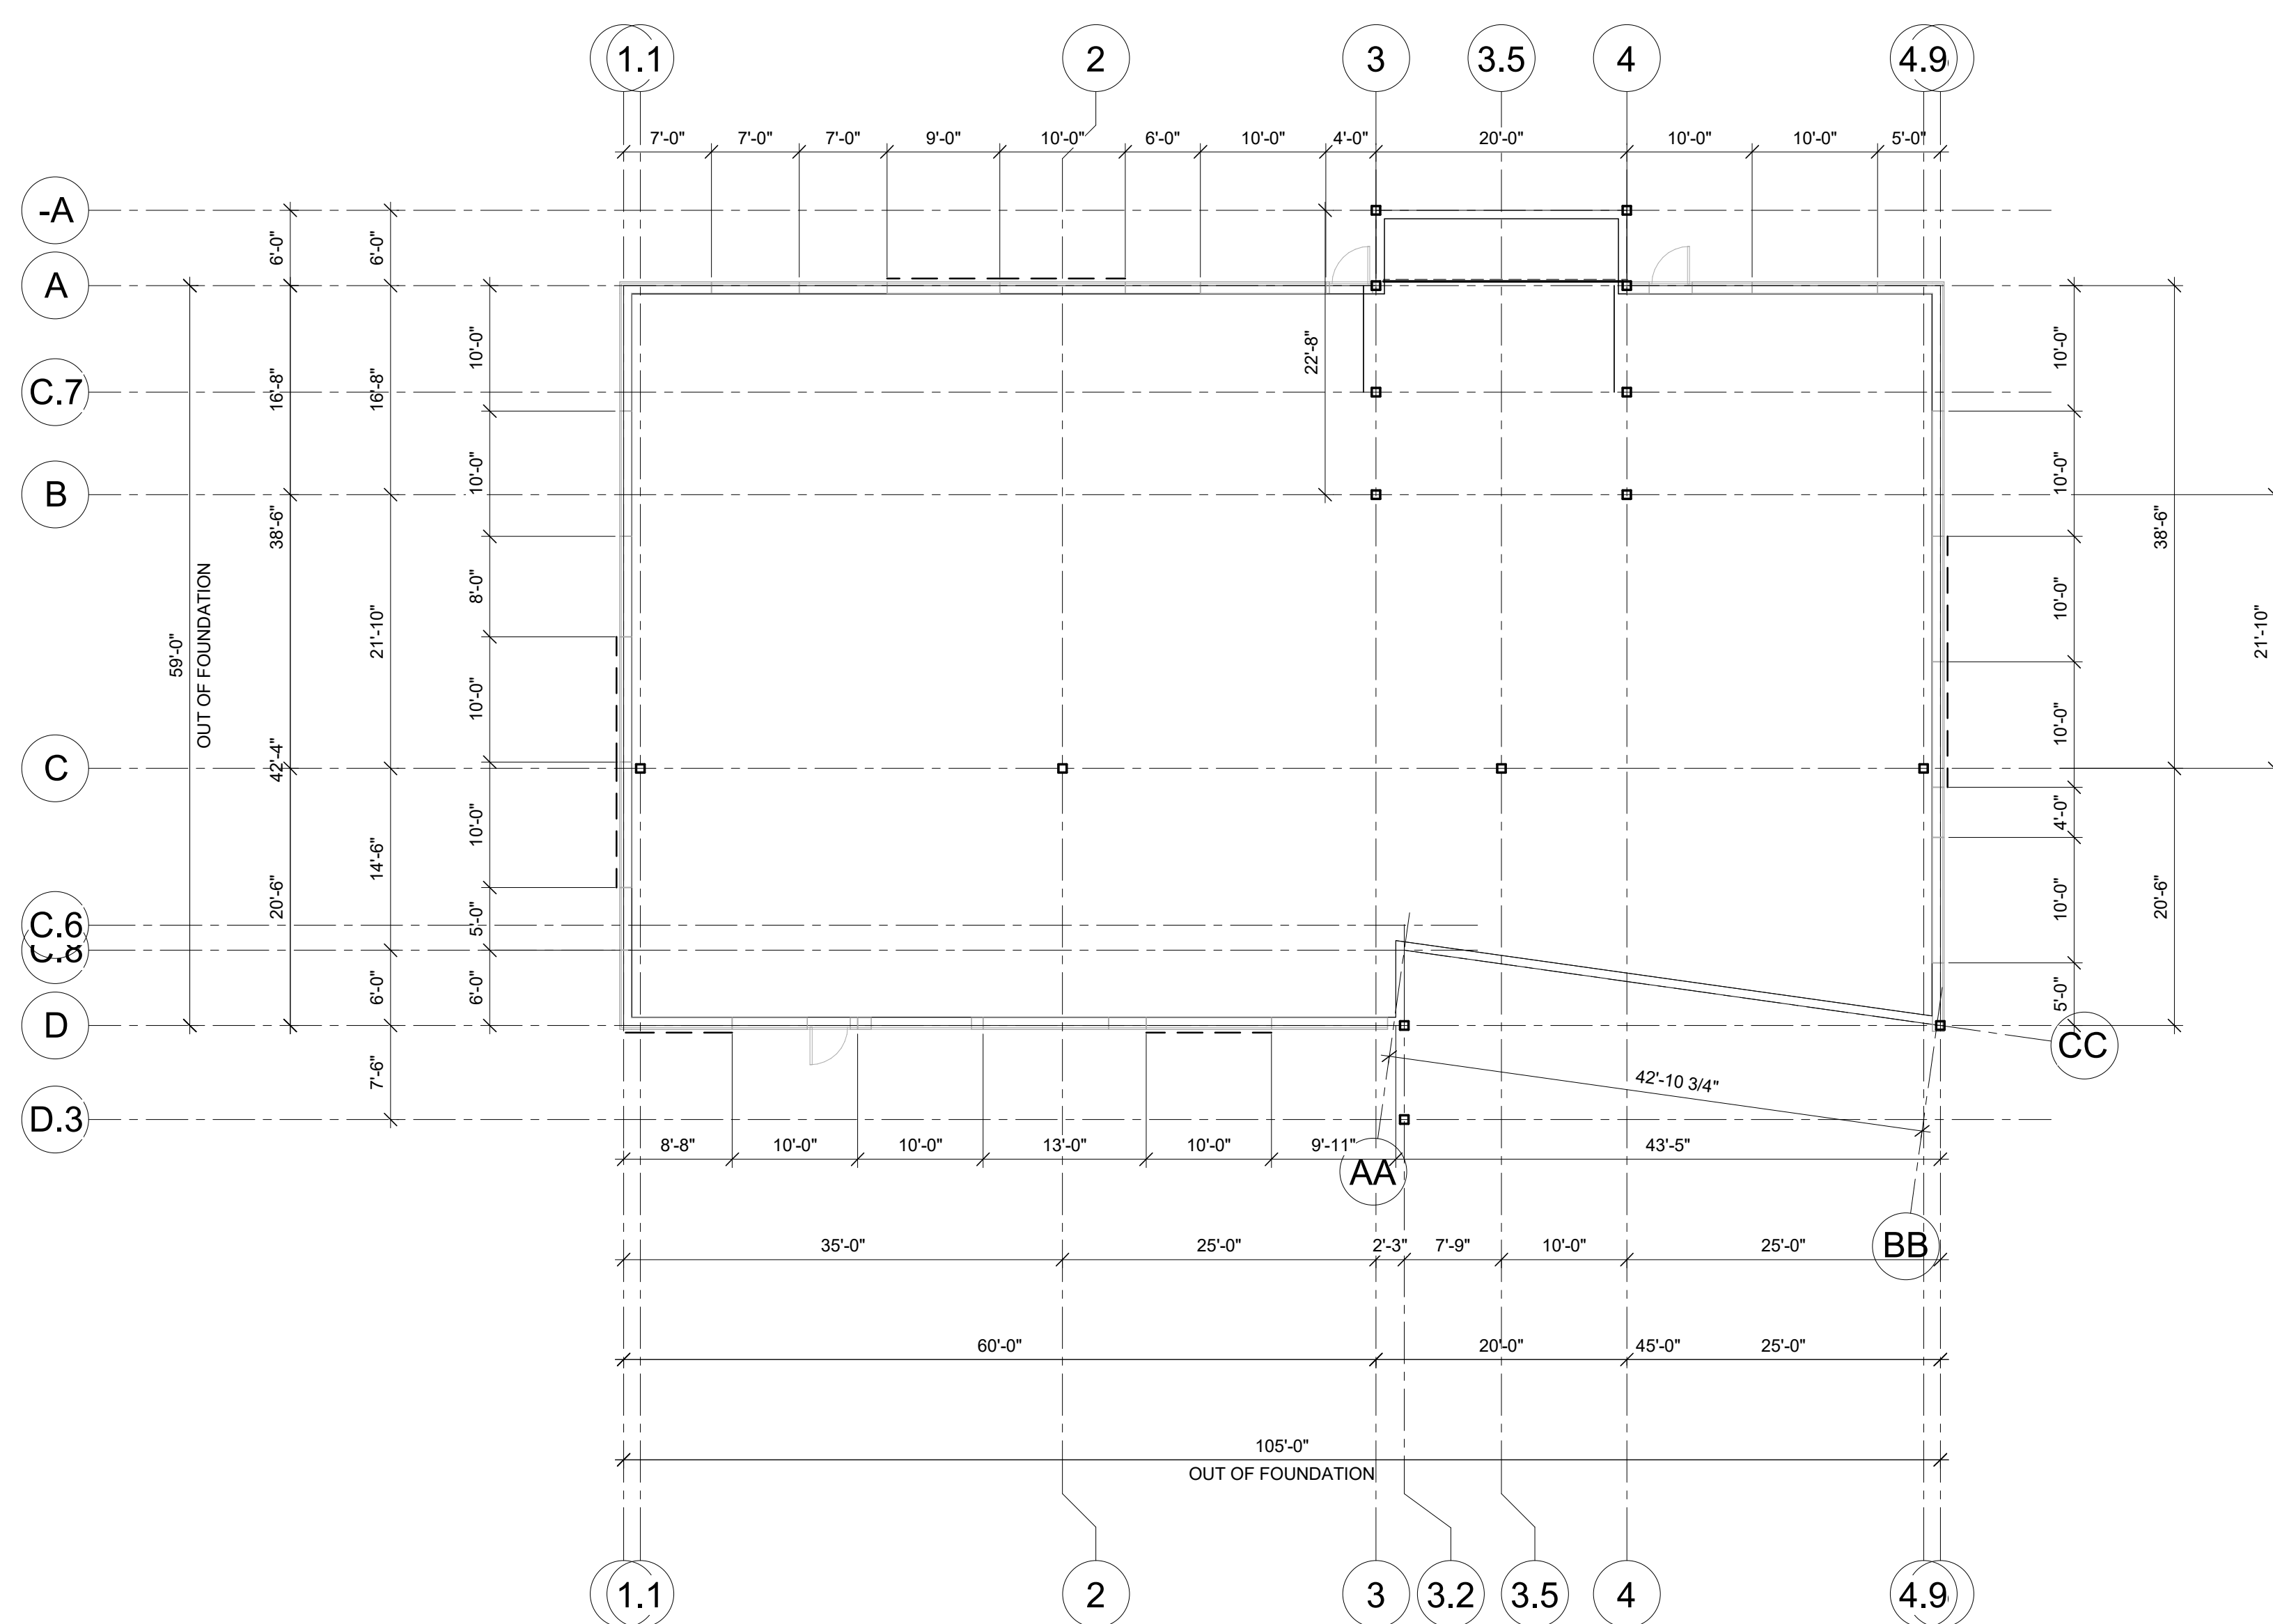

ANCHOR PLAN
3/32" = 1'-0"

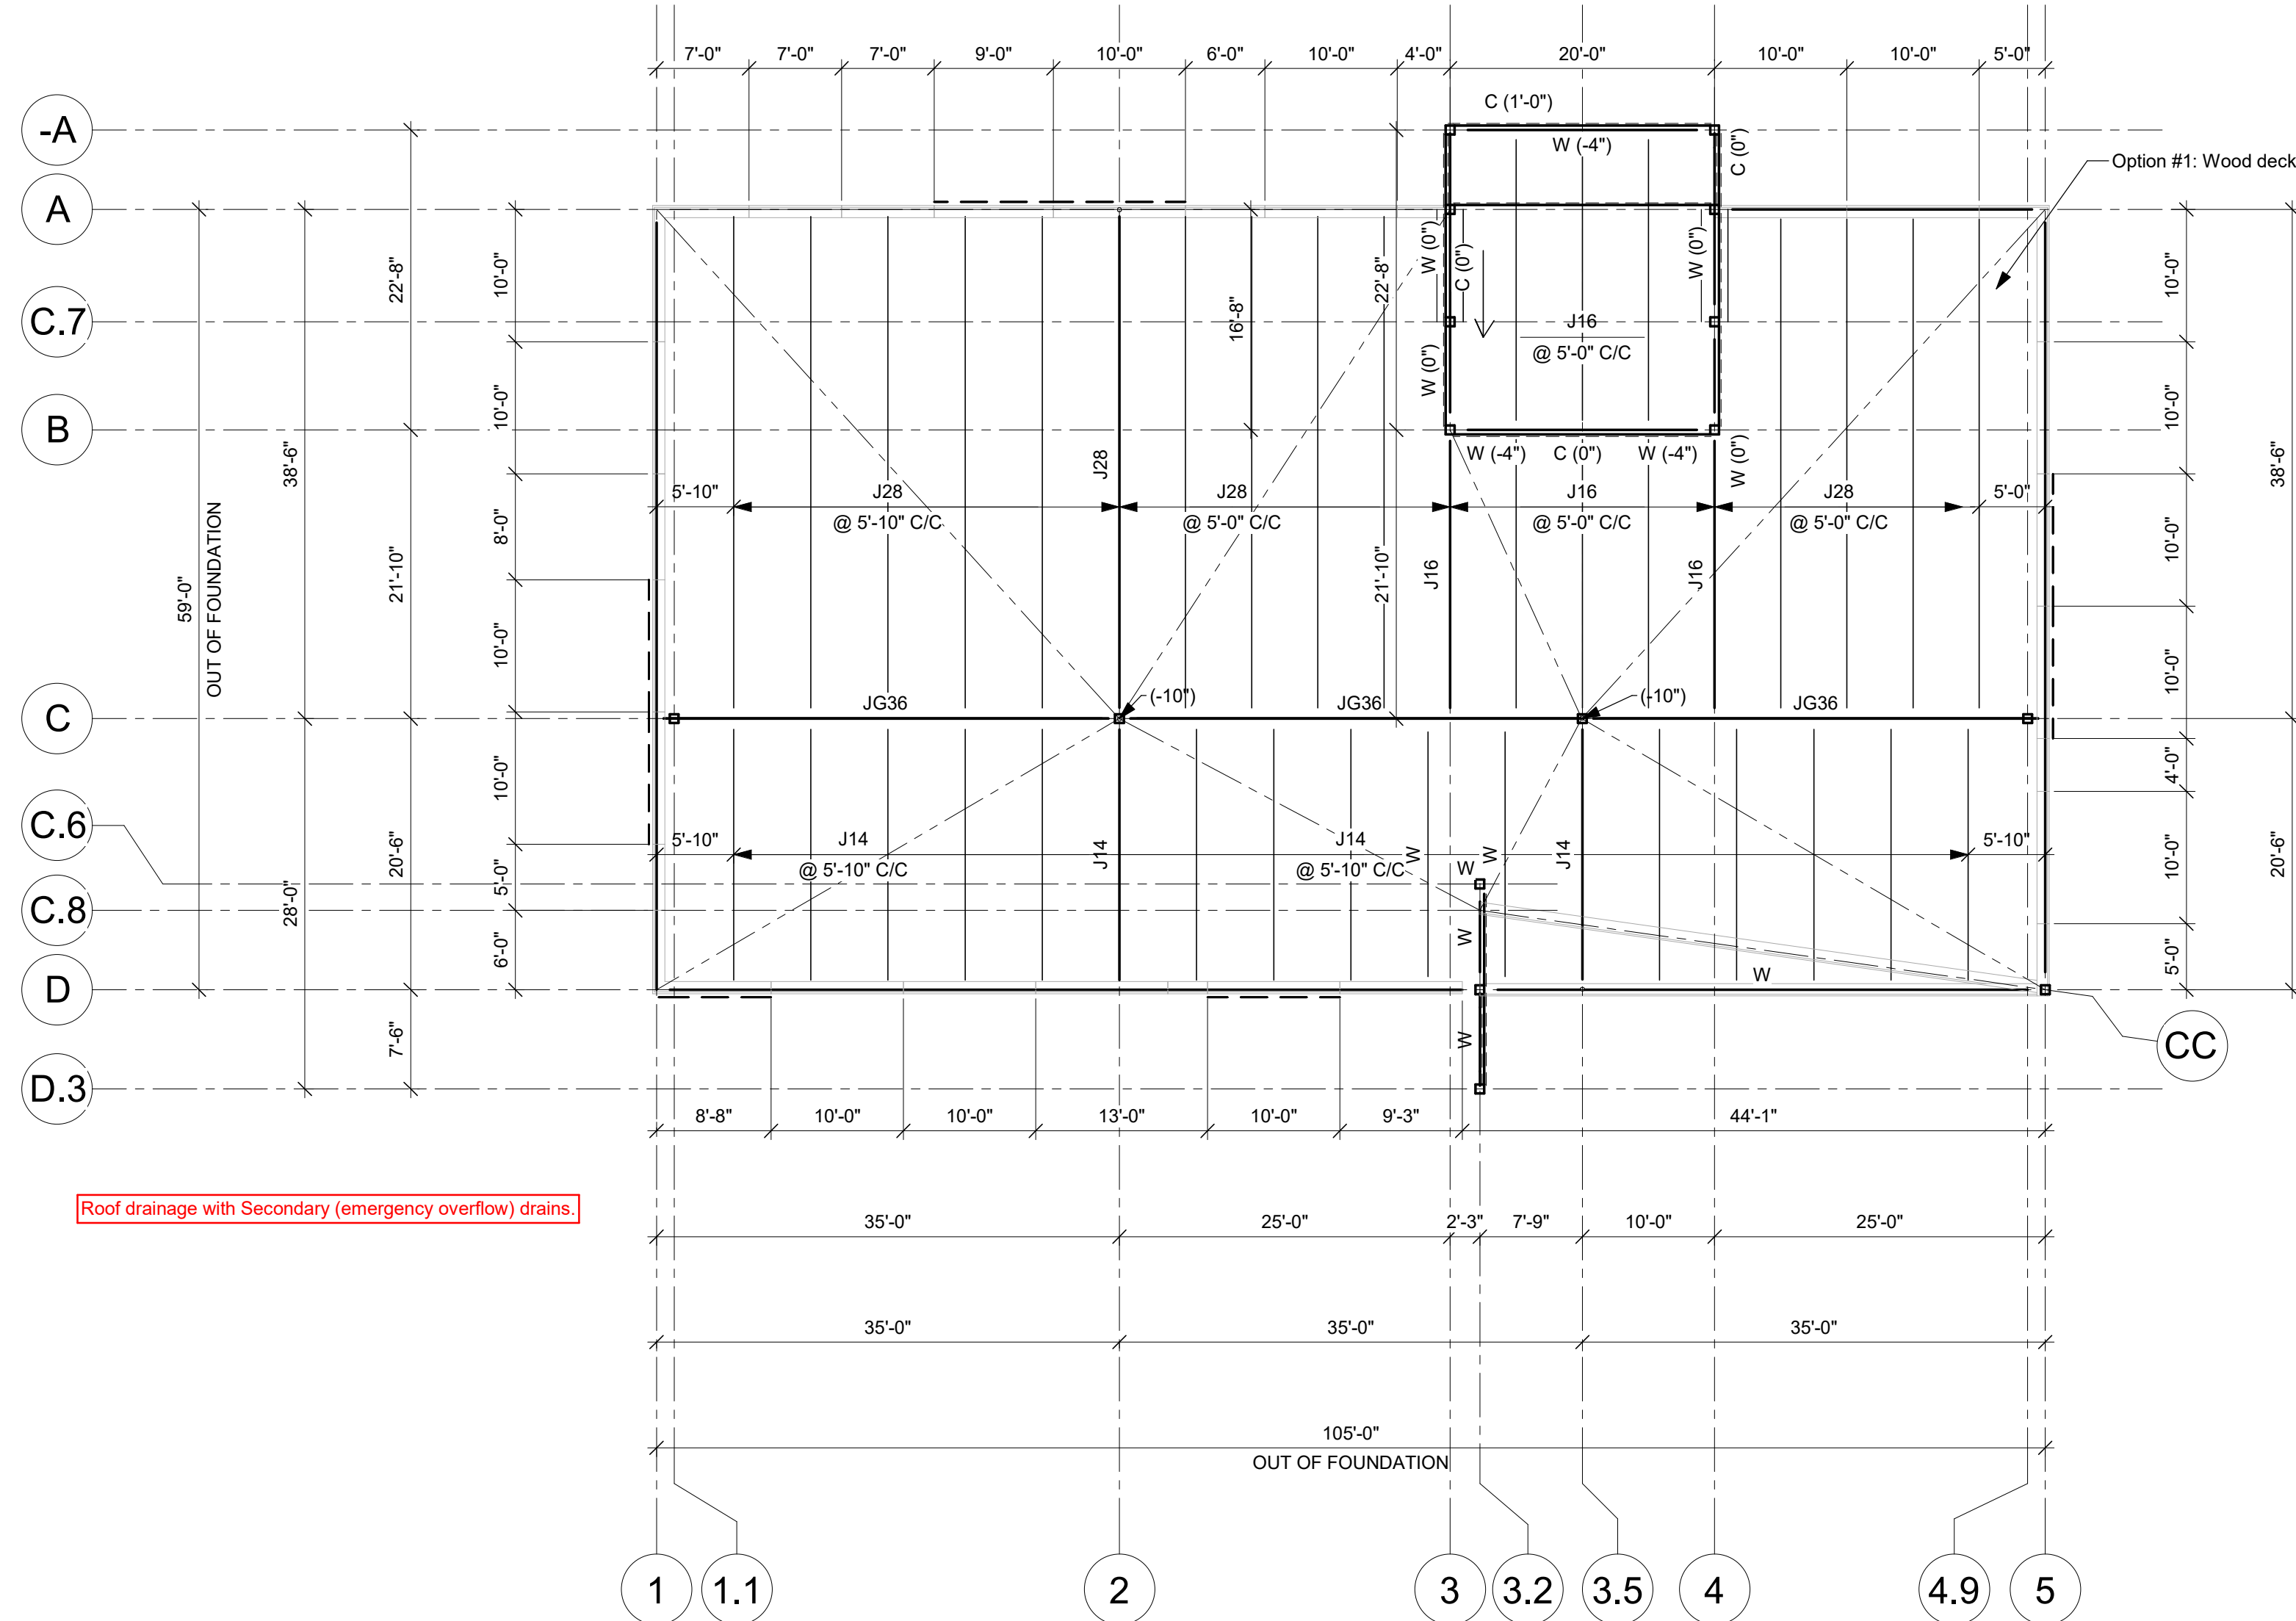

ROOF PLAN
3/32" = 1'-0"

Steel Deck: 1.5B gage 22, double span
Perimeter Angles: L3x3x1/4"

PRELIMINARY

NOT TO BE USED FOR CONSTRUCTION

REVISION	DATE	DESCRIPTION	DRAWN	VER
PROJECT MANAGER				
		-		
		-		
		-		
		-		
		-		
DRAFTING				
		-		
DRAWN	DESIGNED	PROJECT ENGINEER	SCALE:	
INITIALE		PROJECT ENG.	Comme indiqué	
CHECKED	CONSULTING ENGINEERS / ARCHITECTS ENGINEER ARCHITECT		DATE (yyyy/mm/dd): YYYYMM/DD	
CUSTOMER				



11505, 1re Avenue, bureau 500, Saint-Georges Beauce
Quebec, Canada, G5Y 7X3
Phone : (418) 228-8031
Toll free : (877) 499-6049
www.canam.com

PROFESSIONAL SEAL

PROJECT	
---------	--

Scarborough, ME

DRAWING TITLE

PRELIMINARY SKETCH - ROOF PLAN

Initials		CONTRACT NUMBER P2026-095	DRAWING NUMBER	DIVISION	REVISION
		PJ NO.	EsMx401		