


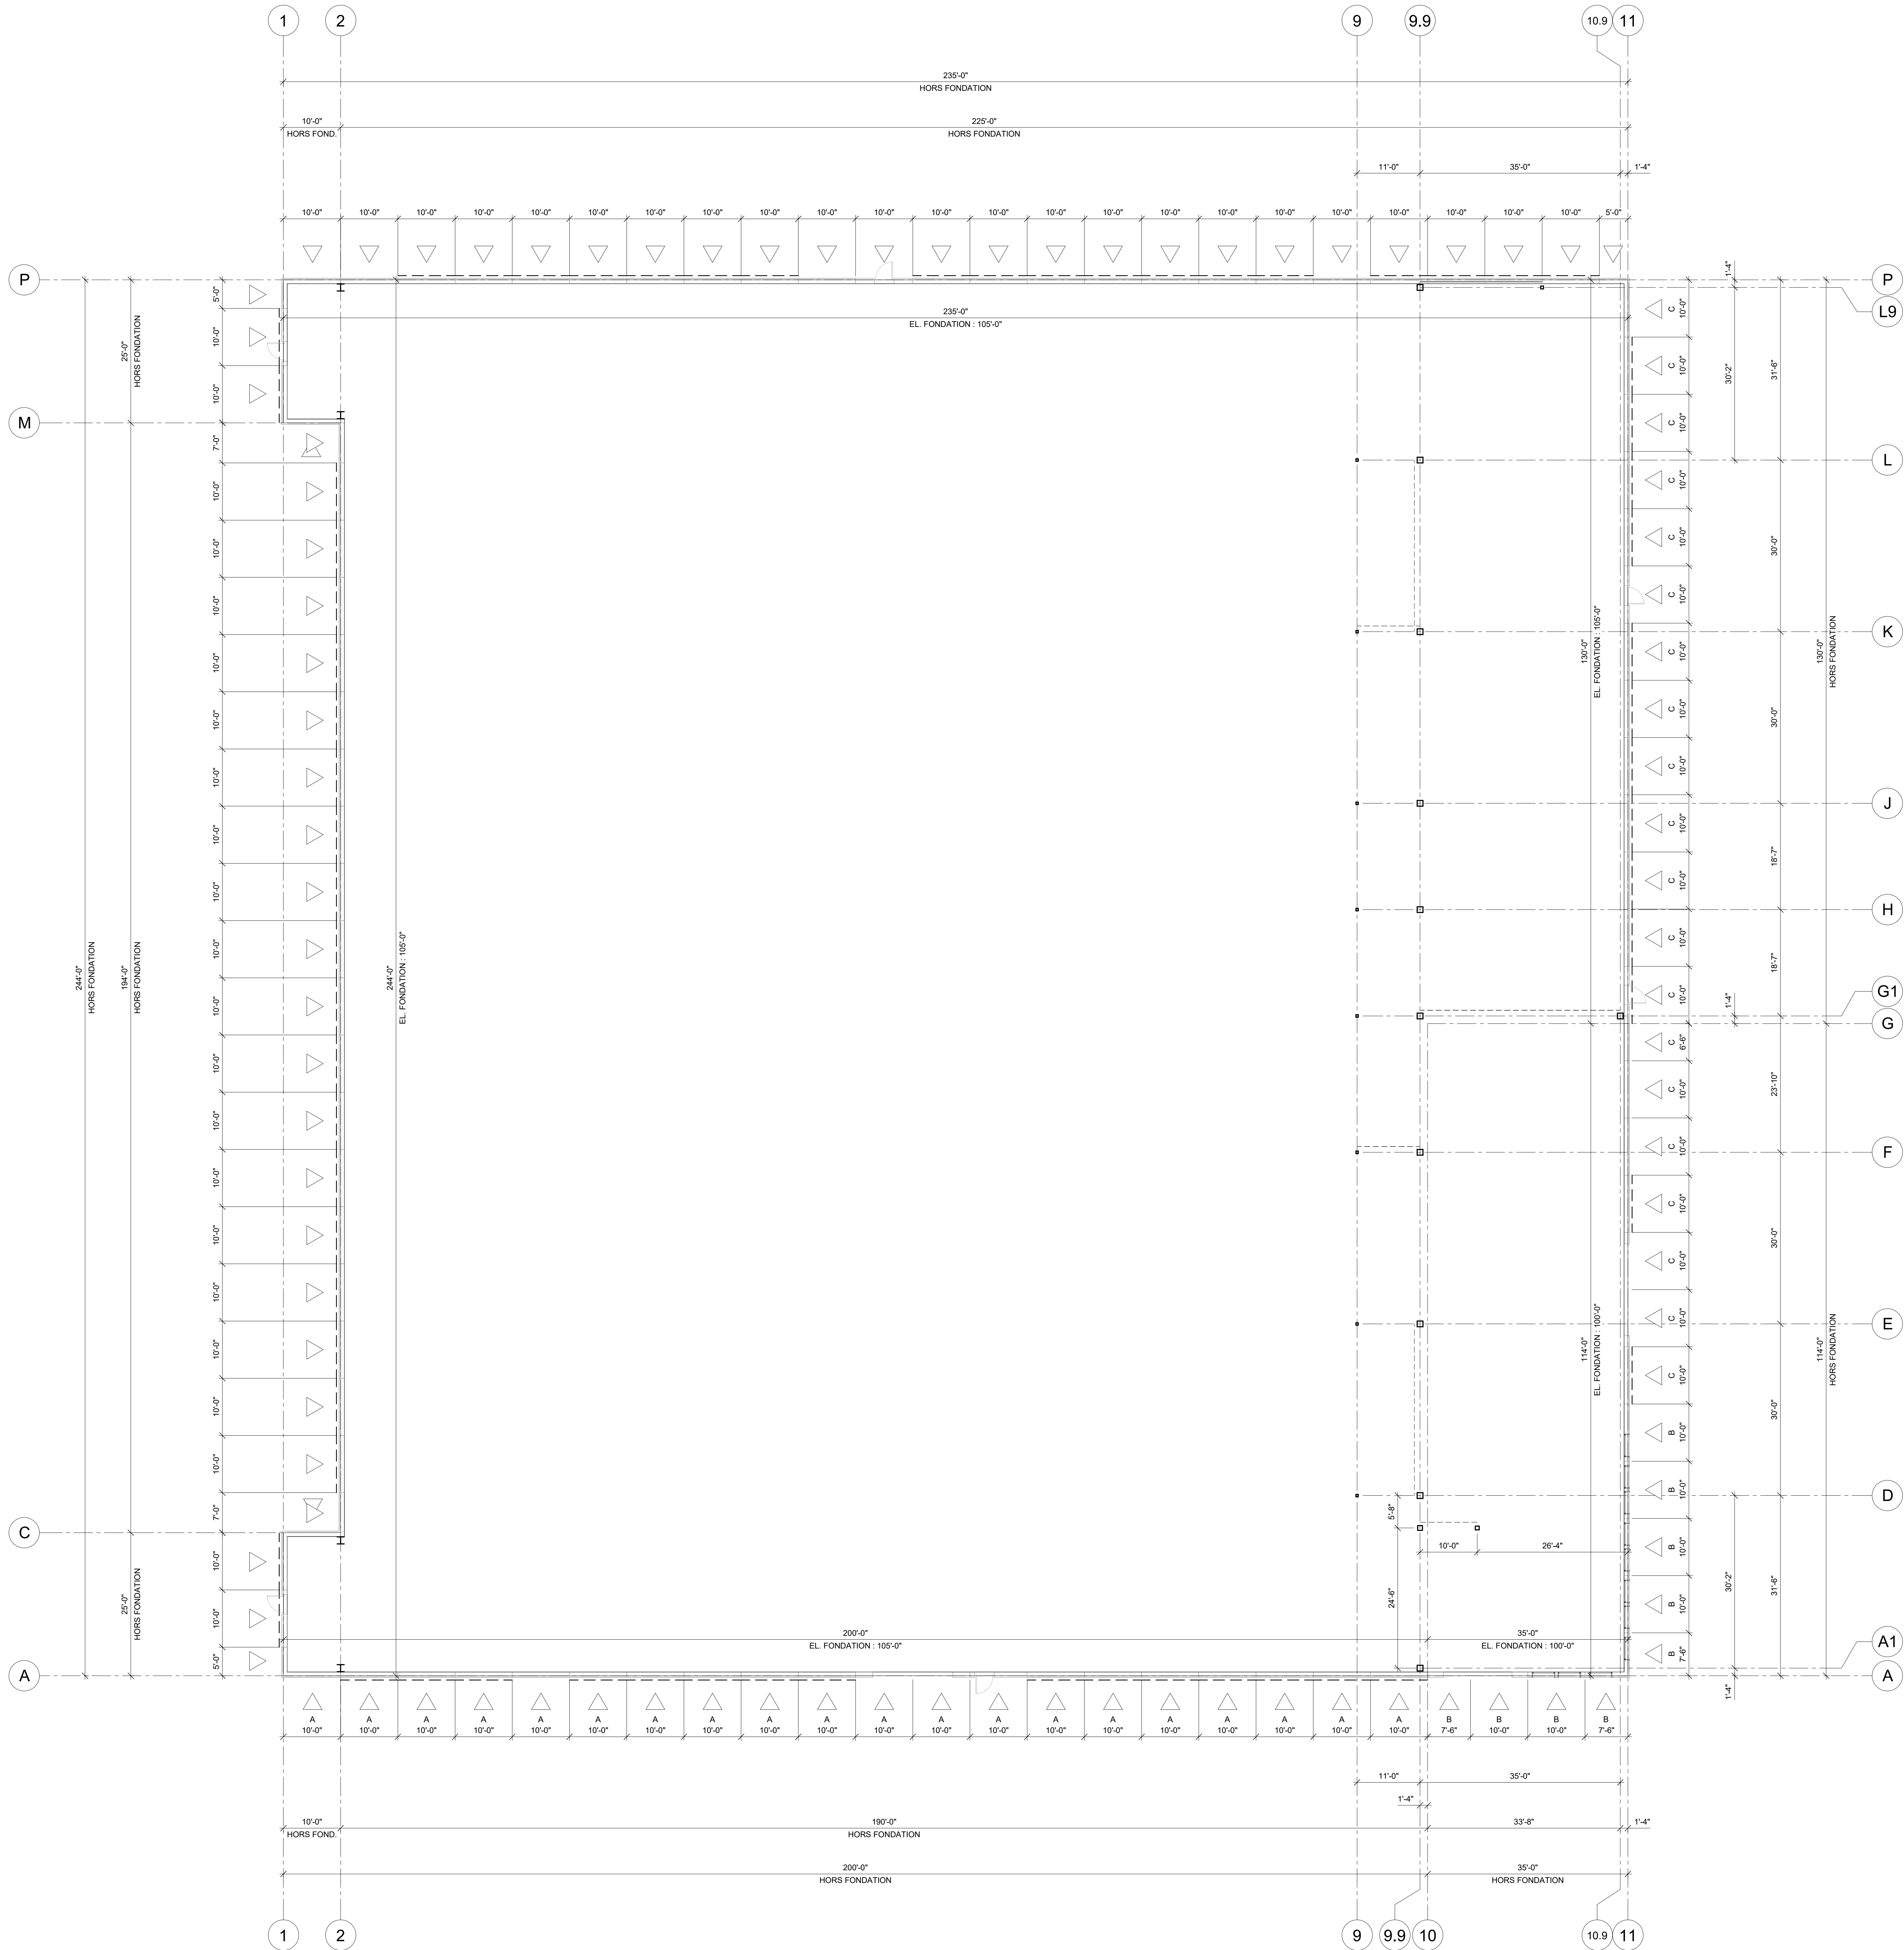

PLAN D'ANCRAGE
3/32" = 1'-0"

NOTE POUR LE CONTRACTEUR/ÉRECTEUR:
IL EST STRICTEMENT DÉFENDU DE MODIFIER, COPIER, REPRODUIRE OU DE DISTRIBUER CES DESSINS OU QUELQUES REPRÉSENTATIONS DE CES DESSINS, PAR TOUTES SOURCES DE MÉDIA INCLUANT ÉLECTRONIQUEMENT, SANS L'APPROBATION ÉCRITE DE GROUPE CANAM INC.

PRÉLIMINAIRE

NE DOIT PAS SERVIR À LA CONSTRUCTION

REVISION	DATE	DESCRIPTION	DESS	VER
----------	------	-------------	------	-----

GERANT DE PROJET	.
.	.
.	.

DESSIN	CONÇU PAR	INGÉNIEUR DU PROJET	ÉCHELLE:
DESSINÉ PAR	INITIALE		3/32" = 1'-0"
VÉRIFIÉ PAR	INGÉNIEURS CONSEILS / ARCHITECTES	DATE (jj/mm/aaaa)	06/05/2026

CLIENT: Urbanex Construction Inc.

CANAM
11505, 1re Avenue, bureau 500, Saint-Georges Beauce
Québec, Canada, G5Y 7X5
Téléphone : (418) 228-8031
Sans frais : (877) 459-8049
www.canam.com

SCAUX PROFESSIONNELS

PROJET
Centre Sportif François Bourrin
Beauport, Québec

TITRE
CROQUIS PRÉLIMINAIRE - PLAN D'ANCRAGE

NUMÉRO CONTRAT	NUMÉRO DESSIN	DIVISION	REVISION
P2026-097	EsMx101		

Initiales

